ПРОЕКТНАЯ ДОКУМЕНТАЦИЯ

Индивидуальный жилой дом

кадастровый номер Россия

#ID Проекта



РОССИЯ
2025

Ведомость листов

Наименование	Лист
Обложка	
Общие данные	02
Сводная ведомость материалов	03
Генеральный план	04
3D Виды	05
План фундамента	06
3Д вид фундамента	07
Схема нижнего армирования фундамента	08
Схема верхнего армирования фундамента	09
Узлы фундамента	10
Схема арматурного каркаса фундаментной плиты	11
План на отм. ±0.000	12
План на отм +3.400	13
План коммуникаций	14
Наружные сети	15
Каталог дверных проемов	16
Каталог оконных проемов	17
Маркировка оконных проемов первого этажа	18
Маркировка оконных проемов второго этажа	19
Маркировка дверных проемов первого этажа	20
Маркировка дверных проемов второго этажа	21
Разрез 1 - 1	22
Разрез 2 - 2	23
Разрез по стене	24
План перекрытия на отм. +3,400	25
План перекрытия на отм. +6,700	26
Монолитный пояс на отм. +6,350	27
План кровли	28
Схема расположения стропил	29
3Д Вид стропильной системы	30
Ведомость материалов (стропильная система)	31
План расстановки мебели 1 этаж	32
План расстановки мебели 2 этаж	33
Экспликация помещений 1- го этажа	34
Экспликация помещений 2-го этажа	35
Фасад в осях 1-4	36
Фасад в осях Г-А	37
Фасад в осях А-Г	38
Фасад в осях 4-1	39

						#ID Проекта		
						кадастровый номер Россия		
Изм.	Кол.уч.	Лист	№Док.	Подп.	Дата			
Разраб.						Индивидуальный жилой дом	Стадия: #Стадия Проекта	Лист: 02 / Листов:
						Общие данные		

Ведомость перекрытия			
Наименование	Количество	Длина, мм	Объем, м3
Балка деревянная 200x50	1	1 300	0,01
Балка деревянная 200x50	1	4 040	0,04
Балка деревянная 200x50	2	1 210	0,02
Балка деревянная 200x50	2	3 740	0,08
Балка деревянная 200x50	14	6 140	0,84
Балка деревянная 200x50	15	2 840	0,45
	35		**1,44 м³**

ИКК-05 Монолитные участки	
Наименование	Объем
Перекрытие	22,56

ВЕДОМОСТЬ КРОВЕЛЬНОГО МАТЕРИАЛА	
Наименование	Площадь, м2
Кровля дома	138,23

ВЕДОМОСТЬ НА МОНОЛИТНЫЙ ПОЯС 2-ГО ЭТАЖА	
Наименование	Объем, м3
	2,51
Монолитный пояс	2,51

ВЕДОМОСТЬ СТРОПИЛЬНОЙ СИСИТЕМЫ	
Наименование	Объем, м3
Коньковый брус 200x100	0,71
Мауэрлат 100x200	0,72
Стропильная нога 200x50	2,04

ВЕДОМОСТЬ БЛОКА ДЛЯ СТЕН		
Имя	Тип конструкций	Объем, м3
Газобетон D400	Несущие 400мм	89,19
Газобетон перегородки	Перегородки 100мм	12,84

ВЕДОМОСТЬ НА УТЕПЛИТЕЛЬ ДЛЯ СТЕН, ПОЛА ПЕРВОГО ЭТАЖА, РОСТВЕРКА			
Наименование	**Компоненты**		
	Толщина [м]	**Объем [м3]**	**Площадь [м2]**
Изоляция - Минеральная Мягкая			
	200	15,50	77,48
Изоляция - ЭППС			
	50	0,82	16,35
	100	7,57	75,75


Конструкция пола			
Наименование	**Толщина [м]**	**Объем [м3]**	**Площадь [м2]**
Бетон В 7,5			
	100	11,28	112,79
Мембрана - Гидроизоляция			
	0	0,00	94,08
Стяжка ЦПР			
	80	6,06	94,08
	100	1,82	18,71

Отделочные материалы		
Наименование	**Компоненты**	
	Толщина [м]	**Площадь [м2]**
клинкерная термопанель		
	50	216,99
Планкен		
	10	5,13


ВЕДОМОСТЬ БЕТОНА	
Наименование	Объем, м3
Плита	50,76

Изм.	Кол.уч.	Лист	№Док.	Подп.	Дата	#ID Проекта		
						кадастровый номер Россия		
Разраб.						Индивидуальный жилой дом	Стадия: #Стадия Проекта	Лист: 03 / Листов:
						Сводная ведомость материалов		

Проектируемый
участок

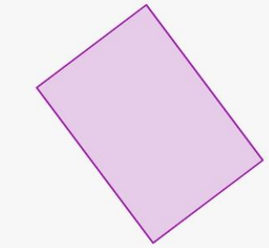



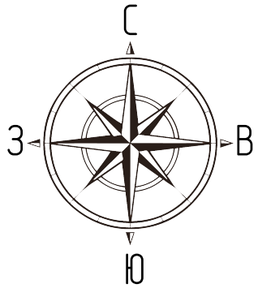


Проектируемый дом

Терраса, крыльцо


						#ID Проекта		
						кадастровый номер Россия		
Изм.	Кол.уч.	Лист	№Док.	Подп.	Дата			
Разраб.						Индивидуальный жилой дом	Стадия	Лист	Листов
							#Стадия Проекта	04	
						Генеральный план			





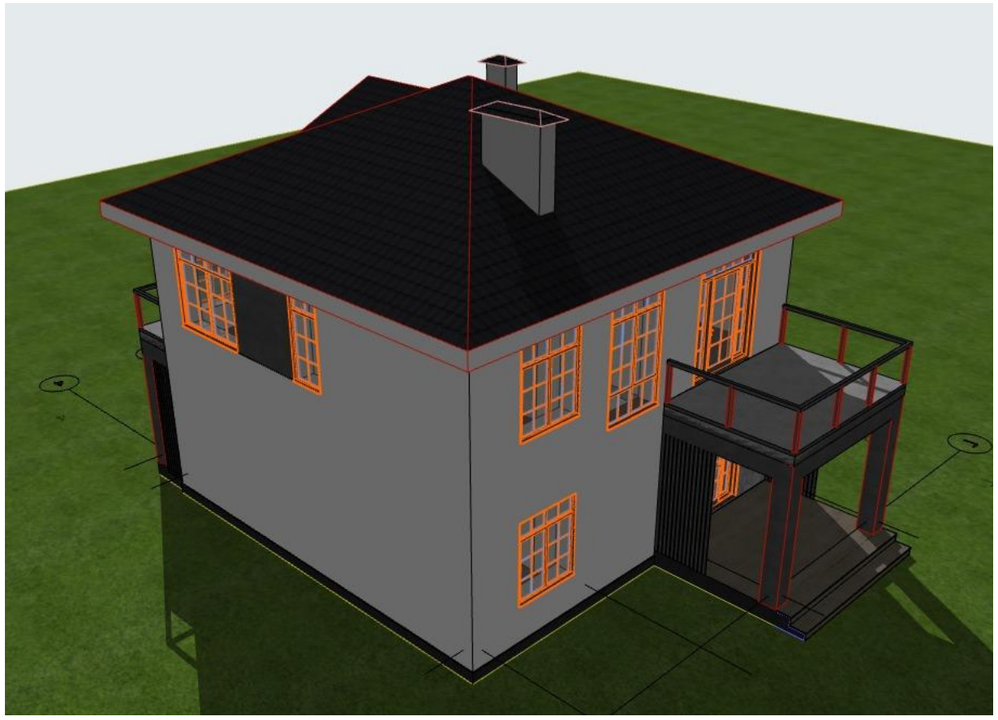

						#ID Проекта		
						кадастровый номер Россия		
Изм.	Кол.уч.	Лист	№Док.	Подп.	Дата			
Разраб.						Индивидуальный жилой дом	Стадия	Лист	Листов
							#Стадия Проекта	05	
						3D Виды			

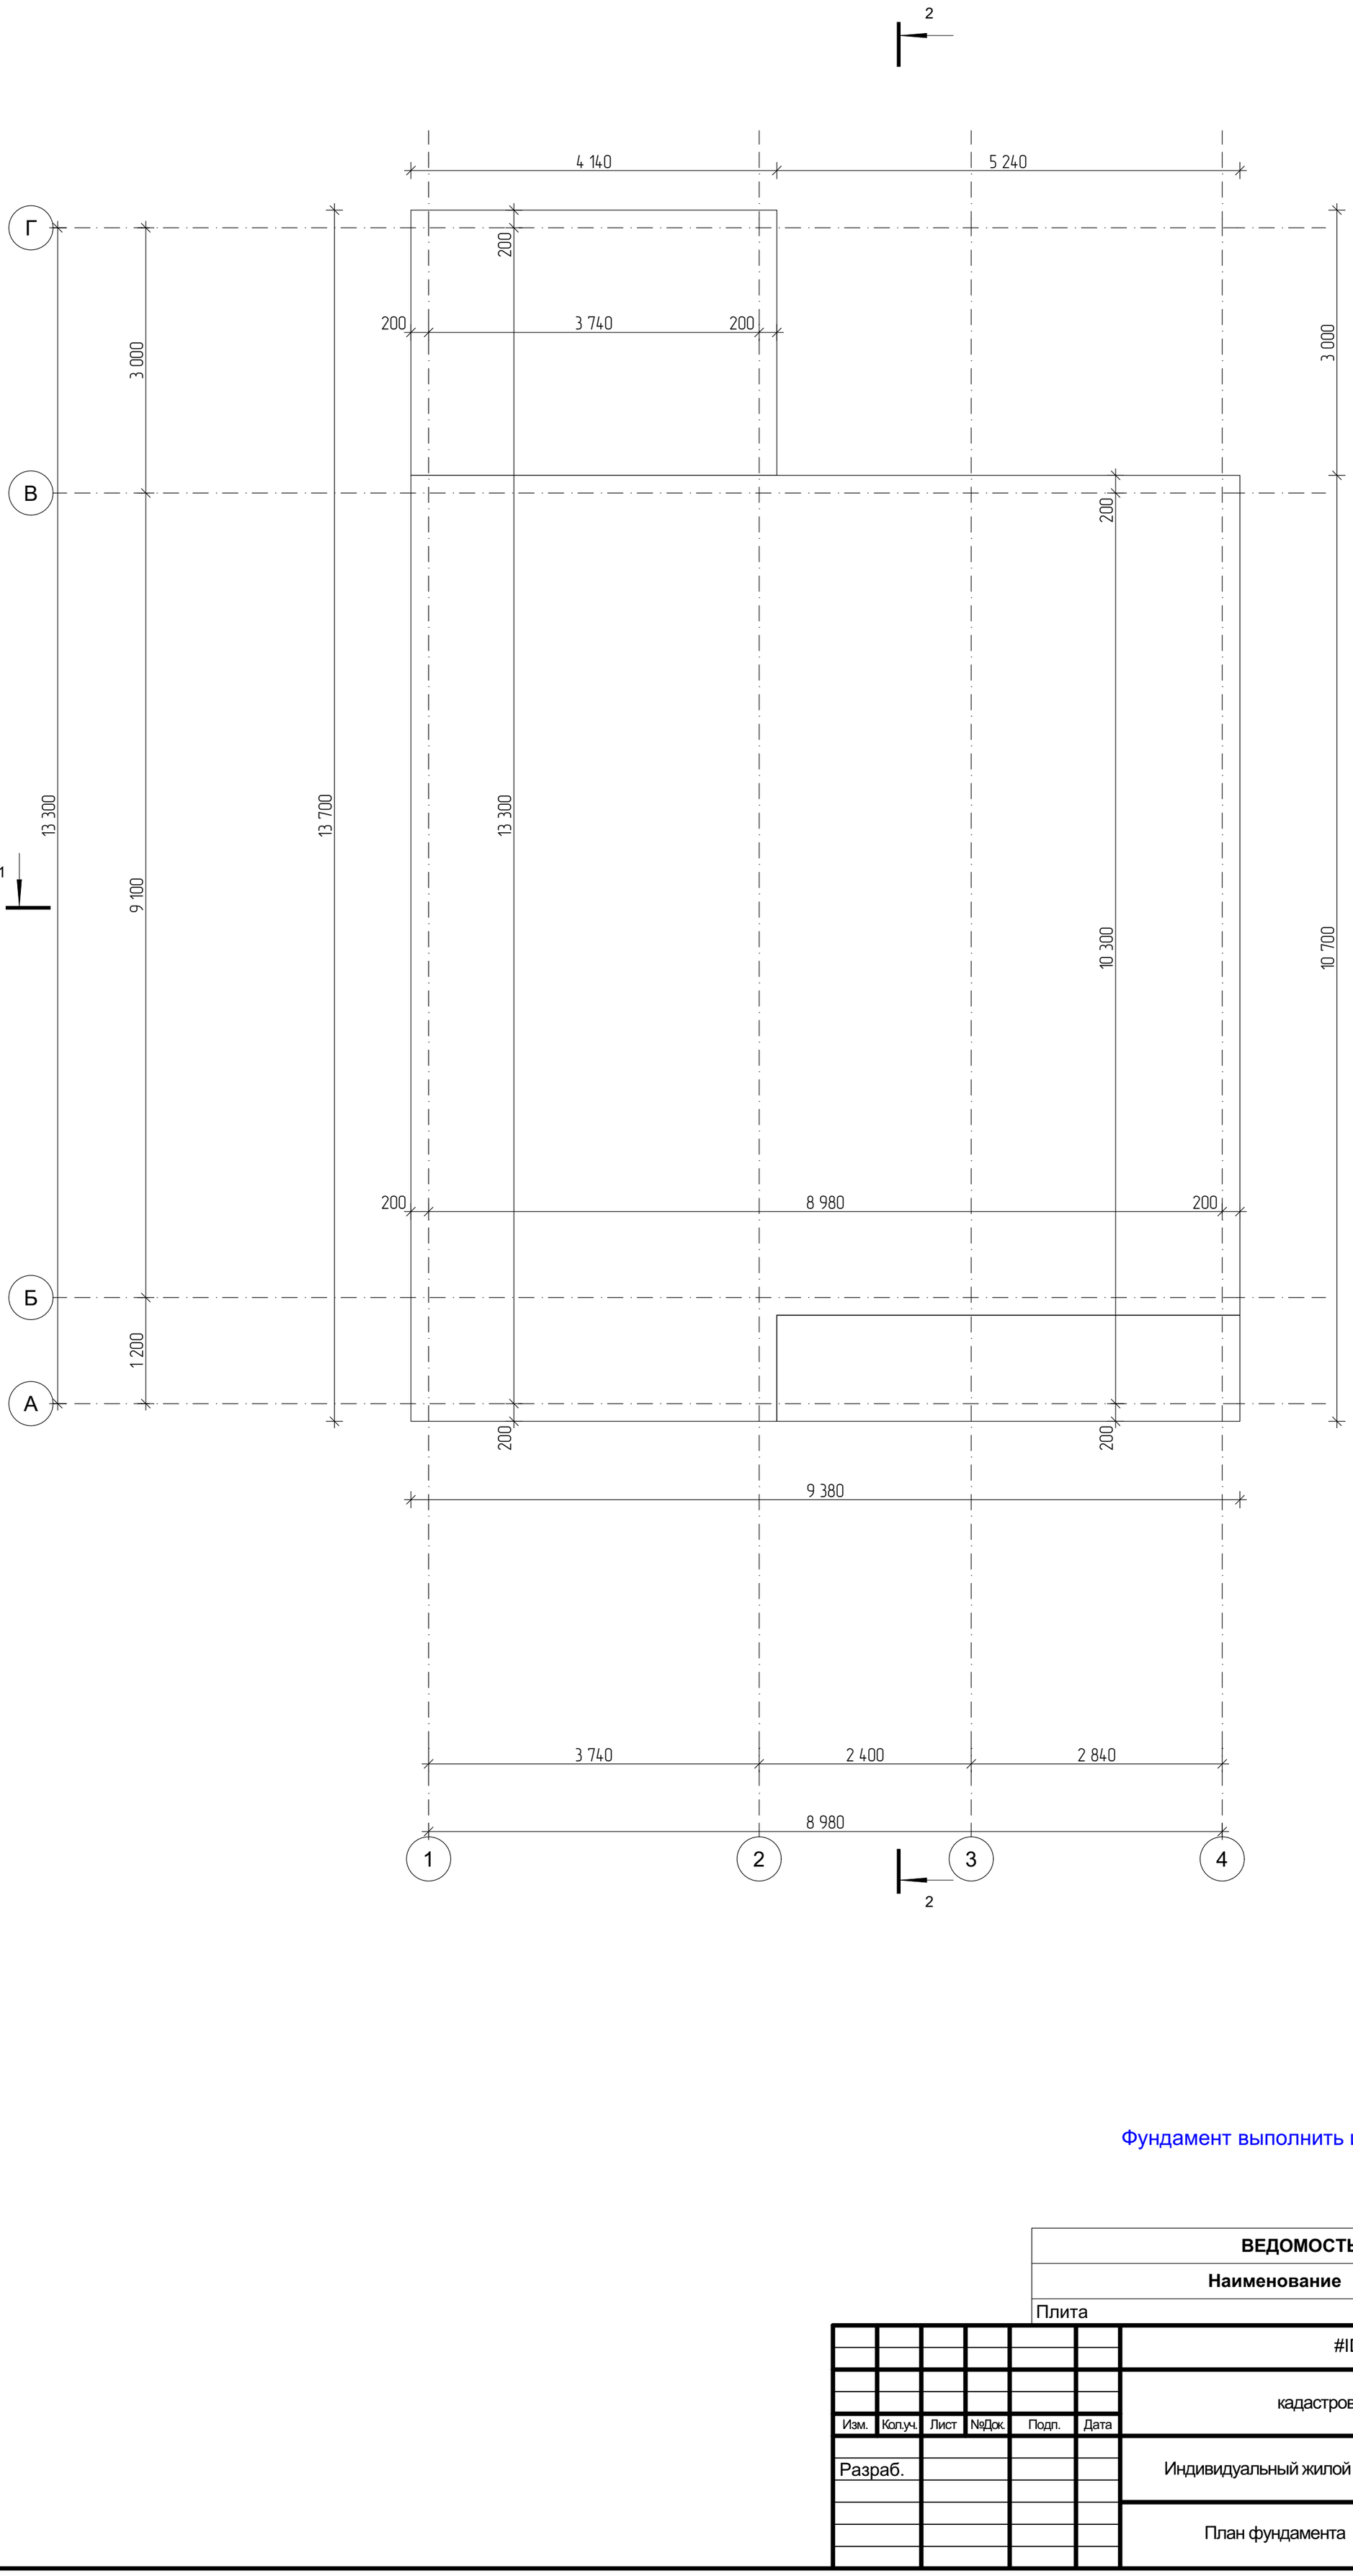


Фундамент выполнить из бетона класса В25

ВЕДОМОСТЬ БЕТОНА


Наименование	Объем, м3
Плита	50,76

						#ID Проекта		
						кадастровый номер Россия		
Изм.	Кол.уч.	Лист	№Док.	Подп.	Дата			
Разраб.						Индивидуальный жилой дом	Стадия: #Стадия Проекта	Лист: 06 / Листов:
						План фундамента		

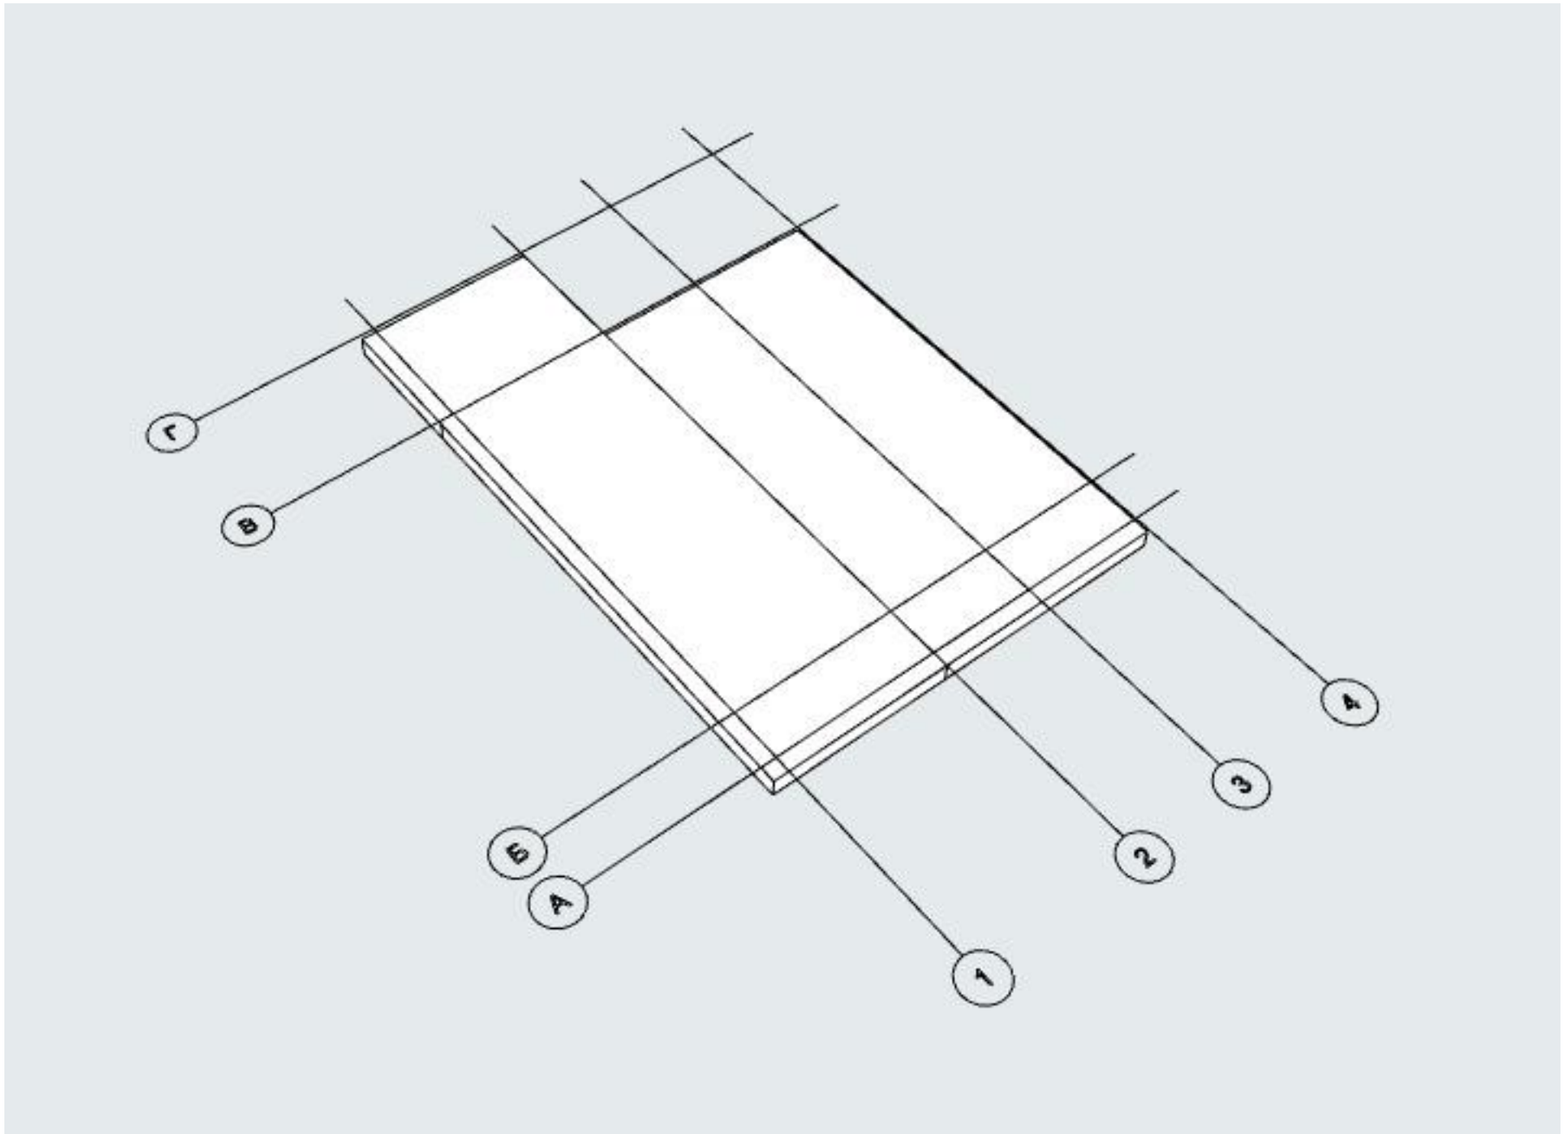



						#ID Проекта
						кадастровый номер Россия
Изм.	Кол.уч.	Лист	№Док.	Подп.	Дата	
Разраб.						Индивидуальный жилой дом
						3Д вид фундамента

Стадия	Лист	Листов
#Стадия Проекта	07	

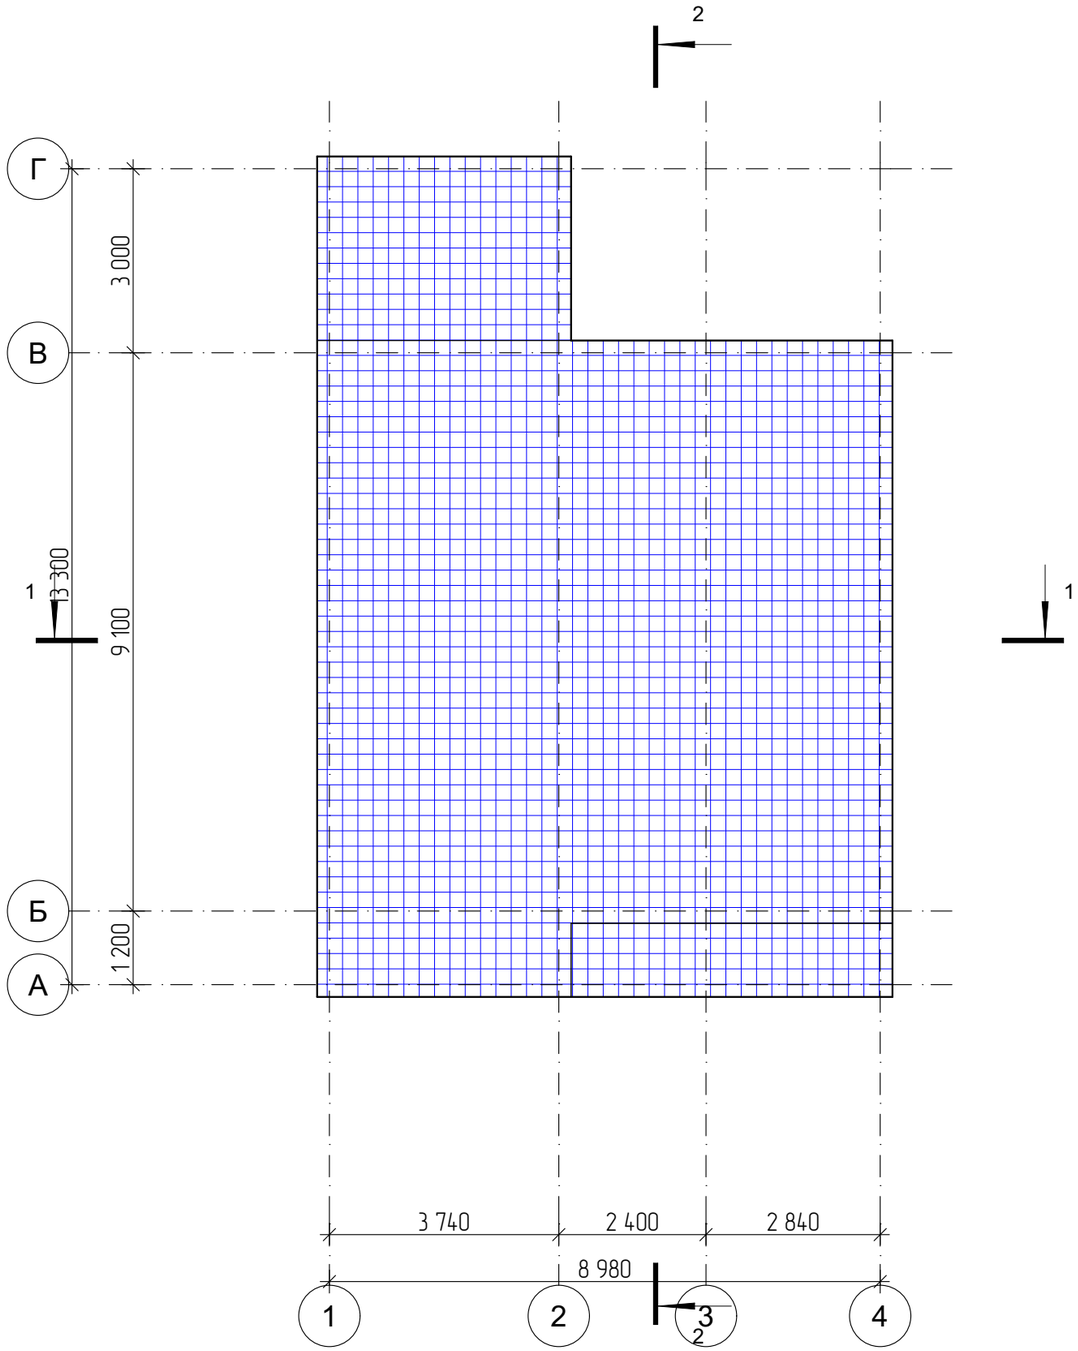


						#ID Проекта		
						кадастровый номер Россия		
Изм.	Кол.уч.	Лист	№Док.	Подп.	Дата			
Разраб.						Индивидуальный жилой дом	Стадия: #Стадия Проекта	Лист: 08 / Листов:
						Схема нижнего армирования фундамента		

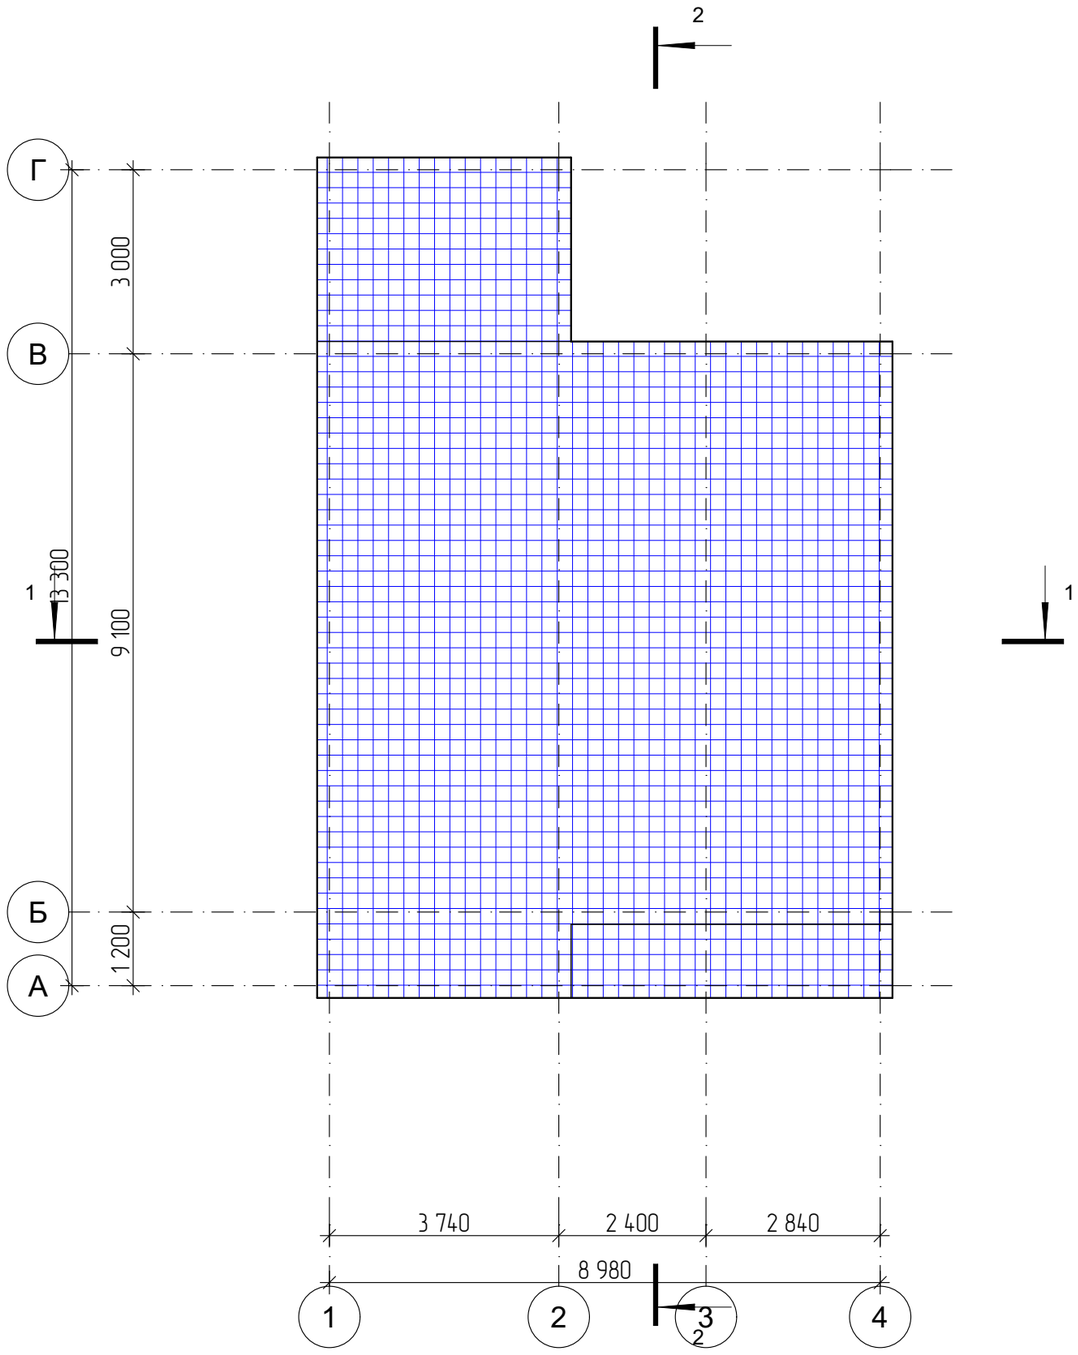

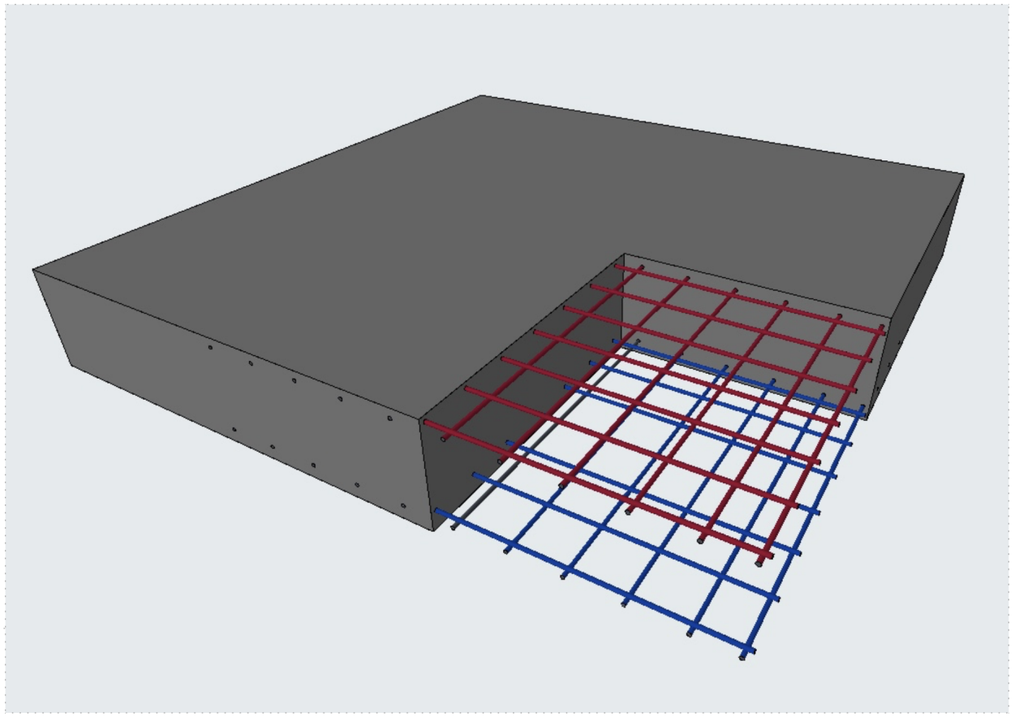



						#ID Проекта		
						кадастровый номер Россия		
Изм.	Кол.уч.	Лист	№Док.	Подп.	Дата			
Разраб.						Индивидуальный жилой дом	Стадия: #Стадия Проекта	Лист: 09 / Листов:
						Схема верхнего армирования фундамента		


Ф2 Разрез 1:10

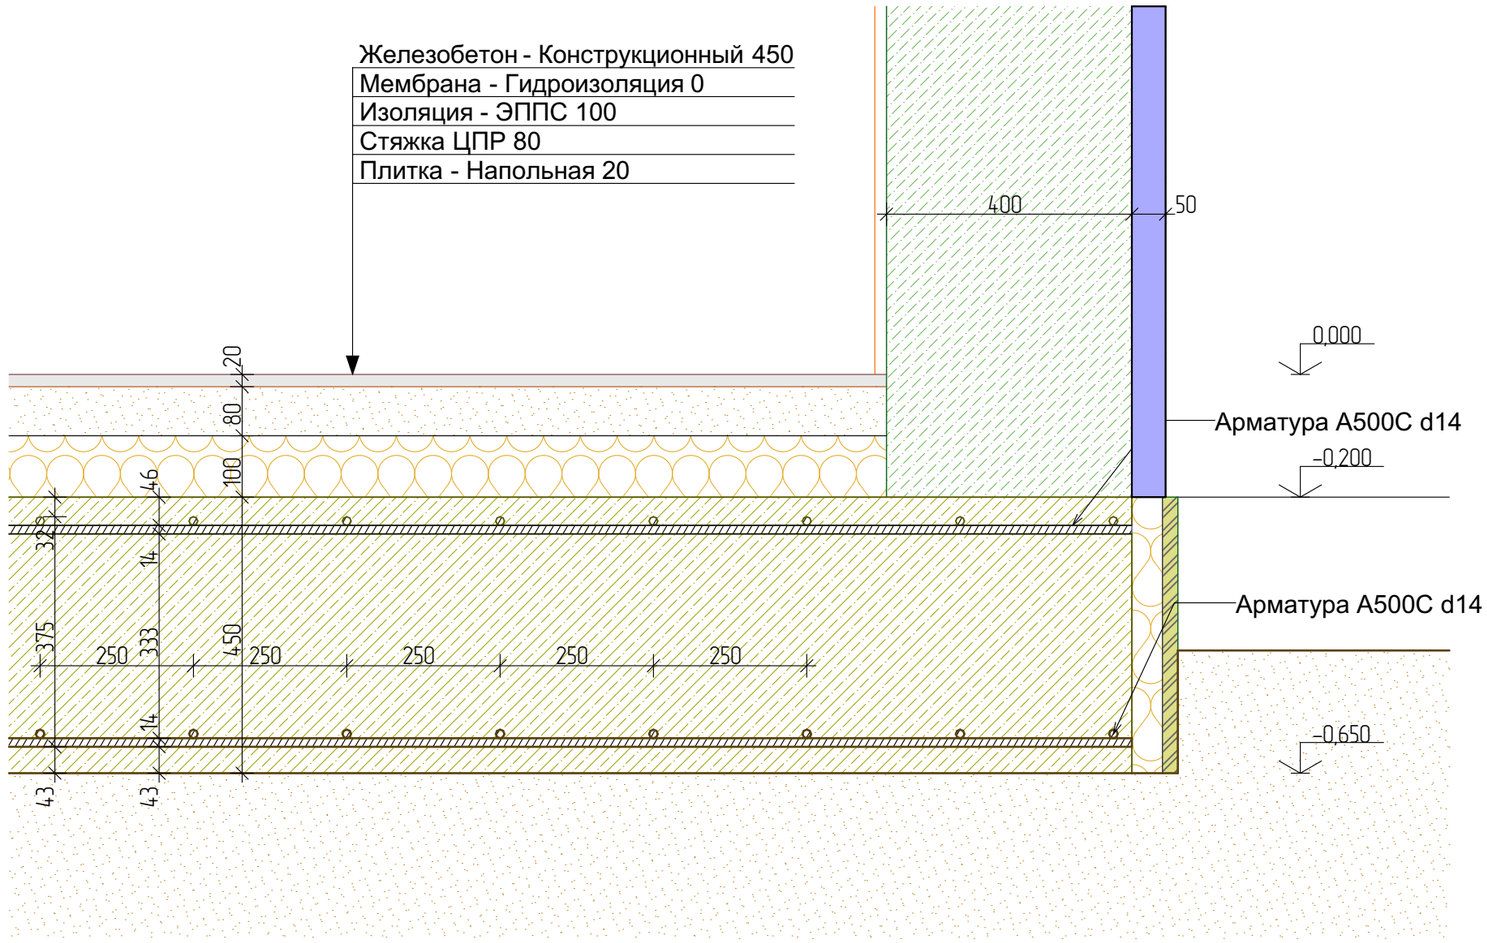

						#ID Проекта	
						кадастровый номер Россия	
Изм.	Кол.уч.	Лист	№Док.	Подп.	Дата		
Разраб.						Индивидуальный жилой дом	Стадия: #Стадия Проекта; Лист: 10; Листов:
						Узлы фундамента	

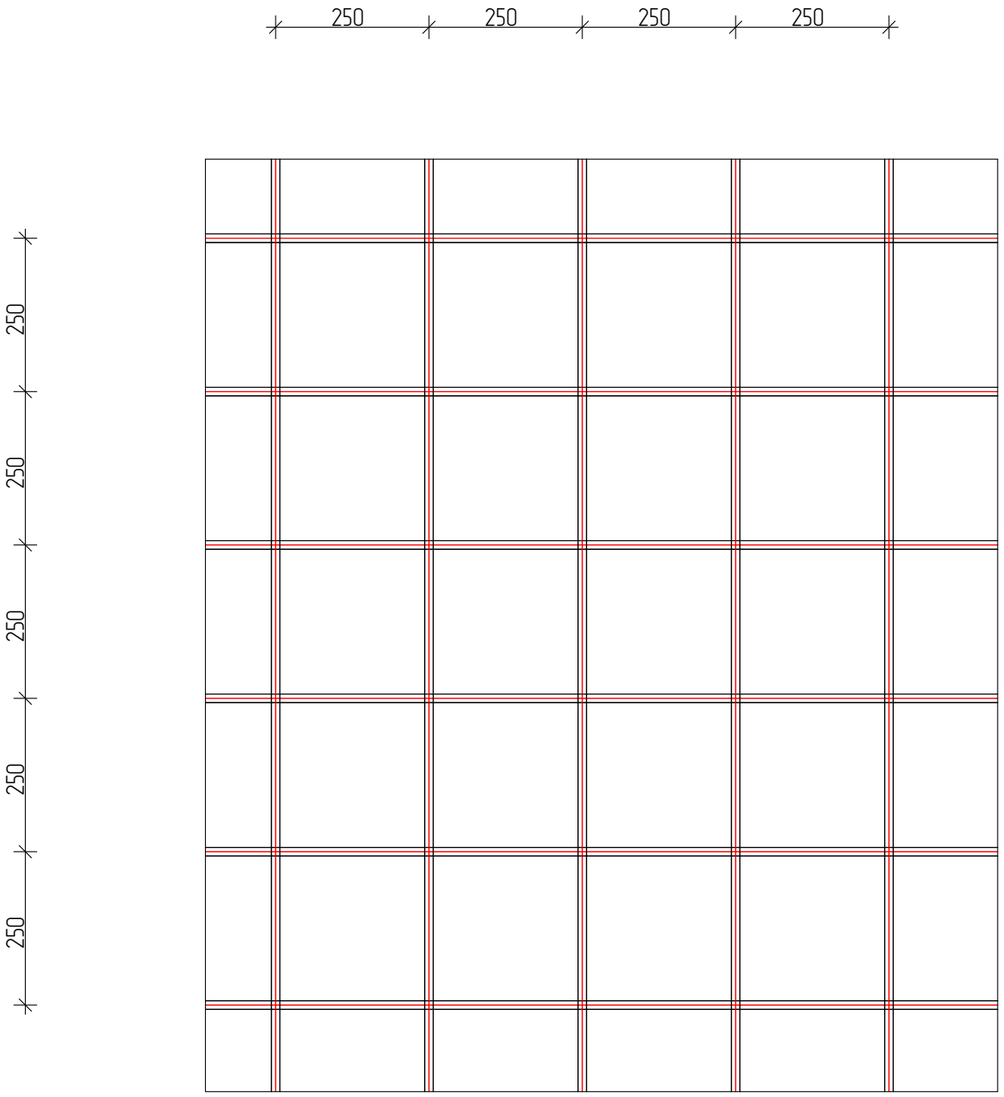

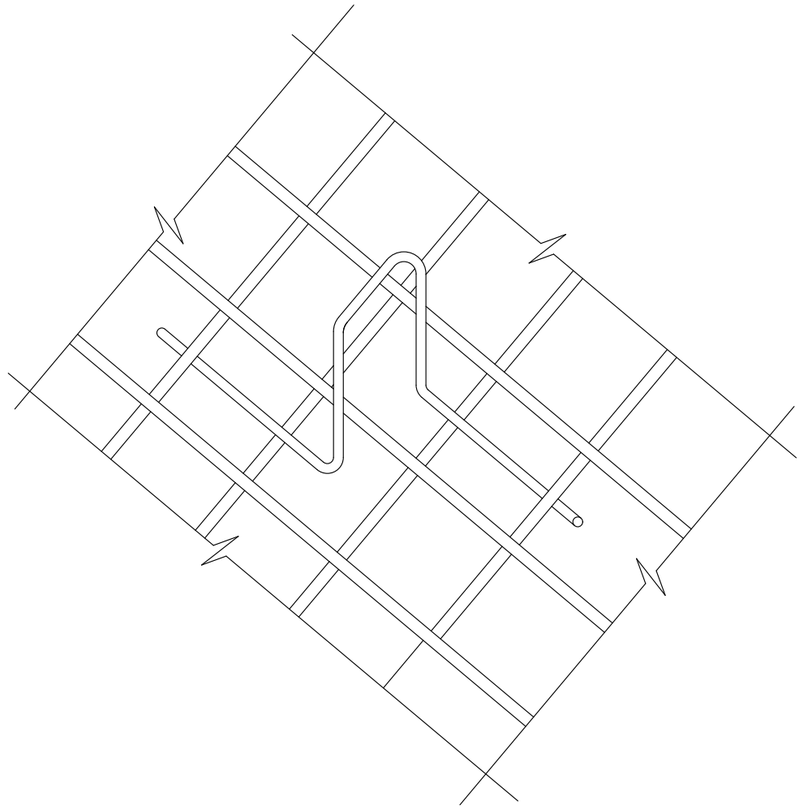


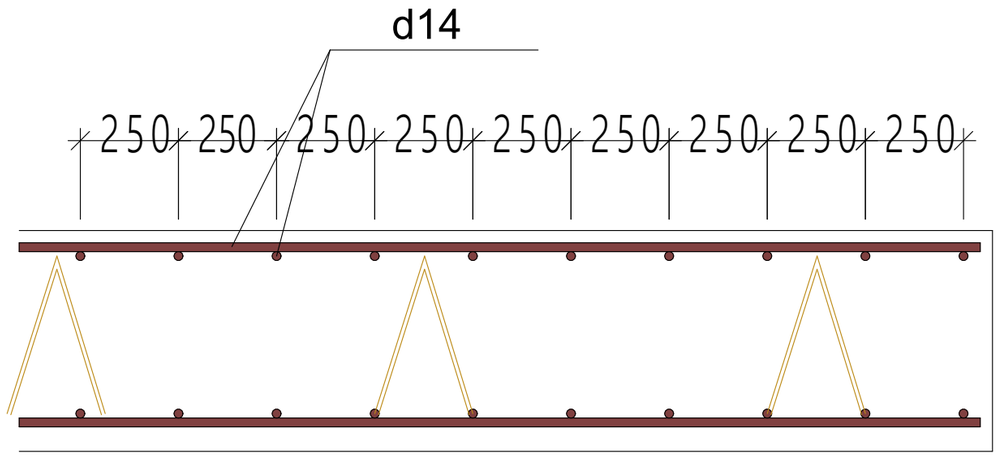

Спецификация элементов к фундаментной плите Фпм-1

МАРКА ПОЗ.	ОБОЗНАЧЕНИЕ	НАИМЕНОВАНИЕ	Кол.	МАССА, КГ	ПРИМЕ-ЧАНИЕ
		Детали			
1		Ø14AIII ГОСТ5781-82* п.м.	1931		


Изм.	Кол.уч.	Лист	№Док.	Подп.	Дата			
Разраб.						#ID Проекта		
						кадастровый номер Россия		
						Индивидуальный жилой дом	Стадия: #Стадия Проекта	Лист: 11 / Листов:
						Схема арматурного каркаса фундаментной плиты		

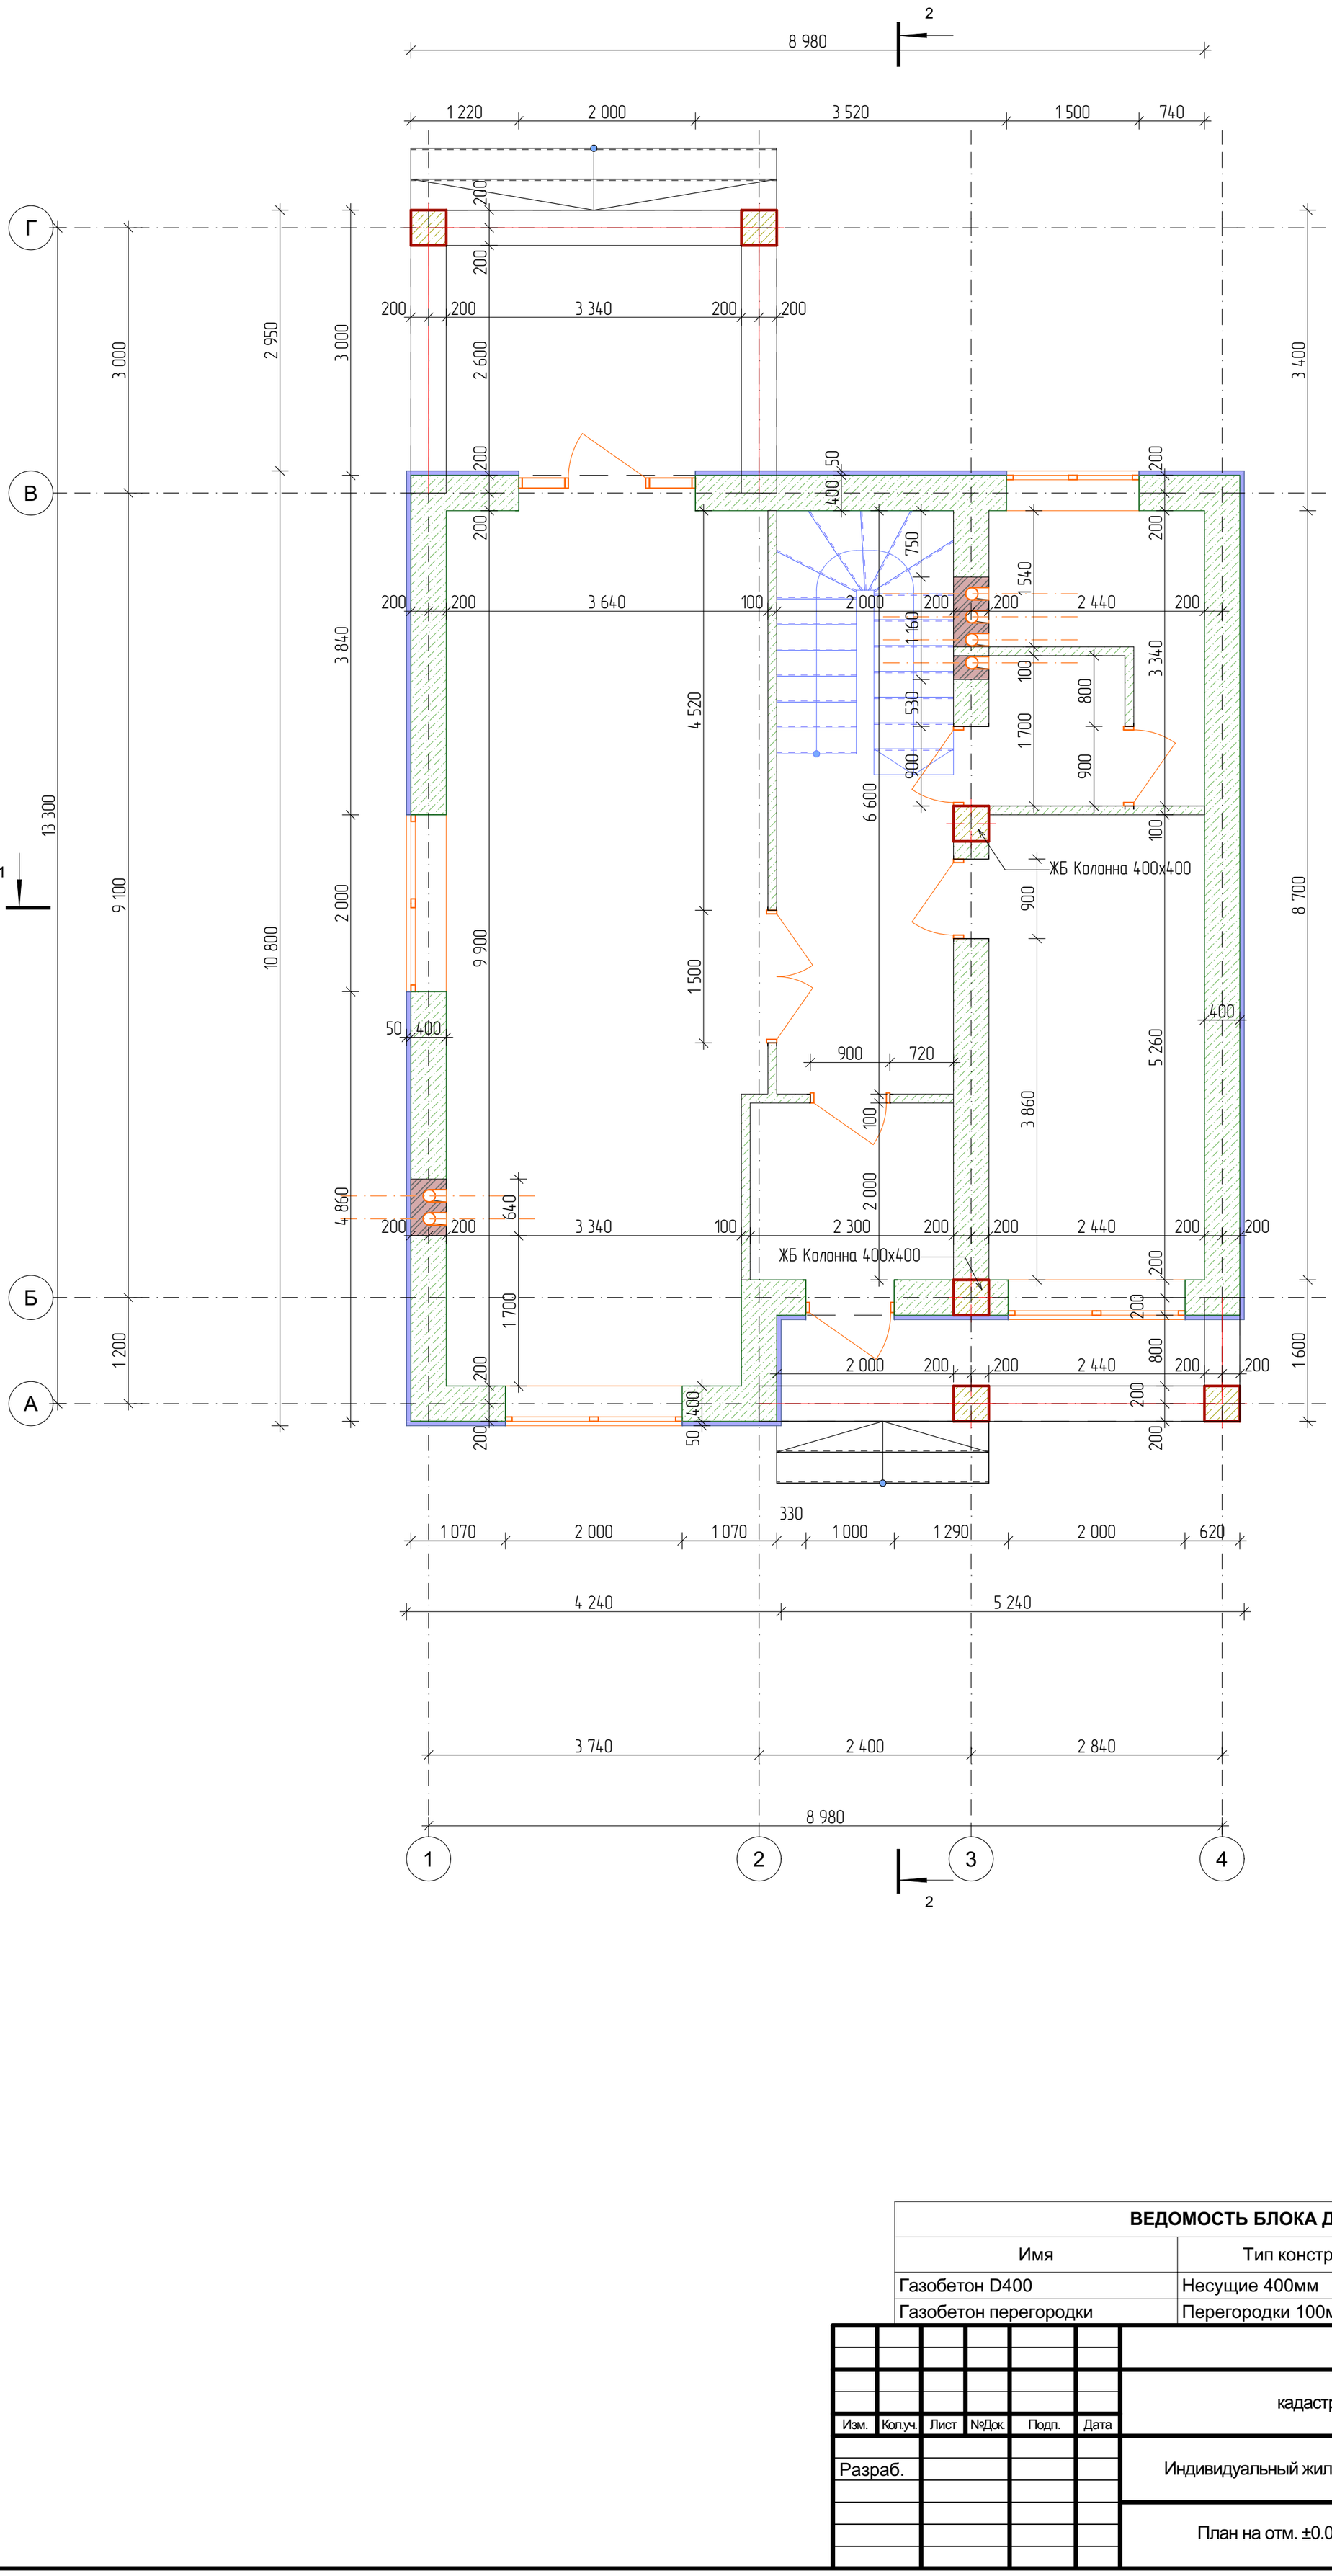


ВЕДОМОСТЬ БЛОКА ДЛЯ СТЕН


Имя	Тип конструкций	Объем, м3
Газобетон D400	Несущие 400мм	89,19
Газобетон перегородки	Перегородки 100мм	12,84

Изм.	Кол.уч.	Лист	№Док.	Подп.	Дата	#ID Проекта			
						кадастровый номер Россия			
Разраб.						Индивидуальный жилой дом	Стадия	Лист	Листов
							#Стадия Проекта	12	
						План на отм. ±0.000			

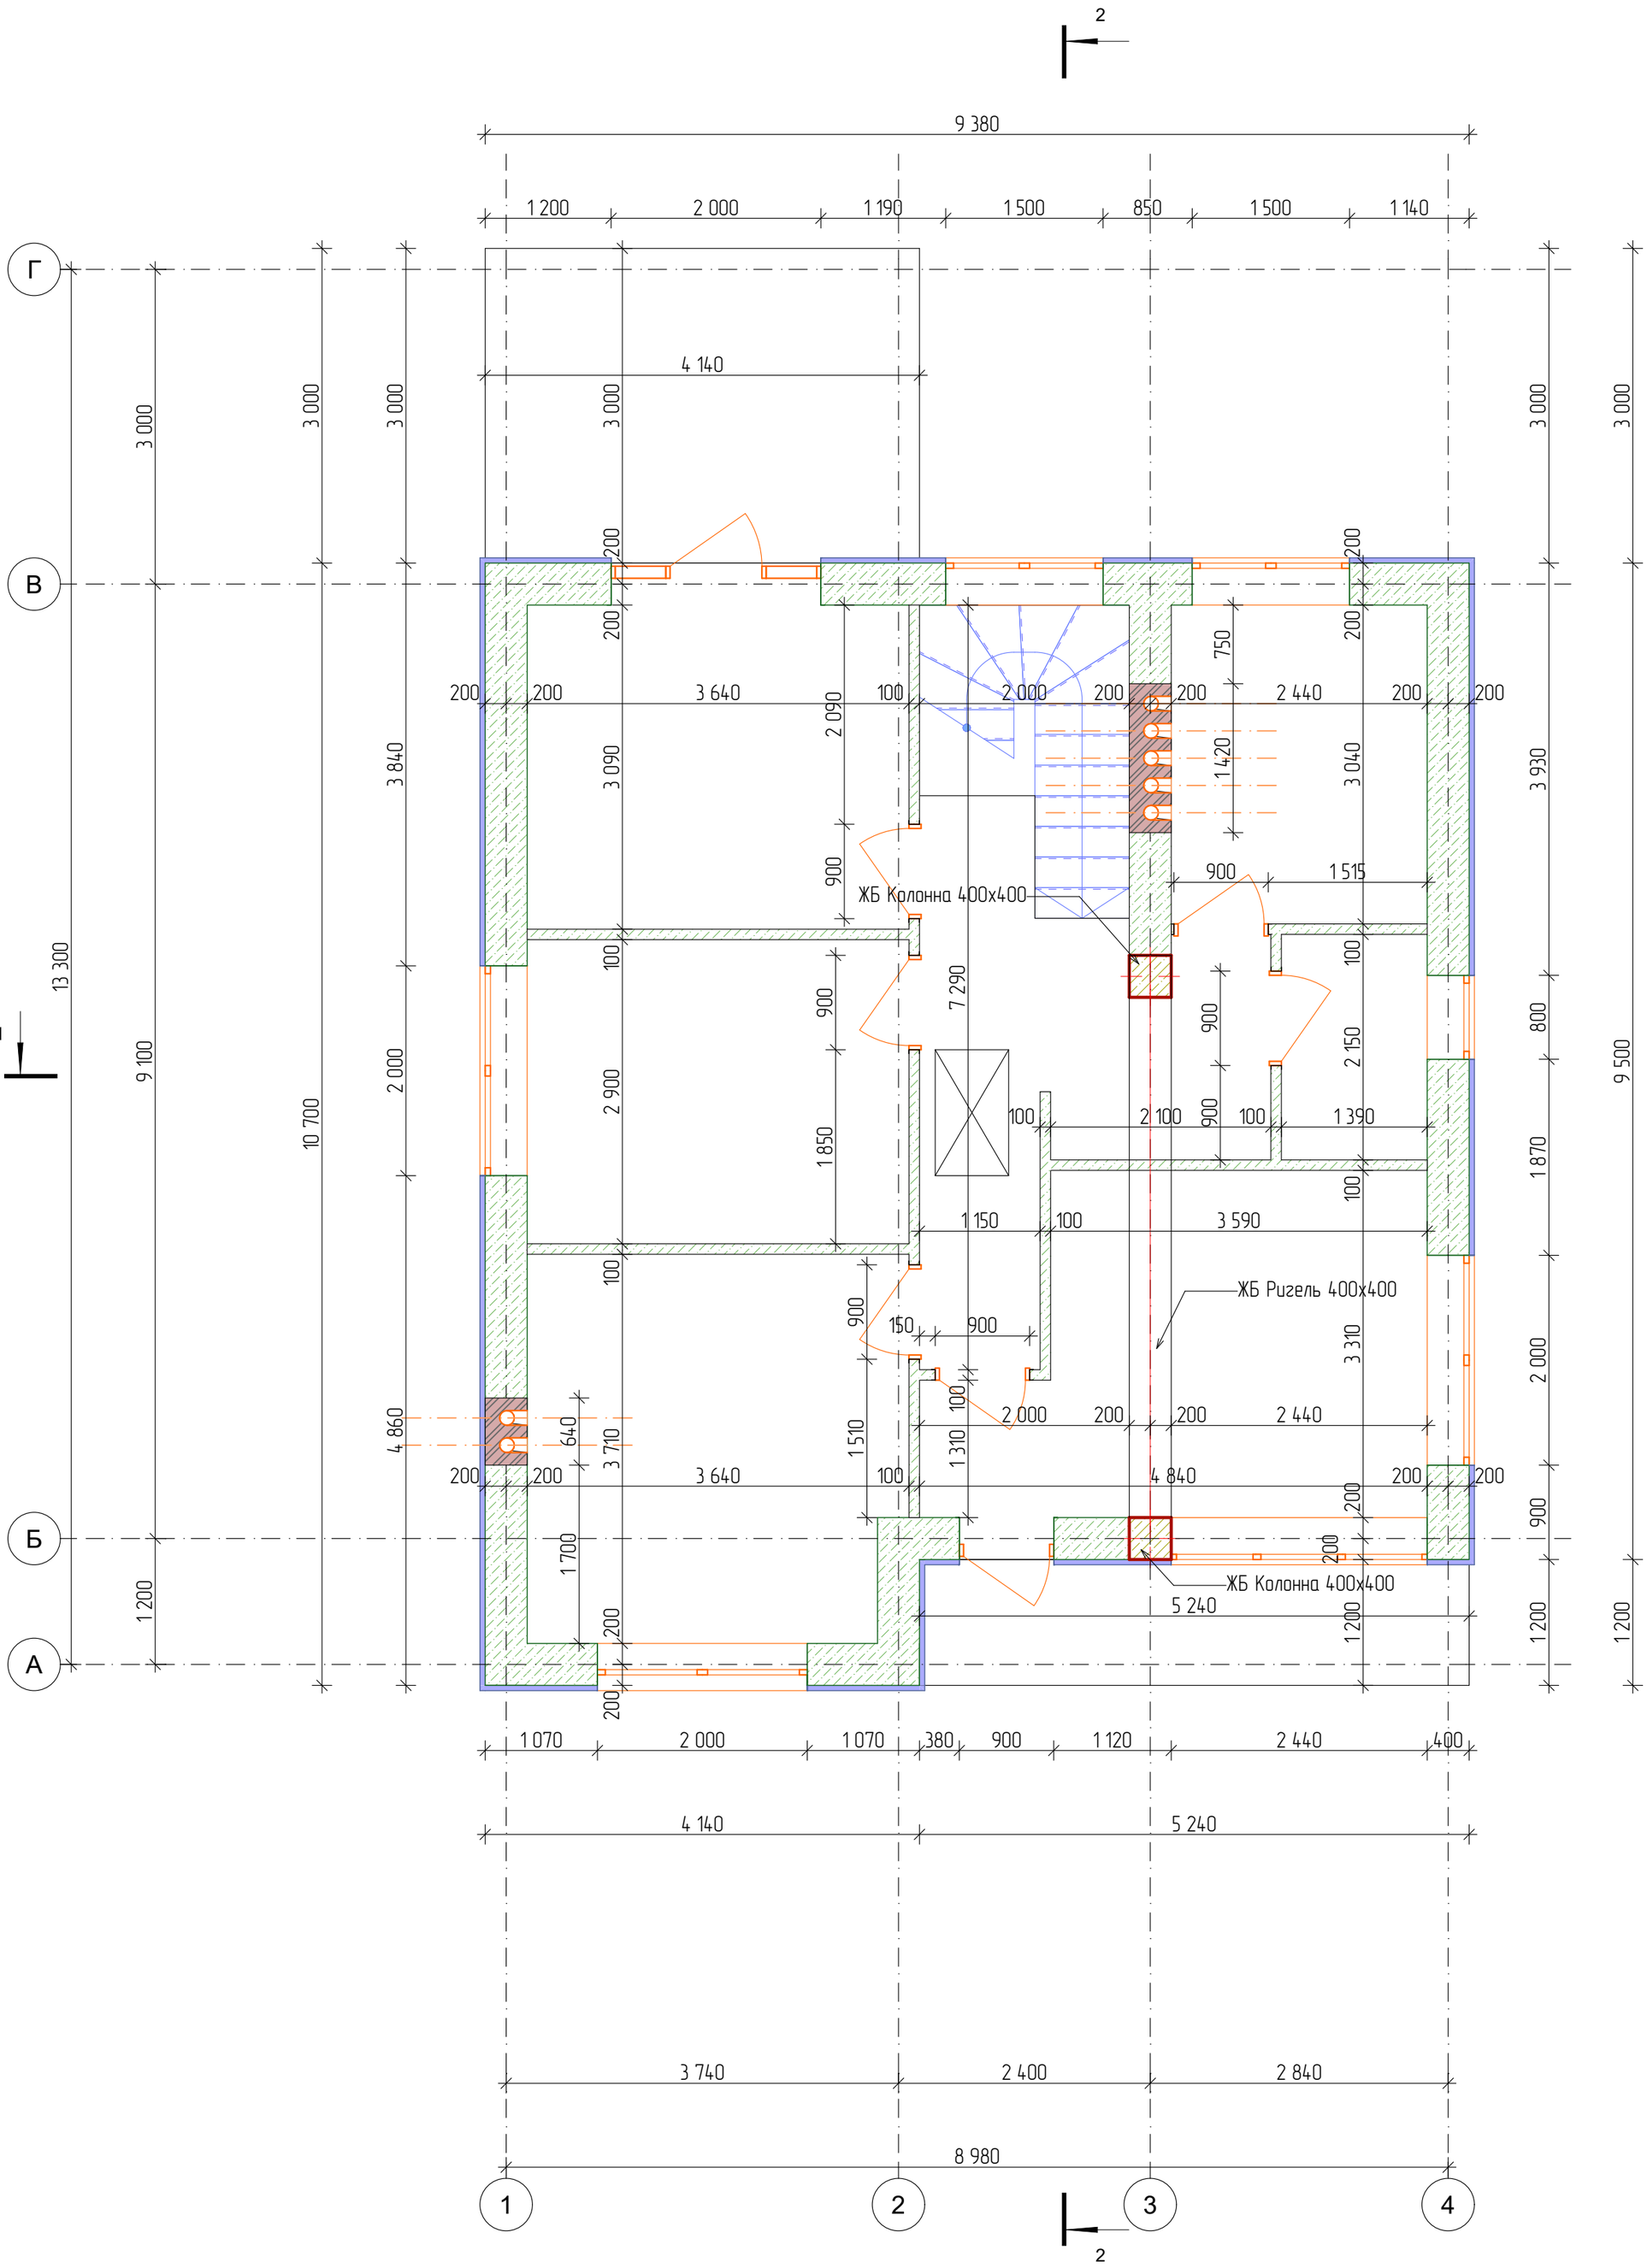
2
9 380
1 200
2 000
1 190
1 500
850
1 500
1 140
Г
В
Б
А
4 140
3 000
3 000
3 000
3 000
3 000
3 000
200
200
200
200
200
200
200
200
200
200
200
200
3 640
100
2 000
200
200
2 440
200
200
750
1 420
3 040
3 930
2 090
3 090
900
1 515
ЖБ Колонна 400х400
7 290
2 900
1 850
2 150
2 100
1 390
1 150
3 590
ЖБ Ригель 400х400
3 310
1 510
1 310
2 000
2 440
4 860
3 710
640
3 640
4 840
1 700
5 240
13 300
9 100
10 700
2 000
1 200
1 200
1 200


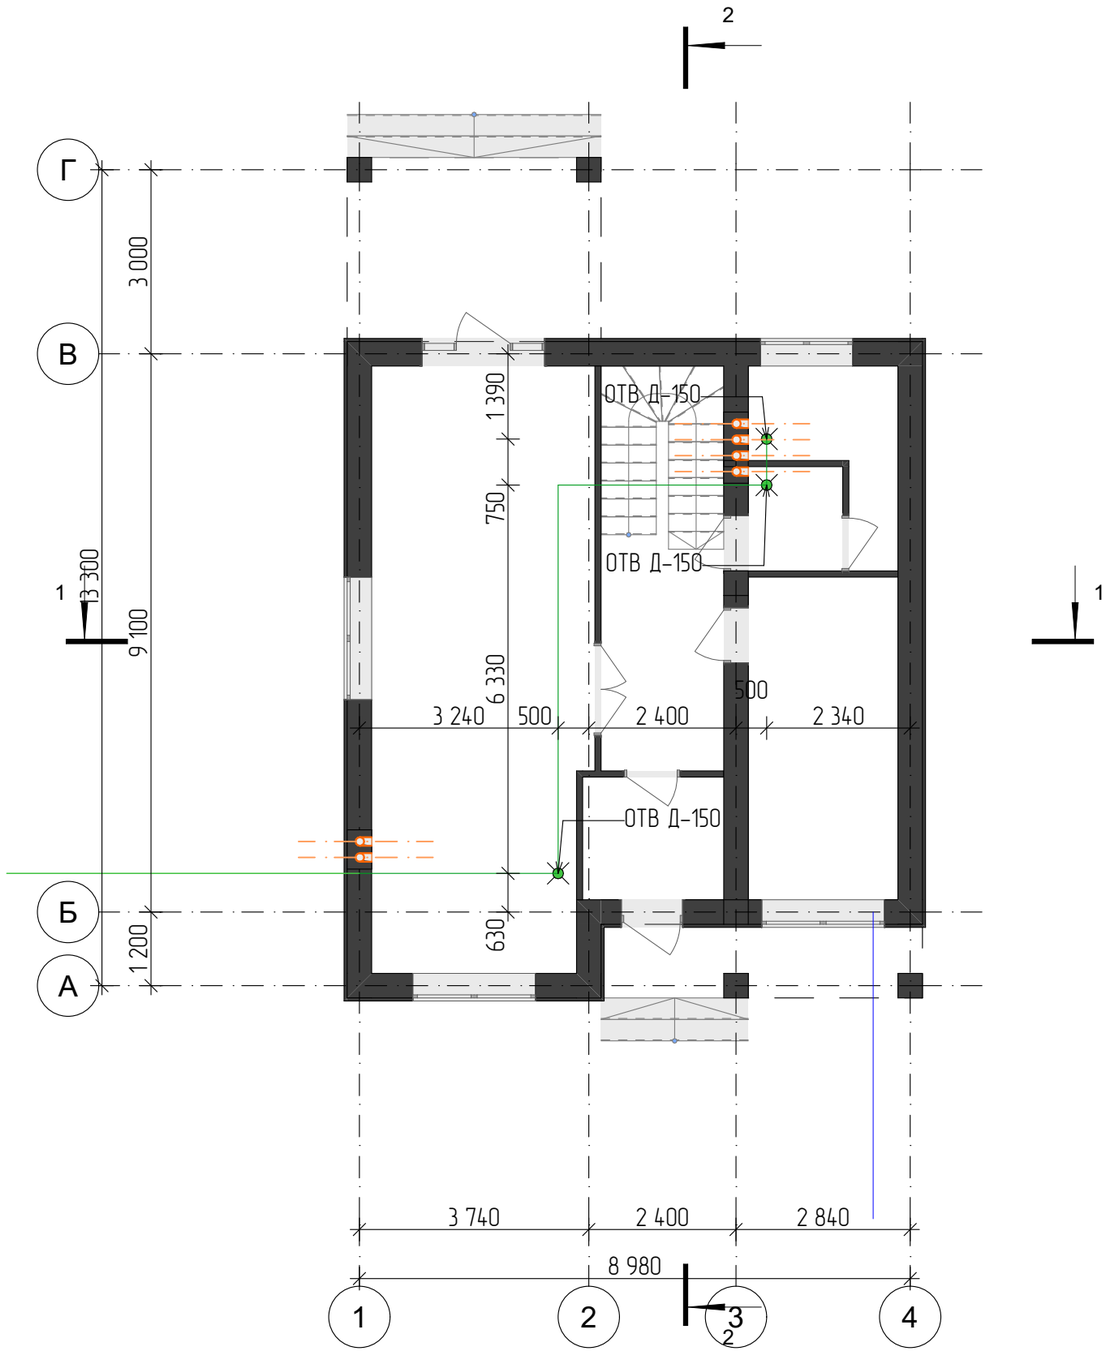


						#ID Проекта	
						кадастровый номер Россия	
Изм.	Кол.уч.	Лист	№Док.	Подп.	Дата		
Разраб.						Индивидуальный жилой дом	Стадия: #Стадия Проекта; Лист: 14; Листов:
						План коммуникаций	

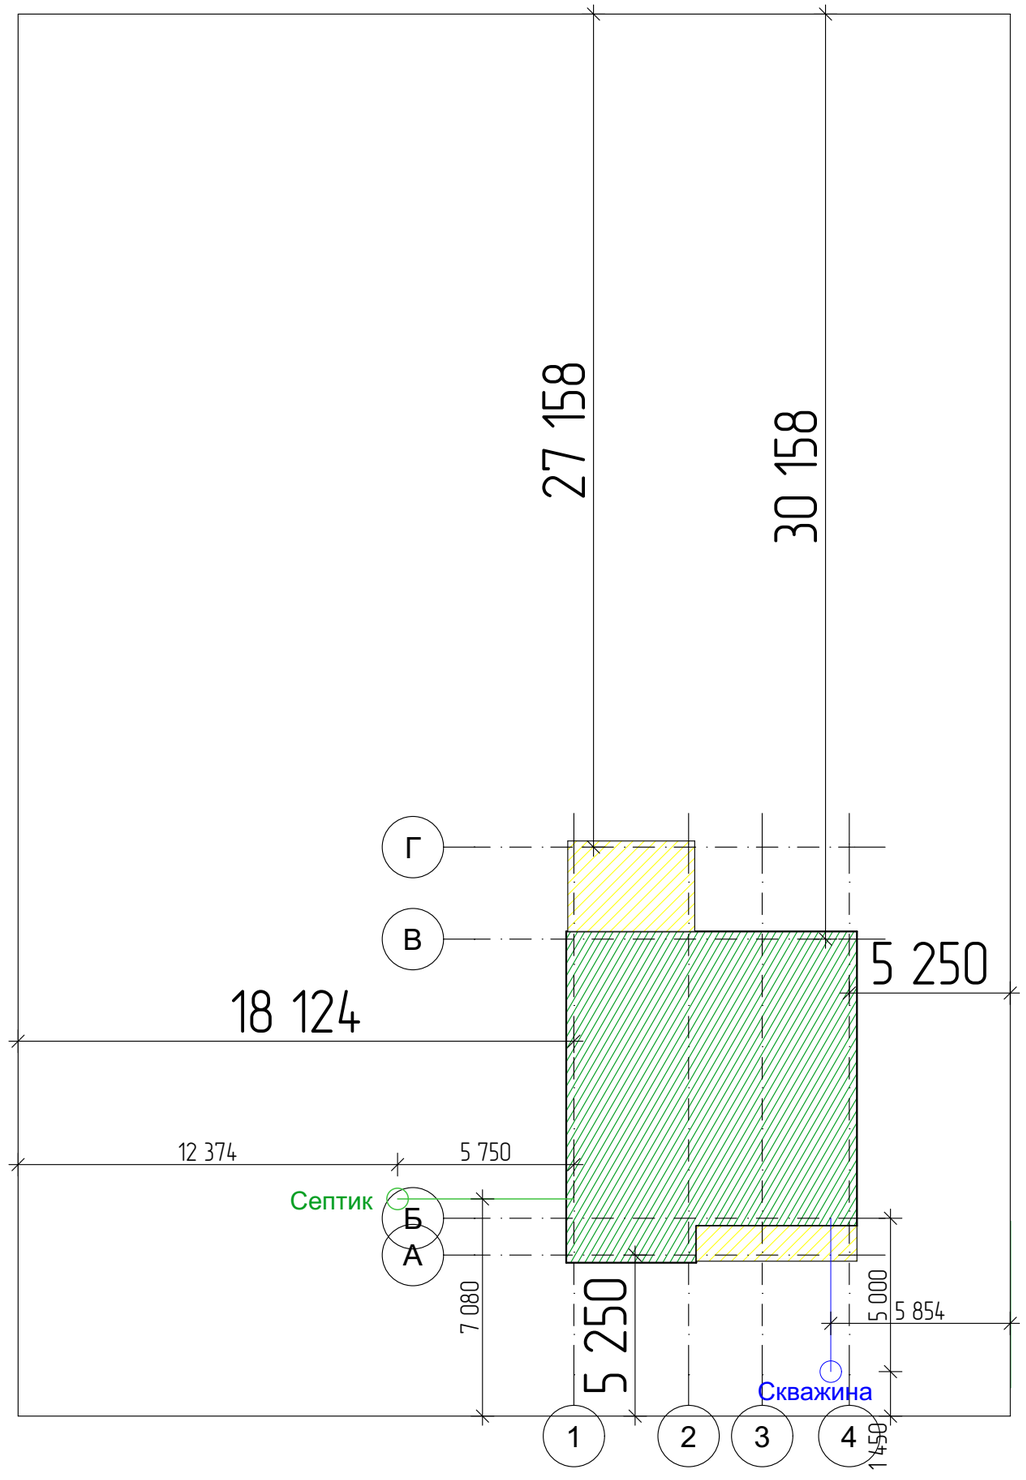







						#ID Проекта		
						кадастровый номер Россия		
Изм.	Кол.уч.	Лист	№Док.	Подп.	Дата			
Разраб.						Индивидуальный жилой дом	Стадия: #Стадия Проекта	Лист: 15 / Листов:
						Наружные сети		

Каталог Дверей

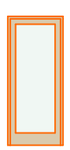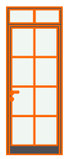
Полный ID Элемента	Д-1	Д-1	Д-1	Д-2	ДВ-1	ДВ-2	ДВ-2	ДВ-3
D по Классификации	Дверь -1	Дверь -1	Дверь -1	Дверь -2	Дверь -1	Дверь -2	Дверь -2	Дверь -3
Наименование Двери	Однопольная Дверь 27	Однопольная Дверь 27	Однопольная Дверь с Фрамугой 27	Двупольная Дверь 27	Однопольная Дверь с Фрамугой 27	Дверь с Боковыми Панелями и Фрамугой 27	Дверь с Боковыми Панелями и Фрамугой 27	Однопольная Дверь с Фрамугой 27
Количество	2	7	1	1	1	1	1	1
Размер Ш x В	900×2 100	900×2 100	900×2 400	1 500×2 100	1 000×2 400	2 000×2 400	2 000×2 400	900×2 400
Ориентация	П	Л	Л	П	Л	Л	П	Л
Высота Порога Двери	0	0	0	0	0	0	0	0
Высота Перемычки Двери	2 100	2 100	2 400	2 100	2 400	2 400	2 400	2 400
2D-символ								
Вид со Стороны, Противоположной Стороне Открывания								

Изм.	Кол.уч.	Лист	№Док.	Подп.	Дата	#ID Проекта		
						кадастровый номер Россия		
Разраб.						Индивидуальный жилой дом	Стадия: #Стадия Проекта	Лист: 16 / Листов:
						Каталог дверных проемов		


Каталог Окон

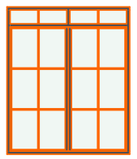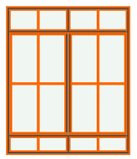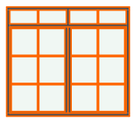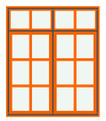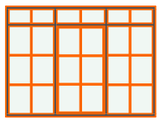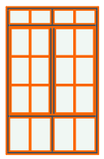Полный ID Элемента	ОК-1	ОК-1	ОК-2	ОК-3	ОК-4	ОК-5	ОК-6	ОК-125
Наименование Окна	Раздвижное Двустворчатое Окно 27	Раздвижное Двустворчатое Окно 27	Раздвижное Двустворчатое Окно 27	Двустворчатое Окно 27	Трехстворчатое Окно 27	Окно 27	Раздвижное Двустворчатое Окно 27	Окно 27
Количество	1	1	4	2	1	1	1	1
Размер Ш x В	2 000×2 400	2 000×2 400	2 000×1 780	1 500×1 780	2 440×1 800	800×1 780	1 500×2 400	180×500
Ориентация	П	П	П			Л	Л	
Высота Подоконника Окна	0	100	620	620	600	620	0	3 400
Высота Перемычки Окна	2 400	2 500	2 400	2 400	2 400	2 400	2 400	3 900
2D-символ								
Вид со Стороны, Противоположной Стороне Открывания								


Изм.	Кол.уч.	Лист	№Док.	Подп.	Дата	#ID Проекта			
						кадастровый номер Россия			
Разраб.						Индивидуальный жилой дом	Стадия	Лист	Листов
							#Стадия Проекта	17	
						Каталог оконных проемов			

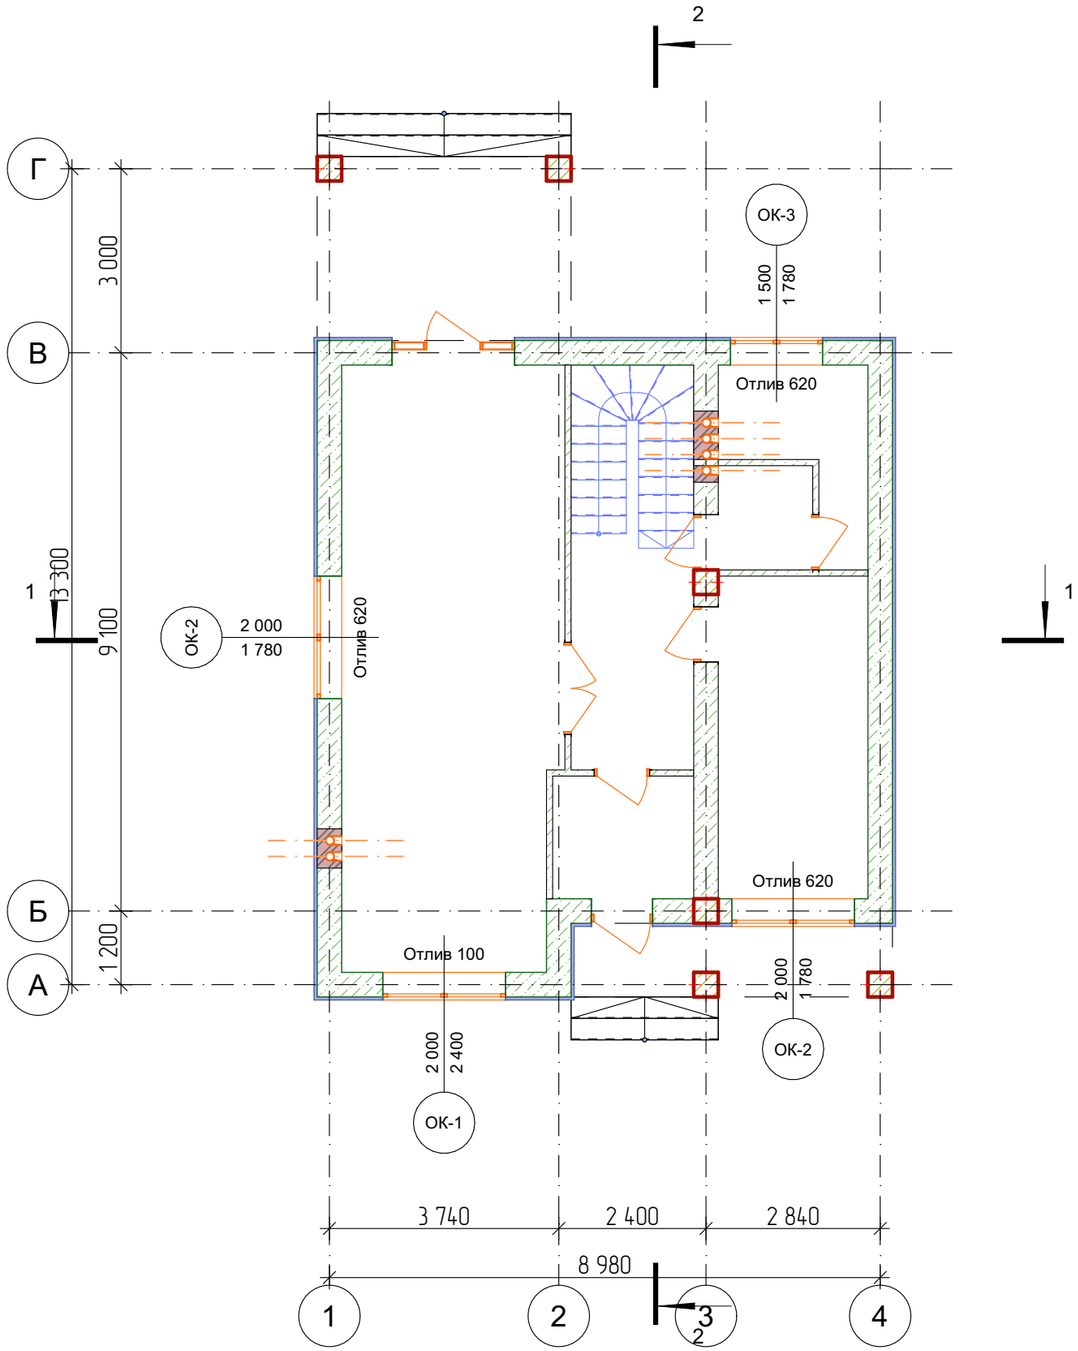


						#ID Проекта	
						кадастровый номер Россия	
Изм.	Кол.уч.	Лист	№Док.	Подп.	Дата		
Разраб.						Индивидуальный жилой дом	Стадия: #Стадия Проекта; Лист: 18; Листов:
						Маркировка оконных проемов первого этажа	

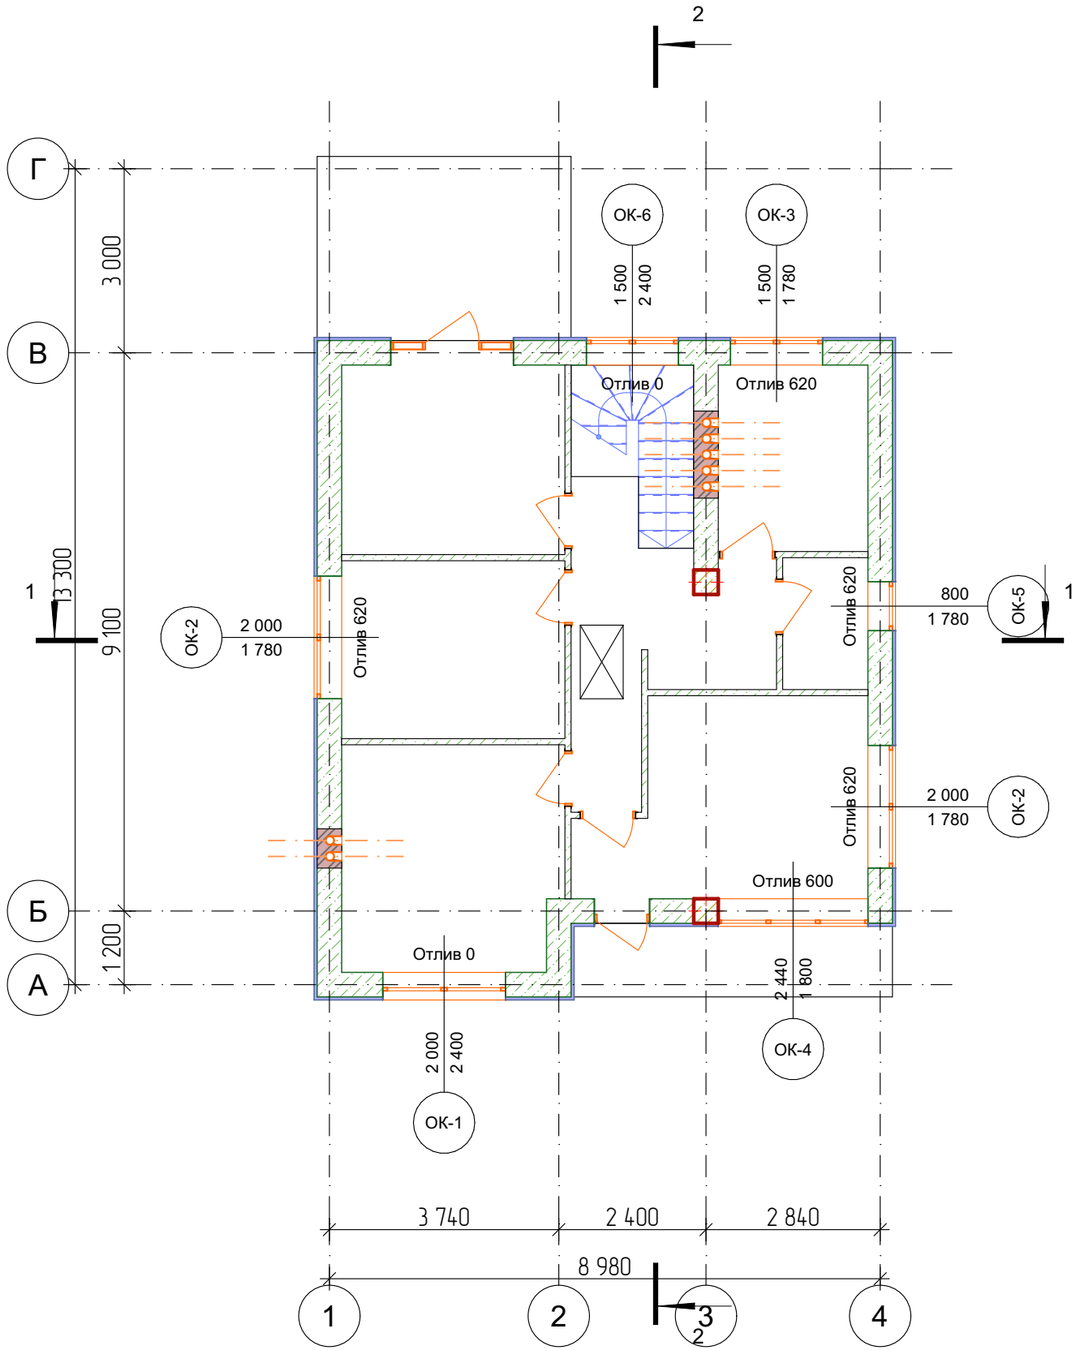


						#ID Проекта		
						кадастровый номер Россия		
Изм.	Кол.уч.	Лист	№Док.	Подп.	Дата			
Разраб.						Индивидуальный жилой дом	Стадия	Лист	Листов
							#Стадия Проекта	19	
						Маркировка оконных проемов второго этажа			

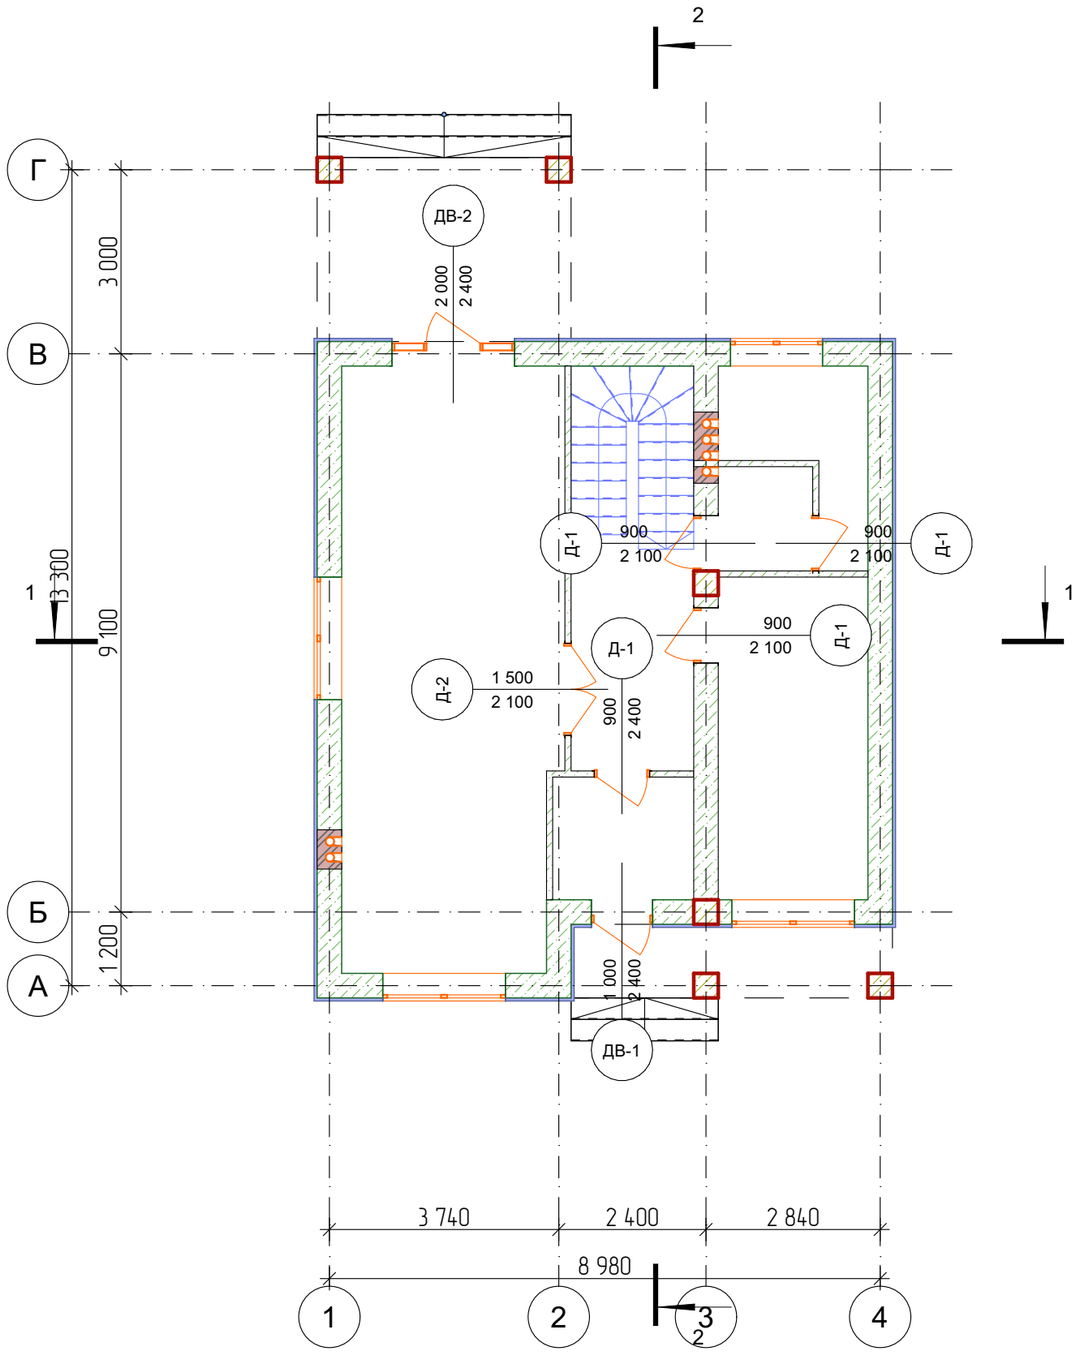


						#ID Проекта	
						кадастровый номер Россия	
Изм.	Кол.уч.	Лист	№Док.	Подп.	Дата		
Разраб.						Индивидуальный жилой дом	Стадия: #Стадия Проекта; Лист: 20; Листов:
						Маркировка дверных проемов первого этажа	

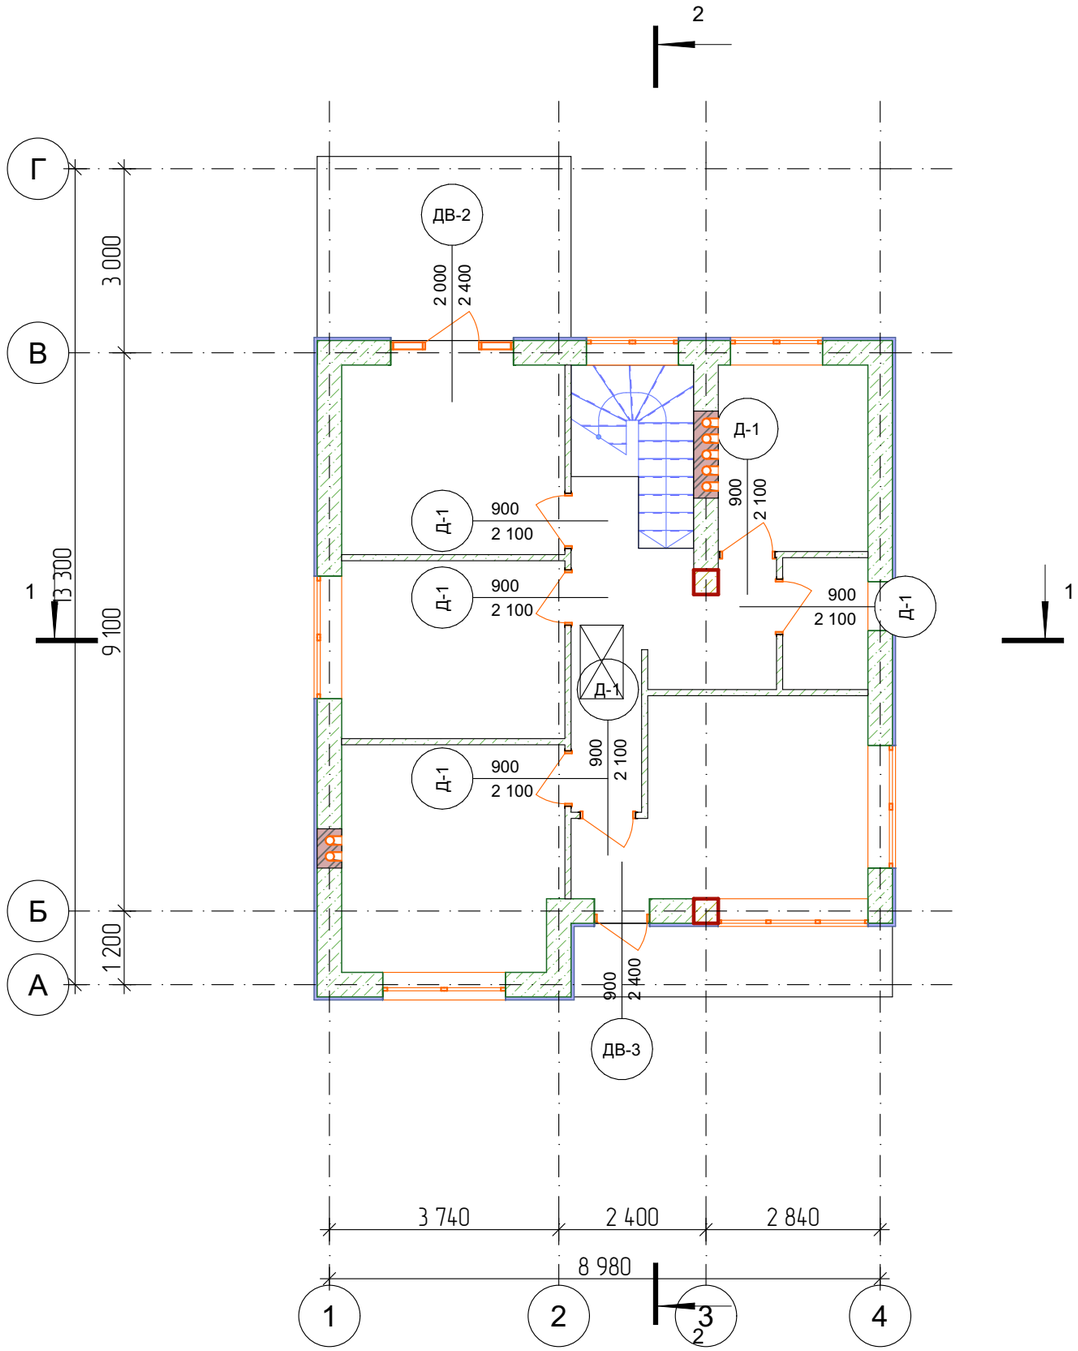


						#ID Проекта	
						кадастровый номер Россия	
Изм.	Кол.уч.	Лист	№Док.	Подп.	Дата		
Разраб.						Индивидуальный жилой дом	Стадия: #Стадия Проекта; Лист: 21; Листов:
						Маркировка дверных проемов второго этажа	

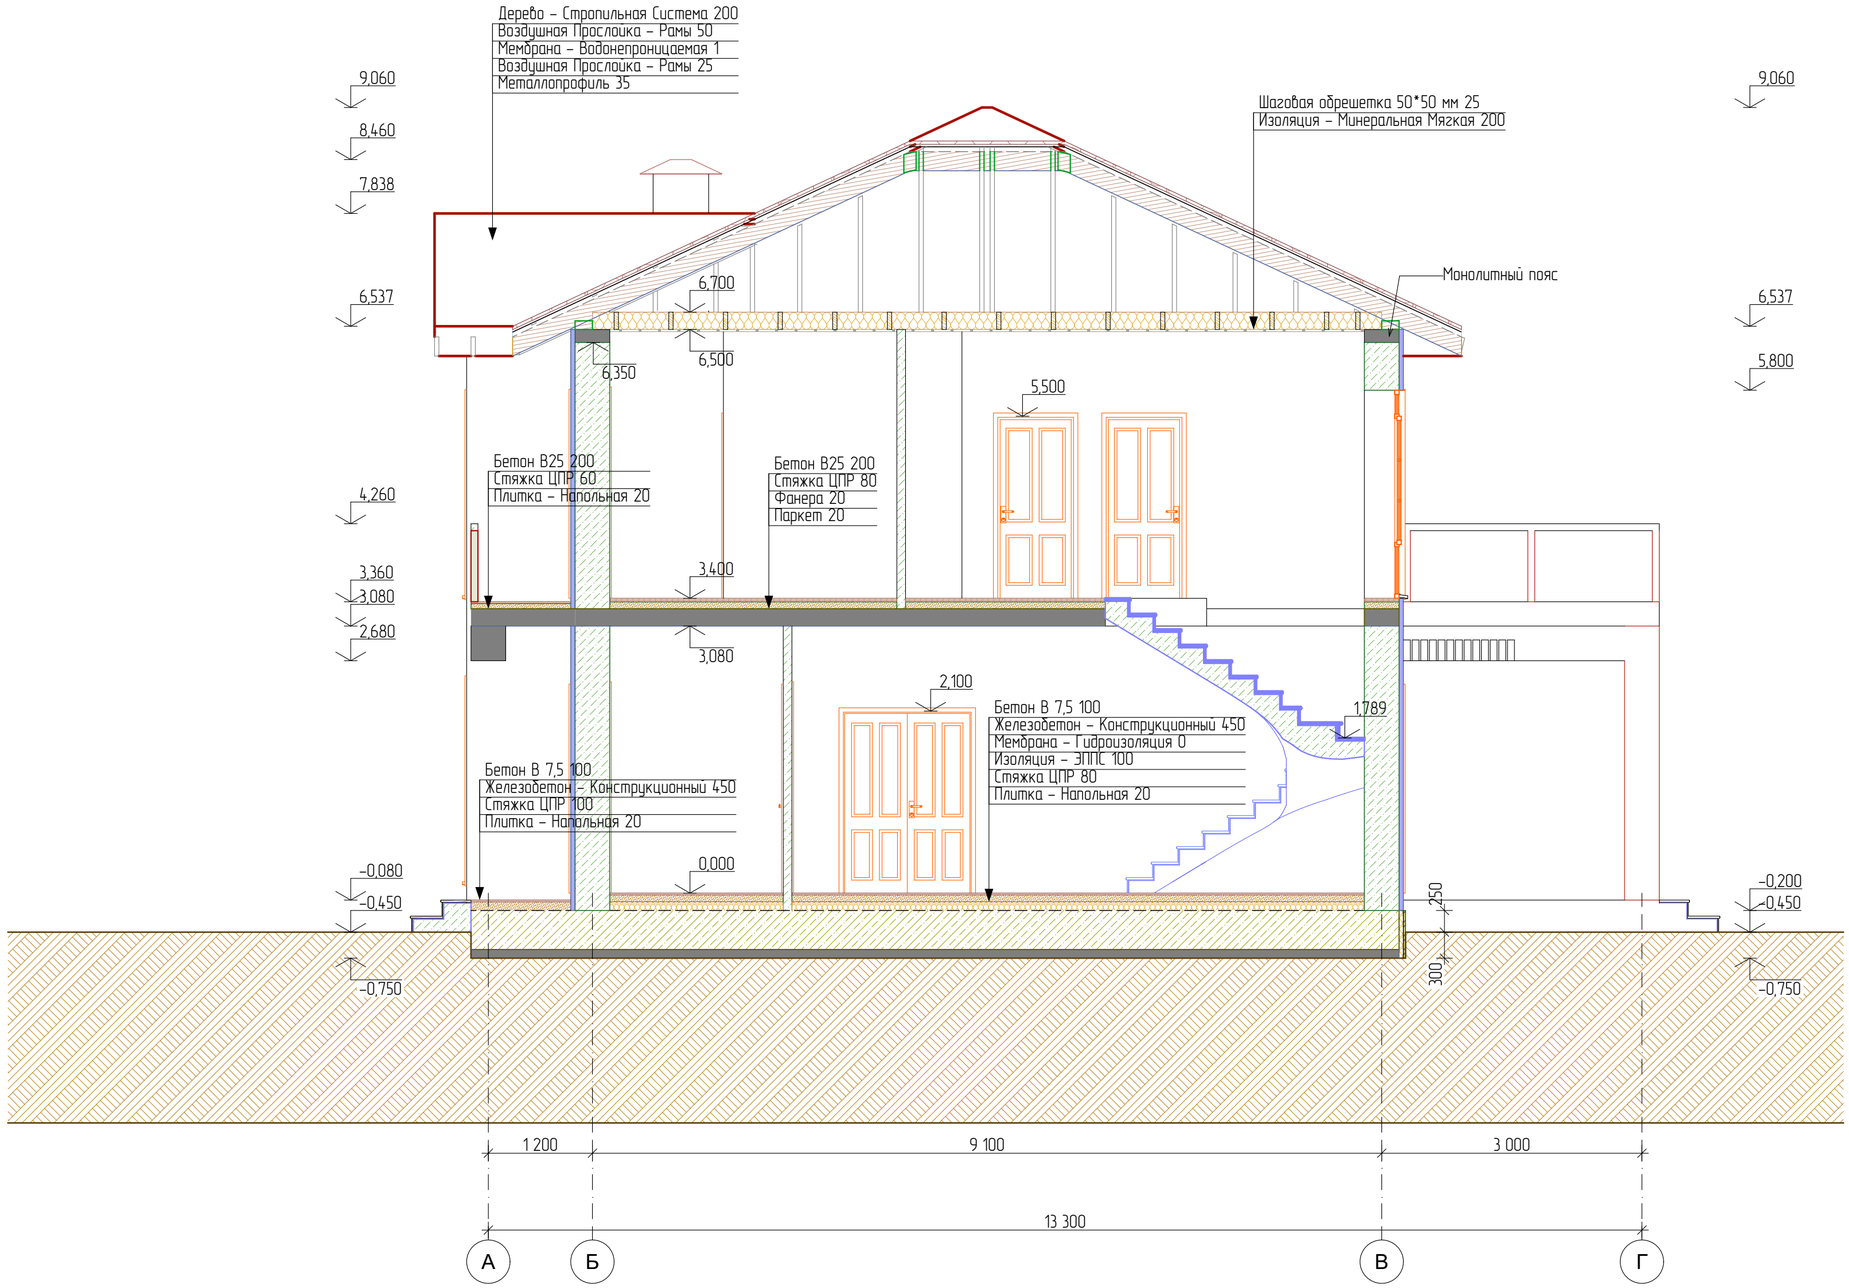

						#ID Проекта	
						кадастровый номер Россия	
Изм.	Кол.уч.	Лист	№Док.	Подп.	Дата		
Разраб.						Индивидуальный жилой дом	Стадия: #Стадия Проекта; Лист: 22; Листов:
						Разрез 1 - 1	

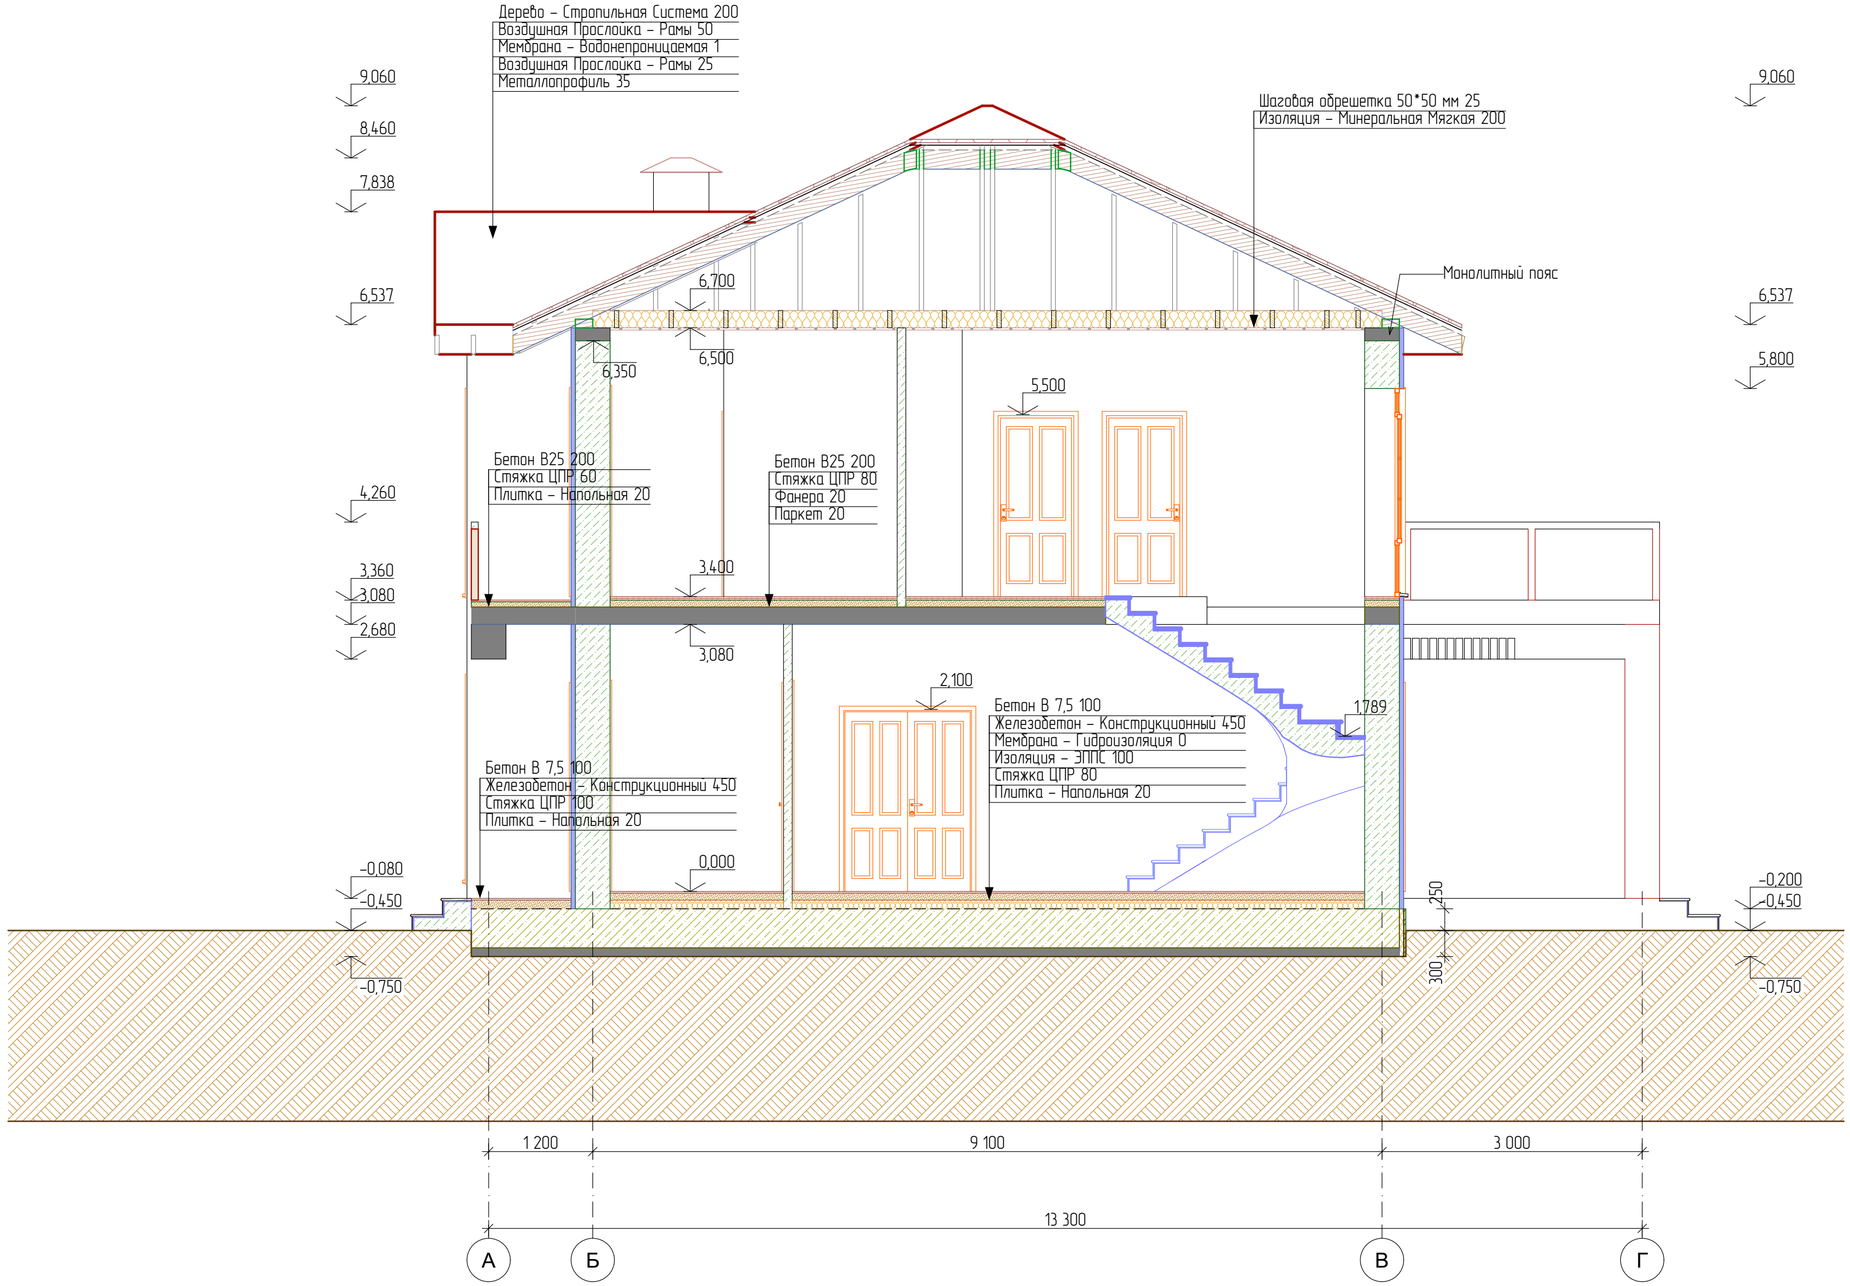


						#ID Проекта	
						кадастровый номер Россия	
Изм.	Кол.уч.	Лист	№Док.	Подп.	Дата		
Разраб.						Индивидуальный жилой дом	Стадия: #Стадия Проекта; Лист: 23; Листов:
						Разрез 2 - 2	

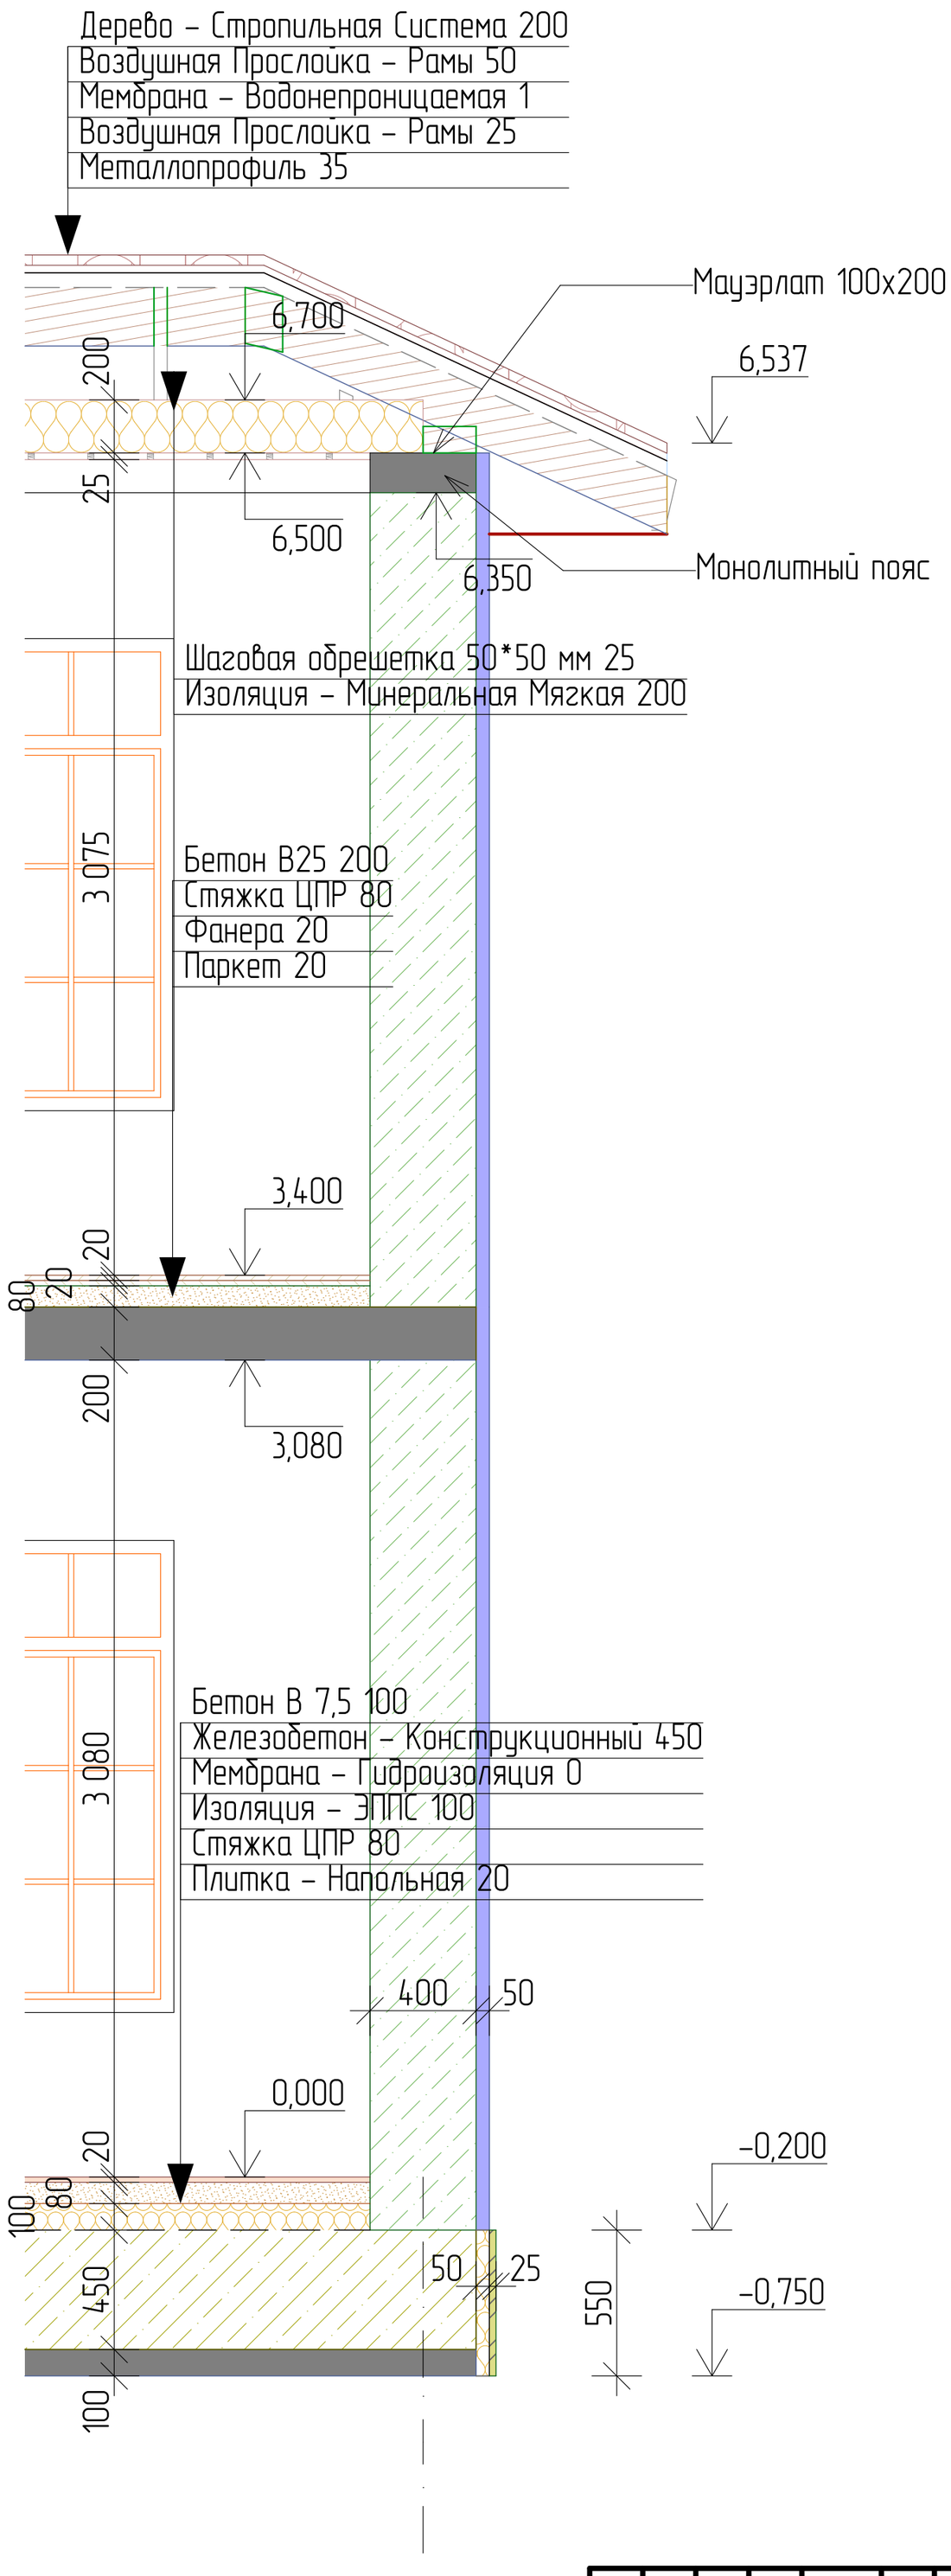


						#ID Проекта	
						кадастровый номер Россия	
Изм.	Кол.уч.	Лист	№Док.	Подп.	Дата		
Разраб.						Индивидуальный жилой дом	Стадия: #Стадия Проекта; Лист: 24; Листов:
						Разрез по стене	


ИКК-05 Монолитные участки	
Наименование	Объем
Перекрытие	22,56

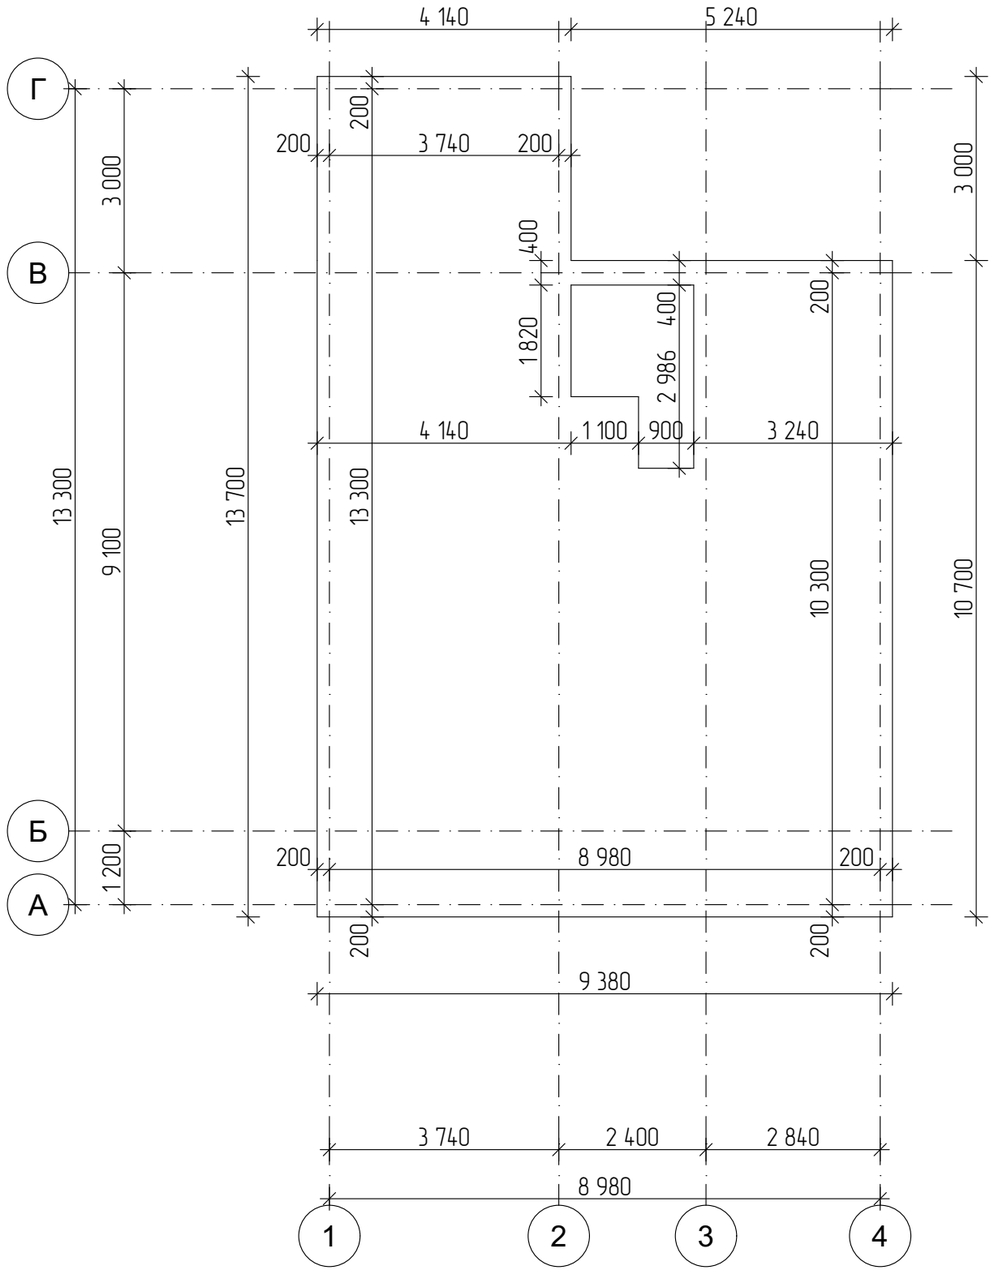

						#ID Проекта
						кадастровый номер Россия
Изм.	Кол.уч.	Лист	№Док.	Подп.	Дата	
Разраб.						Индивидуальный жилой дом
						План перекрытия на отм. +3,400


Стадия	Лист	Листов
#Стадия Проекта	25	

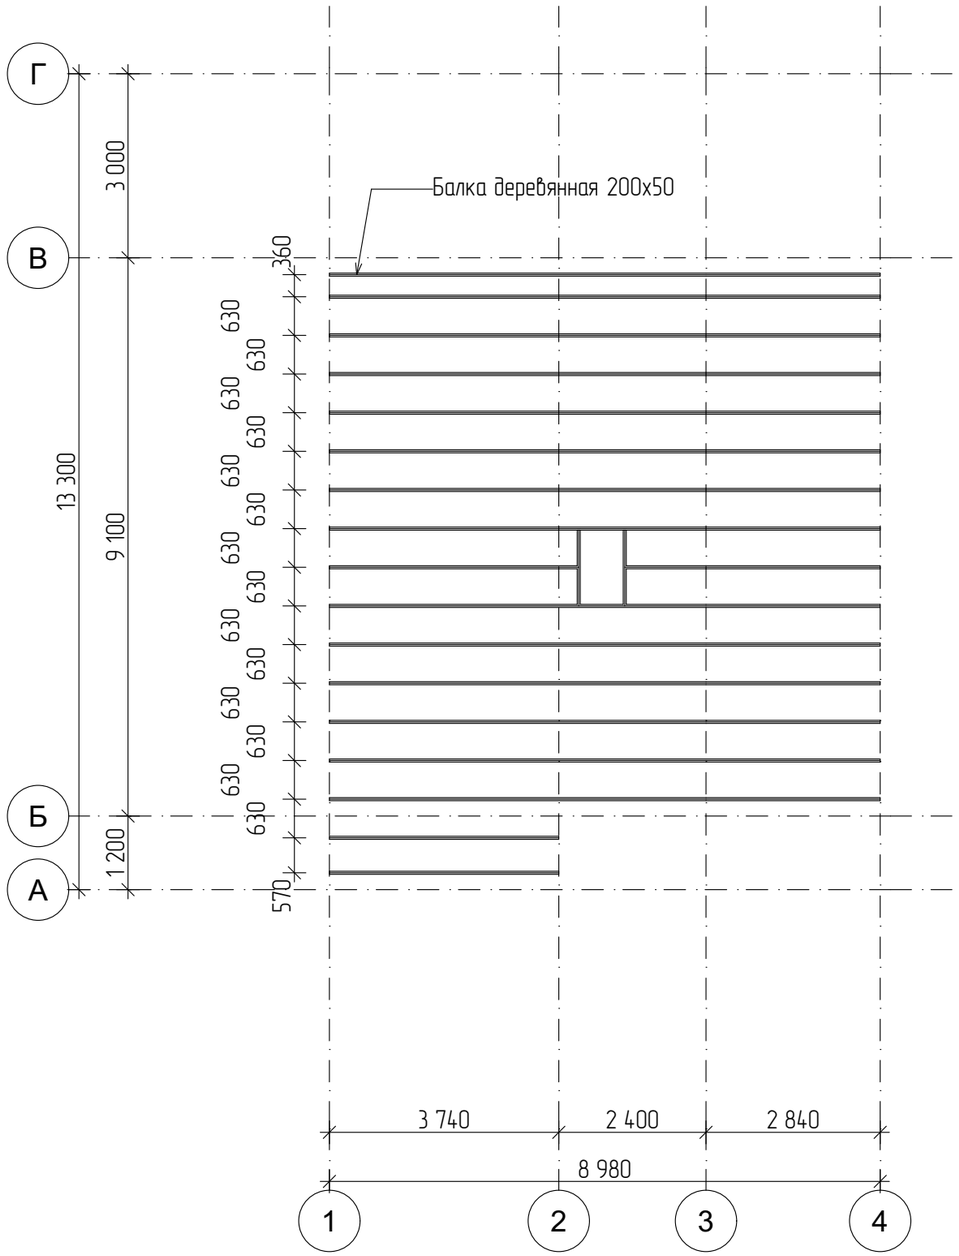


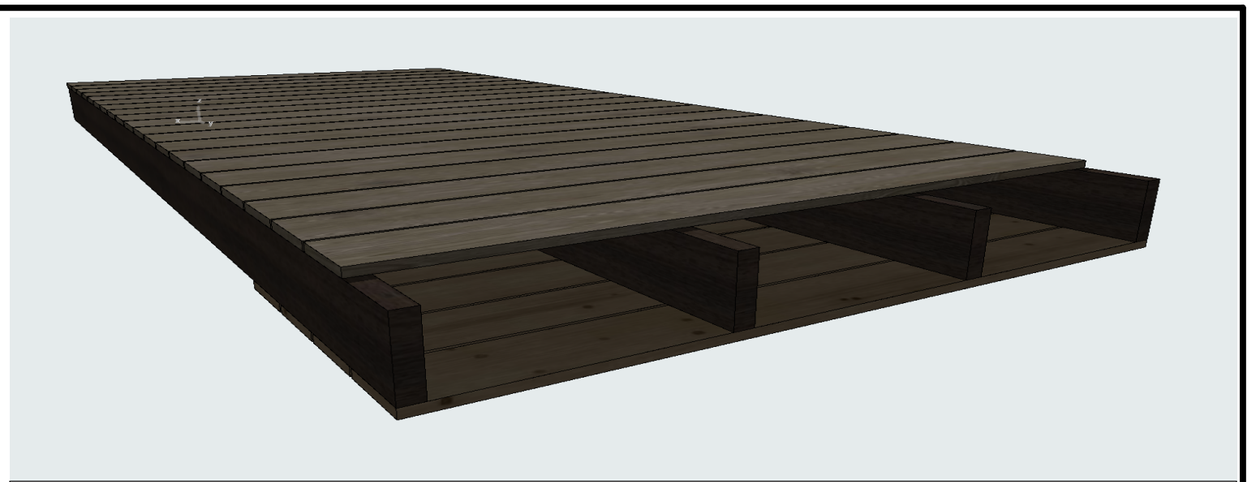


Ведомость перекрытия			
Наименование	Количество	Длина, мм	Объем, м3
Балка деревянная 200х50	1	1 300	0,01
Балка деревянная 200х50	1	4 040	0,04
Балка деревянная 200х50	2	1 210	0,02
Балка деревянная 200х50	2	3 740	0,08
Балка деревянная 200х50	14	6 140	0,84
Балка деревянная 200х50	15	2 840	0,45
	35		**1,44 м³**

Изм.	Кол.уч.	Лист	№Док.	Подп.	Дата	#ID Проекта		
						кадастровый номер Россия		
Разраб.						Индивидуальный жилой дом	Стадия: #Стадия Проекта	Лист: 26 / Листов:
						План перекрытия на отм. +6,700		

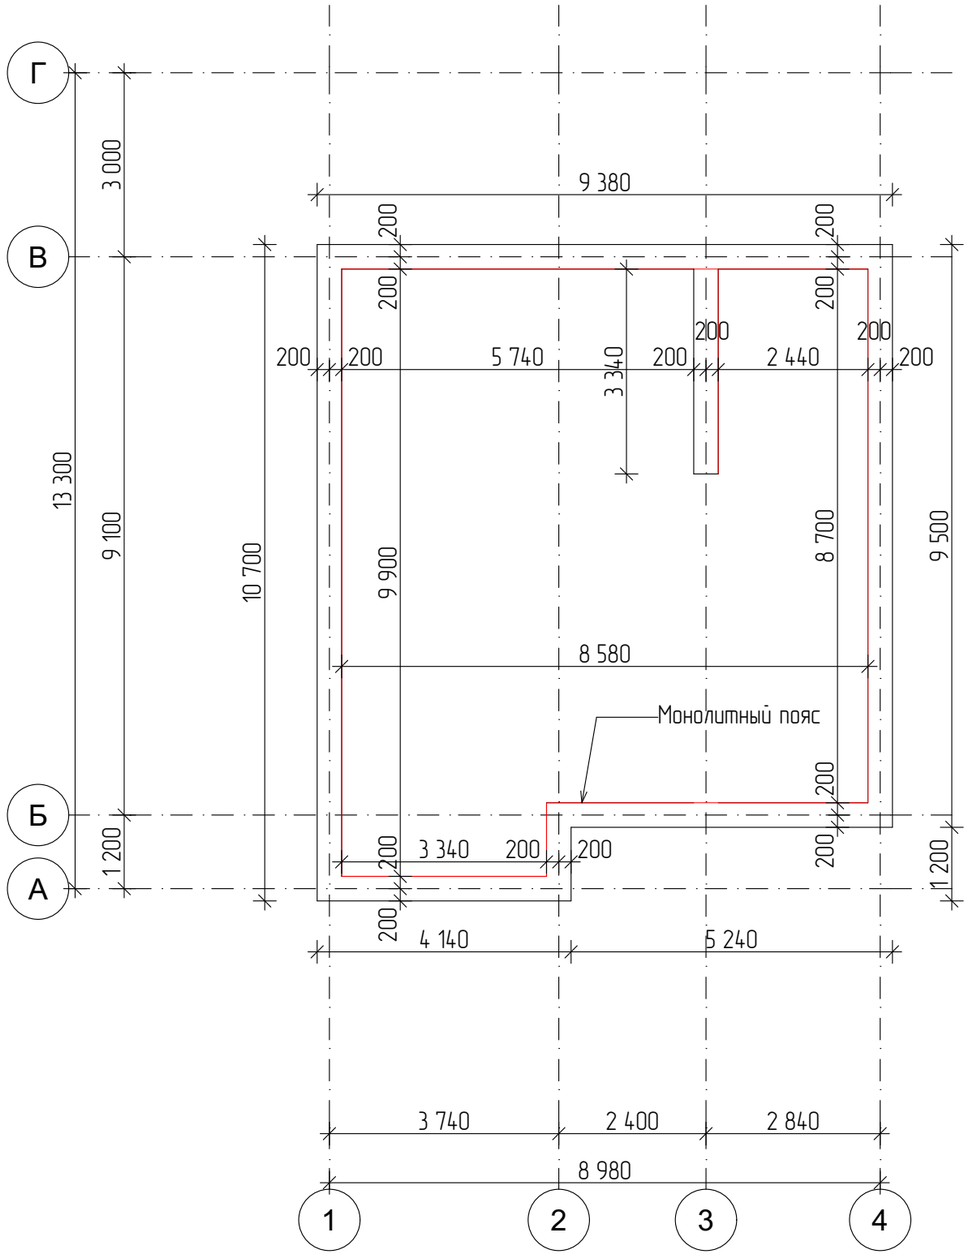

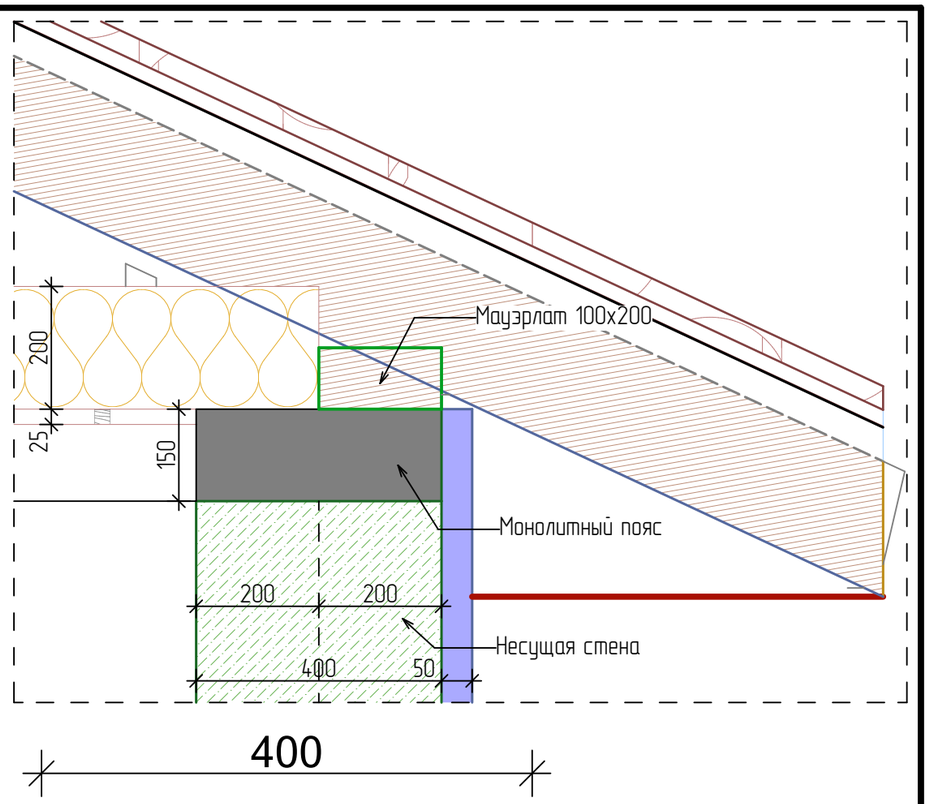

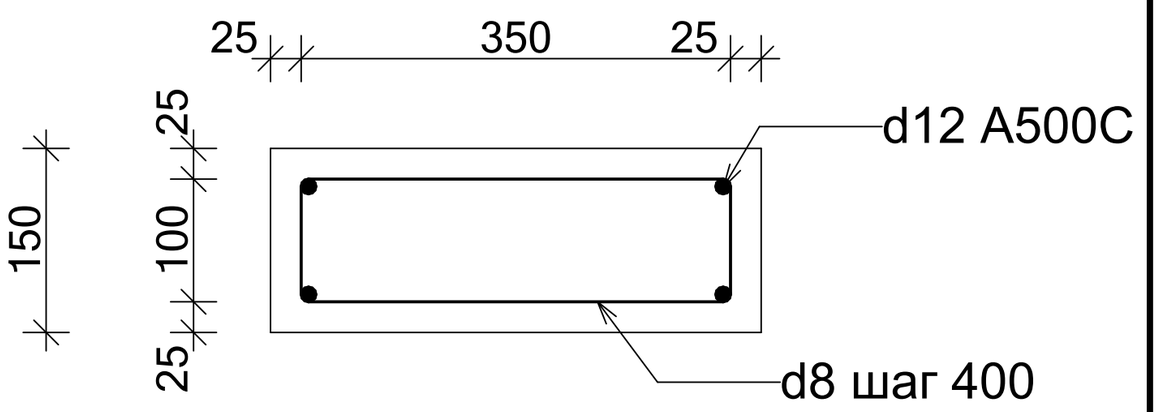



ВЕДОМОСТЬ НА МОНОЛИТНЫЙ ПОЯС 2-ГО ЭТАЖА

Наименование	Объем, м3
	2,51
Монолитный пояс	2,51

1. Монолитный пояс расположен согласно отметкам
2. Армирование выполнить используя арматуру С500 d12 в виде пространственного каркаса из 4-х стержней
3. Нахлест арматуры 420 мм
4. Бетон класса В20
5. Конструктивная арматура d8 мм с шагом 400 мм, гладкая

Изм.	Кол.уч.	Лист	№Док.	Подп.	Дата	#ID Проекта		
						кадастровый номер Россия		
Разраб.						Индивидуальный жилой дом	Стадия: #Стадия Проекта	Лист: 27 / Листов:
						Монолитный пояс на отм. +6,350		

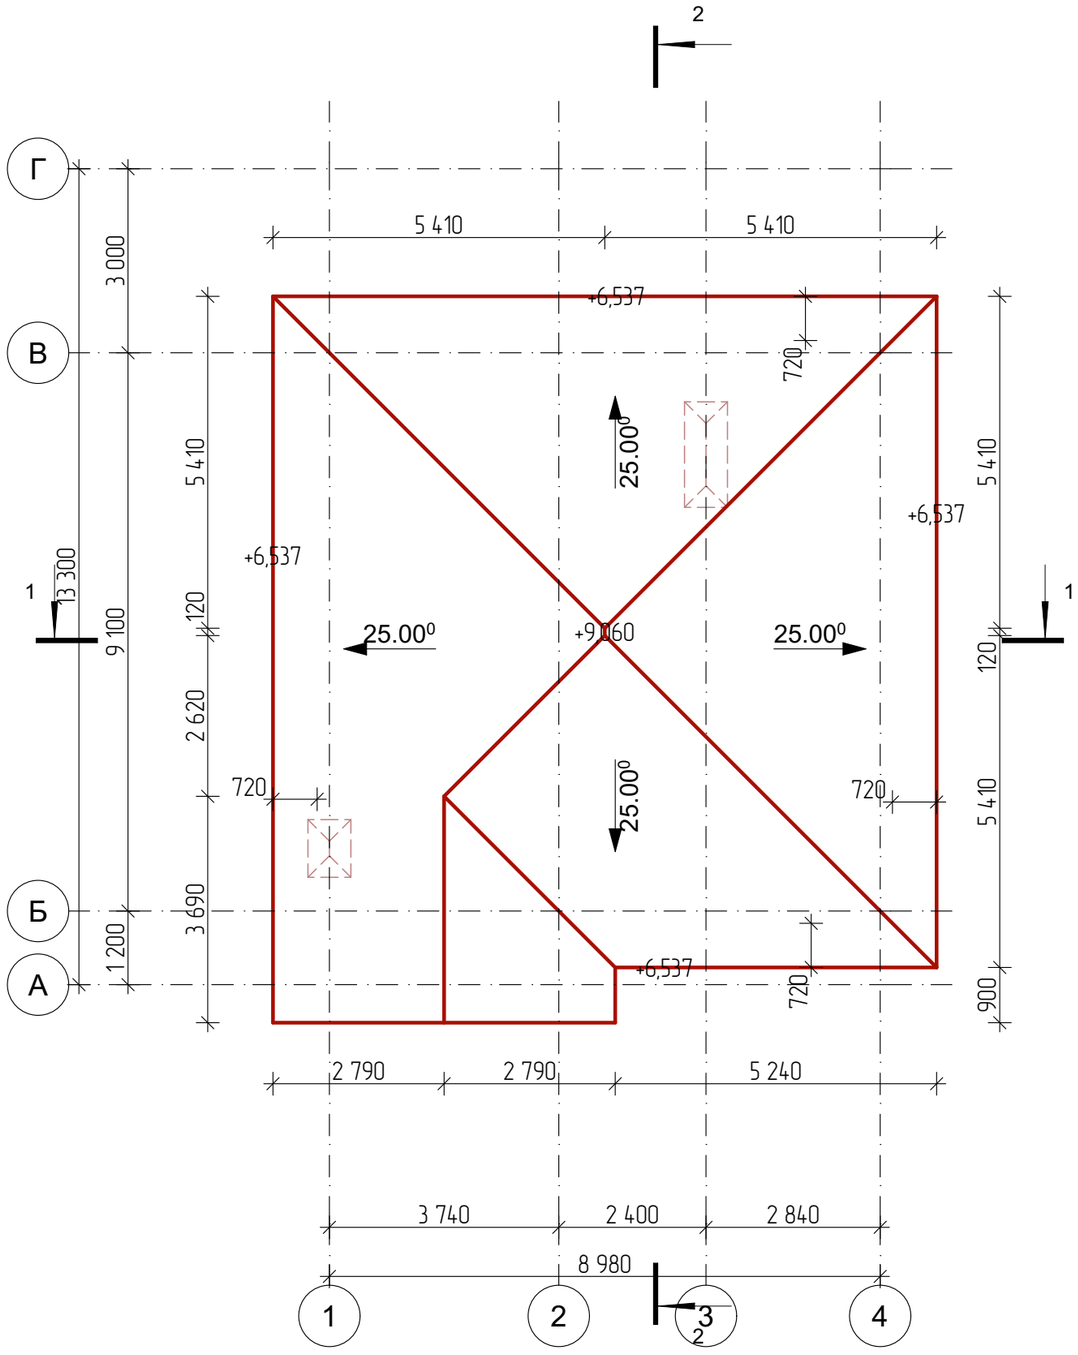


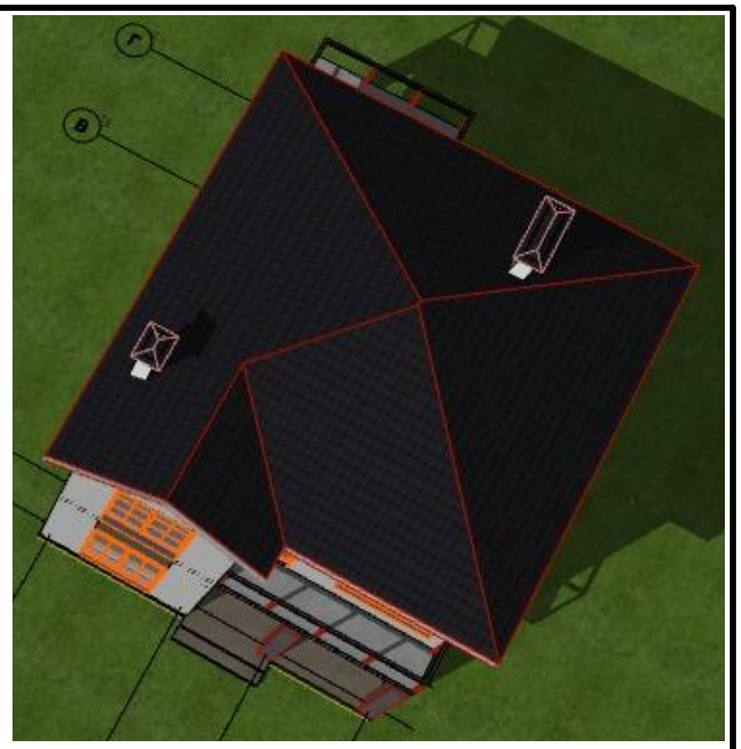

ВЕДОМОСТЬ КРОВЕЛЬНОГО МАТЕРИАЛА

Наименование	Площадь, м2
Кровля дома	138,23


						#ID Проекта		
						кадастровый номер Россия		
Изм.	Кол.уч.	Лист	№Док.	Подп.	Дата			
Разраб.						Индивидуальный жилой дом	Стадия: #Стадия Проекта	Лист: 28 / Листов:
						План кровли		

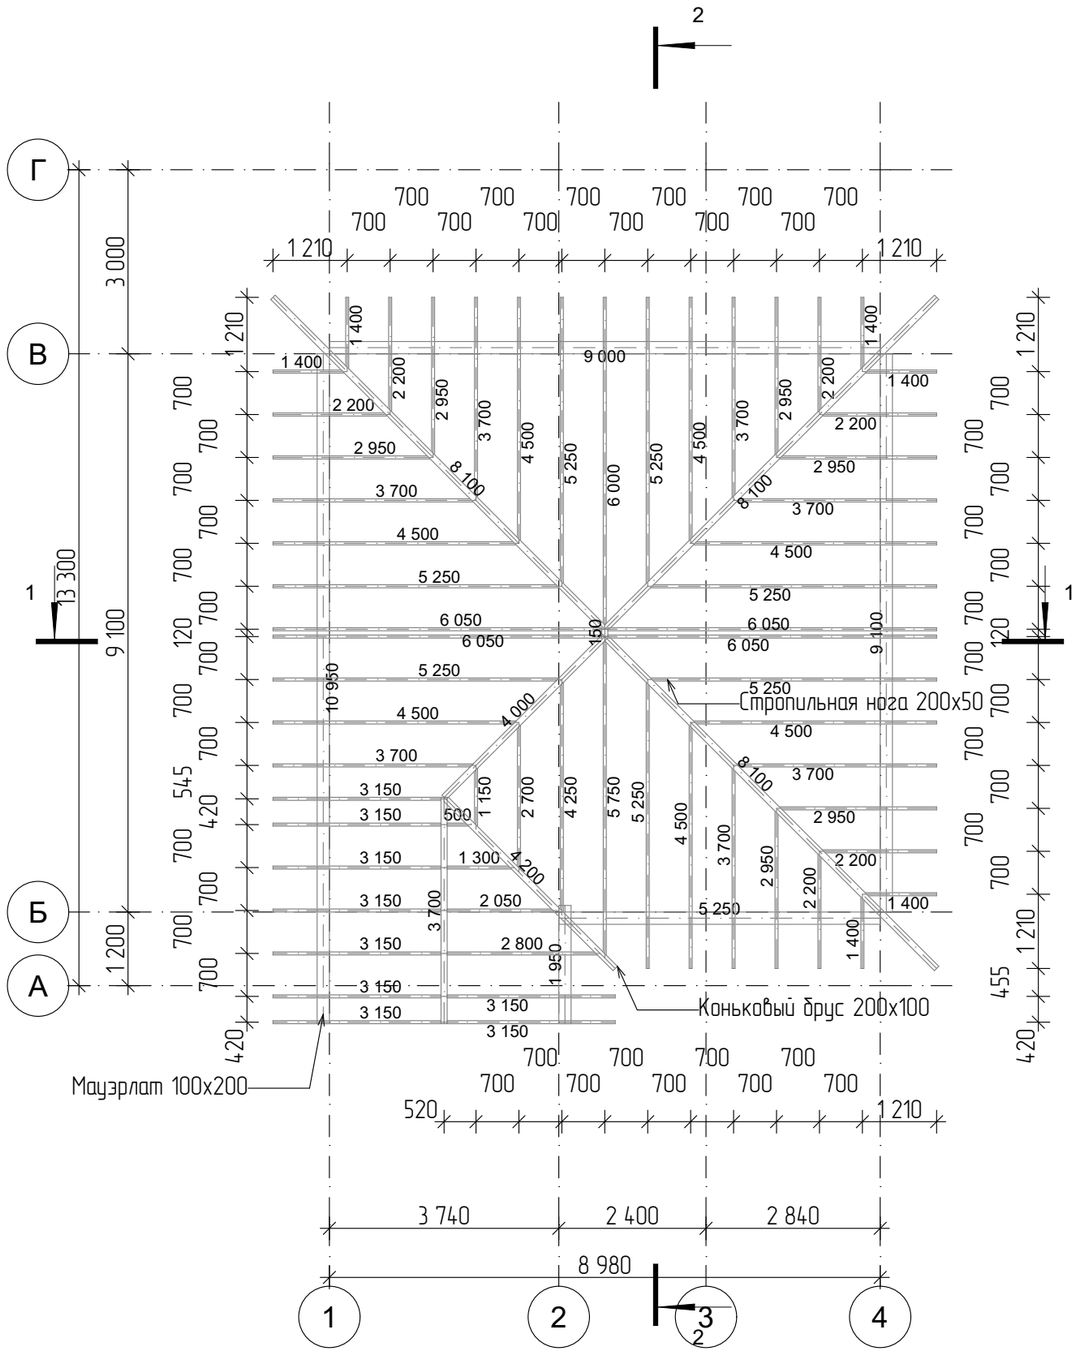


ВЕДОМОСТЬ СТРОПИЛЬНОЙ СИСИТЕМЫ

Наименование	Объем, м3
Коньковый брус 200х100	0,71
Мауэрлат 100х200	0,72
Стропильная нога 200х50	2,04


Изм.	Кол.уч.	Лист	№Док.	Подп.	Дата	#ID Проекта			
						кадастровый номер Россия			
Разраб.						Индивидуальный жилой дом	Стадия	Лист	Листов
							#Стадия Проекта	29	
						Схема расположения стропил			

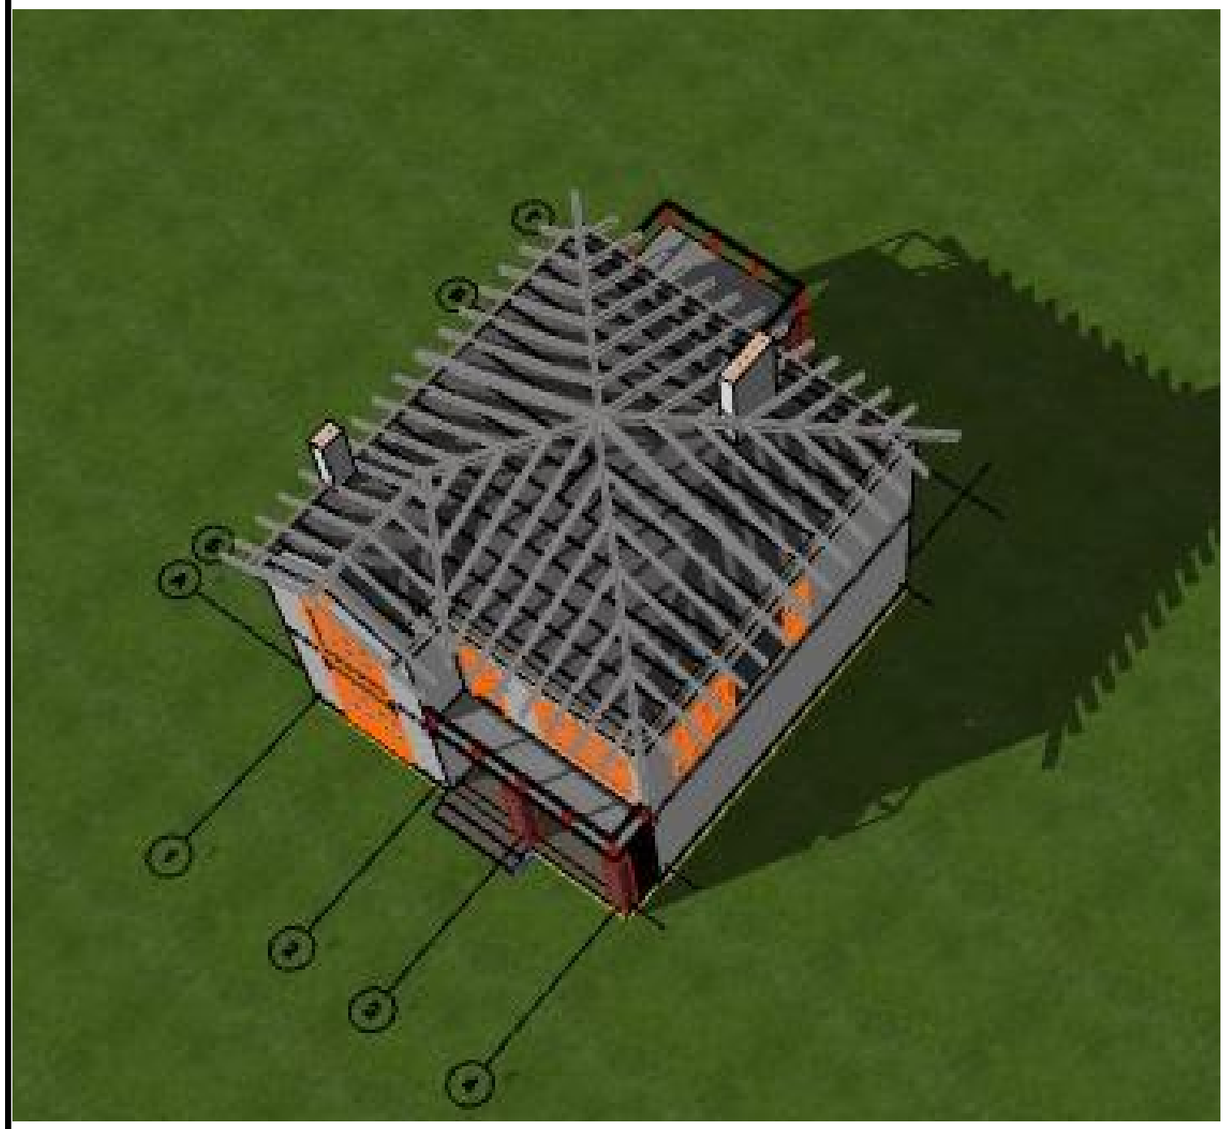

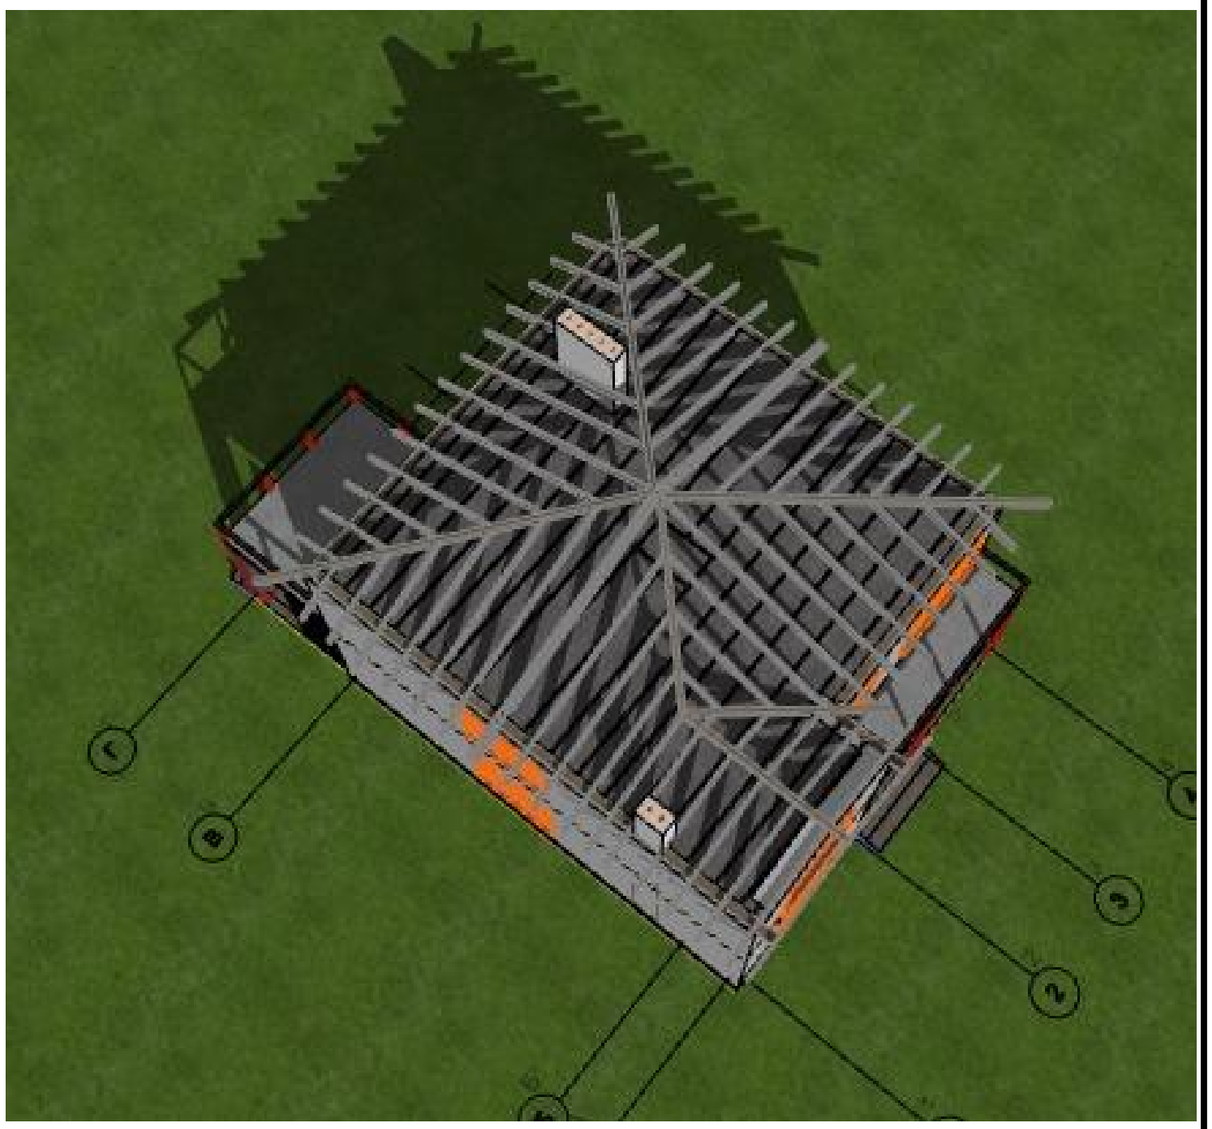


						#ID Проекта		
						кадастровый номер Россия		
Изм.	Кол.уч.	Лист	№Док.	Подп.	Дата			
Разраб.						Индивидуальный жилой дом	Стадия	Лист	Листов
							#Стадия Проекта	30	
						3Д Вид стропильной системы			


ИКК-03 Стропильная система				
Наименование	Объе...	Округл...	Длина (...	Кол...
Коньковый брус 200x100	0,00	150	120	1
Коньковый брус 200x100	0,07	3 700	3 690	1
Коньковый брус 200x100	0,08	4 000	3 705	1
Коньковый брус 200x100	0,08	4 200	3 946	1
Коньковый брус 200x100	0,48	8 100	7 651	3
Мауэрлат 100x200	0,04	1 950	1 927	1
Мауэрлат 100x200	0,10	5 250	5 240	1
Мауэрлат 100x200	0,18	9 000	8 980	1
Мауэрлат 100x200	0,18	9 100	9 100	1
Мауэрлат 100x200	0,22	10 950	10 920	1
Стропильная нога 200x50	0,00	500	349	1
Стропильная нога 200x50	0,01	1 150	949	1
Стропильная нога 200x50	0,01	1 300	1 049	1
Стропильная нога 200x50	0,06	1 400	1 164	6
Стропильная нога 200x50	0,02	2 050	1 749	1
Стропильная нога 200x50	0,12	2 200	1 864	6
Стропильная нога 200x50	0,03	2 700	2 349	1
Стропильная нога 200x50	0,03	2 800	2 449	1
Стропильная нога 200x50	0,18	2 950	2 564	6
Стропильная нога 200x50	0,27	3 150	2 740	9
Стропильная нога 200x50	0,28	3 700	3 264	7
Стропильная нога 200x50	0,04	4 250	3 749	1
Стропильная нога 200x50	0,28	4 500	3 964	7
Стропильная нога 200x50	0,35	5 250	4 664	7
Стропильная нога 200x50	0,06	5 750	5 124	1
Стропильная нога 200x50	0,06	6 000	5 339	1
Стропильная нога 200x50	0,24	6 050	5 360	4

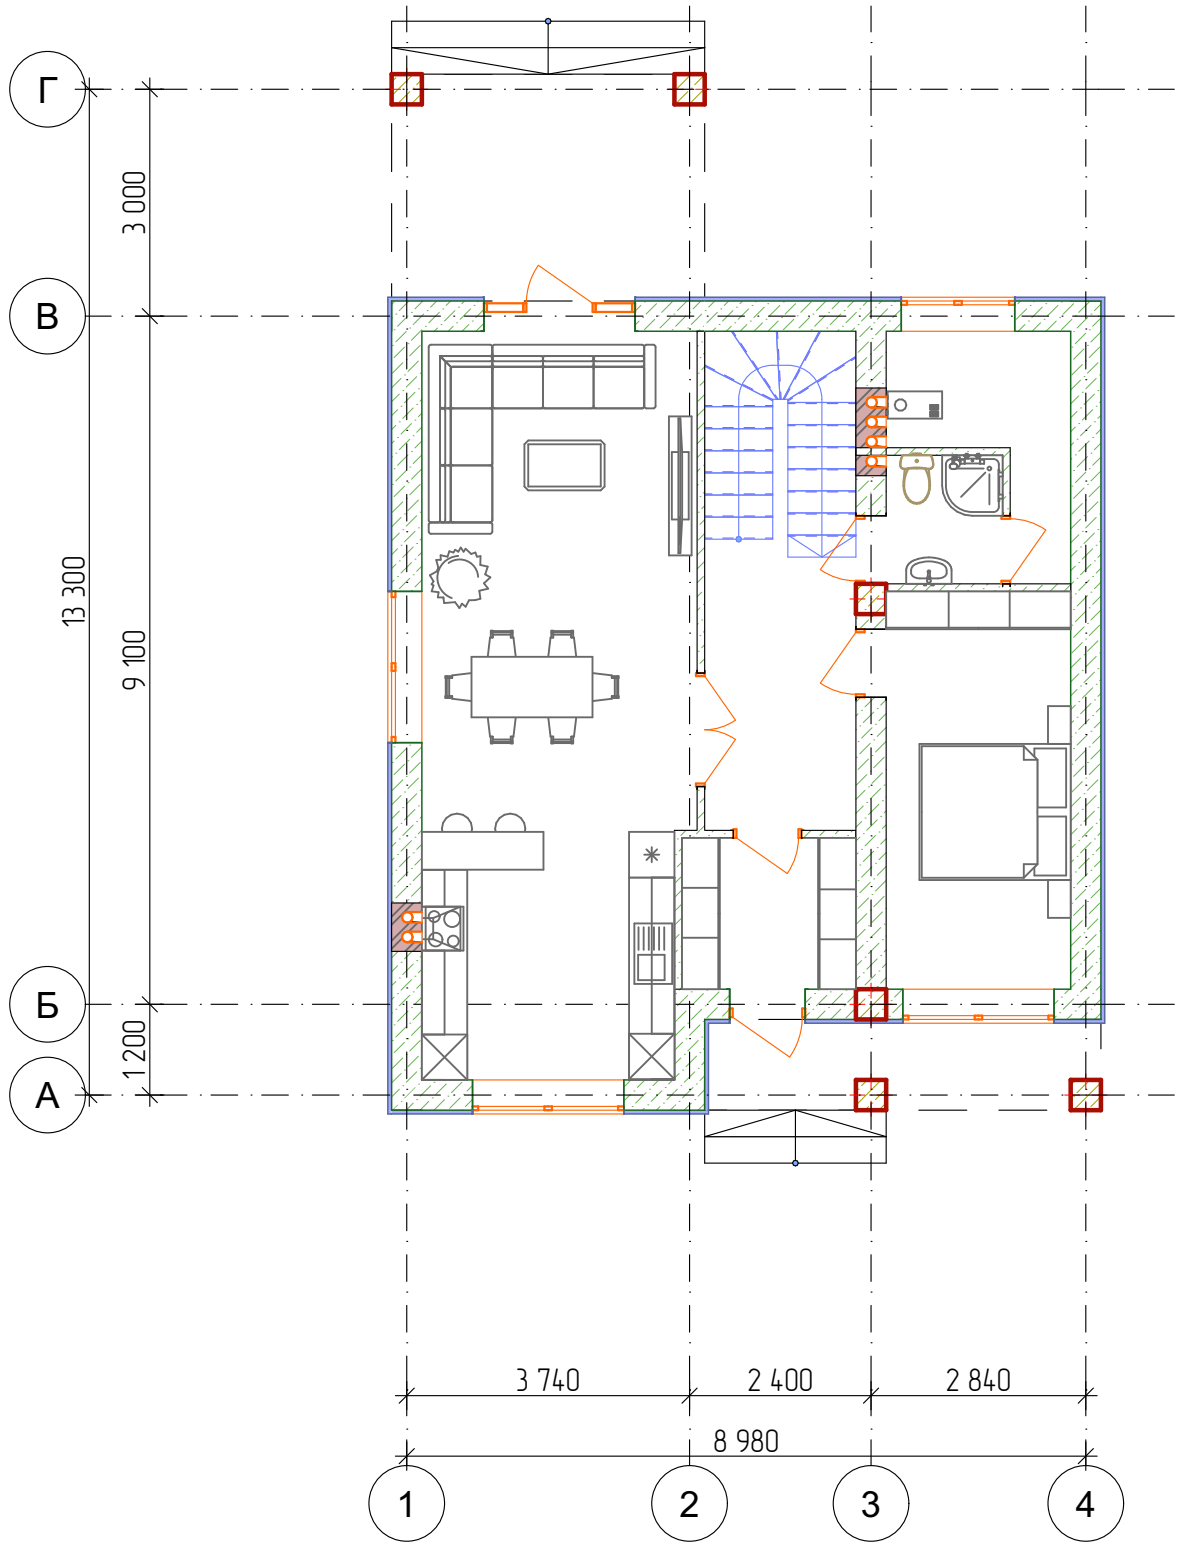

						#ID Проекта		
						кадастровый номер Россия		
Изм.	Кол.уч.	Лист	№Док.	Подп.	Дата			
Разраб.						Индивидуальный жилой дом	Стадия: #Стадия Проекта	Лист: 32 / Листов:
						План расстановки мебели 1 этаж		

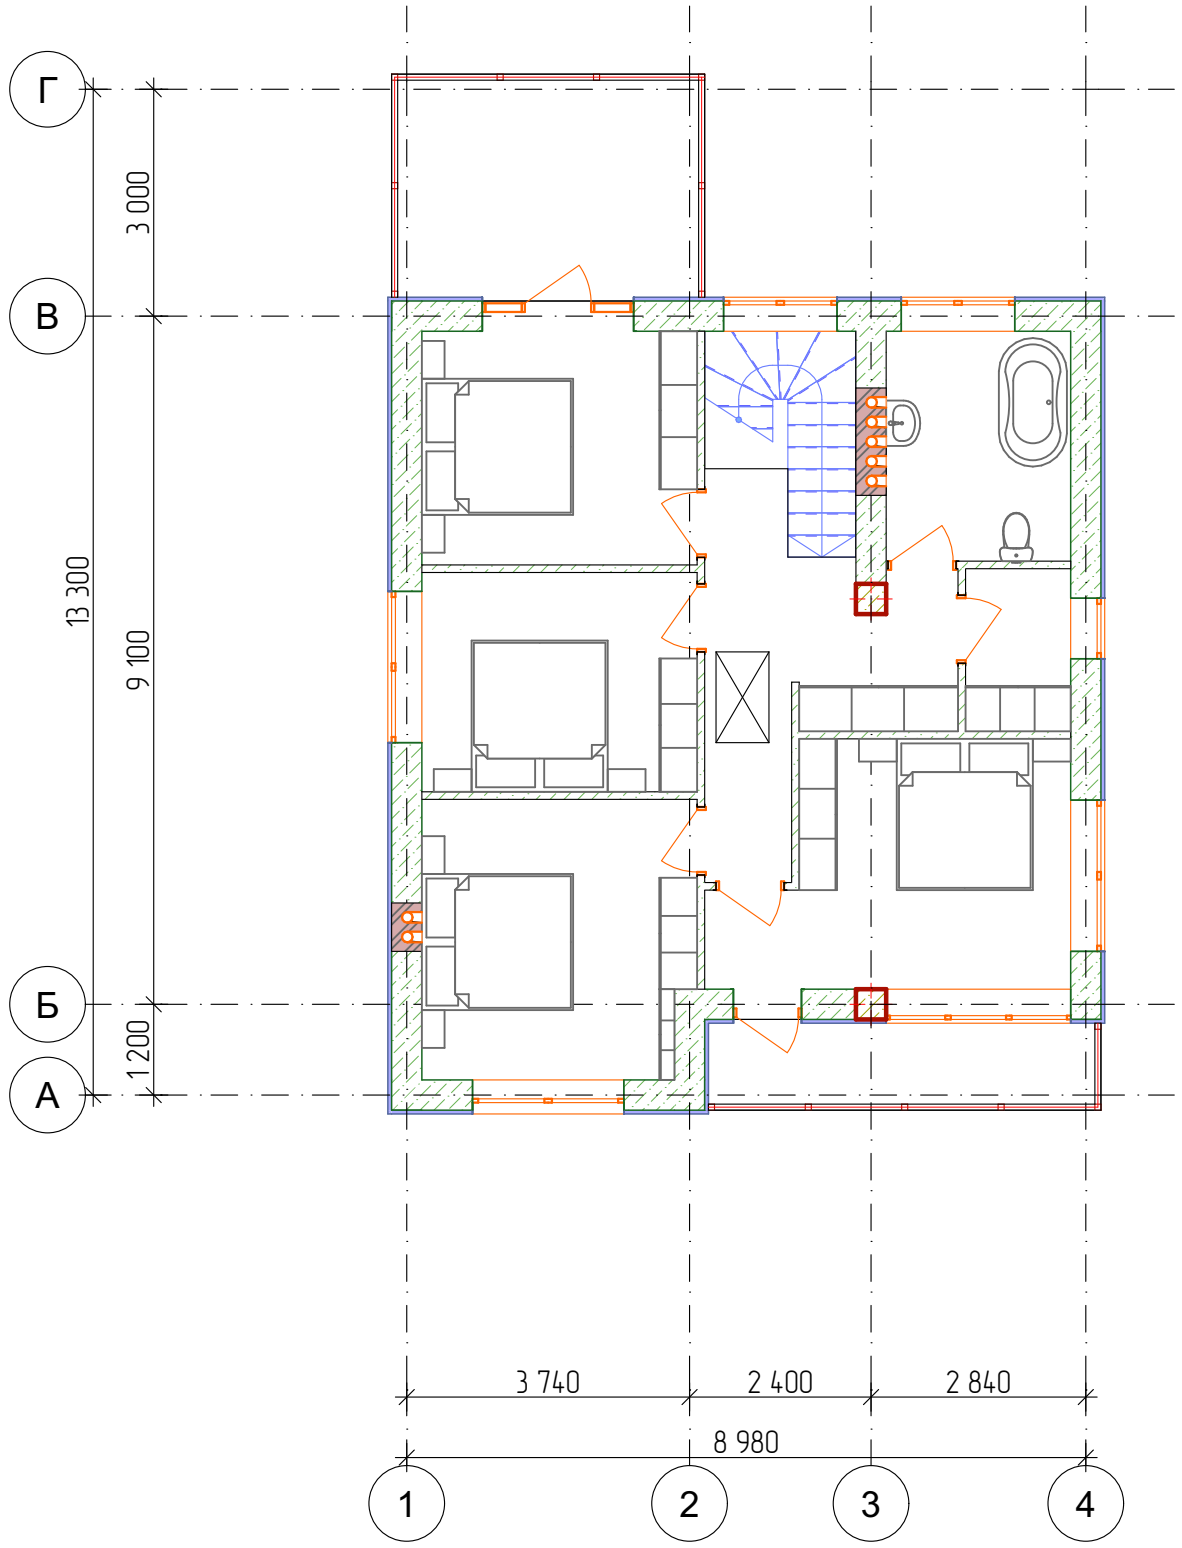


						#ID Проекта	
						кадастровый номер Россия	
Изм.	Кол.уч.	Лист	№Док.	Подп.	Дата		
Разраб.						Индивидуальный жилой дом	Стадия: #Стадия Проекта; Лист: 33; Листов:
						План расстановки мебели 2 этаж	

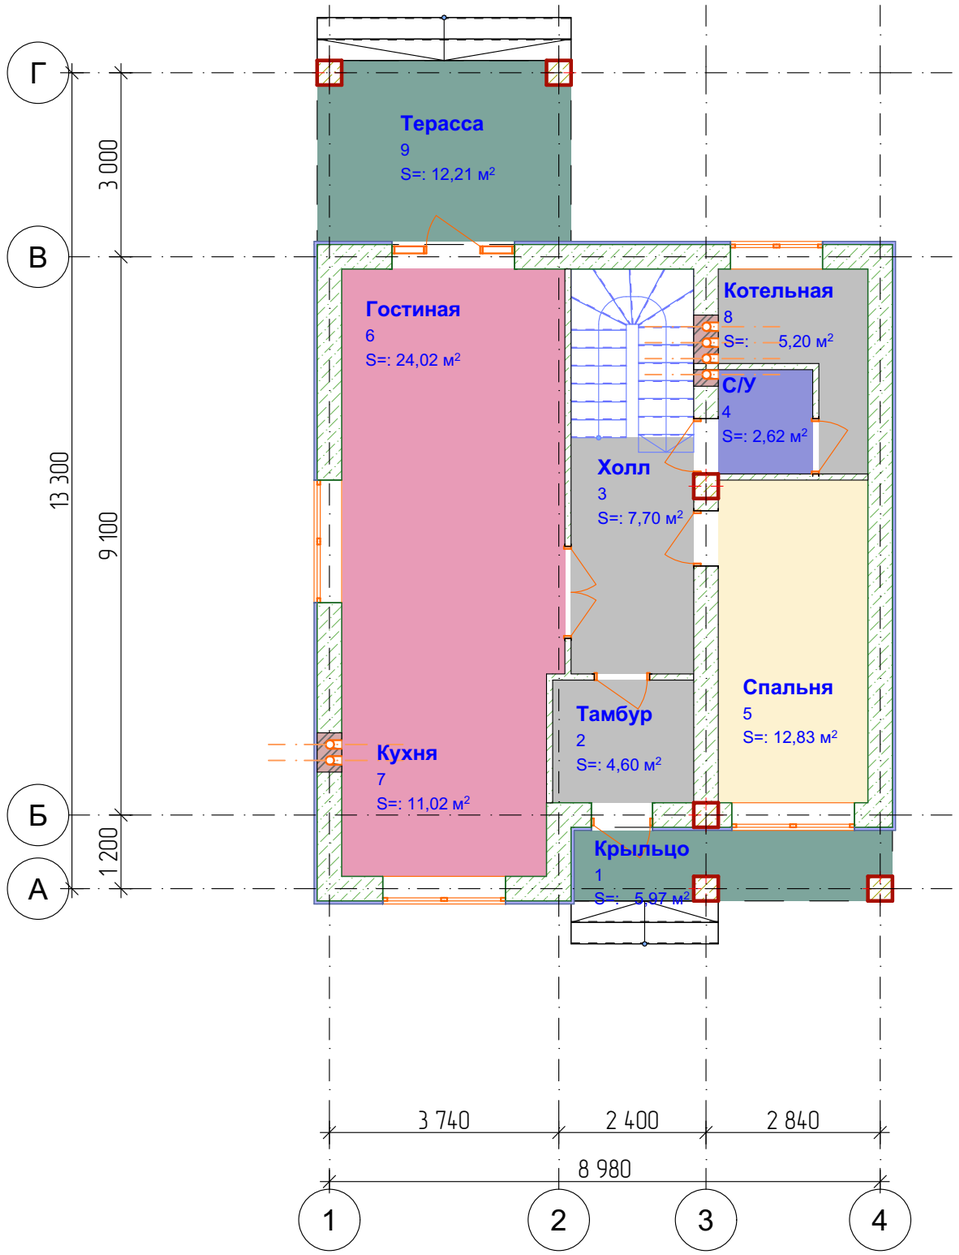

№	Наименование	Площадь
1	Крыльцо	5,97
2	Тамбур	4,60
3	Холл	7,70
4	С/У	2,62
5	Спальня	12,83
6	Гостиная	24,02
7	Кухня	11,02
8	Котельная	5,20
9	Терасса	12,21
		86,17 м²


						#ID Проекта
						кадастровый номер Россия
Изм.	Кол.уч.	Лист	№Док.	Подп.	Дата	
Разраб.						Индивидуальный жилой дом
						Экспликация помещений 1- го этажа

Стадия	Лист	Листов
#Стадия Проекта	34	

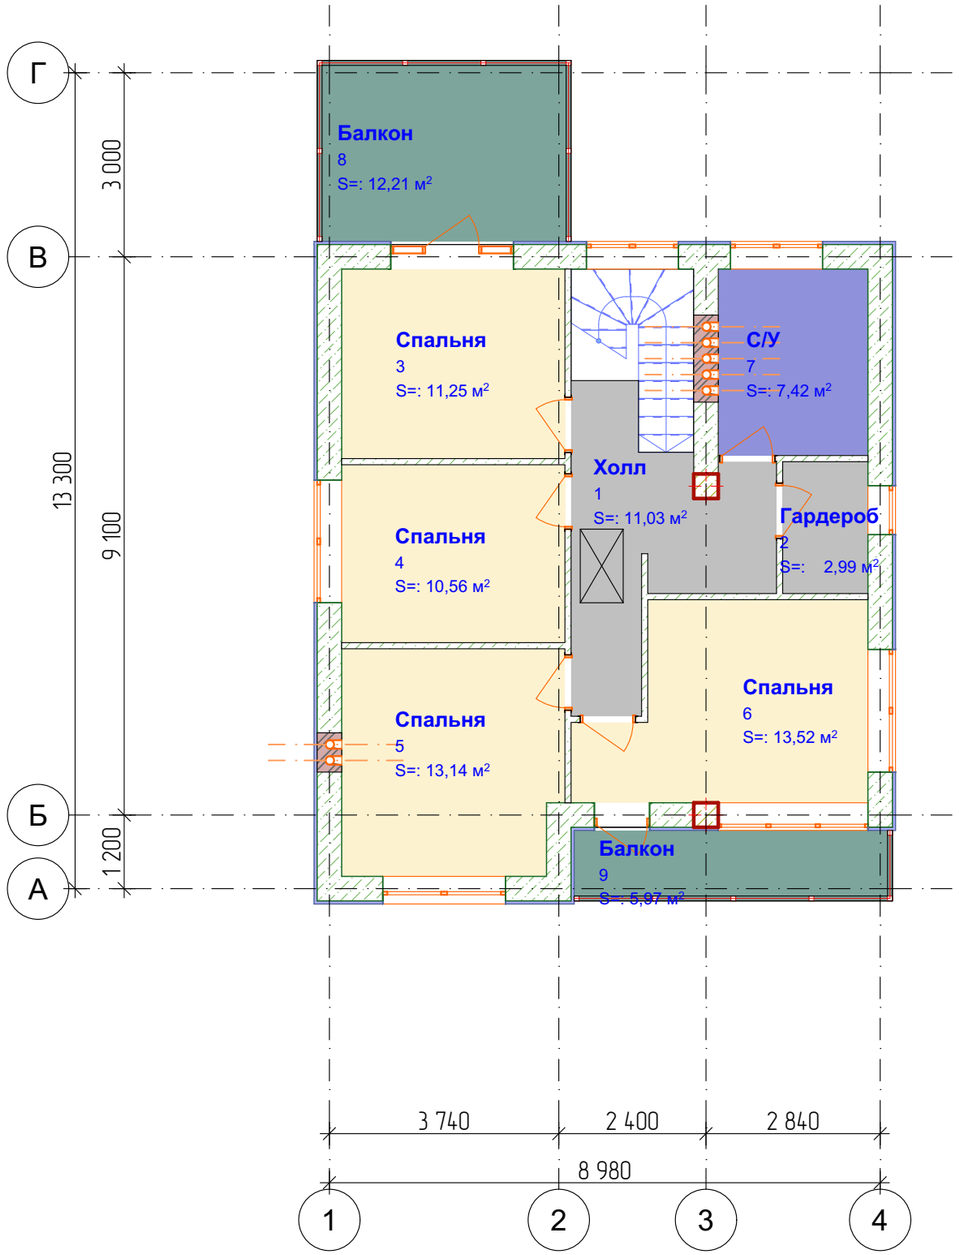


№	Наименование	Площадь
1	Холл	11,03
2	Гардероб	2,99
3	Спальня	11,25
4	Спальня	10,56
5	Спальня	13,14
6	Спальня	13,52
7	С/У	7,42
8	Балкон	12,21
9	Балкон	5,97
		88,09 м²


Изм.	Кол.уч.	Лист	№Док.	Подп.	Дата	#ID Проекта		
						кадастровый номер Россия		
Разраб.						Индивидуальный жилой дом	Стадия: #Стадия Проекта	Лист: 35 / Листов:
						Экспликация помещений 2-го этажа		

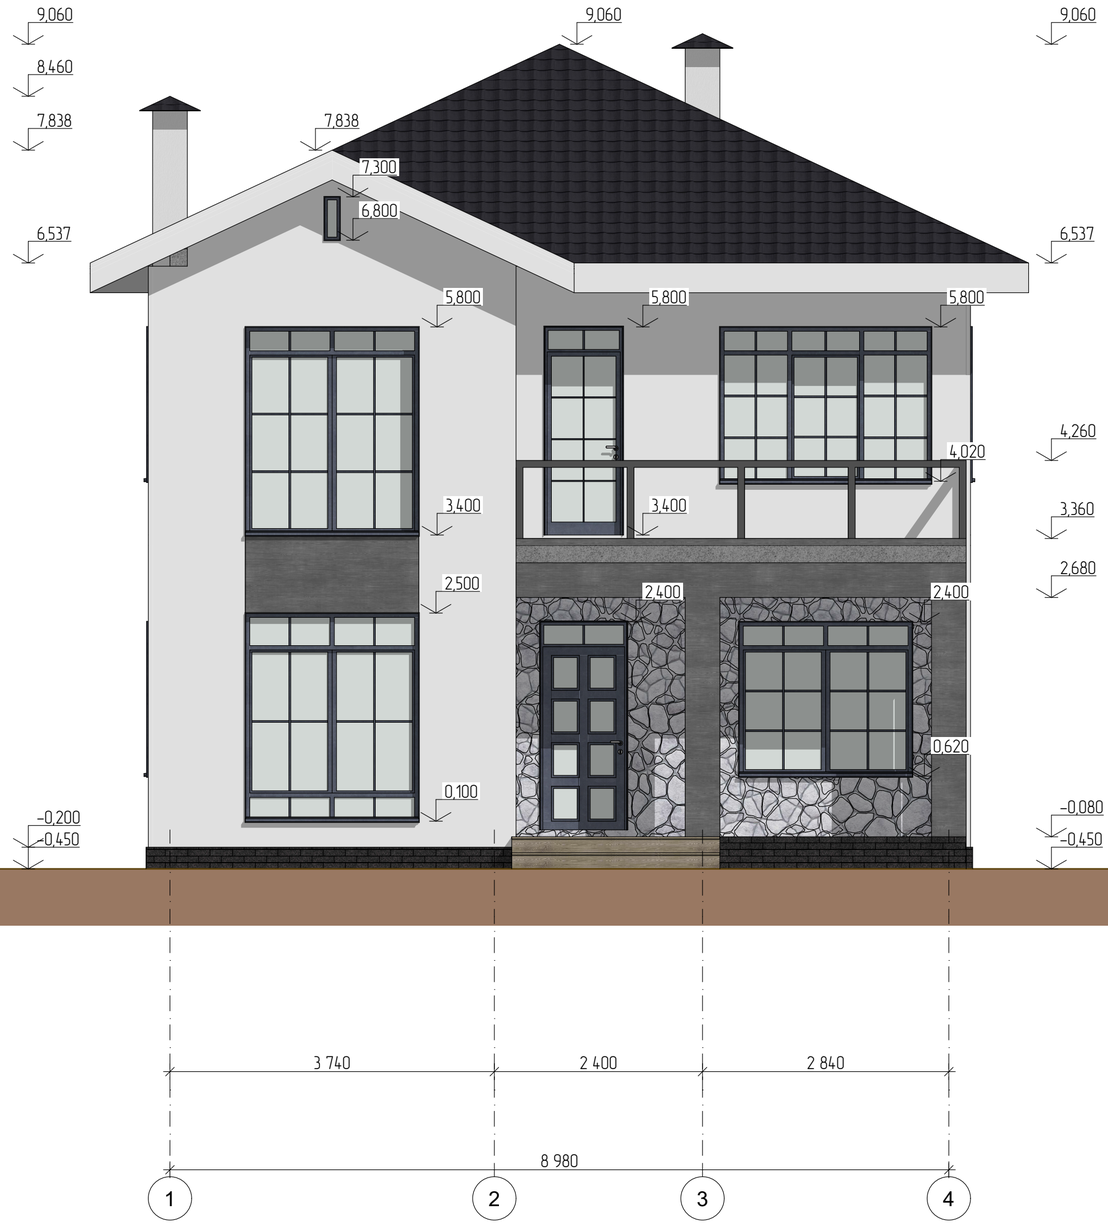


						#ID Проекта	
						кадастровый номер Россия	
Изм.	Колуч.	Лист	№Док.	Подп.	Дата		
Разраб.						Индивидуальный жилой дом	Стадия: #Стадия Проекта; Лист: 36; Листов:
						Фасад в осях 1-4	

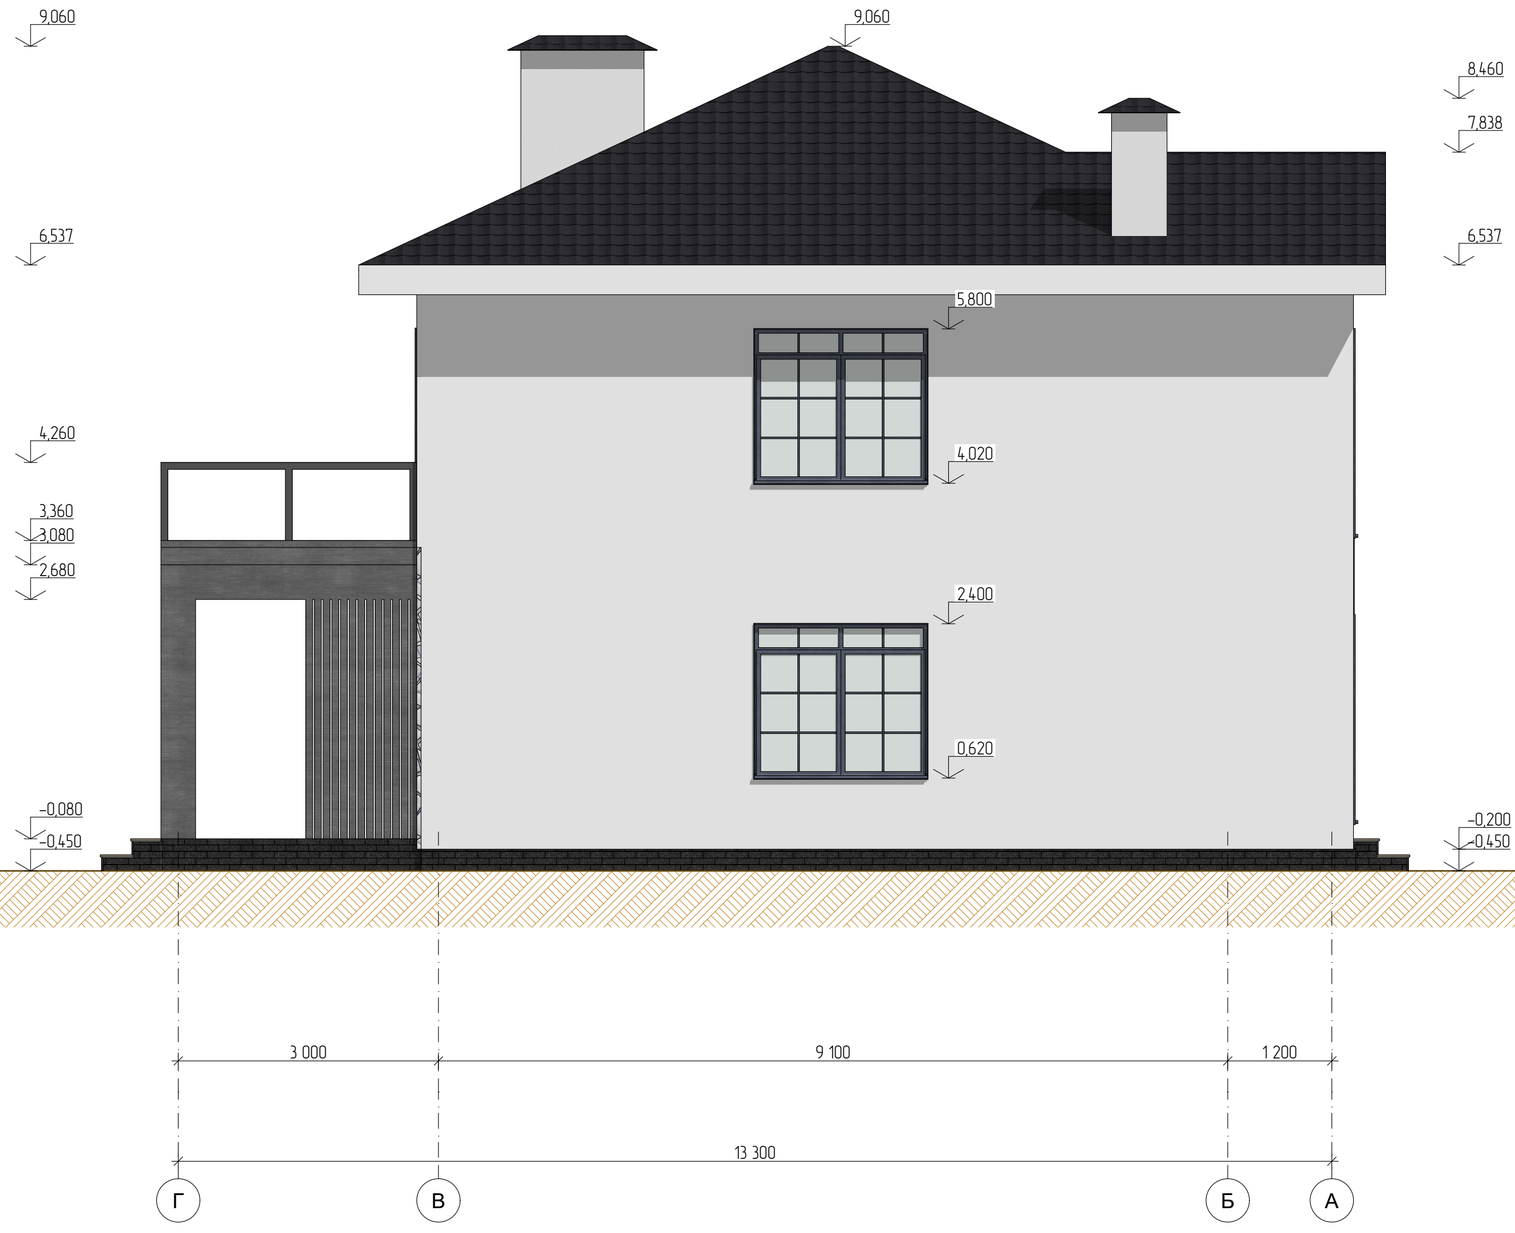

						#ID Проекта	
						кадастровый номер Россия	
Изм.	Кол.уч.	Лист	№Док.	Подп.	Дата		
Разраб.						Индивидуальный жилой дом	Стадия: #Стадия Проекта; Лист: 37; Листов:
						Фасад в осях Г-А	

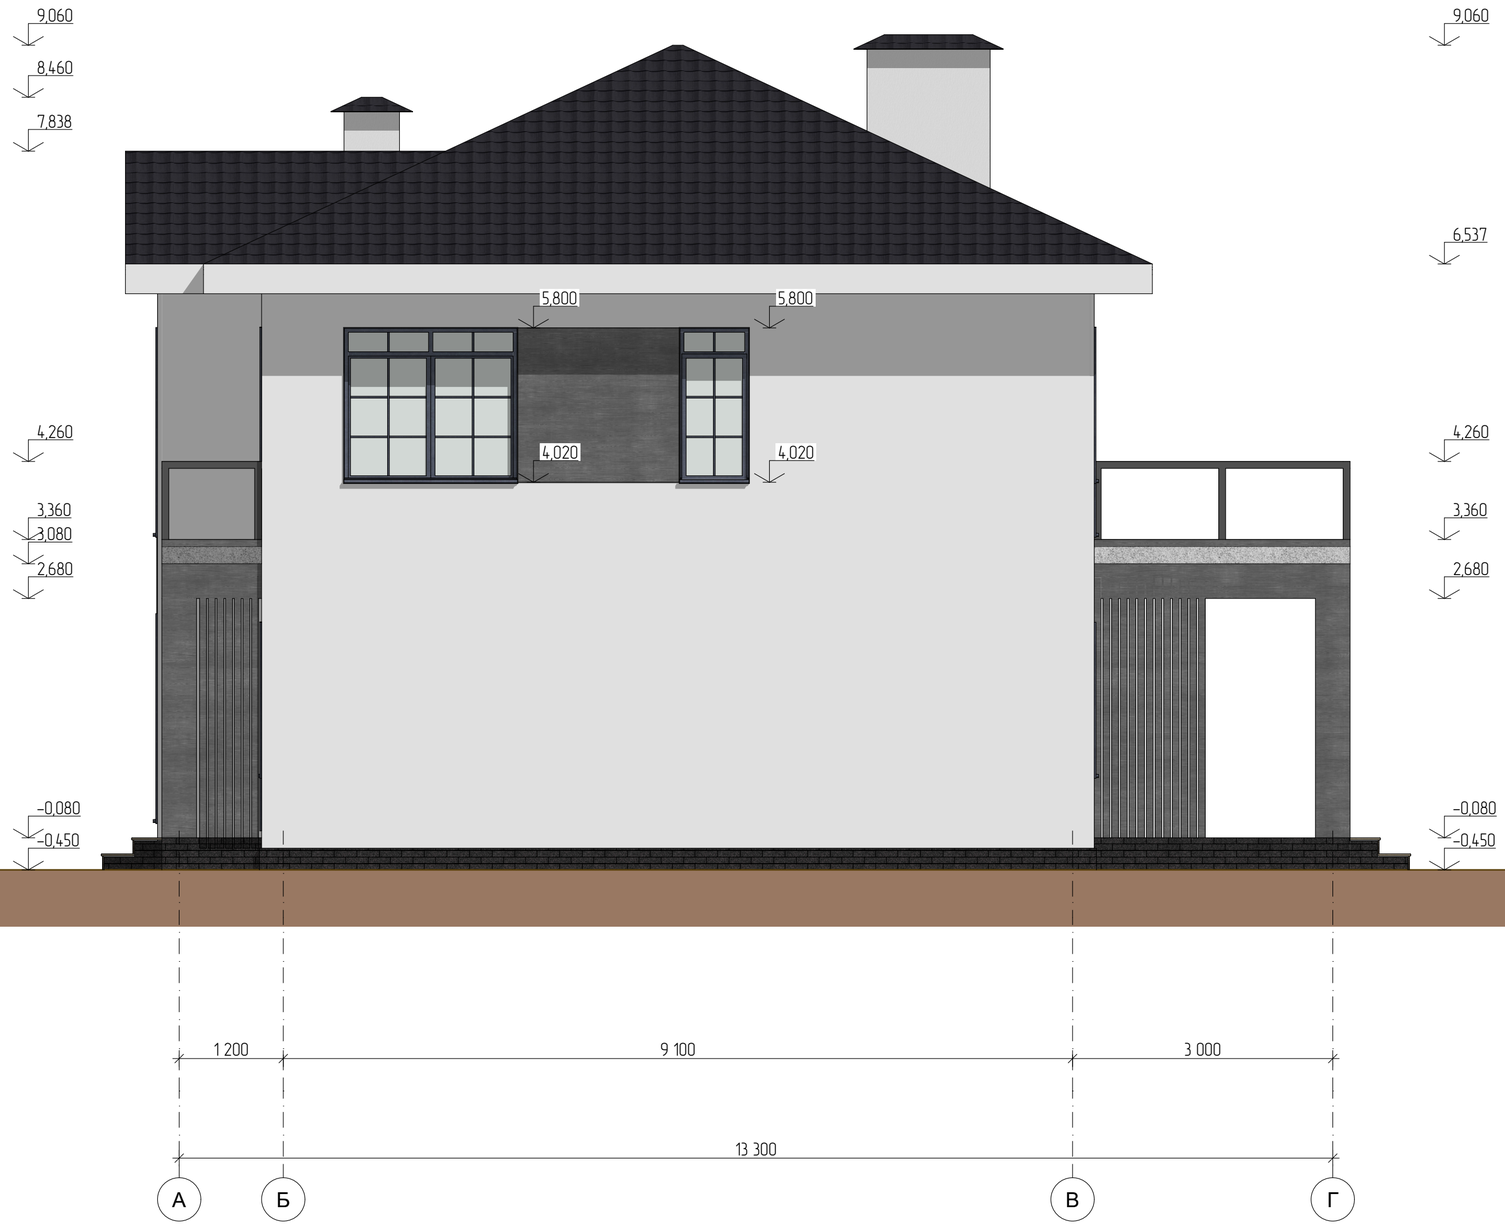

						#ID Проекта		
						кадастровый номер Россия		
Изм.	Кол.уч.	Лист	№Док.	Подп.	Дата			
Разраб.						Индивидуальный жилой дом	Стадия: #Стадия Проекта	Лист: 38 / Листов:
						Фасад в осях А-Г		

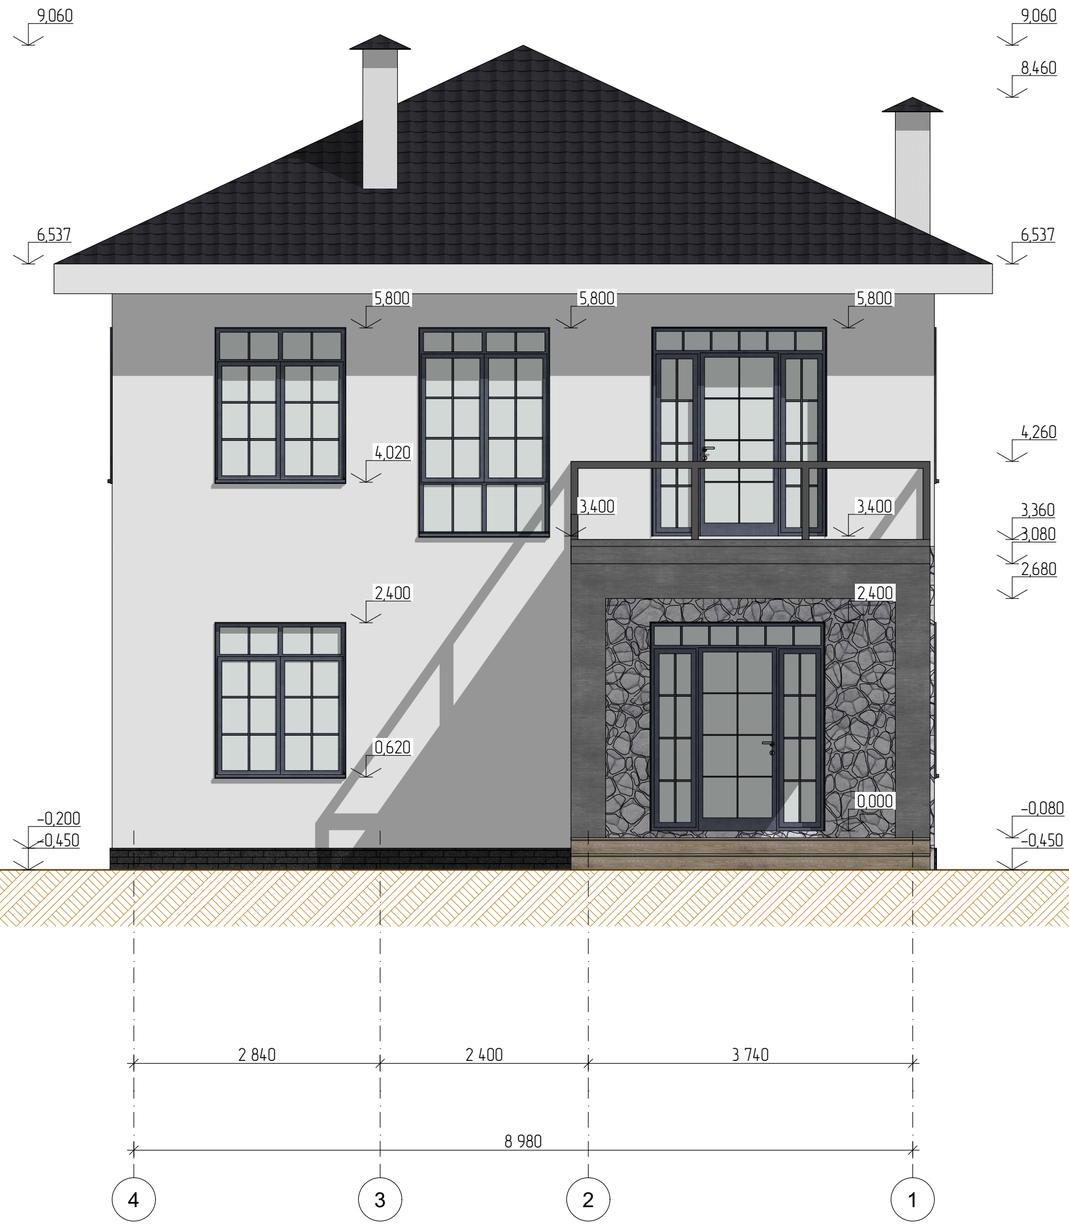

						#ID Проекта	
						кадастровый номер Россия	
Изм.	Колуч.	Лист	№Док.	Подп.	Дата		
Разраб.						Индивидуальный жилой дом	Стадия: #Стадия Проекта; Лист: 39; Листов:
						Фасад в осях 4-1	