ПРОЕКТНАЯ ДОКУМЕНТАЦИЯ

Индивидуальный жилой дом

кадастровый номер 47:07:0157001:3873, Ленинградская область, Всеволожский муниципальный район, Агалатовское сельское поселение, территория "История Парк", улица Петровская, з/у №20 Россия



Разработал Салыкова В.

2024

Ведомость листов	
Наименование	Лист
Обложка	
Общие данные	02
Сводная ведомость материалов	03
Генеральный план	04
3D Виды	05
План фундамента	06
План фундамента с закладными	07
Схема нижнего армирования фундамента	08
Схема верхнего армирования фундамента	09
Узел фундамента	10
Схема арматурного каркаса фундаментной плиты	11
План 1 этажа	12
План 2 этажа	13
Маркировочный план 1 этаж	14
Маркировочный план 2 этаж	15
Каталог дверных проемов	16
Каталог оконных проемов	17
Разрез 1 - 1	18
Разрез 2 - 2	19
Разрез по стене	20
План перекрытия на отм+3,050	21
План перекрытий на отм 6,500	22
Монолитный пояс на отм 2,800	23
Монолитный пояс на отм 6,250	24
План кровли на отм. 3,432	25
План кровли на отм. 6,735	26
Схема расположения стропил на отм. 6,735	27
3Д Вид стропильной системы	28
3Д вид лестницы	29
План расстановки мебели 1 этаж	30
План расстановки мебели 2 этаж	31
Экспликация помещений 1- го этажа	32
Экспликация помещений 2-го этажа	33
Фасад в осях 1-3	34
Фасад в осях Е-А	35
Фасад в осях А-Е	36
Фасад в осях 3-1	37

Изм.	Кол.уч.	Лист	№Док.	Подп.	Дата	кадастровый номер 47:07:0157001:3873, Ленинградская область, Всеволожский муниципальный район, Агалатовское сельское поселение, территория "История Парк", улица Петровская, з/у №20 Россия			
Разраб.		Салыкова Е.				Индивидуальный жилой дом	Стадия	Лист	Листов
							ЭП	02	
						Общие данные			

ВЕДОМОСТЬ ПЕРЕКРЫТИЯ	
Наименование	Объем
Монолитное перекрытие	24,37

ИКК-03 Ведомость перекрытий 1	
Наименование	Объем

Балка деревянная 200x50	1,50

Ведомость перекрытия	
Наименование	Объем

Балка деревянная 200x50	2,04

ВЕДОМОСТЬ КРОВЕЛЬНОГО МАТЕРИАЛА	
Наименование	Площадь, м2
Кровля дома	126,56

ИКК-03 Кровля	
Наименование	Площадь
Кровля плоская	80,58

ВЕДОМОСТЬ СТРОПИЛЬНОЙ СИСИТЕМЫ	
Наименование	Объем, м3
	1,06
Мауэрлат 100x200	0,20
Подстропильная нога 200x50	1,36
Стойка 200x50	0,34
Стойка 200x100	0,46
Стропильная нога 200x50	2,55

ВЕДОМОСТЬ НА МОНОЛИТНЫЙ ПОЯС 1-ГО ЭТАЖА	
Наименование	Объем, м3
	3,75
Монолитный пояс из U-блоков	3,75

ВЕДОМОСТЬ НА МОНОЛИТНЫЙ ПОЯС 2-ГО ЭТАЖА	
Наименование	Объем, м3
	5,86
Монолитный пояс из U-блоков	5,86

ВЕДОМОСТЬ НА УТЕПЛИТЕЛЬ ДЛЯ СТЕН, ПОЛА ПЕРВОГО ЭТАЖА, РОСТВЕРКА			
Наименование	**Компоненты**		
	Толщина [м]	**Объем [м3]**	**Площадь [м2]**
Изоляция - Минеральная Жесткая			
	200	39,57	201,93
Изоляция - ЭППС			
	50	1,49	29,75
	100	16,65	167,00

Отделочные материалы		
Наименование	**Компоненты**	
	Толщина [м]	**Площадь [м2]**
Клинкерная плитка (фасадная)		
	20	282,90
Планкен		
	20	64,20
Штукатурка - фасадная		
	10	96,22


ВЕДОМОСТЬ БЕТОНА	
Наименование	Объем, м3
Лента фундамента	2,06
Плита фундамента	78,14
	80,20 м³

ВЕДОМОСТЬ БЛОКА ДЛЯ СТЕН	
ID Элемента	Объем, м3
Несущие 400мм	179,79
Перегородки 100мм	13,83

Изм.	Кол.уч.	Лист	№Док.	Подп.	Дата	
						кадастровый номер 47:07:0157001:3873, Ленинградская область, Всеволожский муниципальный район, Агалатовское сельское поселение, территория "История Парк", улица Петровская, з/у №20 Россия
Разраб.		Салыкова Е.				Индивидуальный жилой дом
						Сводная ведомость материалов

Стадия	Лист	Листов
ЭП	03	

Проектируемый участок

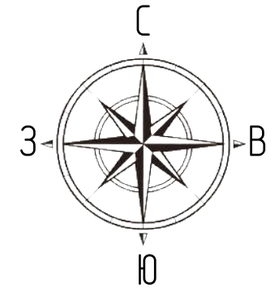





Проектируемый дом

Гараж

Навес

Крыльцо

						кадастровый номер 47:07:0157001:3873, Ленинградская область, Всеволожский муниципальный район, Агалатовское сельское поселение, территория "История Парк", улица Петровская, з/у №20 Россия
Изм.	Кол.уч.	Лист	№Док.	Подп.	Дата	
Разраб.		Салыкова Е.				Индивидуальный жилой дом
						Генеральный план

Стадия	Лист	Листов
ЭП	04	











						кадастровый номер 47:07:0157001:3873, Ленинградская область, Всеволожский муниципальный район, Агалатовское сельское поселение, территория "История Парк", улица Петровская, з/у №20 Россия	
Изм.	Кол.уч.	Лист	№Док.	Подп.	Дата		
Разраб.		Салыкова Е.				Индивидуальный жилой дом	Стадия: ЭП; Лист: 05; Листов:
						3D Виды	

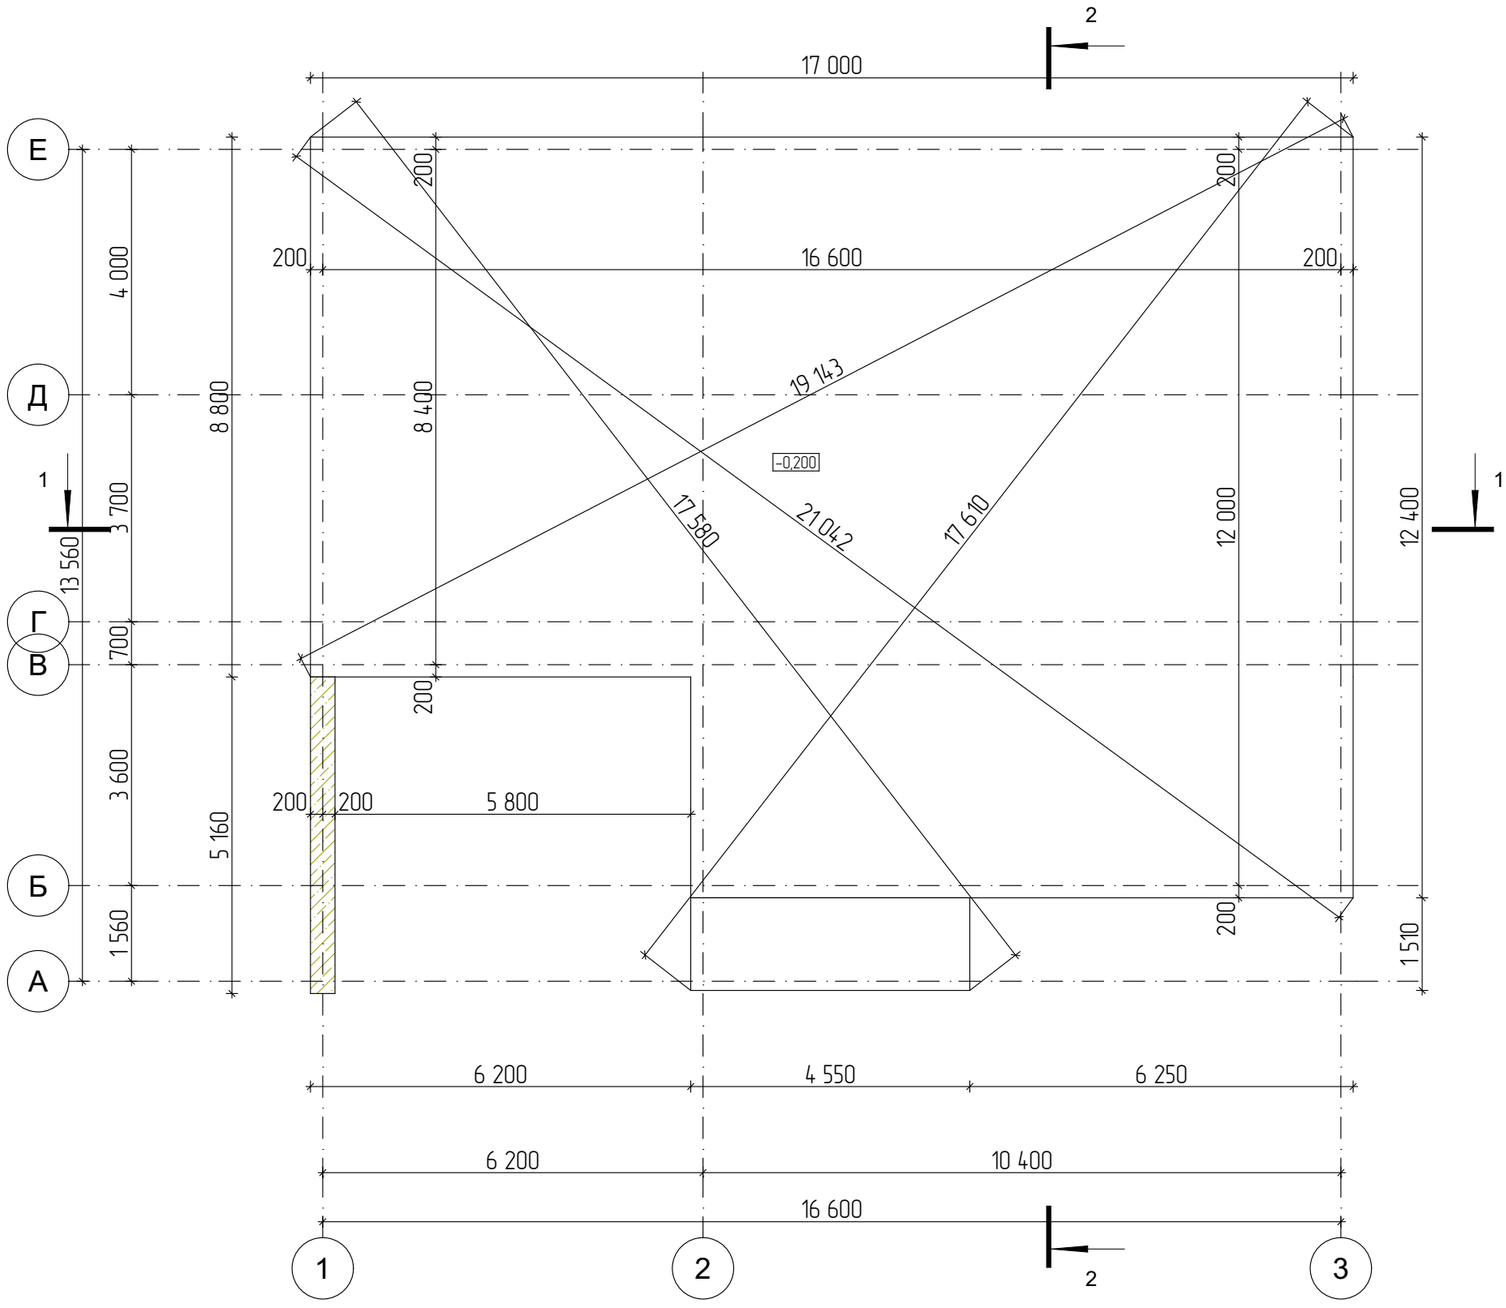

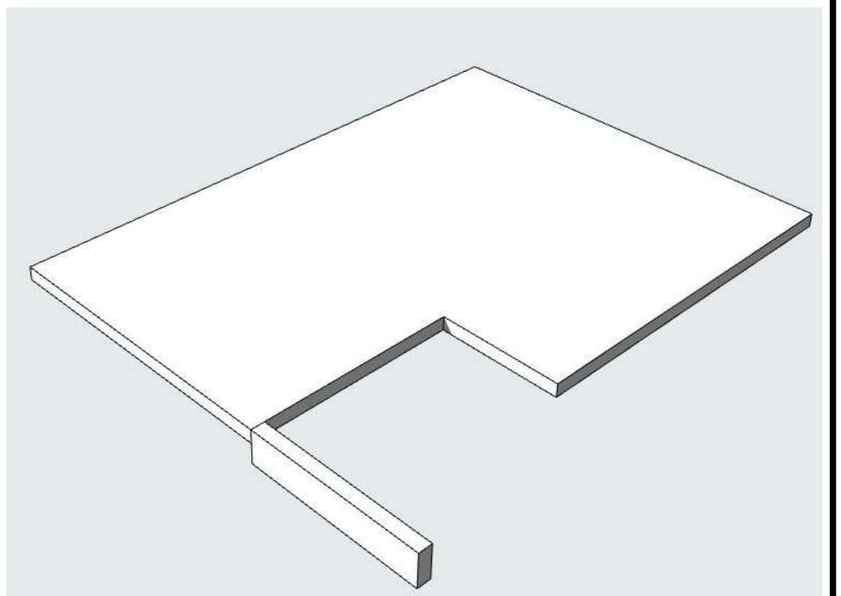


ВЕДОМОСТЬ БЕТОНА

Наименование	Объем, м3
Лента фундамента	2,06
Плита фундамента	78,14
	80,20 м³


Изм.	Кол.уч.	Лист	№Док.	Подп.	Дата	
						кадастровый номер 47:07:0157001:3873, Ленинградская область, Всеволожский муниципальный район, Агалатовское сельское поселение, территория "История Парк", улица Петровская, з/у №20 Россия
Разраб.		Салыкова Е.				Индивидуальный жилой дом
						План фундамента


Стадия	Лист	Листов
ЭП	06	

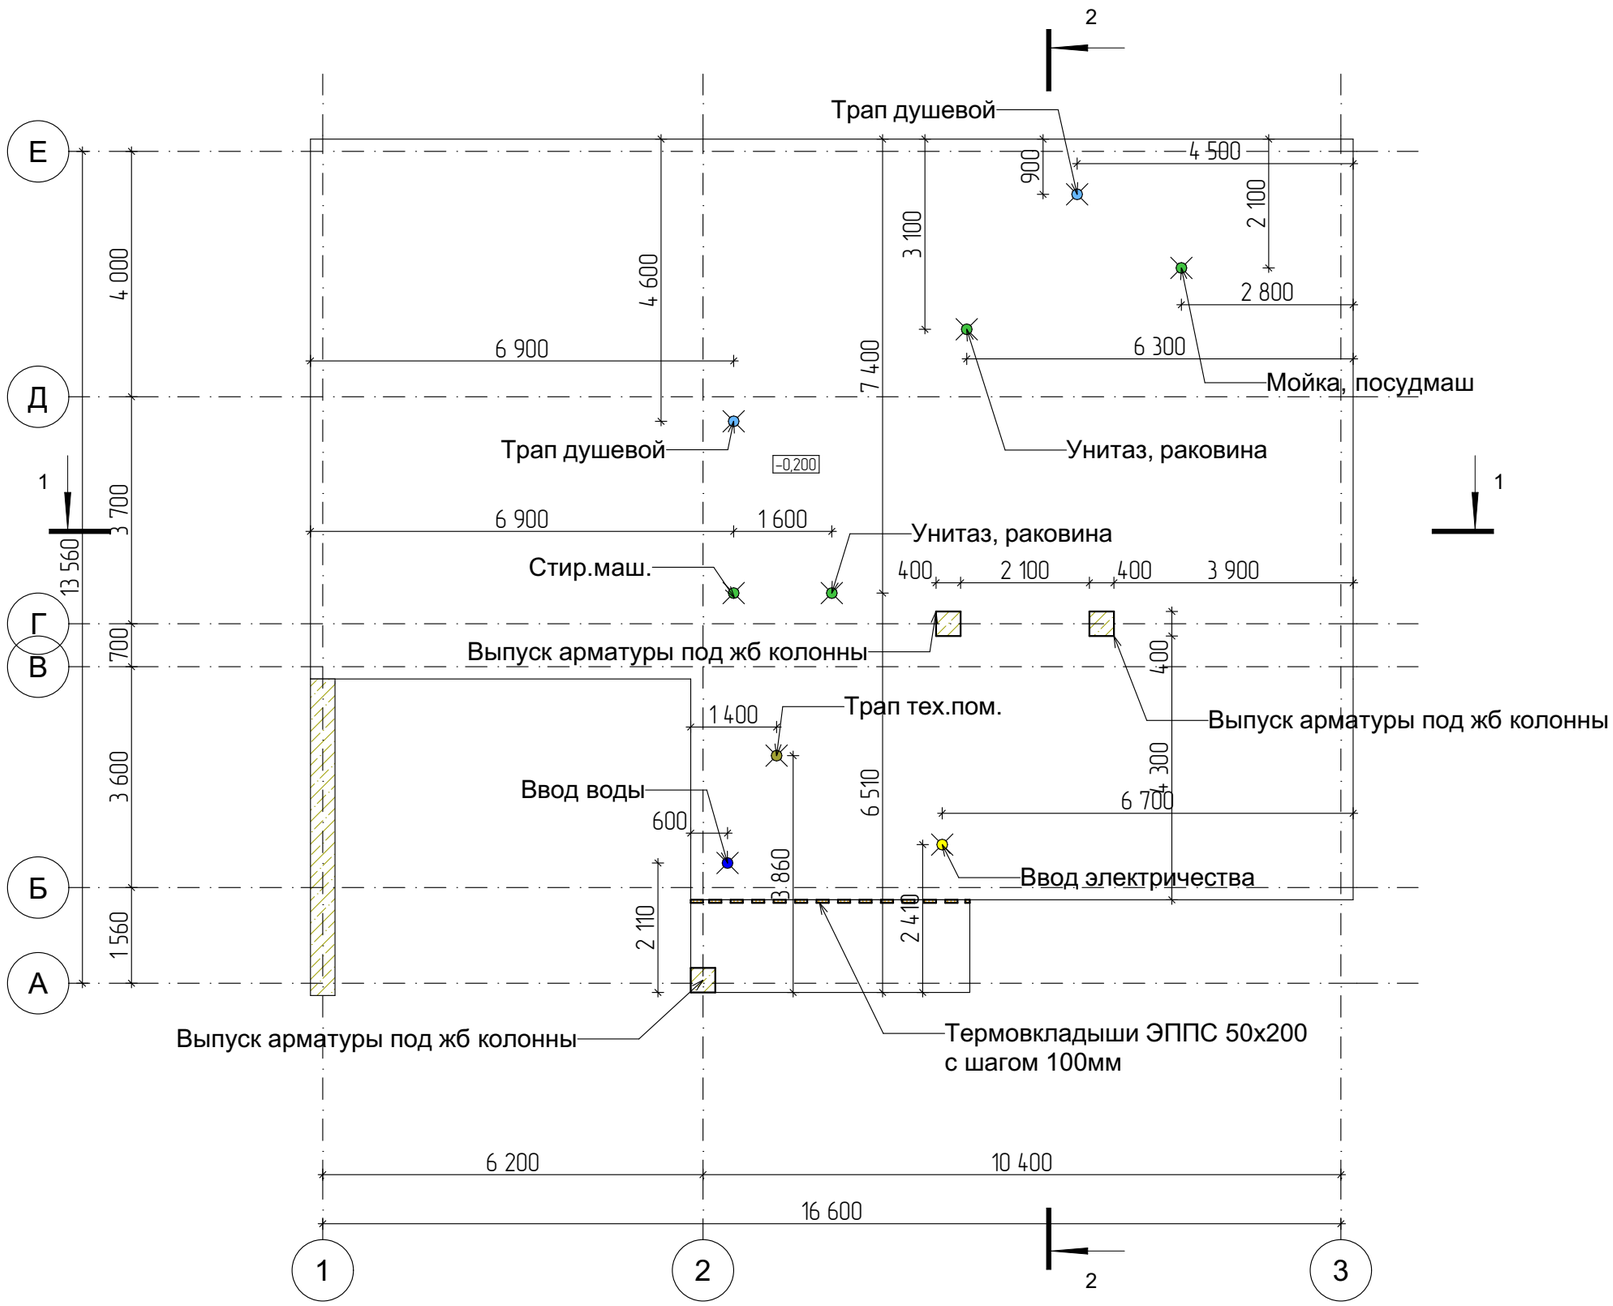

						кадастровый номер 47:07:0157001:3873, Ленинградская область, Всеволожский муниципальный район, Агалатовское сельское поселение, территория "История Парк", улица Петровская, з/у №20 Россия
Изм.	Кол.уч.	Лист	№Док.	Подп.	Дата	
Разраб.		Салыкова Е.				Индивидуальный жилой дом
						План фундамента с закладными


Стадия	Лист	Листов
ЭП	07	

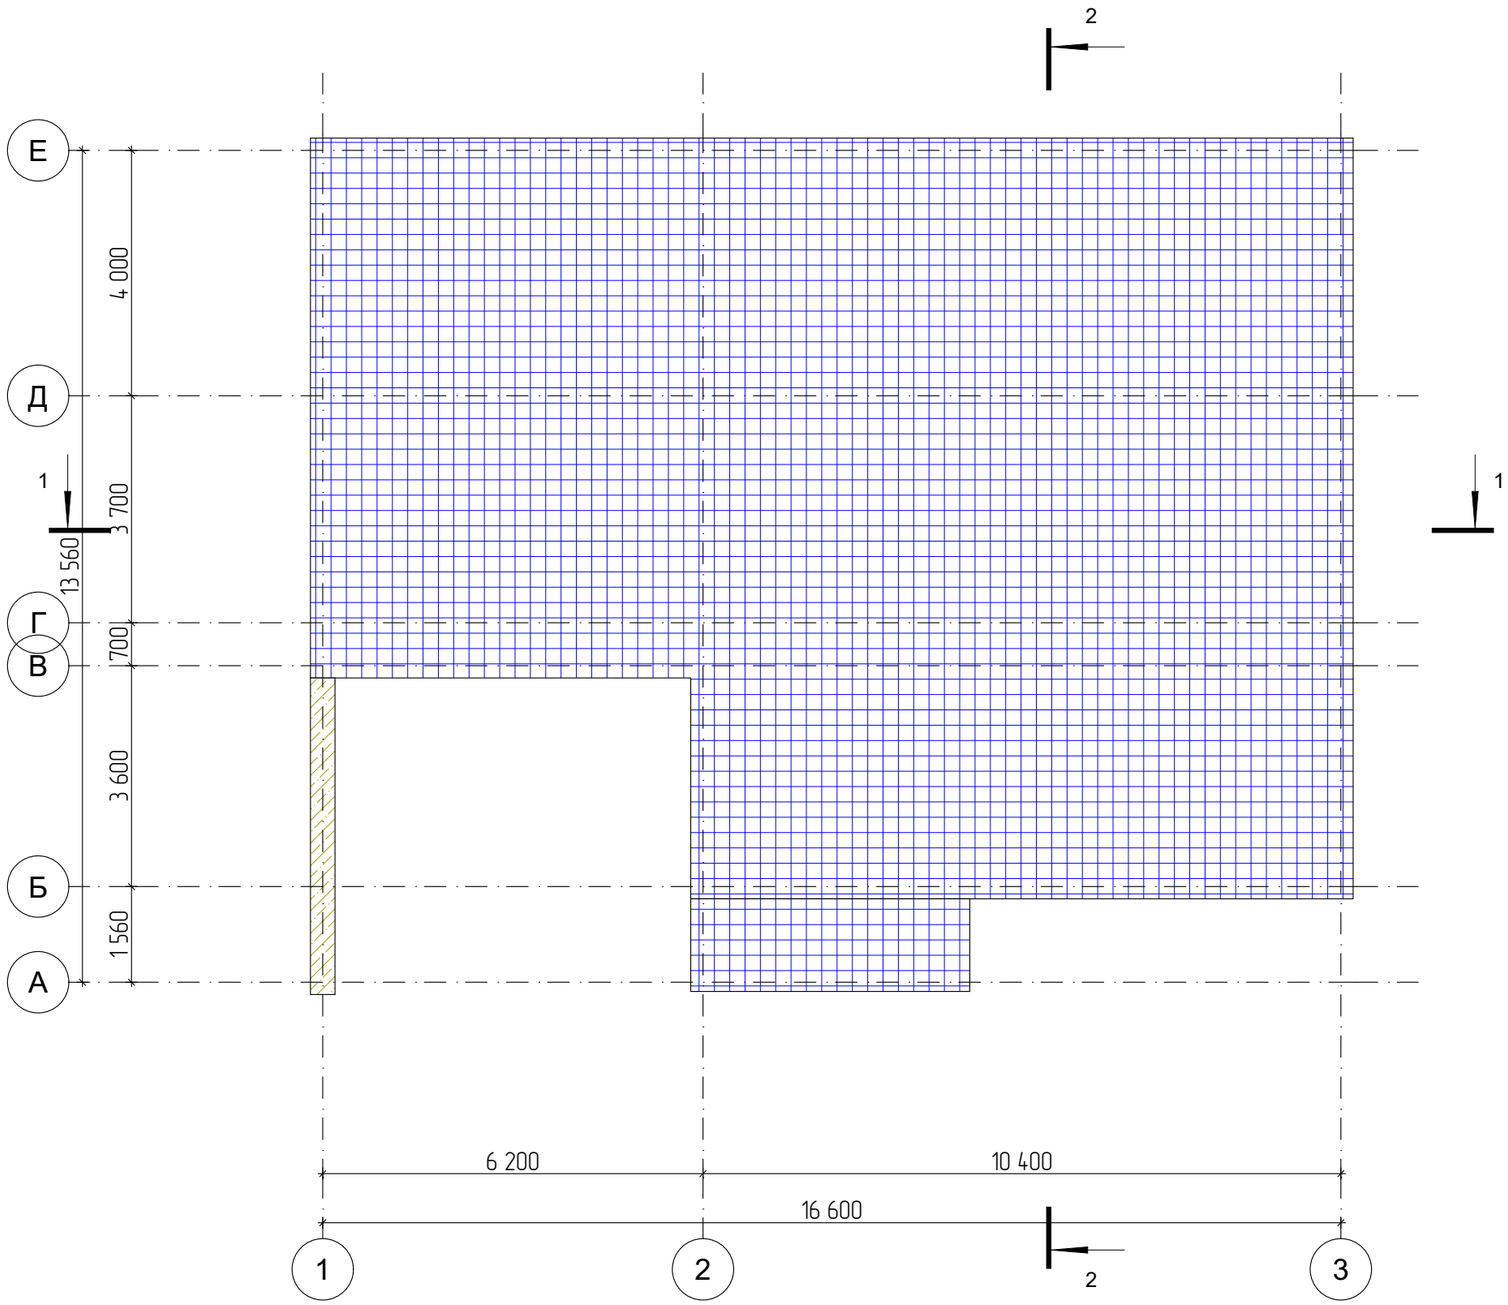


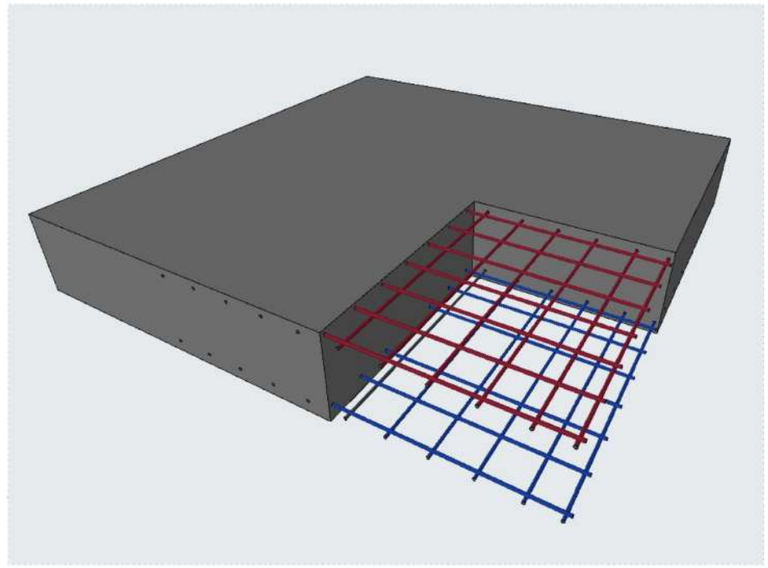

						кадастровый номер 47:07:0157001:3873, Ленинградская область, Всеволожский муниципальный район, Агалатовское сельское поселение, территория "История Парк", улица Петровская, з/у №20 Россия
Изм.	Кол.уч.	Лист	№Док.	Подп.	Дата	
Разраб.		Салыкова Е.				Индивидуальный жилой дом
						Схема нижнего армирования фундамента


Стадия	Лист	Листов
ЭП	08	

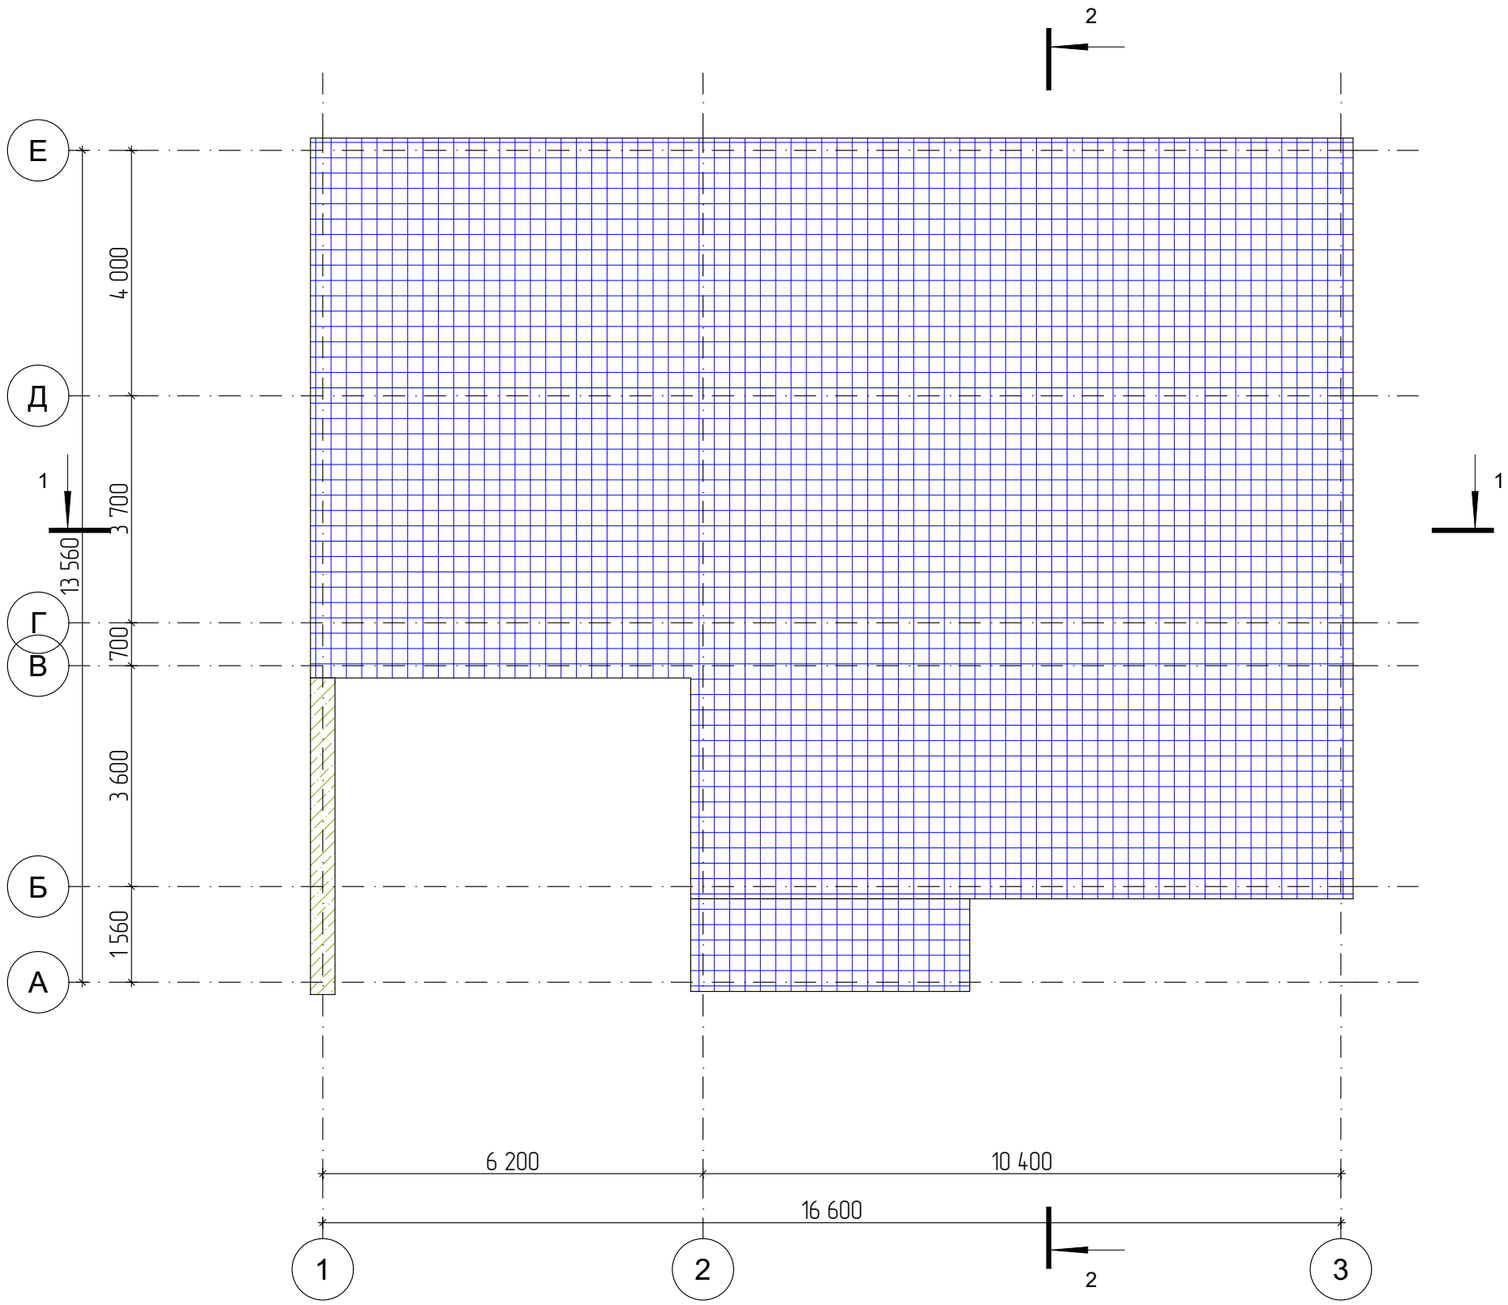

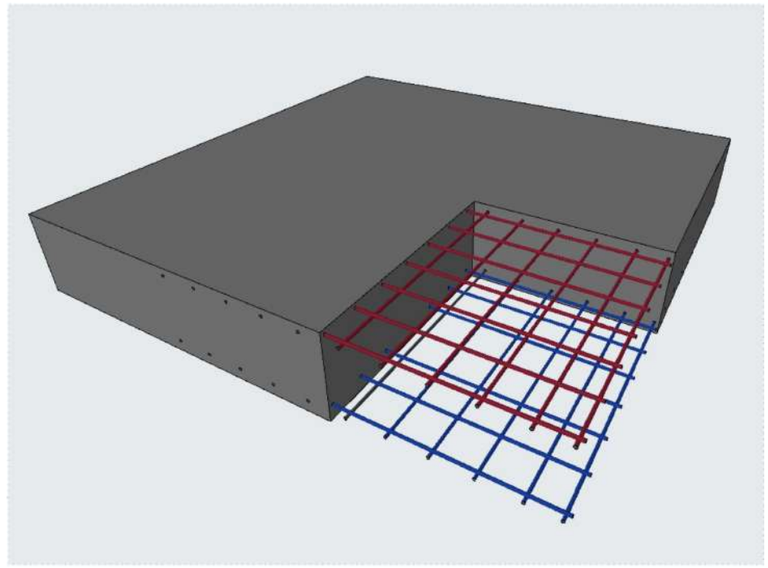

						кадастровый номер 47:07:0157001:3873, Ленинградская область, Всеволожский муниципальный район, Агалатовское сельское поселение, территория "История Парк", улица Петровская, з/у №20 Россия
Изм.	Кол.уч.	Лист	№Док.	Подп.	Дата	
Разраб.		Салыкова Е.				Индивидуальный жилой дом
						Схема верхнего армирования фундамента


Стадия	Лист	Листов
ЭП	09	

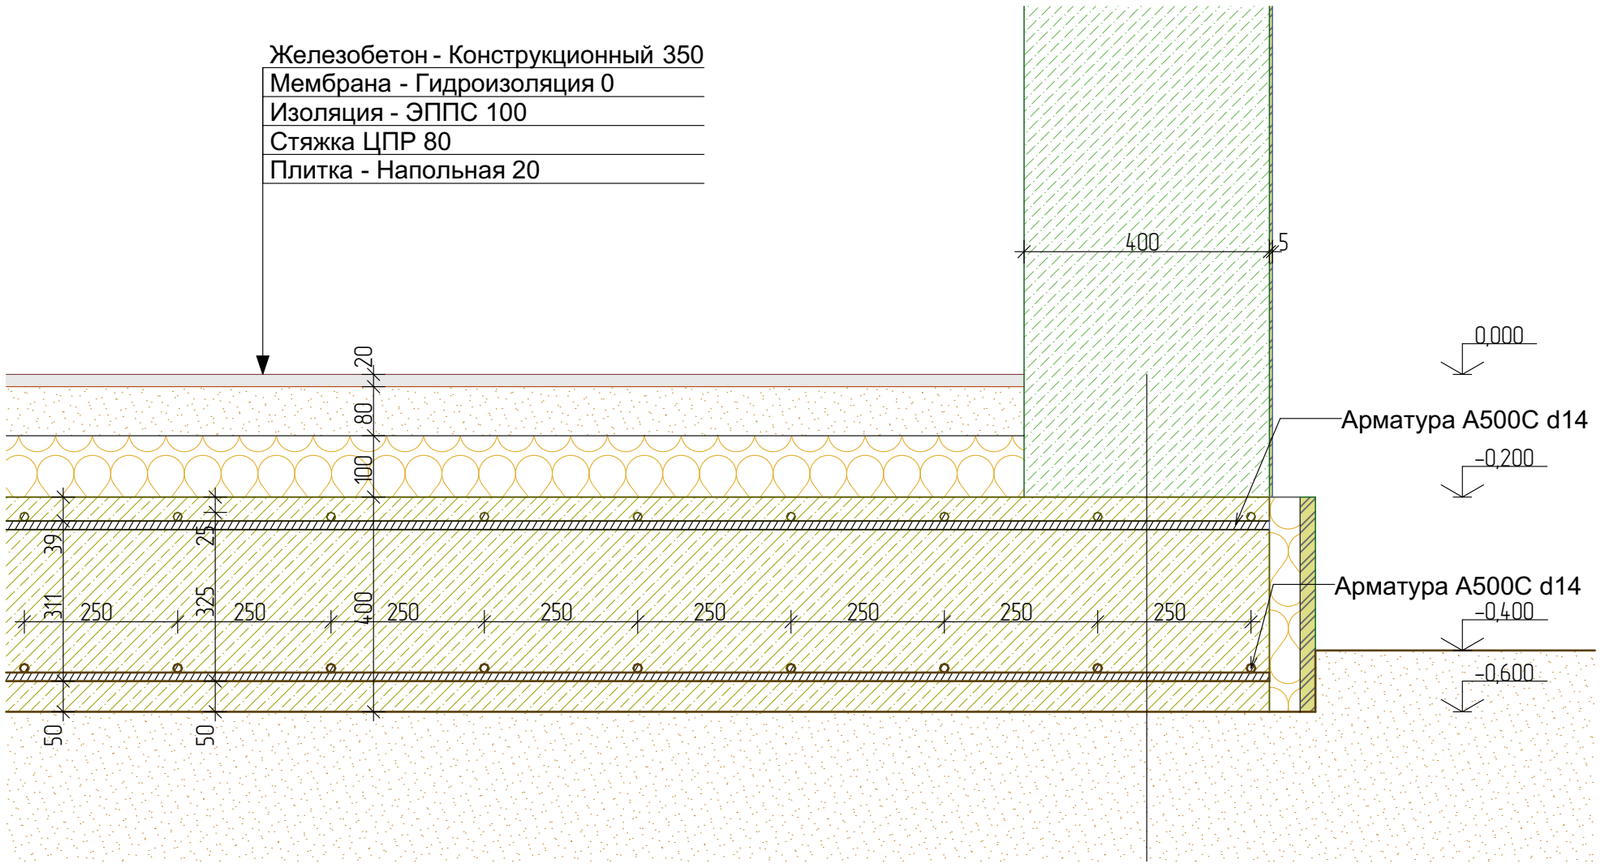



Изм.	Кол.уч.	Лист	№Док.	Подп.	Дата	
Разраб.		Салыкова Е.				

кадастровый номер 47:07:0157001:3873, Ленинградская область, Всеволожский муниципальный район, Агалатовское сельское поселение, территория "История Парк", улица Петровская, з/у №20 Россия

Индивидуальный жилой дом	Стадия	Лист	Листов
	ЭП	10	
Узел фундамента			

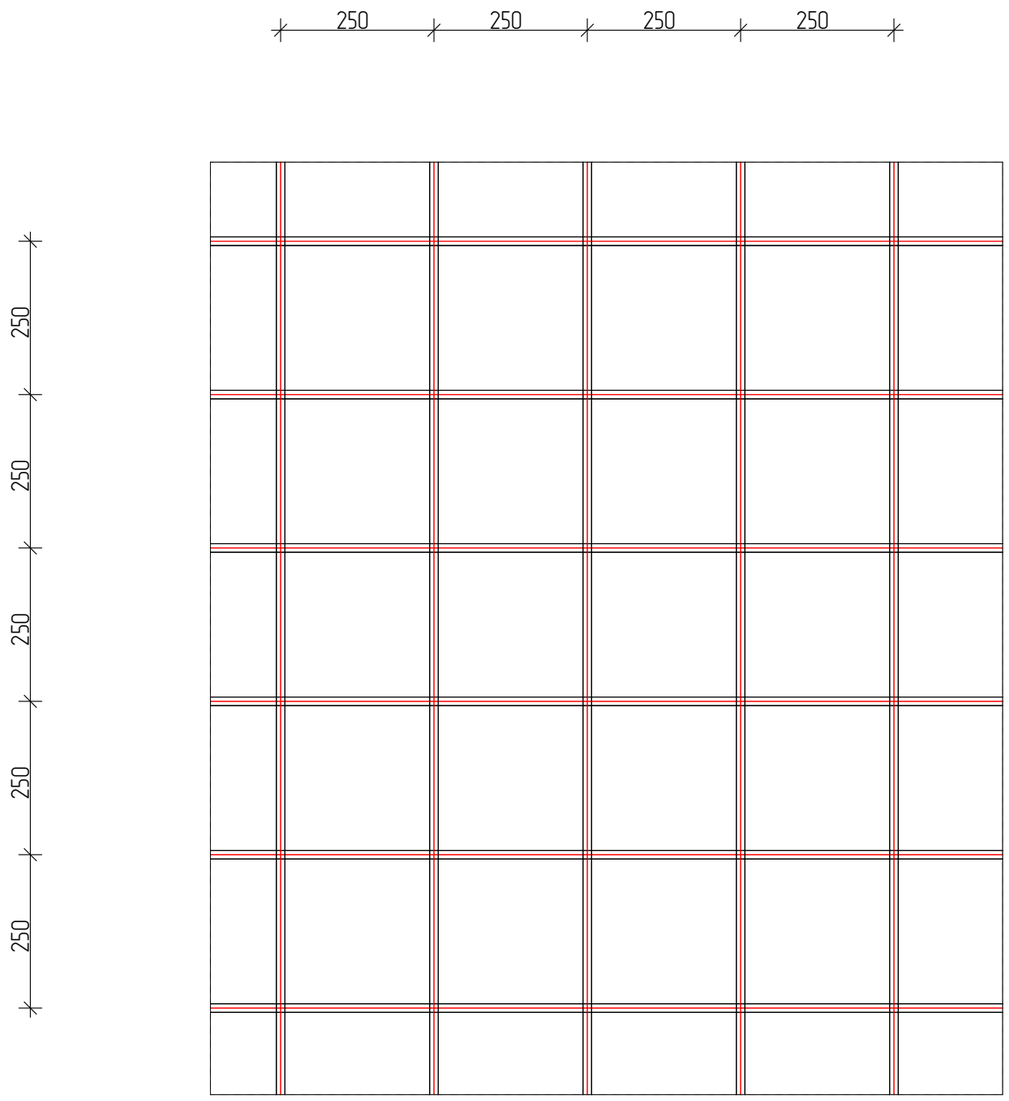

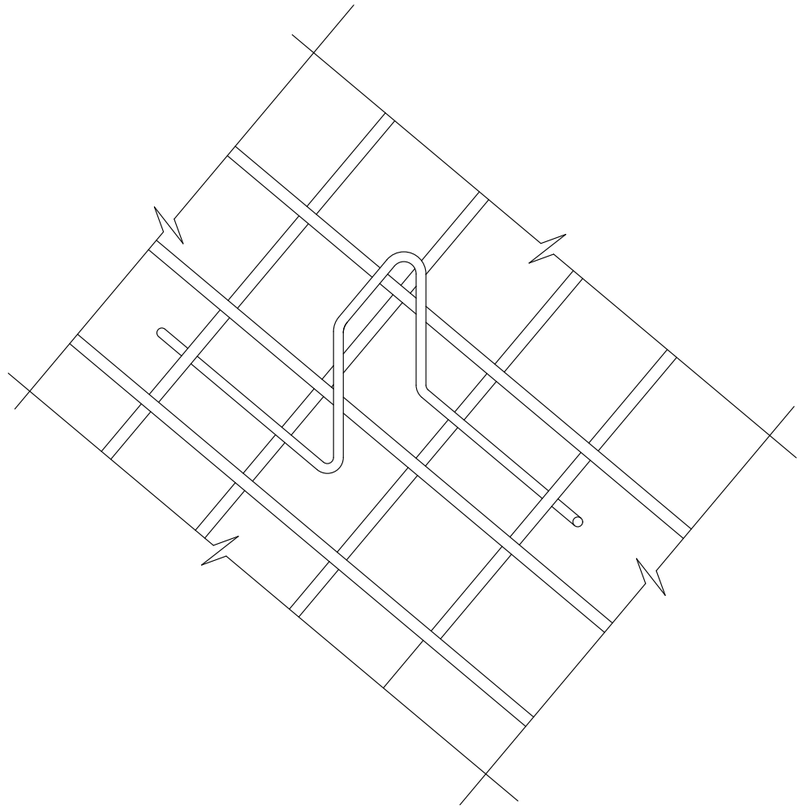

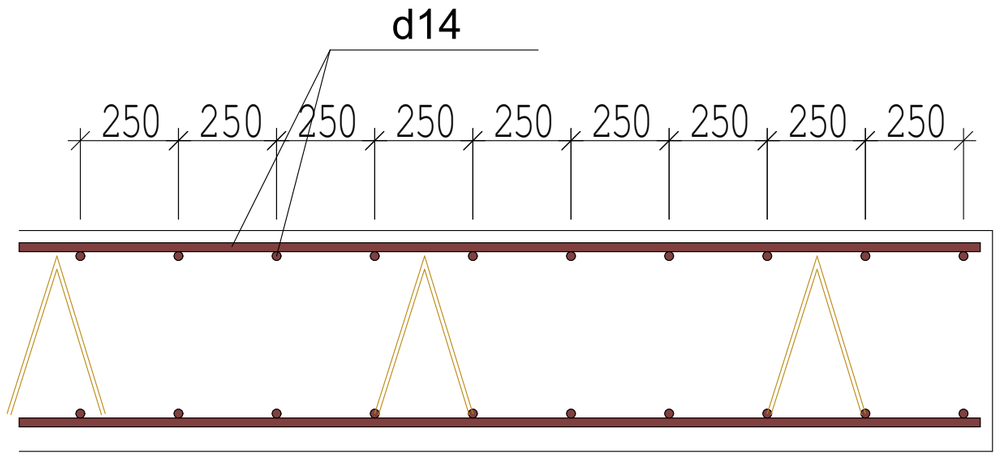

Спецификация элементов к фундаментной плите Фпм-1

МАРКА ПОЗ.	ОБОЗНАЧЕНИЕ	НАИМЕНОВАНИЕ	Кол.	МАССА, КГ	ПРИМЕ-ЧАНИЕ
		Детали			
1		Ø14AIII ГОСТ5781-82* п.м.	3413		
2		Ø8AI(A240) ГОСТ5781-82* l=370	35		


Изм.	Кол.уч.	Лист	№Док.	Подп.	Дата
Разраб.		Салыкова Е.			

кадастровый номер 47:07:0157001:3873, Ленинградская область, Всеволожский муниципальный район, Агалатовское сельское поселение, территория "История Парк", улица Петровская, з/у №20 Россия

Индивидуальный жилой дом


Стадия	Лист	Листов
ЭП	11	

Схема арматурного каркаса фундаментной плиты

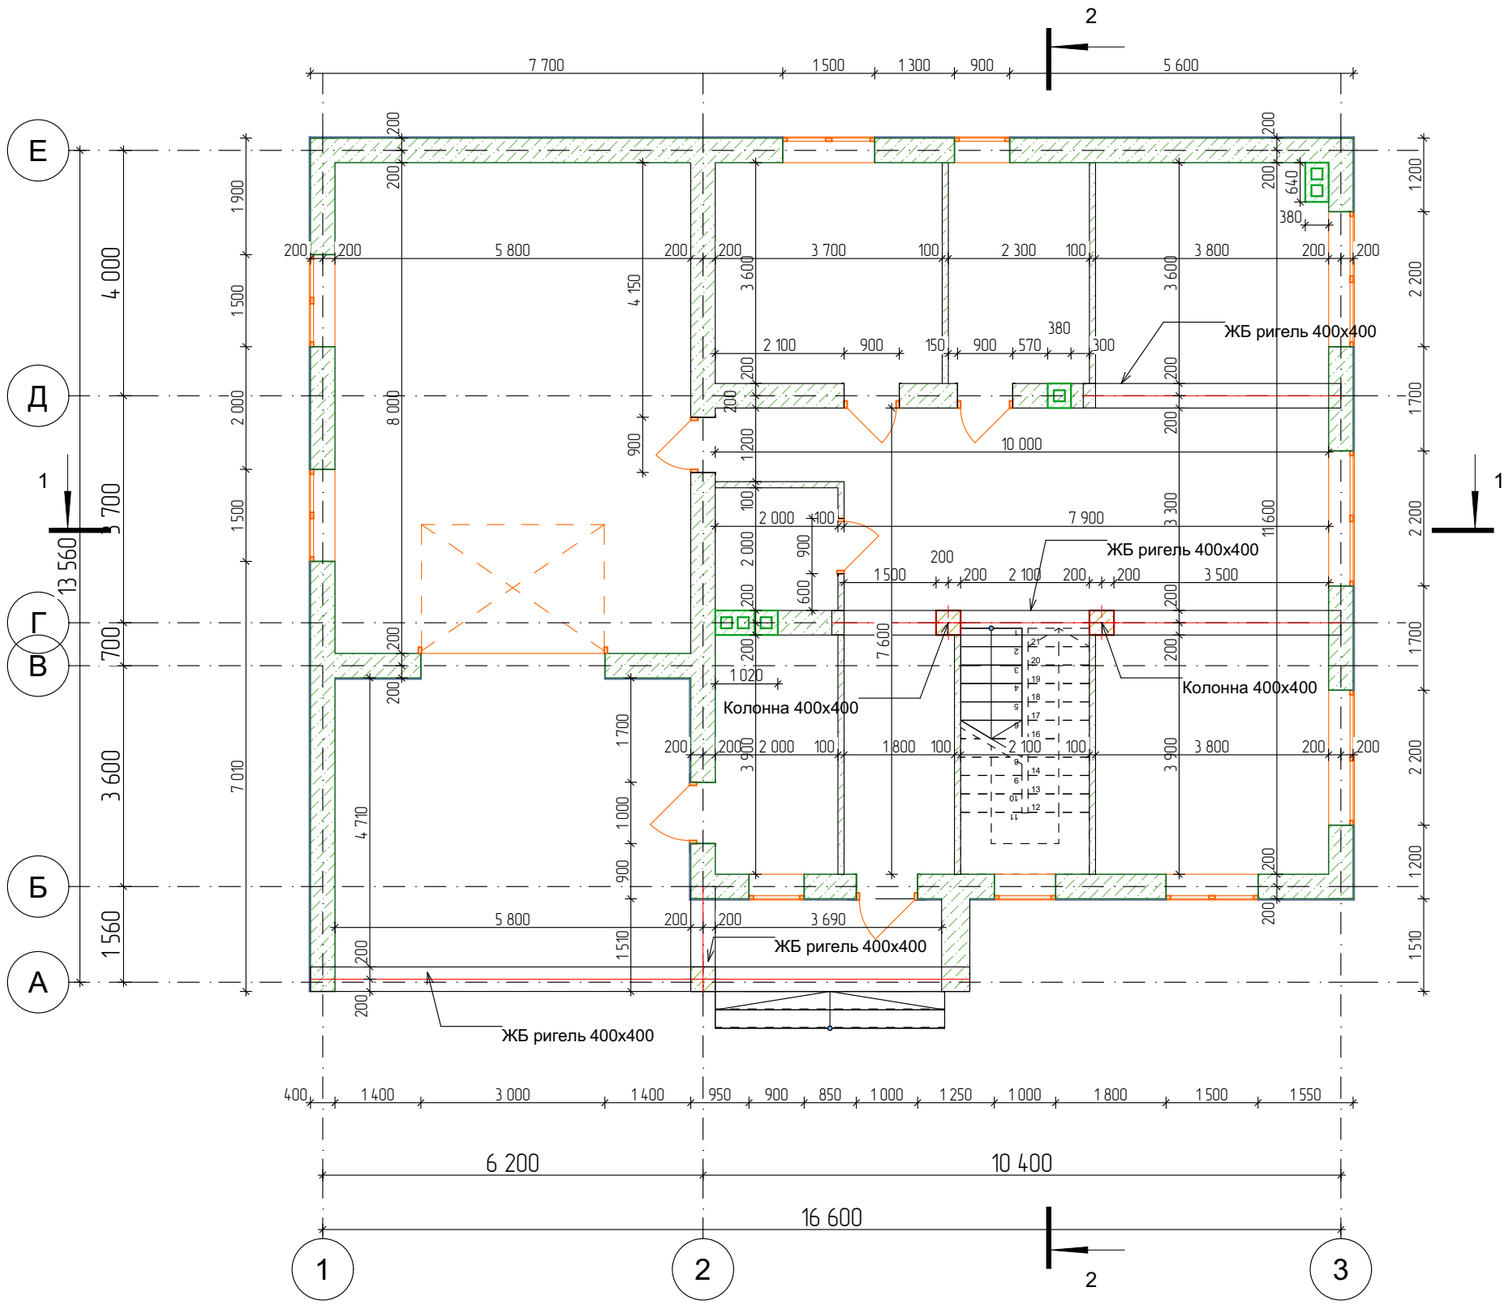

ВЕДОМОСТЬ БЛОКА ДЛЯ СТЕН	
ID Элемента	Объем, м3
Несущие 400мм	179,79
Перегородки 100мм	13,83


Изм.	Кол.уч.	Лист	№Док.	Подп.	Дата	кадастровый номер 47:07:0157001:3873, Ленинградская область, Всеволожский муниципальный район, Агалатовское сельское поселение, территория "История Парк", улица Петровская, з/у №20 Россия			
Разраб.		Салыкова Е.				Индивидуальный жилой дом	Стадия	Лист	Листов
							ЭП	12	
						План 1 этажа			

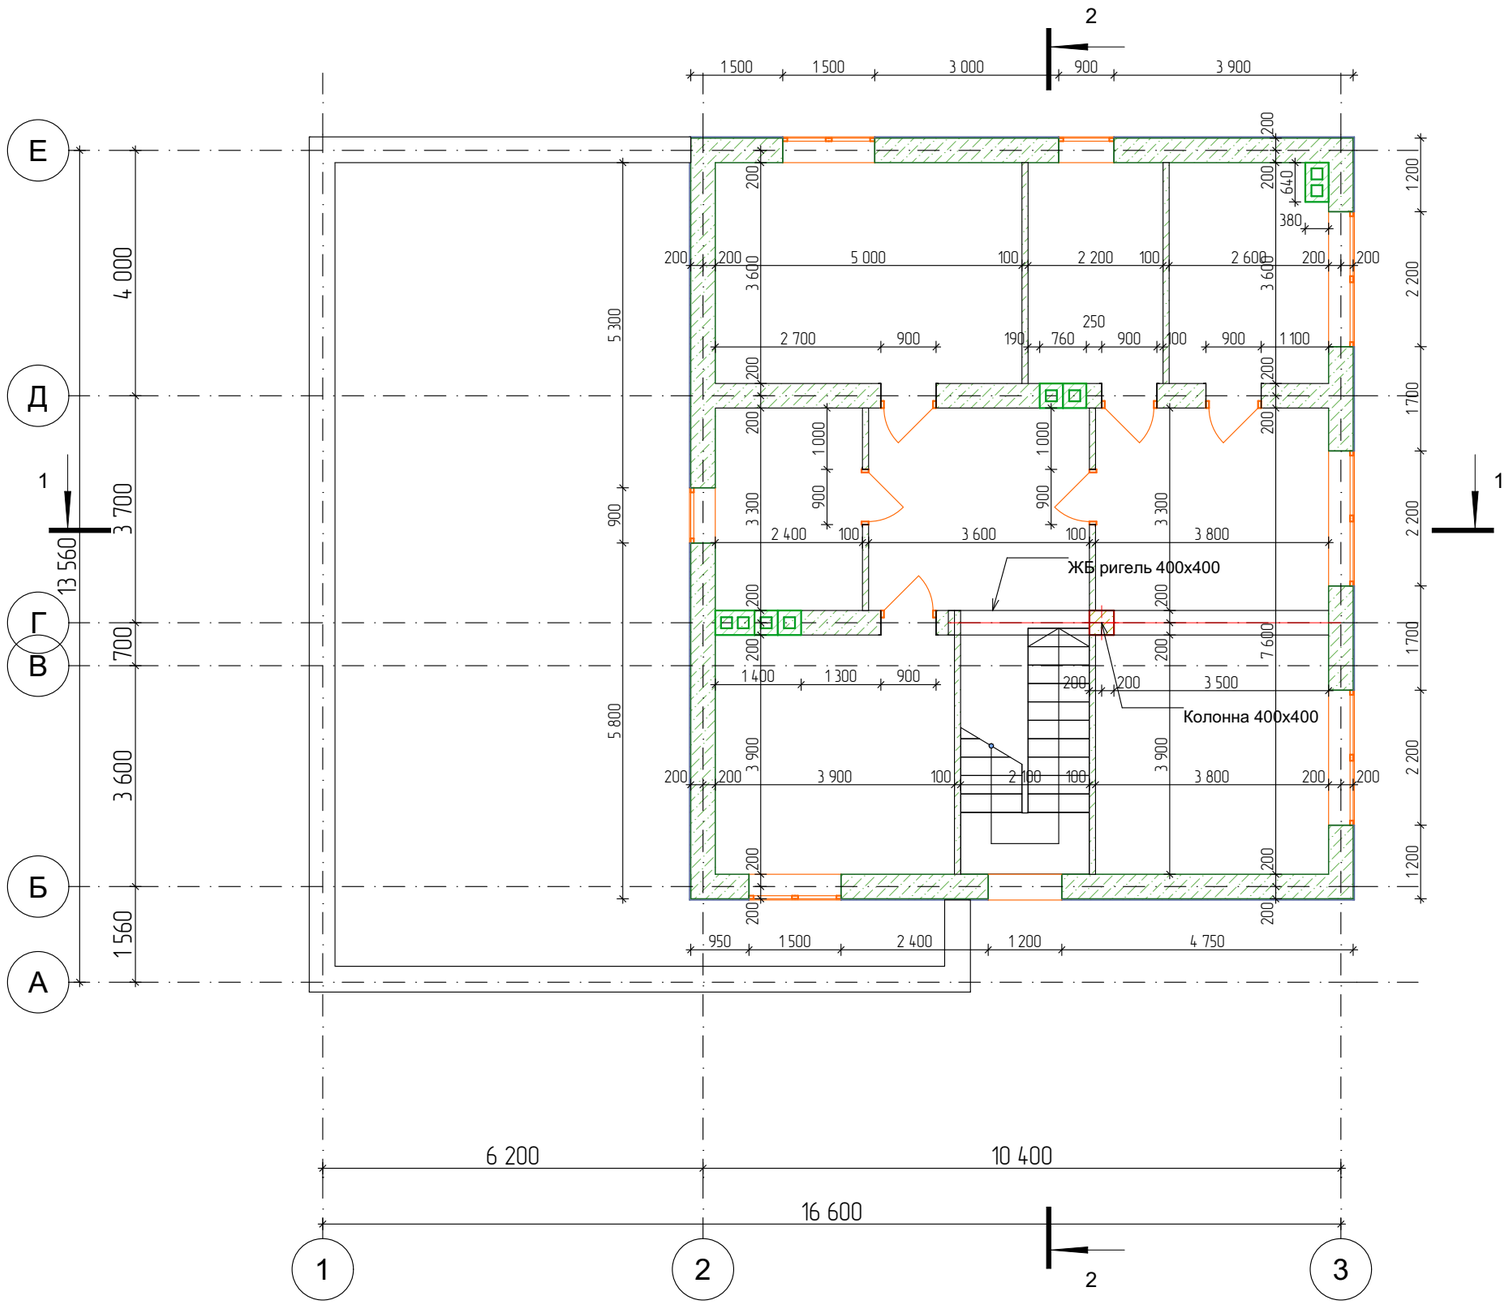

Изм.	Кол.уч.	Лист	№Док.	Подп.	Дата	
Разраб.		Салыкова Е.				

кадастровый номер 47:07:0157001:3873, Ленинградская область, Всеволожский муниципальный район, Агалатовское сельское поселение, территория "История Парк", улица Петровская, з/у №20 Россия


	Стадия	Лист	Листов
Индивидуальный жилой дом	ЭП	13	
План 2 этажа			

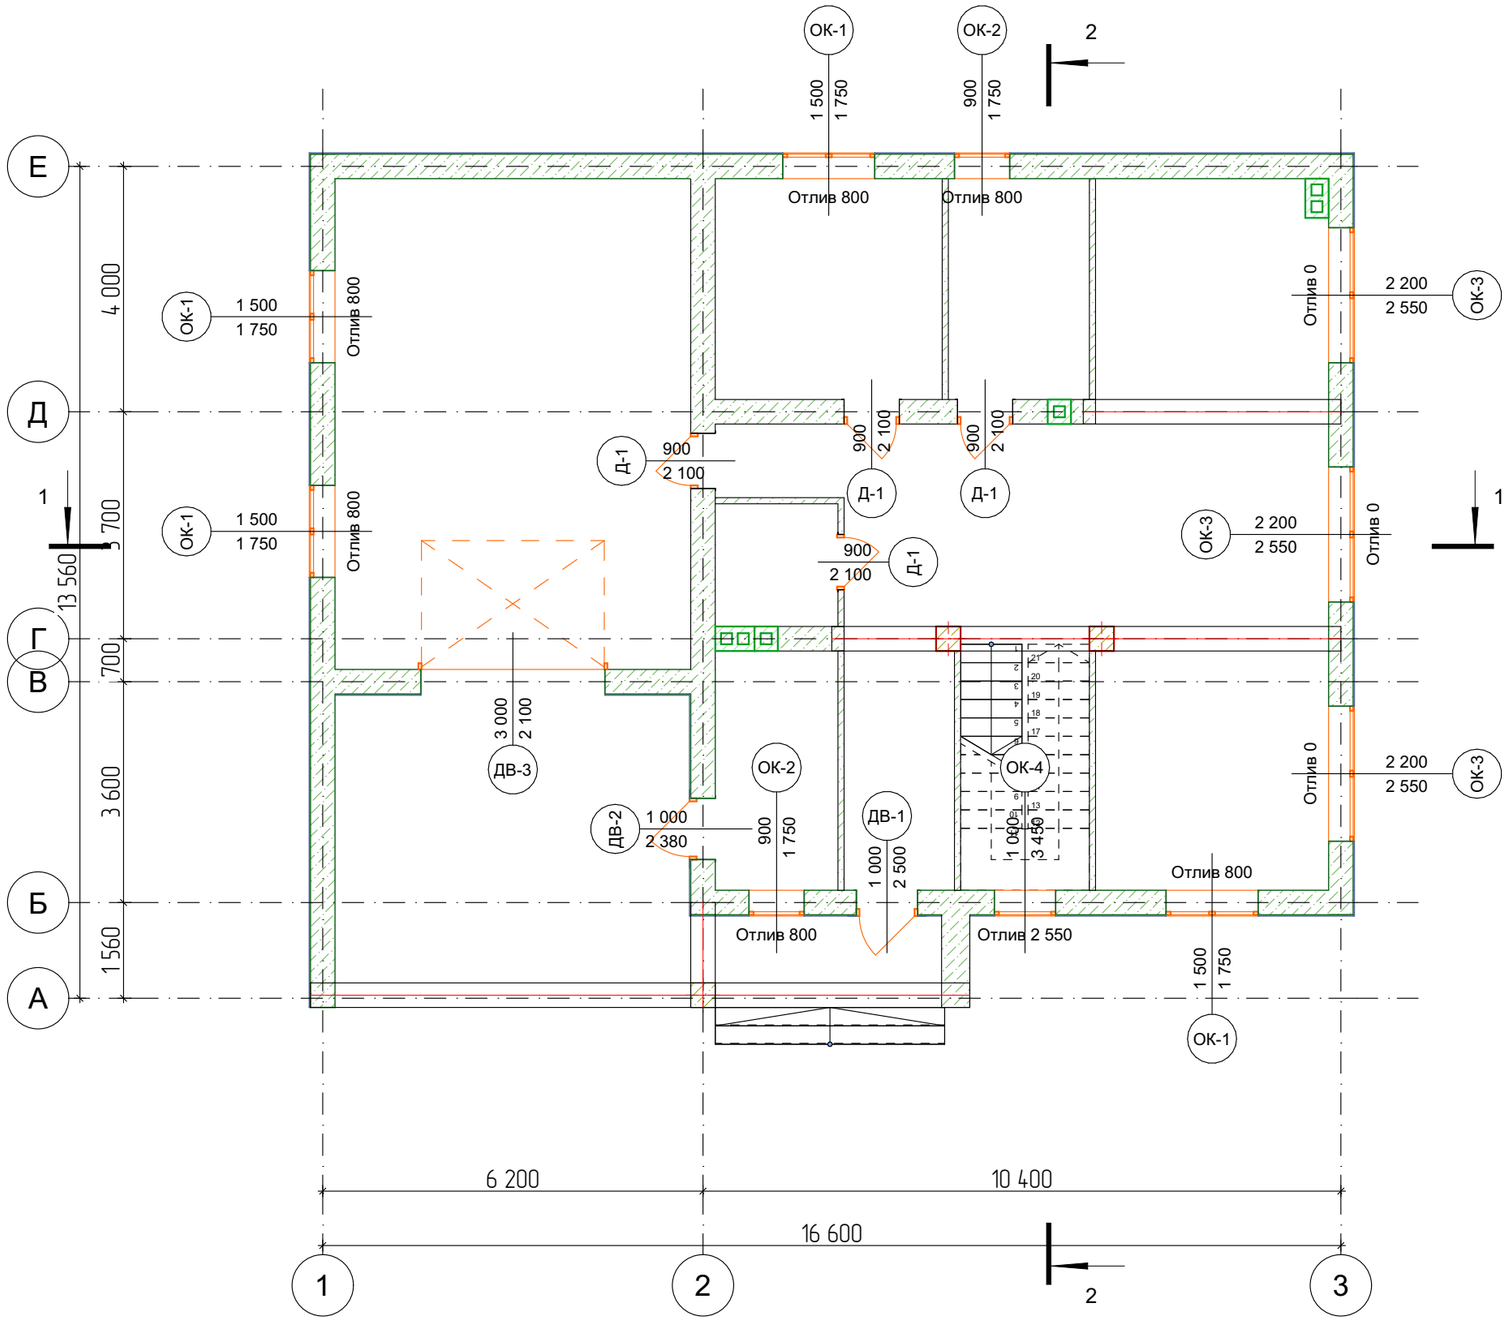

Изм.	Кол.уч.	Лист	№Док.	Подп.	Дата	
Разраб.		Салыкова В.				

кадастровый номер 47:07:0157001:3873, Ленинградская область, Всеволожский муниципальный район, Агалатовское сельское поселение, территория "История Парк", улица Петровская, з/у №20 Россия

Индивидуальный жилой дом	Стадия	Лист	Листов
	ЭП	14	
Маркировочный план 1 этаж			



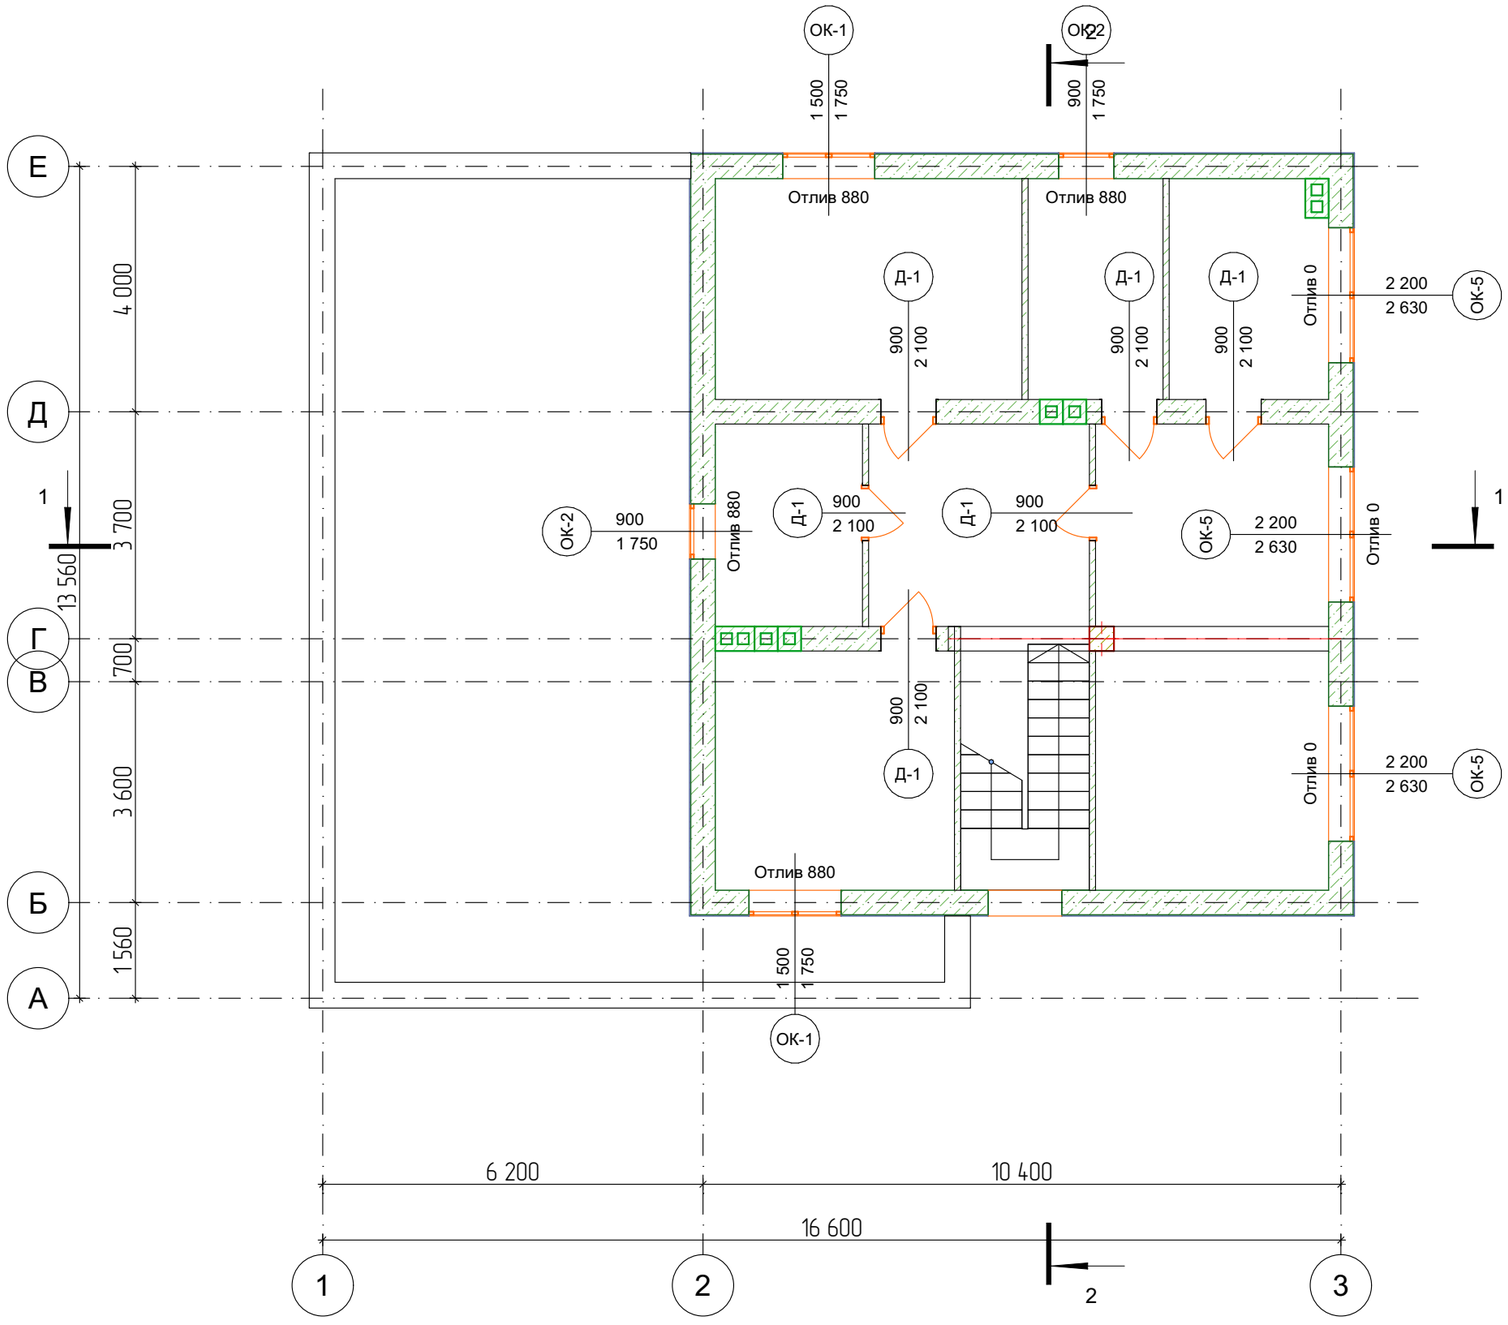


Изм.	Кол.уч.	Лист	№Док.	Подп.	Дата	
Разраб.		Салыкова В.				

кадастровый номер 47:07:0157001:3873, Ленинградская область, Всеволожский муниципальный район, Агалатовское сельское поселение, территория "История Парк", улица Петровская, з/у №20 Россия





Индивидуальный жилой дом	Стадия	Лист	Листов
	ЭП	15	
Маркировочный план 2 этаж			

Каталог Дверей

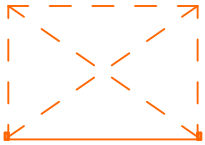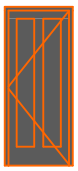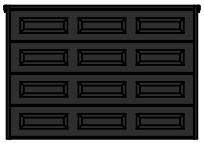
Полный ID Элемента	Д-1	ДВ-1	ДВ-2	ДВ-3
D по Классификации	Дверь -1	Дверь -1	Дверь -2	Дверь -3
Наименование Двери	Однопольная Дверь 27	Однопольная Дверь с Фрамугой 27	Однопольная Дверь с Фрамугой 27	Ворота Гаражные Подъемные 27
Количество	10	1	1	1
Размер Ш x В	900×2 100	1 000×2 500	1 000×2 380	3 000×2 100
2D-символ				
Вид со Стороны, Противоположной Стороне Открывания				

Изм.	Кол.уч.	Лист	№Док.	Подп.	Дата	кадастровый номер 47:07:0157001:3873, Ленинградская область, Всеволожский муниципальный район, Агалатовское сельское поселение, территория "История Парк", улица Петровская, з/у №20 Россия			
Разраб.		Григорян Е.				Индивидуальный жилой дом	Стадия	Лист	Листов
							ЭП	16	
		Григорян Е.				Каталог дверных проемов			

Каталог Окон

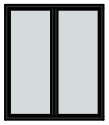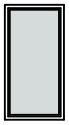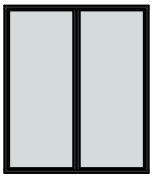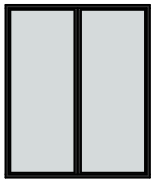Полный ID Элемента	ОК-1	ОК-2	ОК-3	ОК-4	ОК-5
Наименование Окна	Раздвижное Двустворчатое Окно 27	Окно 27	Раздвижное Двустворчатое Окно 27	Окно 27	Раздвижное Двустворчатое Окно 27
Количество	6	4	3	1	3
Размер Ш x В	1 500×1 750	900×1 750	2 200×2 550	1 000×3 450	2 200×2 630
2D-символ					
Вид со Стороны, Противоположной Стороне Открывания					


Изм.	Кол.уч.	Лист	№Док.	Подп.	Дата	кадастровый номер 47:07:0157001:3873, Ленинградская область, Всеволожский муниципальный район, Агалатовское сельское поселение, территория "История Парк", улица Петровская, з/у №20 Россия			
Разраб.		Григорян Е.				Индивидуальный жилой дом	Стадия	Лист	Листов
							ЭП	17	
		Григорян Е.				Каталог оконных проемов			

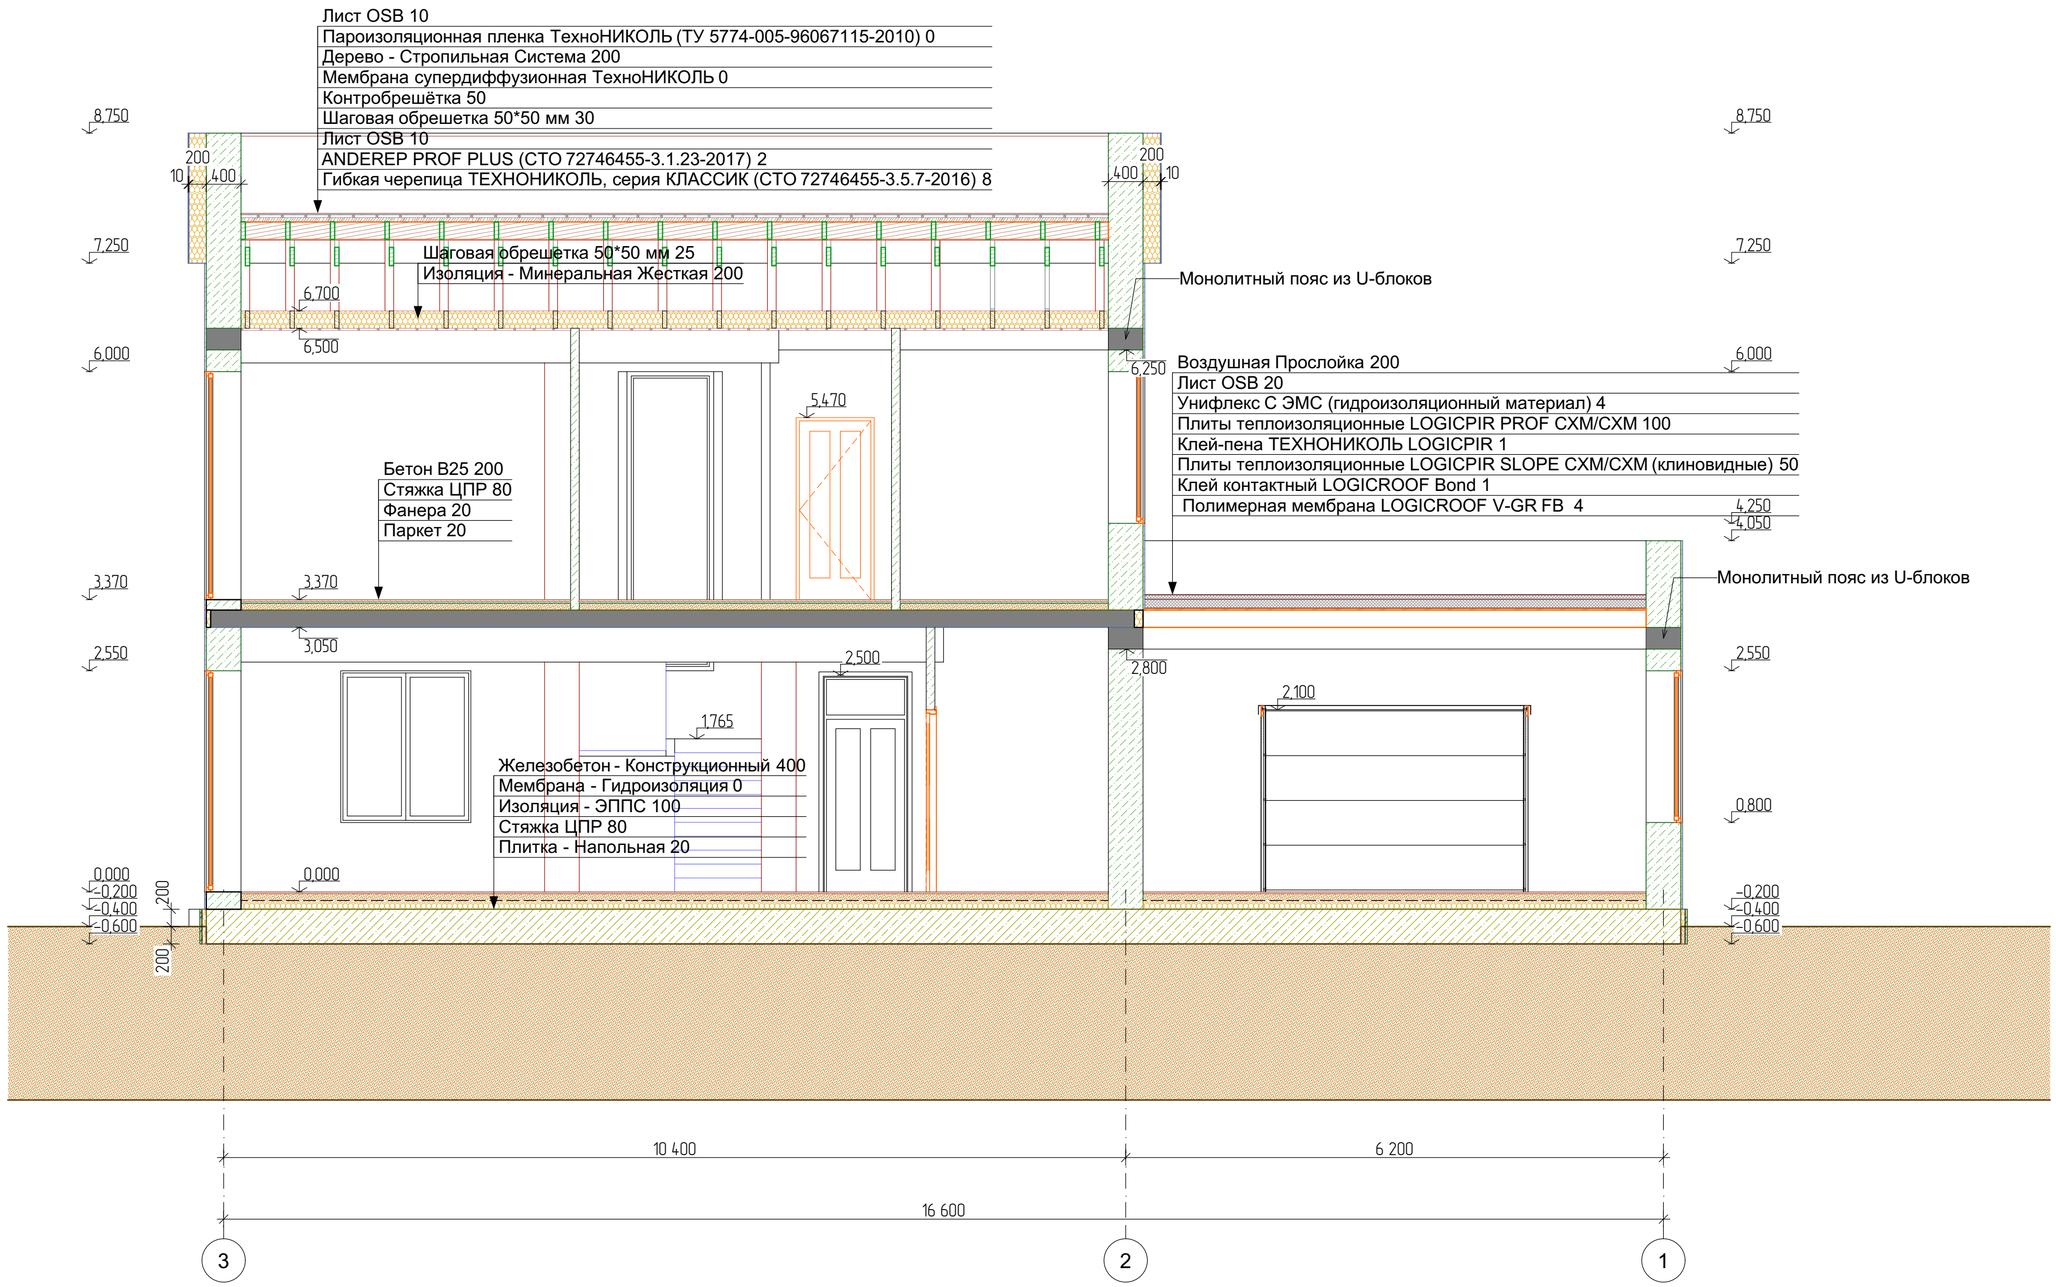

Изм.	Кол.уч.	Лист	№Док.	Подп.	Дата		
Разраб.		Салыкова	В.				

кадастровый номер 47:07:0157001:3873, Ленинградская область, Всеволожский муниципальный район, Агалатовское сельское поселение, территория "История Парк", улица Петровская, з/у №20 Россия


Индивидуальный жилой дом	Стадия	Лист	Листов
	ЭП	18	
Разрез 1 - 1			

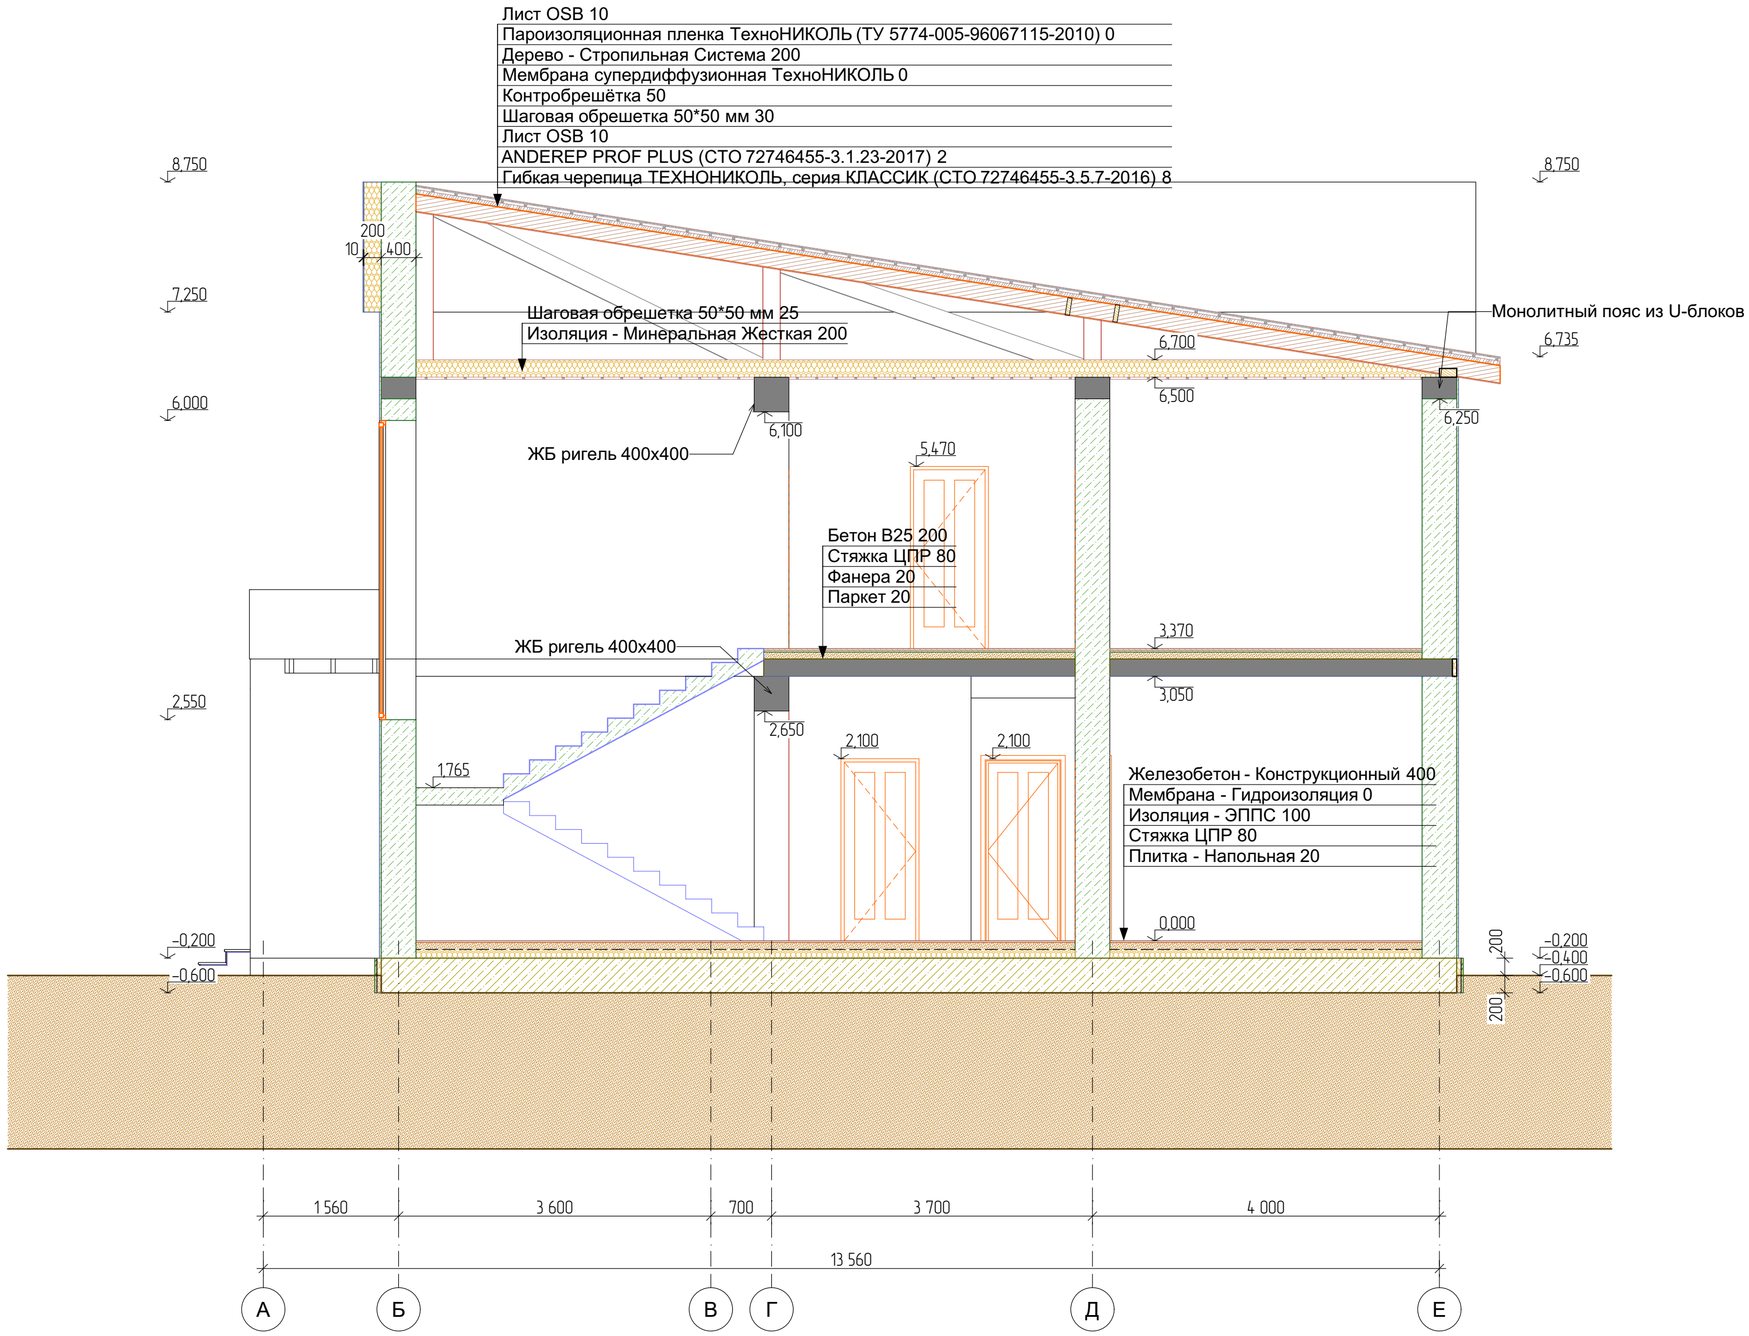


Изм.	Колуч.	Лист	№Док.	Подп.	Дата	
Разраб.		Салыкова	В.			

кадастровый номер 47:07:0157001:3873, Ленинградская область, Всеволожский муниципальный район, Агалатовское сельское поселение, территория "История Парк", улица Петровская, з/у №20 Россия

Индивидуальный жилой дом	Стадия	Лист	Листов
	ЭП	19	
Разрез 2 - 2			

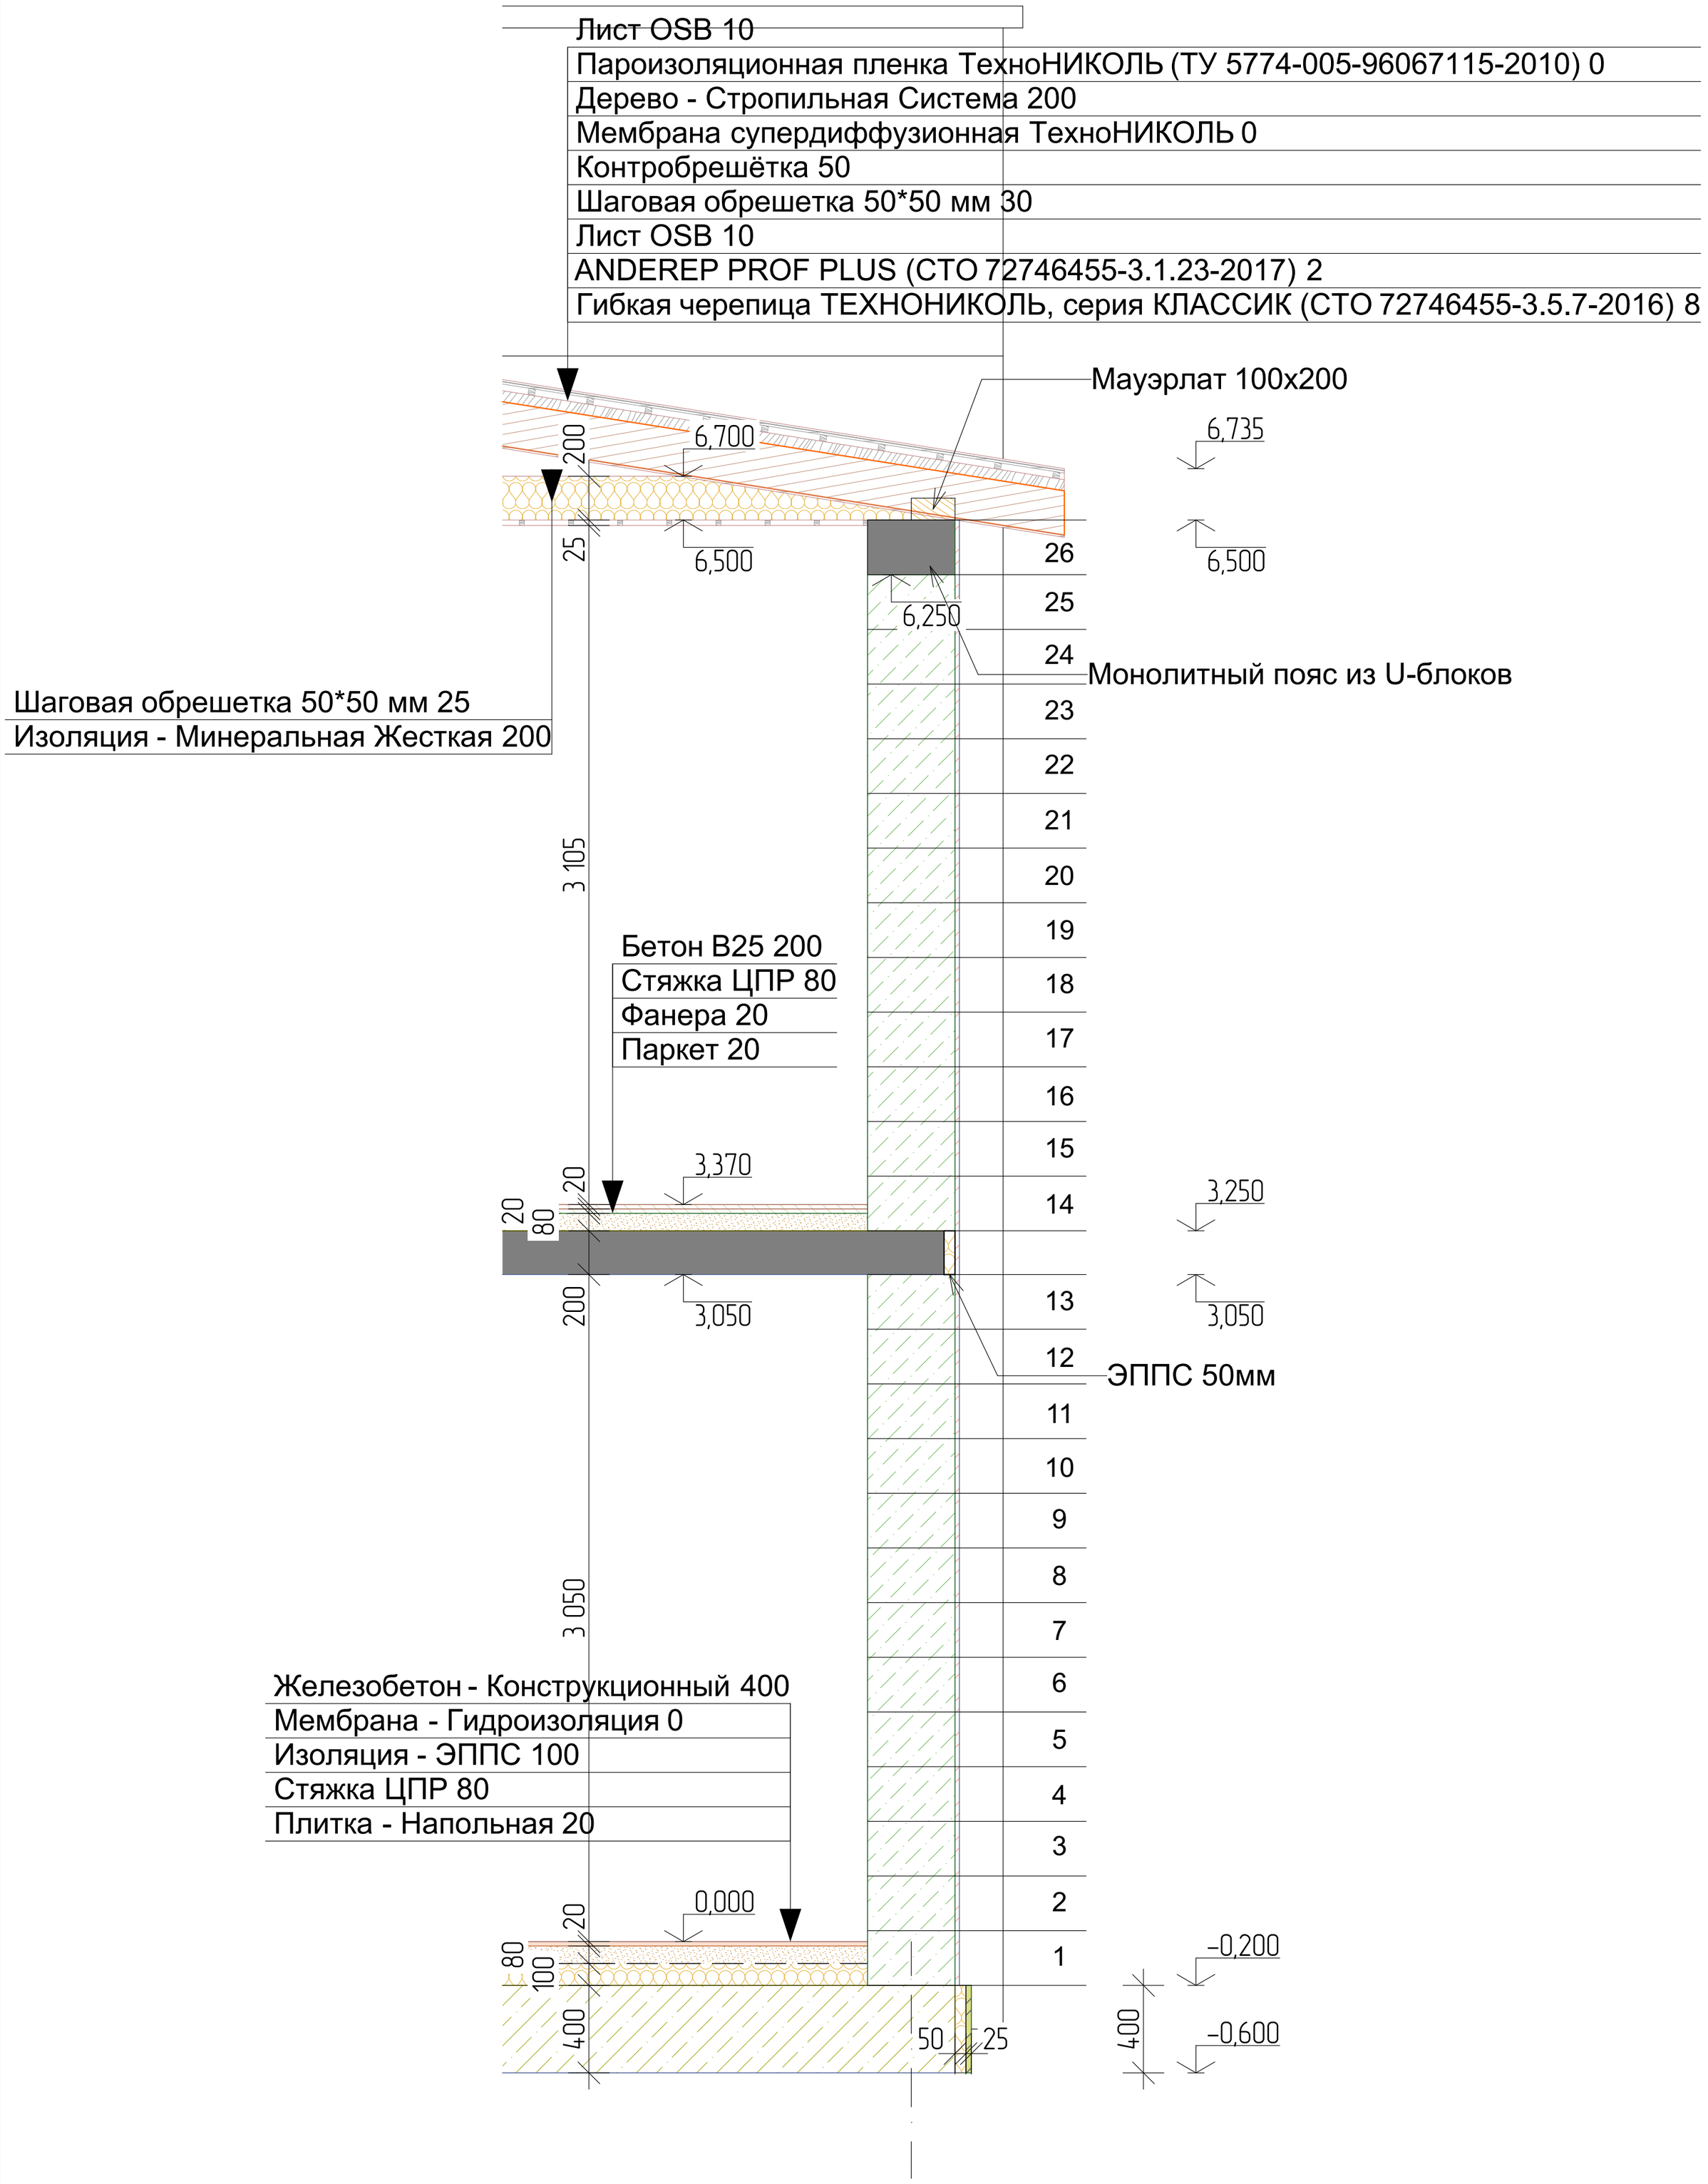


Изм.	Кол.уч.	Лист	№Док.	Подп.	Дата	кадастровый номер 47:07:0157001:3873, Ленинградская область, Всеволожский муниципальный район, Агалатовское сельское поселение, территория "История Парк", улица Петровская, з/у №20 Россия			
Разраб.		Салыкова Е.				Индивидуальный жилой дом	Стадия	Лист	Листов
							ЭП	20	
						Разрез по стене			

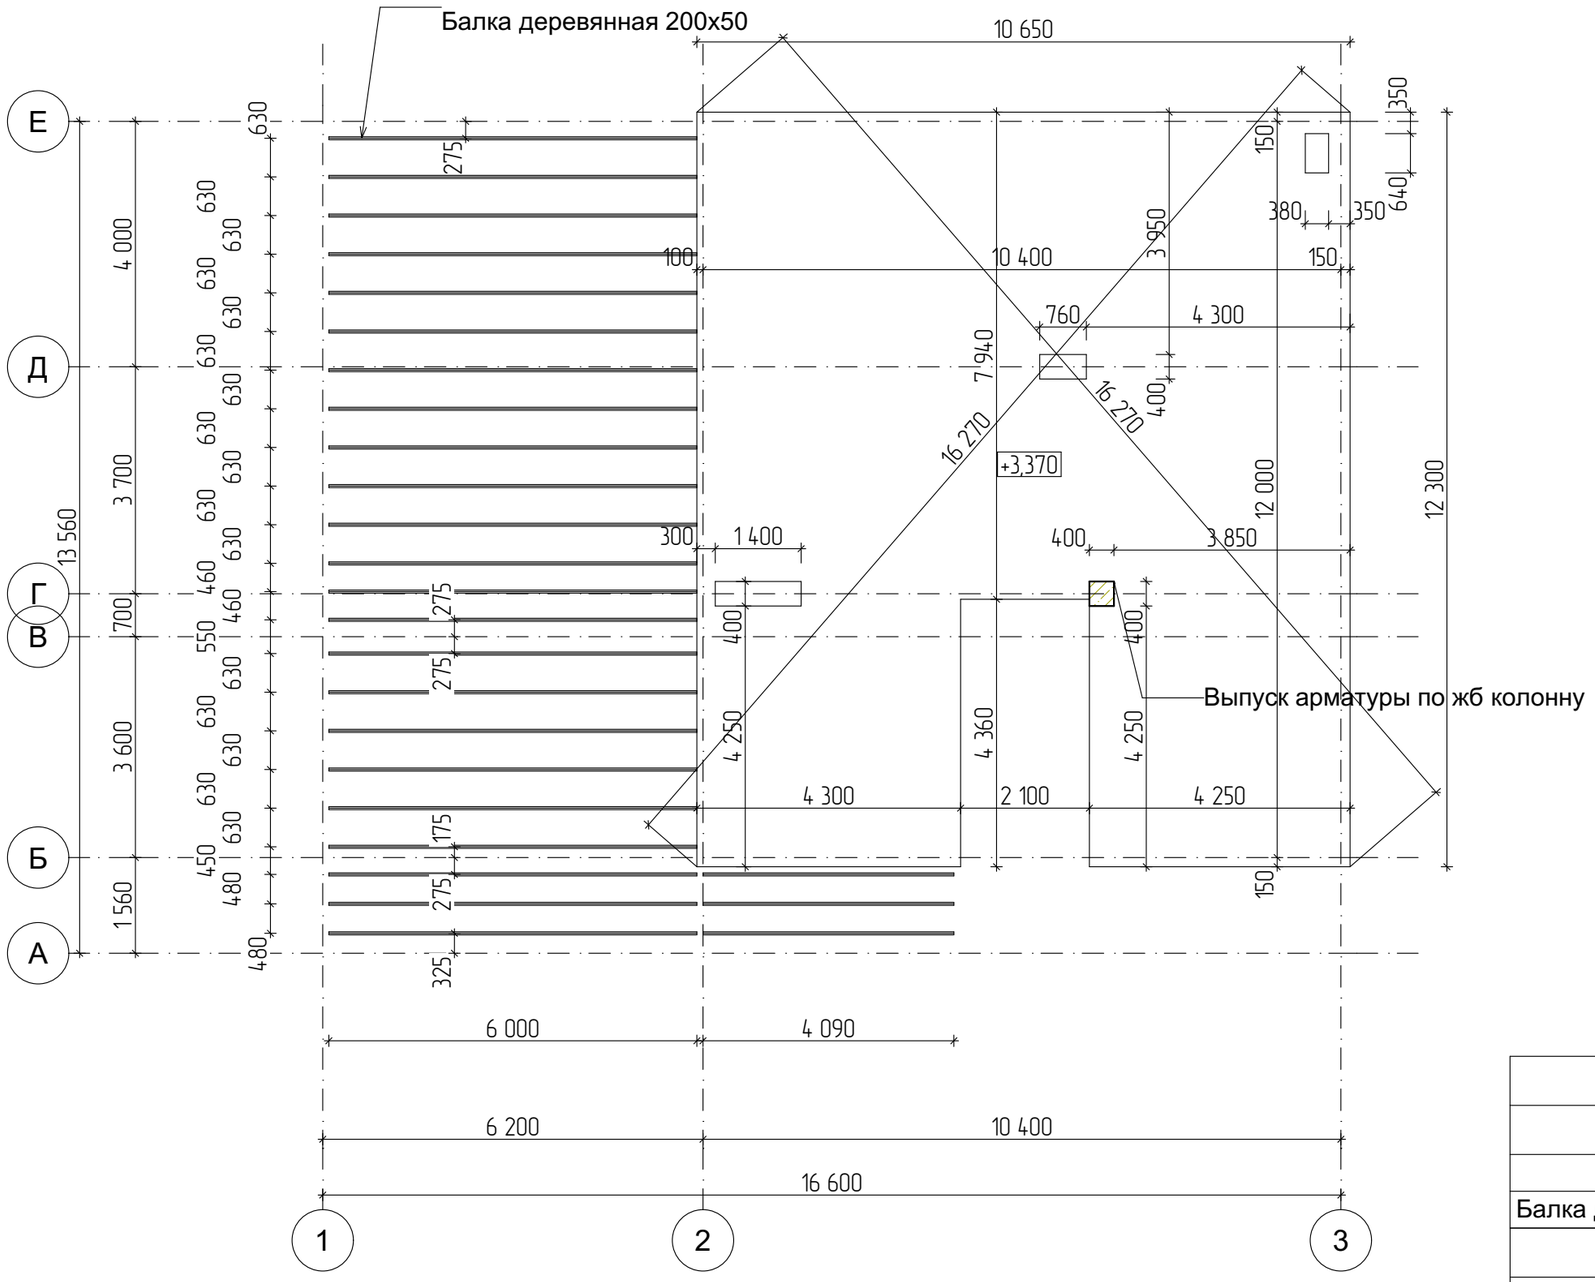

ИКК-03 Ведомость перекрытий 1	
Наименование	Объем

Балка деревянная 200х50	1,50
ВЕДОМОСТЬ ПЕРЕКРЫТИЯ	
Наименование	Объем
Монолитное перекрытие	24,37

Изм.	Кол.уч.	Лист	№Док.	Подп.	Дата	кадастровый номер 47:07:0157001:3873, Ленинградская область, Всеволожский муниципальный район, Агалатовское сельское поселение, территория "История Парк", улица Петровская, з/у №20 Россия			
Разраб.		Салыкова Е.				Индивидуальный жилой дом	Стадия	Лист	Листов
							ЭП	21	
						План перекрытия на отм+3,050			

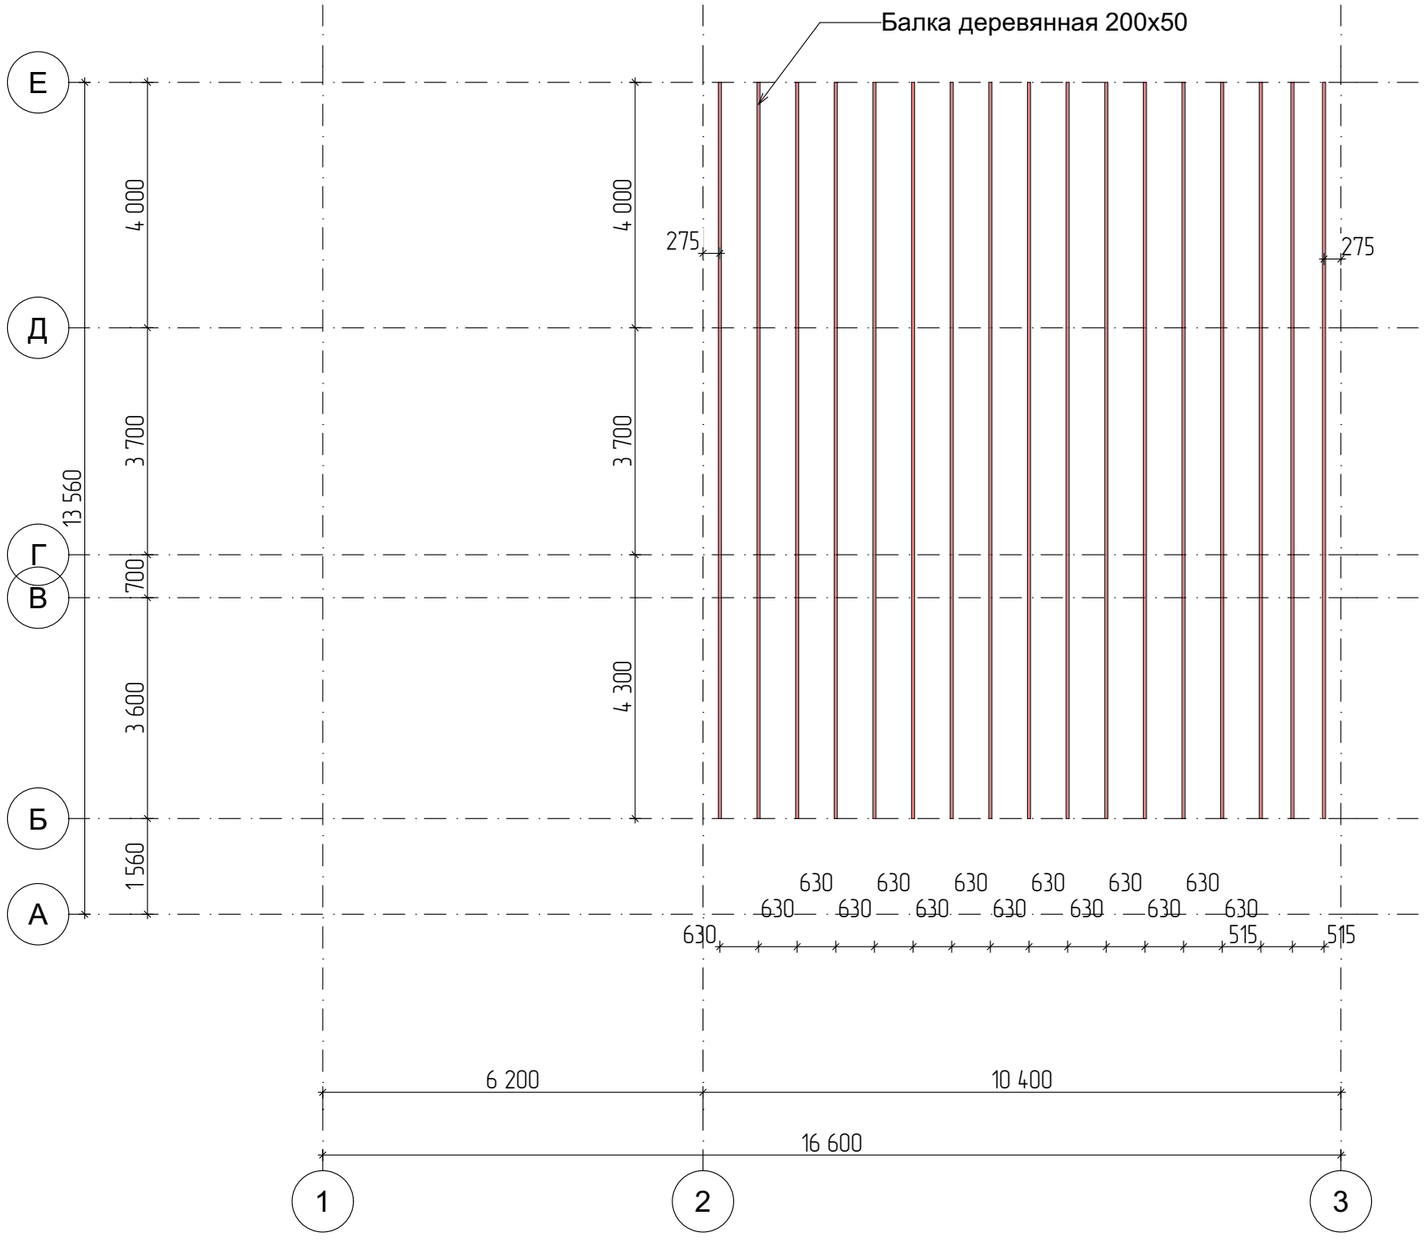


Ведомость перекрытия

Наименование	Объем

Балка деревянная 200х50	2,04

Изм.	Кол.уч.	Лист	№Док.	Подп.	Дата	
						кадастровый номер 47:07:0157001:3873, Ленинградская область, Всеволожский муниципальный район, Агалатовское сельское поселение, территория "История Парк", улица Петровская, з/у №20 Россия
Разраб.		Салыкова Е.				Индивидуальный жилой дом
						План перекрытий на отм 6,500

Стадия	Лист	Листов
ЭП	22	

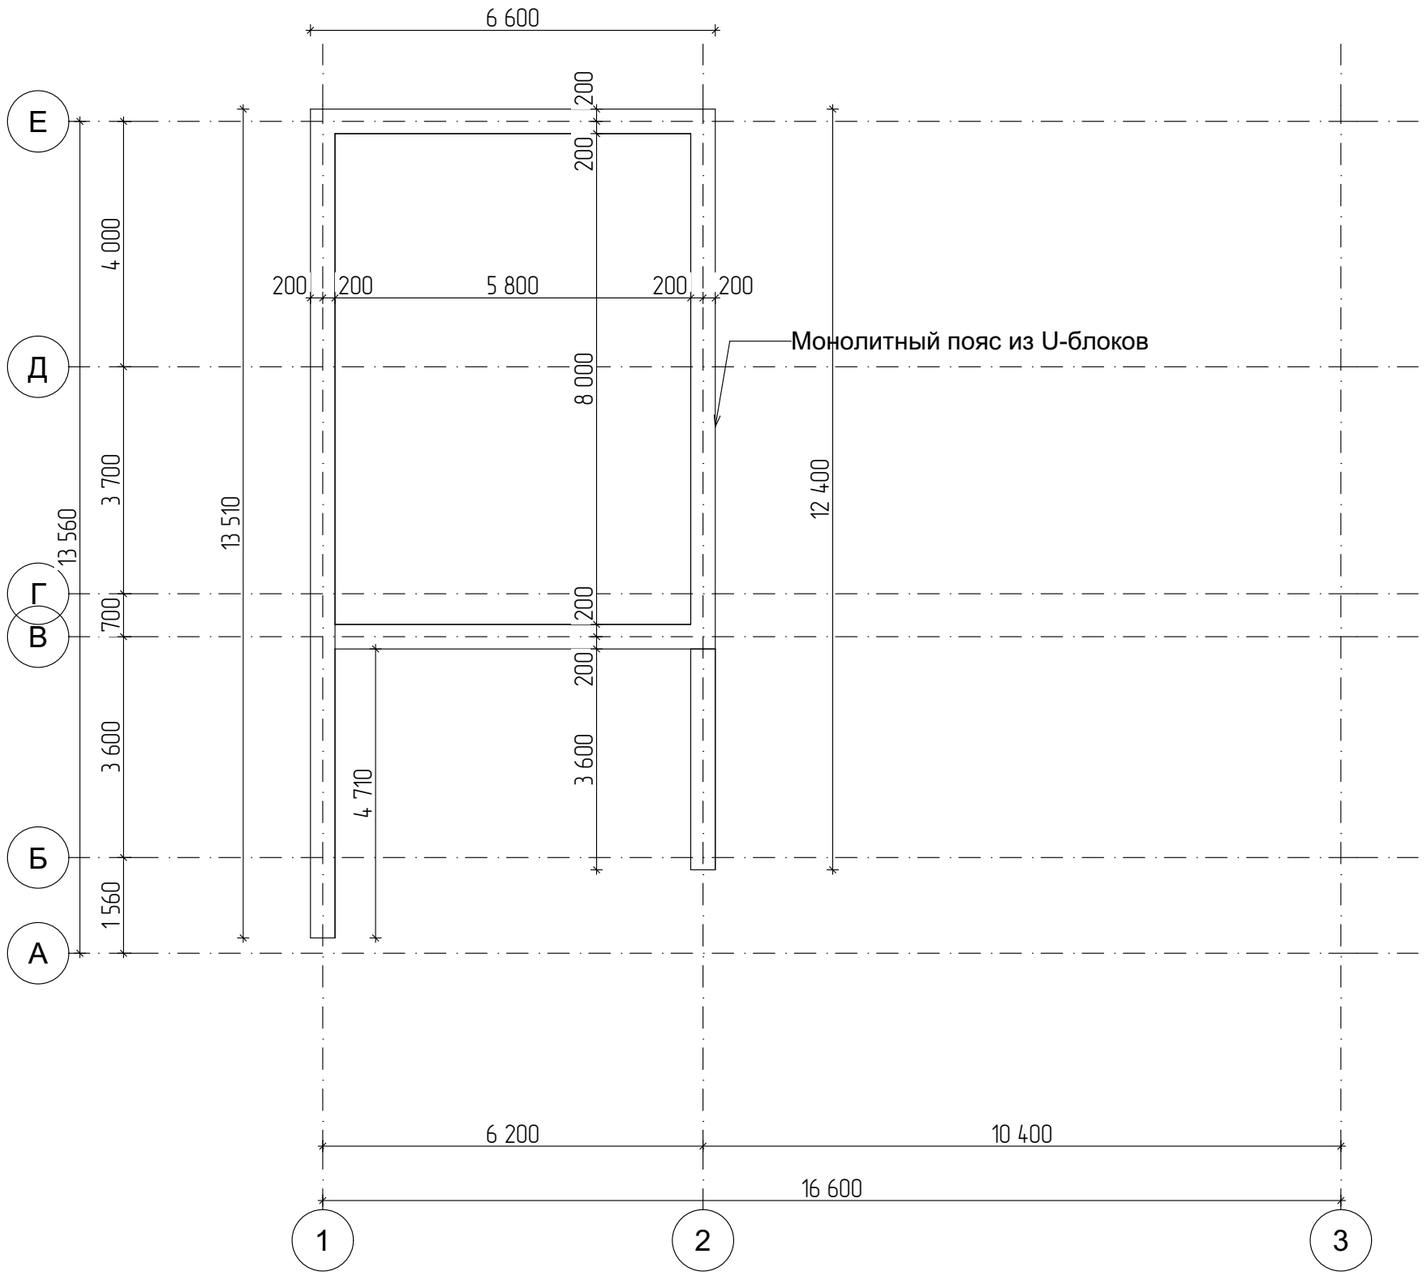


ВЕДОМОСТЬ НА МОНОЛИТНЫЙ ПОЯС 1-ГО ЭТАЖА

Наименование	Объем, м3
	3,75
Монолитный пояс из U-блоков	3,75

Изм.	Кол.уч.	Лист	№Док.	Подп.	Дата	
						кадастровый номер 47:07:0157001:3873, Ленинградская область, Всеволожский муниципальный район, Агалатовское сельское поселение, территория "История Парк", улица Петровская, з/у №20 Россия
Разраб.		Салыкова Е.				Индивидуальный жилой дом
						Монолитный пояс на отм 2,800

Стадия	Лист	Листов
ЭП	23	

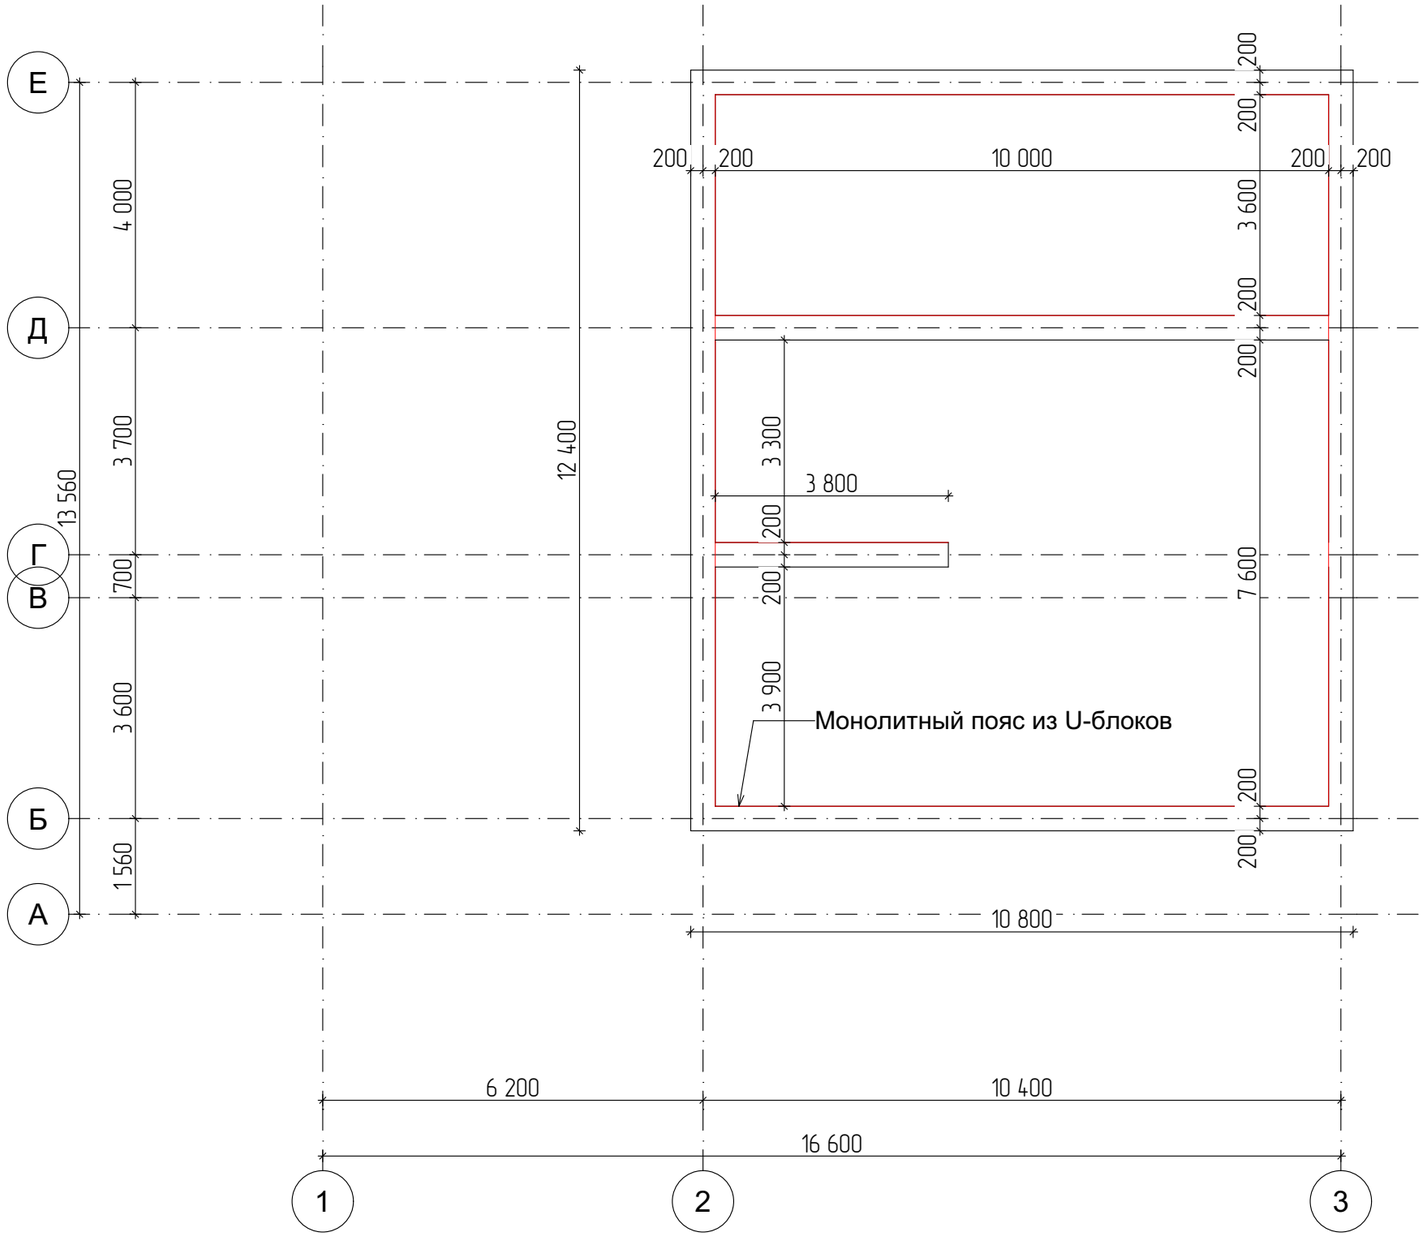


ВЕДОМОСТЬ НА МОНОЛИТНЫЙ ПОЯС 2-ГО ЭТАЖА

Наименование	Объем, м3
	5,86
Монолитный пояс из U-блоков	5,86

Изм.	Кол.уч.	Лист	№Док.	Подп.	Дата	
						кадастровый номер 47:07:0157001:3873, Ленинградская область, Всеволожский муниципальный район, Агалатовское сельское поселение, территория "История Парк", улица Петровская, з/у №20 Россия
Разраб.		Салыкова Е.				Индивидуальный жилой дом
						Монолитный пояс на отм 6,250


Стадия	Лист	Листов
ЭП	24	

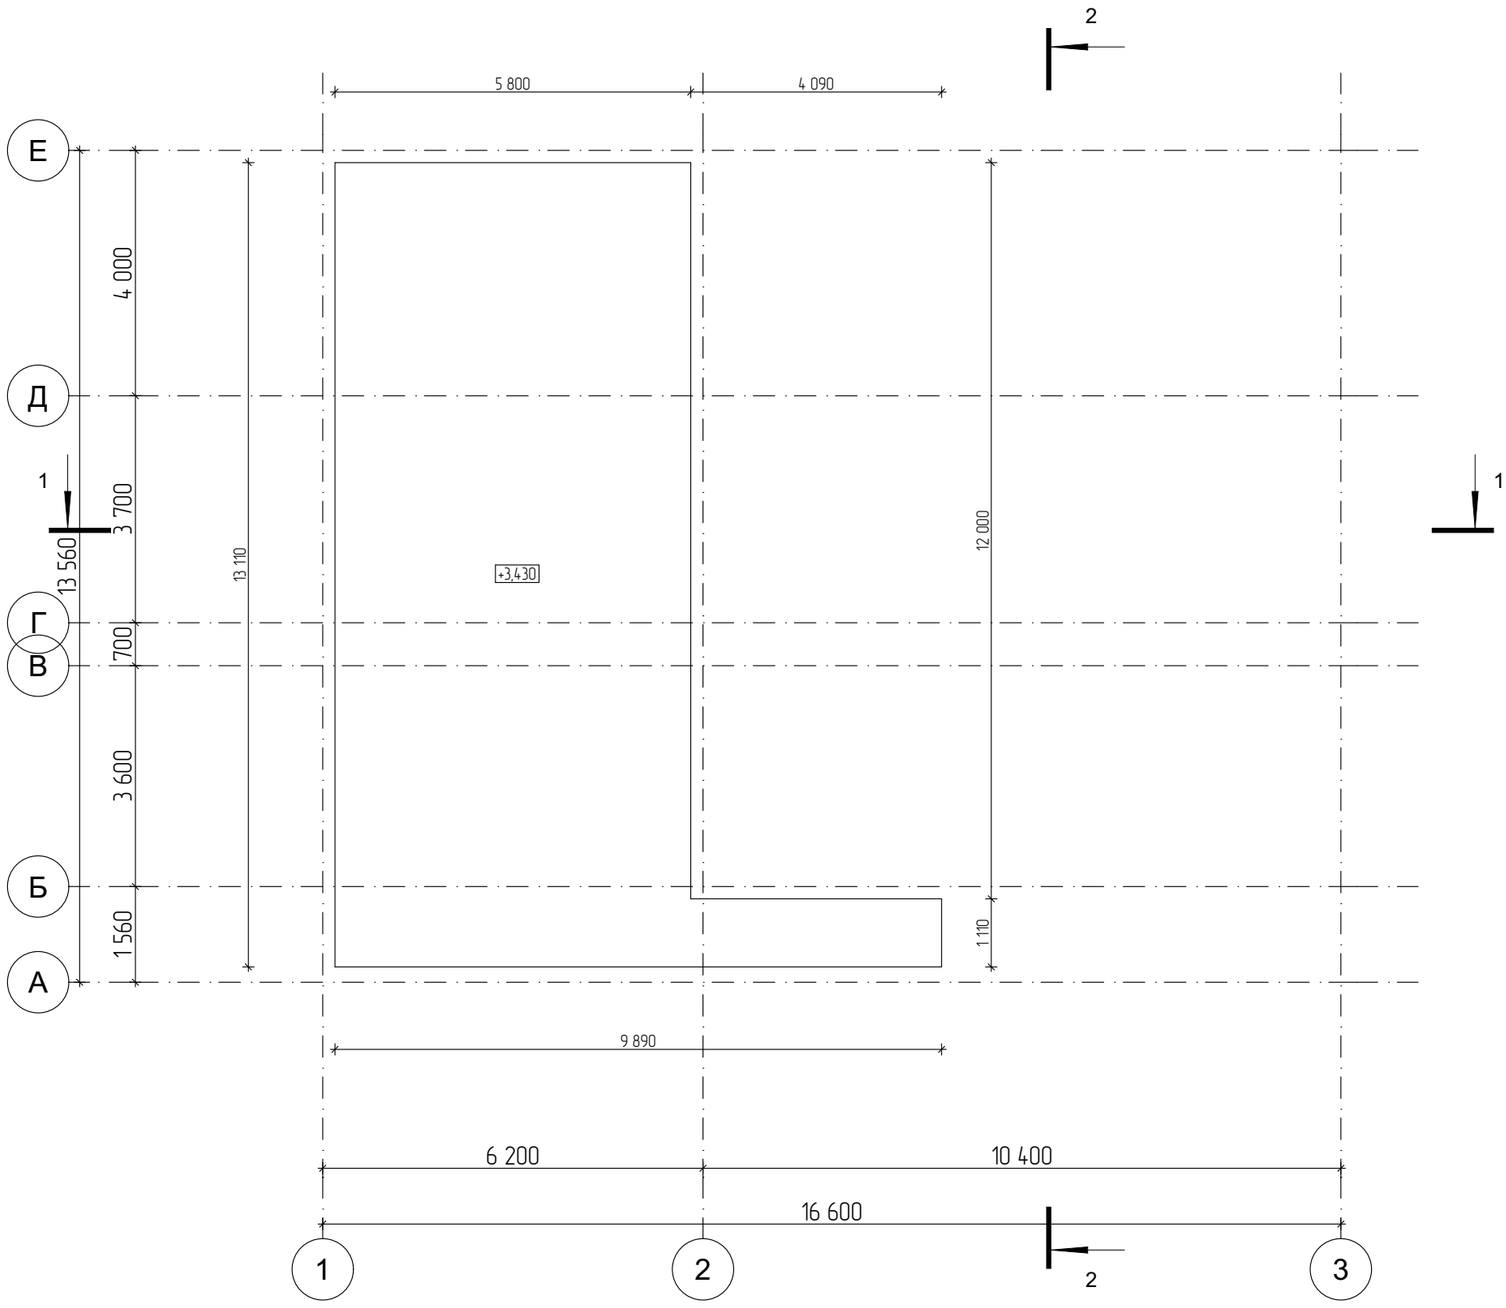

ИКК-03 Кровля	
Наименование	Площадь
Кровля плоская	80,58

Изм.	Кол.уч.	Лист	№Док.	Подп.	Дата	
						кадастровый номер 47:07:0157001:3873, Ленинградская область, Всеволожский муниципальный район, Агалатовское сельское поселение, территория "История Парк", улица Петровская, з/у №20 Россия
Разраб.		Салыкова Е.				Индивидуальный жилой дом
						План кровли на отм. 3,432

Стадия	Лист	Листов
ЭП	25	

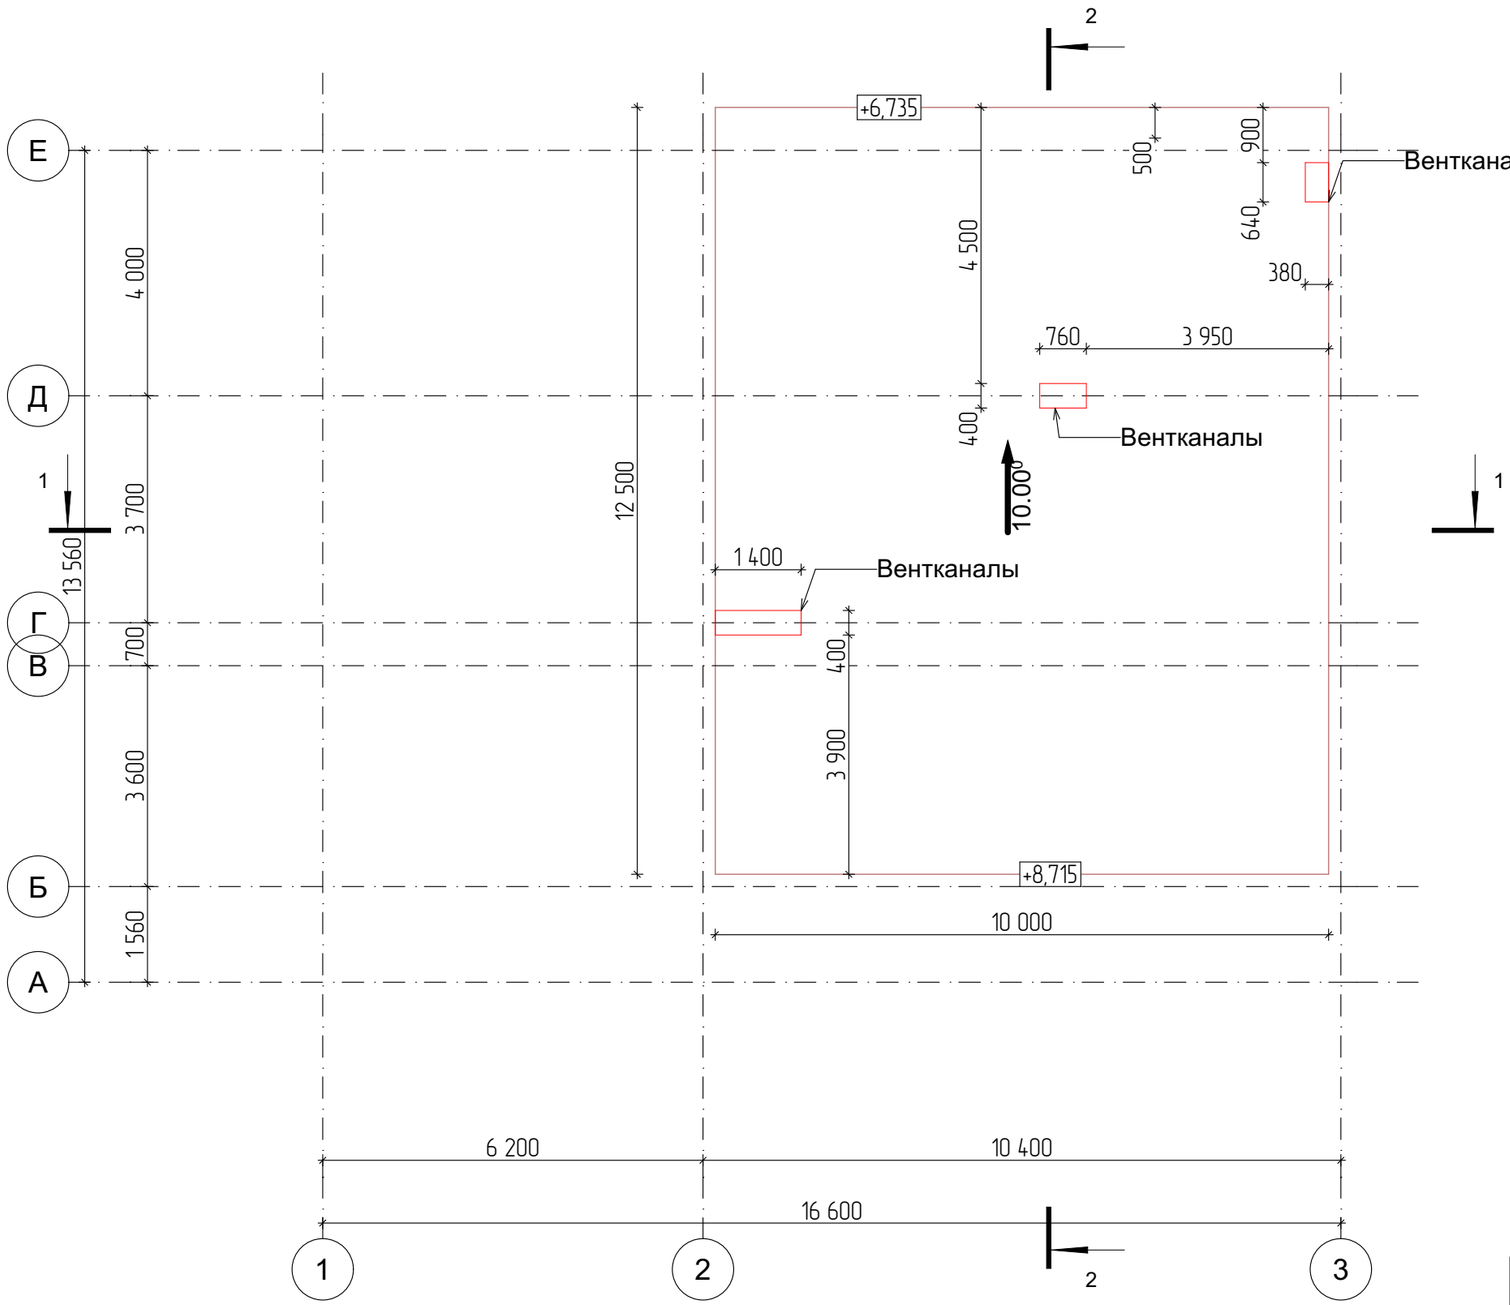




ВЕДОМОСТЬ КРОВЕЛЬНОГО МАТЕРИАЛА

Наименование	Площадь, м2
Кровля дома	126,56

Изм.	Кол.уч.	Лист	№Док.	Подп.	Дата	
						кадастровый номер 47:07:0157001:3873, Ленинградская область, Всеволожский муниципальный район, Агалатовское сельское поселение, территория "История Парк", улица Петровская, з/у №20 Россия
Разраб.		Салыкова Е.				Индивидуальный жилой дом
						План кровли на отм. 6,735

Стадия	Лист	Листов
ЭП	26	

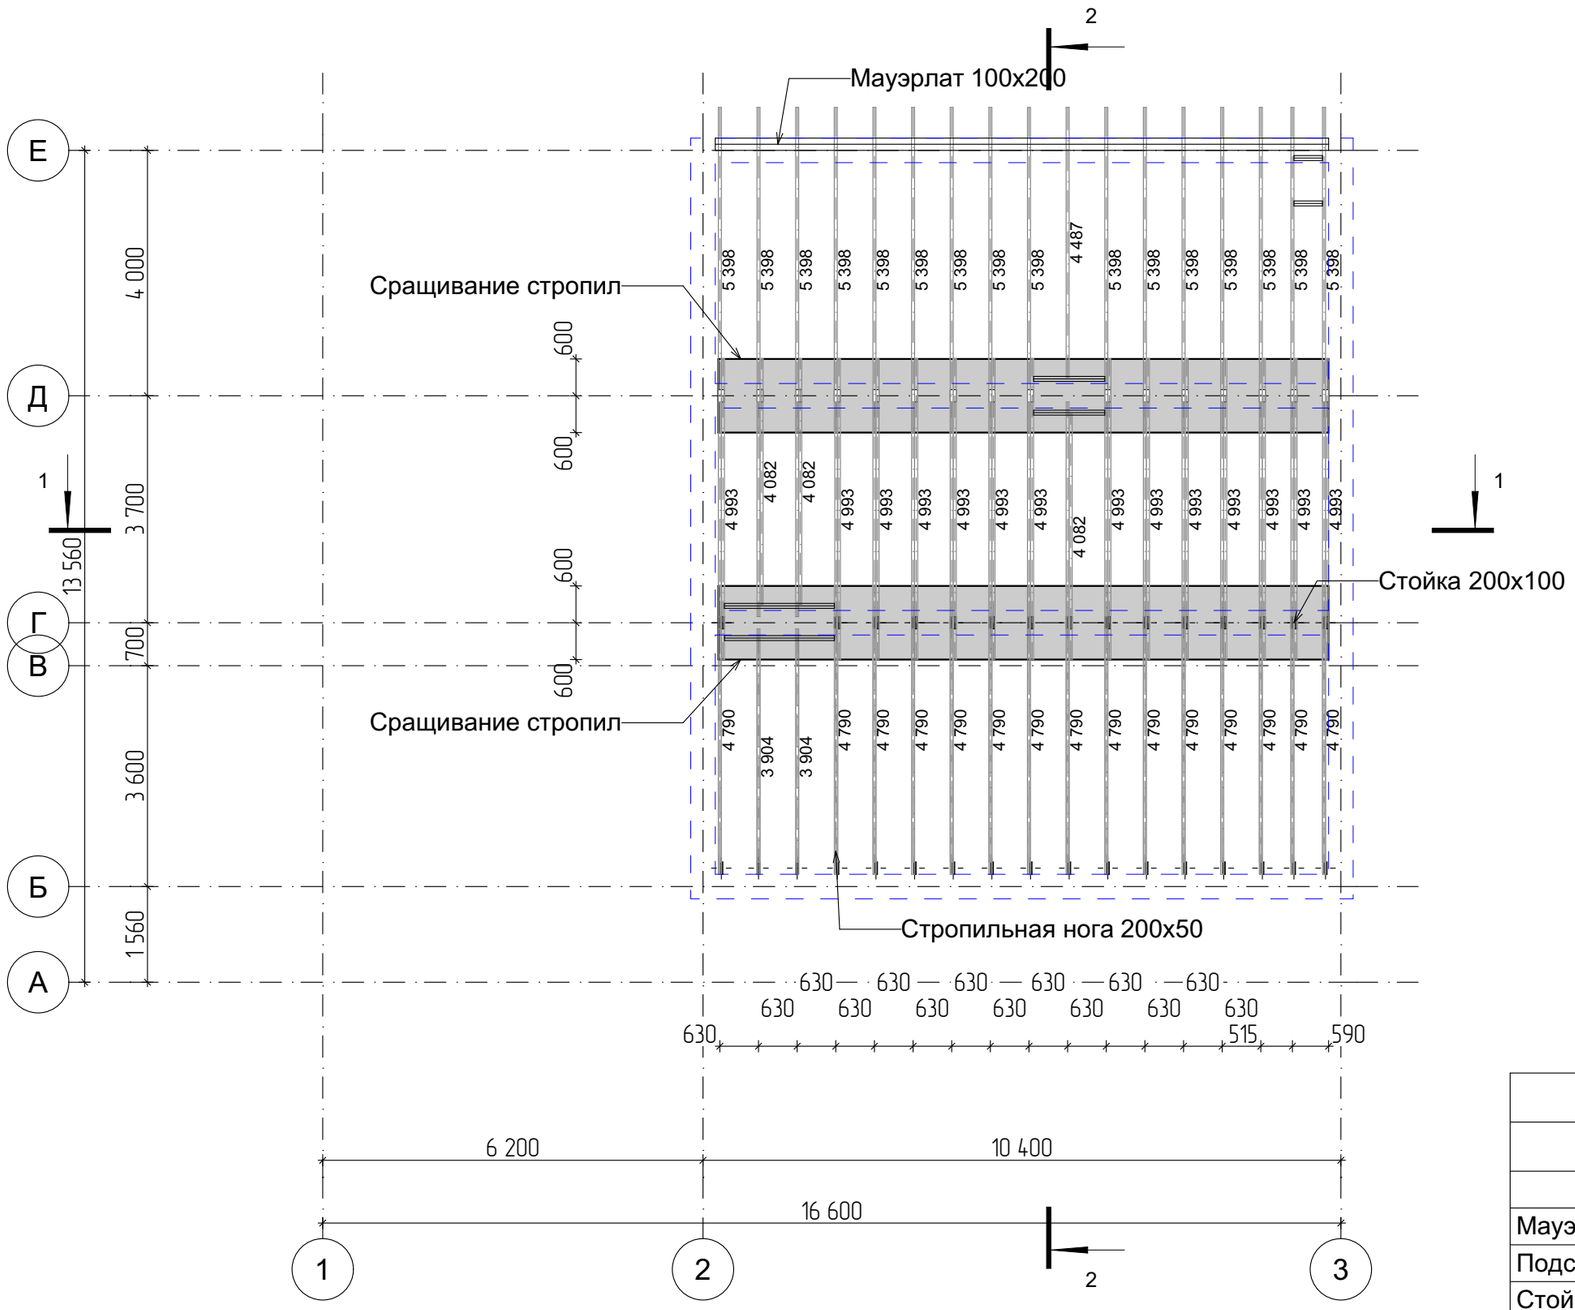

Контур несущей стены

ВЕДОМОСТЬ СТРОПИЛЬНОЙ СИСИТЕМЫ

Наименование	Объем, м3
	1,06
Мауэрлат 100х200	0,20
Подстропильная нога 200х50	1,36
Стойка 200х50	0,34
Стойка 200х100	0,46
Стропильная нога 200х50	2,55


Изм.	Кол.уч.	Лист	№Док.	Подп.	Дата
Разраб.		Салыкова Е.			


кадастровый номер 47:07:0157001:3873, Ленинградская область, Всеволожский муниципальный район, Агалатовское сельское поселение, территория "История Парк", улица Петровская, з/у №20 Россия

Индивидуальный жилой дом


Стадия	Лист	Листов
ЭП	27	

Схема расположения стропил на отм. 6,735

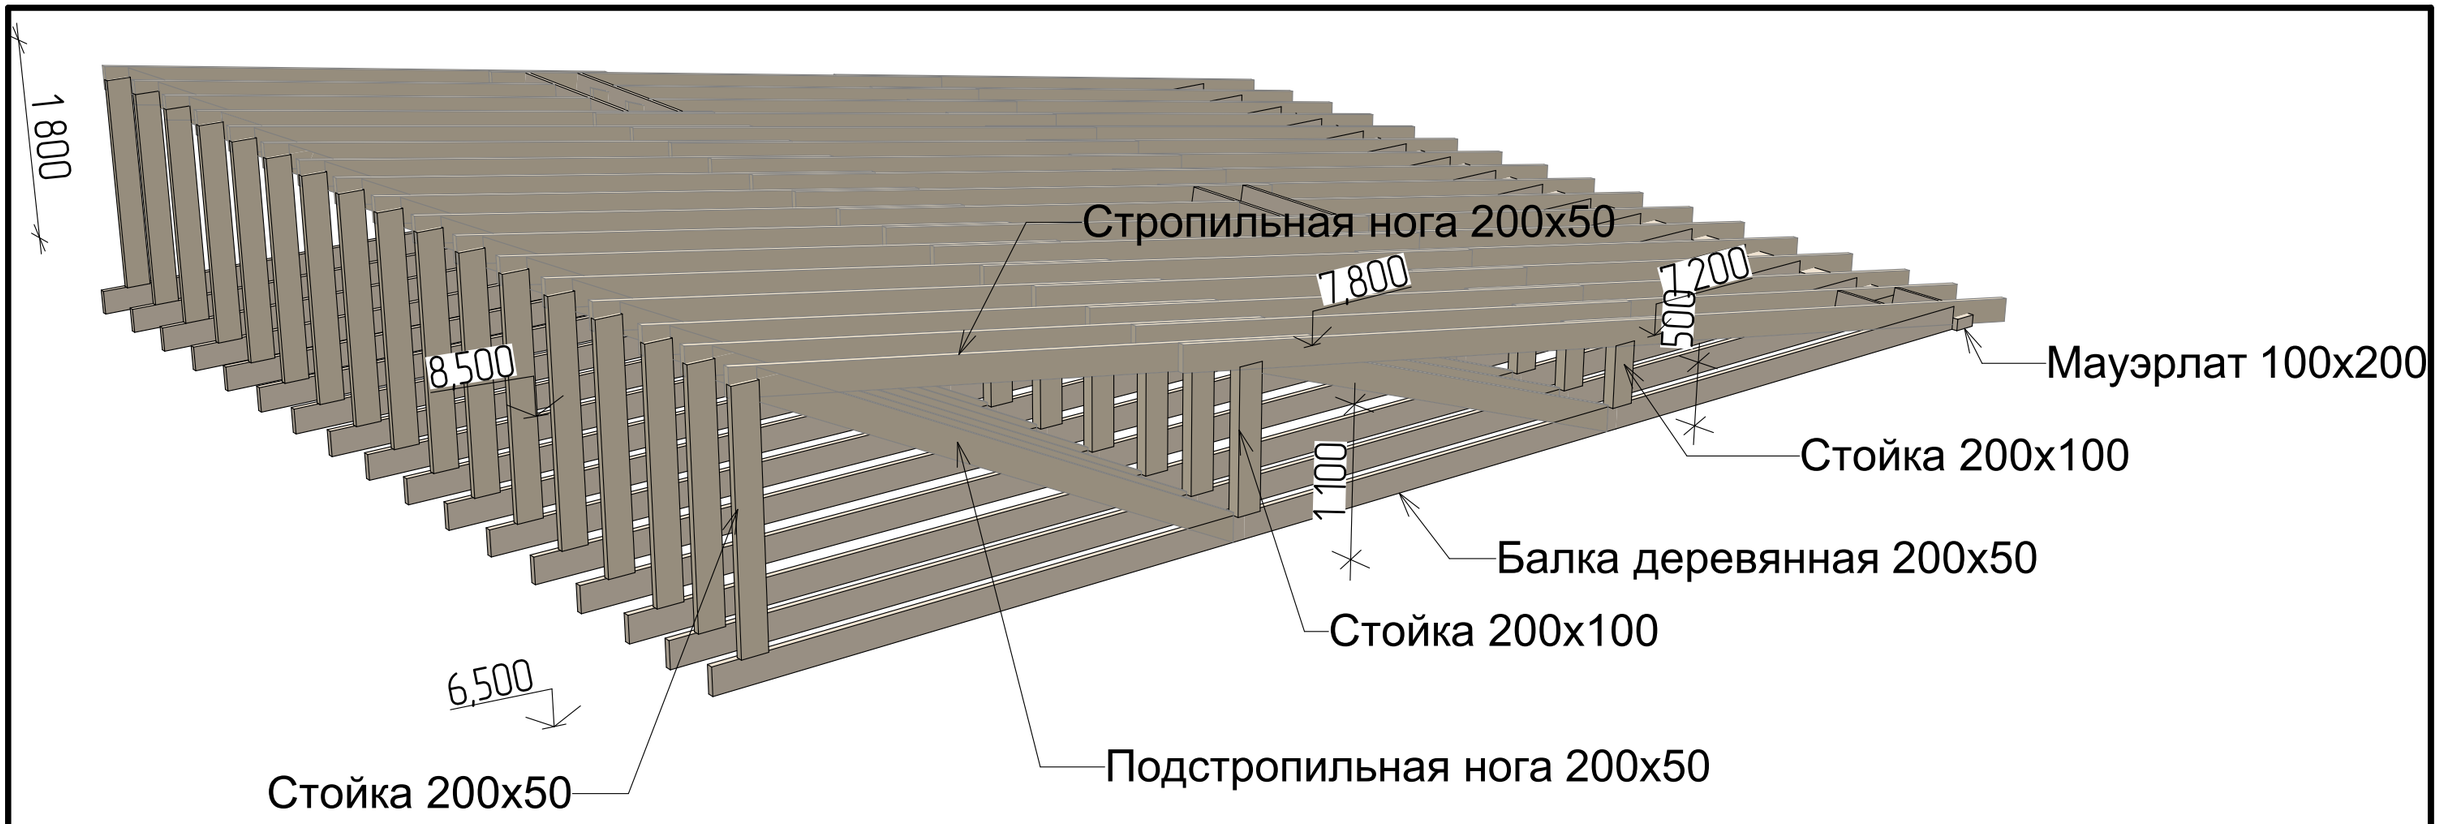

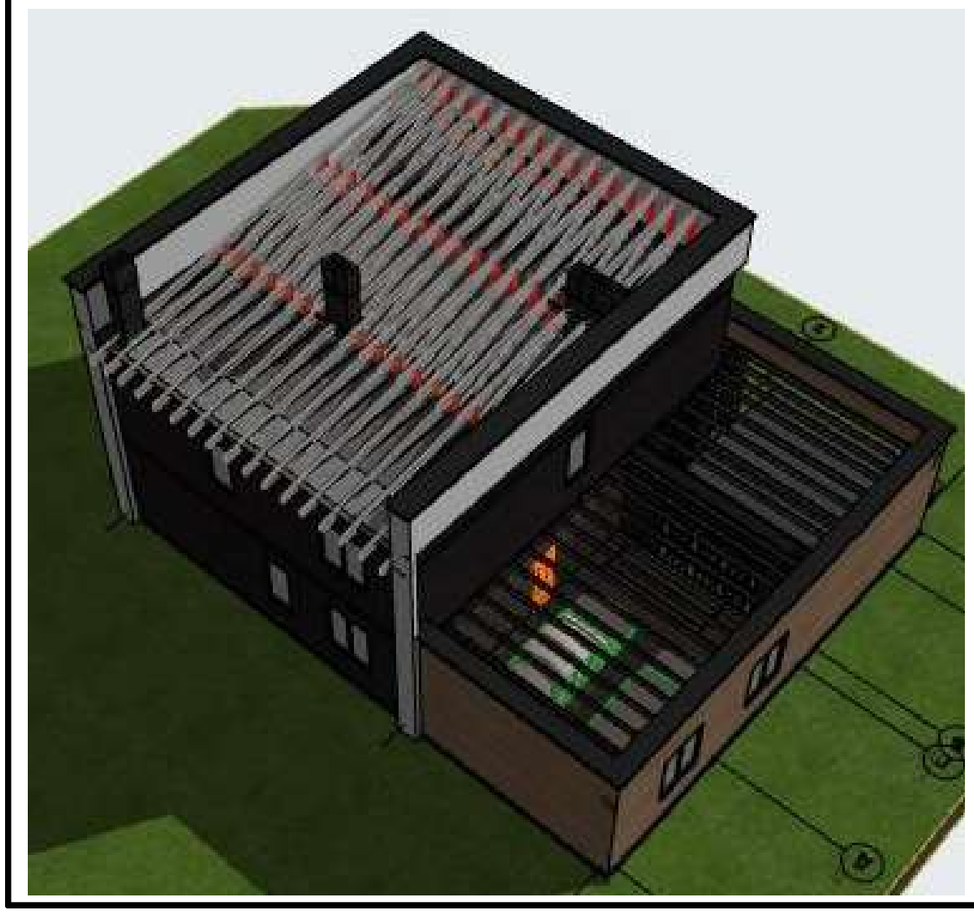


Изм.	Кол.уч.	Лист	№Док.	Подп.	Дата	кадастровый номер 47:07:0157001:3873, Ленинградская область, Всеволожский муниципальный район, Агалатовское сельское поселение, территория "История Парк", улица Петровская, з/у №20 Россия			
Разраб.		Салыкова Е.				Индивидуальный жилой дом	Стадия	Лист	Листов
							ЭП	28	
						3Д Вид стропильной системы			

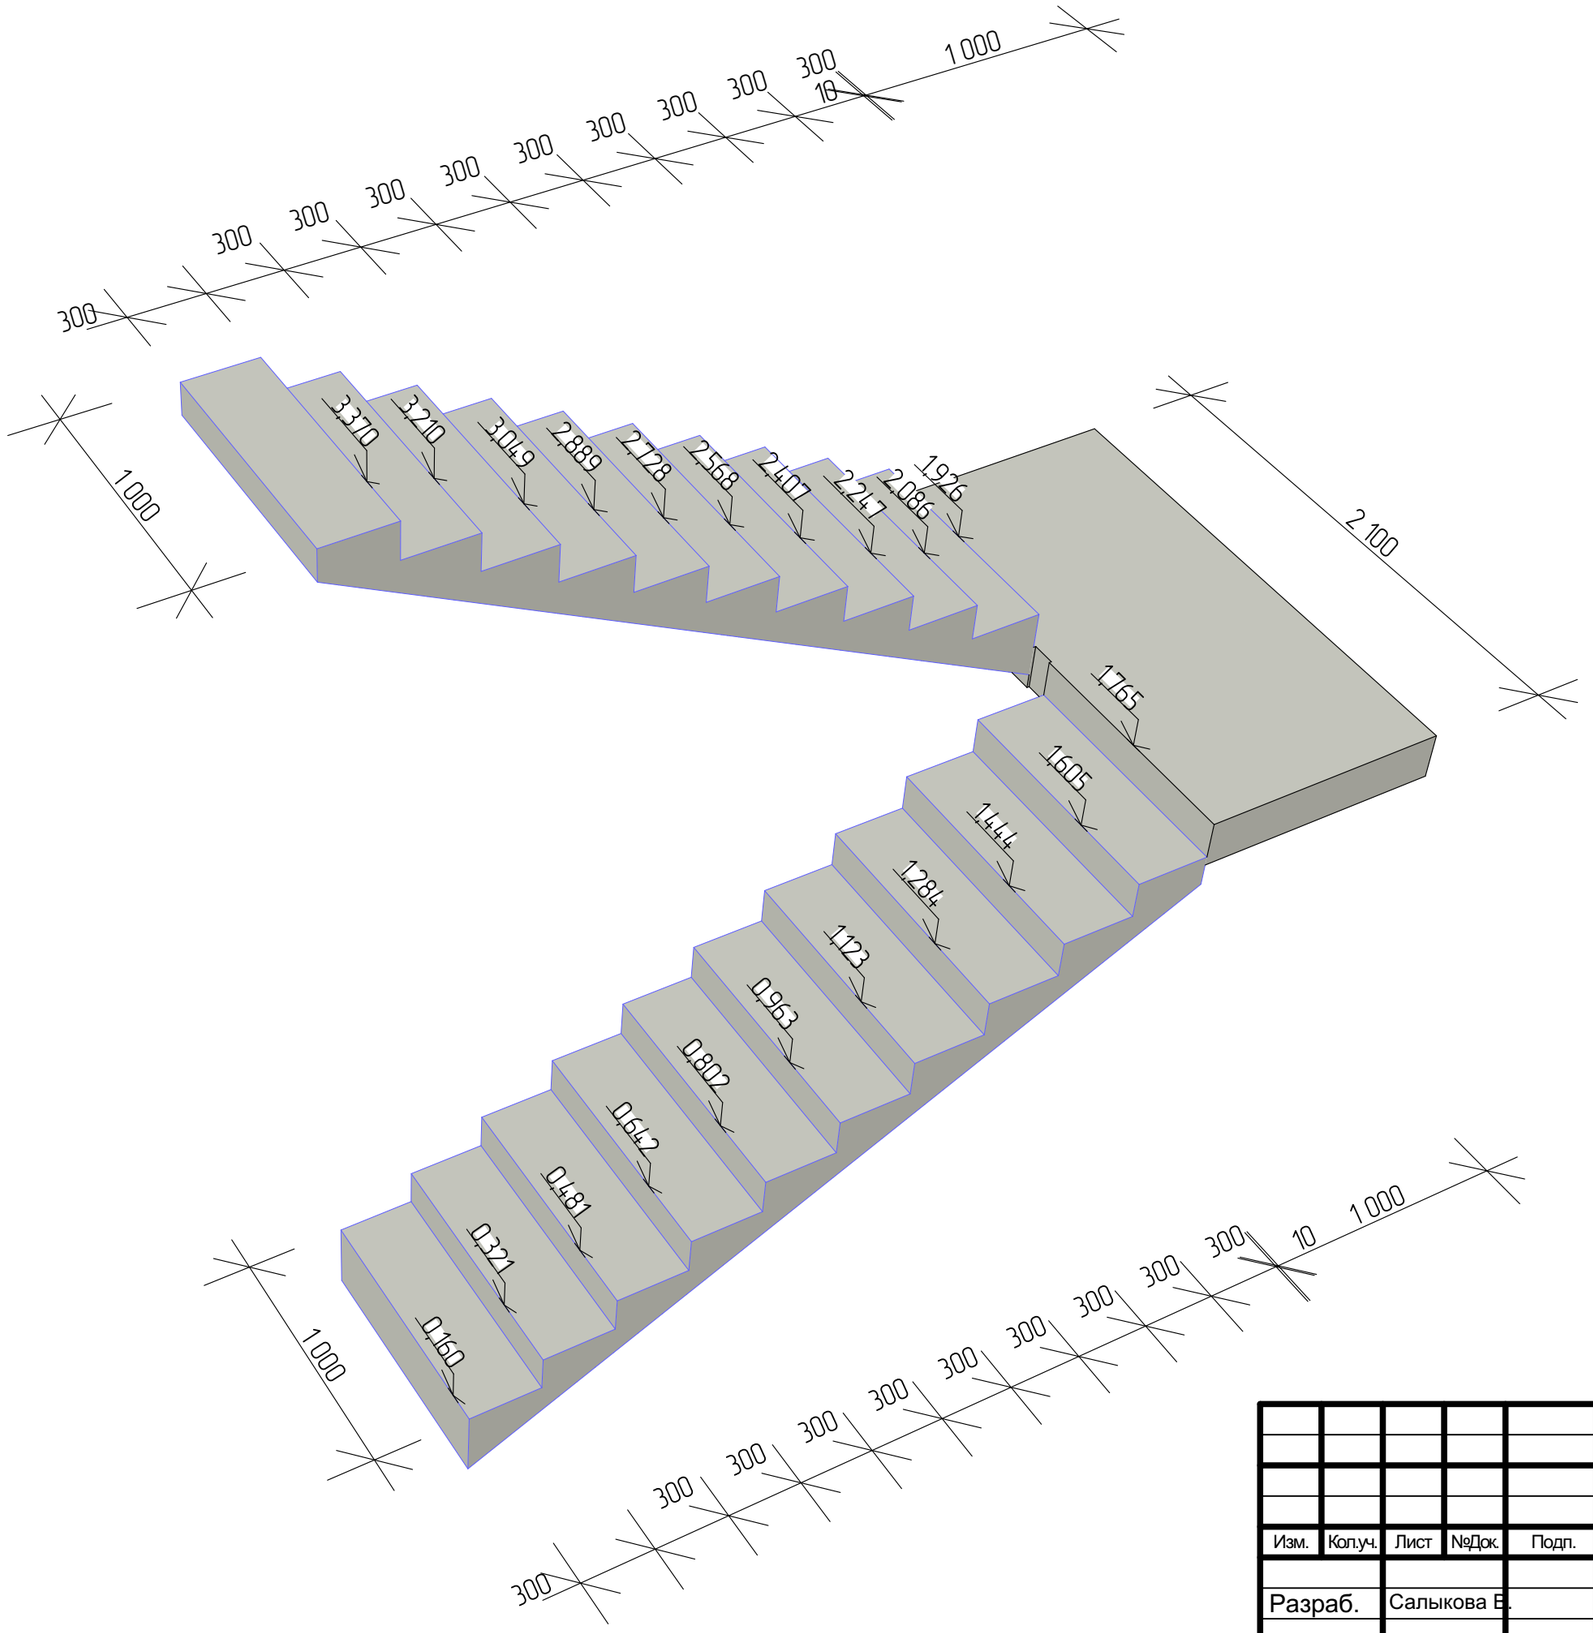


						кадастровый номер 47:07:0157001:3873, Ленинградская область, Всеволожский муниципальный район, Агалатовское сельское поселение, территория "История Парк", улица Петровская, з/у №20 Россия
Изм.	Кол.уч.	Лист	№Док.	Подп.	Дата	
Разраб.		Салыкова Е.				Индивидуальный жилой дом
						3Д вид лестницы

Стадия	Лист	Листов
ЭП	29	

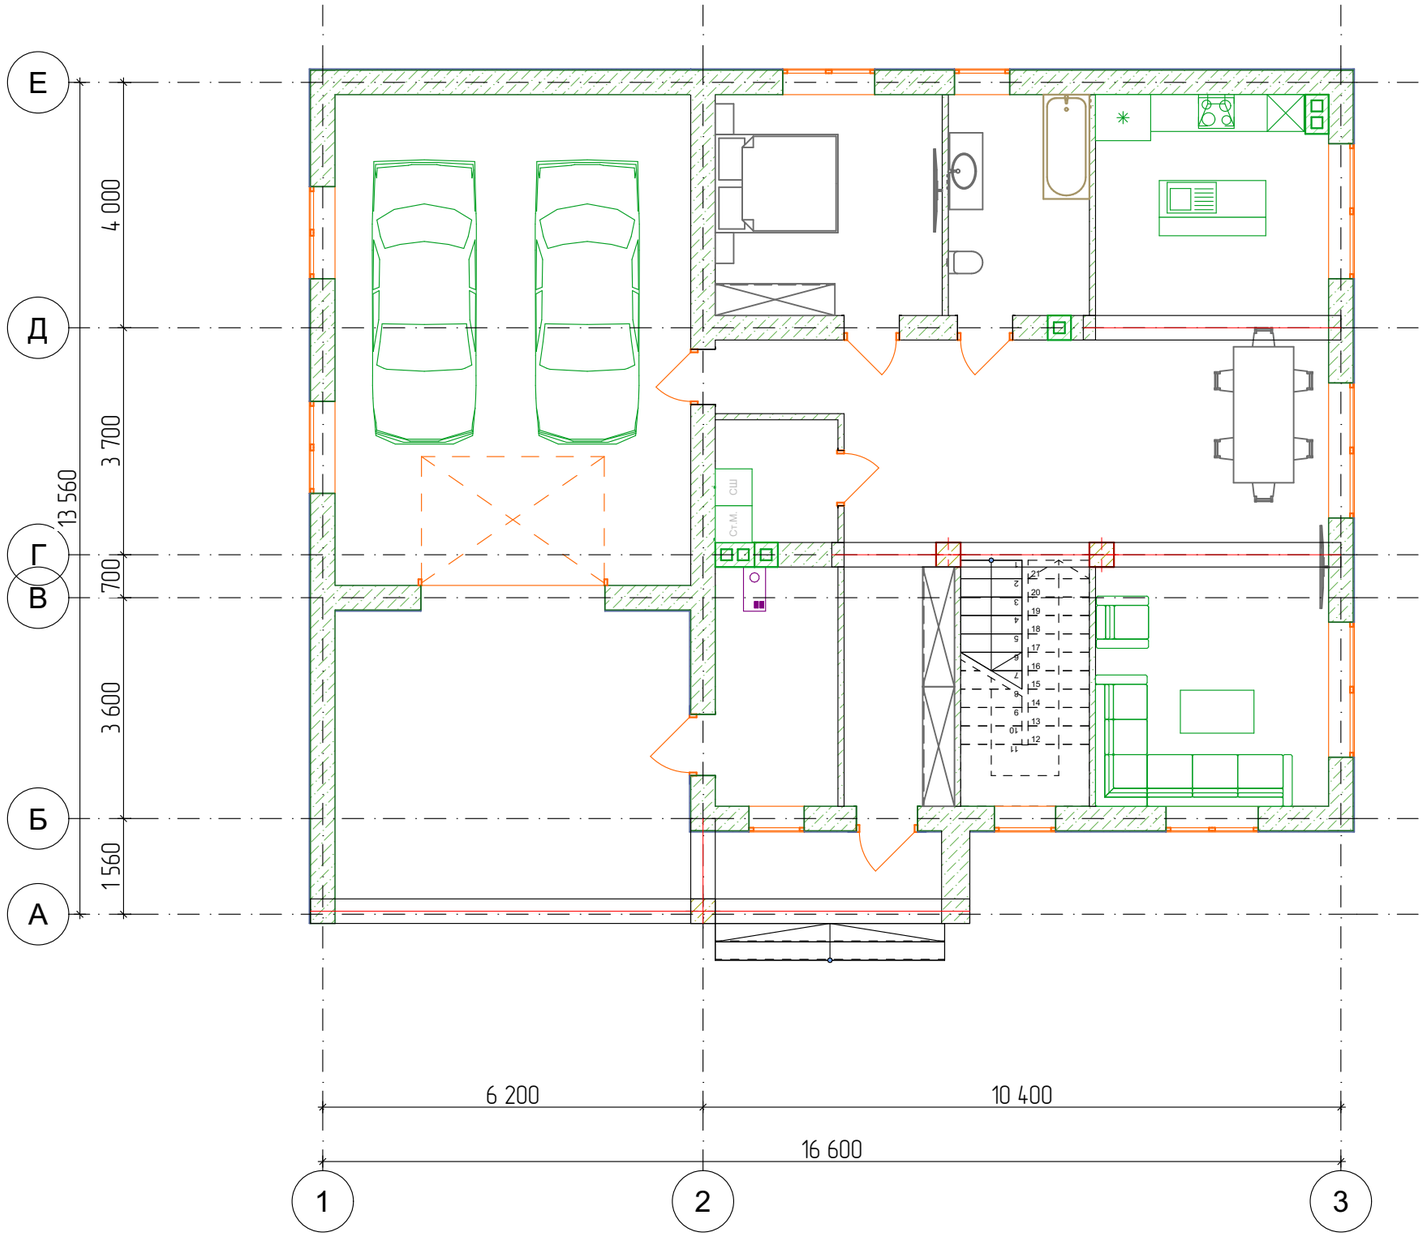


						кадастровый номер 47:07:0157001:3873, Ленинградская область, Всеволожский муниципальный район, Агалатовское сельское поселение, территория "История Парк", улица Петровская, з/у №20 Россия
Изм.	Кол.уч.	Лист	№Док.	Подп.	Дата	
Разраб.		Салыкова Е.				Индивидуальный жилой дом
						План расстановки мебели 1 этаж

Стадия	Лист	Листов
ЭП	30	

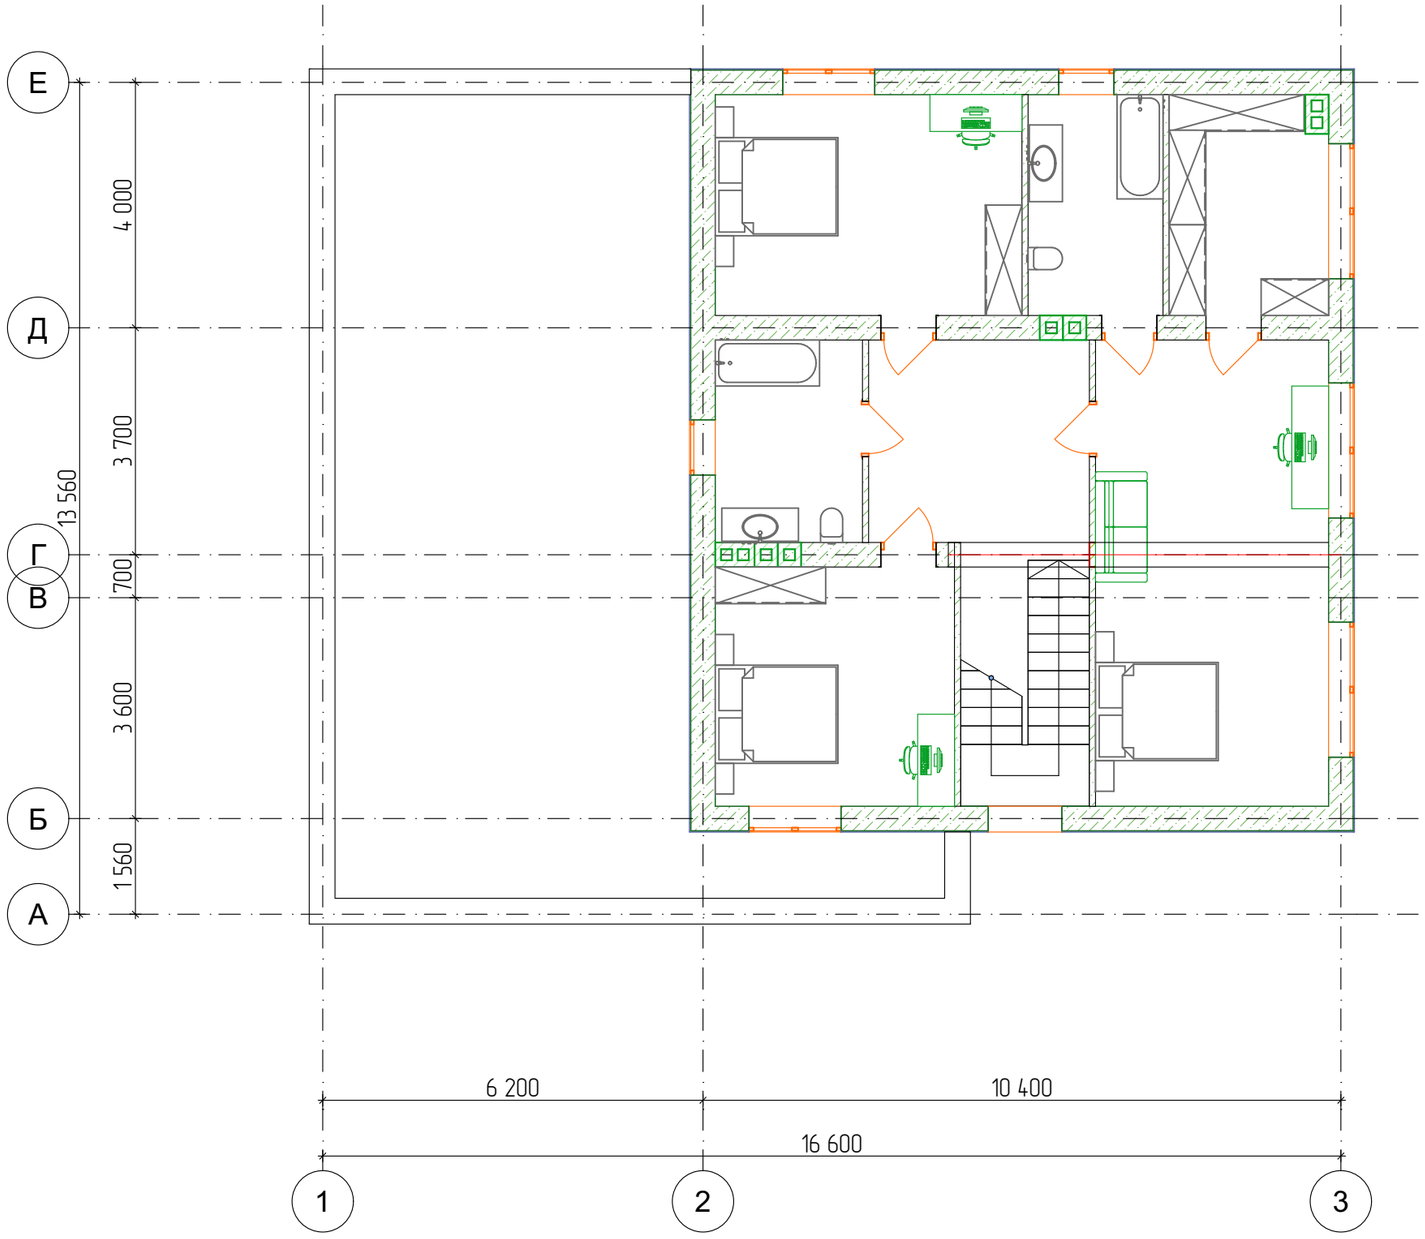


Изм.	Кол.уч.	Лист	№Док.	Подп.	Дата	кадастровый номер 47:07:0157001:3873, Ленинградская область, Всеволожский муниципальный район, Агалатовское сельское поселение, территория "История Парк", улица Петровская, з/у №20 Россия			
Разраб.		Салыкова В.				Индивидуальный жилой дом	Стадия	Лист	Листов
							ЭП	31	
						План расстановки мебели 2 этаж			

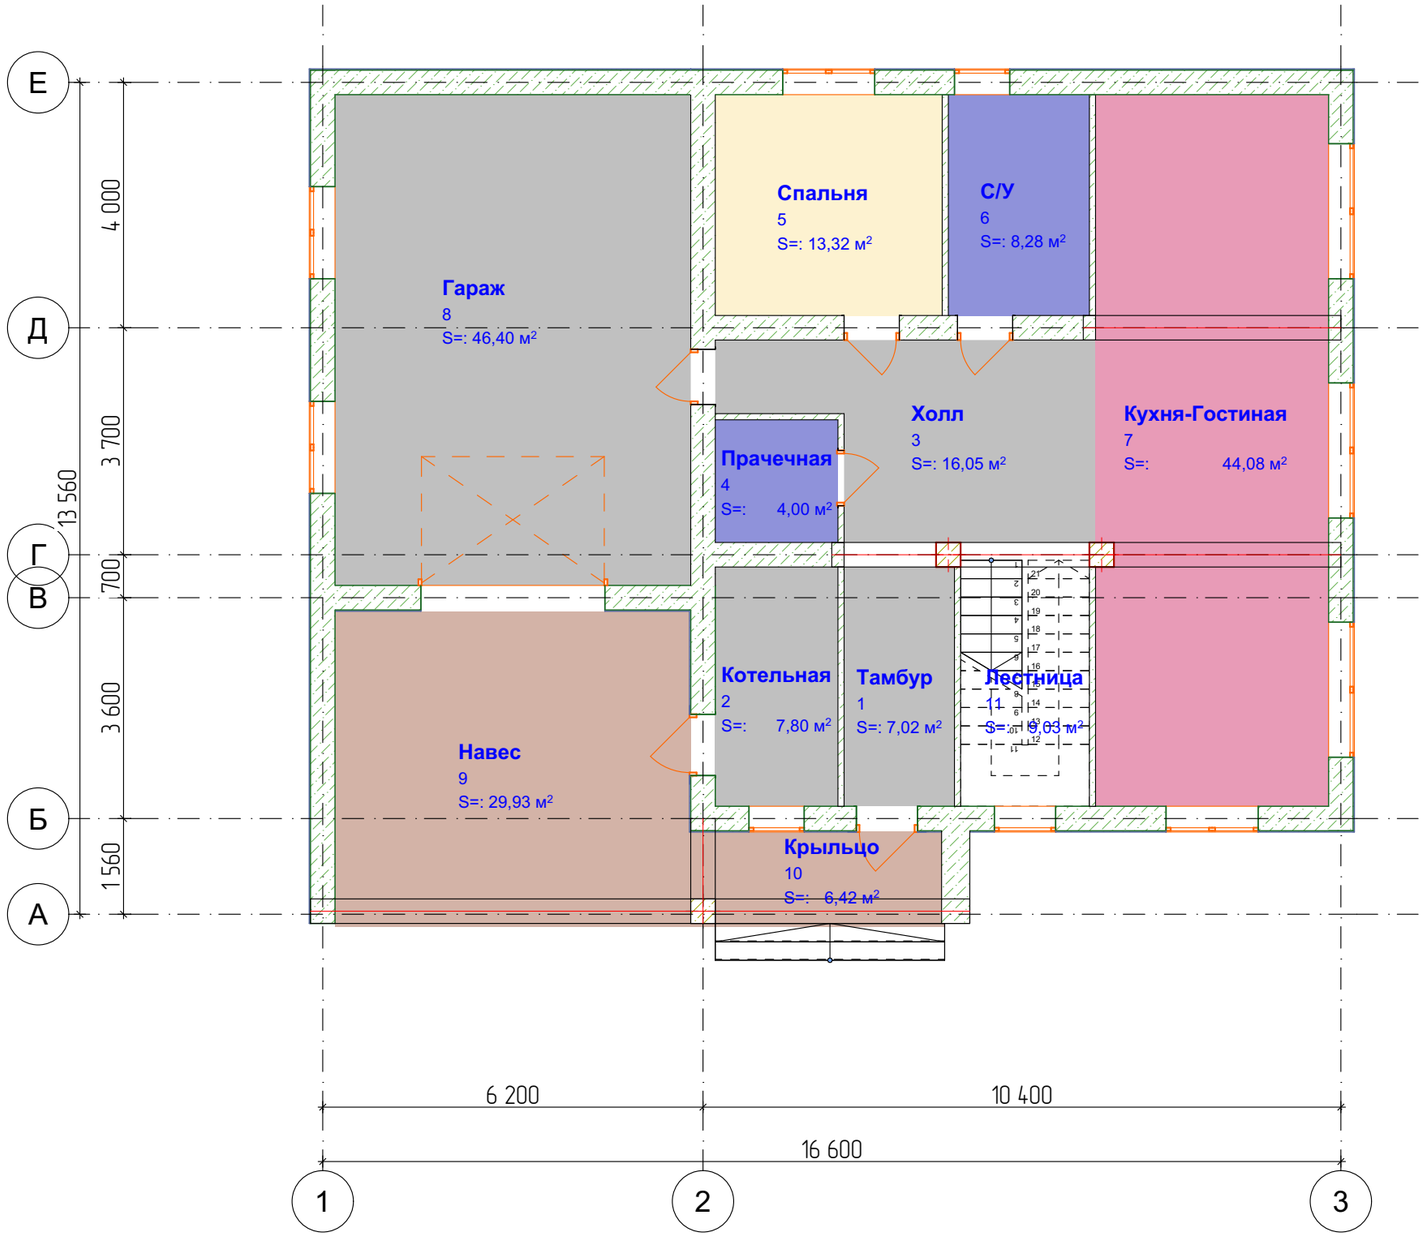

№	Наименование	Площадь
1	Тамбур	7,02
2	Котельная	7,80
3	Холл	16,05
4	Прачечная	4,00
5	Спальня	13,32
6	С/У	8,28
7	Кухня-Гостиная	44,08
8	Гараж	46,40
9	Навес	29,93
10	Крыльцо	6,42
11	Лестница	9,03
		192,33 м²

Изм.	Кол.уч.	Лист	№Док.	Подп.	Дата	
						кадастровый номер 47:07:0157001:3873, Ленинградская область, Всеволожский муниципальный район, Агалатовское сельское поселение, территория "История Парк", улица Петровская, з/у №20 Россия
Разраб.		Салыкова Е.				Индивидуальный жилой дом
						Экспликация помещений 1- го этажа

Стадия	Лист	Листов
ЭП	32	

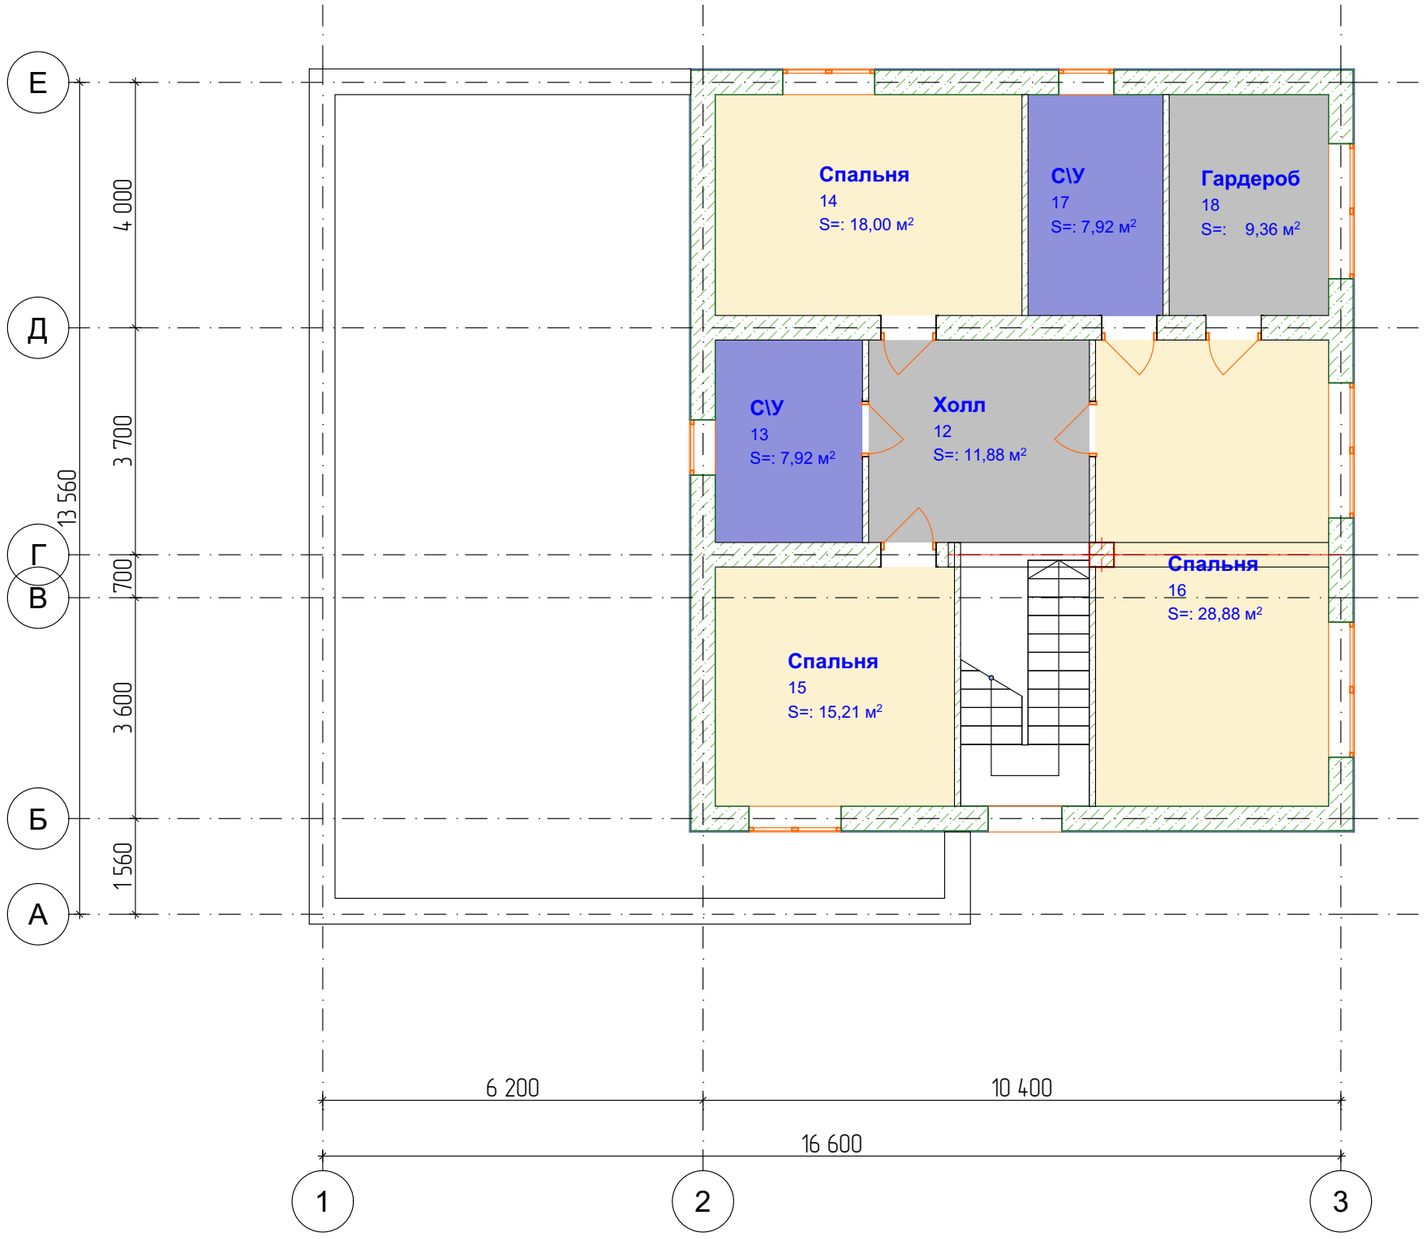

№	Наименование	Площадь
12	Холл	11,88
13	С\У	7,92
14	Спальня	18,00
15	Спальня	15,21
16	Спальня	28,88
17	С\У	7,92
18	Гардероб	9,36
		99,17 м²

Изм.	Кол.уч.	Лист	№Док.	Подп.	Дата	
						кадастровый номер 47:07:0157001:3873, Ленинградская область, Всеволожский муниципальный район, Агалатовское сельское поселение, территория "История Парк", улица Петровская, з/у №20 Россия
Разраб.		Салыкова В.				Индивидуальный жилой дом
						Экспликация помещений 2-го этажа

Стадия	Лист	Листов
ЭП	33	



Изм.	Кол.уч.	Лист	№Док.	Подп.	Дата	кадастровый номер 47:07:0157001:3873, Ленинградская область, Всеволожский муниципальный район, Агалатовское сельское поселение, территория "История Парк", улица Петровская, з/у №20 Россия			
Разраб.		Салыкова		В.		Индивидуальный жилой дом	Стадия	Лист	Листов
							ЭП	34	
						Фасад в осях 1-3			



						кадастровый номер 47:07:0157001:3873, Ленинградская область, Всеволожский муниципальный район, Агалатовское сельское поселение, территория "История Парк", улица Петровская, з/у №20 Россия
Изм.	Колуч.	Лист	№Док.	Подп.	Дата	
Разраб.		Салыкова	В.			Индивидуальный жилой дом
						Фасад в осях Е-А

Стадия	Лист	Листов
ЭП	35	



						кадастровый номер 47:07:0157001:3873, Ленинградская область, Всеволожский муниципальный район, Агалатовское сельское поселение, территория "История Парк", улица Петровская, з/у №20 Россия
Изм.	Кол.уч.	Лист	№Док.	Подп.	Дата	
Разраб.		Салыкова	В.			Индивидуальный жилой дом
						Фасад в осях А-Е

Стадия	Лист	Листов
ЭП	36	



Изм.	Кол.уч.	Лист	№Док.	Подп.	Дата	
Разраб.		Салыкова	В.			

кадастровый номер 47:07:0157001:3873, Ленинградская область, Всеволожский муниципальный район, Агалатовское сельское поселение, территория "История Парк", улица Петровская, з/у №20 Россия

Индивидуальный жилой дом	Стадия	Лист	Листов
	ЭП	37	
Фасад в осях 3-1			