ПРОЕКТНАЯ ДОКУМЕНТАЦИЯ

Индивидуальный жилой дом

кадастровый номер Россия

#ID Проекта

РОССИЯ
2026

Ведомость листов	
Наименование	Лист
Обложка	
СОДЕРЖАНИЕ	01
Ведомость материалов - фундамент	02
Ведомость материалов - стены	03
Ведомость материалов - монолитный пояс	04
Ведомость материалов - перемычки	05
Ведомость материалов - перекрытия	06
Ведомость материалов - кровля	07
Ведомость материалов ЖБ элементы	08
Генеральный план	09
ПЗ Генеральный план	10
3D Виды	11
ПЗ Фундамент	12
План котлована	13
ПЗ Фундаментная плита	14
План фундамента	15
Наружные сети	16
План коммуникаций (только пол)	17
План коммуникаций	18
Ведомость материалов ниже отм 0.000	19
3D Вид фундамента	20
Схема нижнего армирования фундаментной плиты	21
Схема верхнего армирования фундаментной пли...	22
Узел армирования фундаментной плиты	23
Схема армирования арматурного каркаса	24
Ведомость материалов - фундаментная плита	25
ПЗ Стены	26
ПЗ Газобетонные блоки	27
План на отм. ±0.000	28
План на отм +3.440	29
Ведомасть материаов стен	30
Ведомость материалов КЖ	31.1
Дымоход Д-1	33
Дымоход Д-2	34
Дымоход Д-3	35
Дымоход Д-4	36
Каталог дверных проемов	37
Каталог оконных проемов	38
Маркировка оконных проемов первого этажа	39

Ведомость листов	
Наименование	Лист
Маркировка оконных проемов второго этажа	40
Маркировка дверных проемов первого этажа	41
Маркировка дверных проемов второго этажа	42
Сводная ведомость проемов	43
Ведомость перемычек	44
Разрез 1 - 1	45
Разрез 2 - 2	46
Разрез по стене	47
ПЗ - монтаж плит 1ПК	48
ПЗ - Деревянное перекрытие	49
План перекрытия +3,100	50
План перекрытий на отм 6,540	51
Ведомость материалов перекрытие	52
ПЗ - монолитный пояс	53
Монолитный пояс на отм 2,950	54
Монолитный пояс на отм 6,390	55
Ведомость материалов монолитного пояса	56
ПЗ - Скатная кровля	57
План кровли первого этажа	58
План кровли на отм. 6,454	59
Ведомость кровельного пирога	60
Схема расположения стропил на отм. 2,783	61
Схема расположения стропил на отм. 6,454	62
3Д Вид стропильной системы	63
Ведомость материалов (стропильная система)	64
Силовой каркас кровли	66
Силовой каркас вид сбоку	67
3Д вид каркаса кровли	68
3Д узлы кровли	69
План расстановки мебели 1 этаж	70
План расстановки мебели 2 этаж	71
Экспликация помещений 1- го этажа	72
Экспликация помещений 2-го этажа	73
Фасад в осях 1-8	74
Фасад в осях И-А	75
Фасад в осях А-И	76
Фасад в осях 8-1	77
Ведомость отделки фасада	78
План раскладки перемычек 1 - го этажа	80

Ведомость листов	
Наименование	Лист
План раскладки перемычек 2-го этажа	81
3Д вид монолитного пояса	82
Р1	83
Р2	84
Р3	85
Р4	86
Р5	87
Р6	88
Р7	89
Р8	90
Р9	91
Р10	92
Р11	93
Р12	94
Р13	95

Ведомость материалов фундаментной плиты			
Строительный материал	**Наименование**	Объем, м3	Площадь, м2
Бетон В 7,5			
	Плита фундамента (дом)	26,20	262,03
	Плита фундамента (крыльцо))	0,38	3,84
	Плита фундамента (терраса))	4,46	44,57
		31,04 м³	
Бетон В25			
	Плита фундамента (дом)	117,77	261,96
	Плита фундамента (крыльцо))	1,73	3,84
	Плита фундамента (терраса))	20,01	44,57
		139,51 м³	
Изоляция - ЭППС			
	Плита фундамента (дом)	21,15	212,59
		21,15 м³	
Плитка - Напольная			
	Плита фундамента (дом)	4,26	212,85
	Плита фундамента (крыльцо))	0,08	3,76
	Плита фундамента (терраса))	0,89	44,29
		5,23 м³	
Стяжка ЦПР			
	Плита фундамента (дом)	17,02	212,84
	Плита фундамента (крыльцо))	0,38	3,76
	Плита фундамента (терраса))	4,39	44,29
		21,79 м³	
		218,72 м³	

Утеплитель на боковую поверхность фундамента			
Наименование	Площадь, м2	Объем, м3	Толщина, мм
Изоляция - ЭППС	16,01	0,81	50

Коммуникации		
Назначение	Строительный Материал	Длина, мм
Водопровод	Труба ПЭ100 SDR11 d40×3,7 (PN16)	3 000
Канализация	Труба ПВХ SN4 d110×3,2 (канализация)	37 680

ВЕДОМОСТЬ БЛОКА ДЛЯ СТЕН			
Этаж	Тип конструкций	Строительный материал	Объем, м3
1-й этаж			
	Внутренние несущие стены	Газобетон D400	25,03
			25,03 м³
	Наружные несущие стены	Газобетон D400	69,28
			69,28 м³
	Перегородки	Газобетон перегородки	7,18
			7,18 м³
2-й этаж			
	Внутренние несущие стены	Газобетон D400	9,54
			9,54 м³
	Наружные несущие стены	Газобетон D400	58,99
			58,99 м³
	Перегородки	Газобетон перегородки	7,67
			7,67 м³
			177,69 м³

Ведомость материалов на фасад			
Наиме...	**Компоненты**		Объем, м3
	Толщина, мм	**Площадь, м2**	
Изоляция - Минеральная Жесткая			
	50	373,45	18,64
Кирпич - Облицовочный			
	120	378,30	45,25

ВЕДОМОСТЬ БЕТОНА НА МОНОЛИТНЫЙ ПОЯС

Этаж	Материал	**Наименование**	Объем, м3
1-й этаж			
	Бетон В20	Монолитный пояс	5,27
2-й этаж			
	Бетон В20	Монолитный пояс	3,83
			9,10 м³

Ведомость арматуры

Этаж	Описание	Кол-во	Ед. изм.	Вес, кг
1-й этаж				
	Арматура А500С d12	412,68	м.п.	366,46
2-й этаж				
	Арматура А500С d12	325,63	м.п.	289,16
		738,28		**655,65**

Хомуты на монолитный пояс

Этаж	Наименование	Кол-во	Ед.изм.	Вес, кг	Длина 1 хомута	Кол-во хомутов
1-й этаж						
	d8	201,69	м.п.	79,67	0,85	237,00
	d8	43,09	м.п.	17,02	1,23	35,00
2-й этаж						
	d8	177,01	м.п.	69,92	0,85	208,00
		421,81		**166,61**		**480,00**

Ведомость материлов - утепление пояса

Этаж	Строительный материал	**Наименование**	Объем
1-й этаж	Изоляция - ЭППС (Монолитный пояс)	Монолитный пояс	0,51
2-й этаж	Изоляция - ЭППС (Монолитный пояс)	Монолитный пояс	0,46
			0,97 м³

Перемычки					
Тип	Марк. поз.	Ширина, мм	Высота, мм	Длина,мм	Объем бетона, м3
Дверь, 1-й этаж, Несущие стены					
	Д-1	400,00	200,00	1400,00	0,11
	Д-1	400,00	200,00	1400,00	0,11
	Д-1	400,00	200,00	1400,00	0,11
	ДВ-1	400,00	200,00	1500,00	0,12
	ДВ-1	400,00	200,00	1500,00	0,12
	ДВ-2	400,00	200,00	4000,00	0,32
Дверь, 1-й этаж, Перегородки					
	Д-1	100,00	200,00	1400,00	0,03
	Д-1	100,00	200,00	1400,00	0,03
	Д-1	100,00	200,00	1400,00	0,03
	Д-1	100,00	200,00	1400,00	0,03
Дверь, 2-й этаж, Несущие стены					
	Д-1	400,00	200,00	1400,00	0,11
	Д-1	400,00	200,00	1400,00	0,11
Дверь, 2-й этаж, Перегородки					
	Д-1	100,00	200,00	1400,00	0,03
	Д-1	100,00	200,00	1400,00	0,03

Перемычки					
Тип	Марк. поз.	Ширина, мм	Высота, мм	Длина,мм	Объем бетона, м3
	Д-1	100,00	200,00	1400,00	0,03
Окно, 1-й этаж, Несущие стены					
	ОК-1	400,00	200,00	3000,00	0,24
	ОК-1	400,00	200,00	3000,00	0,24
	ОК-2	400,00	200,00	1400,00	0,11
	ОК-2	400,00	200,00	1400,00	0,11
	ОК-2	400,00	200,00	1400,00	0,11
	ОК-2	400,00	200,00	1400,00	0,11
	ОК-2	400,00	200,00	1400,00	0,11
	ОК-2	400,00	200,00	1400,00	0,11
	ОК-4	400,00	200,00	1100,00	0,09
	ОК-5	400,00	200,00	2000,00	0,16
	ОК-6	400,00	200,00	2500,00	0,20
	П/П	400,00	200,00	2500,00	0,20
Окно, 2-й этаж, Несущие стены					
	ОК-3	400,00	200,00	1500,00	0,12

Перемычки					
Тип	Марк. поз.	Ширина, мм	Высота, мм	Длина,мм	Объем бетона, м3
	ОК-7	400,00	200,00	1400,00	0,11
	ОК-8	400,00	200,00	2460,00	0,20
	ОК-8	400,00	200,00	2460,00	0,20
	ОК-9	400,00	200,00	3000,00	0,24
	ОК-10	400,00	200,00	2000,00	0,16
	ОК-11	400,00	200,00	3590,00	0,29
	ОК-11	400,00	200,00	3590,00	0,29
	П/П	400,00	200,00	1500,00	0,12
					4,84

							#ID Проекта
							кадастровый номер Россия
Изм.	Колуч.	Лист	№Док.	Подп.	Дата		
Разраб.						Индивидуальный жилой дом	Стадия: #Стадия Проекта; Лист: 05; Листов:
ГАП							
Ведомость материалов - перемычки							

ВЕДОМОСТЬ ПЕРЕКРЫТИЙ			
Этаж	**Наименование**	Кол-во	Длина, мм
1-й этаж			
	1ПК.54-10	1	---
	1ПК.54-12	1	---
	1ПК.36-15	1	---
	1ПК.60-12	2	---
	1ПК.60-10	2	---
	1ПК.54-15	4	---
	1ПК.60-15	5	---
2-й этаж			
		21	---
	Балка деревянная 200х50	21	4 400
Кровля			
	Балка деревянная 200х50	1	5 240
	Балка деревянная 200х50	1	5 840
	Балка деревянная 200х50	2	1 210
	Балка деревянная 200х50	8	8 040
	Балка деревянная 200х50	13	5 540
	Балка деревянная 200х50	22	6 140
		47	---

Состав кровли		
Элемент	Наименование	Площадь, м2
Кровля гаража		
	Мембрана - Водонепроницаемая	78,11
	Черепица - Черепица	78,35
	Шаговая обрешетка 25*250	78,28
Кровля дома		
	Мембрана - Водонепроницаемая	270,62
	ОБЩИЙ - КОНСТРУКТИВНЫЙ	1,60
	Черепица - Черепица	271,85
	Шаговая обрешетка 25*250	271,47
Кровля крыльца		
	Мембрана - Водонепроницаемая	6,77
	Черепица - Черепица	6,80
	Шаговая обрешетка 25*250	6,79
Кровля террасы		
	Мембрана - Водонепроницаемая	68,56
	Черепица - Черепица	68,77
	Шаговая обрешетка 25*250	68,71

Стропильная система		
Уровень	**Наименование**	Объем, м3
2-й этаж		
		0,00
	Коньковый брус 200x100	1,07
	Лобовая доска 200x25	0,27
	Мауэрлат 100x200	0,41
	Подшивка кровли - вертикальный эле...	0,00
	Подшивная доска 100x25	0,00
	Стропильная нога 200x50	2,35
Кровля		
		0,00
	Контрбрус 50x50	1,13
	Коньковый брус 200x100	1,74
	Лобовая доска 200x25	0,37
	Мауэрлат 100x200	1,16
	Подшивка кровли - вертикальный эле...	0,00
	Подшивная доска 100x25	0,00
	Стропильная нога 200x50	4,08
		12,58 м³

Ведомость кровельного материала	
Наименование	Площадь, м2
Кровля гаража	78,10
Кровля дома	273,23
Кровля крыльца	6,77
Кровля террасы	68,56
	426,66 м²

ВЕДОМОСТЬ НА УТЕПЛИТЕЛЬ (кровля)				
	Наименование	Компоненты		
		Толщина, мм	Объем, м3	Площадь, м2
Кровля				
	Изоляция - Минеральная Мягкая	200	31,19	162,06

							#ID Проекта
							кадастровый номер Россия
Изм.	Кол.уч.	Лист	№Док.	Подп.	Дата		
						Индивидуальный жилой дом	Стадия: #Стадия Проекта; Лист: 07; Листов:
Разраб.							
ГАП							
						Ведомость материалов - кровля	

Н3 Колонны			
Этаж	Наиенование	Кол-во,шт	Объем, м3
1-й этаж	ЖБ колонна 400х400	7	3,30
2-й этаж	ЖБ колонна 350х350	2	0,68
2-й этаж	ЖБ колонна 400х400	3	1,47

Н3 Ригель			
Этаж	Наиенование	Кол-во,шт	Объем, м3
1-й этаж	ЖБ ригель 400х400	2	1,35
2-й этаж	ЖБ ригель 400х400	1	1,07

н Армирование колонн					
Наименование	Арматура	Кол-во стержней	Общая длина	Ед. изм.	Всего, кг
ЖБ колонна 350х350	Арматура А500С d18	4	---	м.п.	---
ЖБ колонна 400х400	Арматура А500С d18	4	---	м.п.	---
			0,00		**0,00**

А Арматура ригель					
Элемент	Наименование	Число стержней	Кол-во	Ед. изм.	Вес, кг
ЖБ ригель 400х400					
	Арматура А500С d20	6	100,02	м.п.	246,64
			100,02		**246,64**

А Хомуты на ригель					
Этаж	ID Элемента	Наименование	Длина	Ед.изм.	Вес, кг
1-й этаж					
	ЖБ ригель 400х400	d8	33,78	м.п.	13,34
2-й этаж					
	ЖБ ригель 400х400	d8	25,67	м.п.	10,14
			59,45		**23,48**

ЖБ ригель 400х400

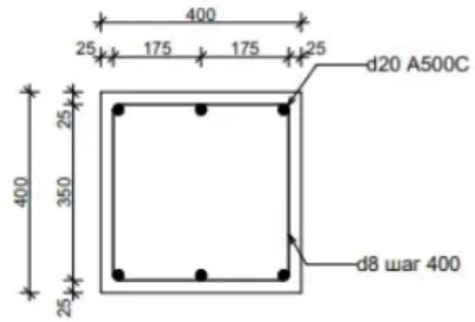

ЖБ Колонна 400х400

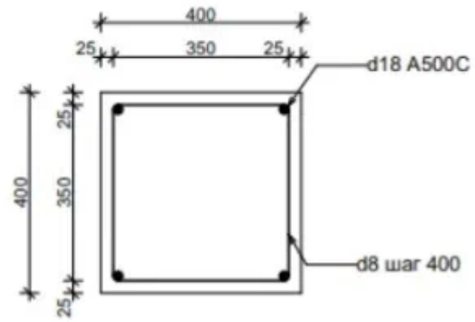

						#ID Проекта	
						кадастровый номер Россия	
Изм.	Кол.уч.	Лист	№Док.	Подп.	Дата		
Разраб.						Индивидуальный жилой дом	Стадия: #Стадия Проекта; Лист: 08; Листов:
ГАП							
Ведомость материалов ЖБ элементы							

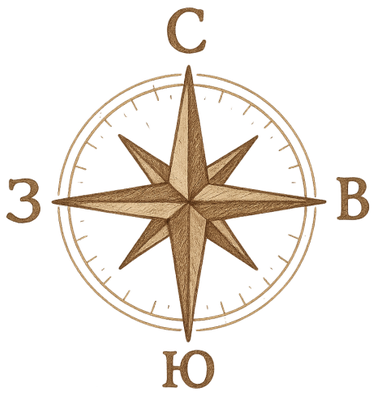

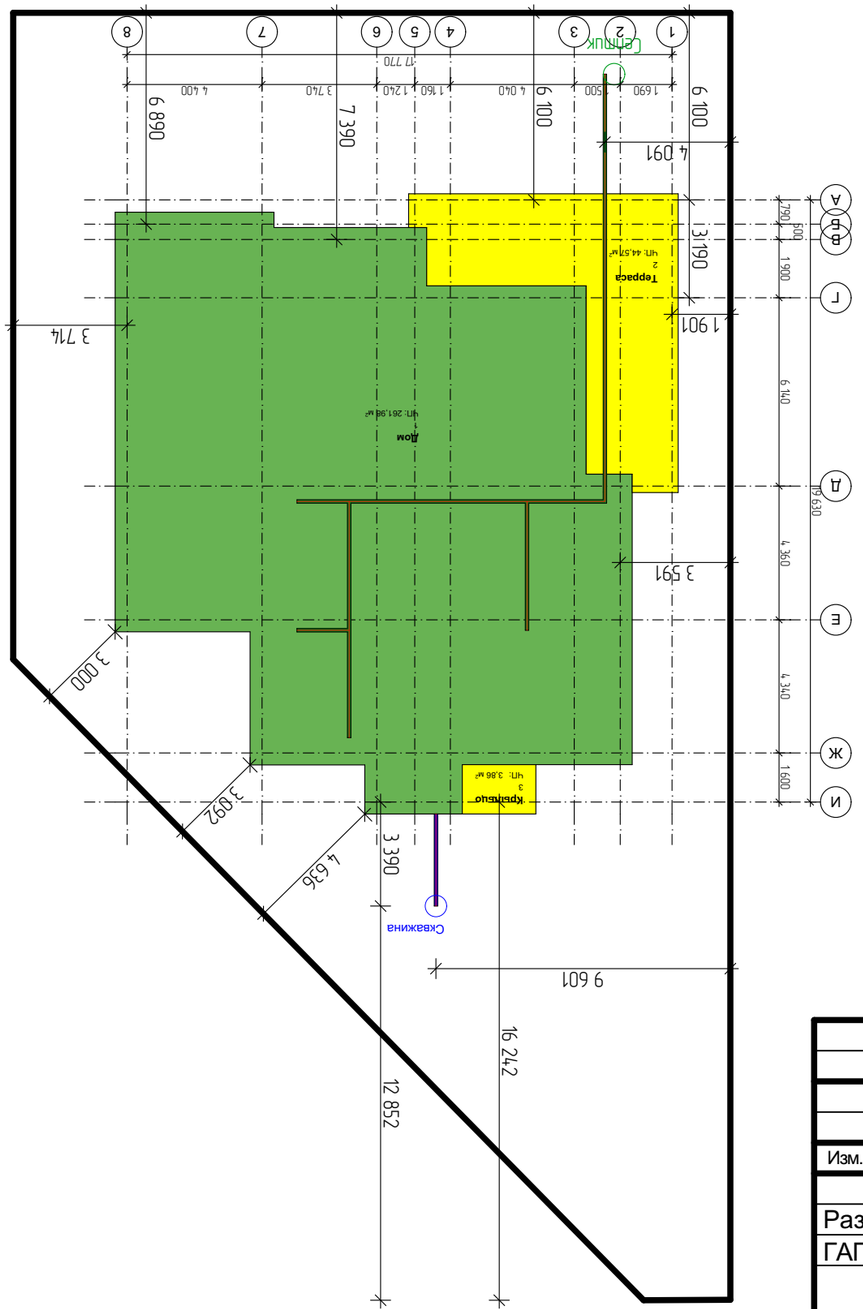

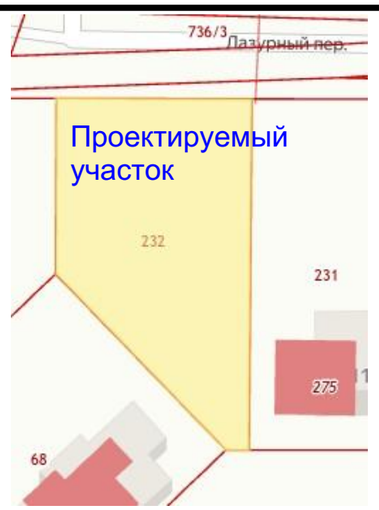

	№	Наименование	Площадь, м2
Генеральный план			
	1	Дом	261,98
	2	Терраса	44,57
	3	Крыльцо	3,86
			310,41 м²

Проектируемый дом

Терраса, крыльцо

						#ID Проекта	
						кадастровый номер Россия	
Изм.	Кол.уч.	Лист	№Док.	Подп.	Дата		
Разраб.						Индивидуальный жилой дом	Стадия: #Стадия Проекта; Лист: 09; Листов:
ГАП							
Генеральный план							

	№	Наименование	Площадь, м2
Генеральный план			
	1	Дом	261,98
	2	Терраса	44,57
	3	Крыльцо	3,86
			310,41 м²

Пояснительная записка к генеральному плану

Генеральный план разработан для земельного участка, расположенного по адресу: кадастровый номер Россия.

При проектировании генерального плана соблюдены требования градостроительного и земельного законодательства Российской Федерации, а также положения СП 42.13330.2016 «Градостроительство. Планировка и застройка городских и сельских поселений». Согласно нормативам, минимальные отступы от границ земельного участка для индивидуального жилого дома должны составлять:

- от красной линии улицы – не менее 5 м;
- от границы соседнего земельного участка – не менее 3 м;
- от хозяйственных построек – не менее 1 м;
- от деревьев – не менее 4 м;
- от кустарников – не менее 1 м.

Размещение проектируемого жилого дома на участке выполнено с учетом указанных требований, а также с обеспечением удобного подъезда, инсоляции и рационального использования территории.

Вынос осей здания в натуру осуществляется геодезическими методами. На основании утверждённого генерального плана геодезист выполняет закрепление основных осей дома на местности с использованием реперов и обноски. При этом:

- на площадке устанавливаются обноски за пределами котлована;
- на обносках закрепляются гвозди/метки, соответствующие пересечению осей здания;
- натягиваются шнуры, по которым производится разметка фундамента;
- все размеры сверяются с генеральным планом и рабочей документацией.

Таким образом, проектируемое здание расположено на участке в соответствии с нормативными требованиями и может быть реализовано без нарушений действующих правил застройки.

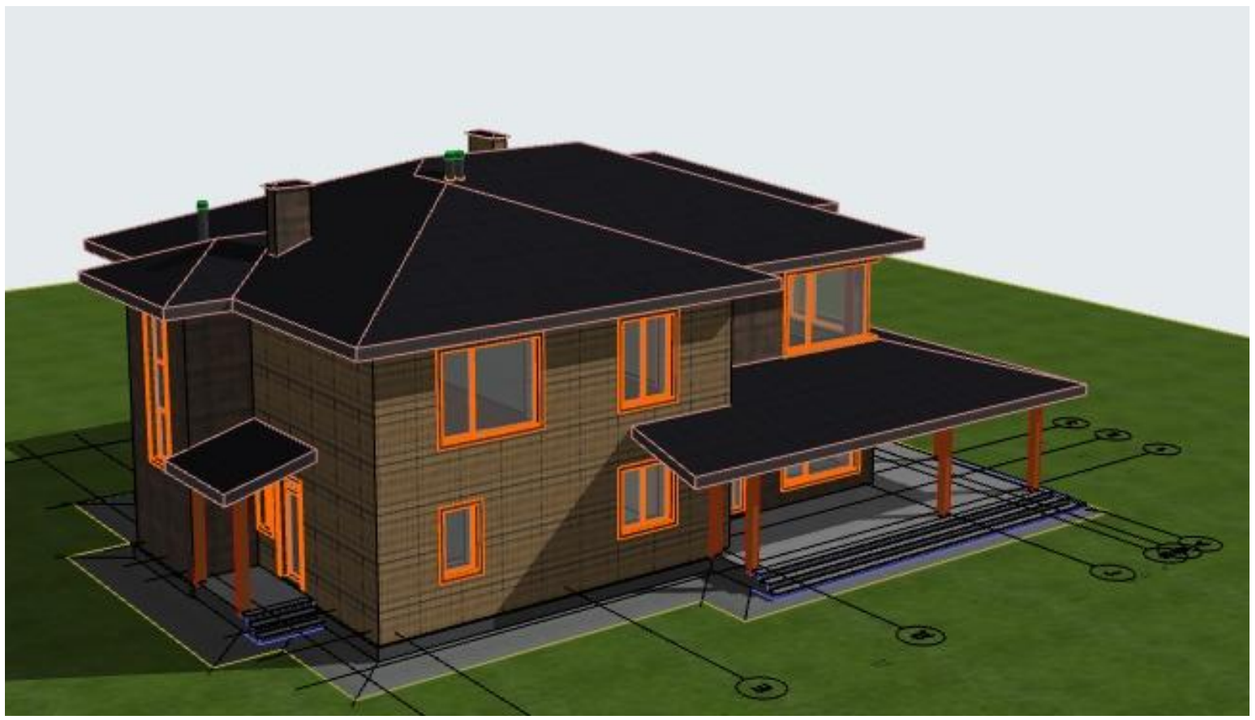

						#ID Проекта	
						кадастровый номер Россия	
Изм.	Кол.уч.	Лист	№Док.	Подп.	Дата		
Разраб.						Индивидуальный жилой дом	Стадия: #Стадия Проекта; Лист: 11; Листов:
ГАП							
3D Виды							

Пояснительная записка по устройству фундаментов

Фундаменты здания выполняются в соответствии с проектной документацией и действующими строительными нормами:

- СП 70.13330.2012 «Несущие и ограждающие конструкции»,
- СП 63.13330.2018 «Бетонные и железобетонные конструкции»,
- СП 28.13330.2017 «Защита строительных конструкций от коррозии»,
- СП 50.13330.2012 «Тепловая защита зданий».

Укладка бетона

Бетонная смесь доставляется на площадку в автосмесителях и укладывается в опалубку слоями толщиной не более 50 см. Укладка должна производиться без перерывов, исключающих образование рабочих швов. При необходимости перерыва поверхность бетона обрабатывается для обеспечения монолитного сцепления с последующим слоем.

Вибрирование

Каждый уложенный слой уплотняется глубинными вибраторами до прекращения выделения воздуха и появления цементного молочка на поверхности. Вибрирование выполняется равномерно, с шагом не более 1,5 радиуса действия вибратора. Недостаточное или избыточное вибрирование не допускается.

Уход за бетоном

После окончания укладки поверхности бетона должны быть защищены от пересыхания, промерзания и механических повреждений. В жаркую погоду бетон увлажняется и укрывается плёнкой, матами или геотекстилем. Снятие опалубки допускается только после достижения бетоном не менее 70 % проектной прочности.

Гидроизоляция подземных конструкций

Все подземные элементы фундаментов подлежат гидроизоляции в соответствии с СП 28.13330.2017. Для защиты от грунтовой влаги и капиллярного подсоса применяются:

- обмазочная битумная или полимерная гидроизоляция;
- рулонные материалы в два слоя с нахлёстом швов;
- проникающие составы или мембранные системы — при высоком уровне грунтовых вод.

Особое внимание уделяется узлам сопряжения вертикальной и горизонтальной гидроизоляции, а также местам ввода инженерных коммуникаций.

Дополнительные мероприятия

- Перед началом работ все материалы (цемент, арматура, гидроизоляционные составы) должны пройти входной контроль качества.
- Арматурные каркасы должны устанавливаться на фиксаторы, обеспечивающие проектные защитные слои бетона.
- Работы ведутся под контролем инженерно-технического персонала с обязательным ведением журнала бетонных работ и оформлением актов на скрытые работы.
- При устройстве фундаментов в зимнее время выполняются мероприятия по прогреву и защите бетона в соответствии с РД 34.48.201–97 и рекомендациями производителей добавок.

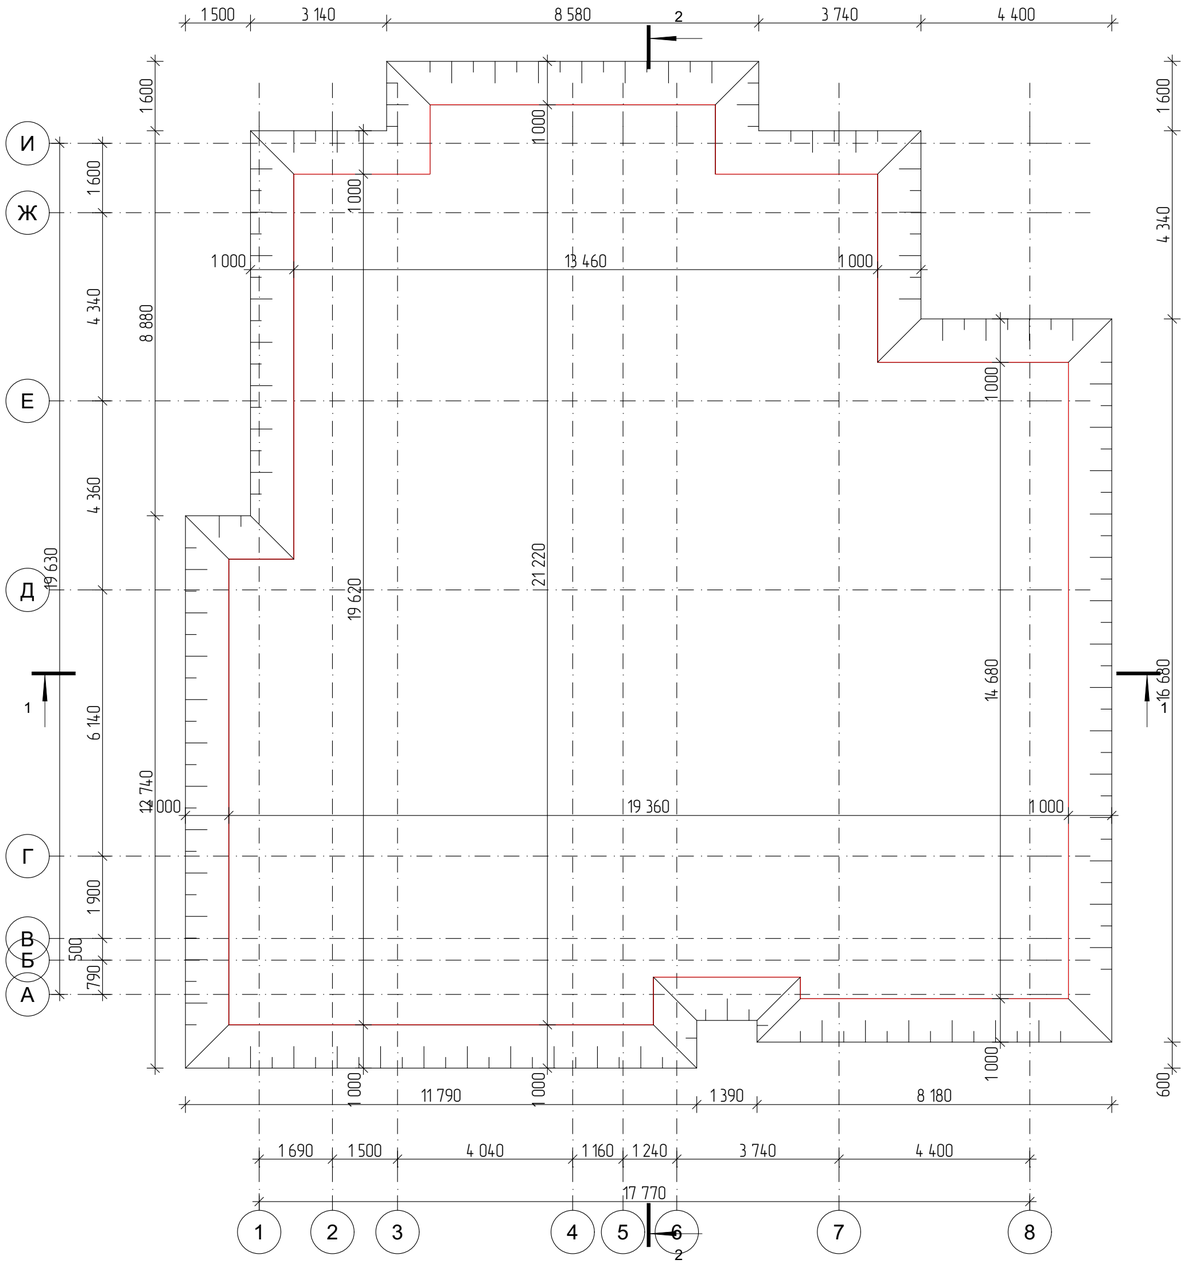

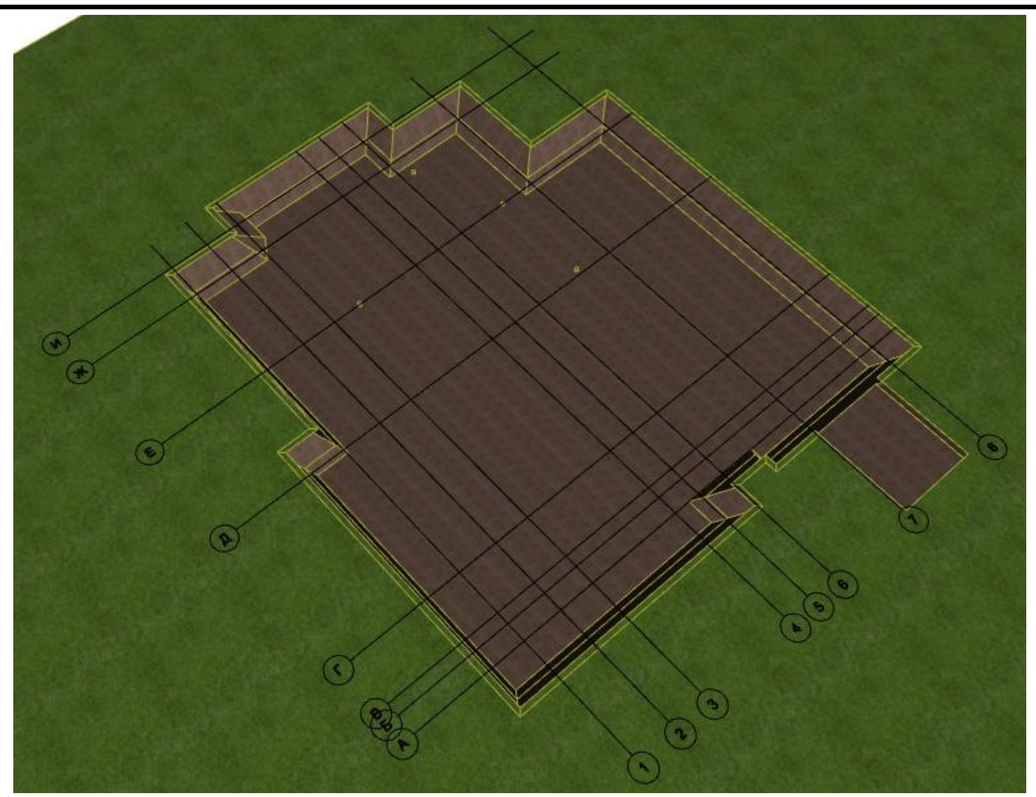

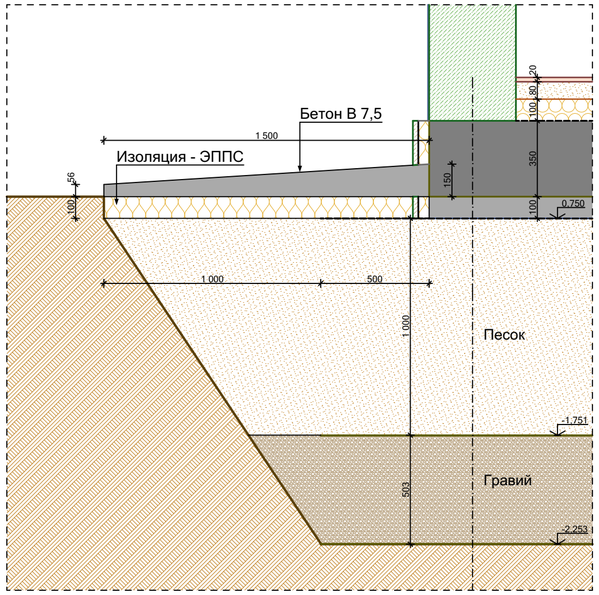

						#ID Проекта		
						кадастровый номер Россия		
Изм.	Колуч.	Лист	№Док.	Подп.	Дата			
Разраб.						Индивидуальный жилой дом	Стадия	Лист	Листов
ГАП							#Стадия Проекта	13	
План котлована									

Пояснительная записка к устройству фундаментной плиты

Фундаментная плита принята в качестве основания здания исходя из расчетных нагрузок от здания и требований нормативных документов (СП 22.13330.2016 «Основания зданий и сооружений», СП 50-101-2004 «Проектирование и устройство оснований и фундаментов зданий и сооружений»).

1. Подготовительные работы

Перед началом устройства фундаментной плиты необходимо:

- выполнить геодезическую разбивку осей здания с вынесением в натуру контуров плиты;
- снять растительный слой грунта на проектную глубину;
- произвести планировку дна котлована, уплотнение грунта основания;
- выполнить подготовку из песка или щебня с послойным уплотнением;
- уложить слой тощего бетона (бетонная подготовка) толщиной 80–100 мм.

2. Гидроизоляция

- На бетонную подготовку укладывается рулонная гидроизоляция (рубероид, ПВХ-мембрана или аналогичные материалы) в два слоя с напуском и проклейкой швов.

3. Армирование

- Армирование выполняется в два рабочих пояса (верхний и нижний), соединённых между собой вертикальными хомутами или сварными каркасами.
- Диаметр арматуры — Ø14 мм, класс А500С, шаг сетки 250 мм.
- Защитный слой бетона: снизу — 50 мм, сверху — 25 мм.

4. Бетонирование

- Бетонная смесь — класс прочности В25, морозостойкость не ниже F150, водонепроницаемость W6.
- Укладка бетона производится за один прием по всей площади плиты.
- При укладке обязательна механическая виброобработка для удаления воздуха и уплотнения смеси.
- Поверхность бетона после выравнивания укрывается полиэтиленовой пленкой и выдерживается во влажных условиях не менее 7 суток.
- Допускаемые отклонения от проектного горизонта поверхности плиты не должны превышать ±10 мм на всё здание и ±5 мм на 2 м длины правила (СП 70.13330.2012 «Несущие и ограждающие конструкции»).

5. Работы в зимнее время

При производстве бетонных работ в зимний период необходимо:

- применять бетонные смеси с противоморозными добавками или обеспечивать прогрев конструкций;
- предусматривать утепление свежеуложенного бетона теплоизоляционными матами, брезентом или пленкой по принципу «термоса»;
- при необходимости применять электротермический прогрев (провода ПНСВ, электроды, инфракрасные излучатели);
- температура бетона при укладке должна быть не ниже +5 °С, в процессе твердения — поддерживаться согласно СП 70.13330.2012;
- запрещается бетонировать при отрицательных температурах без мер по обогреву или добавкам.

6. Контроль качества

- Контроль геометрических размеров котлована, подготовки и толщины слоев выполняется геодезическими средствами.
- Контроль качества бетона осуществляется лабораторными испытаниями образцов.
- Работы выполняются в соответствии с требованиями СП 70.13330.2012 «Несущие и ограждающие конструкции».

						#ID Проекта		
						кадастровый номер Россия		
Изм.	Кол.уч.	Лист	№Док.	Подп.	Дата			
Разраб.						Индивидуальный жилой дом	Стадия: #Стадия Проекта	Лист: 14 / Листов:
ГАП								
ПЗ Фундаментная плита								

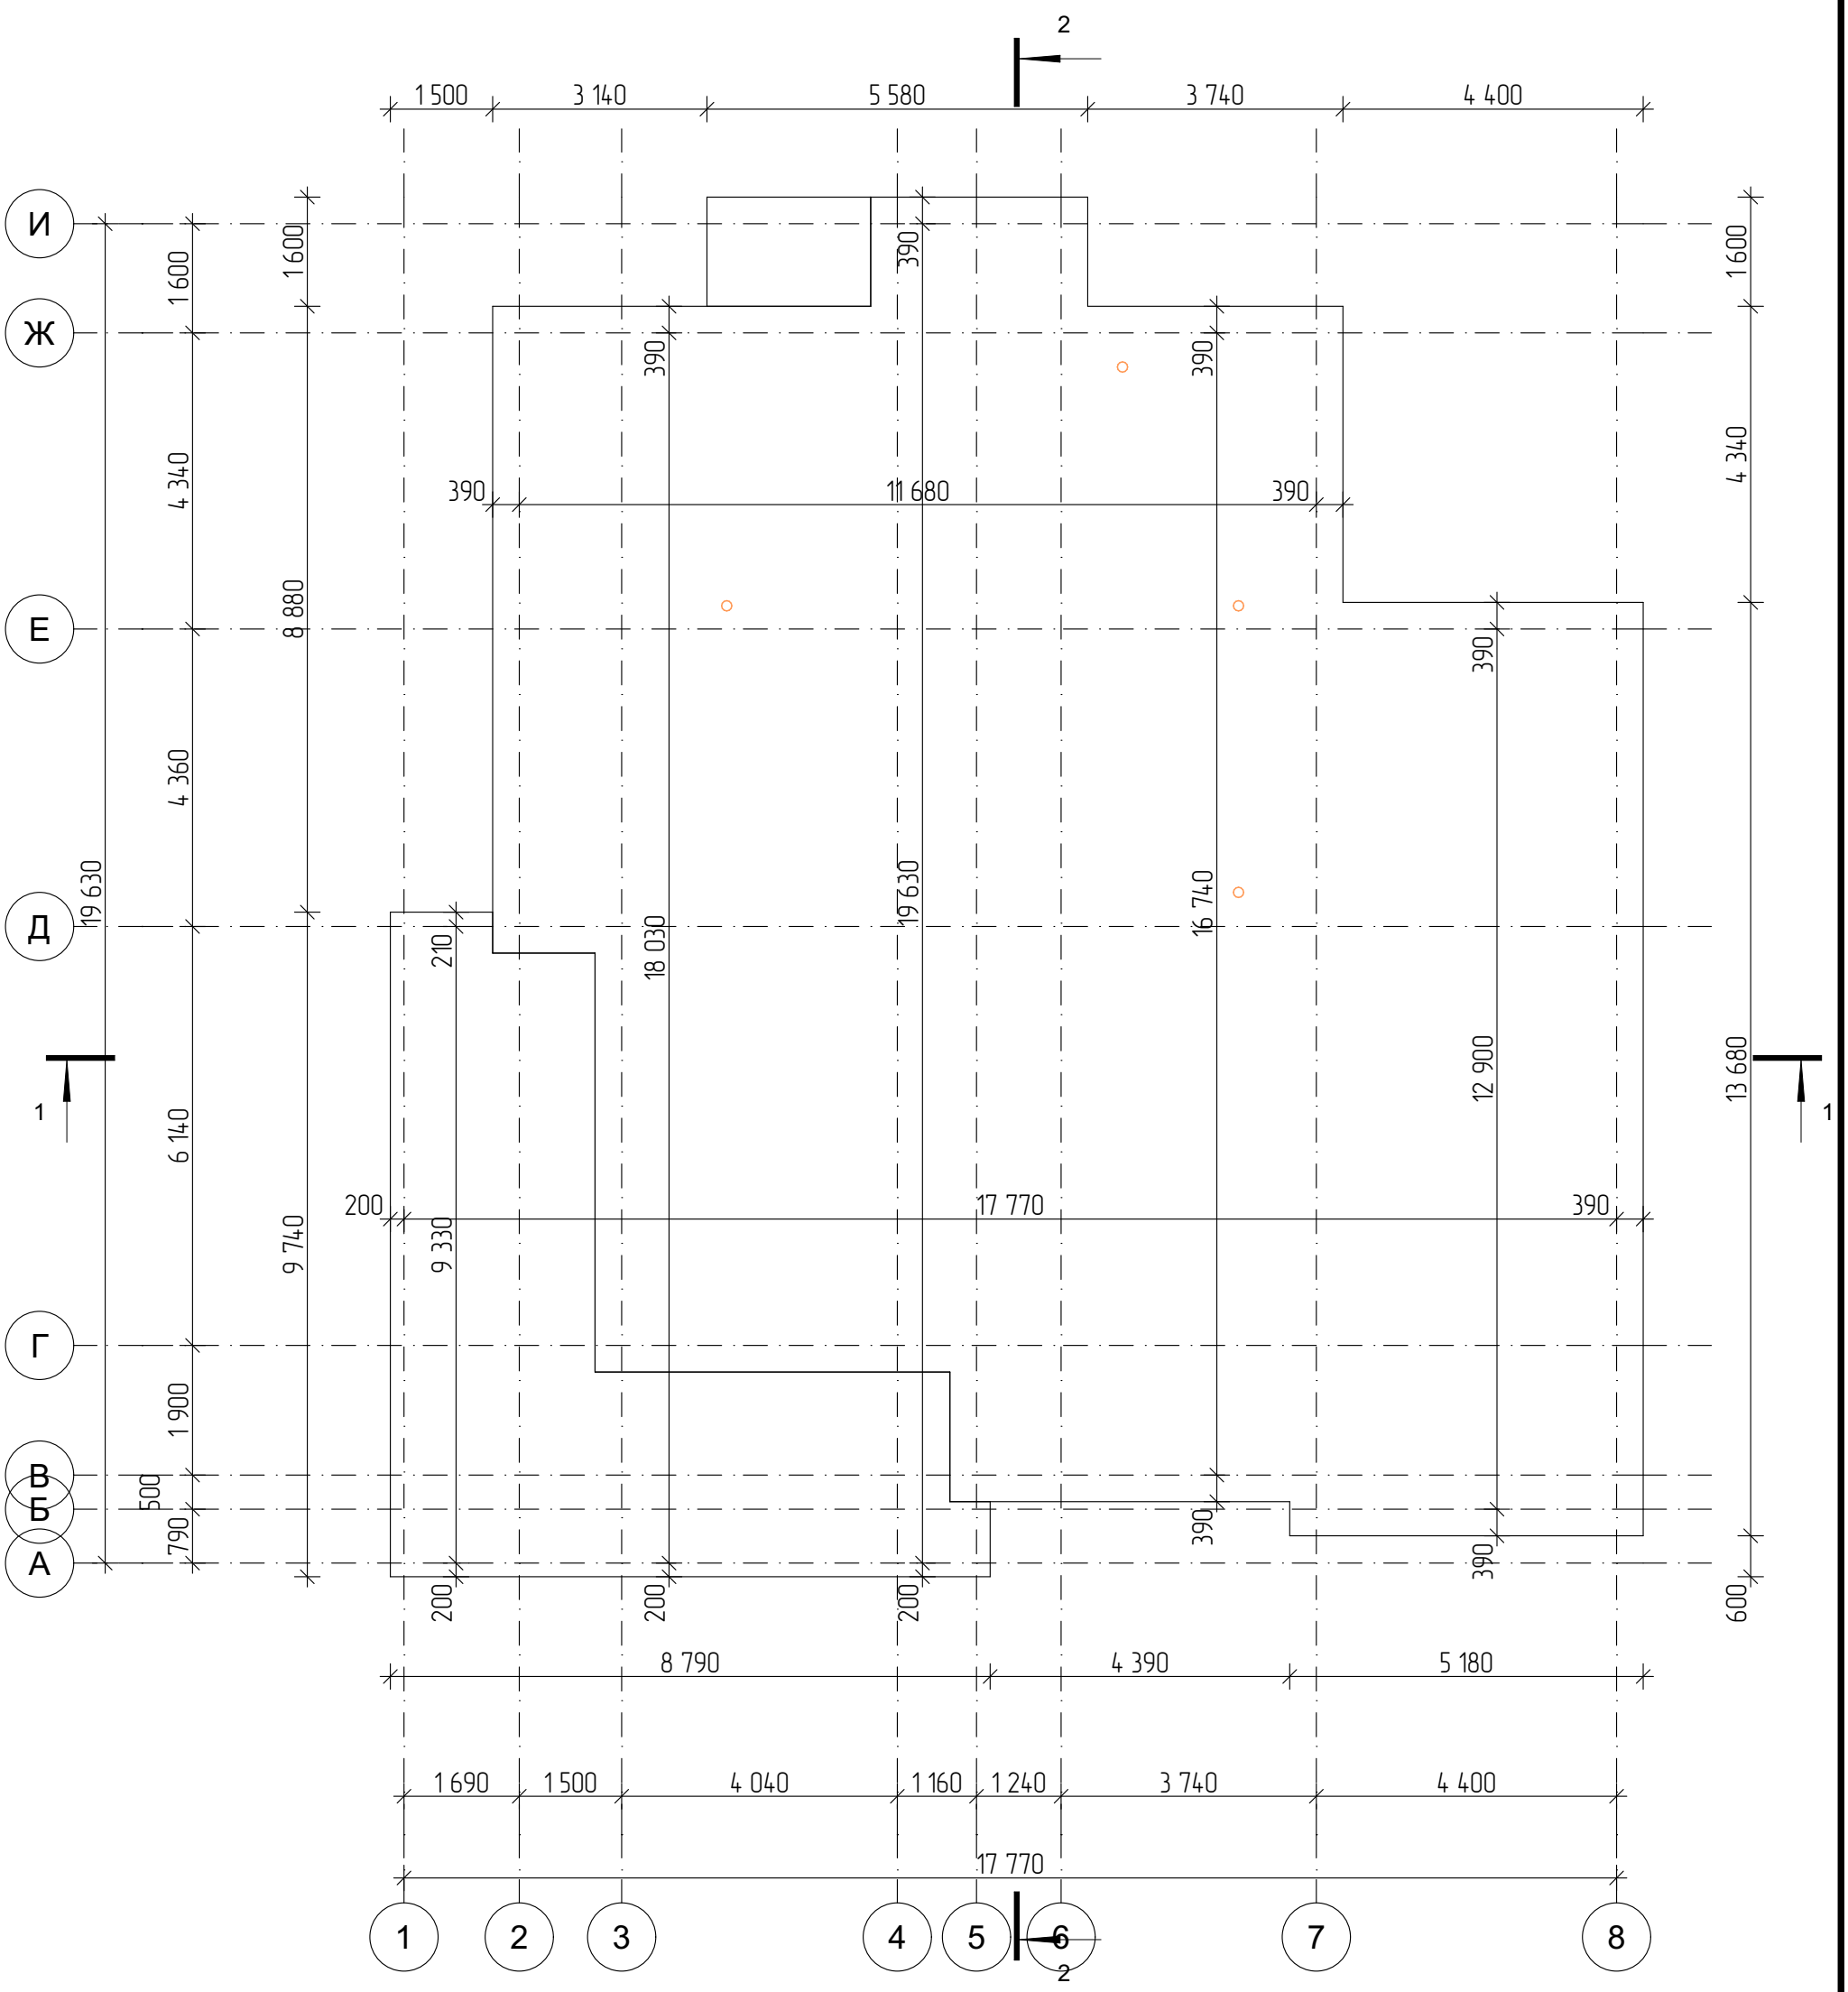

						#ID Проекта		
						кадастровый номер Россия		
Изм.	Кол.уч.	Лист	№Док.	Подп.	Дата			
Разраб.						Индивидуальный жилой дом	Стадия: #Стадия Проекта	Лист: 15 / Листов:
ГАП								
План фундамента								

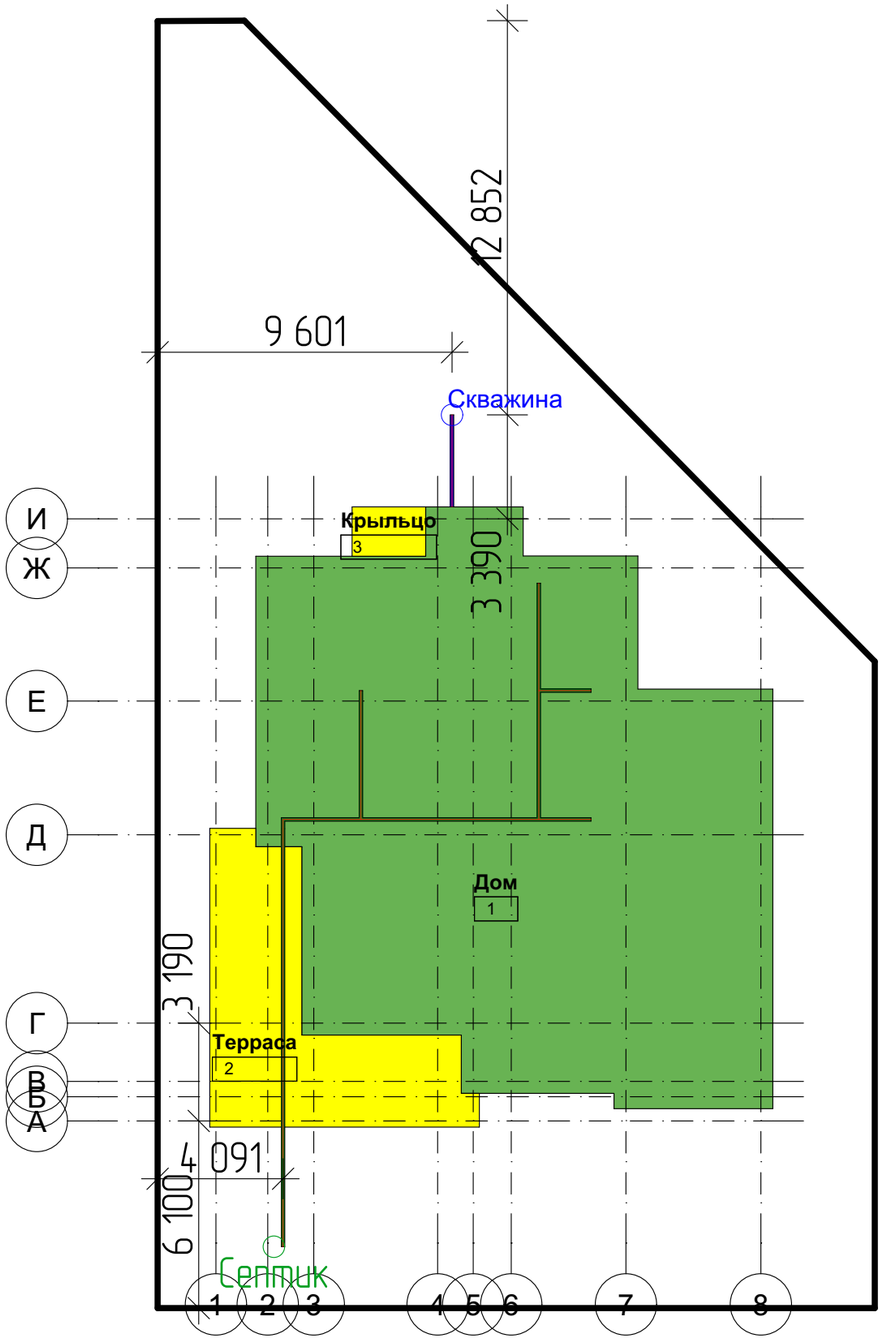

						#ID Проекта		
						кадастровый номер Россия		
Изм.	Кол.уч.	Лист	№Док.	Подп.	Дата			
Разраб.						Индивидуальный жилой дом	Стадия	Лист	Листов
ГАП							#Стадия Проекта	16	
Наружные сети									

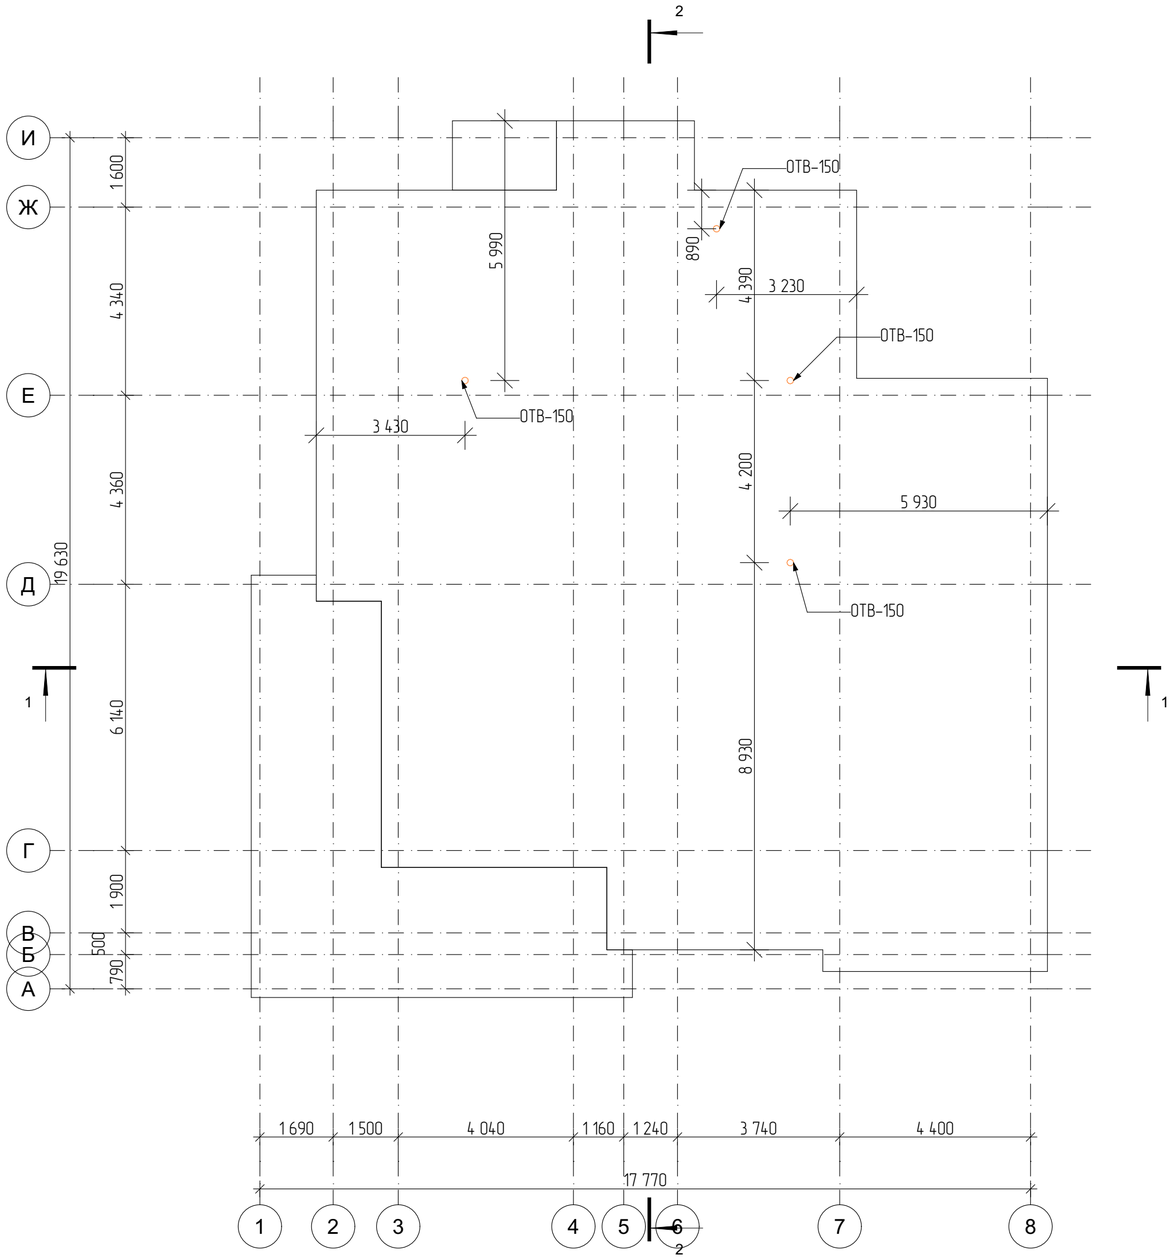

Пояснительная записка

1. Для устройства водопровода используется труба ПЭ100 SDR11 d40×3,7 (PN16), обеспечивающая подачу воды под рабочим давлением до 16 атм.

2. Для системы канализации применяется труба ПВХ SN4 d110×3,2 (канализация), предназначенная для наружной и внутренней самотечной разводки.

3. Указанные трубопроводы необходимо смонтировать в проектное положение до выполнения монолитных работ, с обеспечением прочной фиксации и защиты от повреждений.

4. На планах предусмотрены отверстия диаметром 150 мм для прокладки канализационных труб, что обеспечивает монтажный зазор и упрощает установку.

Внутренняя разводка по сантехническим приборам выполняется в толще стяжки пола и требует разработки отдельного специализированного раздела проекта. На представленных планах коммуникаций показаны только основные магистрали.

Коммуникации		
Назначение	Строительный Материал	Длина, мм
Водопровод	Труба ПЭ100 SDR11 d40×3,7 (PN16)	3 000
Канализация	Труба ПВХ SN4 d110×3,2 (канализация)	37 680

							#ID Проекта	
							кадастровый номер Россия	
Изм.	Колуч.	Лист	№Док.	Подп.	Дата			
Разраб.						Индивидуальный жилой дом	Стадия	Лист	Листов
ГАП							#Стадия Проекта	17	
План коммуникаций (только пол)									

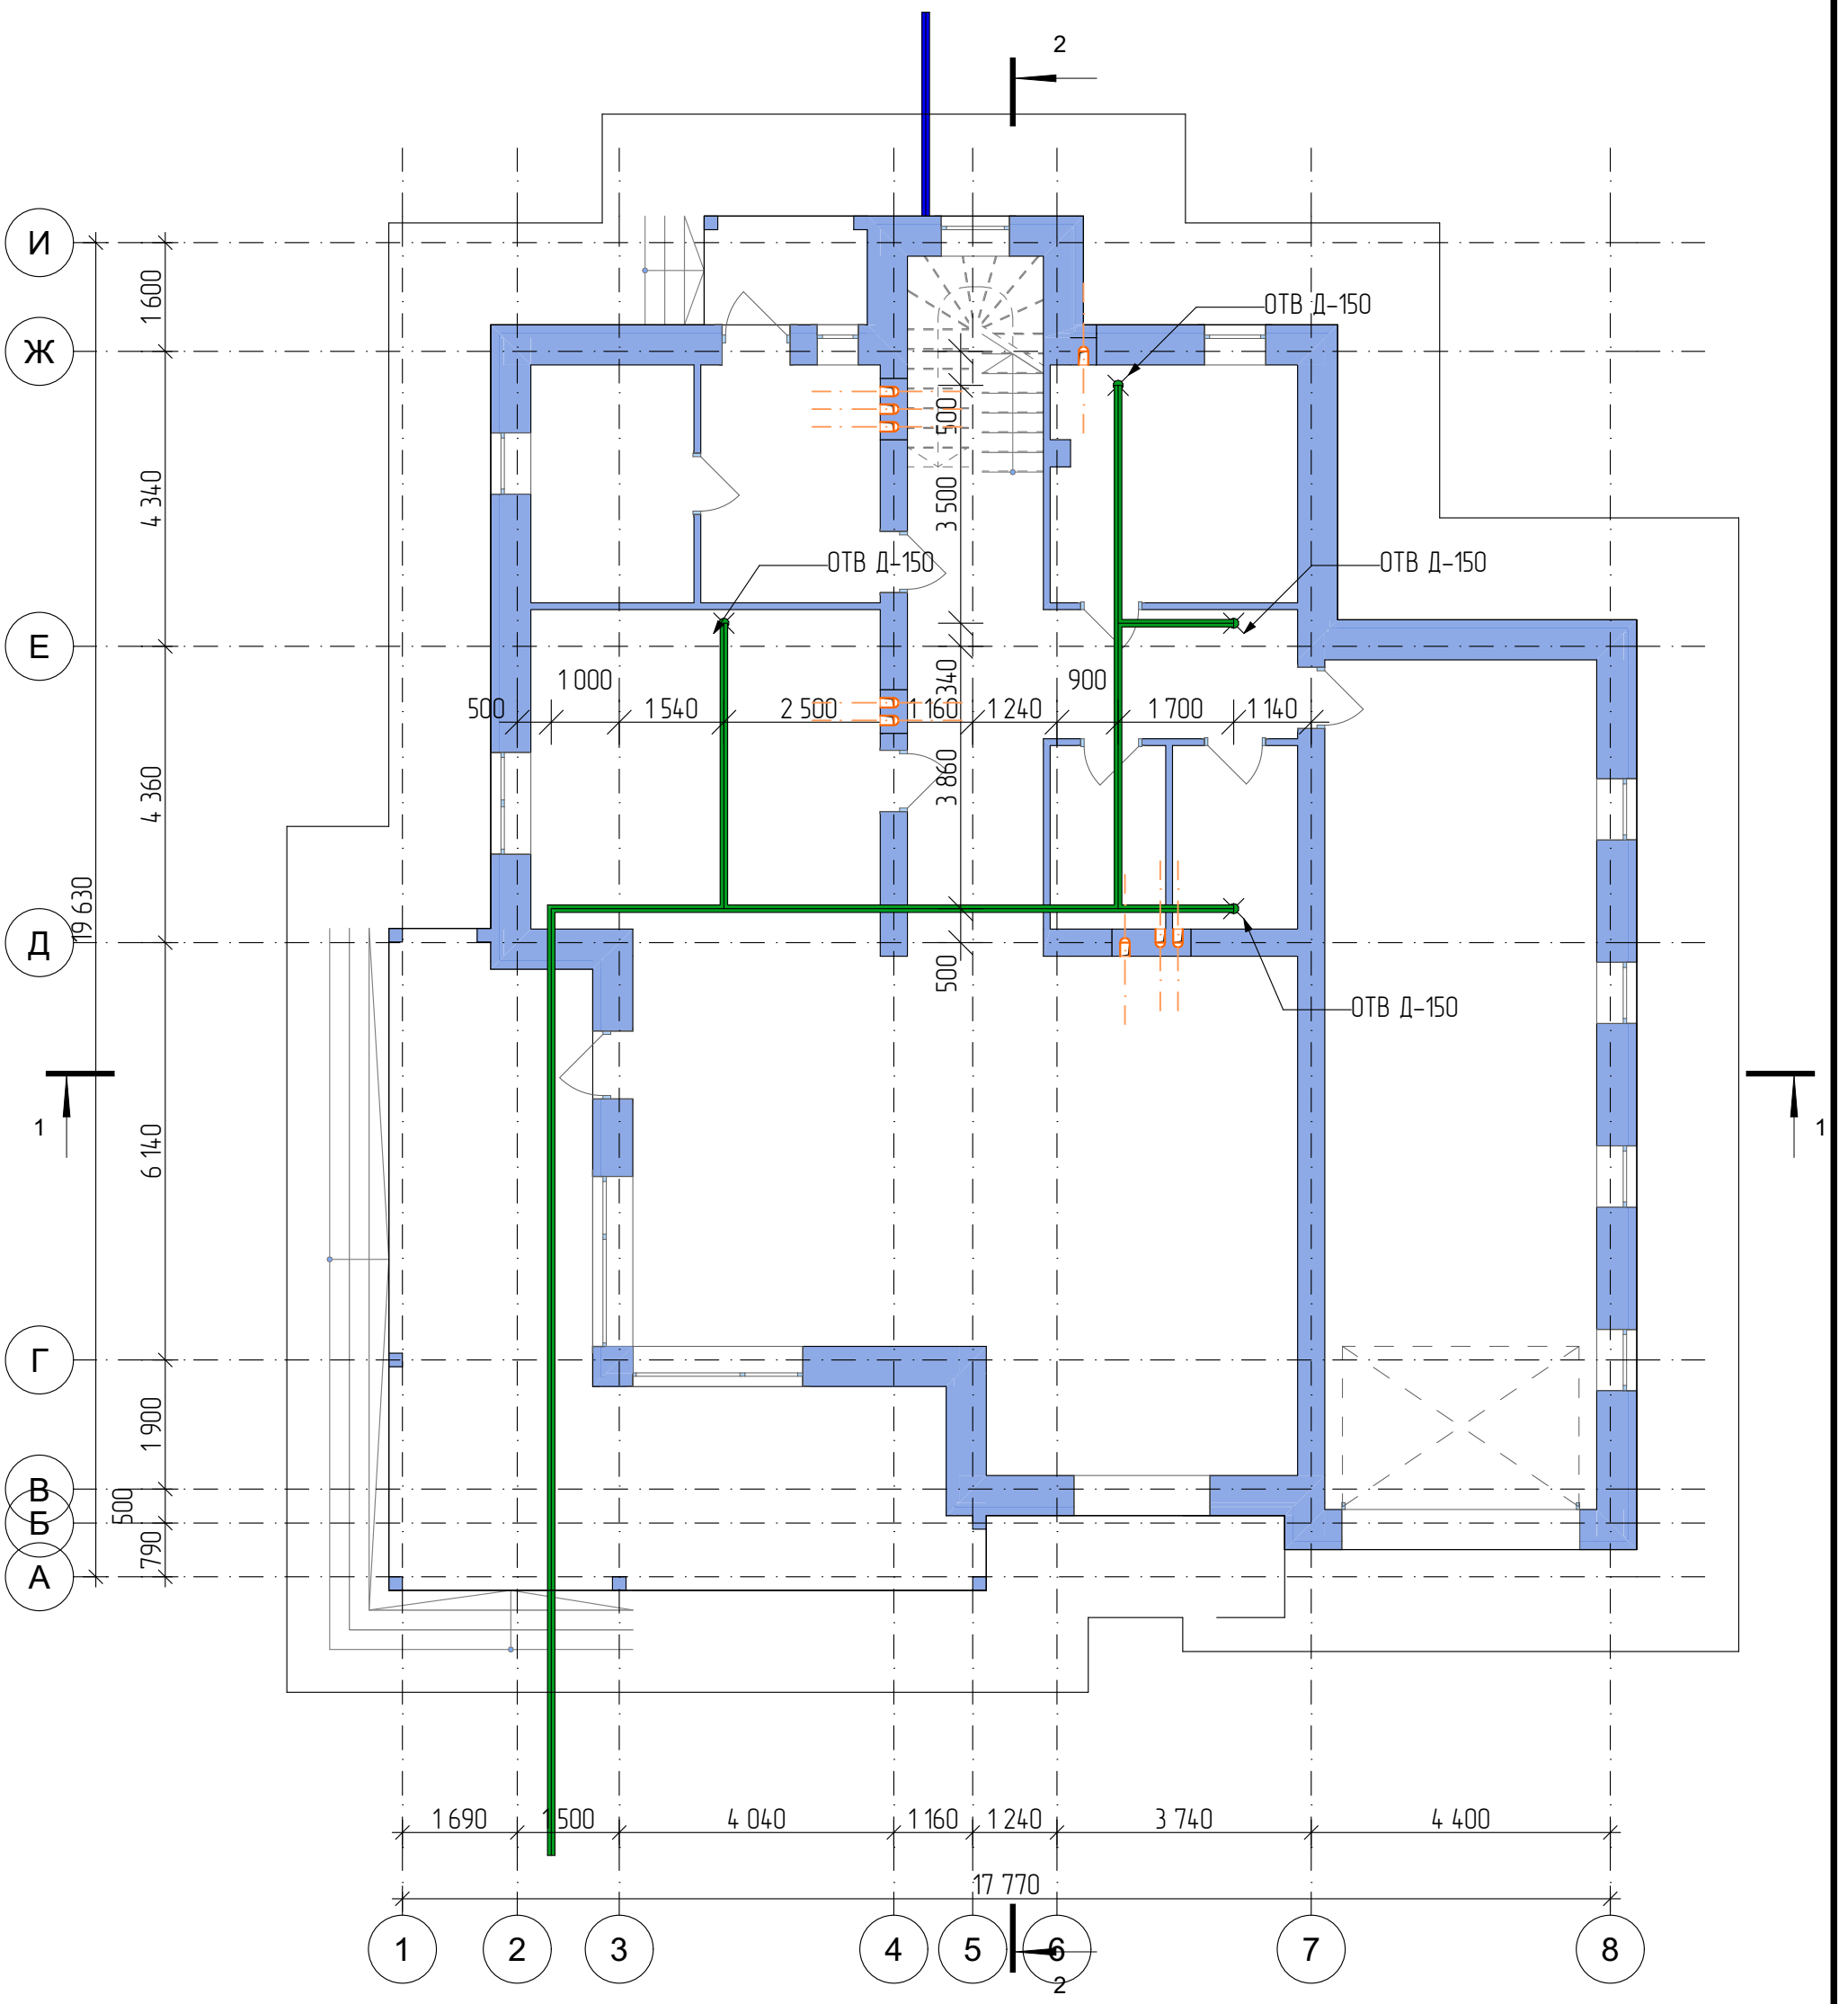

						#ID Проекта	
						кадастровый номер Россия	
Изм.	Кол.уч.	Лист	№Док.	Подп.	Дата		
Разраб.						Индивидуальный жилой дом	Стадия: #Стадия Проекта; Лист: 18; Листов:
ГАП							
План коммуникаций							

Ведомость материалов фундаментной плиты			
Строительный материал	**Наименование**	Объем, м3	Площадь, м2
Бетон В 7,5			
	Плита фундамента (дом)	26,20	262,03
	Плита фундамента (крыльцо))	0,38	3,84
	Плита фундамента (терраса))	4,46	44,57
		31,04 м³	
Бетон В25			
	Плита фундамента (дом)	117,77	261,96
	Плита фундамента (крыльцо))	1,73	3,84
	Плита фундамента (терраса))	20,01	44,57
		139,51 м³	
Изоляция - ЭППС			
	Плита фундамента (дом)	21,15	212,59
		21,15 м³	
Плитка - Напольная			
	Плита фундамента (дом)	4,26	212,85
	Плита фундамента (крыльцо))	0,08	3,76
	Плита фундамента (терраса))	0,89	44,29
		5,23 м³	
Стяжка ЦПР			
	Плита фундамента (дом)	17,02	212,84
	Плита фундамента (крыльцо))	0,38	3,76
	Плита фундамента (терраса))	4,39	44,29
		21,79 м³	
		218,72 м³	

Утеплитель на боковую поверхность фундамента			
Наименование	Площадь, м2	Объем, м3	Толщина, мм
Изоляция - ЭППС	16,01	0,81	50

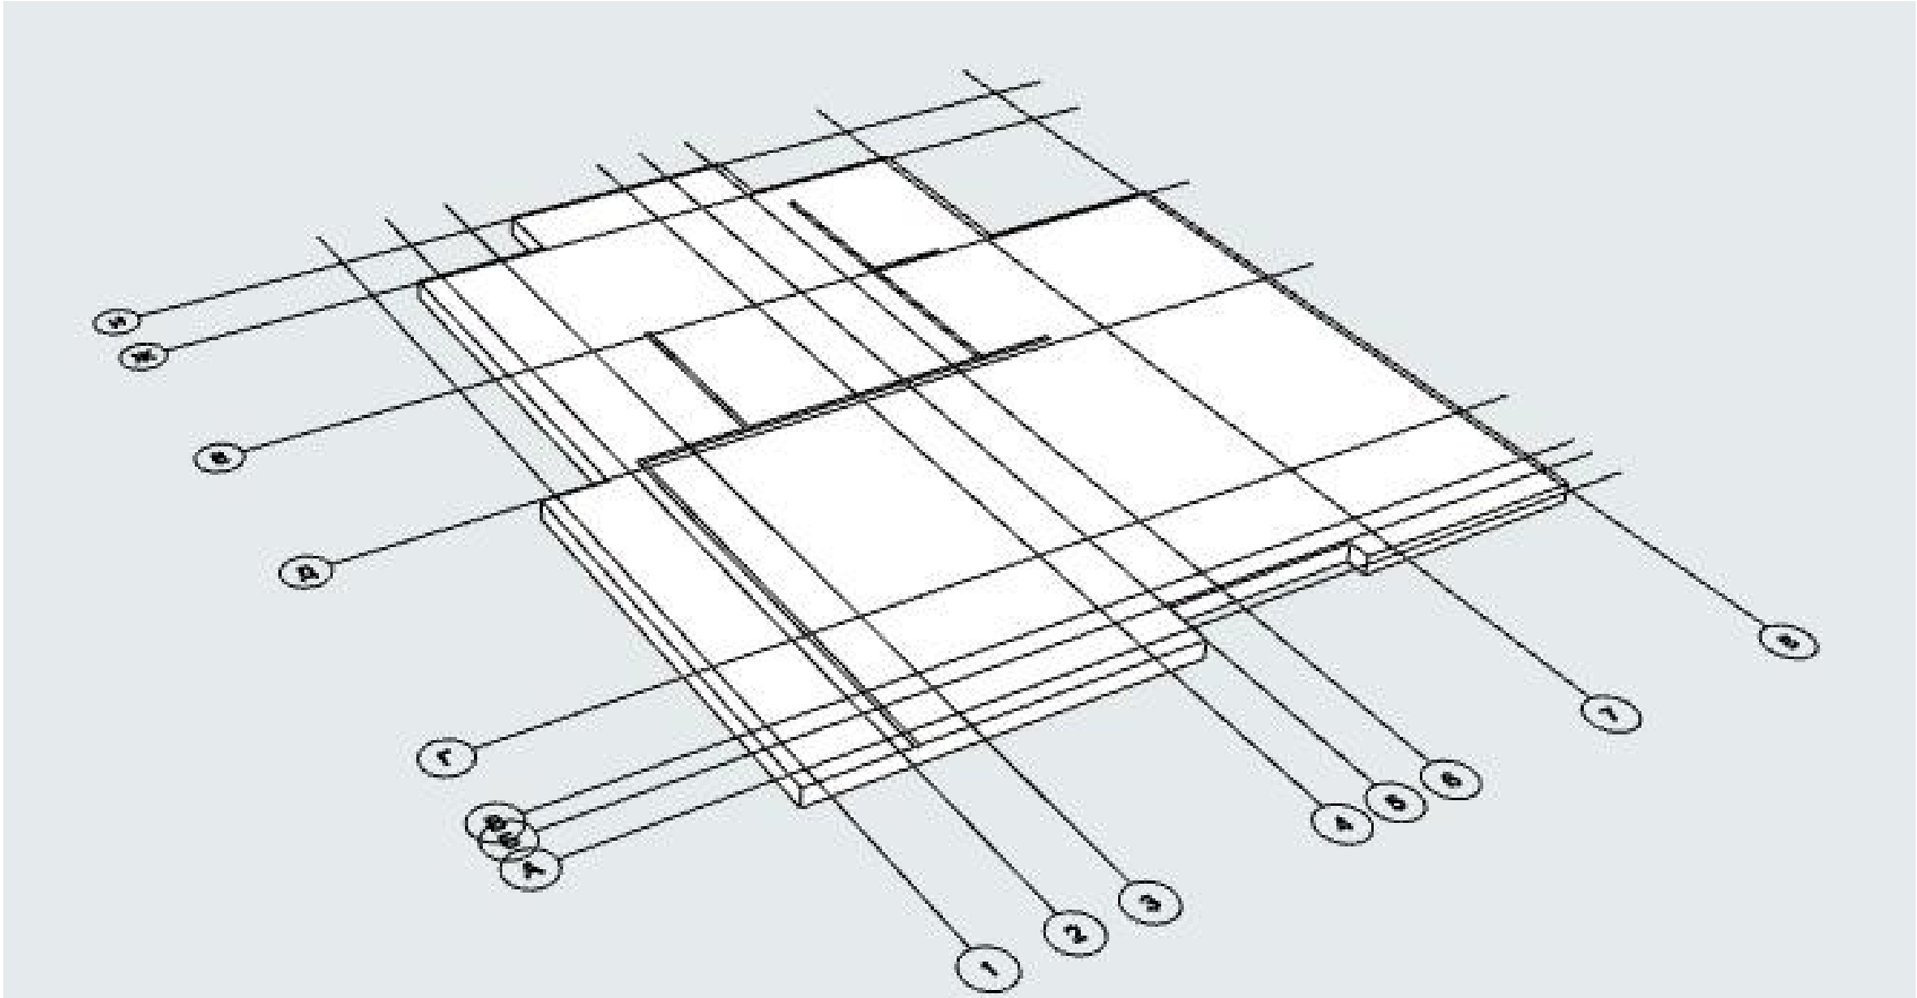

						#ID Проекта		
						кадастровый номер Россия		
Изм.	Кол.уч.	Лист	№Док.	Подп.	Дата			
Разраб.						Индивидуальный жилой дом	Стадия	Лист	Листов
ГАП							#Стадия Проекта	20	
3D Вид фундамента									

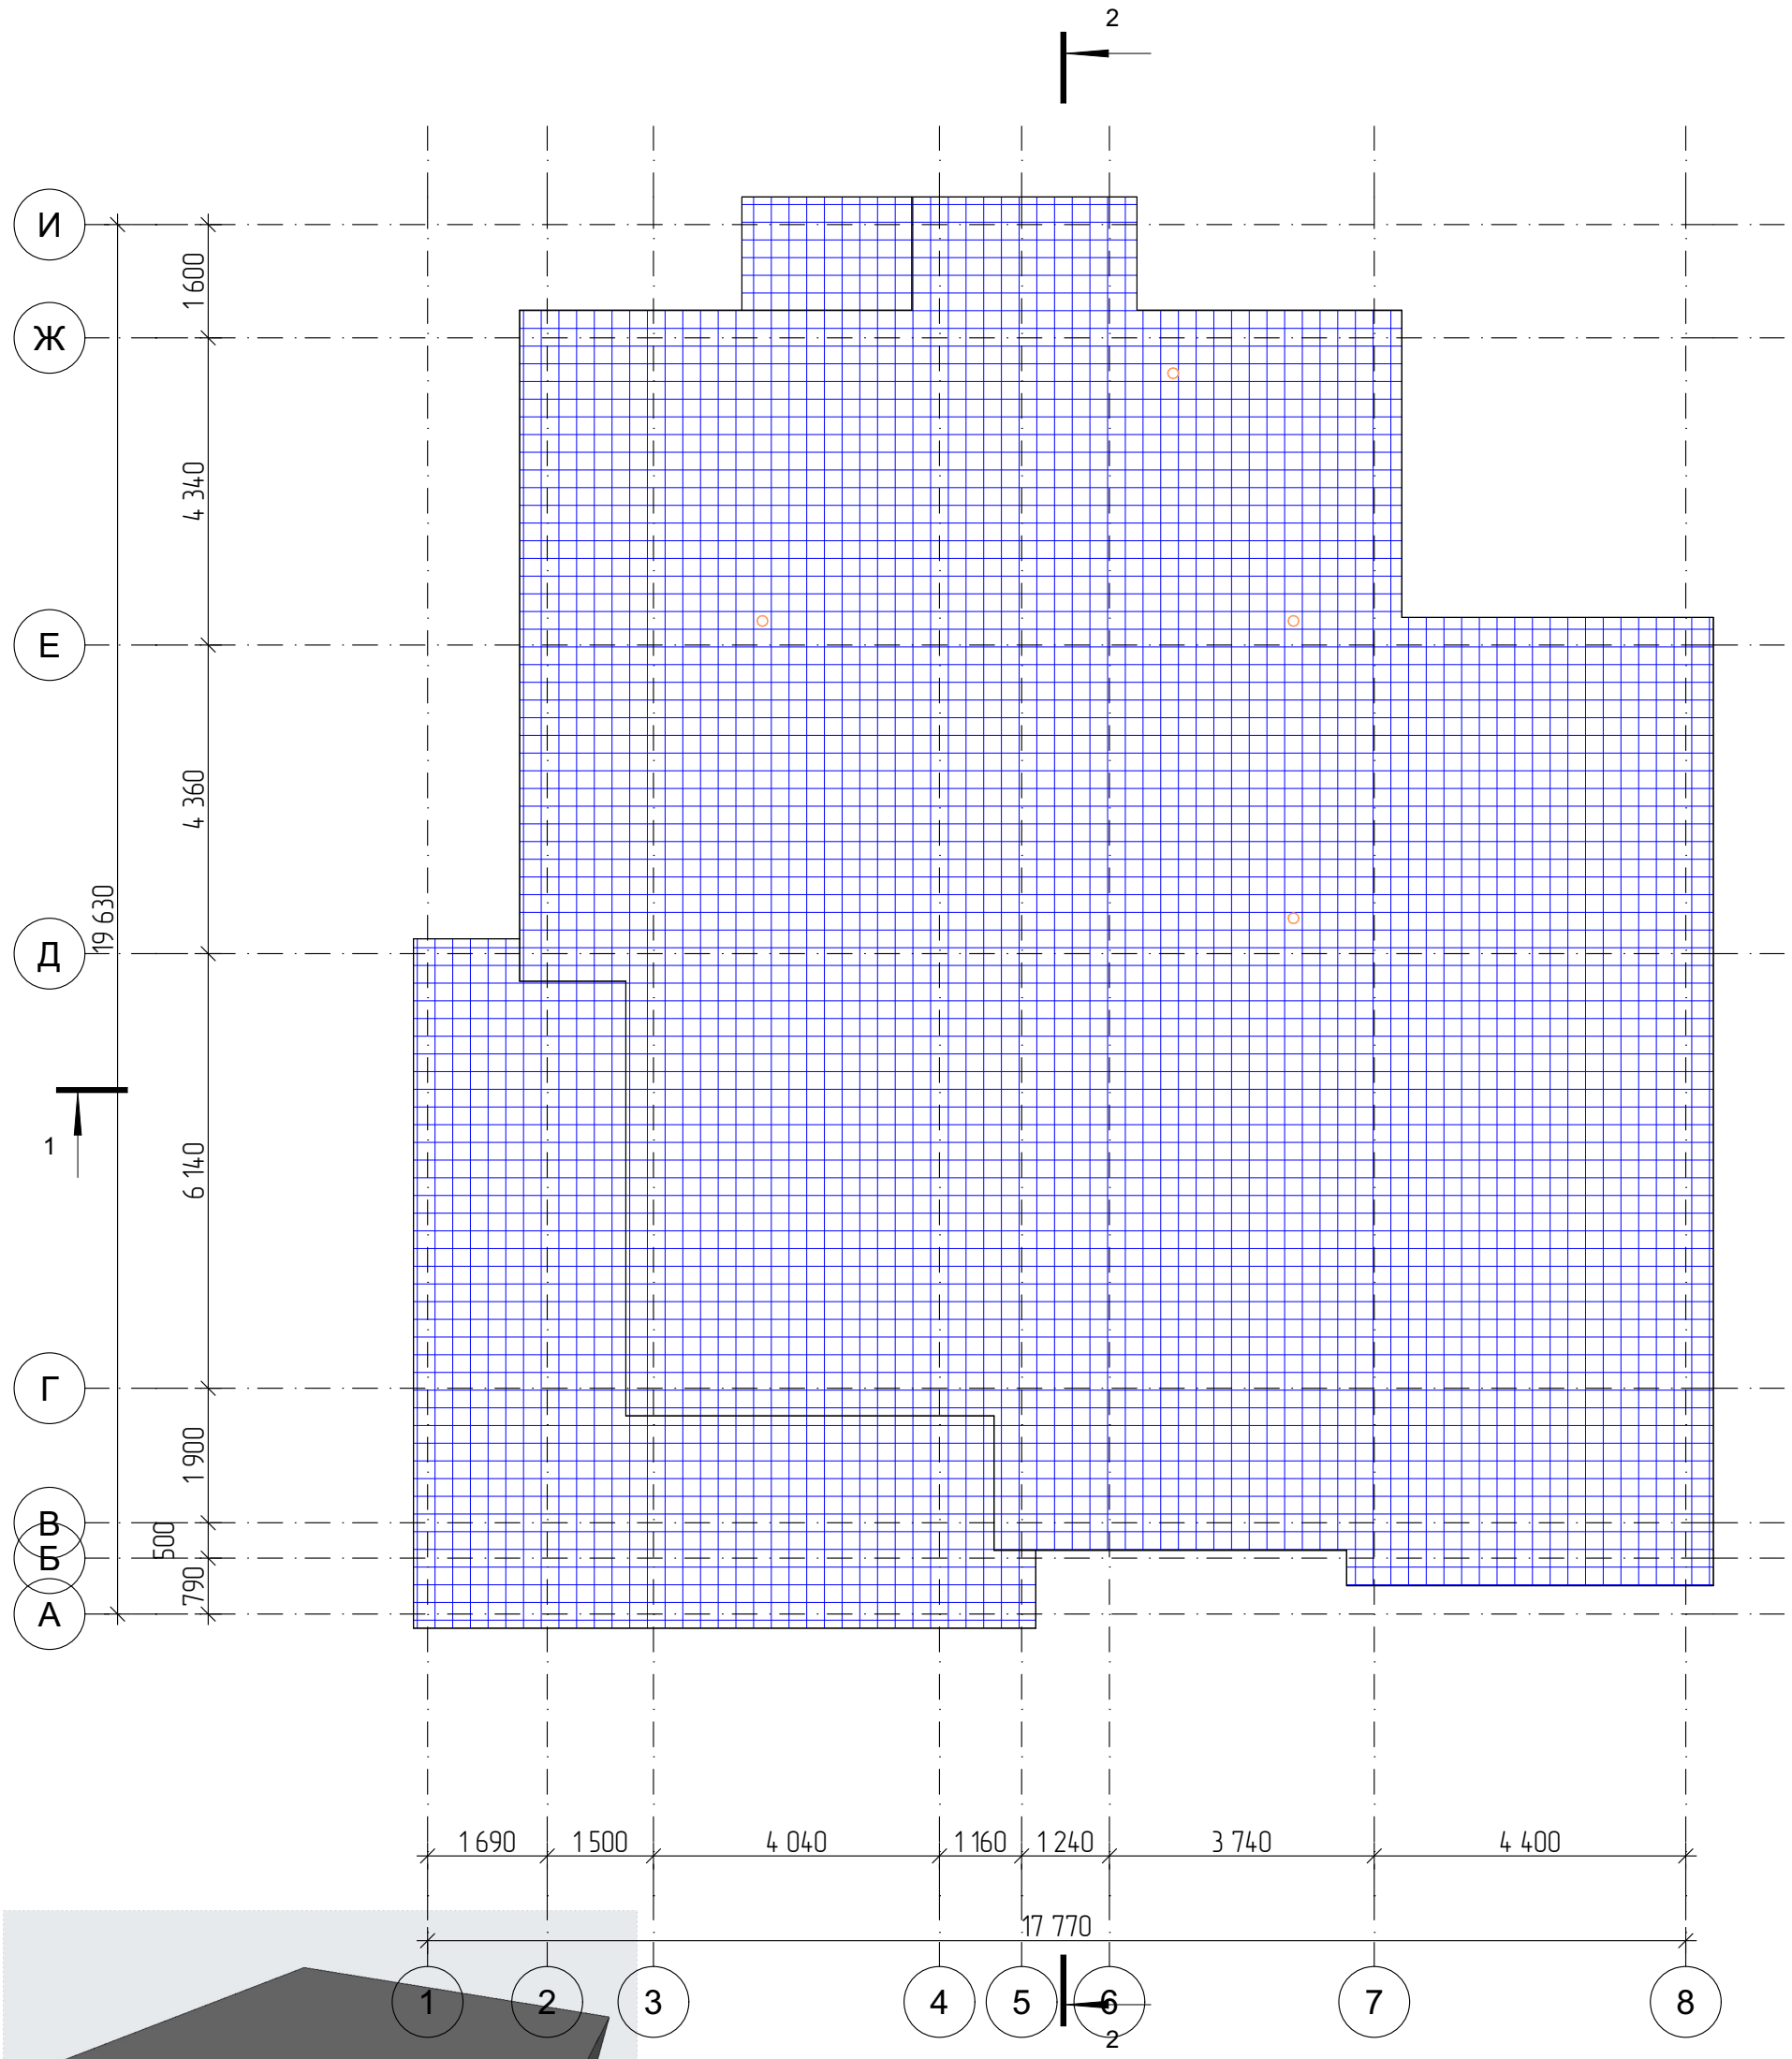

						#ID Проекта	
						кадастровый номер Россия	
Изм.	Кол.уч.	Лист	№Док.	Подп.	Дата		
Разраб.						Индивидуальный жилой дом	Стадия: #Стадия Проекта; Лист: 21; Листов:
ГАП							
Схема нижнего армирования фундаментной плиты							

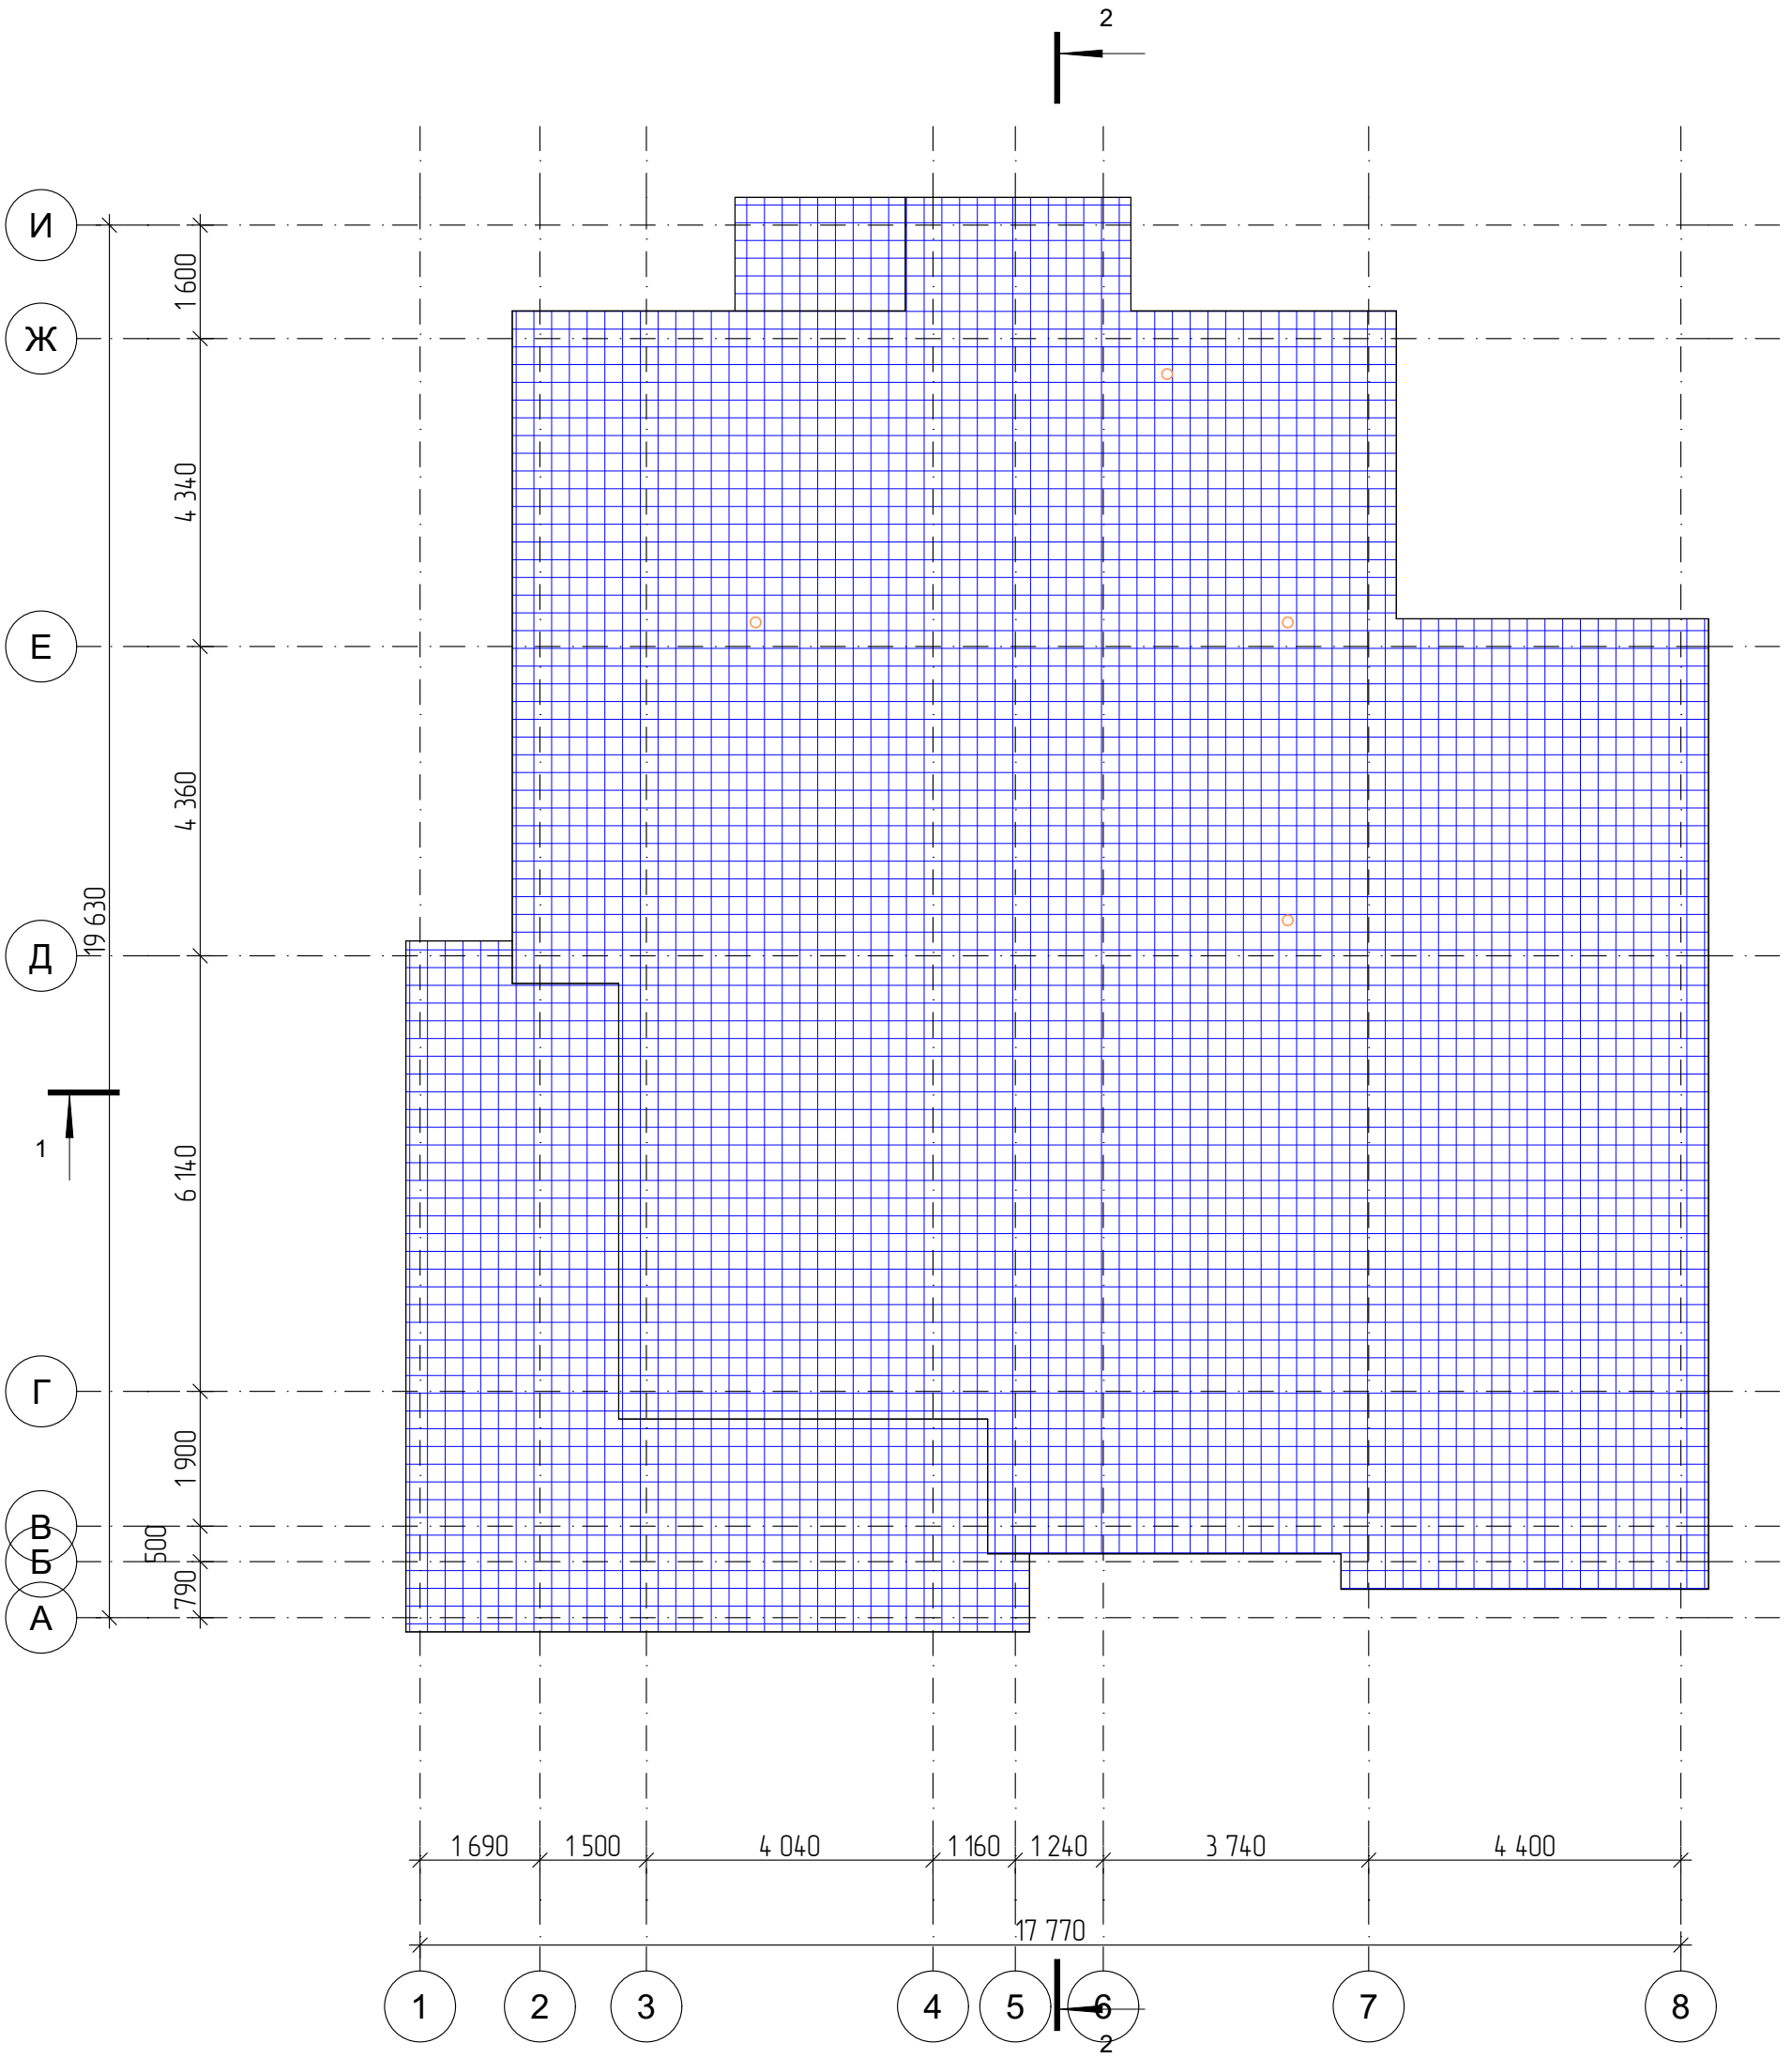

						#ID Проекта	
						кадастровый номер Россия	
Изм.	Кол.уч.	Лист	№Док.	Подп.	Дата		
Разраб.						Индивидуальный жилой дом	Стадия: #Стадия Проекта; Лист: 22; Листов:
ГАП							
Схема верхнего армирования фундаментной плиты							

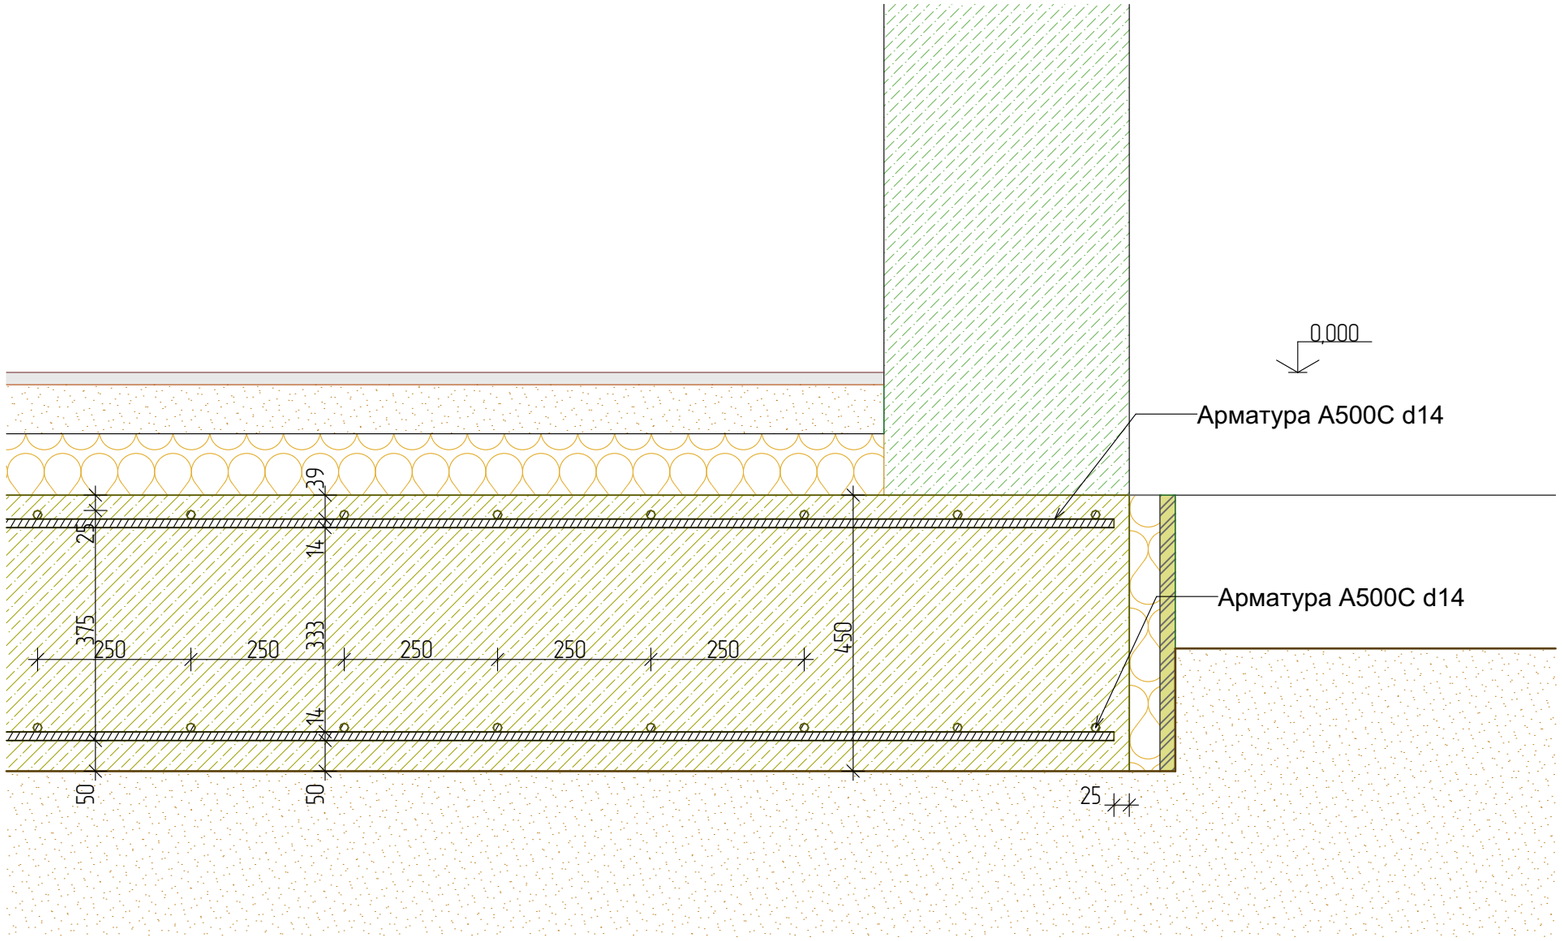

						#ID Проекта		
						кадастровый номер Россия		
Изм.	Кол.уч.	Лист	№Док.	Подп.	Дата			
Разраб.						Индивидуальный жилой дом	Стадия	Лист	Листов
ГАП							#Стадия Проекта	23	
Узел армирования фундаментной плиты									

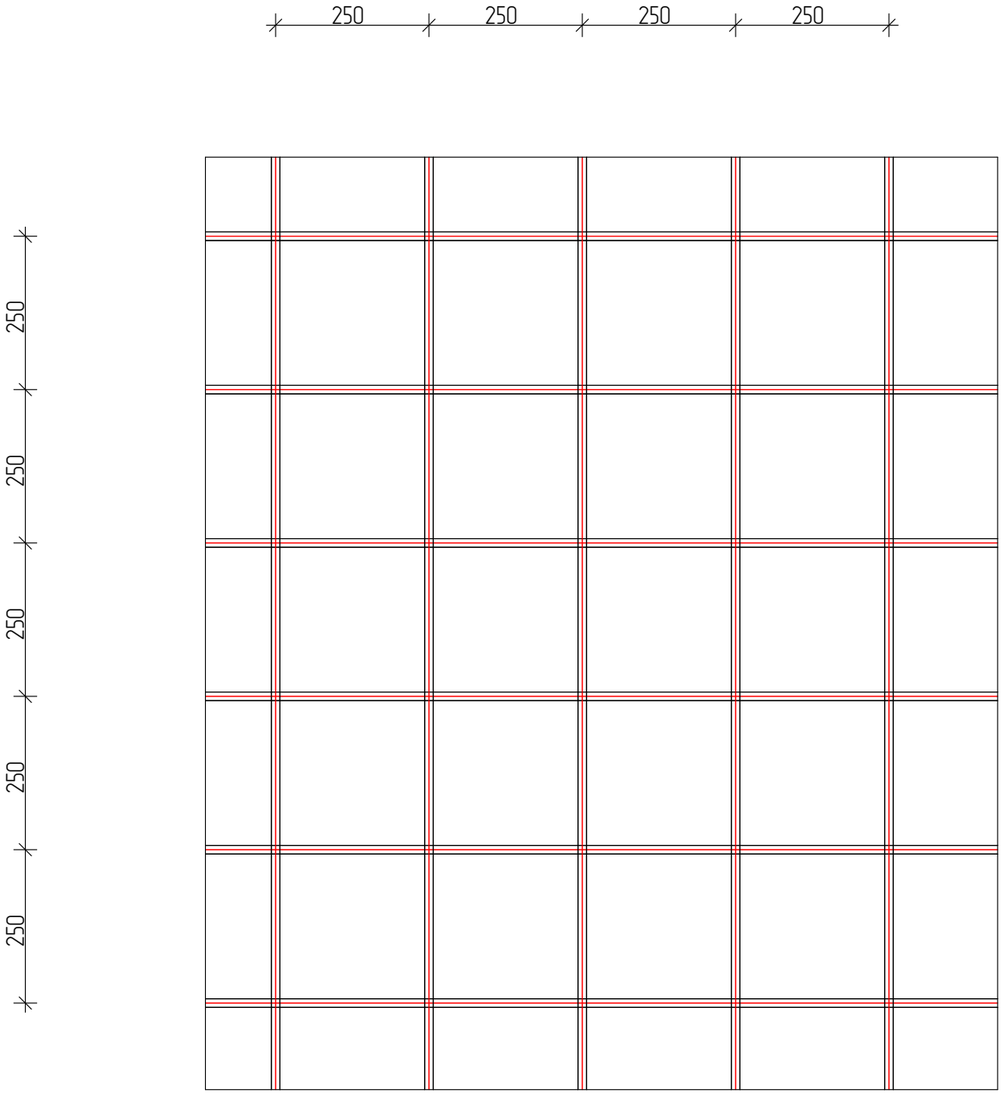

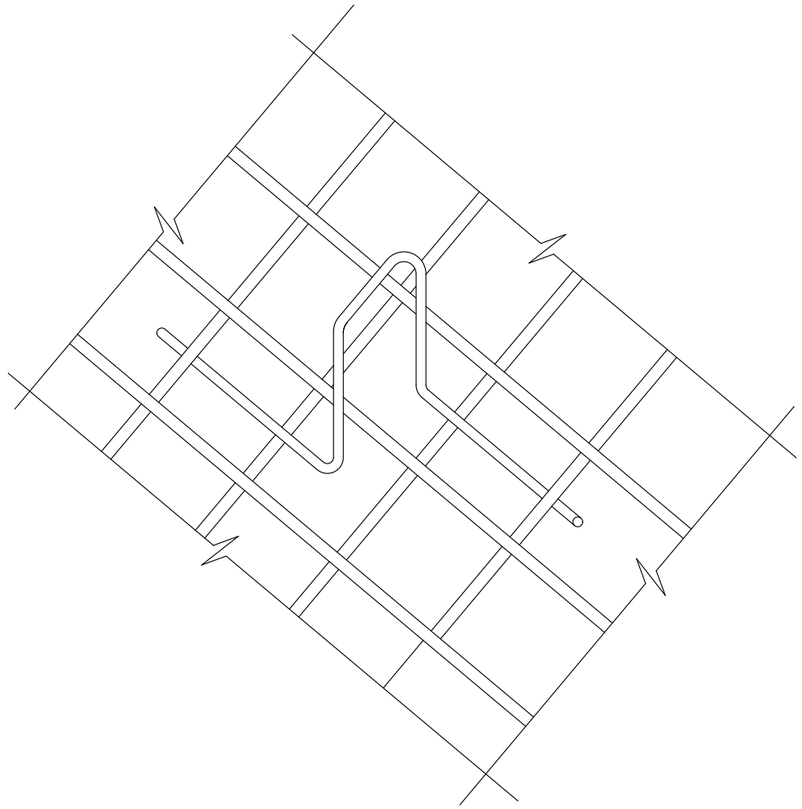

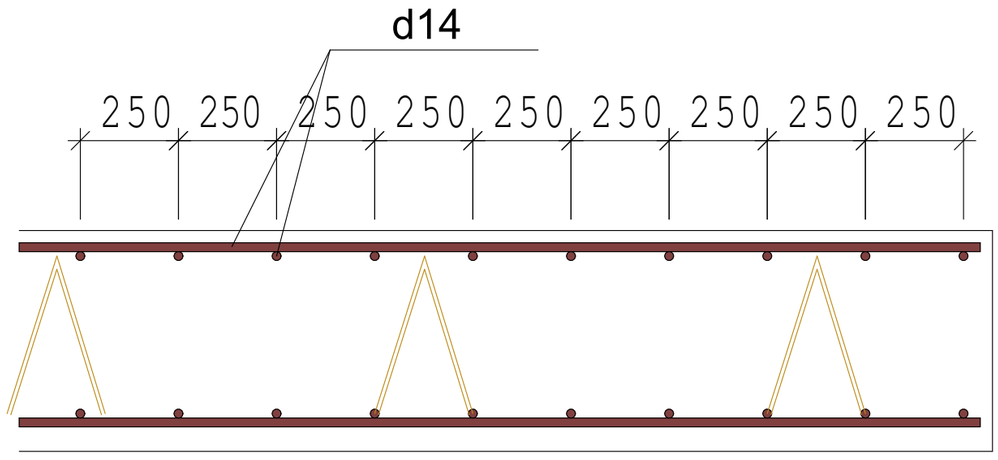

						#ID Проекта		
						кадастровый номер Россия		
Изм.	Кол.уч.	Лист	№Док.	Подп.	Дата			
Разраб.						Индивидуальный жилой дом	Стадия: #Стадия Проекта	Лист: 24 / Листов:
ГАП								
Схема армирования арматурного каркаса								

Ведомость арматуры				
Наименование	Диаметр арматуры	Кол-во	Ед.изм.	Вес, кг
Плита фундамента (дом)	Арматура А500С d14	3643,94	м.п.	4401,88
Плита фундамента (крыльцо))	Арматура А500С d14	64,37	м.п.	77,76
Плита фундамента (терраса))	Арматура А500С d14	758,22	м.п.	915,93
		4466,53		**5395,57**

Ведомость материалов фундаментной плиты			
Строительный материал	**Наименование**	Объем, м3	Площадь, м2
Бетон В 7,5			
	Плита фундамента (дом)	26,20	262,03
	Плита фундамента (крыльцо))	0,38	3,84
	Плита фундамента (терраса))	4,46	44,57
		31,04 м³	
Бетон В25			
	Плита фундамента (дом)	117,77	261,96
	Плита фундамента (крыльцо))	1,73	3,84
	Плита фундамента (терраса))	20,01	44,57
		139,51 м³	
Изоляция - ЭППС			
	Плита фундамента (дом)	21,15	212,59
		21,15 м³	
Плитка - Напольная			
	Плита фундамента (дом)	4,26	212,85
	Плита фундамента (крыльцо))	0,08	3,76
	Плита фундамента (терраса))	0,89	44,29
		5,23 м³	
Стяжка ЦПР			
	Плита фундамента (дом)	17,02	212,84
	Плита фундамента (крыльцо))	0,38	3,76
	Плита фундамента (терраса))	4,39	44,29
		21,79 м³	
		218,72 м³	

Пояснительная записка по монтажу стен

Монтаж стен осуществляется после завершения устройства и набора прочности фундаментов и перекрытий. До начала работ выполняется подготовка строительной площадки: производится вынос осей здания, проверка геометрии фундамента, устройство гидроизоляции по верхней плоскости фундамента (или перекрытия), а также организация складирования строительных материалов в зоне доступности грузоподъёмной техники.

При разметке необходимо учитывать, что оси здания не совпадают с краем стены. На чертежах указаны размеры от внутренней грани стены до оси и от оси до наружной поверхности стены. Это требование принципиально важно для правильного позиционирования стен и соблюдения проектных габаритов здания. Нарушение расположения осей может привести к смещению несущих конструкций и расхождениям в размерах.

Укладка первого ряда или установка первых элементов выполняется строго по разметке осей с проверкой диагоналей, уровней и вертикали. Первый ряд задаёт правильную геометрию и точность всех последующих рядов или монтажных панелей.

Монтаж стен ведётся поэтапно, с контролем вертикальности и горизонтальности каждого ряда. Для перевязки элементов и обеспечения монолитности конструкции применяются растворы, клеевые составы или специальные соединительные элементы — в зависимости от проектного материала. По мере возведения стен предусматриваются технологические зазоры под монтаж перекрытий и оконных блоков.

В процессе работ осуществляется постоянный контроль геометрии: проверяются диагонали, отвесы, отметки по высоте, соответствие проектным размерам от осей до границ стен. При необходимости выполняется временное крепление стен или установка распорок до достижения проектной жёсткости.

По завершении возведения стен производится устройство армопояса и закладных деталей, предусмотренных проектом. В местах сопряжения стен с перекрытиями и перегородками оставляются технологические зазоры, которые заполняются согласно проектным решениям.

Все работы выполняются в соответствии с проектной документацией, строительными нормами и правилами, а также инструкциями производителей материалов.

						#ID Проекта			
						кадастровый номер Россия			
Изм.	Кол.уч.	Лист	№Док.	Подп.	Дата				
						Индивидуальный жилой дом	Стадия	Лист	Листов
Разраб.							#Стадия Проекта	26	
ГАП									
ПЗ Стены									

Пояснительная записка к возведению стен из газобетонных блоков

Возведение стен из газобетонных блоков предусмотрено проектом на основании требований нормативных документов (СП 15.13330.2012 «Каменные и армокаменные конструкции», ГОСТ 31360-2007 «Блоки из ячеистых бетонов»).

1. Подготовительные работы

Перед началом кладки необходимо:

- проверить соответствие геометрии и отметок фундамента/перекрытия проекту;
- выполнить горизонтальную гидроизоляцию по цоколю (рулонные материалы в 2 слоя с проклейкой швов);
- нанести разметку положения несущих стен и перегородок;
- подготовить кладочные смеси и инструменты.

2. Кладка газобетонных блоков

- Первый ряд блоков укладывается на цементно-песчаный раствор М100 для выравнивания;
- последующие ряды — на клеевую смесь толщиной шва 2–3 мм;
- блоки укладываются со смещением вертикальных швов не менее 80 мм;
- отклонения кладки: по вертикали — не более 10 мм на этаж, по горизонтали — не более 5 мм на 10 м длины стены (СП 70.13330.2012);
- за один день допускается укладывать не более 4 рядов блоков, чтобы исключить осадку и деформации свежей кладки.

3. Армирование кладки

- Армирование выполняется в первом ряду блоков и далее через каждые 3–4 ряда;
- штробы под арматуру прорезаются в верхней части блока, очищаются и заполняются клеем;
- укладываются два стержня арматуры Ø8 мм класса А500С;
- армирование обязательно в зонах опирания перекрытий и поясов жёсткости.

4. Опирание перекрытий

- Перекрытия (сборные, деревянные или другие конструкции) опираются исключительно на монолитный железобетонный пояс, выполняемый поверх кладки;
- армирование и размеры армопояса принимаются по проекту;
- в случае устройства монолитного перекрытия оно опирается непосредственно на стены без дополнительного армопояса.

5. Теплотехника и защита кладки

- Толщина наружных стен принимается по проекту с учётом теплотехнического расчёта;
- швы кладки должны быть полностью заполнены клеем без пустот;

- наружные стены подлежат обязательной защите отделкой (штукатурка, облицовка, вентилируемый фасад и др.) для предотвращения намокания газобетона.

6. Работы в зимнее время

При производстве кладочных работ в зимний период необходимо:

- применять клеевые смеси с противоморозными добавками;
- не допускать замерзания раствора до его набора прочности;
- блоки перед кладкой очищать от снега и наледи;
- температура воздуха при кладке должна соответствовать требованиям СП 70.13330.2012.

7. Контроль качества

- Контроль геометрии кладки осуществляется нивелиром и отвесом;
- проверка заполнения швов выполняется выборочно вскрытием;
- контроль качества клеевых растворов — по паспортам поставщика и лабораторным испытаниям;
- работы выполняются в соответствии с требованиями СП 70.13330.2012 «Несущие и ограждающие конструкции» и СП 15.13330.2012 «Каменные и армокаменные конструкции».

						#ID Проекта		
						кадастровый номер Россия		
Изм.	Кол.уч.	Лист	№Док.	Подп.	Дата			
						Индивидуальный жилой дом	Стадия	Лист	Листов
Разраб.							#Стадия Проекта	27	
ГАП									
ПЗ Газобетонные блоки									

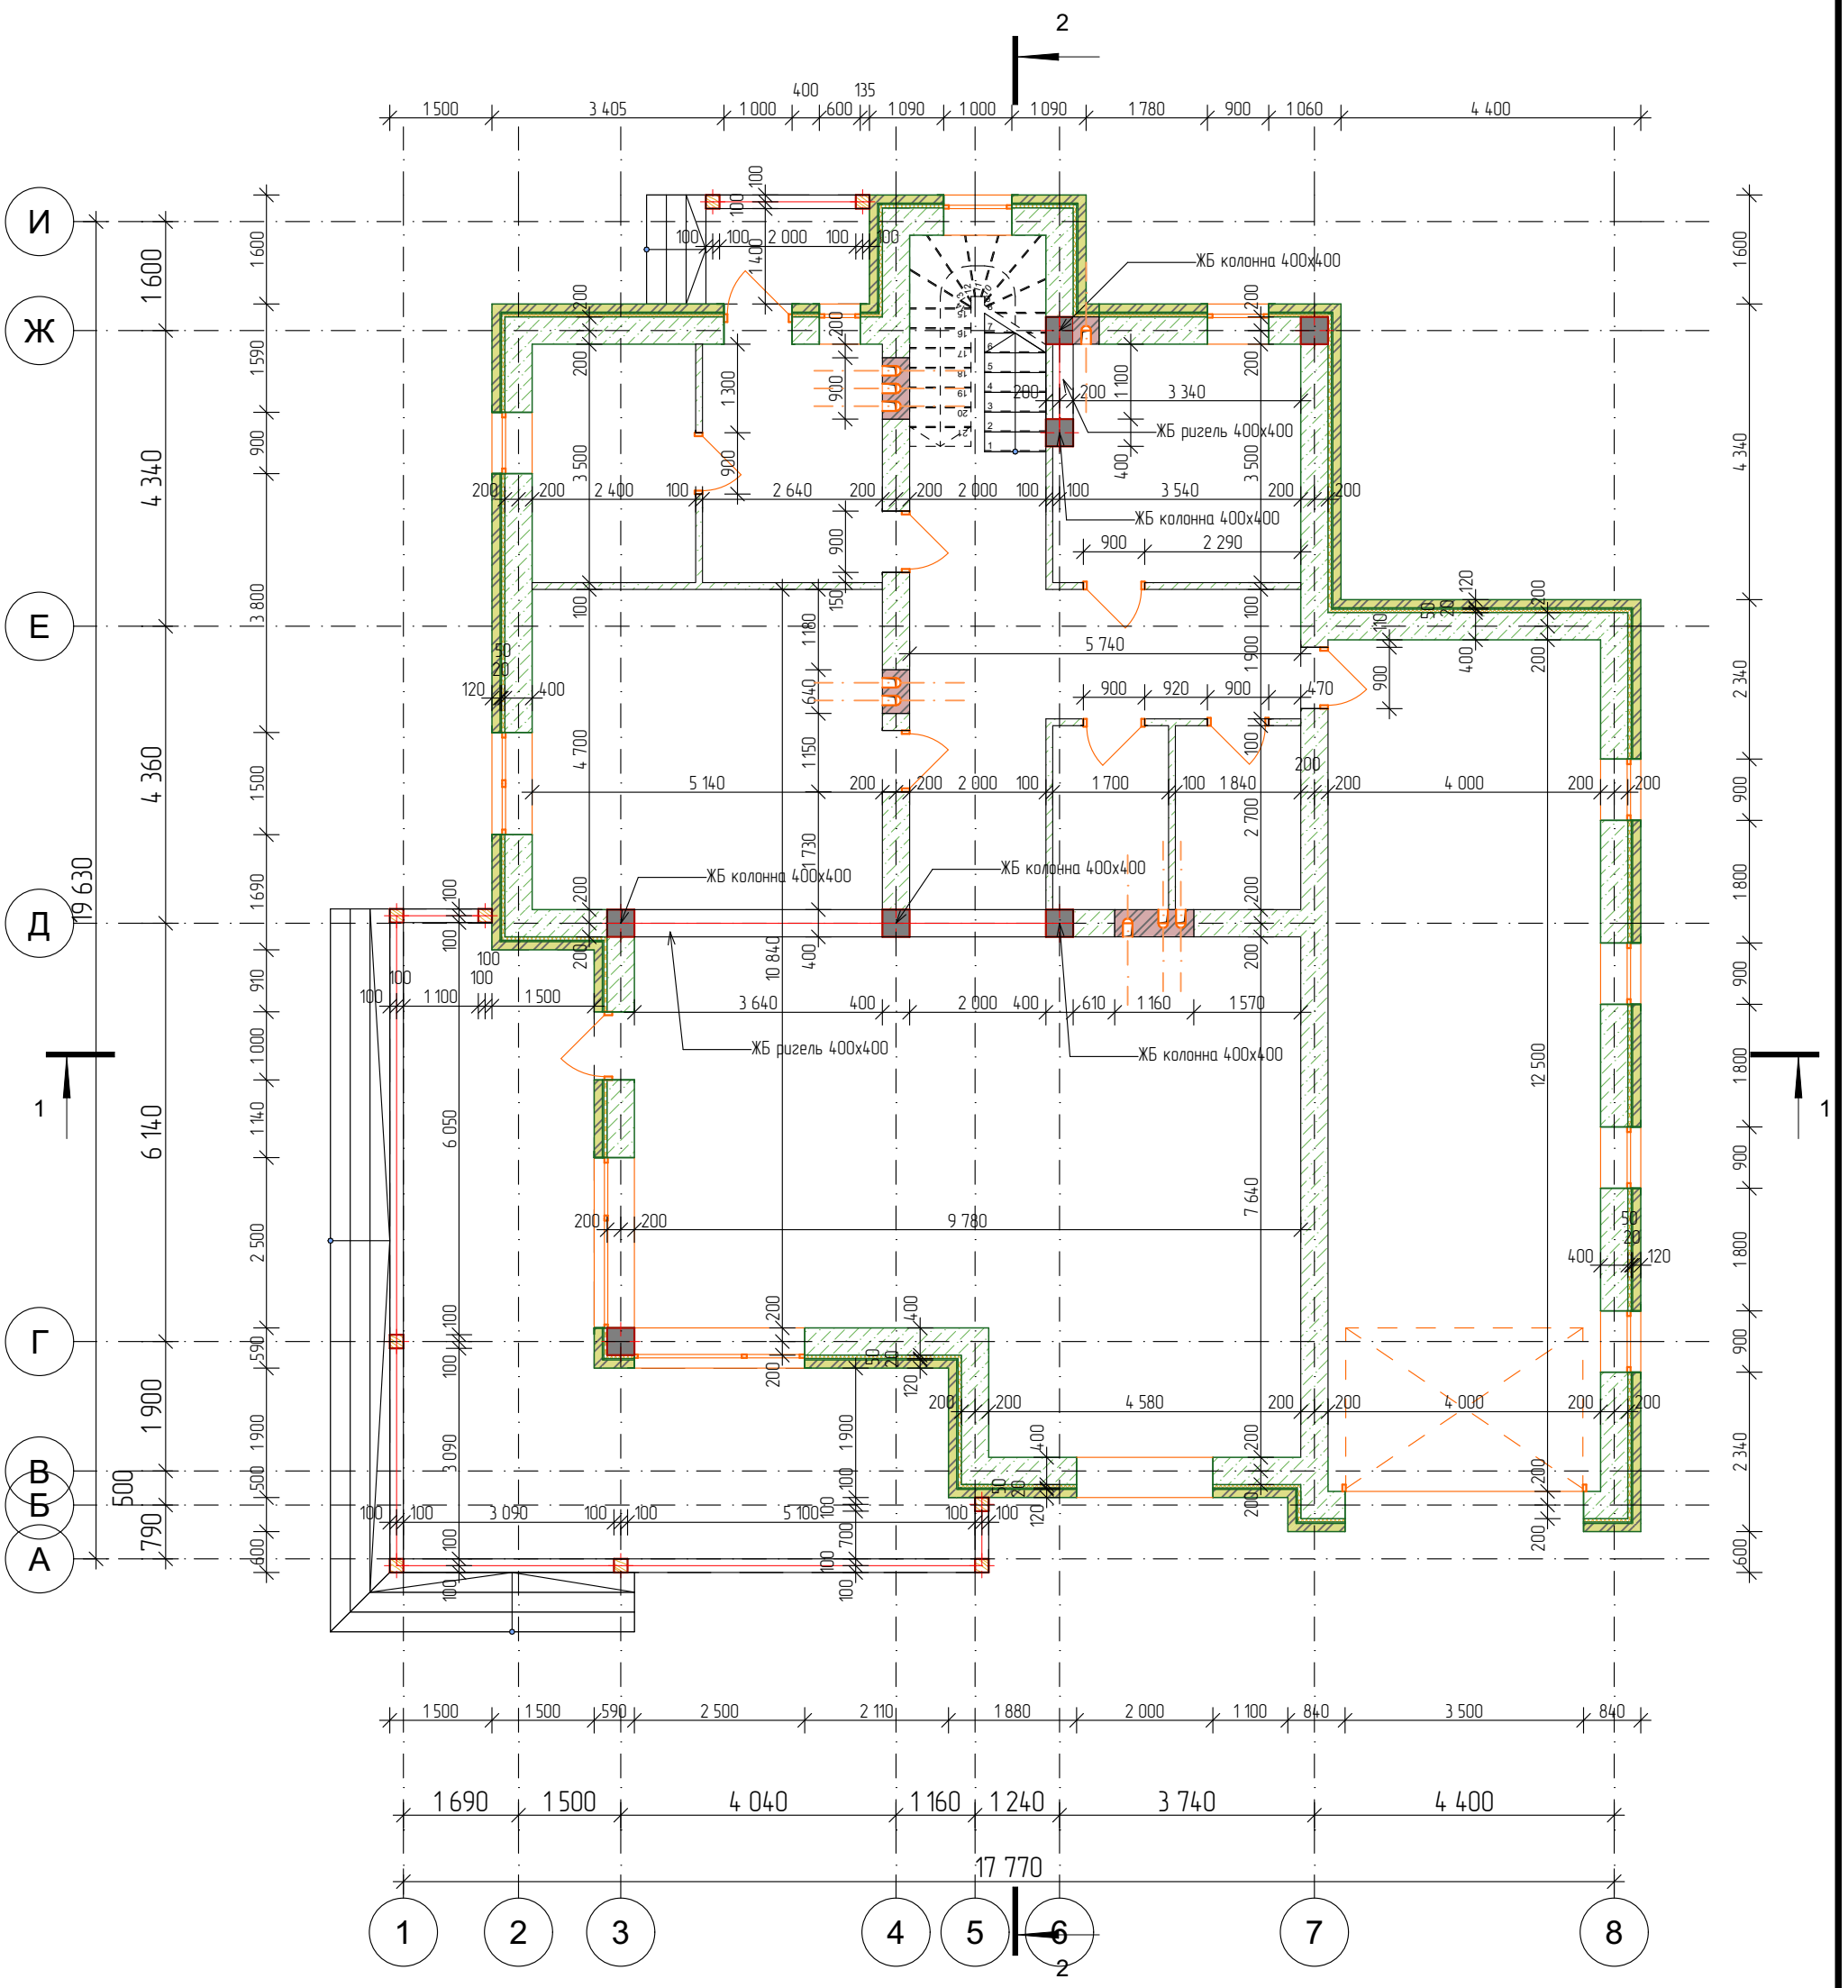

						#ID Проекта	
						кадастровый номер Россия	
Изм.	Кол.уч.	Лист	№Док.	Подп.	Дата		
Разраб.						Индивидуальный жилой дом	Стадия: #Стадия Проекта; Лист: 28; Листов:
ГАП							
План на отм. ±0.000							

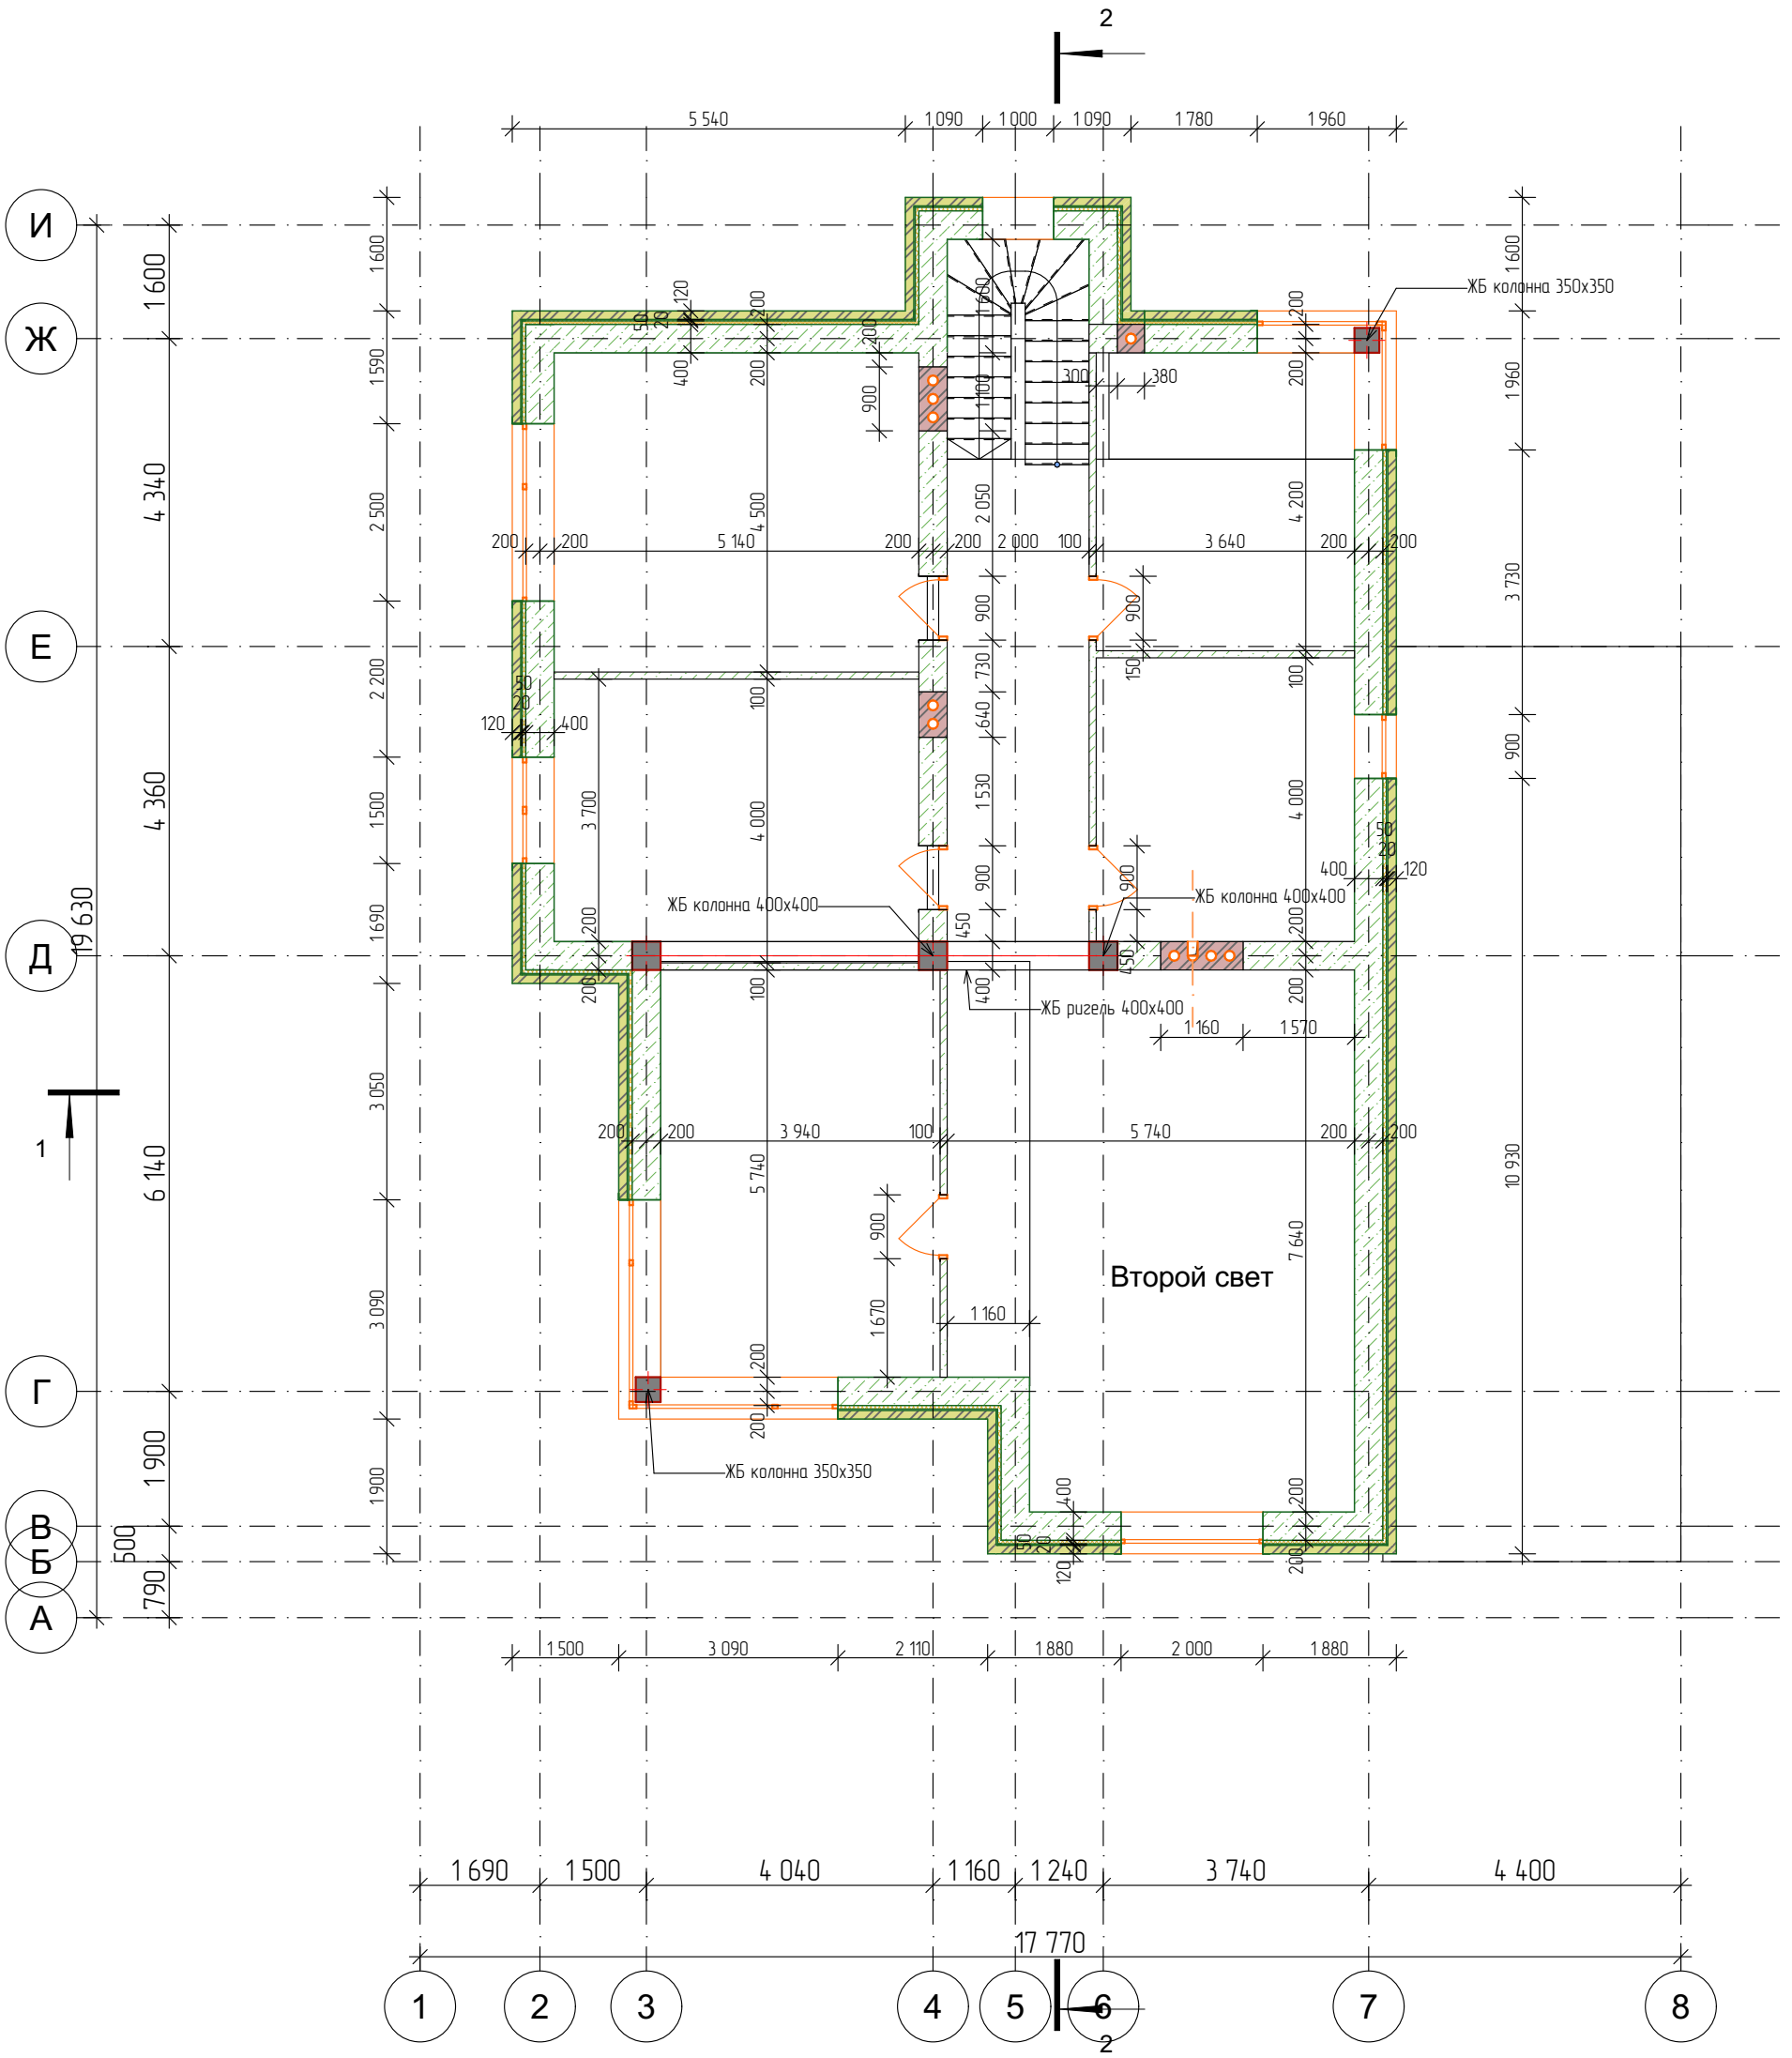

						#ID Проекта	
						кадастровый номер Россия	
Изм.	Кол.уч.	Лист	№Док.	Подп.	Дата		
Разраб.						Индивидуальный жилой дом	Стадия: #Стадия Проекта; Лист: 29; Листов:
ГАП							
План на отм +3.440							

ВЕДОМОСТЬ БЛОКА ДЛЯ СТЕН			
Этаж	Тип конструкций	Строительный материал	Объем, м3
1-й этаж			
	Внутренние несущие стены	Газобетон D400	25,03
			25,03 м³
	Наружные несущие стены	Газобетон D400	69,28
			69,28 м³
	Перегородки	Газобетон перегородки	7,18
			7,18 м³
2-й этаж			
	Внутренние несущие стены	Газобетон D400	9,54
			9,54 м³
	Наружные несущие стены	Газобетон D400	58,99
			58,99 м³
	Перегородки	Газобетон перегородки	7,67
			7,67 м³
			177,69 м³

Ведомость материалов на фасад			
Наиме...	**Компоненты**		Объем, м3
	Толщина, мм	**Площадь, м2**	
Изоляция - Минеральная Жесткая			
	50	373,45	18,64
Кирпич - Облицовочный			
	120	378,30	45,25

						#ID Проекта		
						кадастровый номер Россия		
Изм.	Кол.уч.	Лист	№Док.	Подп.	Дата			
						Индивидуальный жилой дом	Стадия	Лист	Листов
Разраб.							#Стадия Проекта	30	
ГАП									
Ведомасть материаов стен									

Н3 Колонны			
Этаж	Наиенование	Кол-во,шт	Объем, м3
1-й этаж	ЖБ колонна 400х400	7	3,30
2-й этаж	ЖБ колонна 350х350	2	0,68
2-й этаж	ЖБ колонна 400х400	3	1,47

Н3 Ригель			
Этаж	Наиенование	Кол-во,шт	Объем, м3
1-й этаж	ЖБ ригель 400х400	2	1,35
2-й этаж	ЖБ ригель 400х400	1	1,07

н Армирование колонн					
Наименование	Арматура	Кол-во стержней	Общая длина	Ед. изм.	Всего, кг
ЖБ колонна 350х350	Арматура А500С d18	4	---	м.п.	---
ЖБ колонна 400х400	Арматура А500С d18	4	---	м.п.	---
			0,00		**0,00**

А Арматура ригель					
Элемент	Наименование	Число стержней	Кол-во	Ед. изм.	Вес, кг
ЖБ ригель 400х400					
	Арматура А500С d20	6	100,02	м.п.	246,64
			100,02		**246,64**

А Хомуты на ригель					
Этаж	ID Элемента	Наименование	Длина	Ед.изм.	Вес, кг
1-й этаж					
	ЖБ ригель 400х400	d8	33,78	м.п.	13,34
2-й этаж					
	ЖБ ригель 400х400	d8	25,67	м.п.	10,14
			59,45		**23,48**

ЖБ ригель 400х400

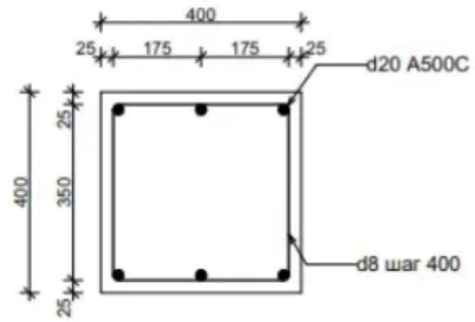

ЖБ Колонна 400х400

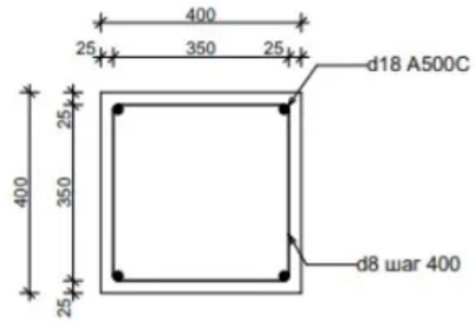

						#ID Проекта	
						кадастровый номер Россия	
Изм.	Кол.уч.	Лист	№Док.	Подп.	Дата		
Разраб.						Индивидуальный жилой дом	Стадия: #Стадия Проекта; Лист: 31.1; Листов:
ГАП							
Ведомость материалов КЖ							

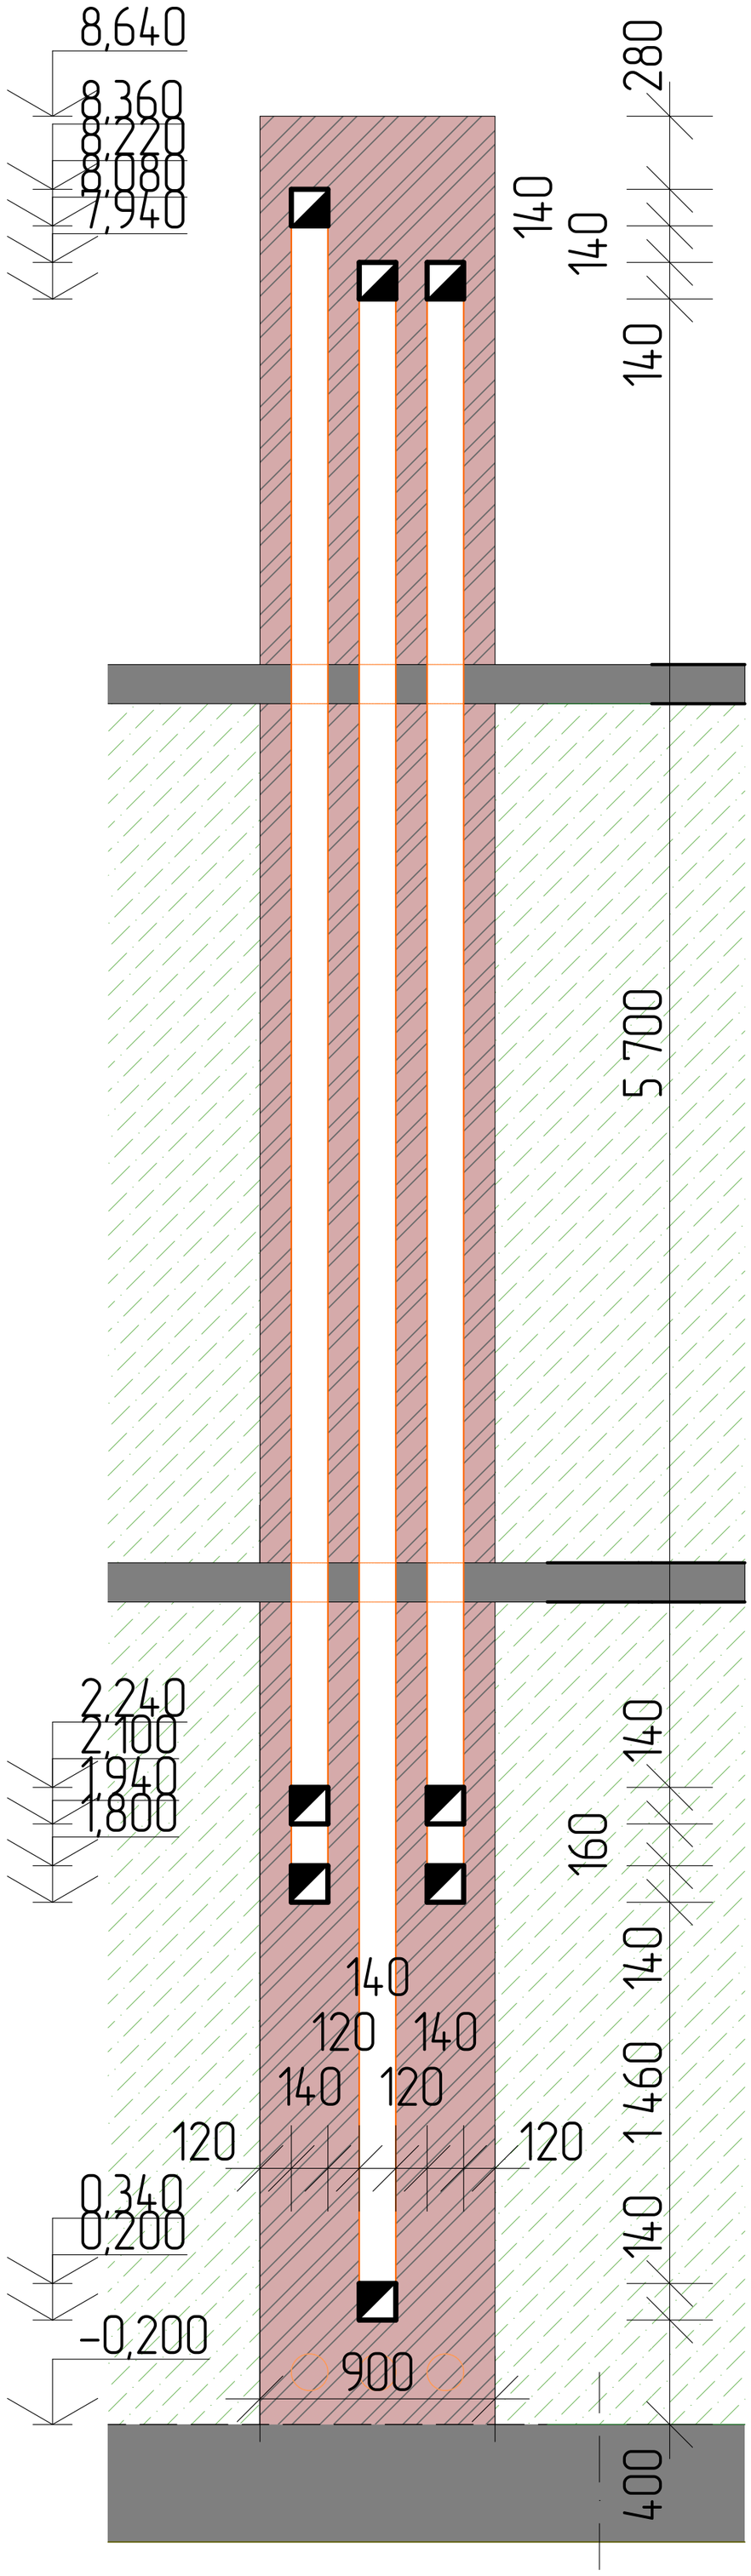

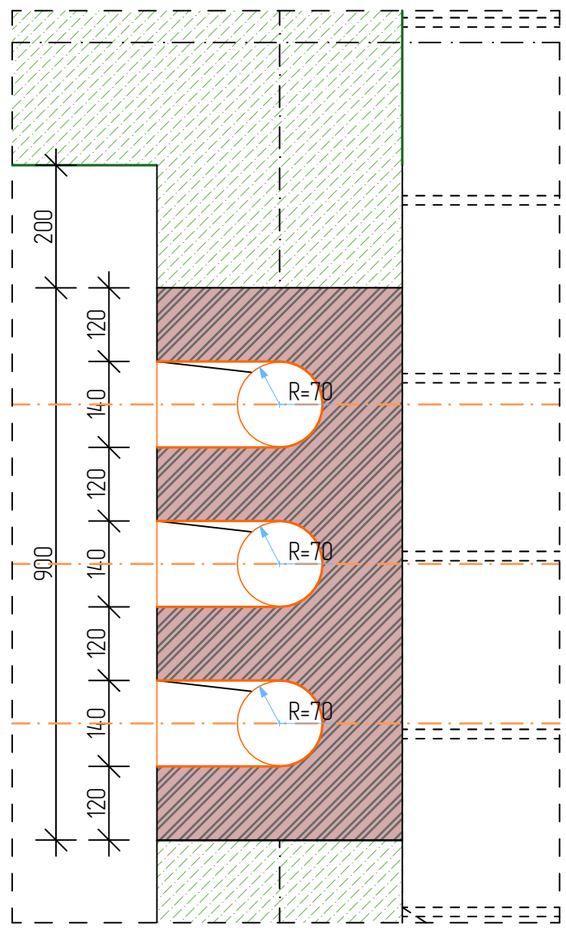

						#ID Проекта		
						кадастровый номер Россия		
Изм.	Кол.уч.	Лист	№Док.	Подп.	Дата			
Разраб.						Индивидуальный жилой дом	Стадия: #Стадия Проекта	Лист: 33 / Листов:
ГАП								
Дымоход Д-1								

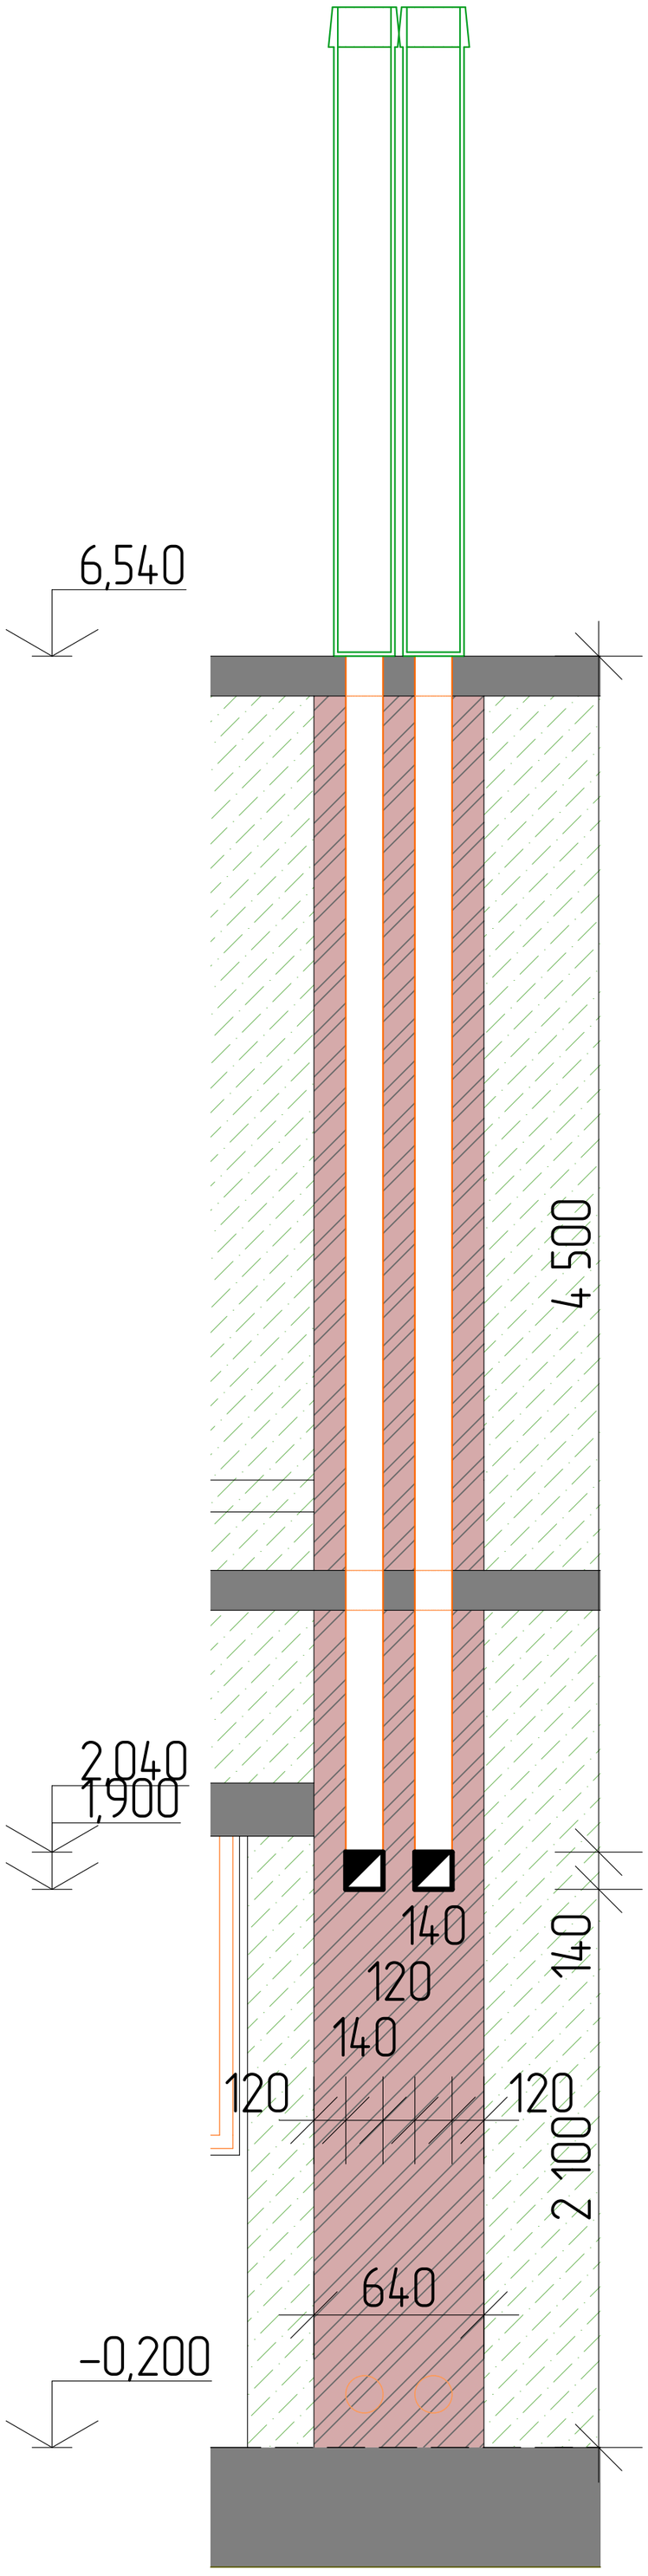

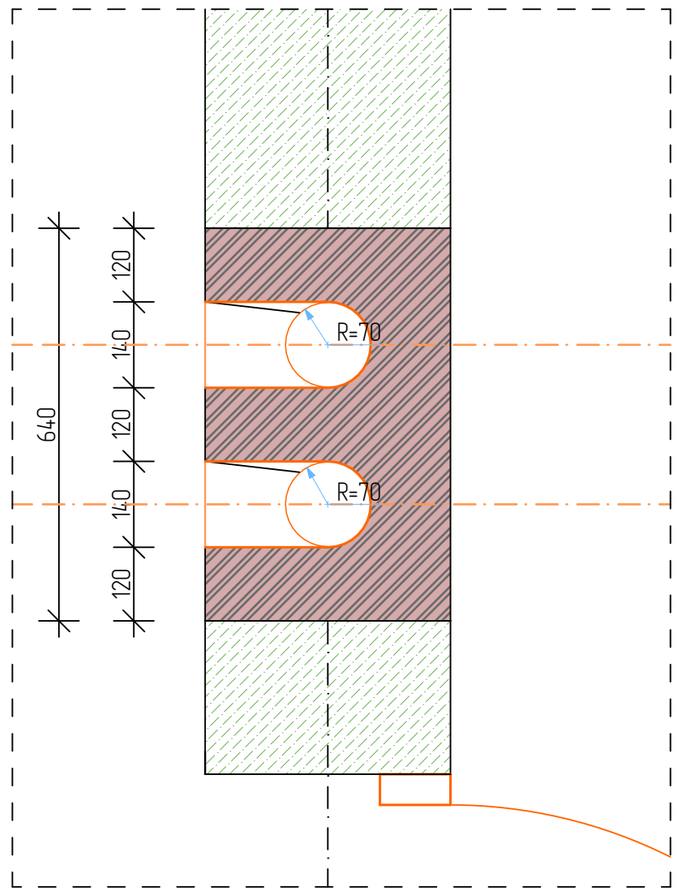

						#ID Проекта	
						кадастровый номер Россия	
Изм.	Кол.уч.	Лист	№Док.	Подп.	Дата		
Разраб.						Индивидуальный жилой дом	Стадия: #Стадия Проекта; Лист: 34; Листов:
ГАП							
Дымоход Д-2							

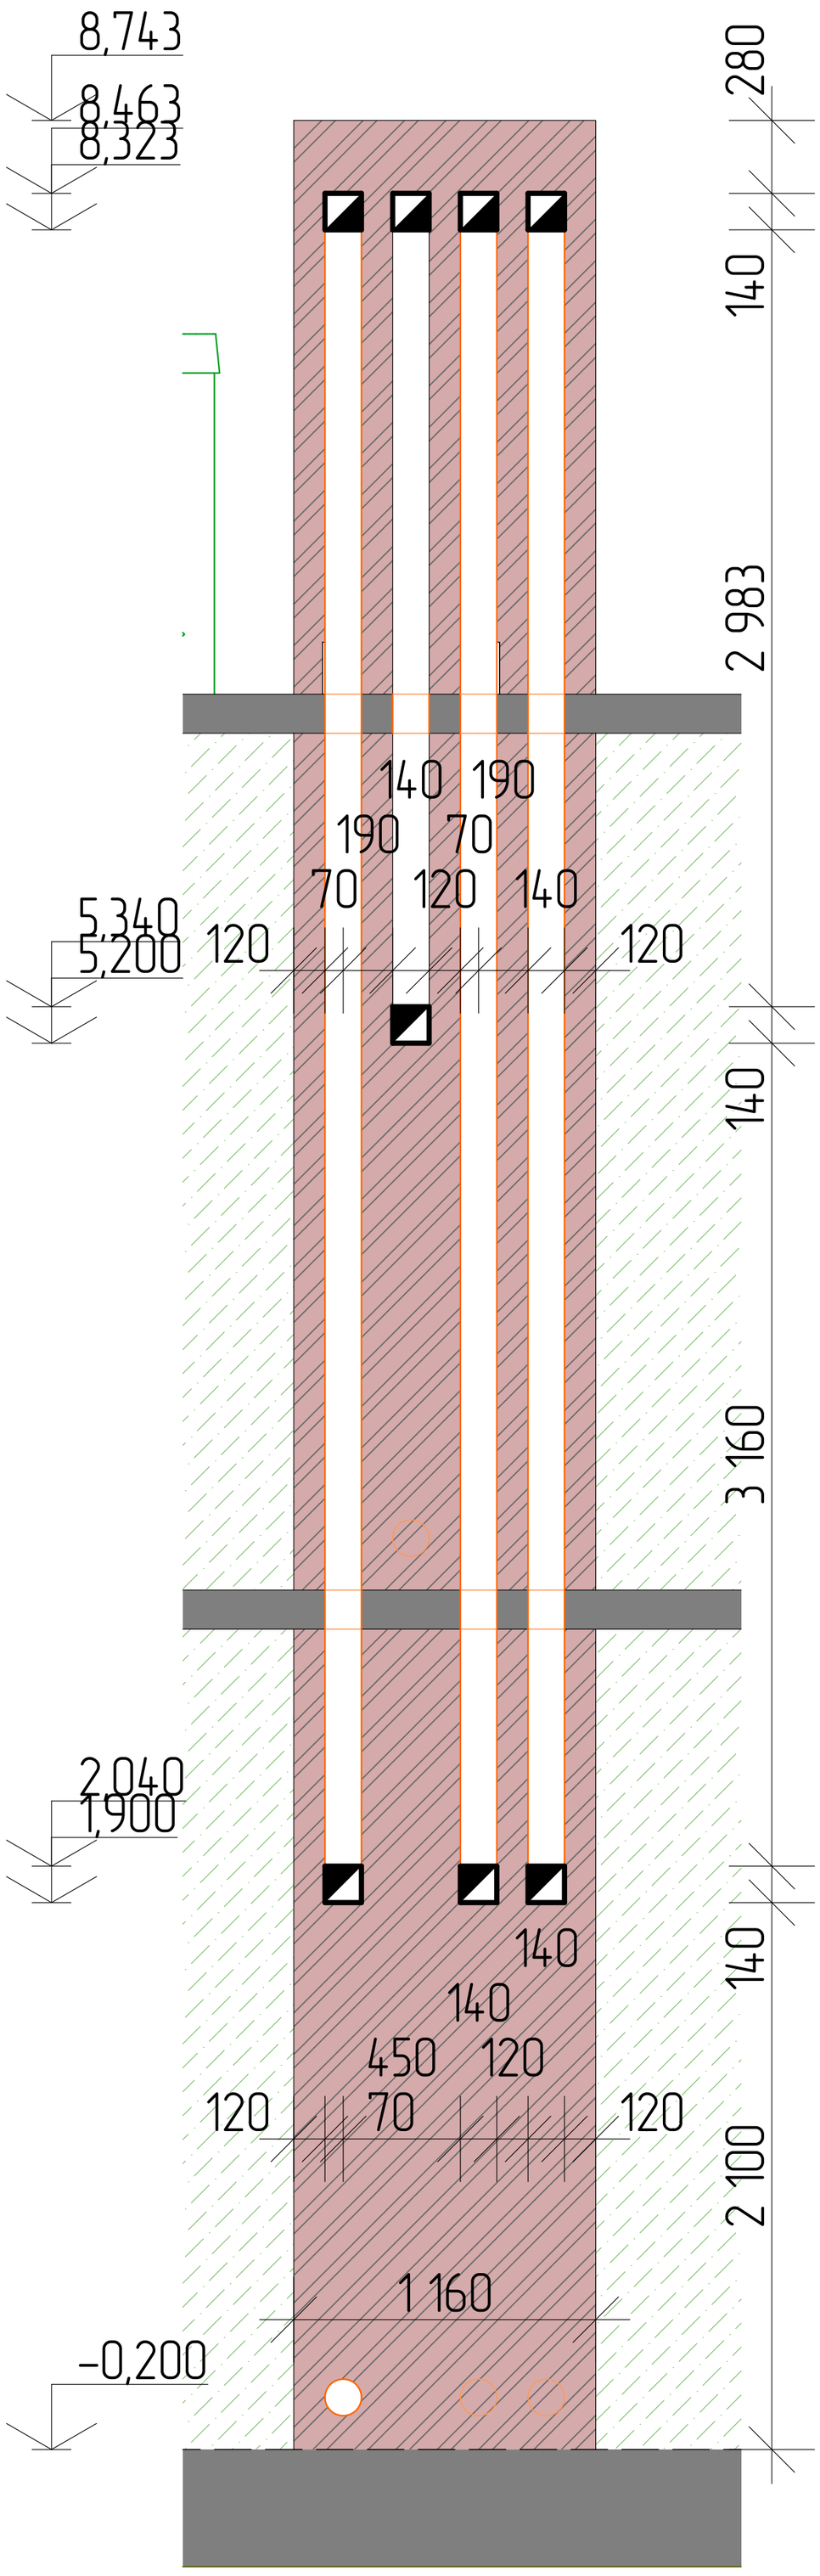

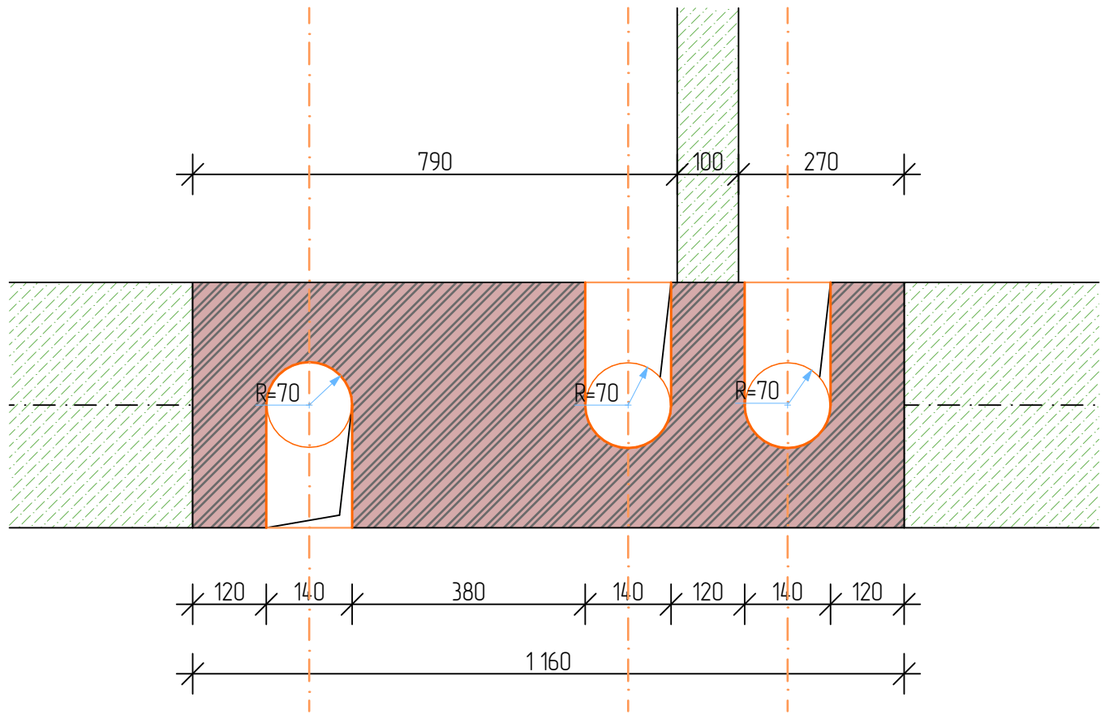

						#ID Проекта	
						кадастровый номер Россия	
Изм.	Кол.уч.	Лист	№Док.	Подп.	Дата		
Разраб.						Индивидуальный жилой дом	Стадия: #Стадия Проекта; Лист: 35; Листов:
ГАП							
Дымоход Д-3							

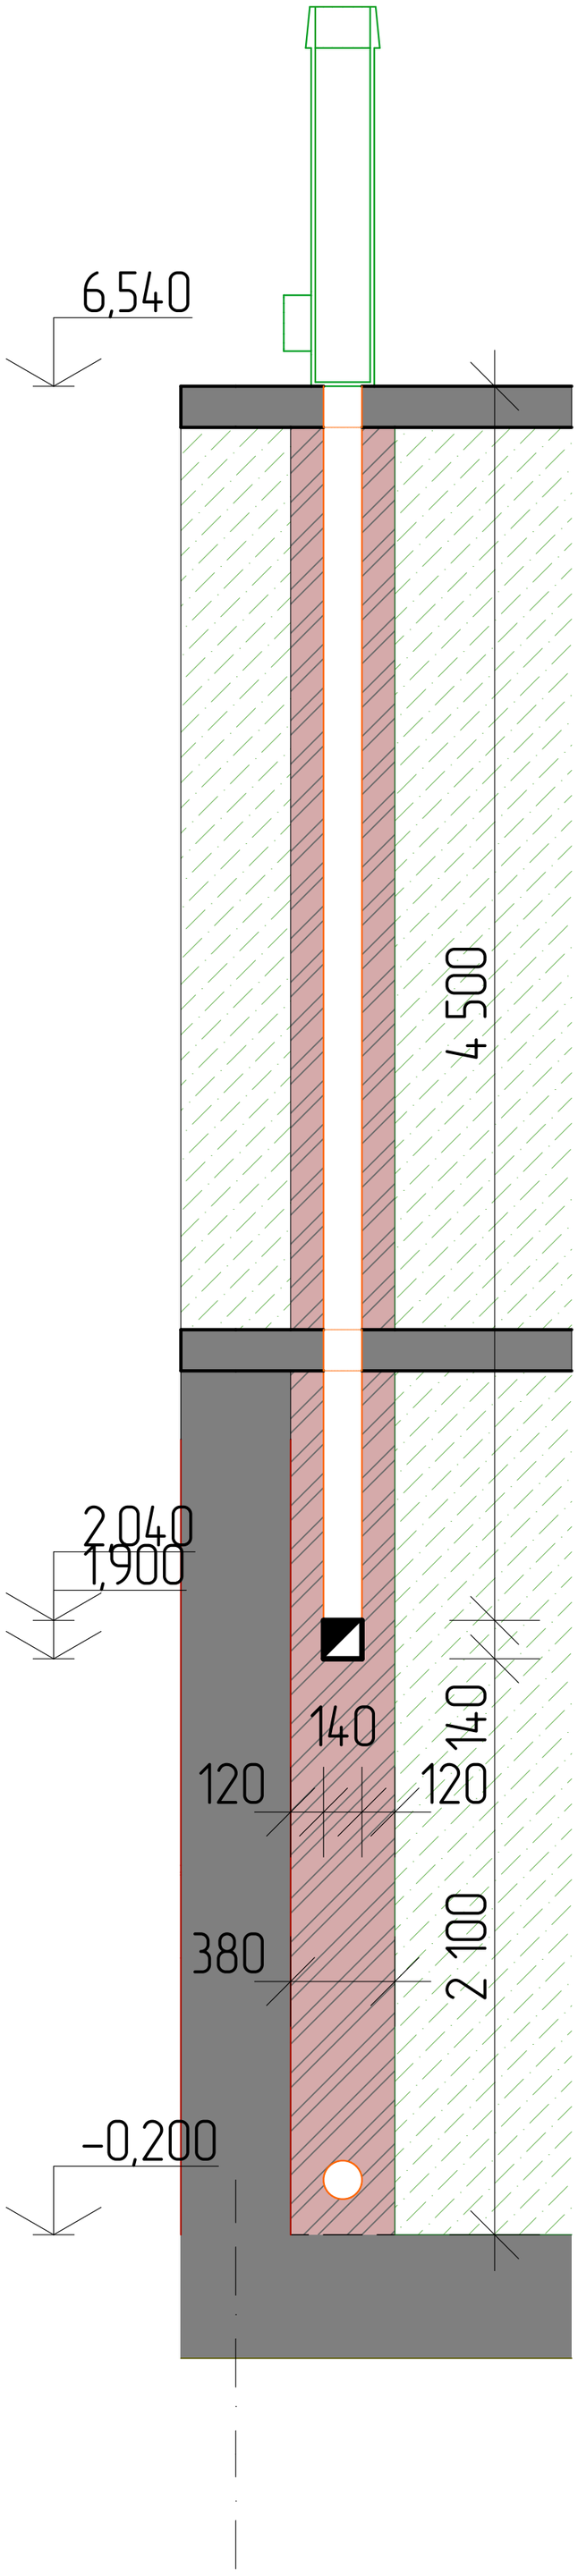

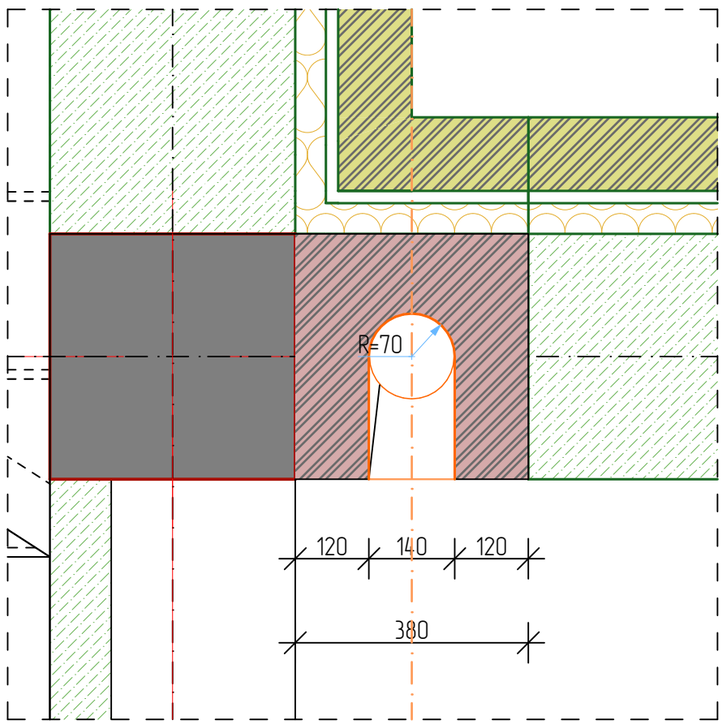

						#ID Проекта		
						кадастровый номер Россия		
Изм.	Кол.уч.	Лист	№Док.	Подп.	Дата			
Разраб.						Индивидуальный жилой дом	Стадия	Лист	Листов
ГАП							#Стадия Проекта	36	
Дымоход Д-4									

Каталог Дверей				
Полный ID Элемента	Д-1	Д-1	ДВ-1	ДВ-2
D по Классификации	Дверь -1	Дверь -1	Дверь -1	Дверь -2
Наименование Двери	Однопольная Дверь 27	Однопольная Дверь 27	Однопольная Дверь с Фрамугой 27	Ворота Гаражные Подъемные 27
Количество	5	7	2	1
Размер Ш x В	900×2 100	900×2 100	1 000×2 400	3 500×2 400
Ориентация	Л	П	Л	
Высота Порога Двери	0	0	0	0
Высота Перемычки Двери	2 100	2 100	2 400	2 400
2D-символ				
Вид со Стороны, Противоположной Стороне Открывания				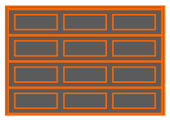

						#ID Проекта		
						кадастровый номер Россия		
Изм.	Кол.уч.	Лист	№Док.	Подп.	Дата			
Разраб.						Индивидуальный жилой дом	Стадия: #Стадия Проекта	Лист: 37 / Листов:
ГАП								
Каталог дверных проемов								

Каталог Окон

Полный ID Элемента	ОК-1	ОК-1	ОК-2	ОК-3	ОК-4	ОК-5	ОК-6	ОК-7	ОК-8	ОК-8	ОК-9	ОК-10
Наименование Окна	Двустворчатое Окно 27	Двустворчатое Окно 27	Окно 27	Вертикальное Многостворчатое Окно 27	Окно 27	Двустворчатое Окно 27	Вертикальное Многостворчатое Окно 27	Окно 27	Окно 27	Окно 27	Двустворчатое Окно 27	Двустворчатое Окно 27
Количество	1	1	6	1	1	1	1	1	1	1	1	1
Размер Ш x В	2 500×2 000	2 500×2 000	900×1 500	1 000×3 500	600×1 500	1 500×1 500	2 000×5 340	900×800	1 760×1 500	1 760×1 500	2 500×2 000	1 500×2 000
Ориентация	Л	П	Л		Л			Л	Л	П	П	
Высота Подоконника Окна	400	400	900	2 240	900	900	-2 940	1 600	900	900	400	400
Высота Перемычки Окна	2 400	2 400	2 400	5 740	2 400	2 400	2 400	2 400	2 400	2 400	2 400	2 400
2D-символ												
Вид со Стороны, Противоположной Стороне Открывания				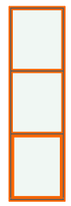			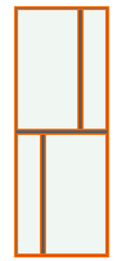					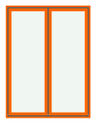

Каталог Окон

Полный ID Элемента	ОК-11	ОК-11	П/П	П/П
Наименование Окна	Двустворчатое Окно 27	Двустворчатое Окно 27	Оконный Проем Прямоугольный 27	Простой Проем Окна
Количество	1	1	1	1
Размер Ш x В	2 890×2 000	2 890×2 000	1 000×2 520	2 000×3 340
Ориентация	Л	П		Л
Высота Подоконника Окна	400	400	-120	400
Высота Перемычки Окна	2 400	2 400	2 400	3 740
2D-символ				
Вид со Стороны, Противоположной Стороне Открывания				 

Изм.	Кол.уч.	Лист	№Док.	Подп.	Дата	#ID Проекта		
						кадастровый номер Россия		
Разраб.						Индивидуальный жилой дом	Стадия: #Стадия Проекта	Лист: 38	Листов:
ГАП								
Каталог оконных проемов								

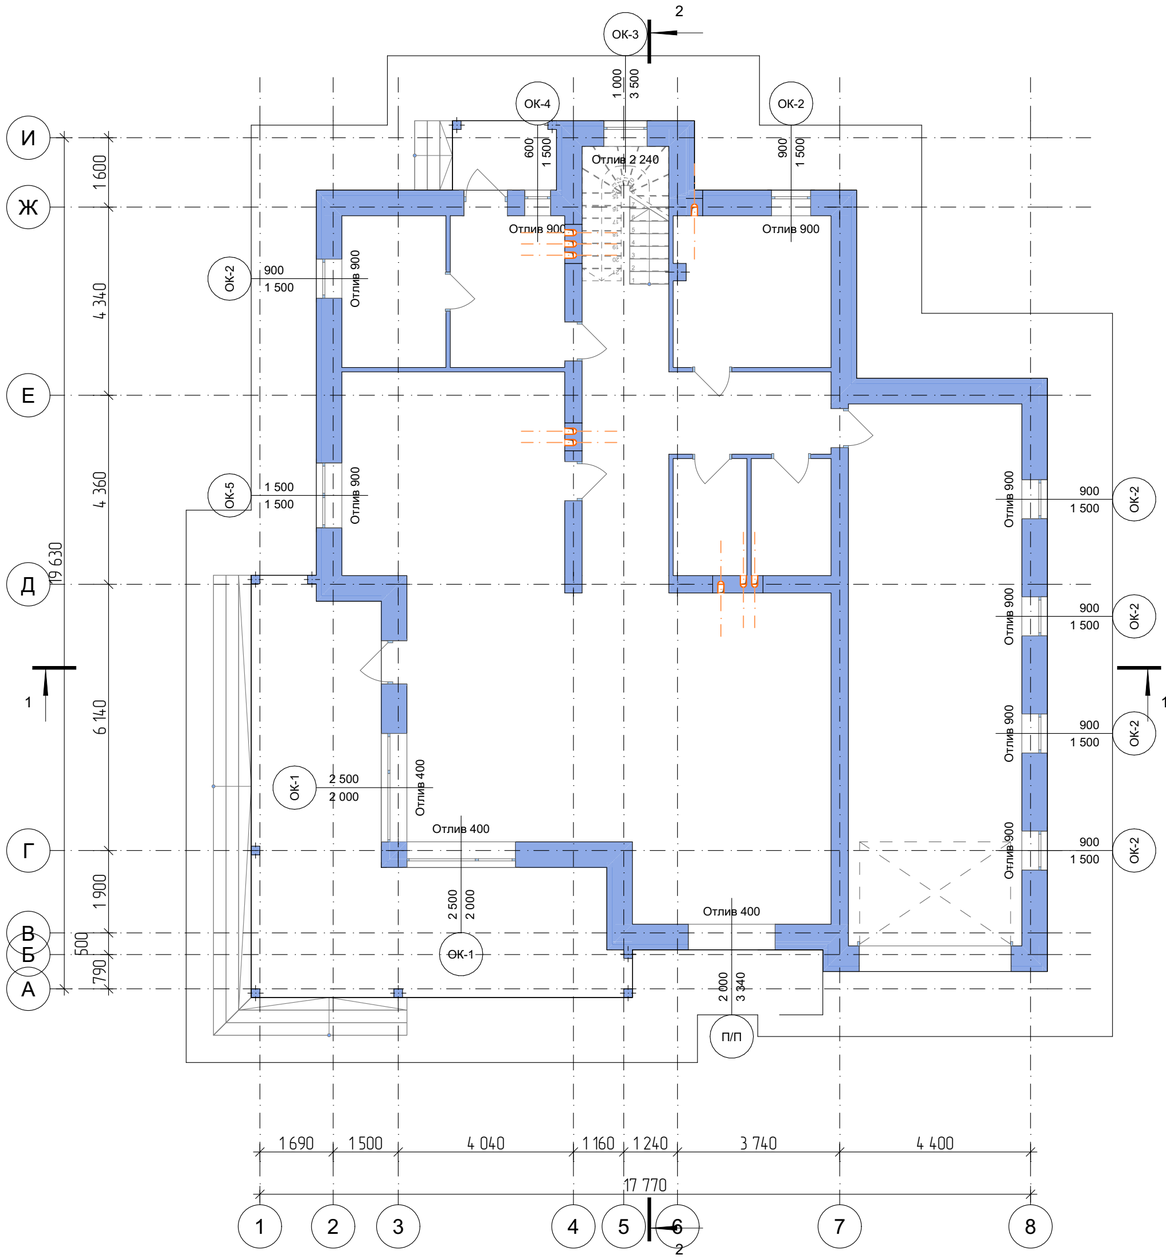

Марка, поз.	Размер проема в кладке, мм	Количество
ОК-1	2 500×2 000	2
ОК-2	900×1 500	6
ОК-4	600×1 500	1
ОК-5	1 500×1 500	1
ОК-6	2 000×5 340	1
П/П	2 000×3 340	1

						#ID Проекта	
						кадастровый номер Россия	
Изм.	Колуч.	Лист	№Док.	Подп.	Дата		
Разраб.						Индивидуальный жилой дом	Стадия: #Стадия Проекта; Лист: 39; Листов:
ГАП							
Маркировка оконных проемов первого этажа							

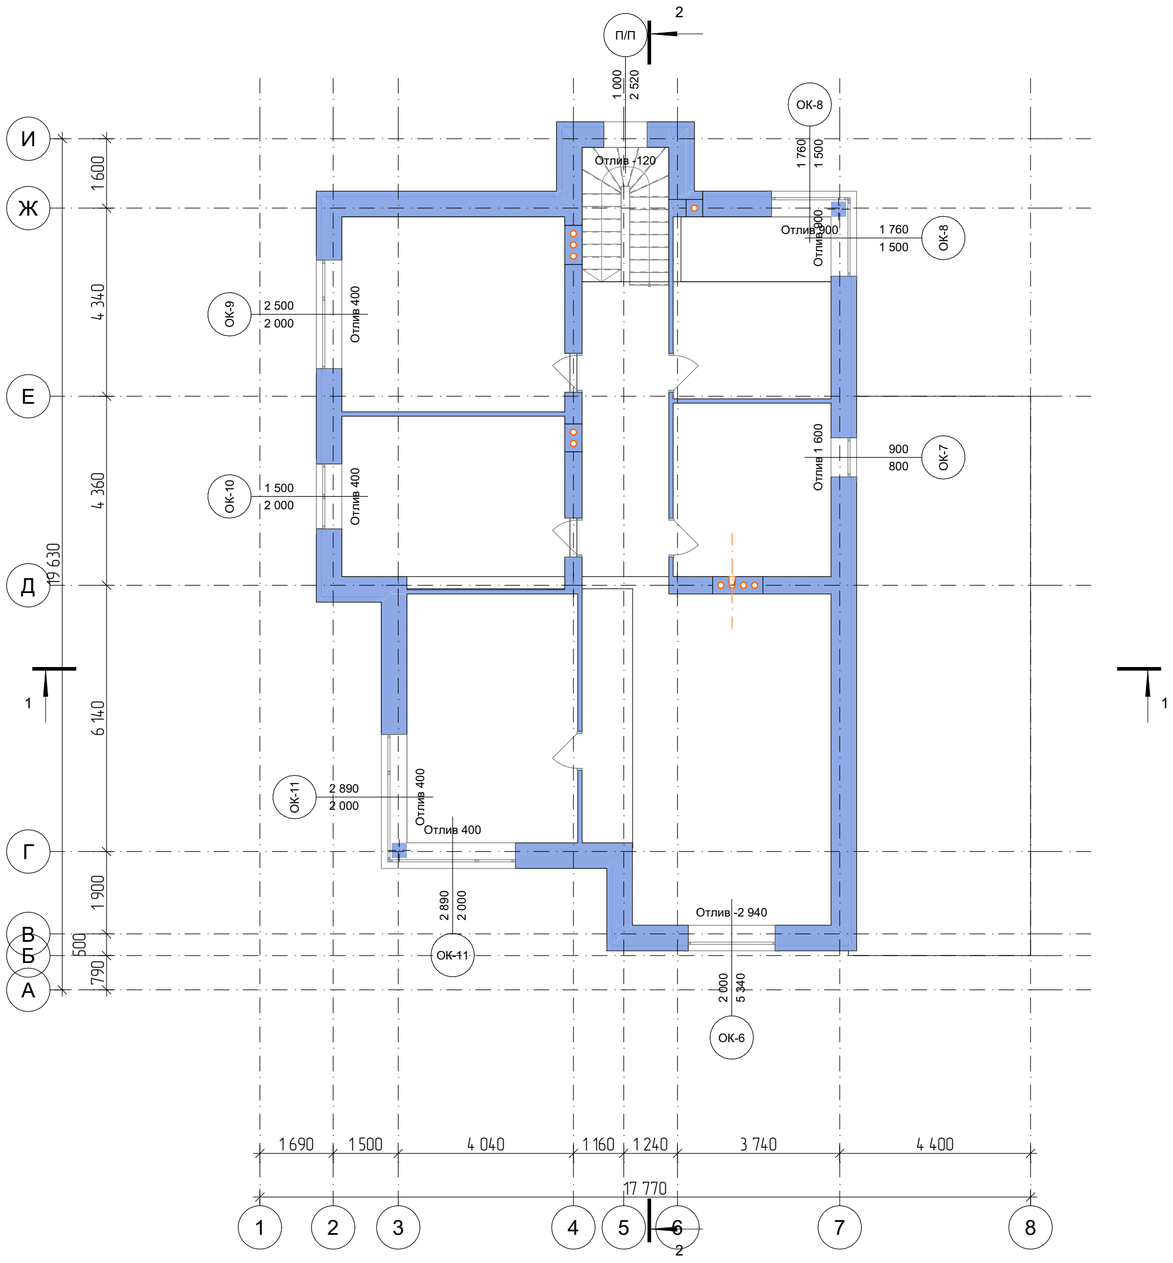

Марка, поз.	Размер проема в кладке, мм	Количество
ОК-3	1 000×3 500	1
ОК-7	900×800	1
ОК-8	1 760×1 500	2
ОК-9	2 500×2 000	1
ОК-10	1 500×2 000	1
ОК-11	2 890×2 000	2
П/П	1 000×2 520	1

						#ID Проекта		
						кадастровый номер Россия		
Изм.	Кол.уч.	Лист	№Док.	Подп.	Дата			
Разраб.						Индивидуальный жилой дом	Стадия	Лист	Листов
ГАП							#Стадия Проекта	40	
						Маркировка оконных проемов второго этажа			

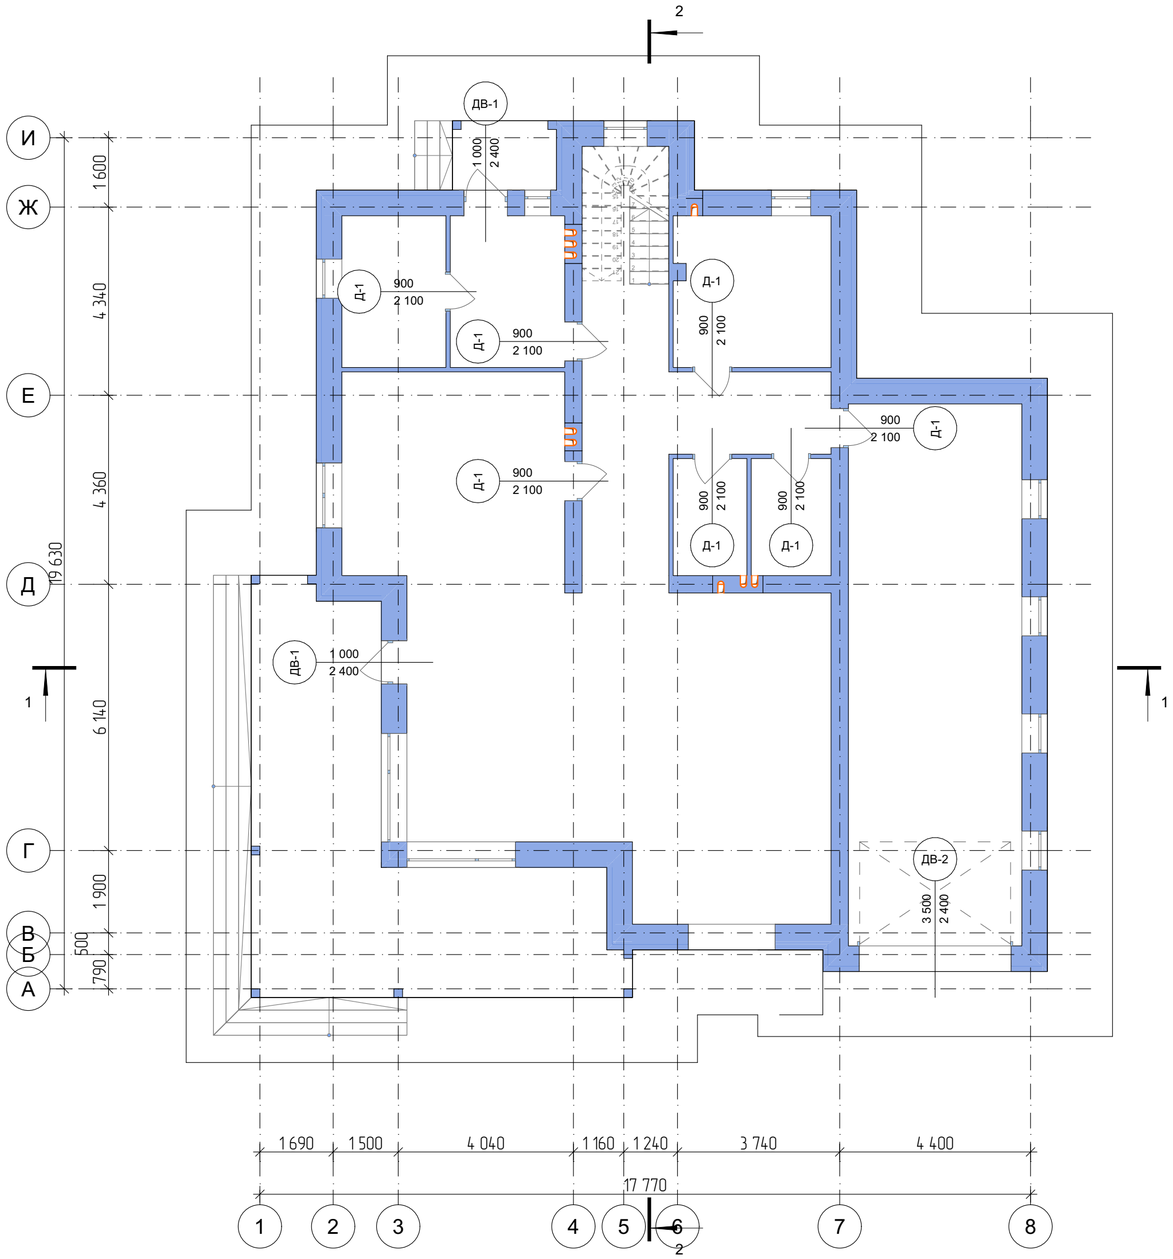

Марка, поз.	Размер проема в кладке, мм	Количество
Д-1	900×2 100	7
ДВ-1	1 000×2 400	2
ДВ-2	3 500×2 400	1

							#ID Проекта
							кадастровый номер Россия
Изм.	Колуч.	Лист	№Док.	Подп.	Дата		
Разраб.						Индивидуальный жилой дом	Стадия: #Стадия Проекта; Лист: 41; Листов:
ГАП							
Маркировка дверных проемов первого этажа							

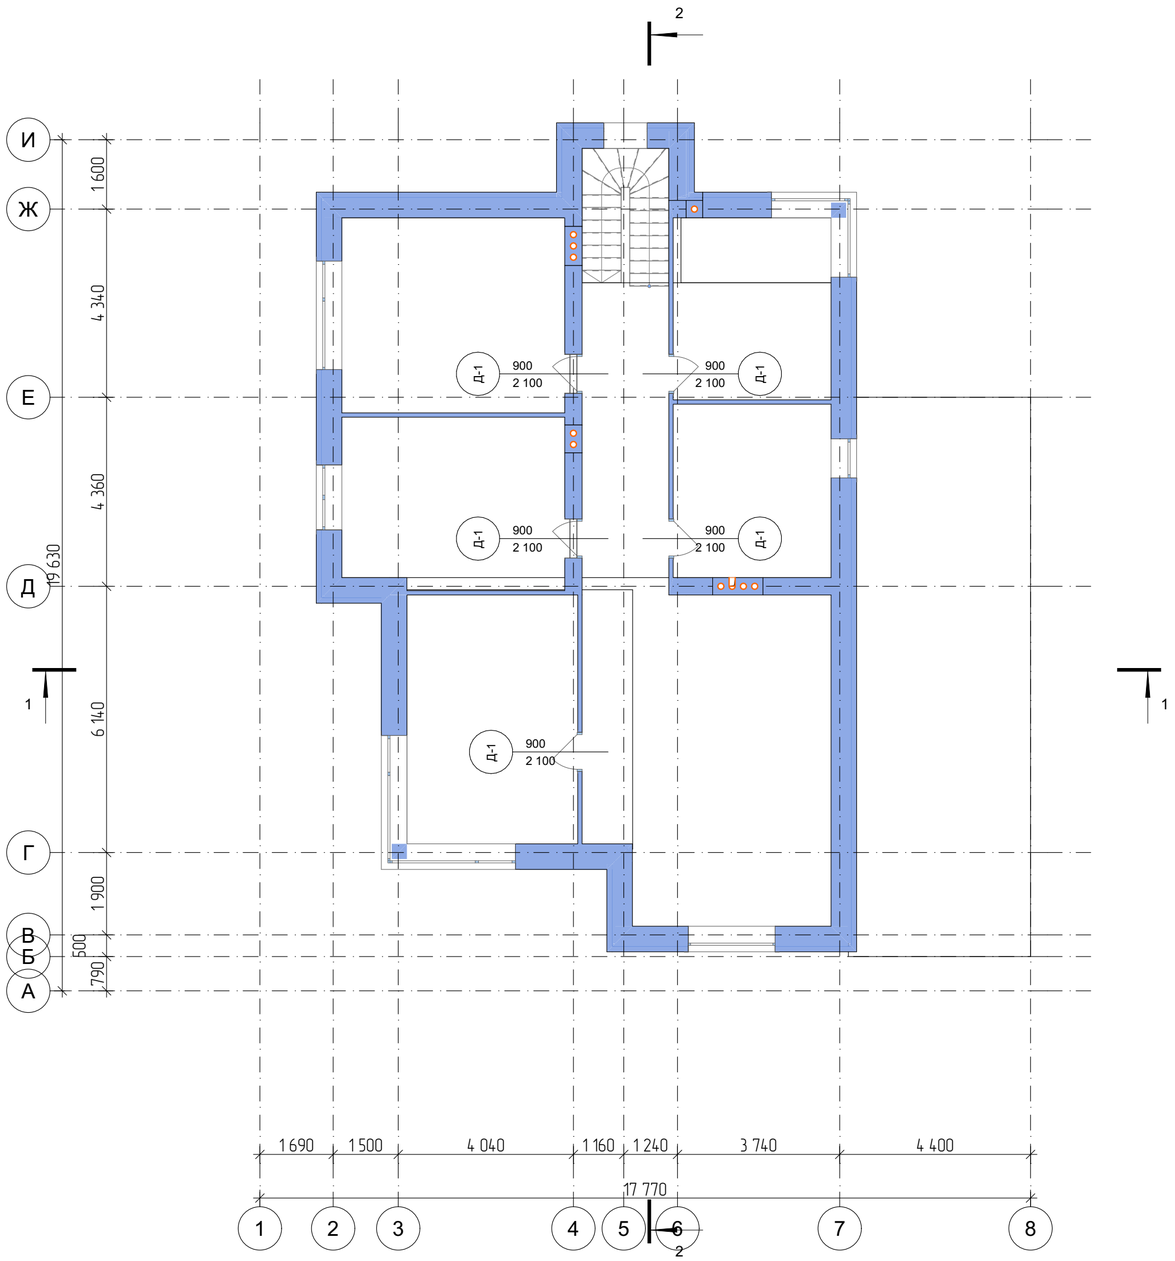

Марка, поз.	Размер проема в кладке, мм	Количество
Д-1	900×2 100	5

						#ID Проекта	
						кадастровый номер Россия	
Изм.	Колуч.	Лист	№Док.	Подп.	Дата		
Разраб.						Индивидуальный жилой дом	Стадия: #Стадия Проекта; Лист: 42; Листов:
ГАП							
Маркировка дверных проемов второго этажа							

Тип	Марка, поз.	Размер проема в кладке, мм	Количество
Дверь, 1-й этаж			
	Д-1	900×2 100	7
	ДВ-1	1 000×2 400	2
	ДВ-2	3 500×2 400	1
Дверь, 2-й этаж			
	Д-1	900×2 100	5
Окно, 1-й этаж			
	ОК-1	2 500×2 000	2
	ОК-2	900×1 500	6
	ОК-4	600×1 500	1
	ОК-5	1 500×1 500	1
	ОК-6	2 000×5 340	1
	П/П	2 000×3 340	1
Окно, 2-й этаж			
	ОК-3	1 000×3 500	1
	ОК-7	900×800	1
	ОК-8	1 760×1 500	2
	ОК-9	2 500×2 000	1
	ОК-10	1 500×2 000	1
	ОК-11	2 890×2 000	2
	П/П	1 000×2 520	1

Перемычки					
Тип	Марк. поз.	Ширина, мм	Высота, мм	Длина,мм	Объем бетона, м3
Дверь, 1-й этаж, Несущие стены					
	Д-1	400,00	200,00	1400,00	0,11
	Д-1	400,00	200,00	1400,00	0,11
	Д-1	400,00	200,00	1400,00	0,11
	ДВ-1	400,00	200,00	1500,00	0,12
	ДВ-1	400,00	200,00	1500,00	0,12
	ДВ-2	400,00	200,00	4000,00	0,32
Дверь, 1-й этаж, Перегородки					
	Д-1	100,00	200,00	1400,00	0,03
	Д-1	100,00	200,00	1400,00	0,03
	Д-1	100,00	200,00	1400,00	0,03
	Д-1	100,00	200,00	1400,00	0,03
Дверь, 2-й этаж, Несущие стены					
	Д-1	400,00	200,00	1400,00	0,11
	Д-1	400,00	200,00	1400,00	0,11
Дверь, 2-й этаж, Перегородки					
	Д-1	100,00	200,00	1400,00	0,03
	Д-1	100,00	200,00	1400,00	0,03

Перемычки					
Тип	Марк. поз.	Ширина, мм	Высота, мм	Длина,мм	Объем бетона, м3
	Д-1	100,00	200,00	1400,00	0,03
Окно, 1-й этаж, Несущие стены					
	ОК-1	400,00	200,00	3000,00	0,24
	ОК-1	400,00	200,00	3000,00	0,24
	ОК-2	400,00	200,00	1400,00	0,11
	ОК-2	400,00	200,00	1400,00	0,11
	ОК-2	400,00	200,00	1400,00	0,11
	ОК-2	400,00	200,00	1400,00	0,11
	ОК-2	400,00	200,00	1400,00	0,11
	ОК-2	400,00	200,00	1400,00	0,11
	ОК-4	400,00	200,00	1100,00	0,09
	ОК-5	400,00	200,00	2000,00	0,16
	ОК-6	400,00	200,00	2500,00	0,20
	П/П	400,00	200,00	2500,00	0,20
Окно, 2-й этаж, Несущие стены					
	ОК-3	400,00	200,00	1500,00	0,12

Перемычки					
Тип	Марк. поз.	Ширина, мм	Высота, мм	Длина,мм	Объем бетона, м3
	ОК-7	400,00	200,00	1400,00	0,11
	ОК-8	400,00	200,00	2460,00	0,20
	ОК-8	400,00	200,00	2460,00	0,20
	ОК-9	400,00	200,00	3000,00	0,24
	ОК-10	400,00	200,00	2000,00	0,16
	ОК-11	400,00	200,00	3590,00	0,29
	ОК-11	400,00	200,00	3590,00	0,29
	П/П	400,00	200,00	1500,00	0,12
					4,84

							#ID Проекта
							кадастровый номер Россия
Изм.	Кол.уч.	Лист	№Док.	Подп.	Дата		
Разраб.						Индивидуальный жилой дом	Стадия: #Стадия Проекта; Лист: 44; Листов:
ГАП							
Ведомость перемычек							

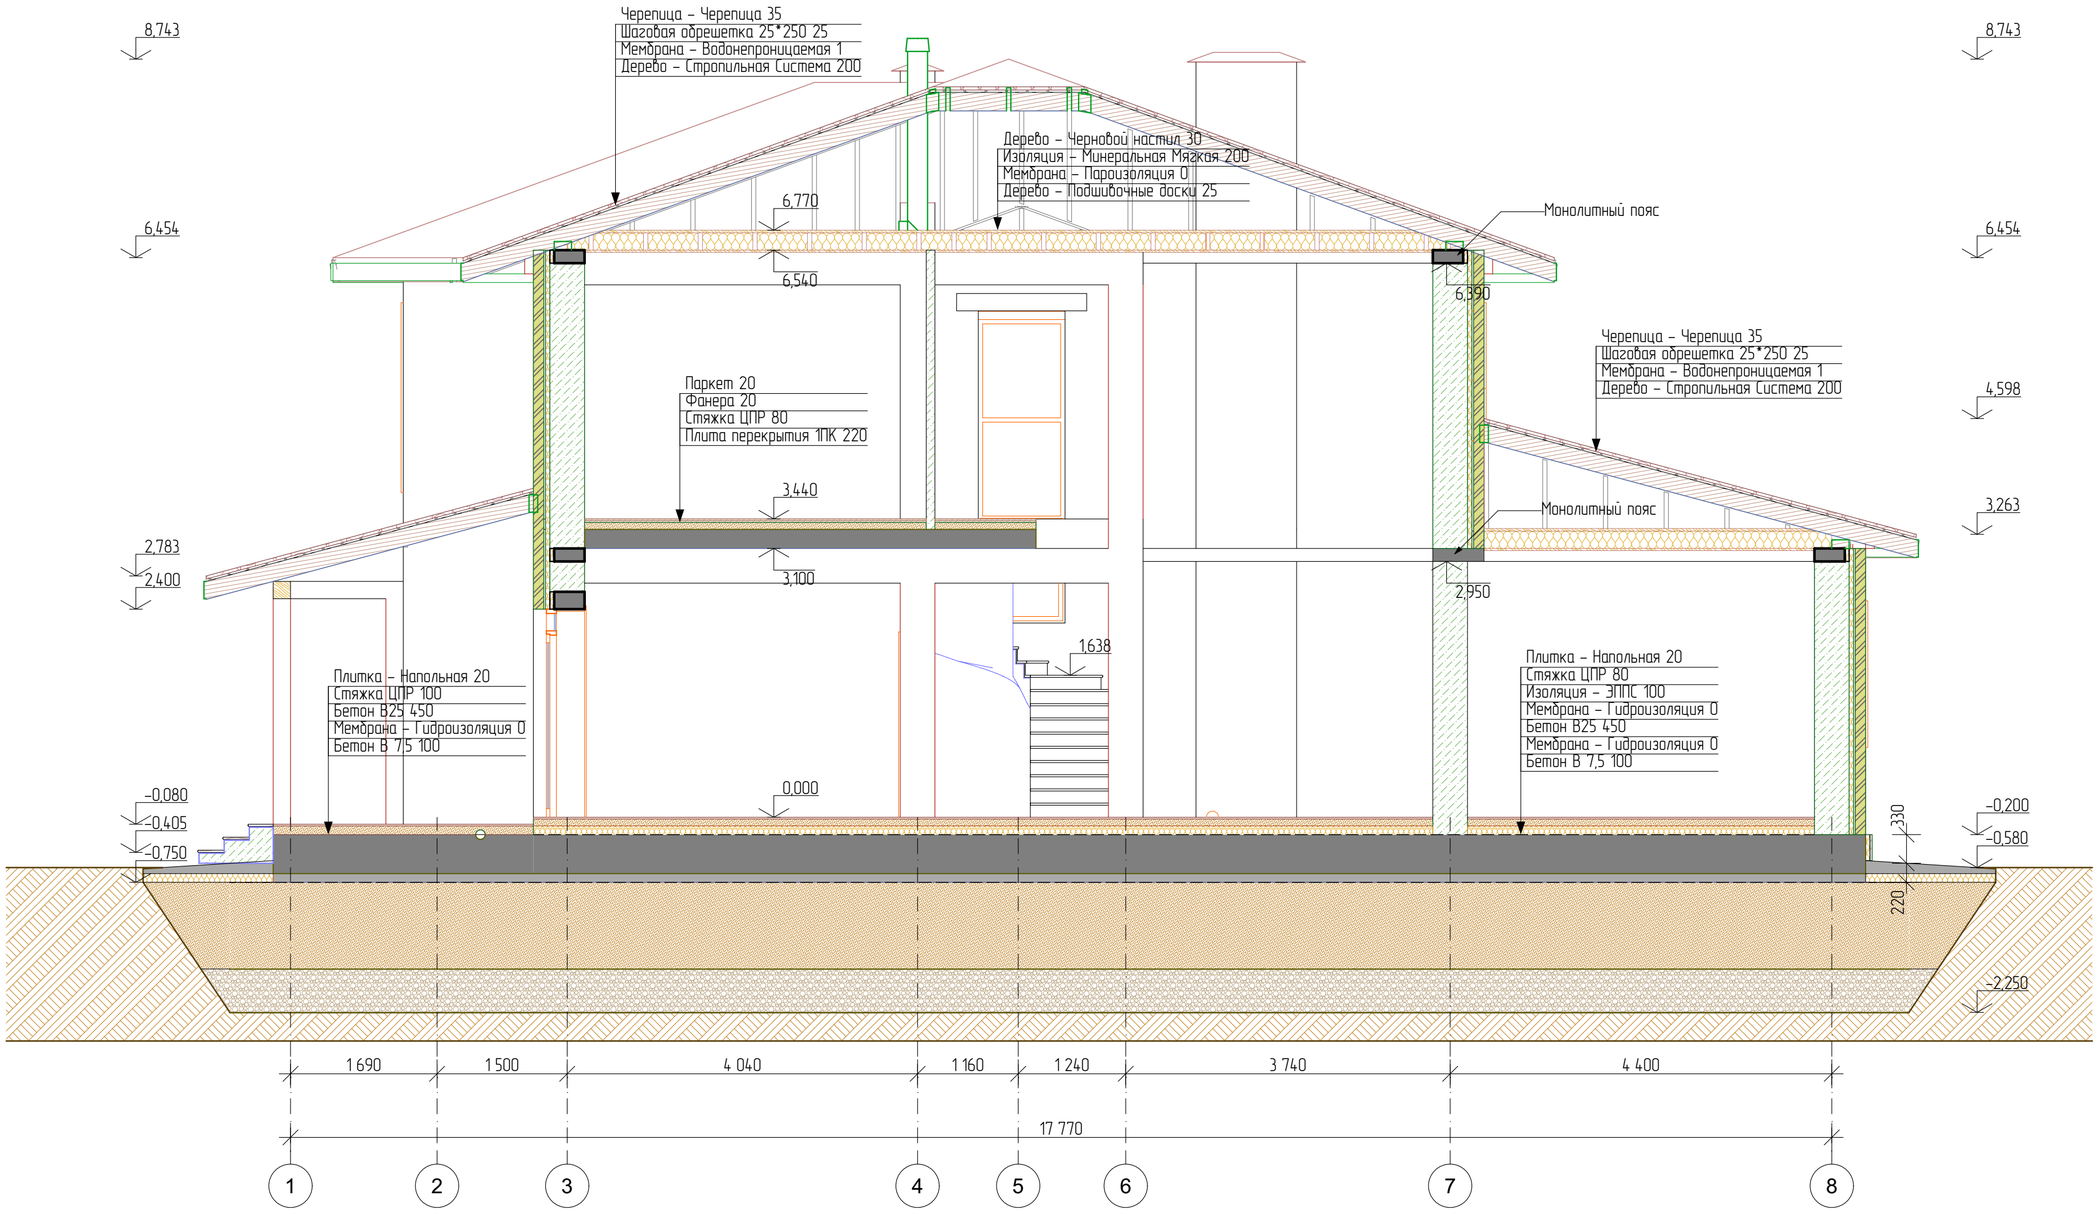

						#ID Проекта	
						кадастровый номер Россия	
Изм.	Колуч.	Лист	№Док.	Подп.	Дата		
Разраб.						Индивидуальный жилой дом	Стадия: #Стадия Проекта; Лист: 45; Листов:
ГАП							
Разрез 1 - 1							

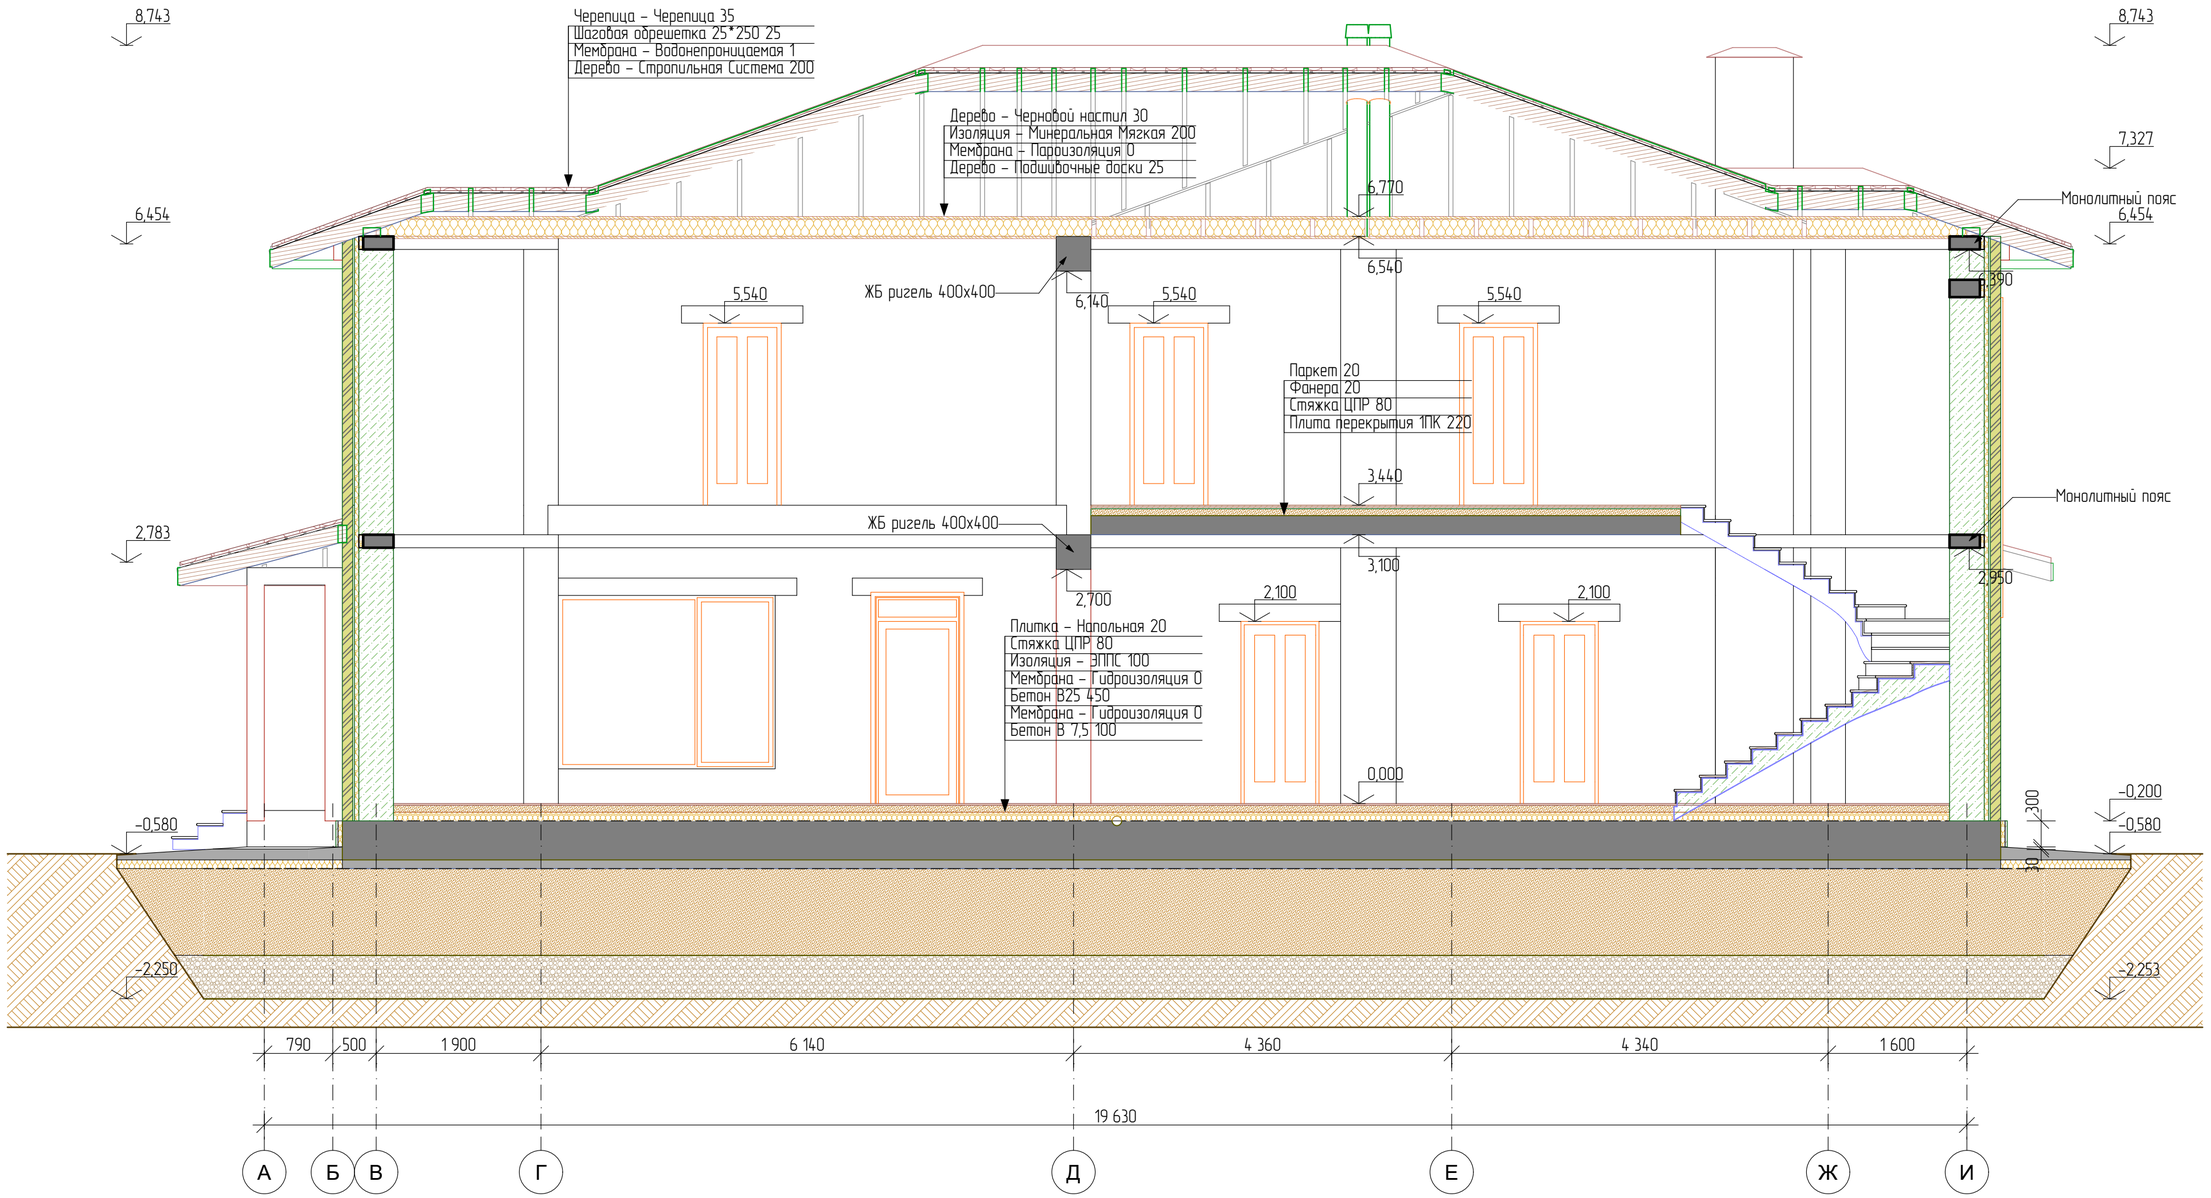

						#ID Проекта	
						кадастровый номер Россия	
Изм.	Колуч.	Лист	№Док.	Подп.	Дата		
Разраб.						Индивидуальный жилой дом	Стадия: #Стадия Проекта; Лист: 46; Листов:
ГАП							
Разрез 2 - 2							

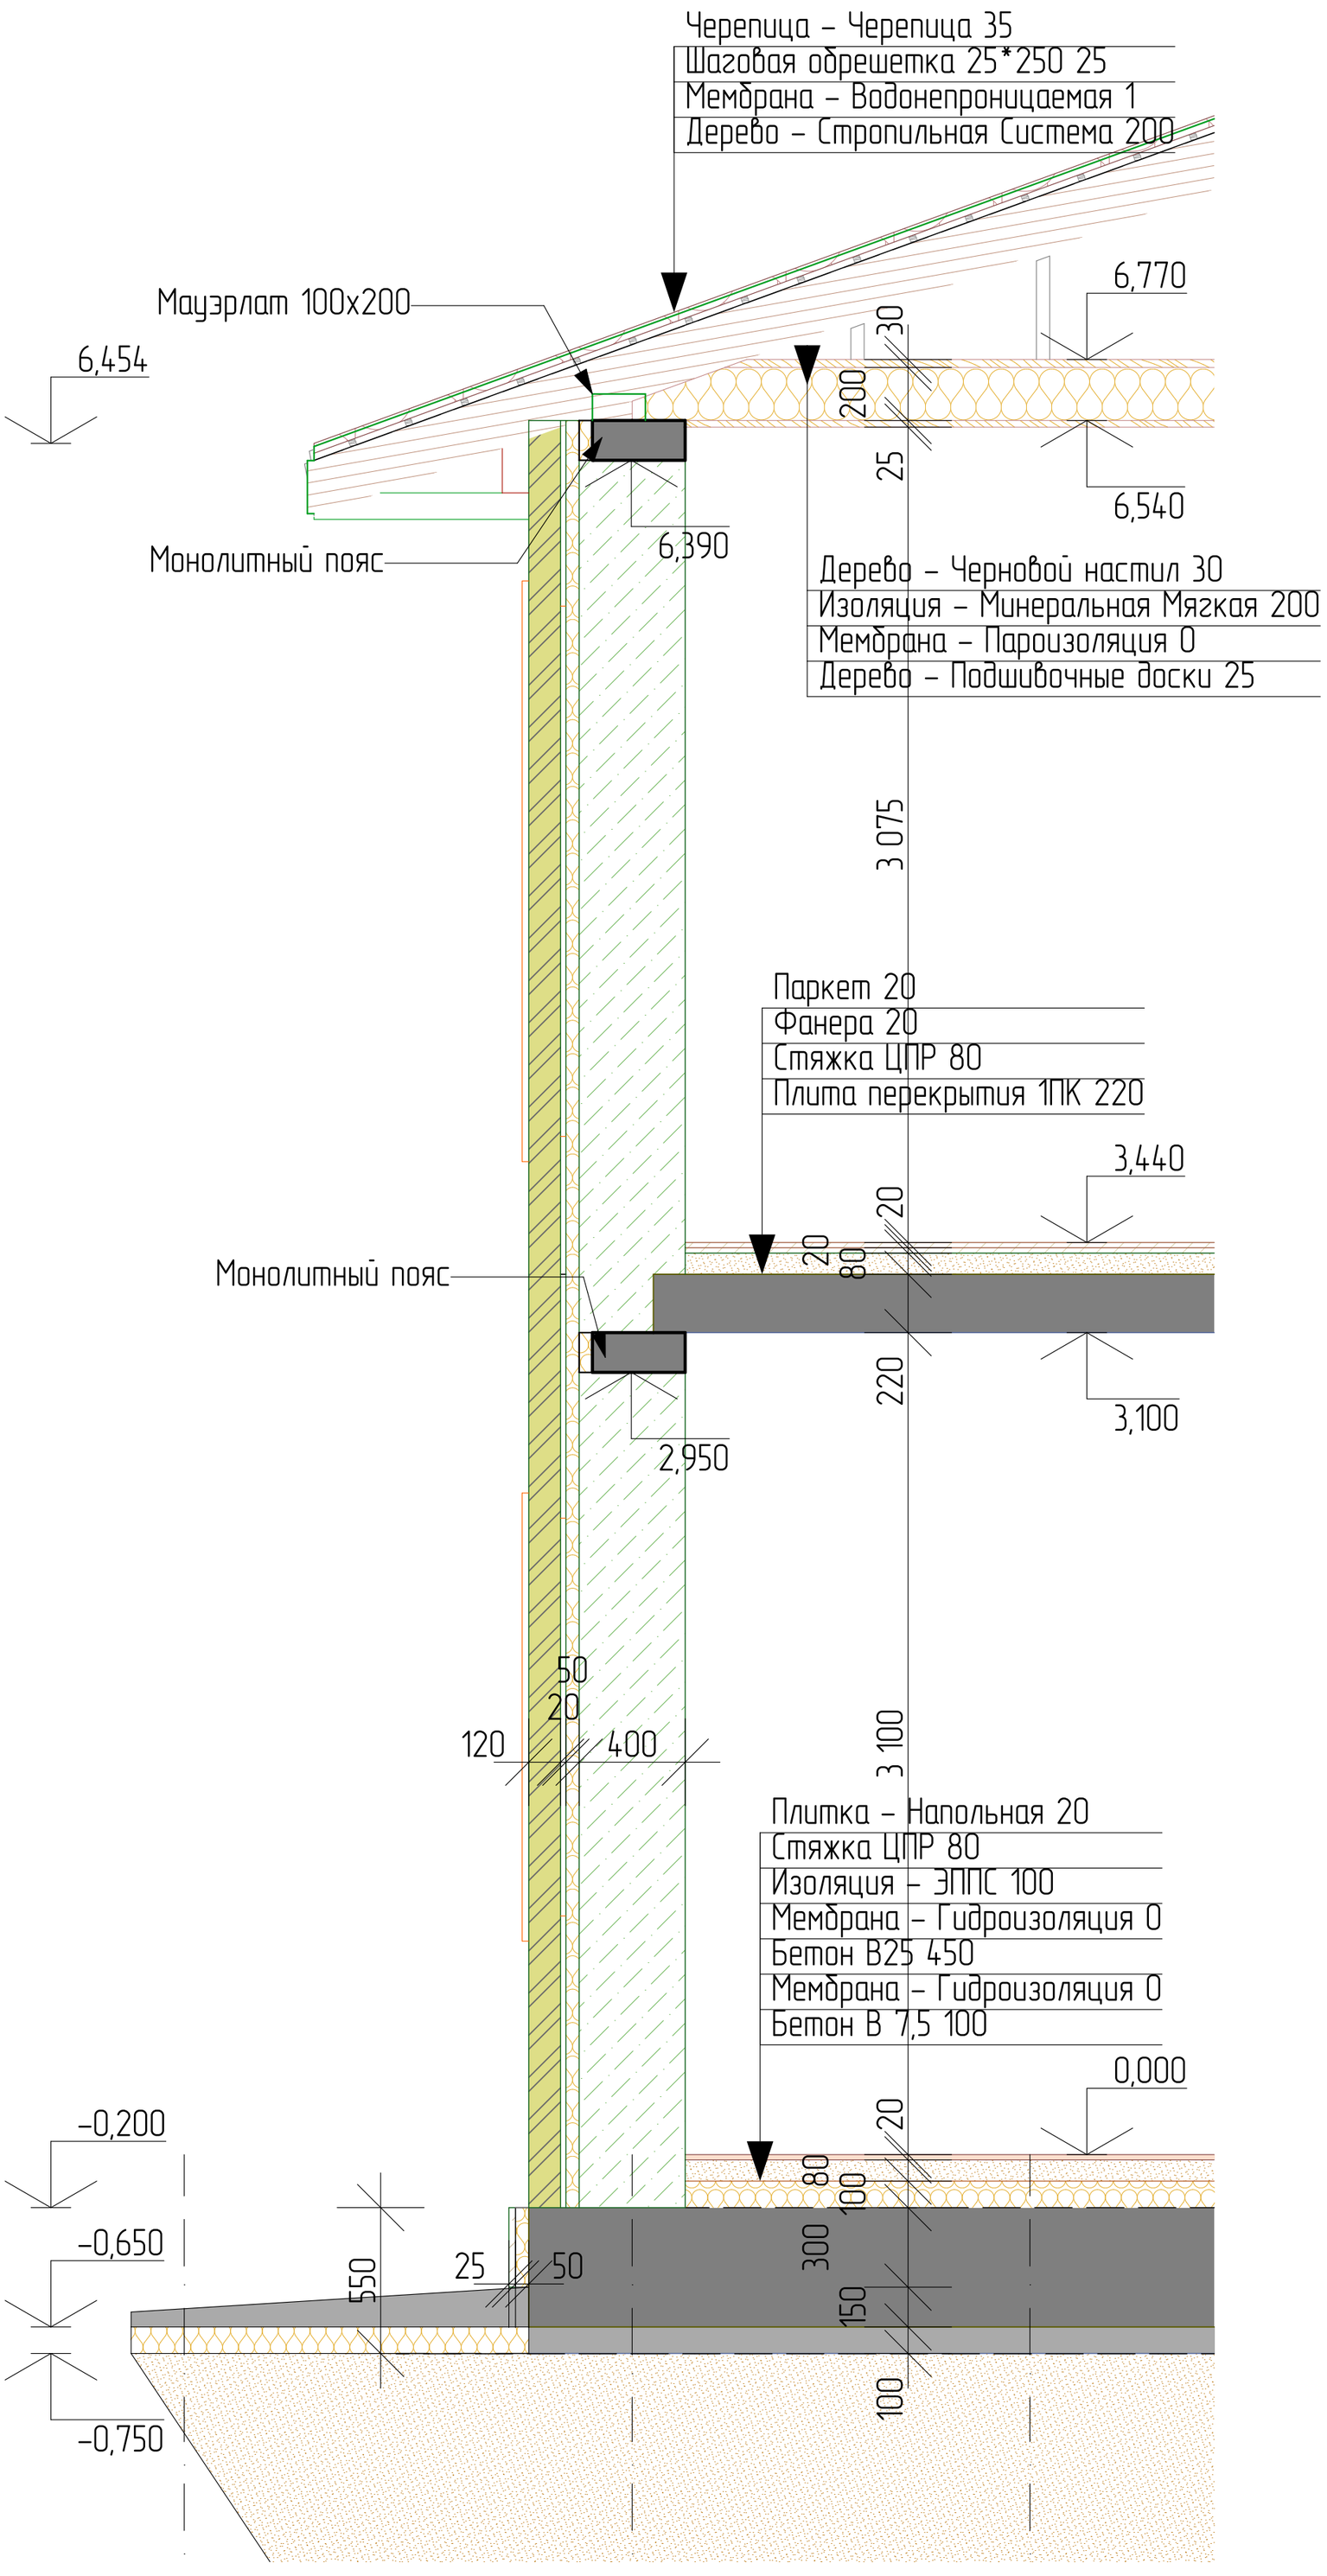

						#ID Проекта	
						кадастровый номер Россия	
Изм.	Кол.уч.	Лист	№Док.	Подп.	Дата		
Разраб.						Индивидуальный жилой дом	Стадия: #Стадия Проекта; Лист: 47; Листов:
ГАП							
Разрез по стене							

Пояснительная записка к монтажу сборных плит перекрытий

Монтаж сборных плит перекрытий выполняется в соответствии с проектной документацией и требованиями нормативных документов (СП 70.13330.2012 «Несущие и ограждающие конструкции», СП 63.13330.2018 «Бетонные и железобетонные конструкции»).

1. Подготовительные работы

- Проверить соответствие размеров и отметок стен, колонн или армопоясов проекту;
- Контролировать горизонтальность поверхностей опирания (допуск ±10 мм на здание и ±5 мм на 2 м длины правила);
- Очистить опорные поверхности от мусора, пыли и влаги;
- Уложить выравнивающий слой цементно-песчаного раствора толщиной 20–30 мм.

2. Монтаж плит

- Подъём плит производится грузоподъёмными механизмами с применением инвентарных строп и траверс;
- Опирание плит на стены или балки должно составлять не менее 120 мм (если проектом не указано иное);
- Укладка выполняется с зазором между плитами 20–30 мм для последующей заделки швов;
- Допускаемые отклонения: по отметке уровня — ±10 мм, по оси — ±20 мм.

3. Стыки и швы

- Зазоры между плитами и местами их опирания на стены заполняются цементно-песчаным раствором или мелкозернистым бетоном марки не ниже М100;
- Швы уплотняются и заглаживаются.

4. Работы в зимнее время

- Работы допускается выполнять при отрицательных температурах при условии применения противоморозных добавок в растворы и бетоны или устройства прогрева;
- Поверхности опирания плит должны быть очищены от снега и наледи;
- Температура раствора при укладке должна соответствовать требованиям СП 70.13330.2012.

5. Контроль качества

- Проверка правильности установки плит выполняется нивелиром и отвесом;
- Контролируется величина опирания плит, заполнение швов и ровность поверхности;
- Контроль качества раствора и замоноличивания швов производится визуально и при необходимости лабораторными испытаниями;
- Все работы выполняются в соответствии с проектной документацией и нормативными требованиями.

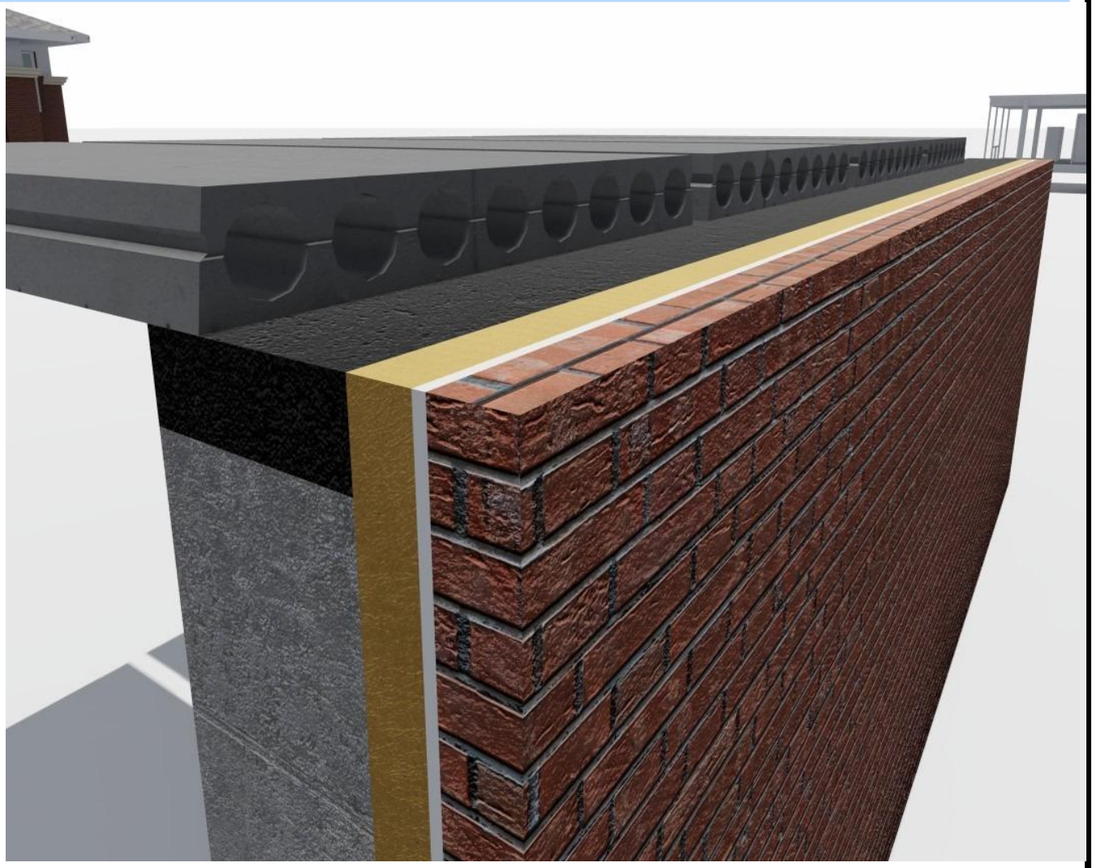

						#ID Проекта		
						кадастровый номер Россия		
Изм.	Кол.уч.	Лист	№Док.	Подп.	Дата			
Разраб.						Индивидуальный жилой дом	Стадия	Лист	Листов
ГАП							#Стадия Проекта	48	
ПЗ - монтаж плит 1ПК									

Пояснительная записка к устройству деревянного межэтажного перекрытия

Деревянное перекрытие выполняется в соответствии с проектной документацией и требованиями нормативных документов (СП 64.13330.2017 «Деревянные конструкции», СП 70.13330.2012 «Несущие и ограждающие конструкции»).

1. Подготовительные работы

- Проверить соответствие размеров и отметок несущих стен и опор проекту;
- Подготовить места опирания балок, при необходимости уложить гидроизоляционные прокладки (рубероид, битумная мастика);
- Заготовить балки сечением 200×50 мм, черновой и чистовой настил, утеплитель и крепёжные элементы;
- Все деревянные элементы обработать антисептическими и огнезащитными составами.

2. Устройство несущих балок

- Балки перекрытия устанавливаются с шагом по осям 600 мм, что позволяет плотно укладывать утеплитель или звукоизоляцию;
- Опирание балок на стены или ригели должно быть не менее 150 мм;
- Концы балок, опираемые на стены, изолируются рулонными материалами от влаги;
- Балки выставляются в одной плоскости, горизонтальность проверяется лазерным уровнем (допуск ±5 мм на 2 м).

3. Черновой настил и пароизоляция

- С нижней стороны балок монтируется сплошной черновой настил из обрезной доски толщиной 25 мм;
- Настил укладывается плотно, без щелей, крепится к балкам гвоздями или саморезами;
- Поверх чернового настила укладывается сплошной слой пароизоляционной плёнки с нахлёстом 150–200 мм и проклейкой стыков.

4. Утепление и звукоизоляция

- Пространство между балками заполняется плитным утеплителем или звукоизоляцией в зависимости от назначения перекрытия;
- Ширина плит должна соответствовать шагу балок (600 мм) и обеспечивать плотную укладку;
- Толщина утеплителя определяется проектом, работы выполняются строго в соответствии с проектной документацией.

5. Чистовой настил (верхний слой перекрытия)

- По верхней плоскости балок укладывается настил из доски толщиной 30 мм;
- Доски прибиваются гвоздями или фиксируются саморезами к каждой балке;
- Настил выполняется сплошным, с плотным примыканием досок;
- Допустимое отклонение по горизонту — ±10 мм на всё перекрытие.

6. Работы в зимнее время

- Деревянные элементы должны быть сухими (влажность не более 20%);
- Запрещается применять отсыревшие или обледеневшие материалы;
- Утеплитель укладывается в сухом состоянии, с последующим контролем после прогрева помещений.

7. Контроль качества

- Проверяется правильность установки балок (сечение 200×50 мм, шаг 600 мм), надёжность креплений и горизонтальность;
- Контролируется плотность укладки утеплителя и герметичность пароизоляции;
- Проверяется качество чернового и чистового настила (отсутствие щелей, ровность поверхности);
- Все деревянные элементы должны быть обработаны антисептическими и огнезащитными составами;
- Работы выполняются в соответствии с требованиями СП 64.13330.2017 и СП 70.13330.2012.

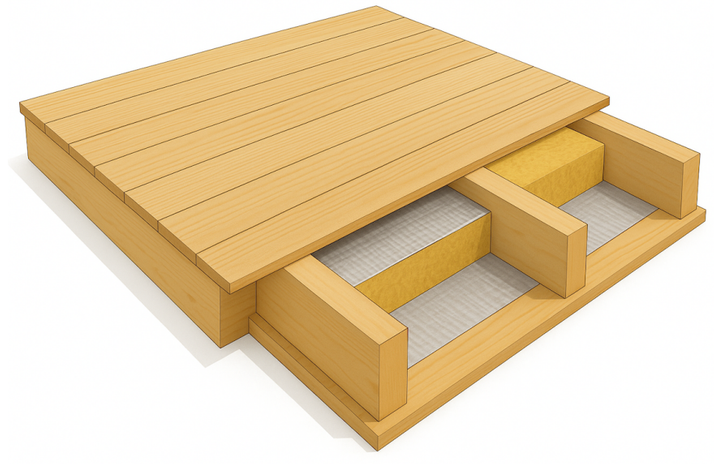

						#ID Проекта		
						кадастровый номер Россия		
Изм.	Кол.уч.	Лист	№Док.	Подп.	Дата			
Разраб.						Индивидуальный жилой дом	Стадия: #Стадия Проекта	Лист: 49 / Листов:
ГАП								
ПЗ - Деревянное перекрытие								

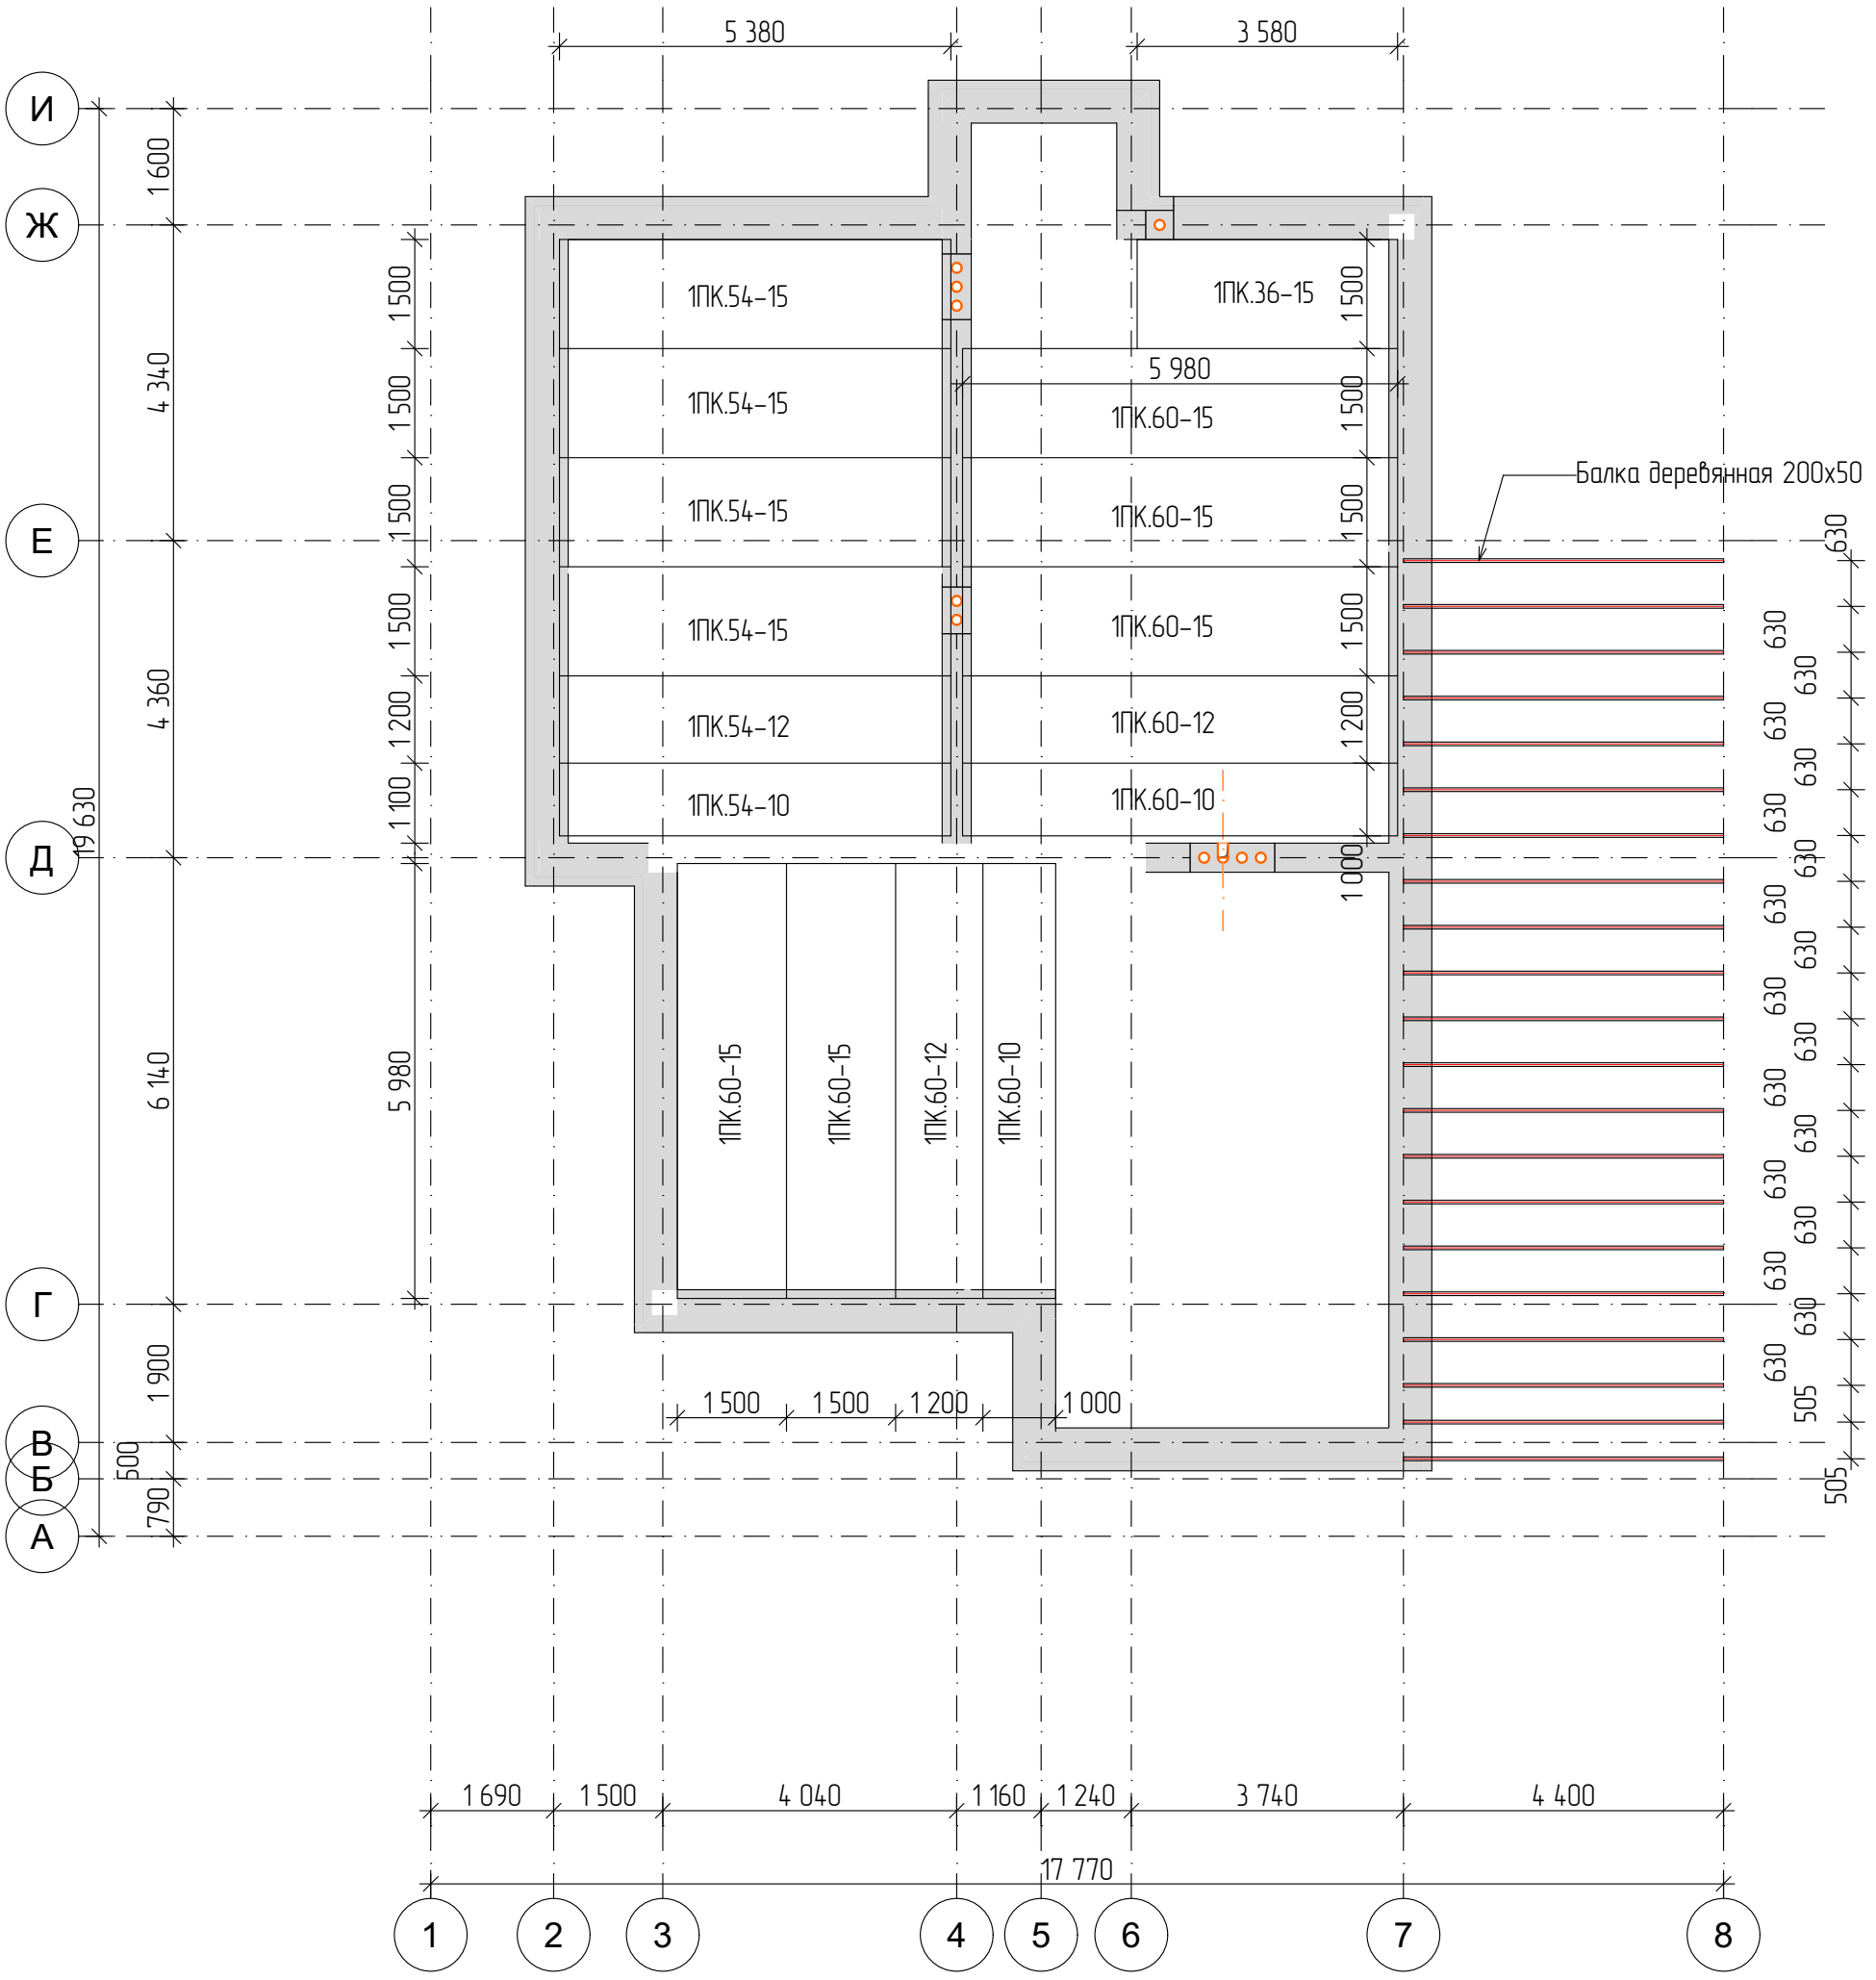

						#ID Проекта	
						кадастровый номер Россия	
Изм.	Кол.уч.	Лист	№Док.	Подп.	Дата		
Разраб.						Индивидуальный жилой дом	Стадия: #Стадия Проекта; Лист: 50; Листов:
ГАП							
План перекрытия +3,100							

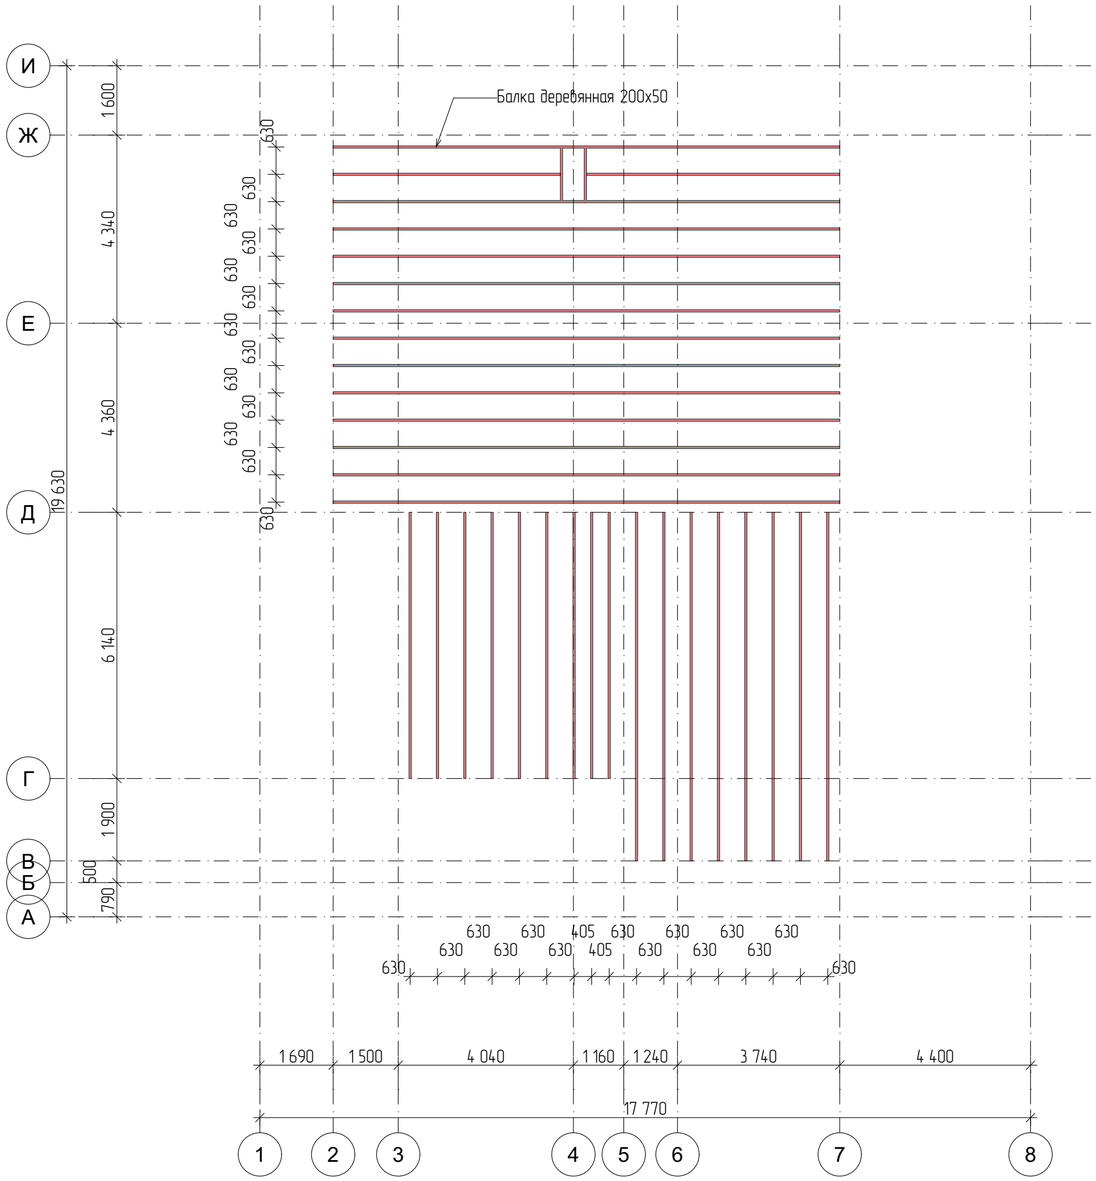

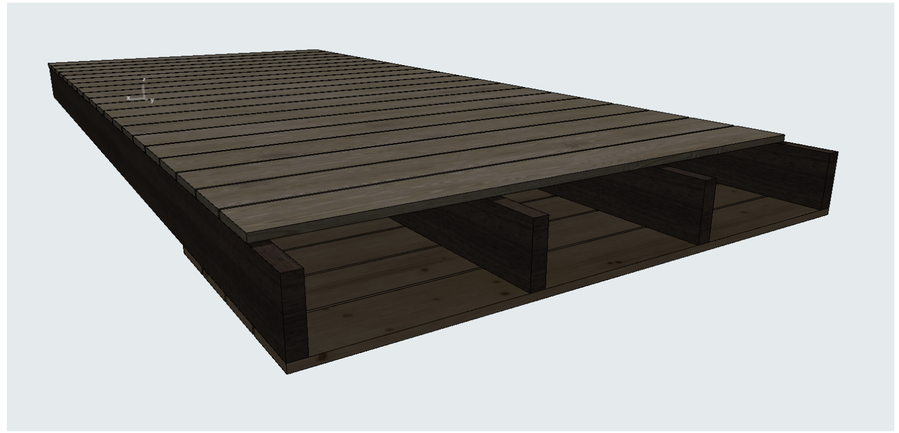

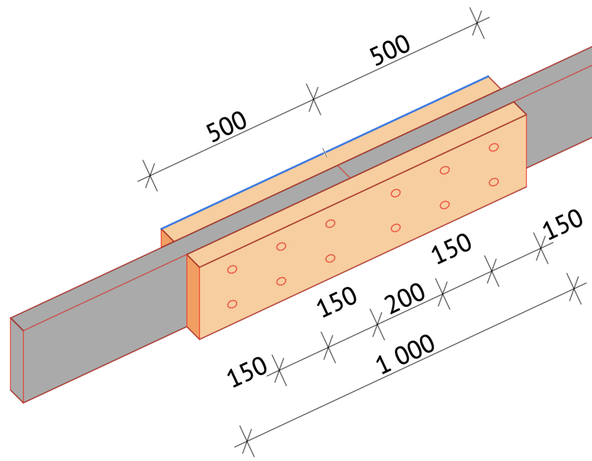

						#ID Проекта	
						кадастровый номер России	
Изм.	Колуч.	Лист	№Док.	Подп.	Дата		
Разраб.						Индивидуальный жилой дом	Стадия: #Стадия Проекта; Лист: 51; Листов:
ГАП							
План перекрытий на отм 6,540							

ВЕДОМОСТЬ ПЕРЕКРЫТИЙ			
Этаж	**Наименование**	Кол-во	Длина, мм
1-й этаж			
	1ПК.54-10	1	---
	1ПК.54-12	1	---
	1ПК.36-15	1	---
	1ПК.60-12	2	---
	1ПК.60-10	2	---
	1ПК.54-15	4	---
	1ПК.60-15	5	---
2-й этаж			
		21	---
	Балка деревянная 200х50	21	4 400
Кровля			
	Балка деревянная 200х50	1	5 240
	Балка деревянная 200х50	1	5 840
	Балка деревянная 200х50	2	1 210
	Балка деревянная 200х50	8	8 040
	Балка деревянная 200х50	13	5 540
	Балка деревянная 200х50	22	6 140
		47	---

Пояснительная записка к устройству монолитного пояса

Монолитный железобетонный пояс (армопояс) выполняется в соответствии с проектной документацией и требованиями нормативных документов (СП 70.13330.2012 «Несущие и ограждающие конструкции», СП 63.13330.2018 «Бетонные и железобетонные конструкции»).

1. Подготовительные работы

- Проверить соответствие размеров и отметок стен проекту;
- Очистить верхнюю поверхность стен от мусора, пыли и остатков раствора;
- Заготовить опалубочные материалы, арматуру и бетонную смесь класса В20;
- Установить временные подмости для безопасного производства работ.

2. Устройство опалубки

- Опалубка для монолитного пояса выполняется из досок, влагостойкой фанеры или инвентарных щитов;
- Внутренние поверхности опалубки должны быть герметичными, чтобы исключить вытекание цементного молочка;
- Опалубка надёжно закрепляется распорками и стяжками, исключающими деформацию при бетонировании;
- Проверяется горизонтальность и размеры опалубки (допуск ±5 мм на 2 м).

3. Армирование

- Армирование выполняется четырьмя продольными стержнями арматуры Ø12 мм класса AIII;
- Продольные стержни объединяются хомутами Ø8 мм с шагом 400 мм;
- Каркас устанавливается на фиксаторы для обеспечения защитного слоя бетона не менее 30 мм;
- Соединения арматуры выполняются вязальной проволокой.

4. Бетонирование

- Применяется бетонная смесь класса В20, морозостойкость не ниже F150, водонепроницаемость W6 (по проекту);
- Бетон укладывается в опалубку равномерно по всей длине пояса за один приём;
- Обязательное уплотнение смеси глубинными вибраторами;
- Поверхность выравнивается правилом или рейкой.

5. Уход за бетоном

- Свежеуложенный бетон укрывается плёнкой или матами и увлажняется в течение не менее 7 суток;
- Опалубка снимается после достижения бетоном прочности не менее 70%;
- Дальнейшие работы (кладка стен выше, монтаж перекрытий) допускаются только после набора проектной прочности бетона.

6. Контроль качества

- Проверяется правильность установки опалубки и её геометрия;
- Контролируется положение арматурного каркаса и толщина защитного слоя бетона;
- Качество бетона подтверждается испытанием контрольных образцов;
- Визуально проверяется сплошность бетона, отсутствие раковин, трещин и расслоений;
- Работы выполняются в соответствии с требованиями СП 70.13330.2012 и СП 63.13330.2018.

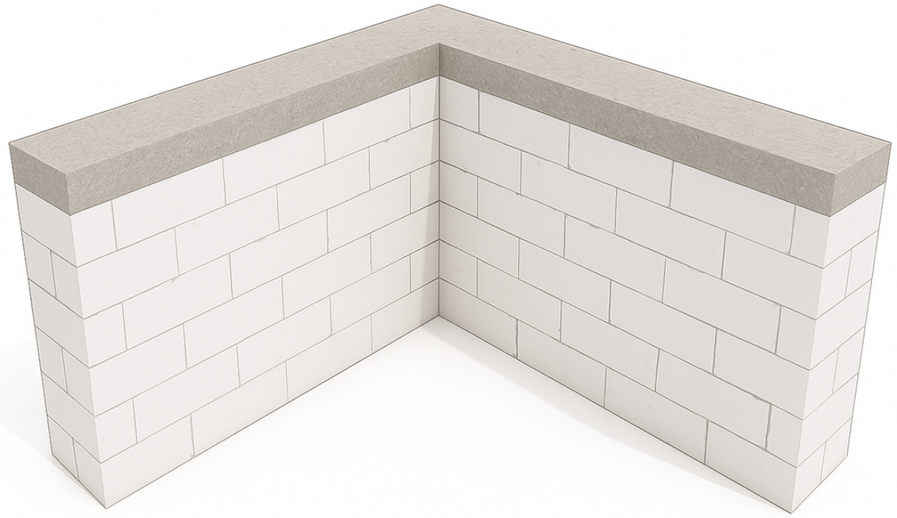

						#ID Проекта		
						кадастровый номер Россия		
Изм.	Кол.уч.	Лист	№Док.	Подп.	Дата			
Разраб.						Индивидуальный жилой дом	Стадия	Лист	Листов
ГАП							#Стадия Проекта	53	
ПЗ - монолитный пояс									

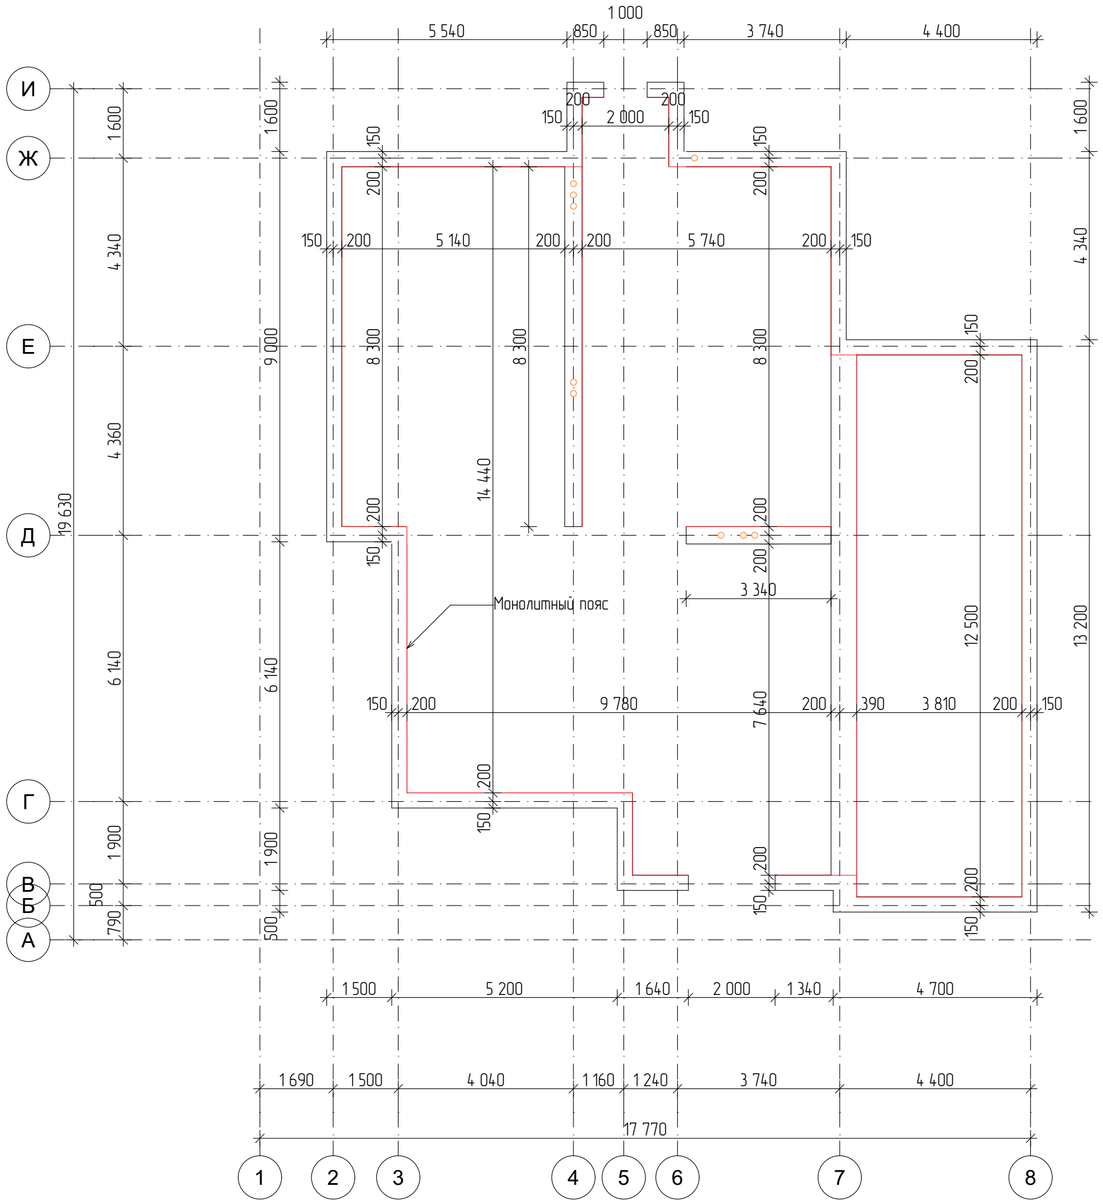

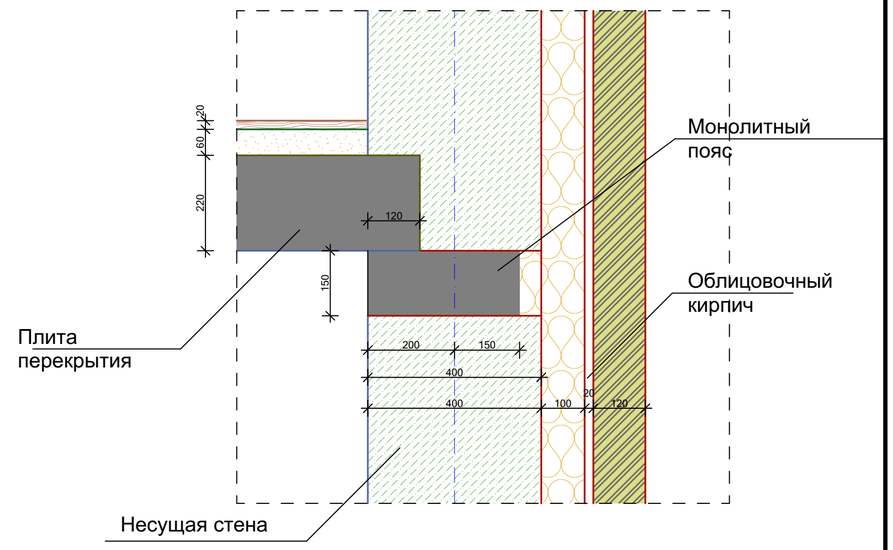

1.Монолитный пояс выполняется по всему периметру здания на уровне проектных отметок, указанных в рабочей документации. Его назначение — объединение несущих стен и перекрытий в единую пространственную систему, распределение нагрузок и обеспечение общей жёсткости сооружения.

2.Армирование пояса выполняется арматурой класса С500 диаметром 12 мм в виде пространственного каркаса, состоящего из четырёх продольных стержней. Стержни объединяются хомутами и связями из конструктивной арматуры. Длина нахлёста рабочих стержней принимается не менее 420 мм (35 диаметров), что соответствует требованиям СП 63.13330 «Бетонные и железобетонные конструкции».

3. Конструктивная арматура выполняется из гладкой стали диаметром 8 мм с шагом 400 мм. Хомуты и поперечные элементы обеспечивают необходимую жёсткость и сохраняют проектное положение продольных стержней при бетонировании.

4.Для устройства монолитного пояса применяется бетон класса не ниже В20 (М250) с подвижностью П3–П4. Перед бетонированием необходимо смонтировать и закрепить опалубку, обеспечить защитный слой бетона для рабочей арматуры (не менее 25 мм со стороны опалубки и не менее 30 мм сверху и снизу).

5.Бетонная смесь должна укладываться послойно с обязательным уплотнением глубинным вибратором. Особое внимание уделяется уплотнению в угловых и стыковых зонах, чтобы исключить образование пустот и раковин. После бетонирования поверхность конструкции необходимо защитить от пересыхания, воздействия дождя и отрицательных температур. Уход за бетоном осуществляется по СП 70.13330 «Несущие и ограждающие конструкции».

						#ID Проекта		
						кадастровый номер Россия		
Изм.	Колуч.	Лист	№Док.	Подп.	Дата			
Разраб.						Индивидуальный жилой дом	Стадия: #Стадия Проекта	Лист: 54 / Листов:
ГАП								
Монолитный пояс на отм 2,950								

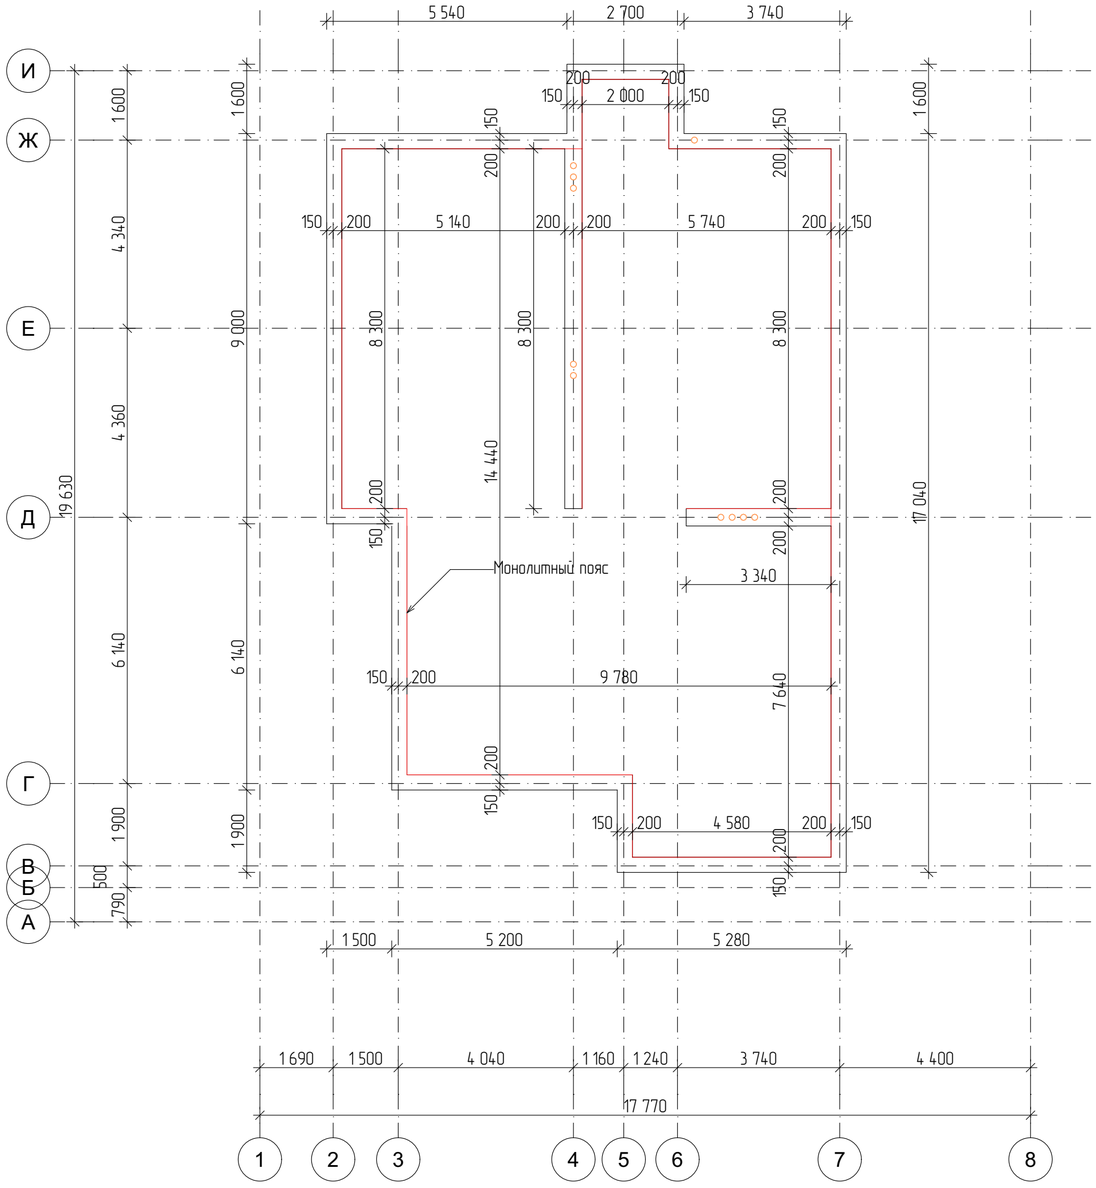

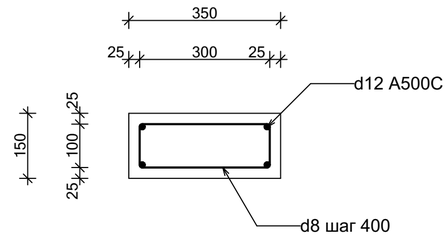

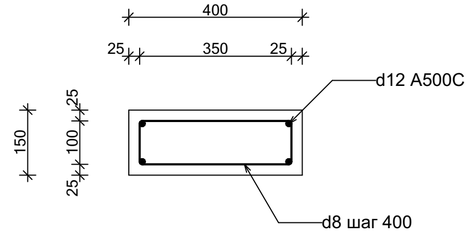

						#ID Проекта		
						кадастровый номер Россия		
Изм.	Кол.уч.	Лист	№Док.	Подп.	Дата			
Разраб.						Индивидуальный жилой дом	Стадия	Лист	Листов
ГАП							#Стадия Проекта	55	
Монолитный пояс на отм 6,390									

ВЕДОМОСТЬ БЕТОНА НА МОНОЛИТНЫЙ ПОЯС			
Этаж	Материал	**Наименование**	Объем, м3
1-й этаж			
	Бетон В20	Монолитный пояс	5,24
2-й этаж			
	Бетон В20	Монолитный пояс	3,80
			9,04 м³

Ведомость арматуры				
Этаж	Описание	Кол-во	Ед. изм.	Вес, кг
1-й этаж				
	Арматура А500С d12	412,68	м.п.	366,46
2-й этаж				
	Арматура А500С d12	325,63	м.п.	289,16
		738,28		**655,65**

Хомуты на монолитный пояс						
Этаж	Наименование	Кол-во	Ед.изм.	Вес, кг	Длина 1 хомута	Кол-во хомутов
1-й этаж						
	d8	201,69	м.п.	79,67	0,85	237,00
	d8	43,09	м.п.	17,02	1,23	35,00
2-й этаж						
	d8	177,01	м.п.	69,92	0,85	208,00
		421,81		**166,61**		**480,00**

Пояснительная записка к устройству скатной кровли

Скатная кровля выполняется в соответствии с проектной документацией и требованиями нормативных документов (СП 17.13330.2017 «Кровли», СП 64.13330.2017 «Деревянные конструкции», СП 70.13330.2012 «Несущие и ограждающие конструкции»).

1. Общие положения

• На представленном проекте отражён план расположения стропил, однако конструктивная часть кровли не проработана в полном объёме: отсутствуют узлы сопряжений, крепёжные решения, элементы жёсткости (ригелей, стоек, подкосов, прогонов и др.).

• Для обеспечения надёжности и пространственной жёсткости стропильной системы требуется дополнительная проработка в разделе КР.

• До разработки конструктивного решения допускается вести только подготовительные работы и укрупнённый монтаж с временными креплениями.

2. Стропильная система

• Основными несущими элементами скатной кровли являются стропила, в нашем случае балки сечением 200×50 мм;

• Шаг установки стропил принимается в соответствии с проектом, исходя из расчётной нагрузки на кровлю и применяемого покрытия;

• Нижние концы стропил опираются на мауэрлат, верхние соединяются в коньковом узле. В проекте данный узел не разработан, требуется уточнение способа сопряжения (врубка, металлические накладки, болтовые соединения);

• Для восприятия распорных усилий и предотвращения деформации стропильной системы необходимо предусмотреть дополнительные элементы — ригели, затяжки, стойки, подкосы, которые должны быть отражены в разделе КР;

• При необходимости устройства больших пролётов должны применяться прогоны с опиранием на стойки.

3. Мауэрлат

• В качестве мауэрлата применяется брус сечением 200×100 мм;

• Мауэрлат укладывается по верхнему ряду стен на гидроизоляционный слой (рулонные материалы в два слоя);

• Крепление мауэрлата выполняется анкерными болтами или шпильками, заранее выпущенными из монолитного армопояса;

• Проверяется правильность укладки и горизонтальность мауэрлата, так как он является базовым опорным элементом всей стропильной системы.

4. Крепление стропил

• Стропила к мауэрлату крепятся гвоздевыми соединениями, болтами, металлическими уголками или перфорированными пластинами в зависимости от выбранного узла;

• Узел крепления должен исключать скольжение и смещение стропил под нагрузкой;

• Дополнительно должны предусматриваться связи для предотвращения «разъезда» стропил.

5. Особенности конструкции

• В проекте отражено только расположение стропил, без конструктивного обеспечения жёсткости. Для нормальной работы системы необходимо разработать рабочие чертежи с указанием:

– узла конька;

– соединения стропил с мауэрлатом;

– устройства ригелей, затяжек и прогона;

– крепления стропил между собой и к вспомогательным элементам.

• Отсутствие этих решений влечёт риск недостаточной устойчивости кровли при ветровых и снеговых нагрузках.

6. Контроль качества

• Проверяется правильность установки стропил (сечение 200×50 мм, шаг по проекту);

• Контролируется горизонтальность мауэрлата и симметрия скатов;

• Оценивается качество креплений и прочность узлов;

• Все деревянные элементы должны быть обработаны антисептическими и огнезащитными составами;

• Работы выполняются в соответствии с требованиями СП 17.13330.2017, СП 64.13330.2017 и СП 70.13330.2012.

						#ID Проекта		
						кадастровый номер Россия		
Изм.	Кол.уч.	Лист	№Док.	Подп.	Дата			
Разраб.						Индивидуальный жилой дом	Стадия: #Стадия Проекта	Лист: 57 / Листов:
ГАП								
ПЗ - Скатная кровля								

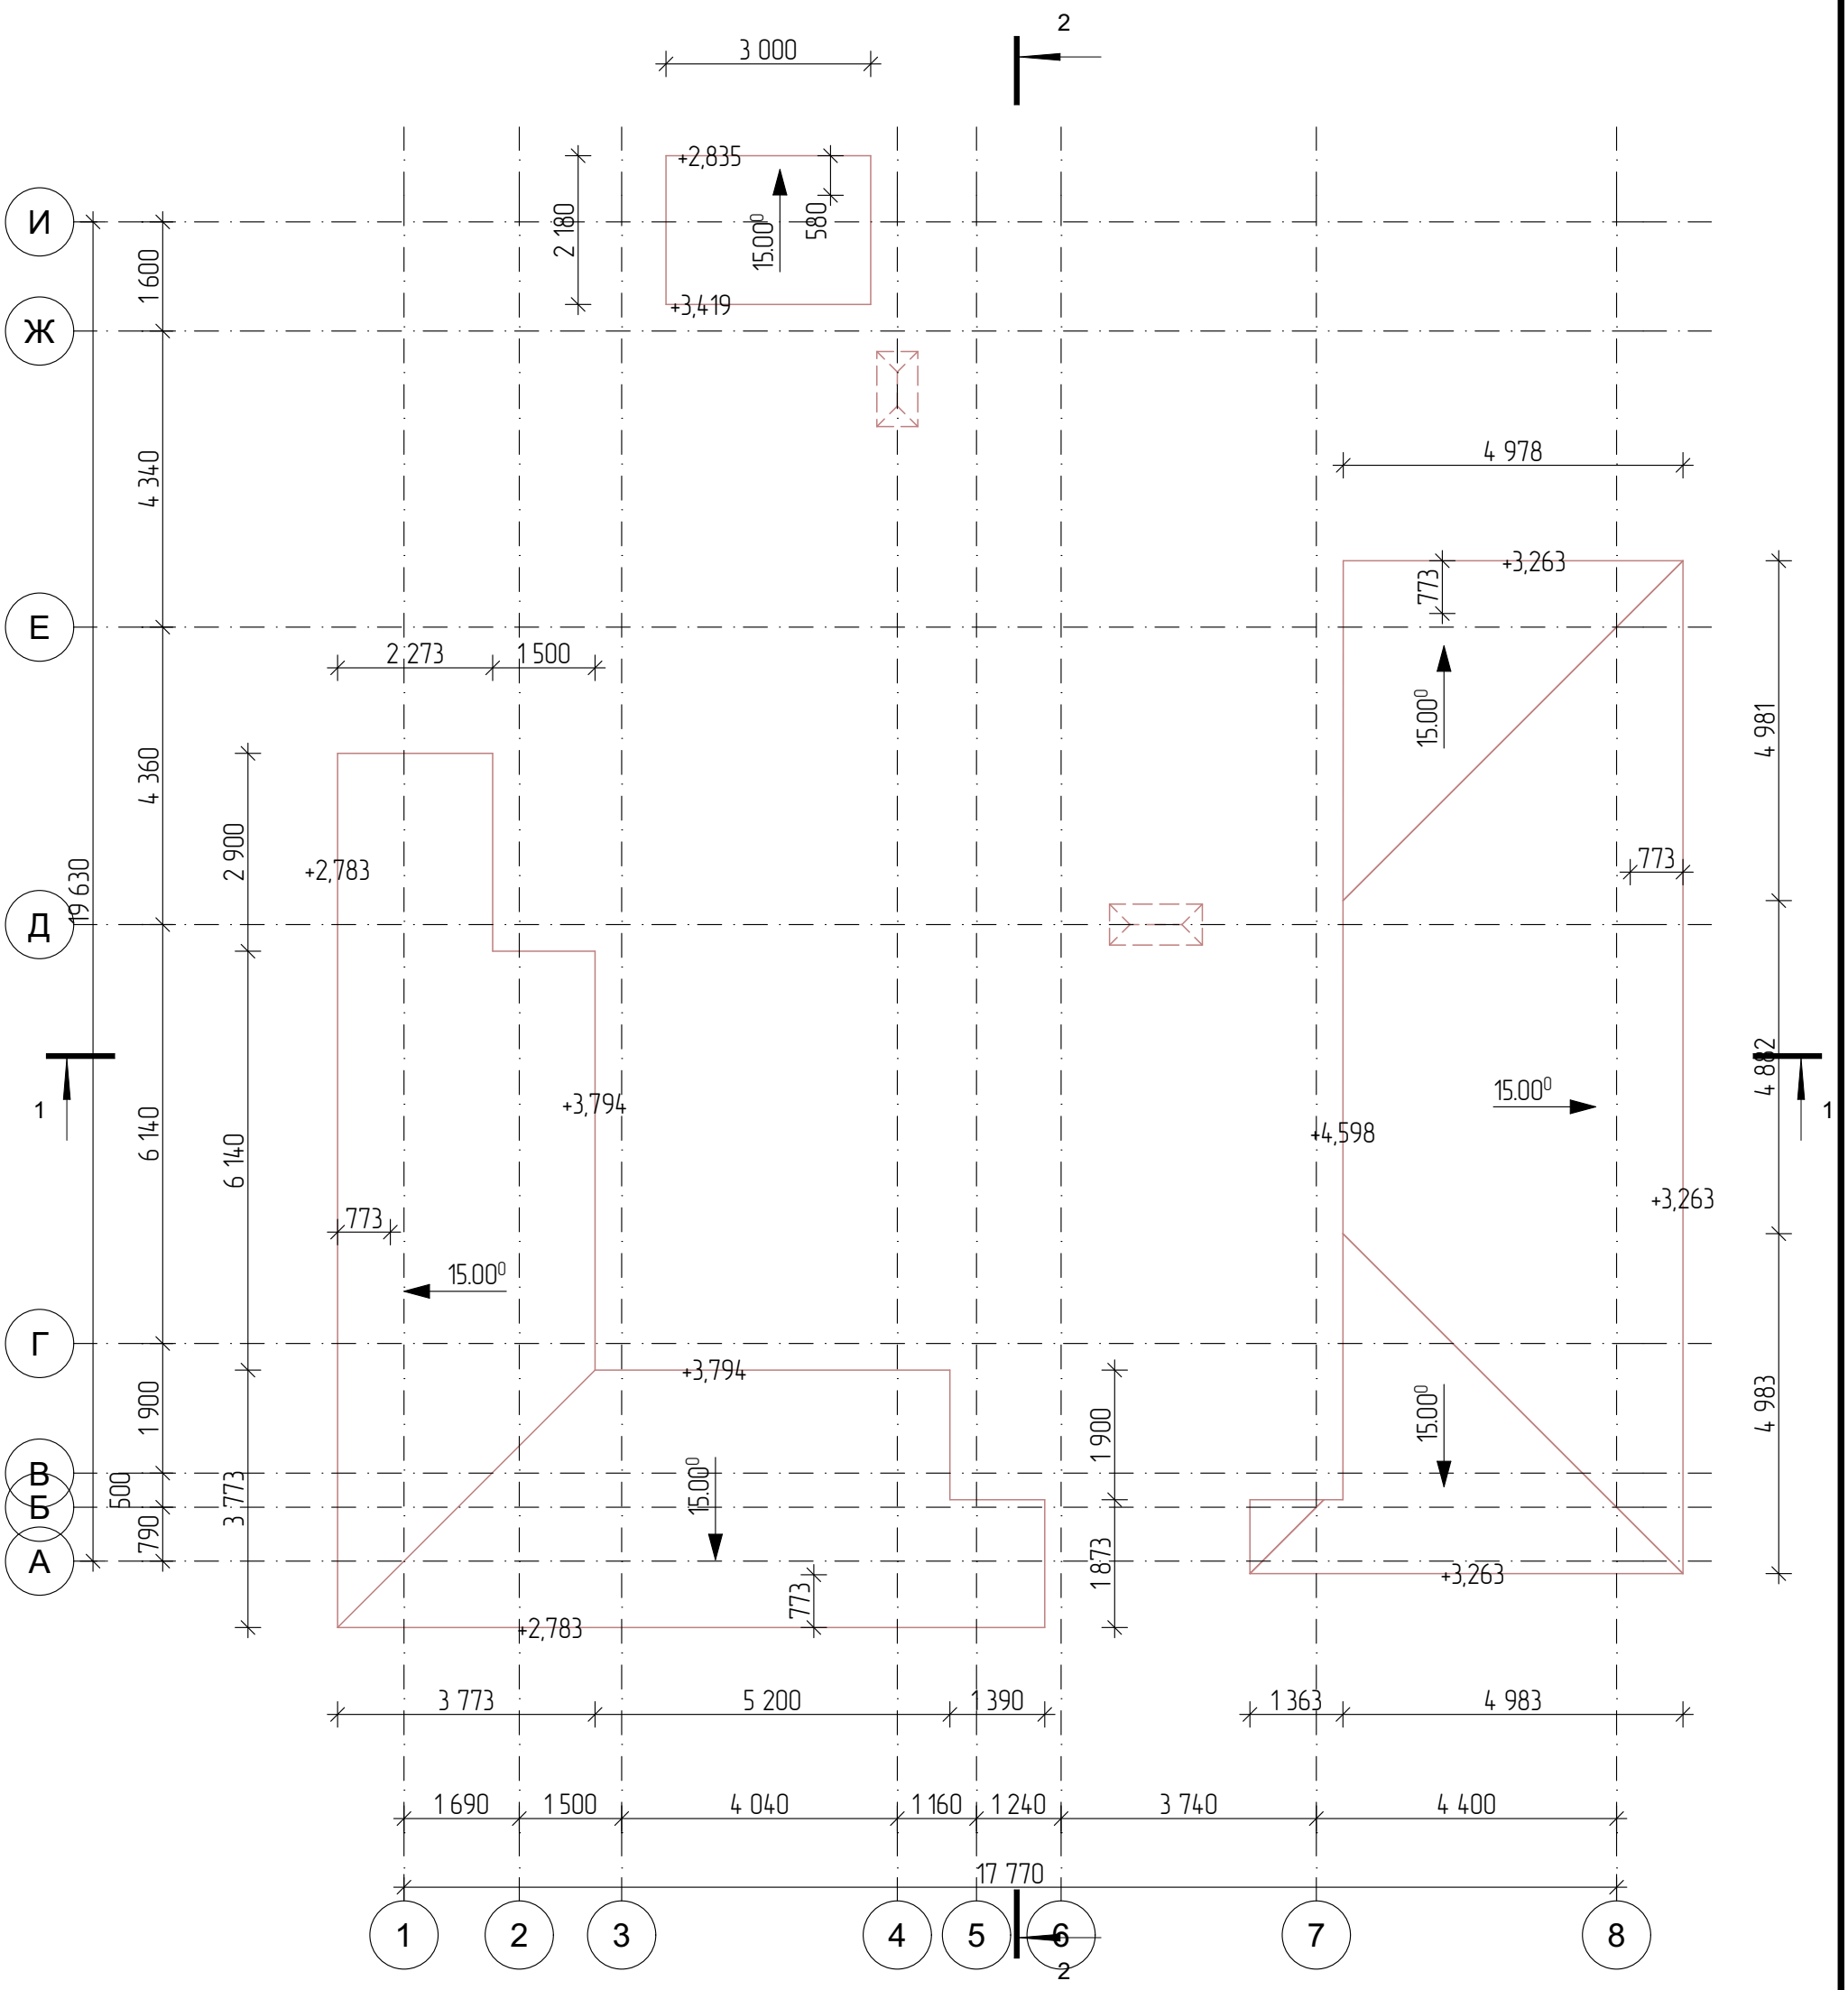

						#ID Проекта	
						кадастровый номер Россия	
Изм.	Кол.уч.	Лист	№Док.	Подп.	Дата		
Разраб.						Индивидуальный жилой дом	Стадия: #Стадия Проекта; Лист: 58; Листов:
ГАП							
План кровли первого этажа							

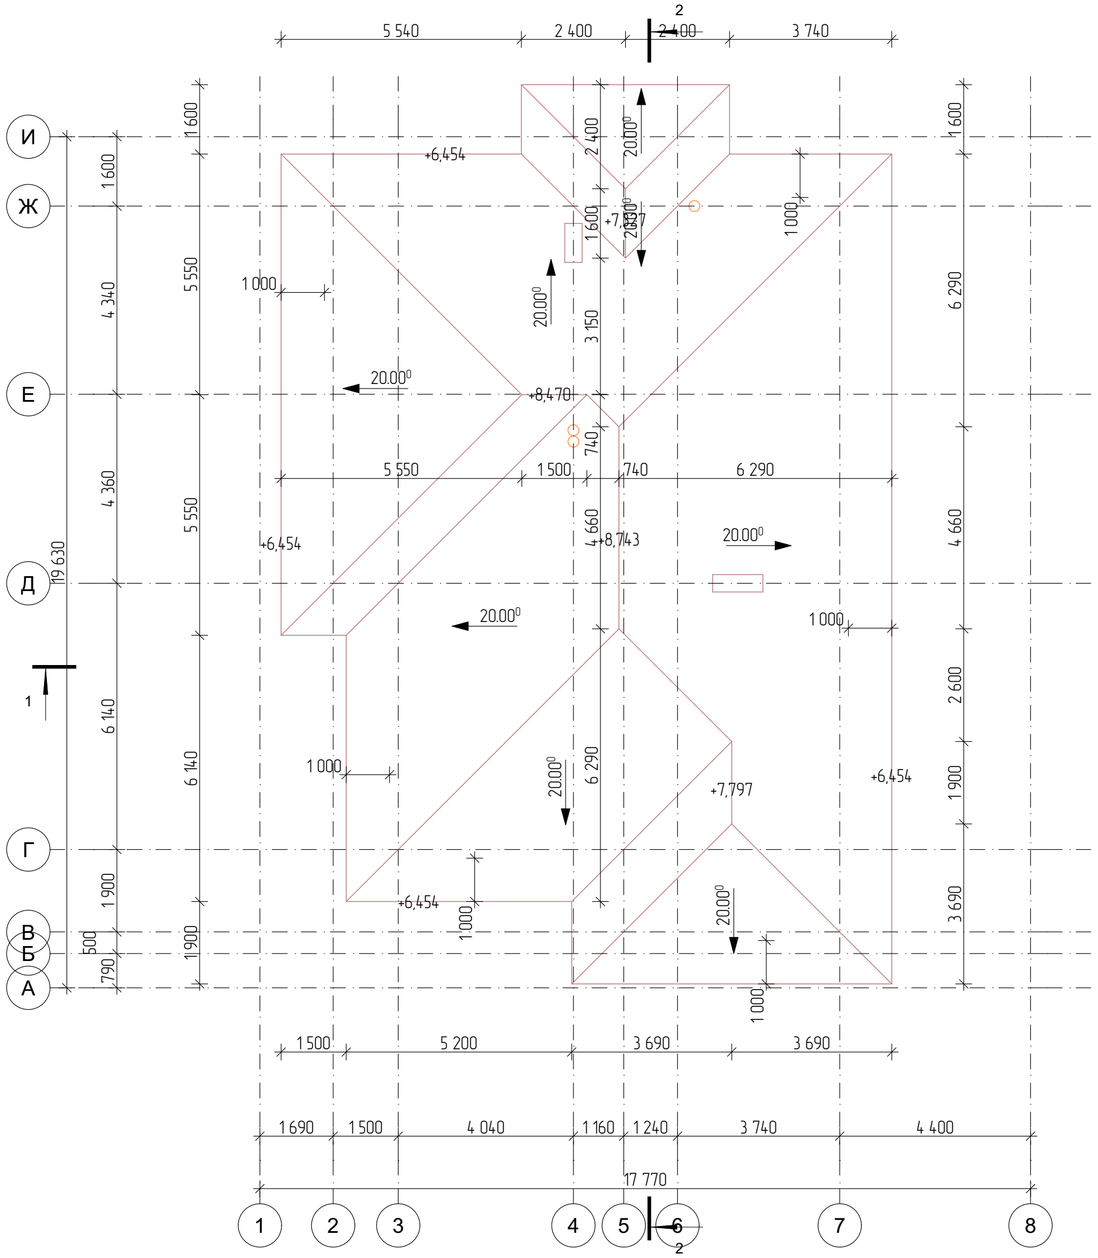

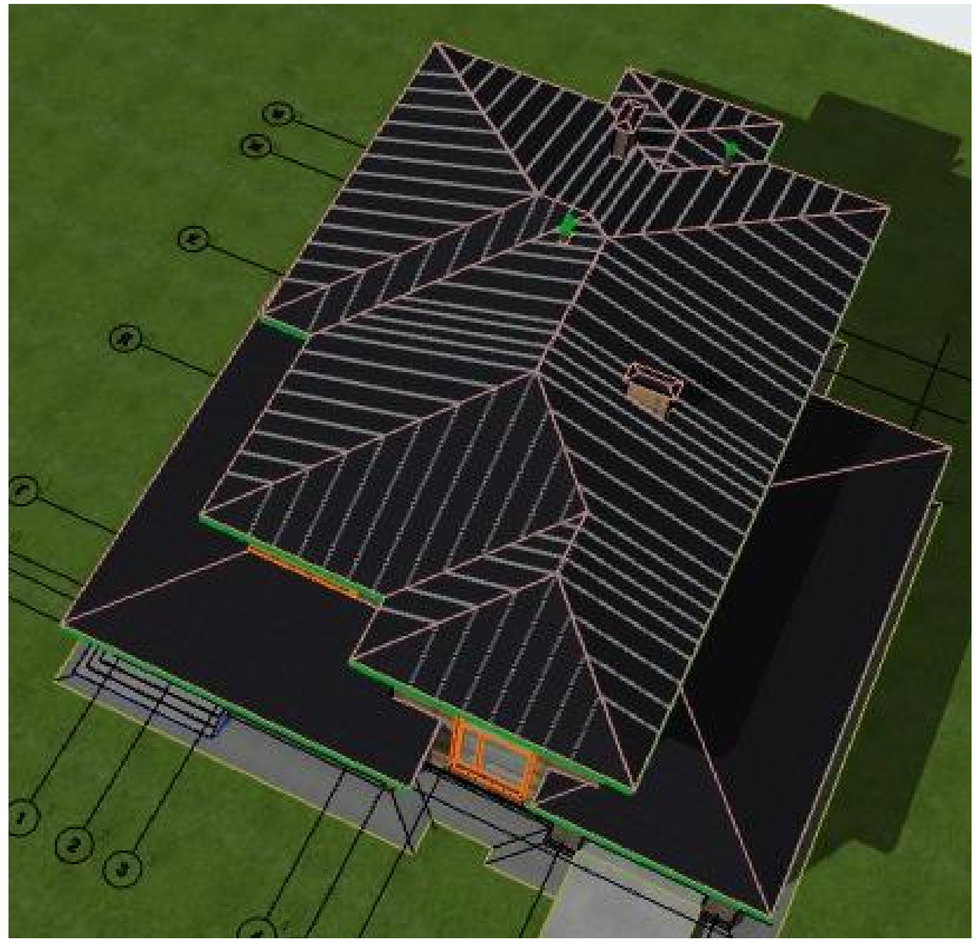

						#ID Проекта	
						кадастровый номер Россия	
Изм.	Кол.уч.	Лист	№Док.	Подп.	Дата		
Разраб.						Индивидуальный жилой дом	Стадия: #Стадия Проекта; Лист: 59; Листов:
ГАП							
План кровли на отм. 6,454							

Состав кровли		
Элемент	Наименование	Площадь, м2
Кровля гаража		
	Мембрана - Водонепроницаемая	78,11
	Черепица - Черепица	78,35
	Шаговая обрешетка 25*250	78,28
Кровля дома		
	Мембрана - Водонепроницаемая	270,62
	ОБЩИЙ - КОНСТРУКТИВНЫЙ	1,60
	Черепица - Черепица	271,85
	Шаговая обрешетка 25*250	271,47
Кровля крыльца		
	Мембрана - Водонепроницаемая	6,77
	Черепица - Черепица	6,80
	Шаговая обрешетка 25*250	6,79
Кровля террасы		
	Мембрана - Водонепроницаемая	68,56
	Черепица - Черепица	68,77
	Шаговая обрешетка 25*250	68,71

Стропильная система		
Уровень	**Наименование**	Объем, м3
2-й этаж		
		0,00
	Коньковый брус 200x100	1,07
	Лобовая доска 200x25	0,27
	Мауэрлат 100x200	0,41
	Подшивка кровли - вертикальный эле...	0,00
	Подшивная доска 100x25	0,00
	Стропильная нога 200x50	2,35
Кровля		
		0,00
	Контрбрус 50x50	1,13
	Коньковый брус 200x100	1,74
	Лобовая доска 200x25	0,37
	Мауэрлат 100x200	1,16
	Подшивка кровли - вертикальный эле...	0,00
	Подшивная доска 100x25	0,00
	Стропильная нога 200x50	4,08
		12,58 м³

Ведомость кровельного материала	
Наименование	Площадь, м2
Кровля гаража	78,10
Кровля дома	273,23
Кровля крыльца	6,77
Кровля террасы	68,56
	426,66 м²

ВЕДОМОСТЬ НА УТЕПЛИТЕЛЬ (кровля)				
	Наименование	Компоненты		
		Толщина, мм	Объем, м3	Площадь, м2
Кровля				
	Изоляция - Минеральная Мягкая	200	31,19	162,06

							#ID Проекта
							кадастровый номер Россия
Изм.	Кол.уч.	Лист	№Док.	Подп.	Дата		
						Индивидуальный жилой дом	Стадия: #Стадия Проекта; Лист: 60; Листов:
Разраб.							
ГАП							
						Ведомость кровельного пирога	

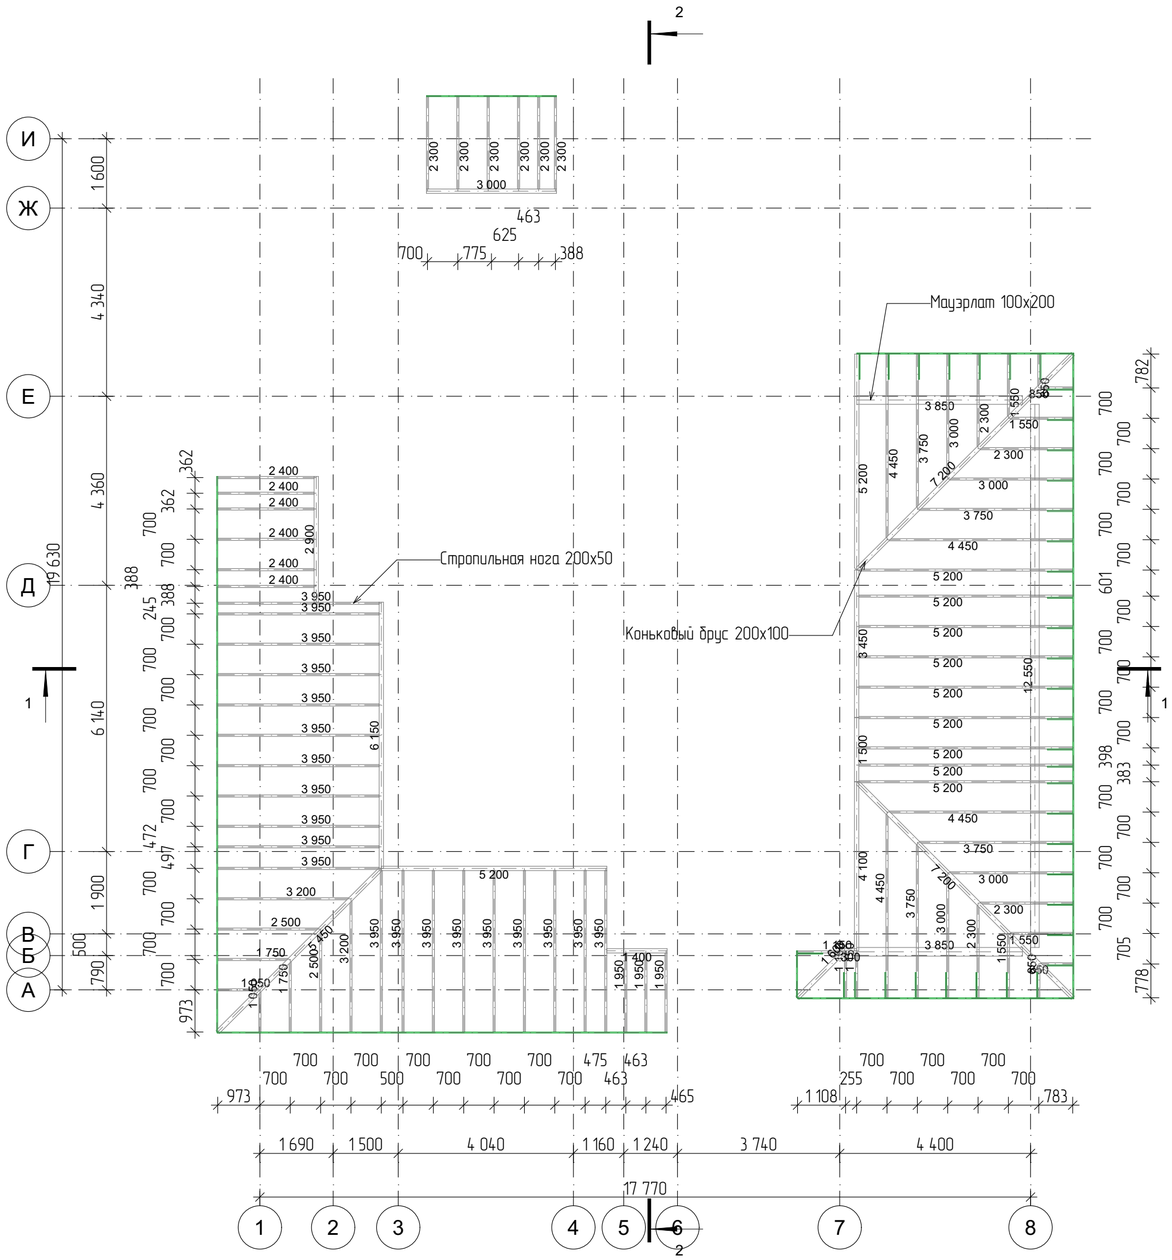
Мауэрлат 100х200
Стропильная нога 200х50
Коньковый брус 200х100
1
2
А
Б
В
Г
Д
Е
Ж
И
1 2 3 4 5 6 7 8
17 770
1 690
1 500
4 040
1 160
1 240
3 740
4 400
973
700
700
700
700
700
475
463
700
700
500
700
700
700
463
465
1 108
255
700
700
700
700
783
19 630
4 340
4 360
6 140
1 900
500
790
1600
362
362
700
700
388
245
700
700
700
700
700

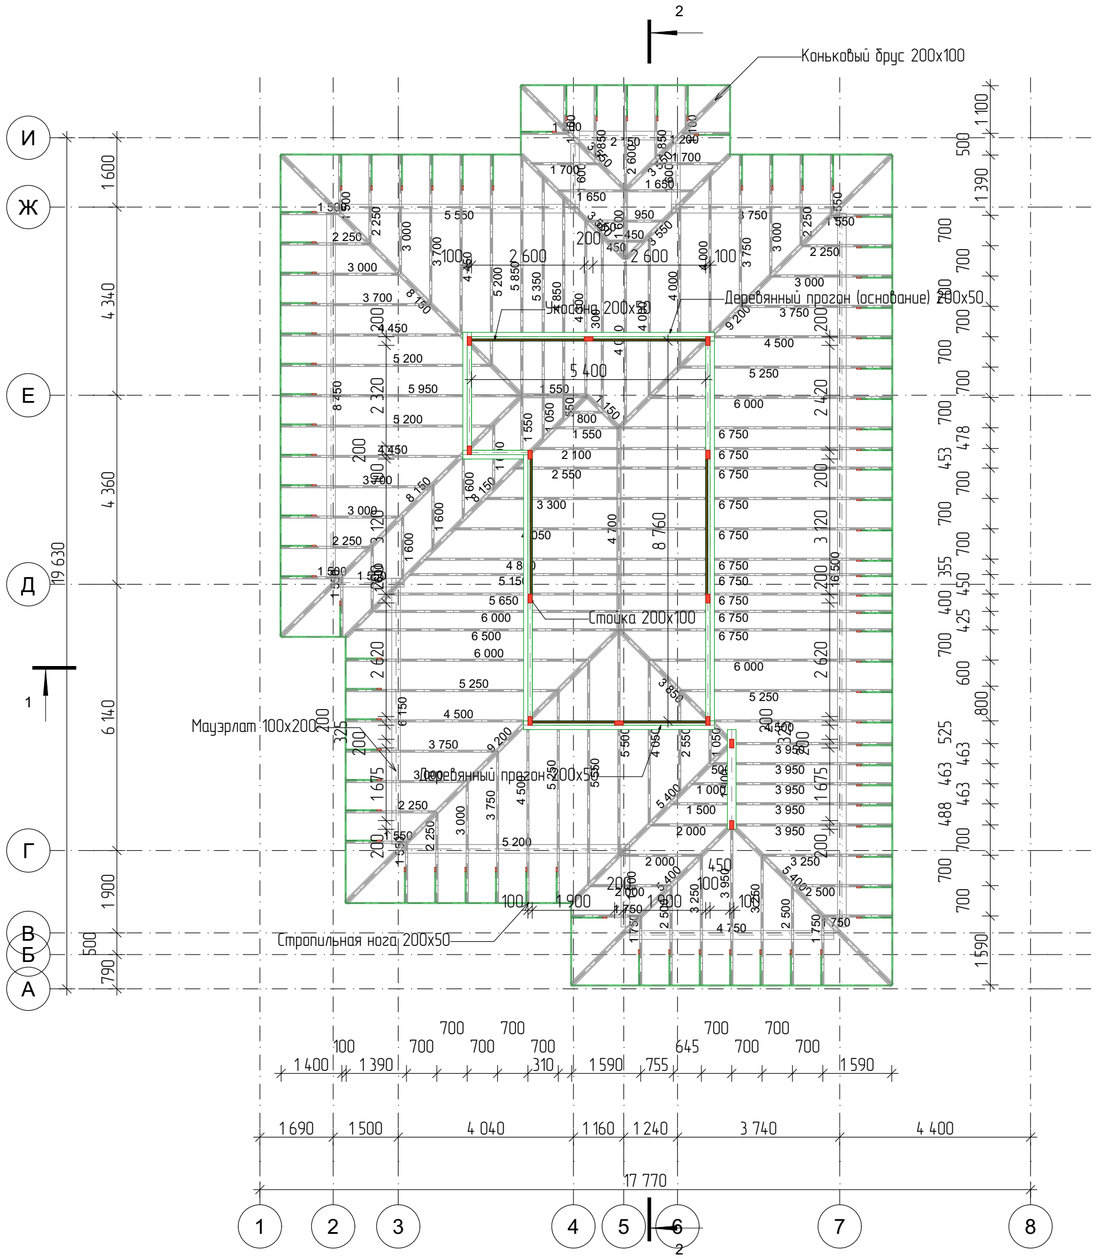

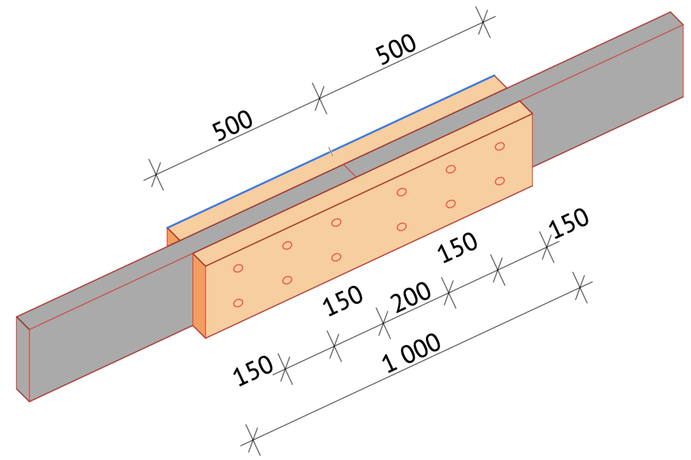

Стропильная система		
Кровля	**Наименование**	Объем, м3
Кровля		0,00
Кровля	Контрбрус 50х50	1,13
Кровля	Коньковый брус 200х100	1,74
Кровля	Лобовая доска 200х25	0,37
Кровля	Мауэрлат 100х200	1,16
Кровля	Подшивка кровли - вертикальный элемент	0,00
Кровля	Подшивная доска 100х25	0,00
Кровля	Стропильная нога 200х50	4,08
		8,48 м³

						#ID Проекта		
						кадастровый номер Россия		
Изм.	Кол.уч.	Лист	№Док.	Подп.	Дата			
Разраб.						Индивидуальный жилой дом	Стадия: #Стадия Проекта	Лист: 62 / Листов:
ГАП								
Схема расположения стропил на отм. 6,454								

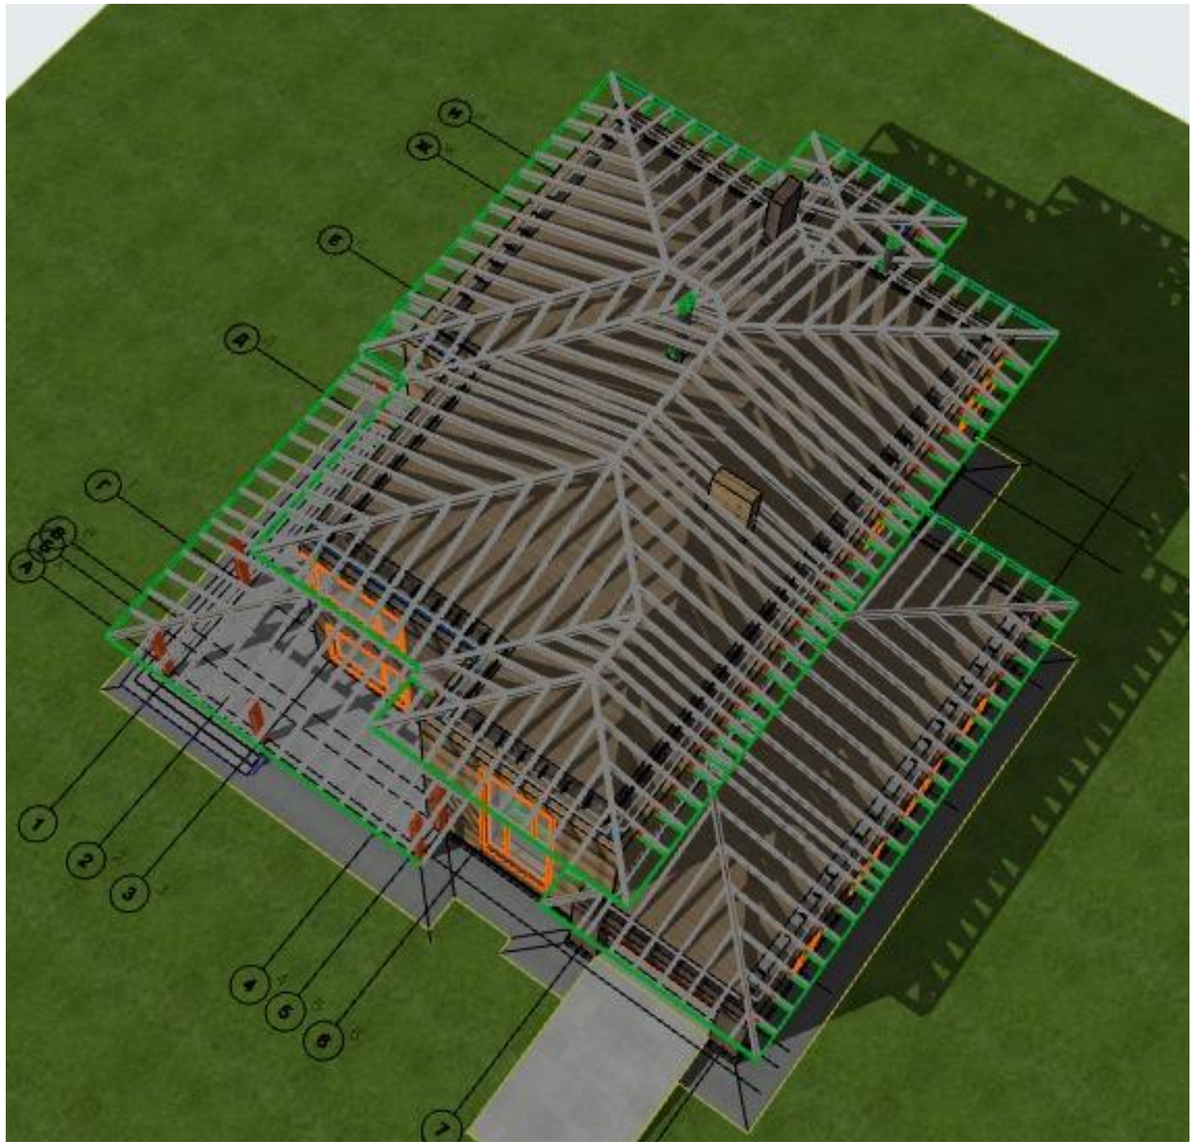

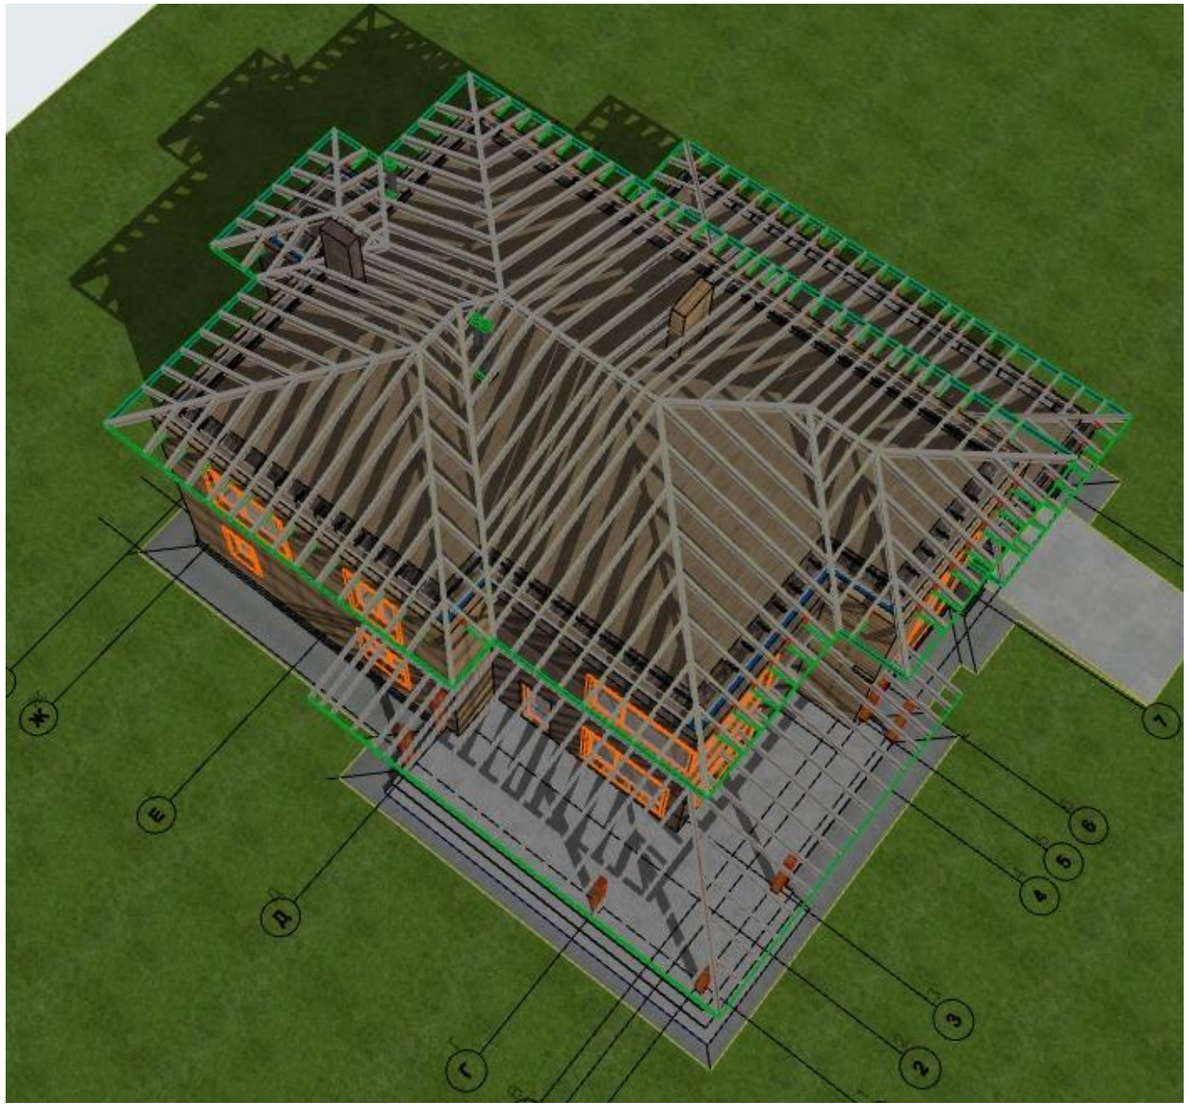

						#ID Проекта
						кадастровый номер Россия
Изм.	Кол.уч.	Лист	№Док.	Подп.	Дата	
Разраб.						Индивидуальный жилой дом
ГАП						

Стадия	Лист	Листов
#Стадия Проекта	63	

3Д Вид стропильной системы

ИКК-03 Стропильная система

Наименование	Округленный Размер Пиломатериала	Длина, мм	Кол-во	Объем, м3
	---	---	117	0,00
Контрбрус 50х50				
	400	317	2	0,00
	450	392	1	0,00
	500	440	1	0,00
	750	674	1	0,00
	850	779	2	0,00
	950	854	1	0,00
	1 000	909	1	0,00
	1 000	910	1	0,00
	1 050	964	2	0,00
	1 100	1 047	1	0,00
	1 150	1 054	2	0,00
	1 450	1 304	3	0,00
	1 450	1 317	1	0,00
	1 450	1 344	4	0,00
	1 500	1 355	1	0,00
	1 500	1 380	1	0,00
	1 500	1 384	1	0,00
	1 550	1 409	5	0,00
	1 550	1 500	1	0,00
	1 600	1 479	2	0,00

ИКК-03 Стропильная система

Наименование	Округленный Размер Пиломатериала	Длина, мм	Кол-во	Объем, м3
	1 600	1 600	1	0,00
	1 650	1 509	2	0,00
	1 700	1 544	4	0,00
	1 800	1 654	2	0,00
	1 900	1 900	1	0,00
	1 950	1 779	1	0,00
	1 950	1 809	2	0,00
	2 000	1 862	1	0,00
	2 200	2 004	3	0,03
	2 200	2 044	4	0,04
	2 450	2 244	3	0,03
	2 500	2 309	1	0,01
	2 500	2 314	1	0,01
	2 500	2 329	1	0,01
	2 900	2 704	3	0,03
	2 950	2 744	4	0,04
	3 200	2 944	3	0,03
	3 250	3 014	1	0,01
	3 550	3 394	4	0,04
	3 650	3 404	3	0,03
	3 700	3 444	4	0,04

ИКК-03 Стропильная система

Наименование	Округленный Размер Пиломатериала	Длина, мм	Кол-во	Объем, м3
	3 850	3 677	1	0,01
	3 900	3 619	1	0,01
	3 900	3 640	5	0,05
	3 950	3 649	4	0,04
	4 000	3 709	1	0,01
	4 000	3 714	1	0,01
	4 250	3 948	1	0,01
	4 250	3 969	1	0,01
	4 400	4 104	3	0,03
	4 450	4 144	4	0,04
	4 700	4 660	1	0,01
	4 750	4 414	1	0,01
	4 800	4 479	1	0,01
	5 100	4 769	1	0,01
	5 150	4 804	3	0,03
	5 200	4 844	4	0,04
	5 300	4 949	1	0,01
	5 400	5 218	3	0,03
	5 450	5 084	1	0,01
	5 500	5 109	1	0,01
	5 600	5 219	1	0,01

ИКК-03 Стропильная система

Наименование	Округленный Размер Пиломатериала	Длина, мм	Кол-во	Объем, м3
	5 800	5 419	1	0,01
	5 850	5 479	1	0,01
	5 950	5 544	3	0,03
	5 950	5 567	1	0,01
	6 450	6 019	1	0,02
	6 700	6 240	10	0,20
	8 150	7 849	3	0,06
	9 200	8 895	2	0,04
Коньковый брус 200х100				
	1 150	1 047	1	0,02
	1 400	1 390	1	0,03
	1 500	1 480	1	0,03
	1 550	1 500	1	0,03
	1 600	1 532	1	0,03
	1 600	1 600	1	0,03
	1 900	1 900	1	0,04
	2 900	2 900	1	0,06
	3 000	3 000	1	0,06
	3 450	3 401	1	0,07
	3 550	3 394	4	0,28
	3 850	3 677	1	0,08
	4 100	3 900	1	0,08

ИКК-03 Стропильная система

Наименование	Округленный Размер Пиломатериала	Длина, мм	Кол-во	Объем, м3
	4 700	4 660	1	0,09
	5 200	4 981	1	0,10
	5 200	5 200	1	0,10
	5 400	5 218	3	0,33
	5 450	5 336	1	0,11
	6 150	6 140	1	0,12
	7 200	7 046	1	0,14
	7 200	7 047	1	0,14
	8 150	7 849	3	0,48
	9 200	8 895	2	0,36
Лобовая доска 200х25				
	---	1 083	1	0,01
	---	1 500	1	0,01
	---	1 587	2	0,02
	---	1 913	1	0,01
	---	3 000	1	0,02
	---	3 740	1	0,02
	---	4 812	1	0,02
	---	5 003	1	0,03
	---	5 200	1	0,03
	---	5 552	1	0,03
	---	6 140	1	0,03

ИКК-03 Стропильная система

Наименование	Округленный Размер Пиломатериала	Длина, мм	Кол-во	Объем, м3
	---	6 371	1	0,03
	---	7 380	1	0,04
	---	10 376	1	0,05
	---	11 100	1	0,06
	---	12 813	1	0,06
	---	14 846	1	0,07
	---	19 140	1	0,10
Мауэрлат 100х200				
	1 550	1 500	1	0,03
	1 600	1 600	2	0,06
	1 900	1 900	1	0,04
	2 150	2 125	1	0,04
	3 750	3 740	1	0,07
	3 850	3 820	1	0,08
	3 850	3 823	1	0,08
	4 750	4 705	1	0,09
	5 200	5 200	1	0,10
	5 550	5 540	1	0,11
	6 150	6 140	1	0,12
	8 450	8 425	1	0,17
	12 550	12 527	1	0,25
	16 500	16 465	1	0,33
Поршивка кровли - вертикальный элемент				

ИКК-03 Стропильная система

Наименование	Округленный Размер Пиломатериала	Длина, мм	Кол-во	Объем, м3
	---	---	117	0,00
Подшивная доска 100х25				
	---	583	37	0,00
	---	810	80	0,00
Стропильная нога 200х50				
	300	280	1	0,01
	450	317	2	0,00
	500	392	1	0,00
	550	440	1	0,00
	800	674	1	0,01
	850	736	1	0,01
	850	736	1	0,01
	850	737	2	0,02
	950	779	2	0,02
	1 000	854	1	0,01
	1 050	909	1	0,01
	1 050	910	1	0,01
	1 050	927	2	0,02
	1 100	964	2	0,02
	1 150	1 012	1	0,01
	1 150	1 033	2	0,02
	1 200	1 054	2	0,02
	1 500	1 304	3	0,03

ИКК-03 Стропильная система

Наименование	Округленный Размер Пиломатериала	Длина, мм	Кол-во	Объем, м3
	1 500	1 317	1	0,01
	1 550	1 344	4	0,04
	1 550	1 355	1	0,01
	1 550	1 380	1	0,01
	1 550	1 384	1	0,01
	1 550	1 436	1	0,01
	1 550	1 436	1	0,01
	1 550	1 437	2	0,02
	1 600	1 409	5	0,05
	1 650	1 479	2	0,04
	1 700	1 509	2	0,04
	1 750	1 544	4	0,08
	1 750	1 627	2	0,04
	1 850	1 654	2	0,04
	1 950	1 823	3	0,06
	2 000	1 779	1	0,02
	2 000	1 809	2	0,04
	2 100	1 862	1	0,02
	2 250	2 004	3	0,06
	2 250	2 044	4	0,08
	2 300	2 139	6	0,12

ИКК-03 Стропильная система

Наименование	Округленный Размер Пиломатериала	Длина, мм	Кол-во	Объем, м3
	2 300	2 136	1	0,02
	2 300	2 136	1	0,02
	2 300	2 137	2	0,04
	2 400	2 223	6	0,12
	2 500	2 244	3	0,06
	2 500	2 327	2	0,04
	2 550	2 309	1	0,02
	2 550	2 314	1	0,02
	2 600	2 329	1	0,02
	3 000	2 704	3	0,09
	3 000	2 744	4	0,12
	3 000	2 836	1	0,03
	3 000	2 836	1	0,03
	3 000	2 837	2	0,06
	3 200	3 027	2	0,06
	3 250	2 944	3	0,09
	3 300	3 014	1	0,03
	3 700	3 404	3	0,12
	3 750	3 444	4	0,16
	3 750	3 536	6	0,24

ИКК-03 Стропильная система

Наименование	Округленный Размер Пиломатериала	Длина, мм	Кол-во	Объем, м3
	3 750	3 537	2	0,08
	3 950	3 619	1	0,04
	3 950	3 640	5	0,20
	3 950	3 723	20	0,80
	4 000	3 649	4	0,16
	4 050	3 709	1	0,04
	4 050	3 714	1	0,04
	4 300	3 948	1	0,04
	4 300	3 969	1	0,04
	4 450	4 104	3	0,12
	4 450	4 236	1	0,04
	4 450	4 236	1	0,04
	4 450	4 237	2	0,08
	4 500	4 144	4	0,16
	4 800	4 414	1	0,05
	4 850	4 479	1	0,05
	5 150	4 769	1	0,05
	5 200	4 804	3	0,15
	5 200	4 932	1	0,05
	5 200	4 932	1	0,05

ИКК-03 Стропильная система

Наименование	Округленный Размер Пиломатериала	Длина, мм	Кол-во	Объем, м3
	5 200	4 932	1	0,05
	5 200	4 932	1	0,05
	5 200	4 933	4	0,20
	5 250	4 844	4	0,20
	5 350	4 949	1	0,05
	5 500	5 084	1	0,05
	5 550	5 109	1	0,05
	5 650	5 219	1	0,06
	5 850	5 419	1	0,06
	5 950	5 479	1	0,06
	6 000	5 544	3	0,18
	6 000	5 567	1	0,06
	6 500	6 019	1	0,06
	6 750	6 240	10	0,70
				12,58 м³

Изм.	Кол.уч.	Лист	№Док.	Подп.	Дата
Разраб.					
ГАП					

#ID Проекта

кадастровый номер Россия

Индивидуальный жилой дом

Стадия	Лист	Листов
#Стадия Проекта	64	

Ведомость материалов (стропильная система)

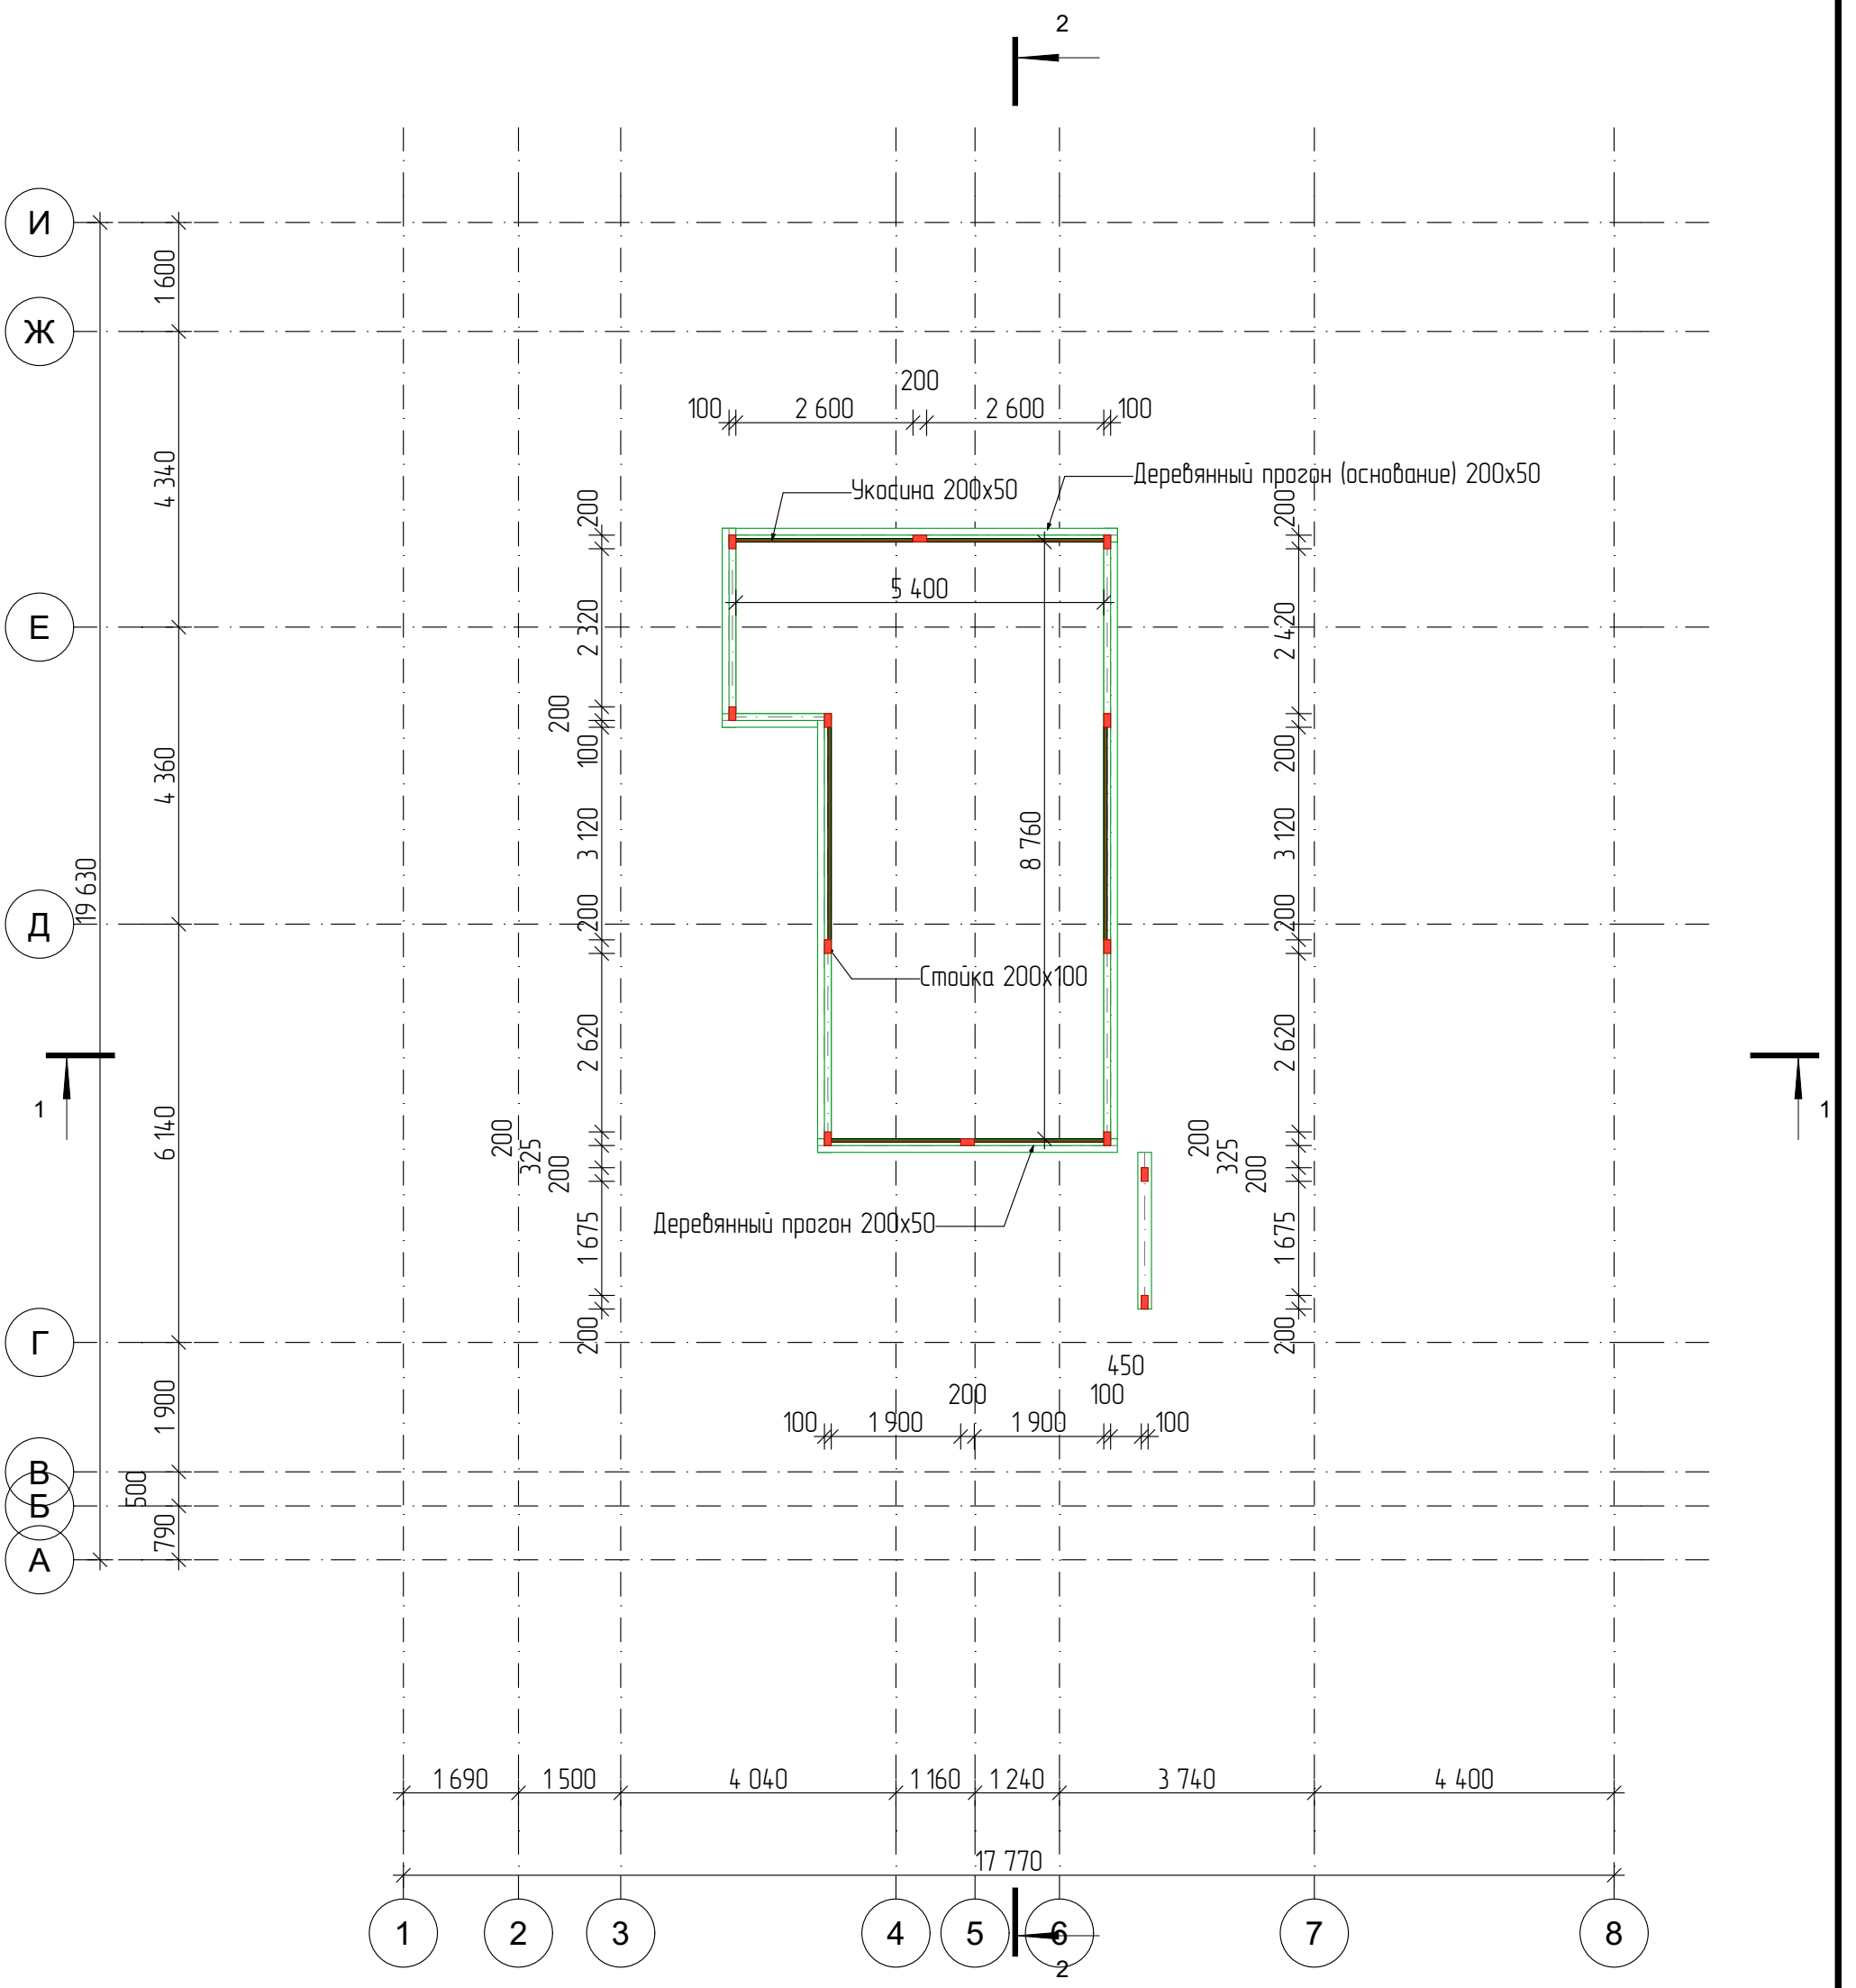

						#ID Проекта	
						кадастровый номер Россия	
Изм.	Кол.уч.	Лист	№Док.	Подп.	Дата		
Разраб.						Индивидуальный жилой дом	Стадия: #Стадия Проекта; Лист: 66; Листов:
ГАП							
Силовой каркас кровли							

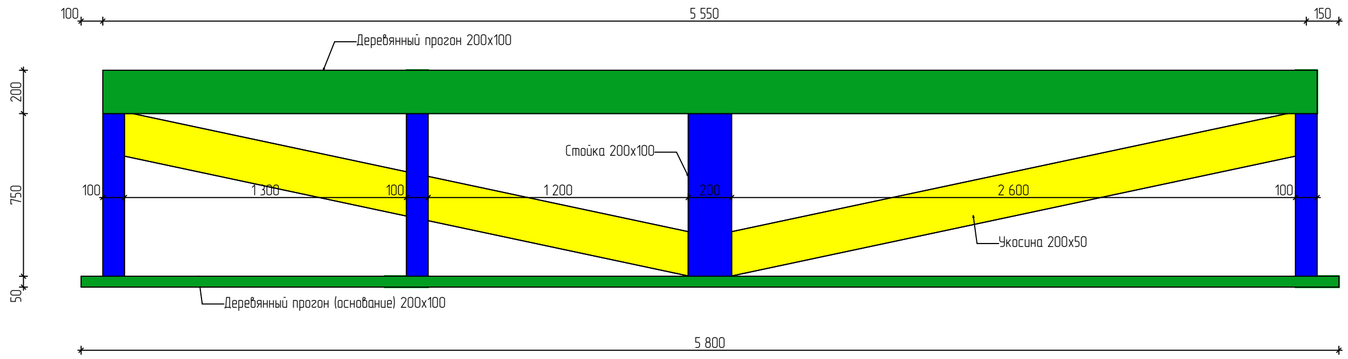

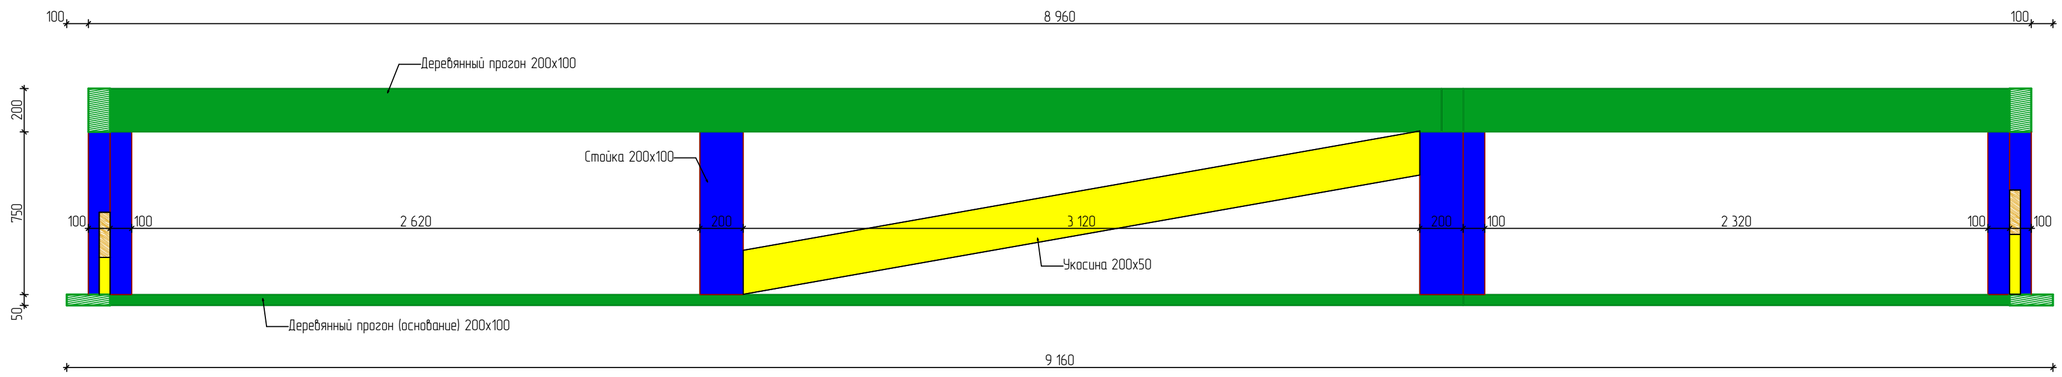

						#ID Проекта	
						кадастровый номер Россия	
Изм.	Колуч.	Лист	№Док.	Подп.	Дата		
Разраб.						Индивидуальный жилой дом	Стадия: #Стадия Проекта; Лист: 67; Листов:
ГАП							
Силовой каркас вид сбоку							

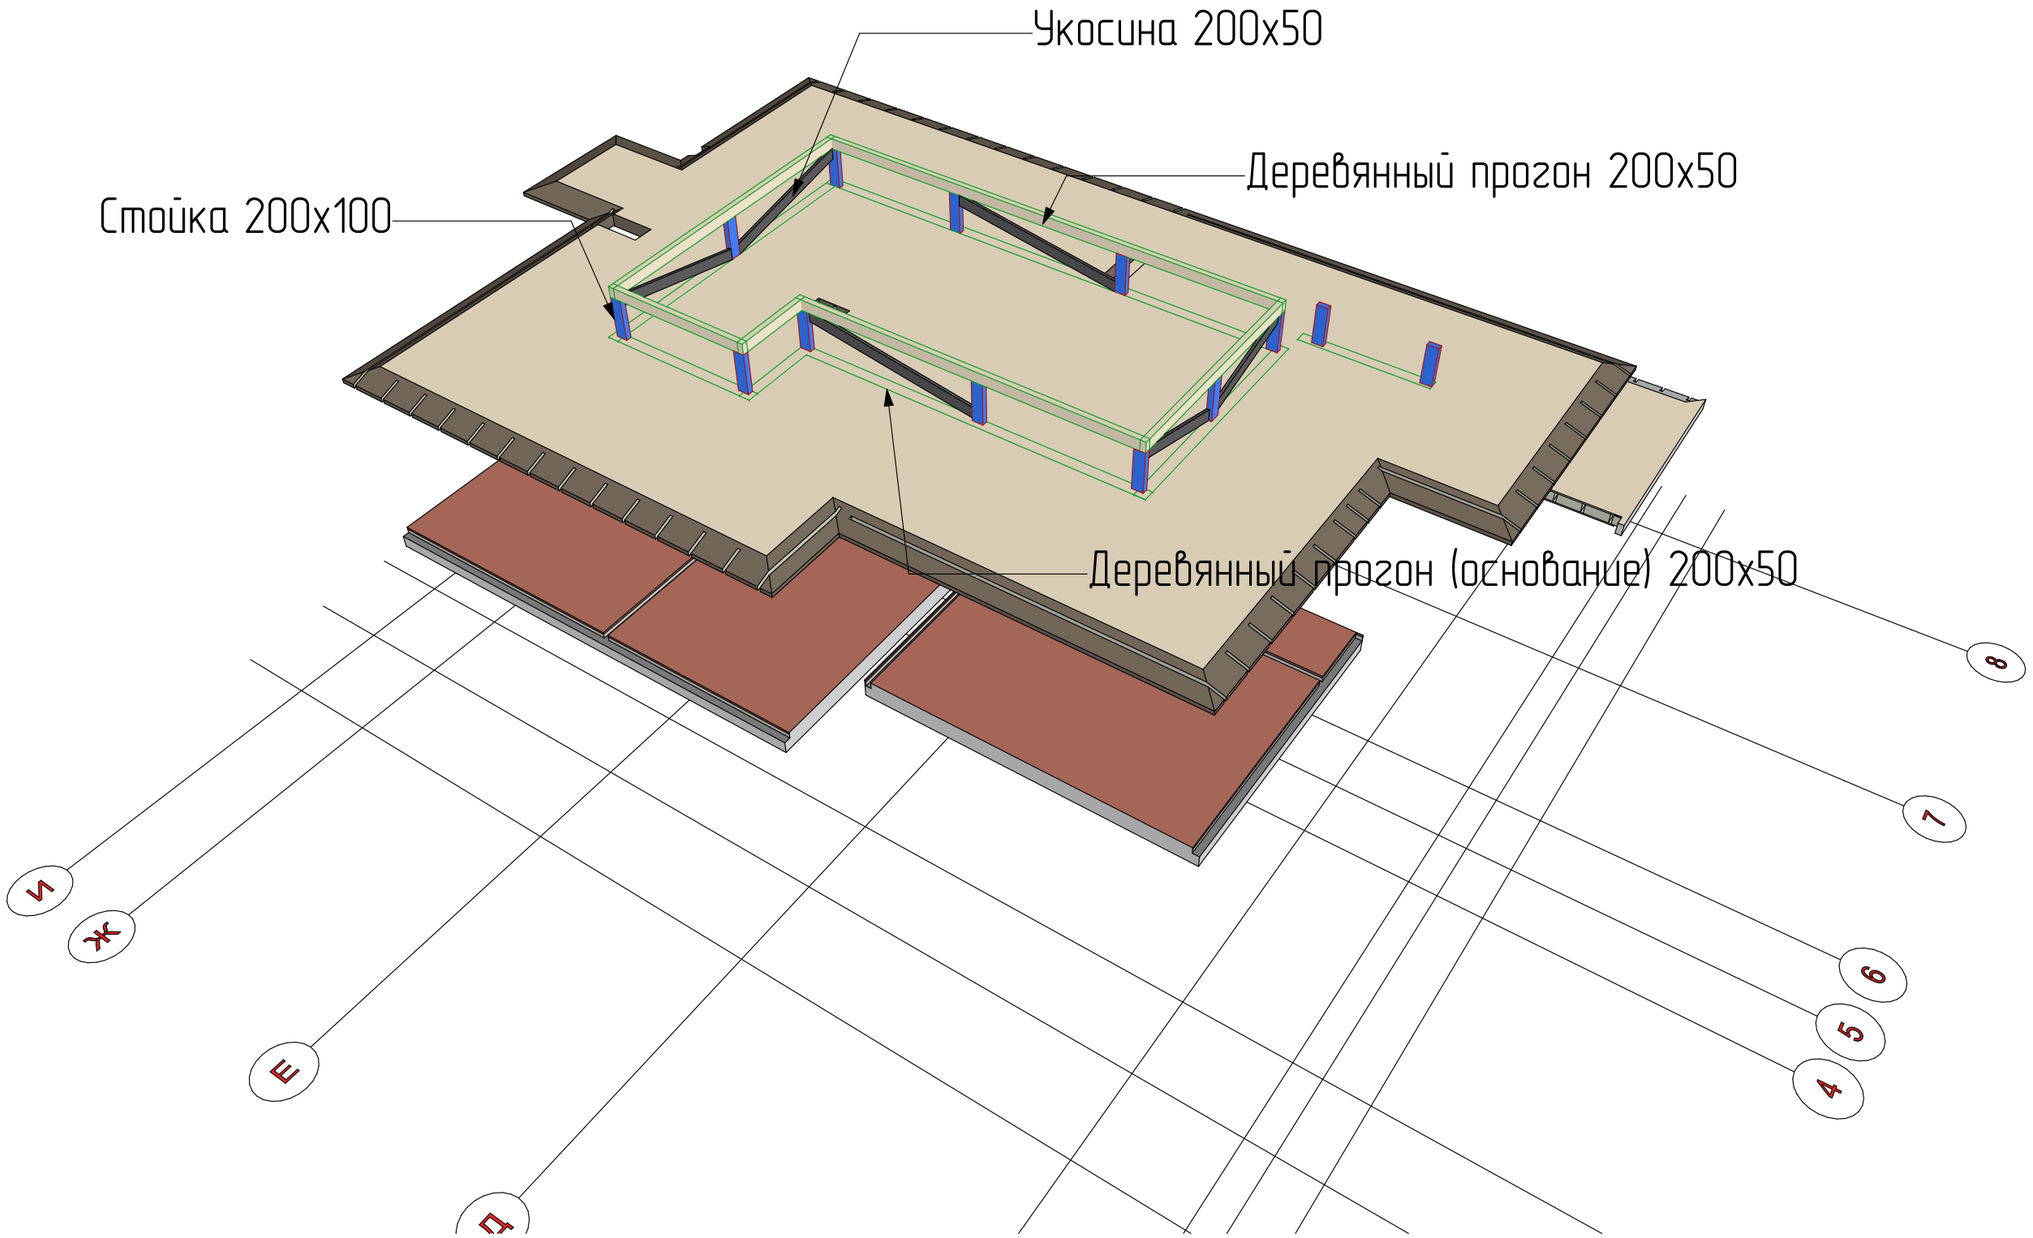

						#ID Проекта
						кадастровый номер Россия
Изм.	Кол.уч.	Лист	№Док.	Подп.	Дата	
Разраб.						Индивидуальный жилой дом
ГАП						
						Стадия: #Стадия Проекта
						Лист: 68
						Листов:
3Д вид каркаса кровли						

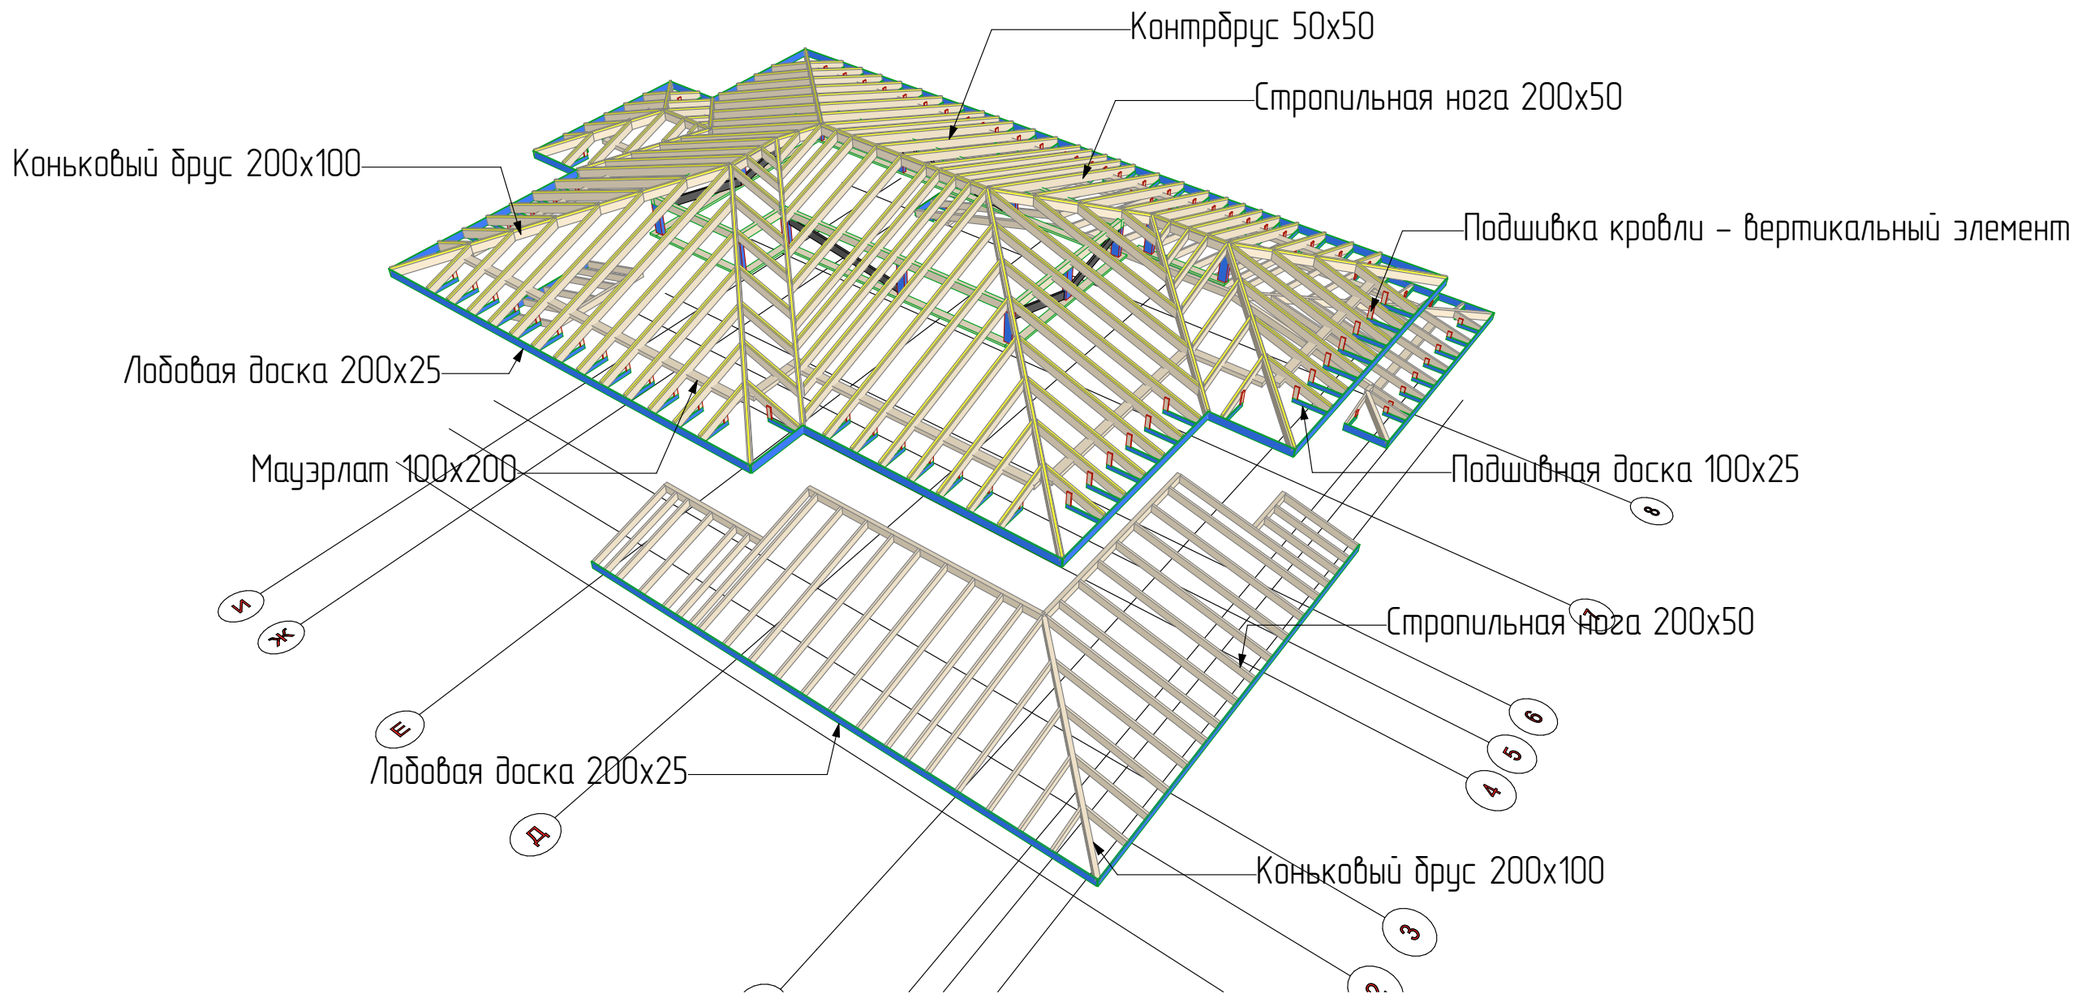

						#ID Проекта		
						кадастровый номер Россия		
Изм.	Кол.уч.	Лист	№Док.	Подп.	Дата			
Разраб.						Индивидуальный жилой дом	Стадия	Лист	Листов
ГАП							#Стадия Проекта	69	
3Д узлы кровли									

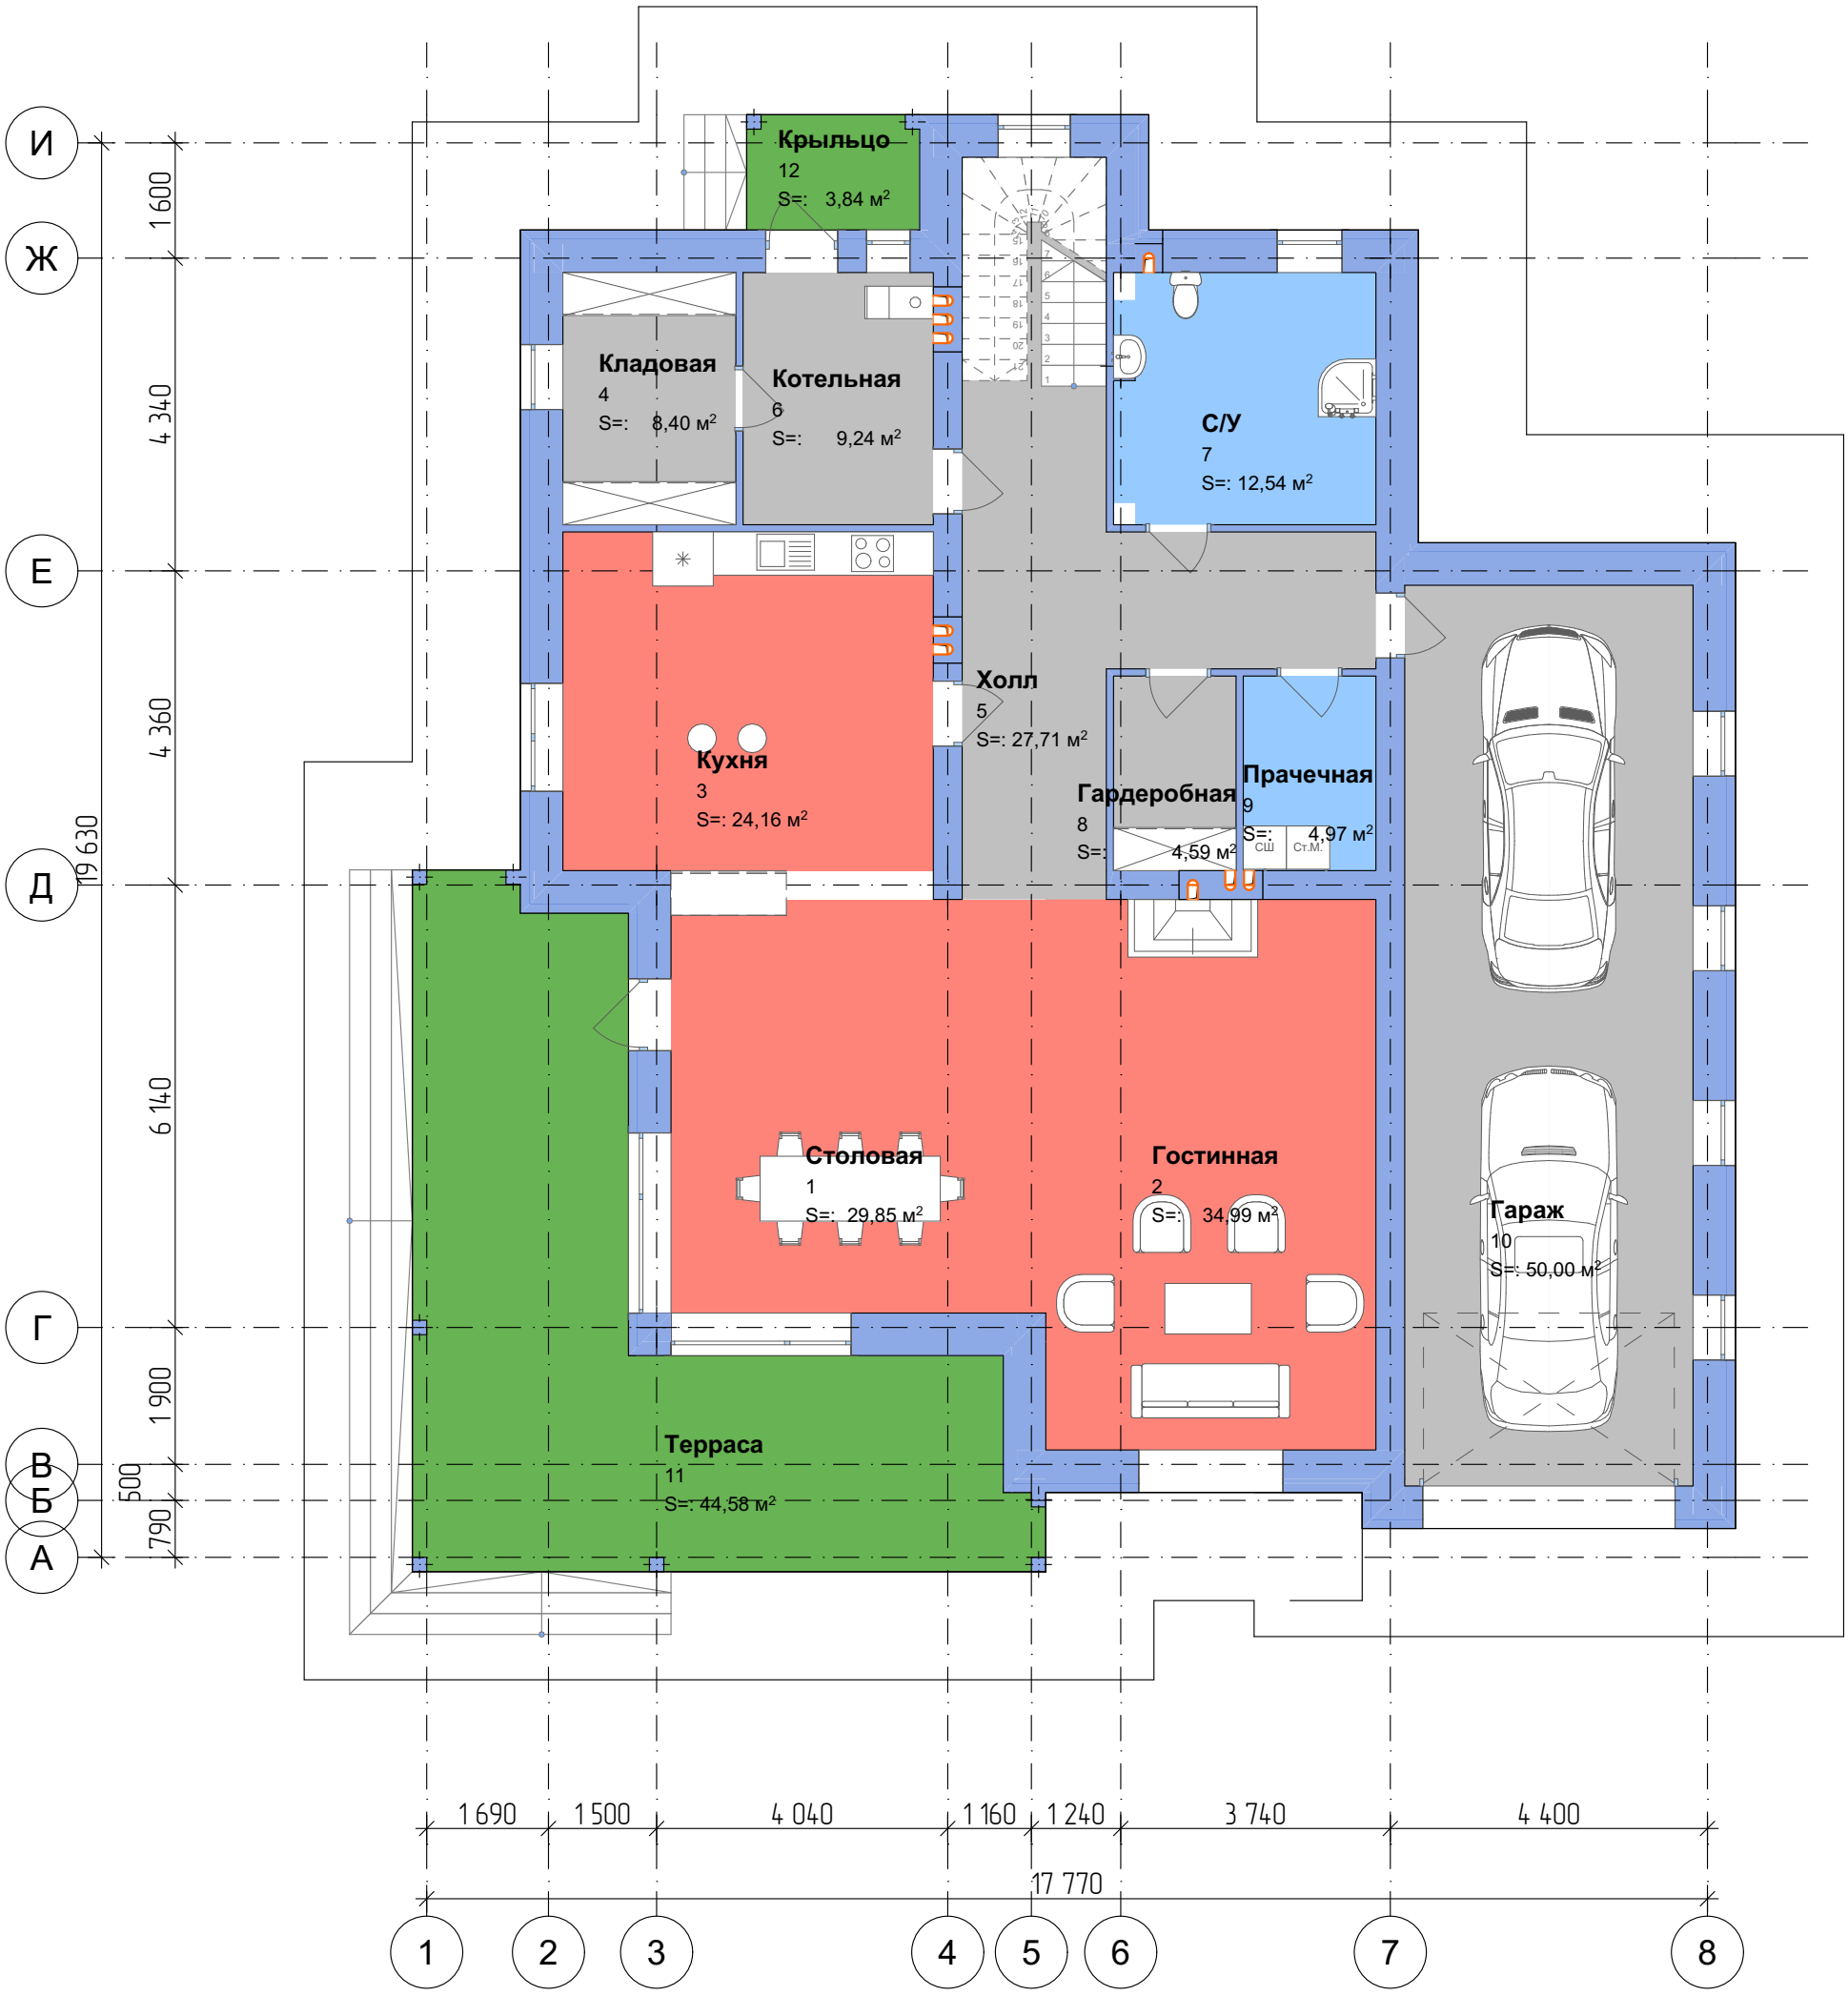

						#ID Проекта	
						кадастровый номер Россия	
Изм.	Кол.уч.	Лист	№Док.	Подп.	Дата		
Разраб.						Индивидуальный жилой дом	Стадия: #Стадия Проекта; Лист: 70; Листов:
ГАП							
План расстановки мебели 1 этаж							

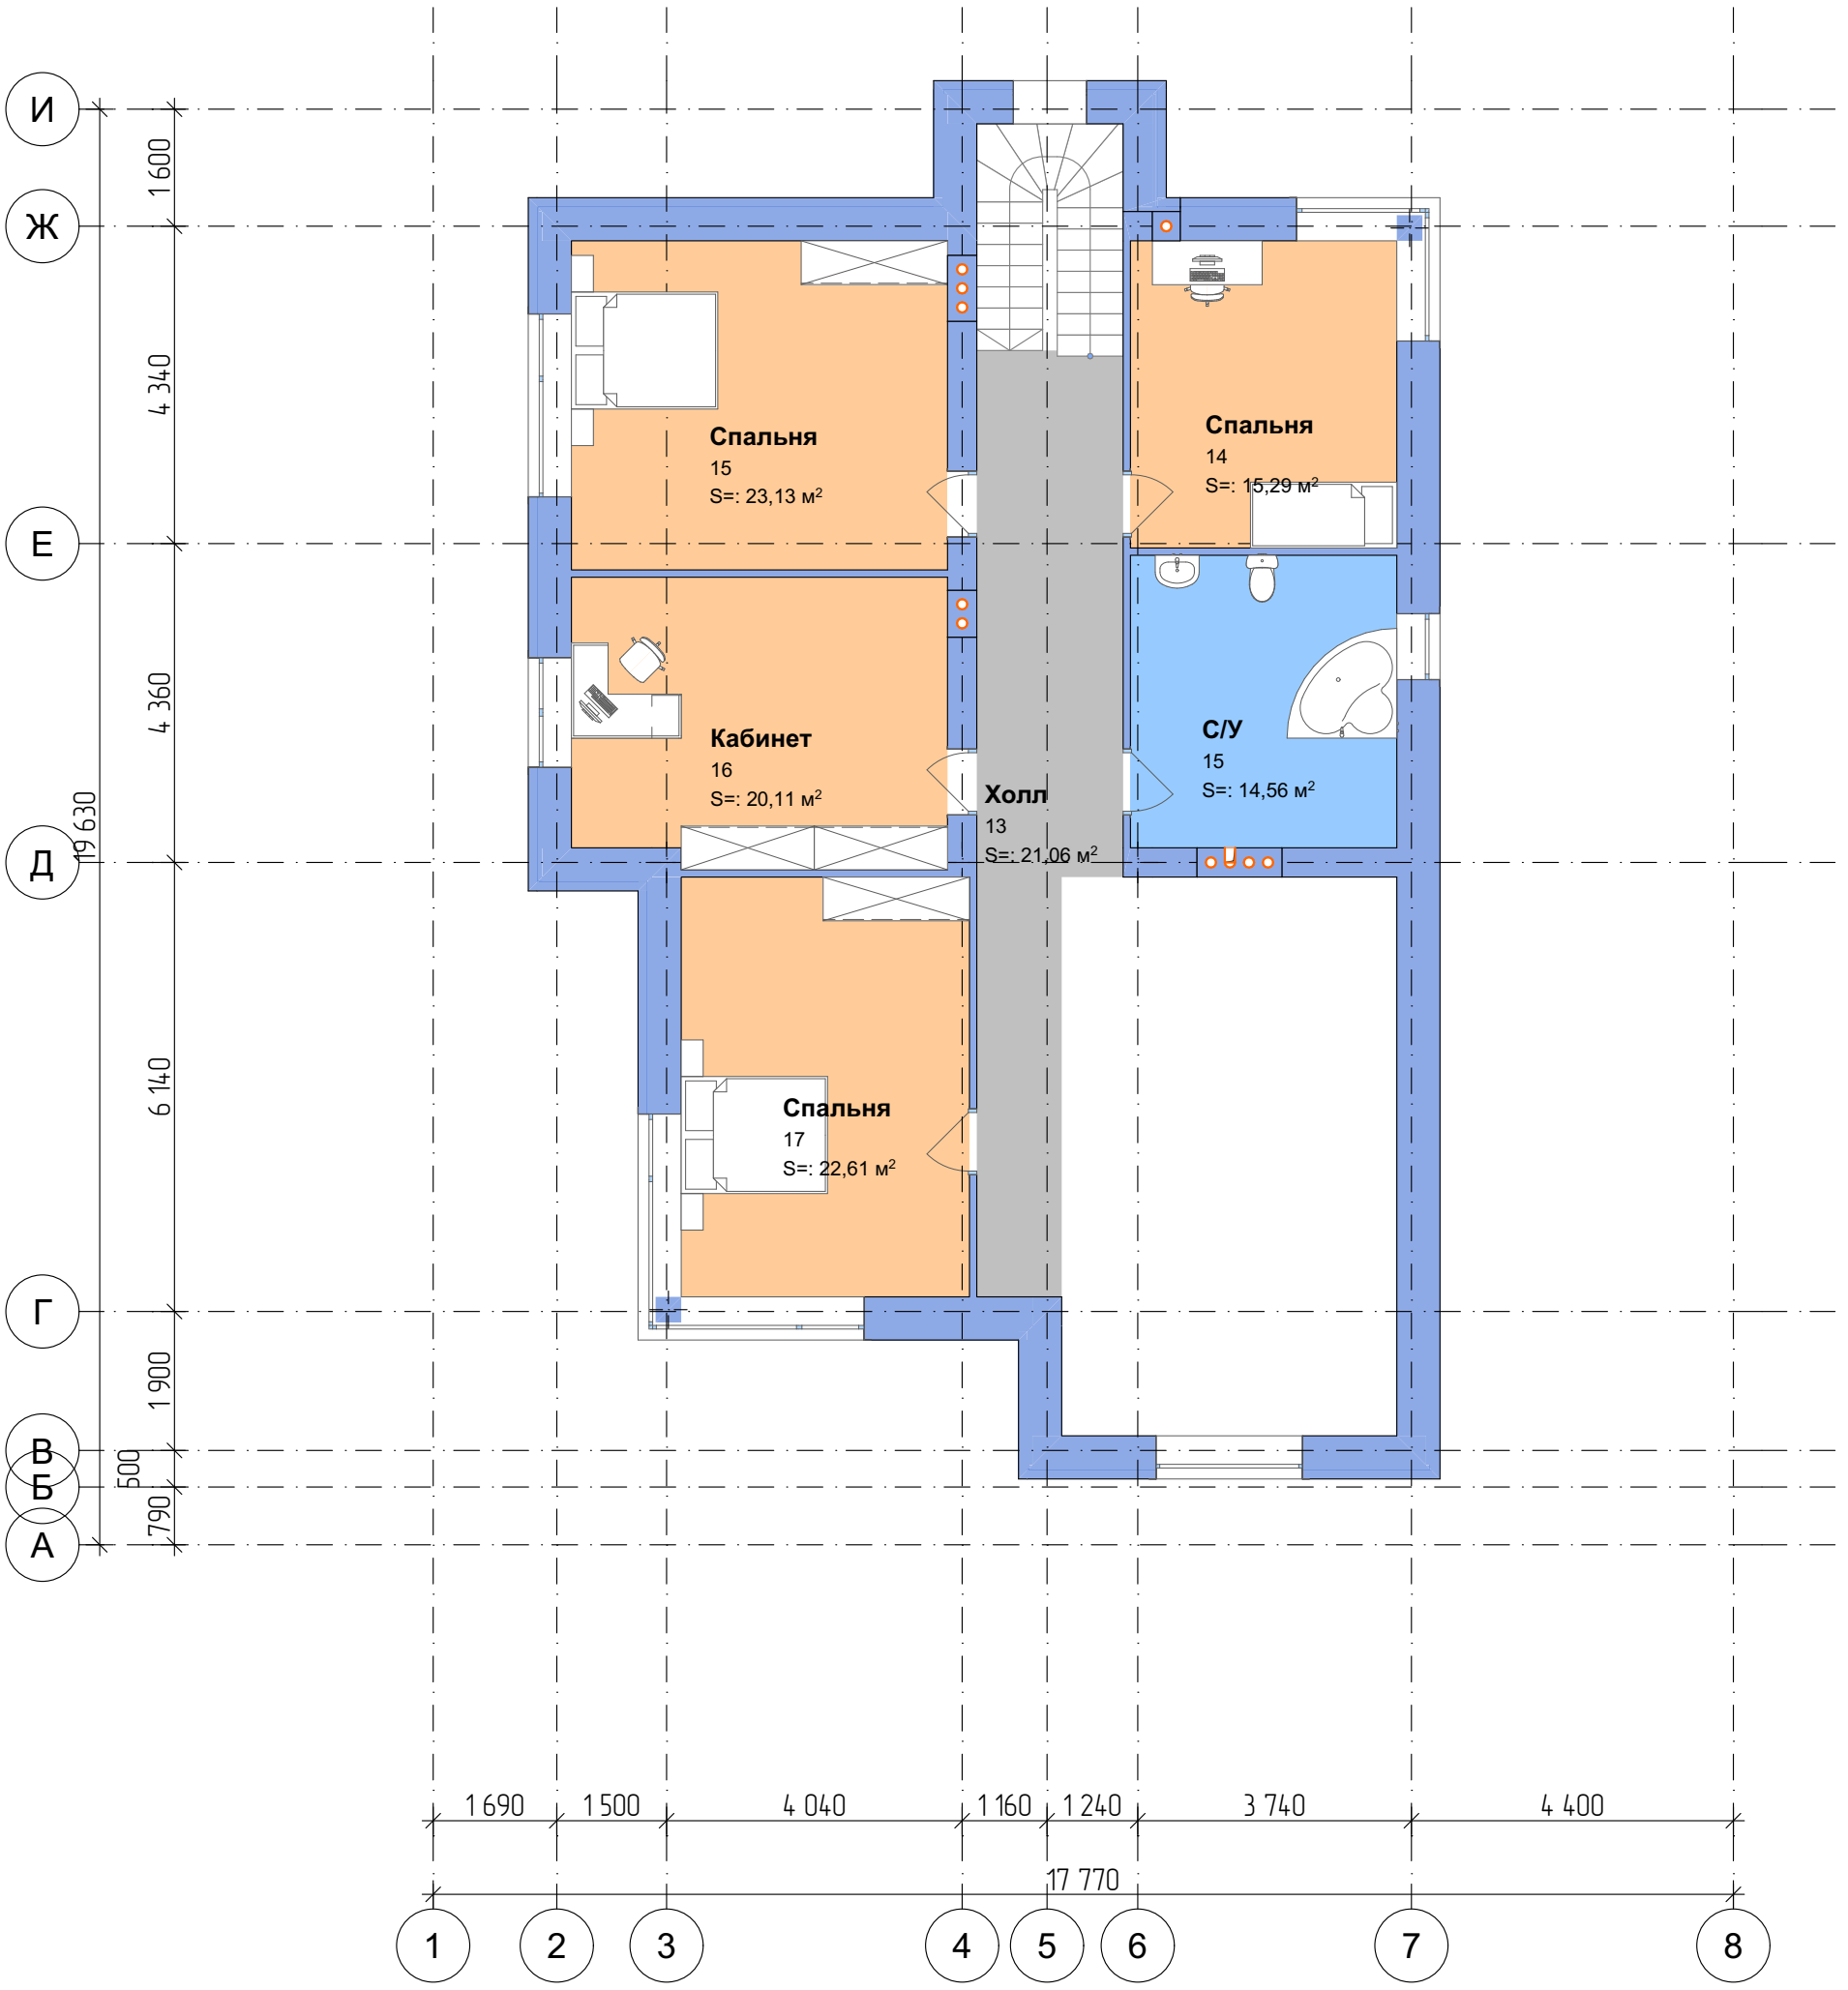

						#ID Проекта	
						кадастровый номер Россия	
Изм.	Кол.уч.	Лист	№Док.	Подп.	Дата		
Разраб.						Индивидуальный жилой дом	Стадия: #Стадия Проекта; Лист: 71; Листов:
ГАП							
План расстановки мебели 2 этаж							

Категория	№	Наименование	Площадь, м2
ОБЩАЯ ПЛОЩАДЬ			
	1	Столовая	29,85
	2	Гостинная	34,99
	3	Кухня	24,16
	4	Кладовая	8,40
	5	Холл	27,71
	6	Котельная	9,24
	7	С/У	12,54
	8	Гардеробная	4,59
	9	Прачечная	4,97
	10	Гараж	50,00
			206,45 м²
Транзитные Помещения			
	11	Терраса	44,58
	12	Крыльцо	3,84
			48,42 м²
			254,87 м²

							#ID Проекта
							кадастровый номер Россия
Изм.	Колуч.	Лист	№Док.	Подп.	Дата		
Разраб.						Индивидуальный жилой дом	Стадия: #Стадия Проекта; Лист: 72; Листов:
ГАП							
Экспликация помещений 1- го этажа							

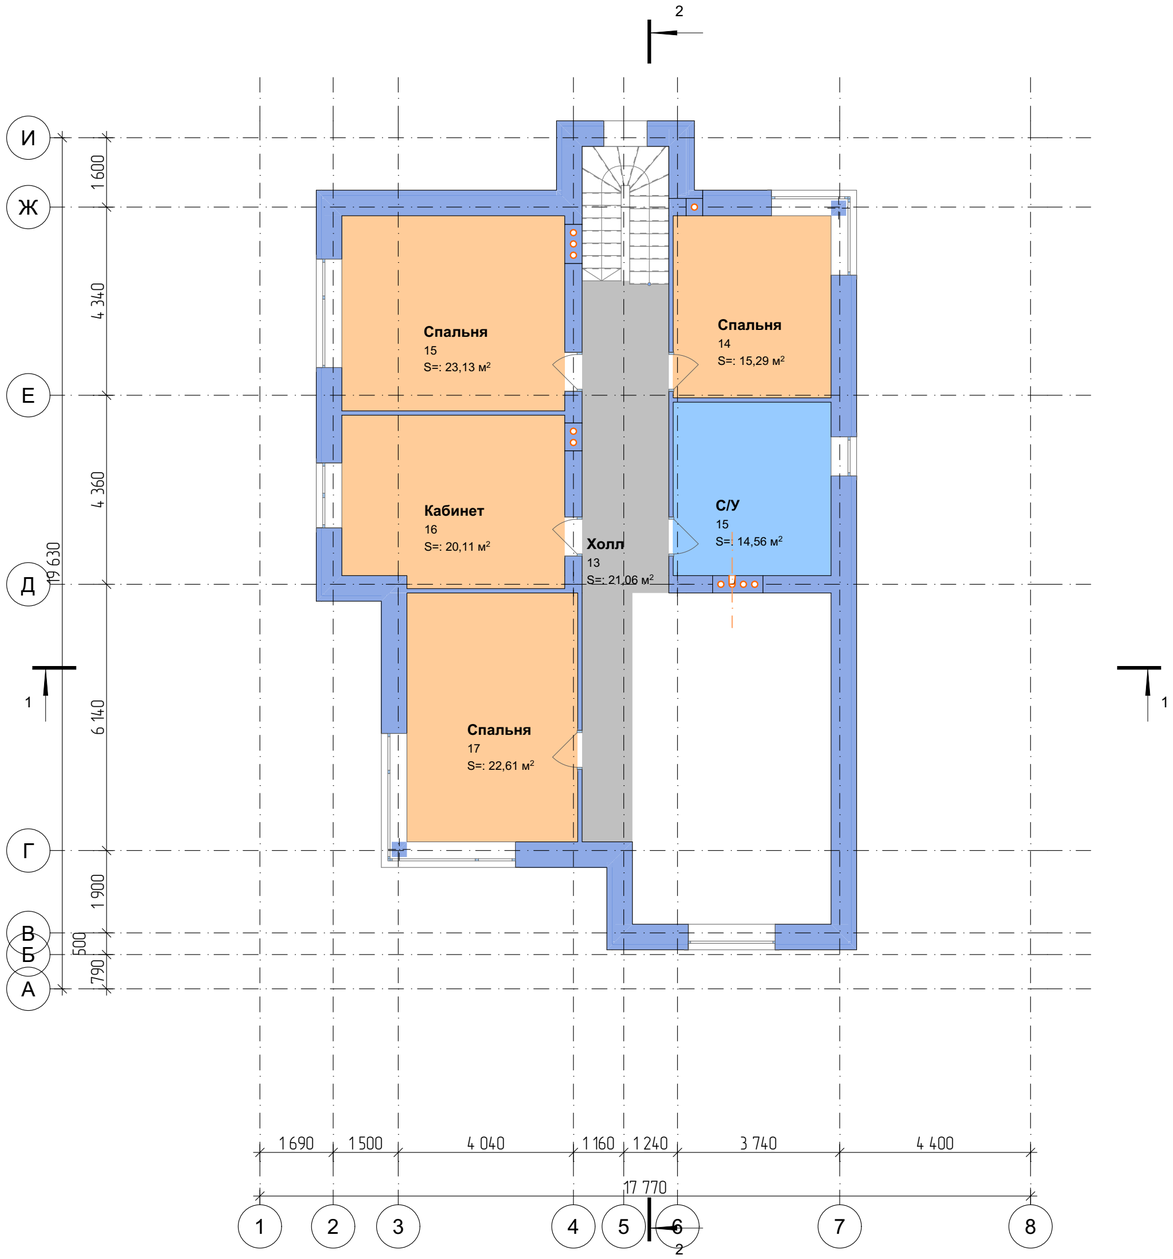

Категория	№	Наименование	Площадь, м2
ОБЩАЯ ПЛОЩАДЬ			
	13	Холл	21,06
	14	Спальня	15,29
	15	С/У	14,56
	15	Спальня	23,13
	16	Кабинет	20,11
	17	Спальня	22,61
			116,76 м²

						#ID Проекта		
						кадастровый номер Россия		
Изм.	Кол.уч.	Лист	№Док.	Подп.	Дата			
Разраб.						Индивидуальный жилой дом	Стадия	Лист	Листов
ГАП							#Стадия Проекта	73	
Экспликация помещений 2-го этажа									

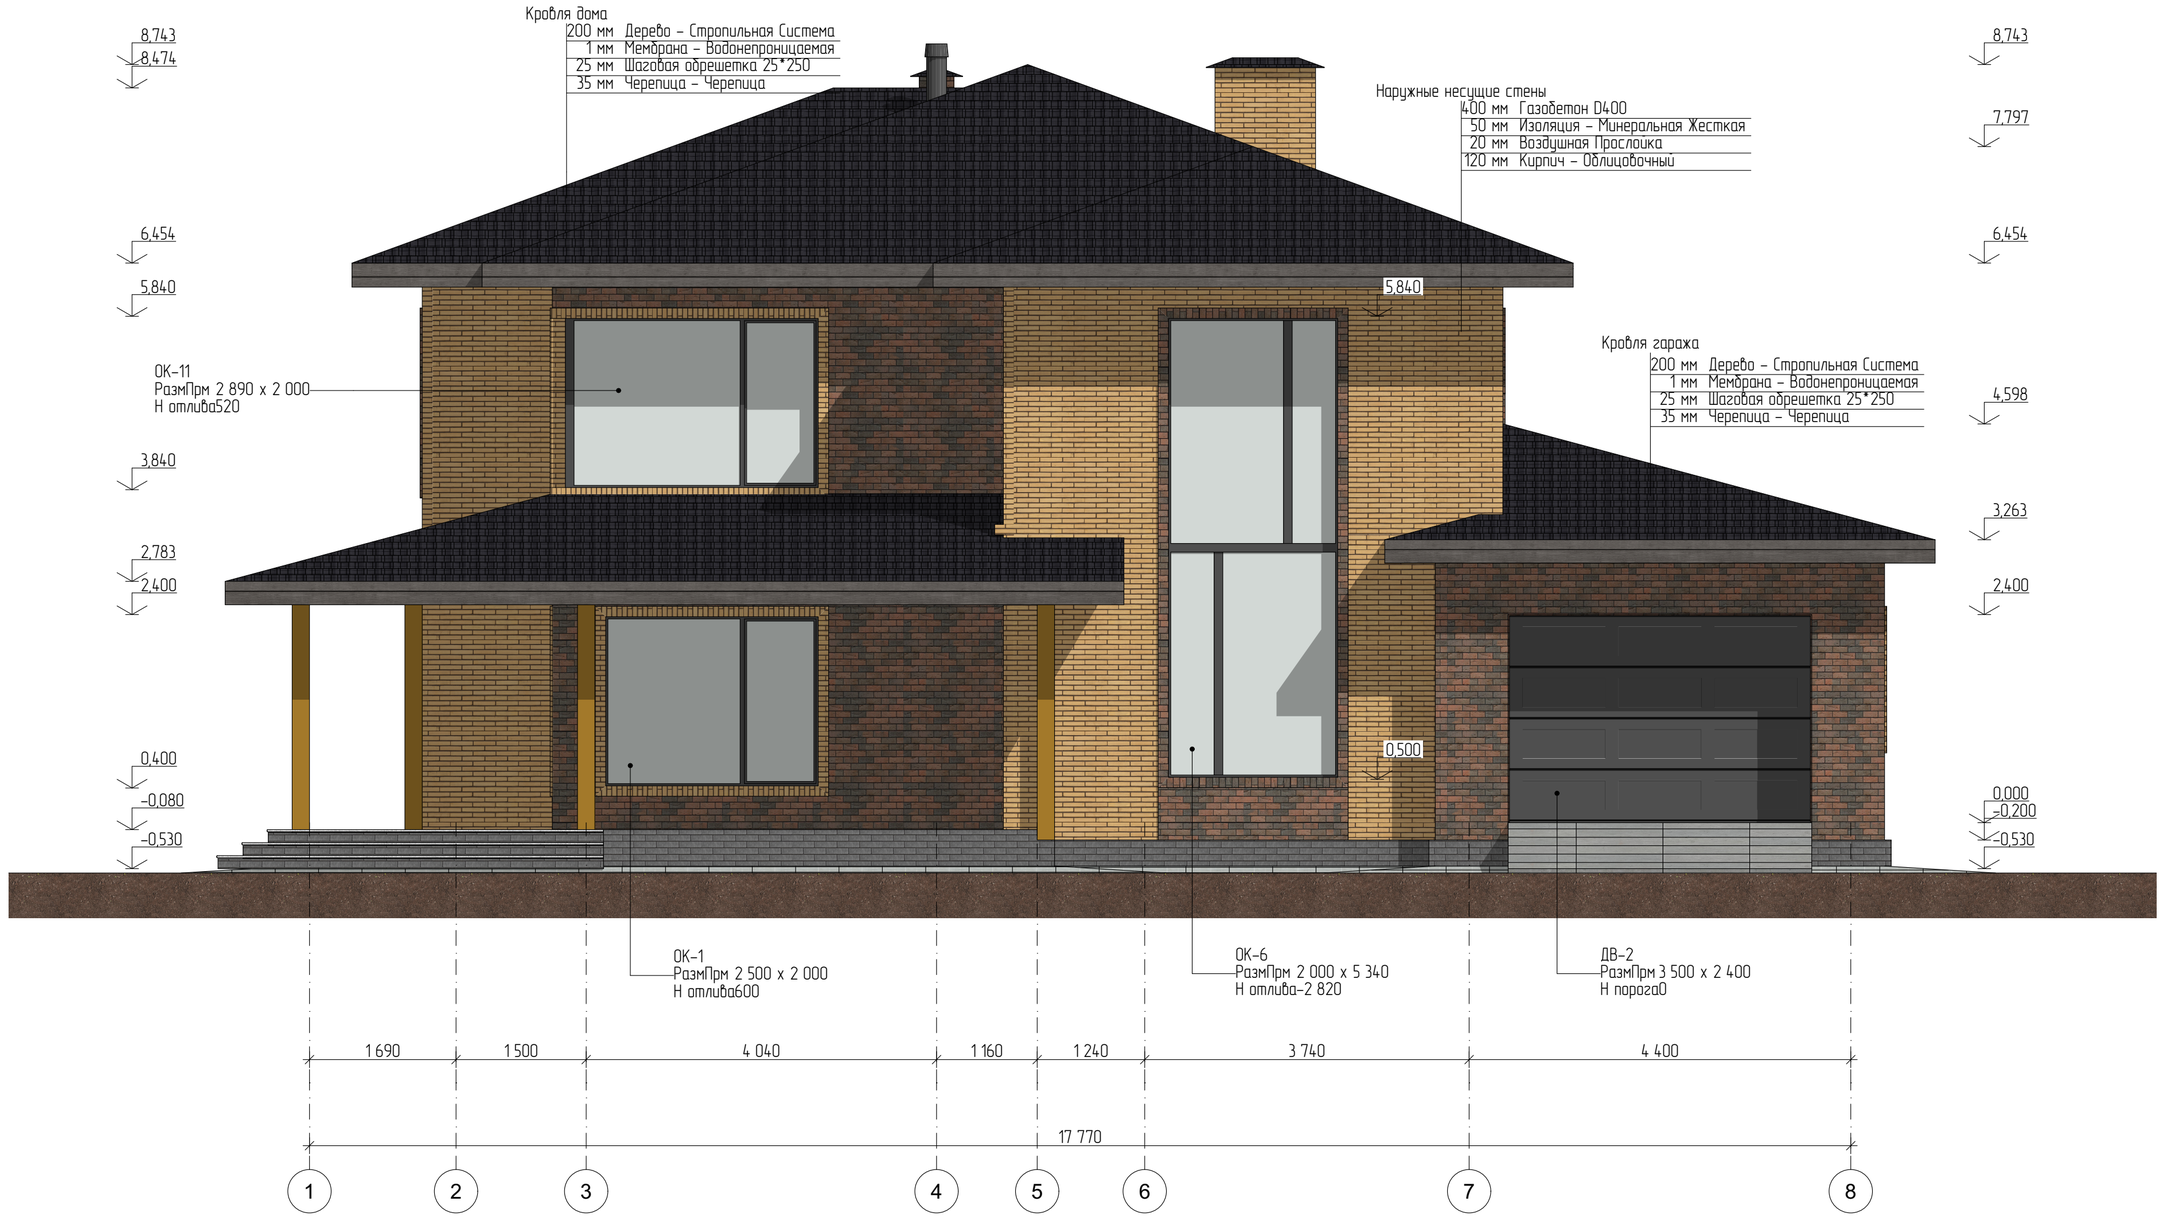

						#ID Проекта	
						кадастровый номер Россия	
Изм.	Колуч.	Лист	№Док.	Подп.	Дата		
Разраб.						Индивидуальный жилой дом	Стадия: #Стадия Проекта; Лист: 74; Листов:
ГАП							
Фасад в осях 1-8							

						#ID Проекта	
						кадастровый номер Россия	
Изм.	Колуч.	Лист	№Док.	Подп.	Дата		
Разраб.						Индивидуальный жилой дом	Стадия: #Стадия Проекта; Лист: 75; Листов:
ГАП							
Фасад в осях И-А							

						#ID Проекта	
						кадастровый номер Россия	
Изм.	Кол.уч.	Лист	№Док.	Подп.	Дата		
Разраб.						Индивидуальный жилой дом	Стадия: #Стадия Проекта; Лист: 76; Листов:
ГАП							
Фасад в осях А-И							

							#ID Проекта
							кадастровый номер Россия
Изм.	Колуч.	Лист	№Док.	Подп.	Дата		
Разраб.						Индивидуальный жилой дом	Стадия: #Стадия Проекта; Лист: 77; Листов:
ГАП							
Фасад в осях 8-1							

Ведомость материалов на фасад			
Наиме...	Компоненты		Объем, м3
	Толщина, мм	Площадь, м2	
Изоляция - Минеральная Жесткая			
	50	373,45	18,64
Кирпич - Облицовочный			
	120	378,30	45,25

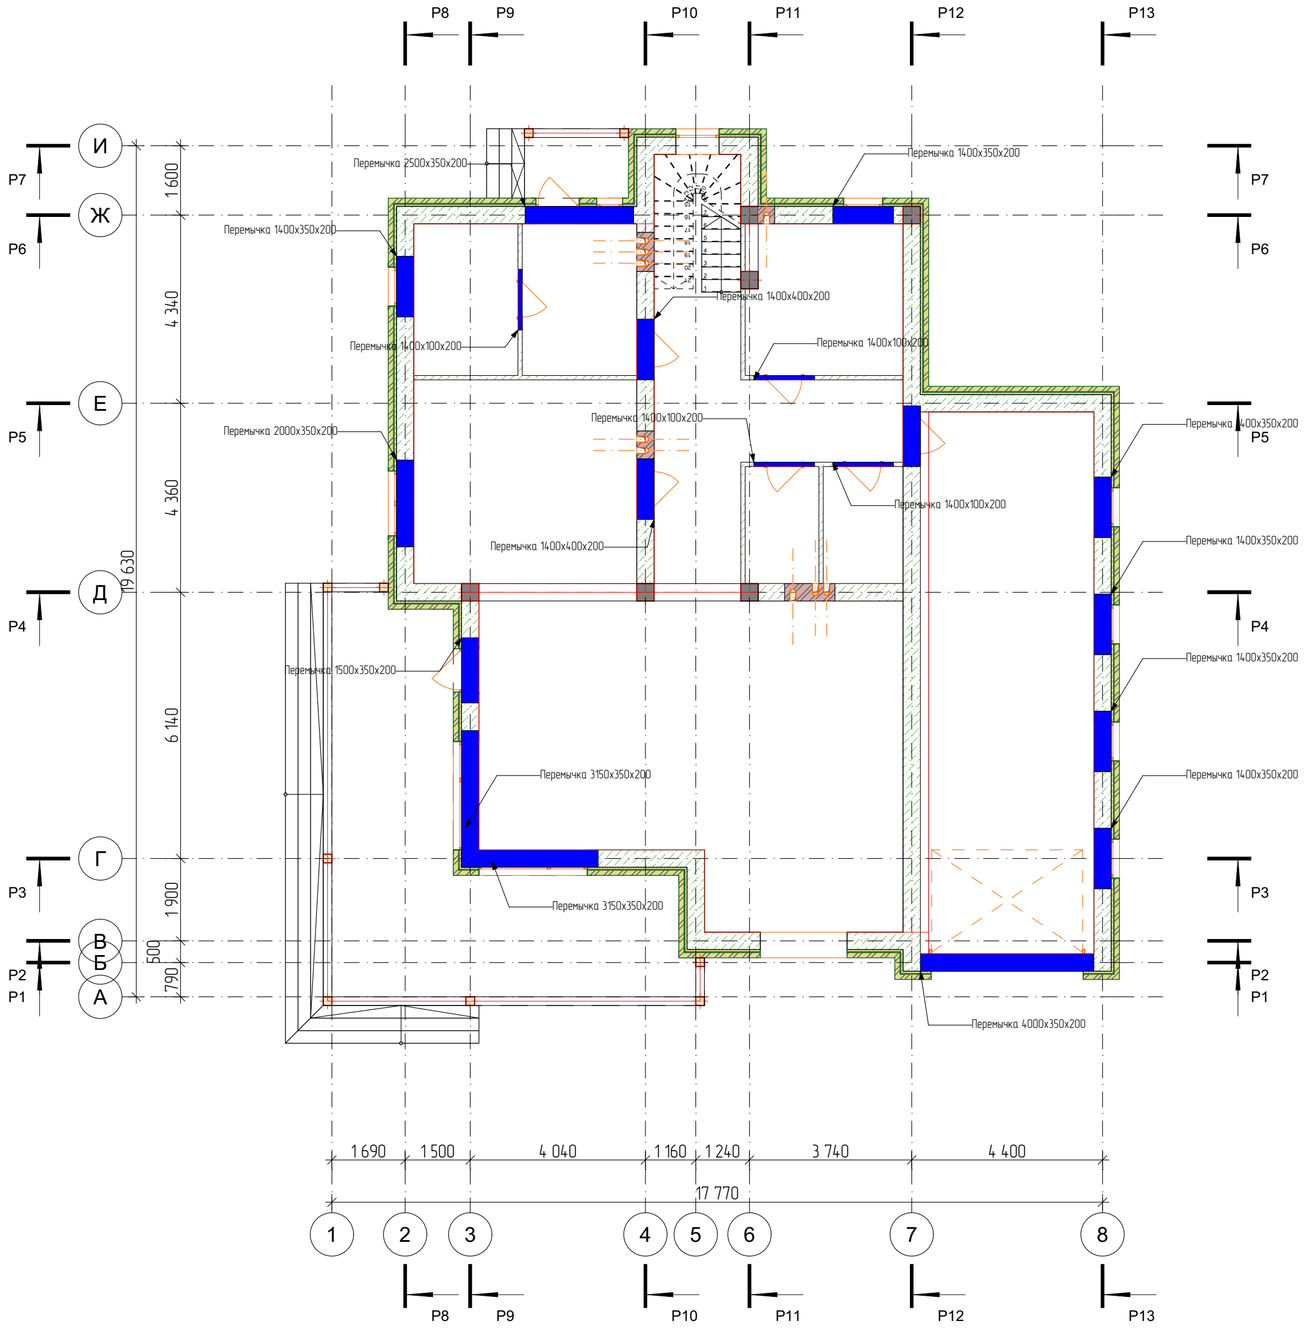

						#ID Проекта	
						кадастровый номер Россия	
Изм.	Кол.уч.	Лист	№Док.	Подп.	Дата		
Разраб.						Индивидуальный жилой дом	Стадия: #Стадия Проекта; Лист: 80; Листов:
ГАП							
План раскладки перемычек 1 - го этажа							

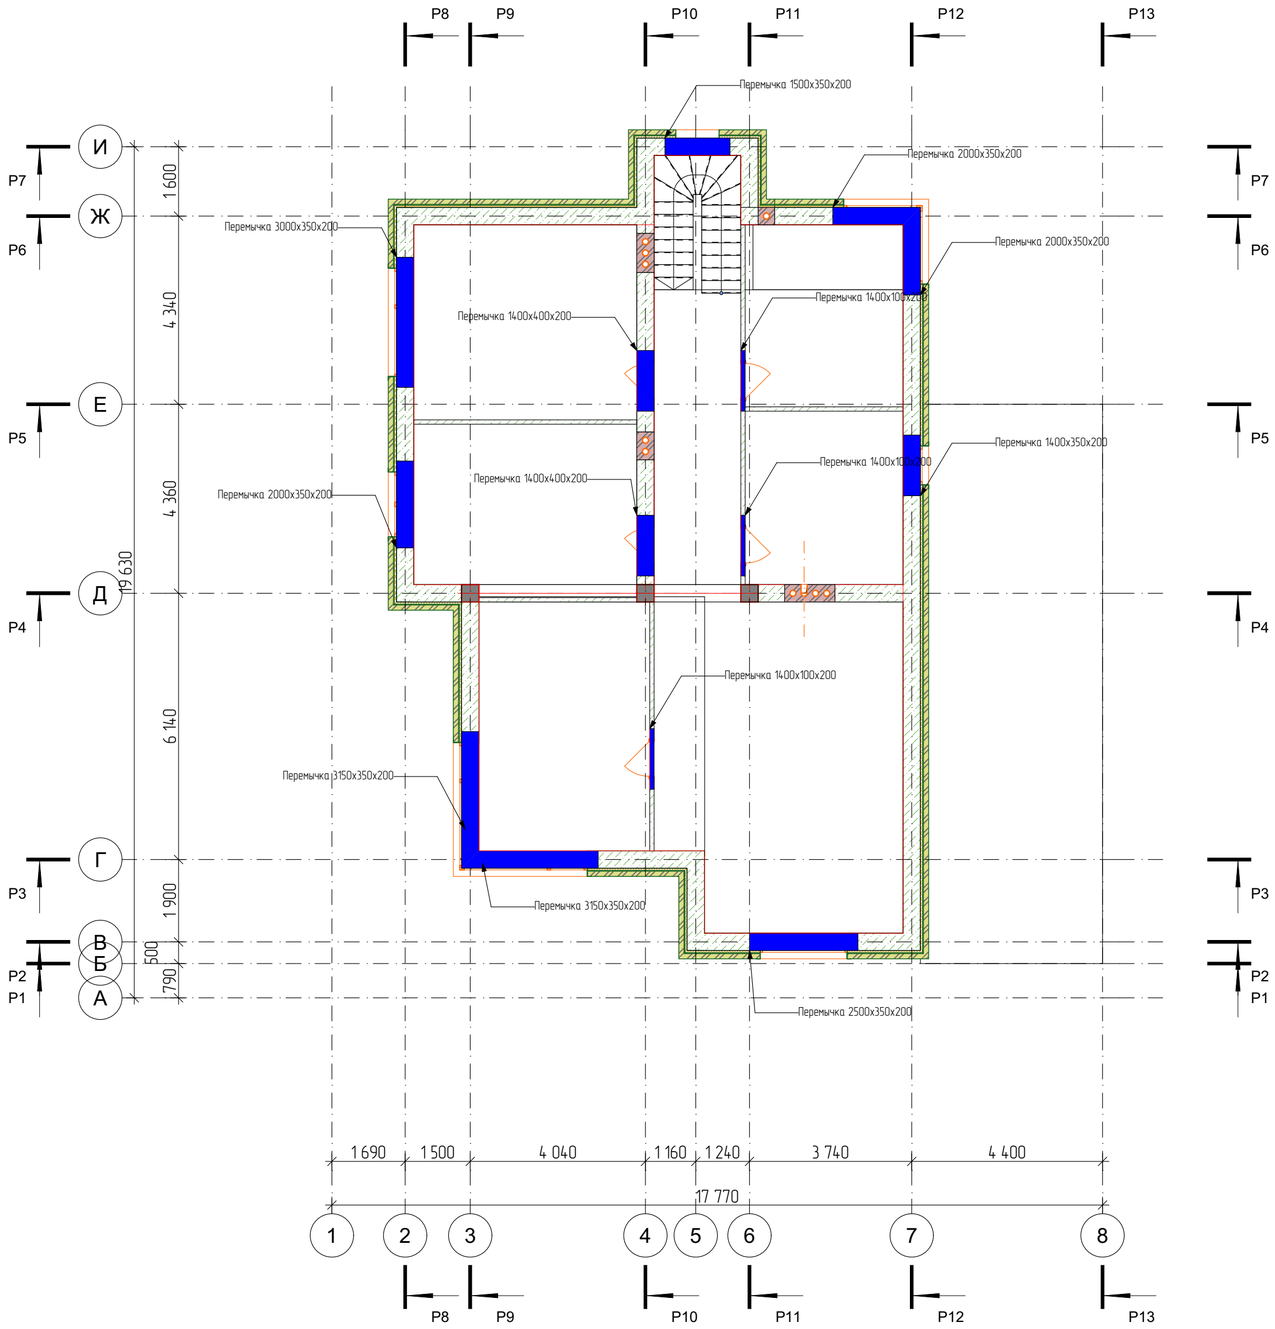

						#ID Проекта	
						кадастровый номер Россия	
Изм.	Кол.уч.	Лист	№Док.	Подп.	Дата		
Разраб.						Индивидуальный жилой дом	Стадия: #Стадия Проекта; Лист: 81; Листов:
ГАП							
План раскладки перемычек 2-го этажа							

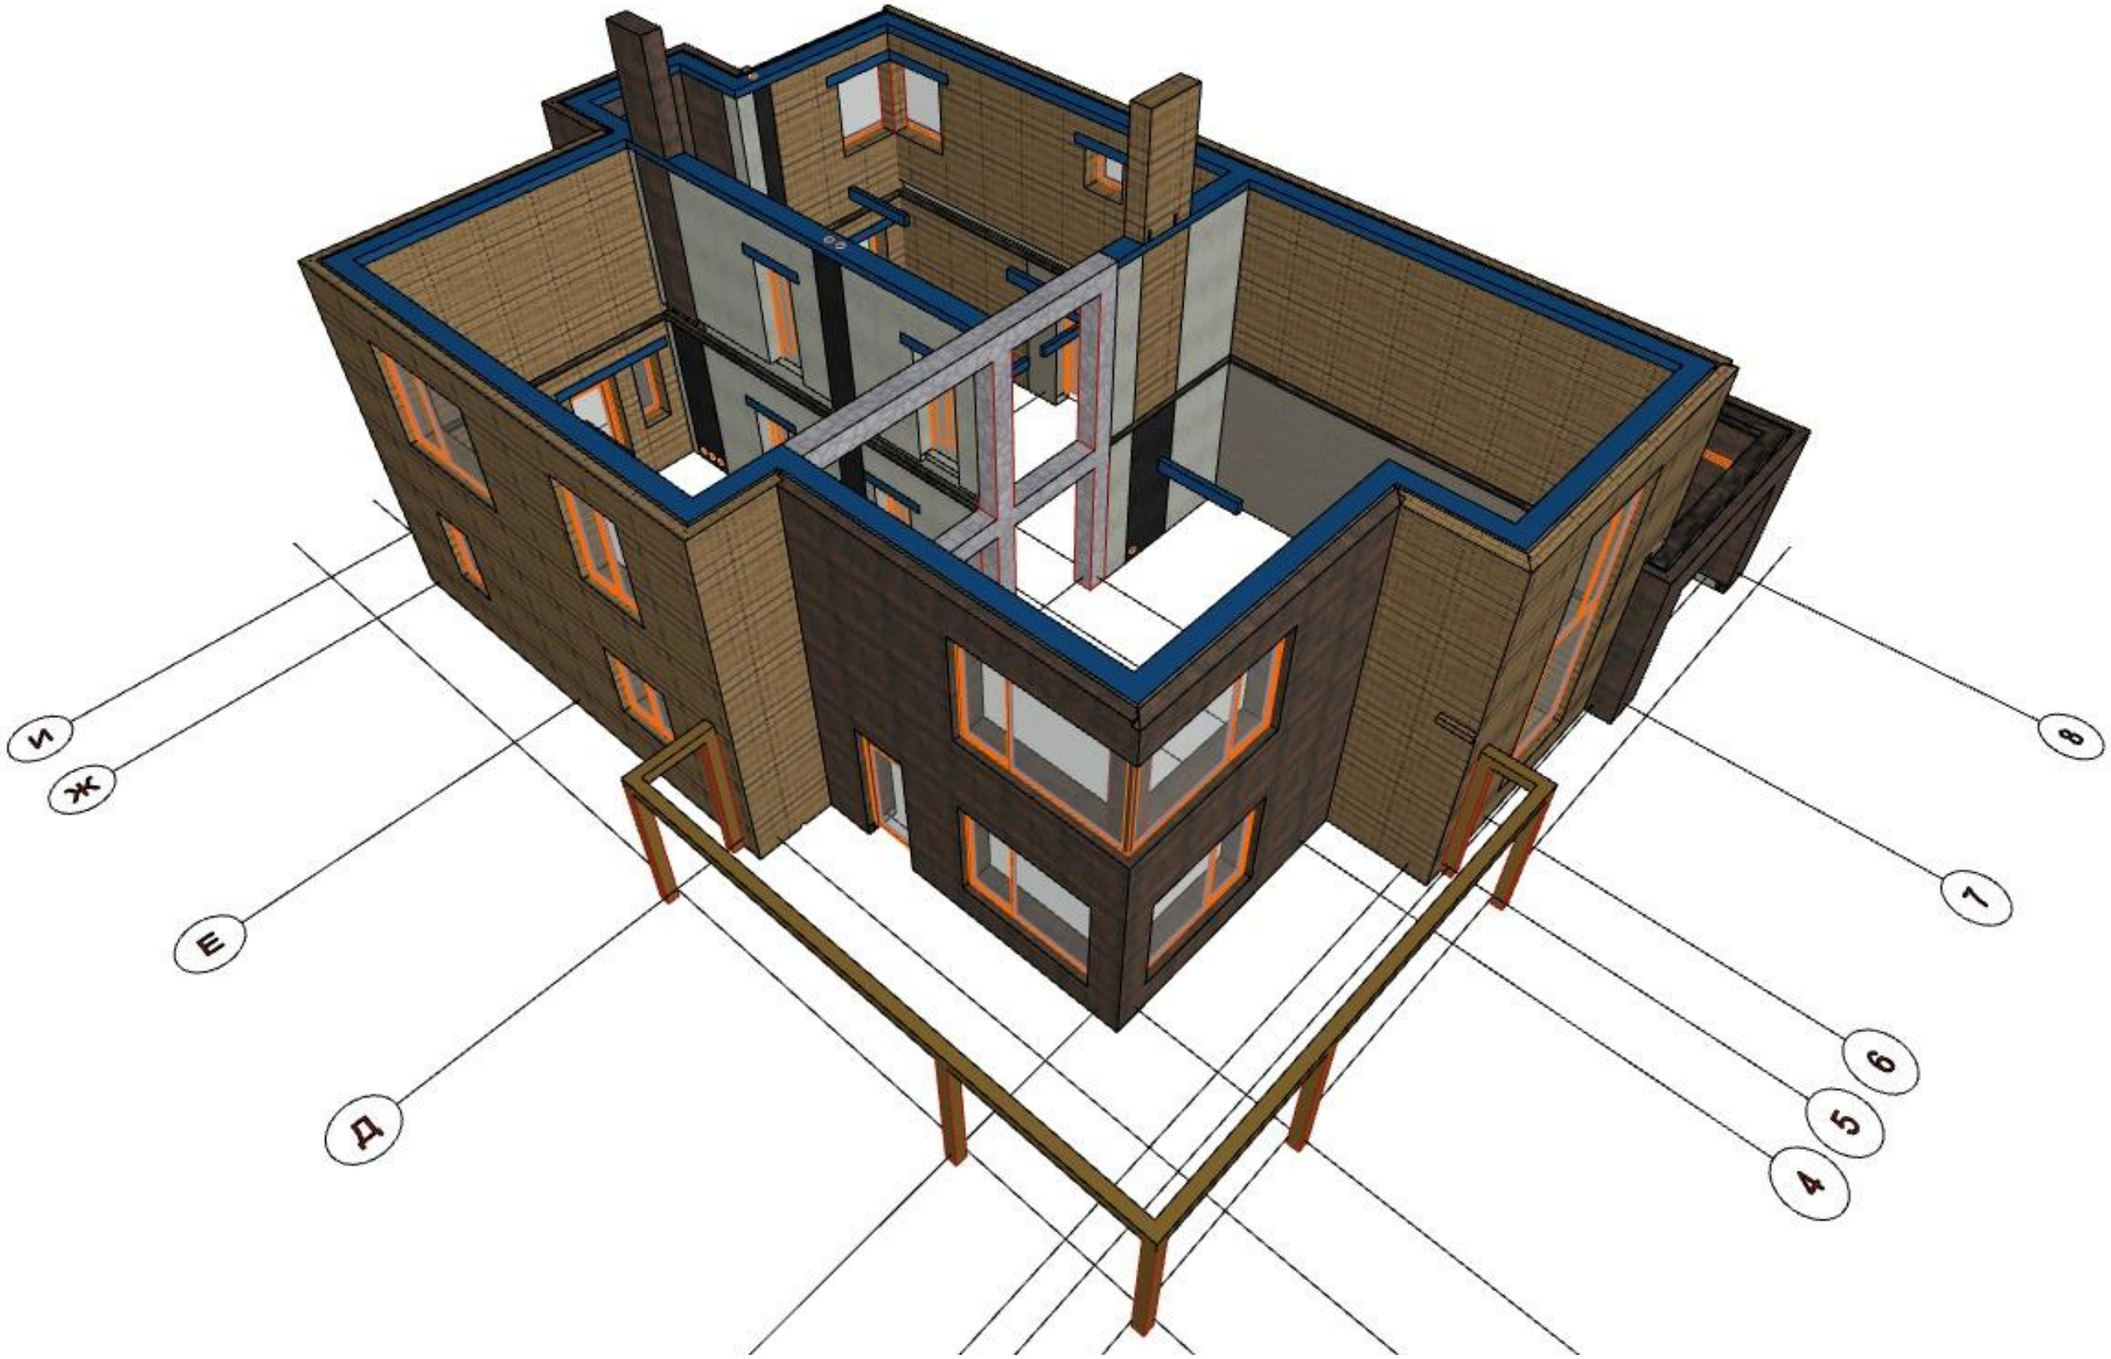

						#ID Проекта		
						кадастровый номер Россия		
Изм.	Кол.уч.	Лист	№Док.	Подп.	Дата			
Разраб.						Индивидуальный жилой дом	Стадия	Лист	Листов
ГАП							#Стадия Проекта	82	
3Д вид монолитного пояса									

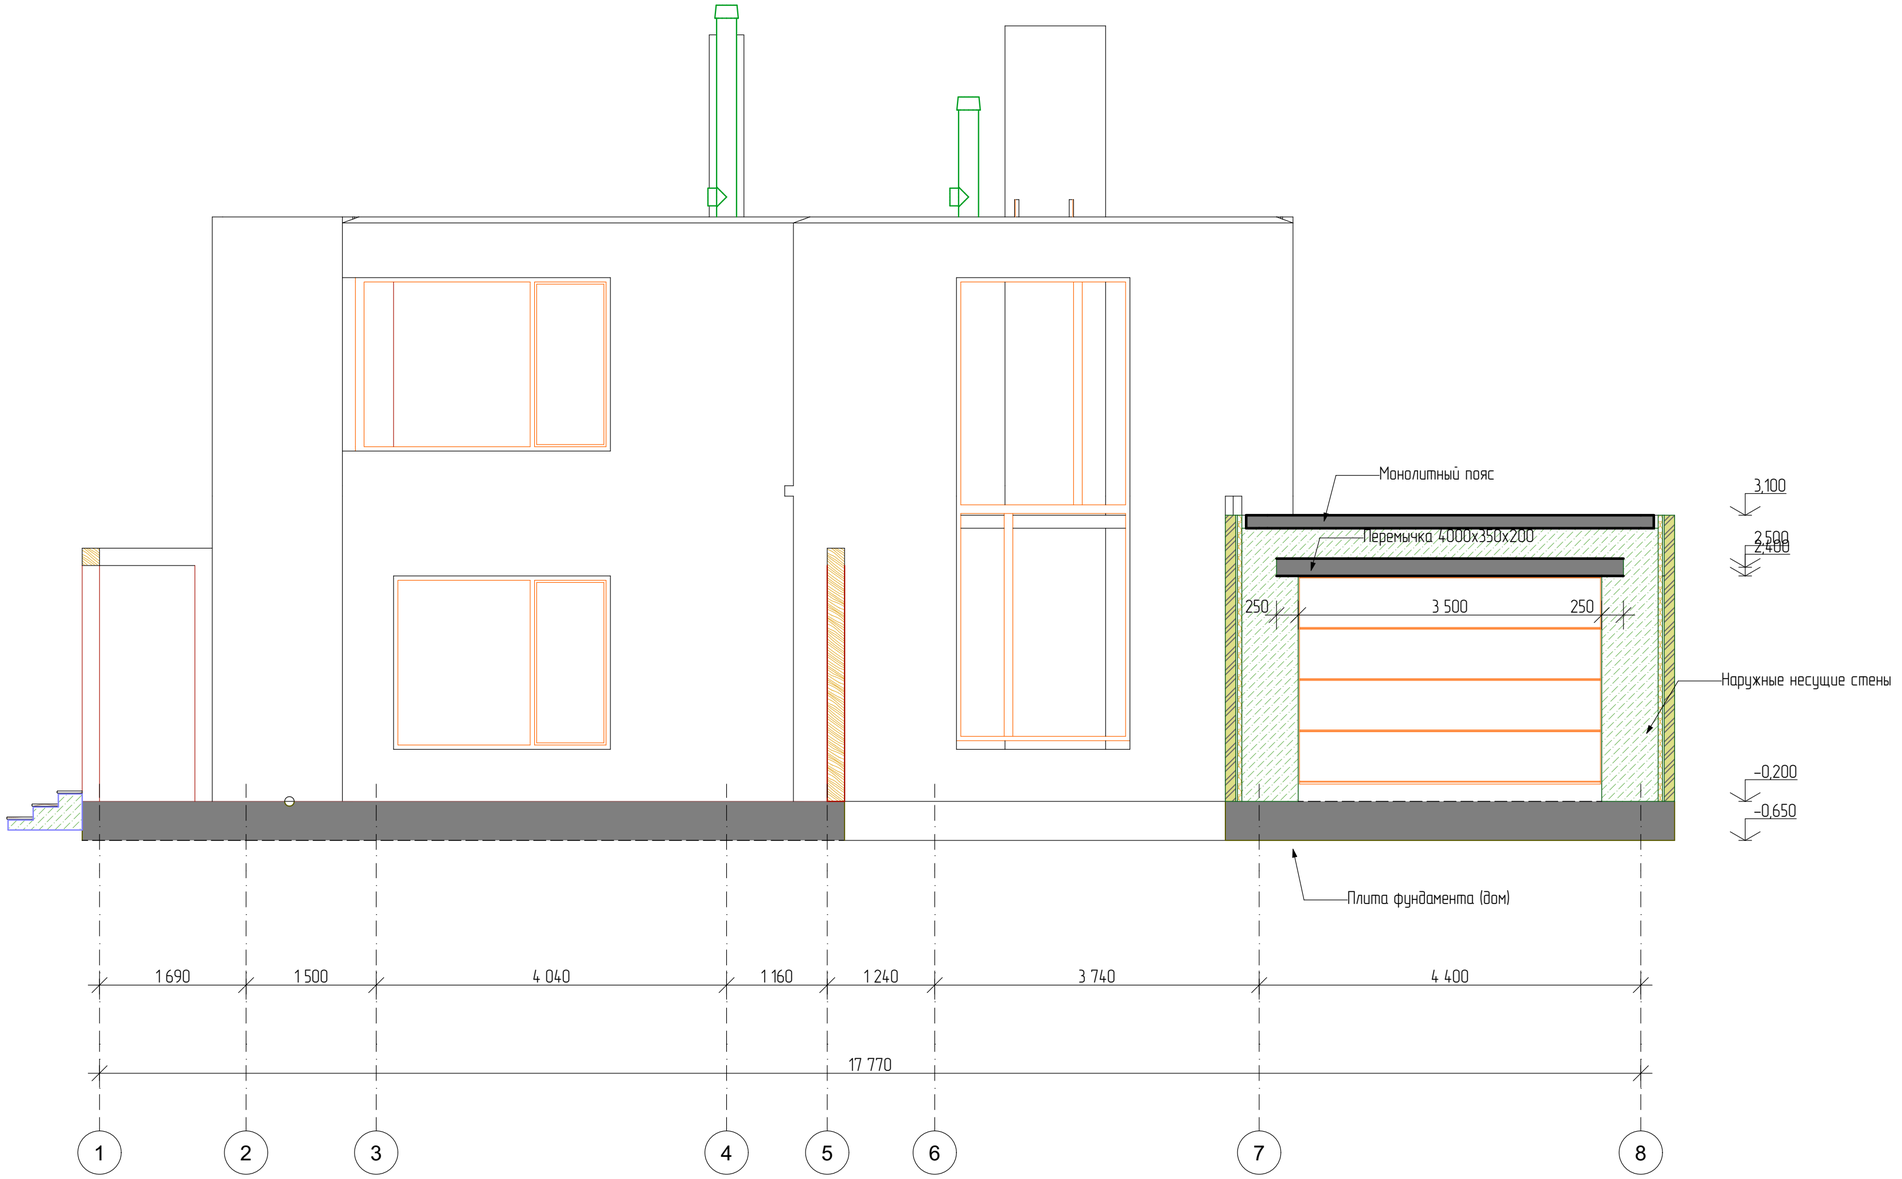

						#ID Проекта	
						кадастровый номер Россия	
Изм.	Колуч.	Лист	№Док.	Подп.	Дата		
Разраб.						Индивидуальный жилой дом	Стадия: #Стадия Проекта; Лист: 83; Листов:
ГАП							
Р1							

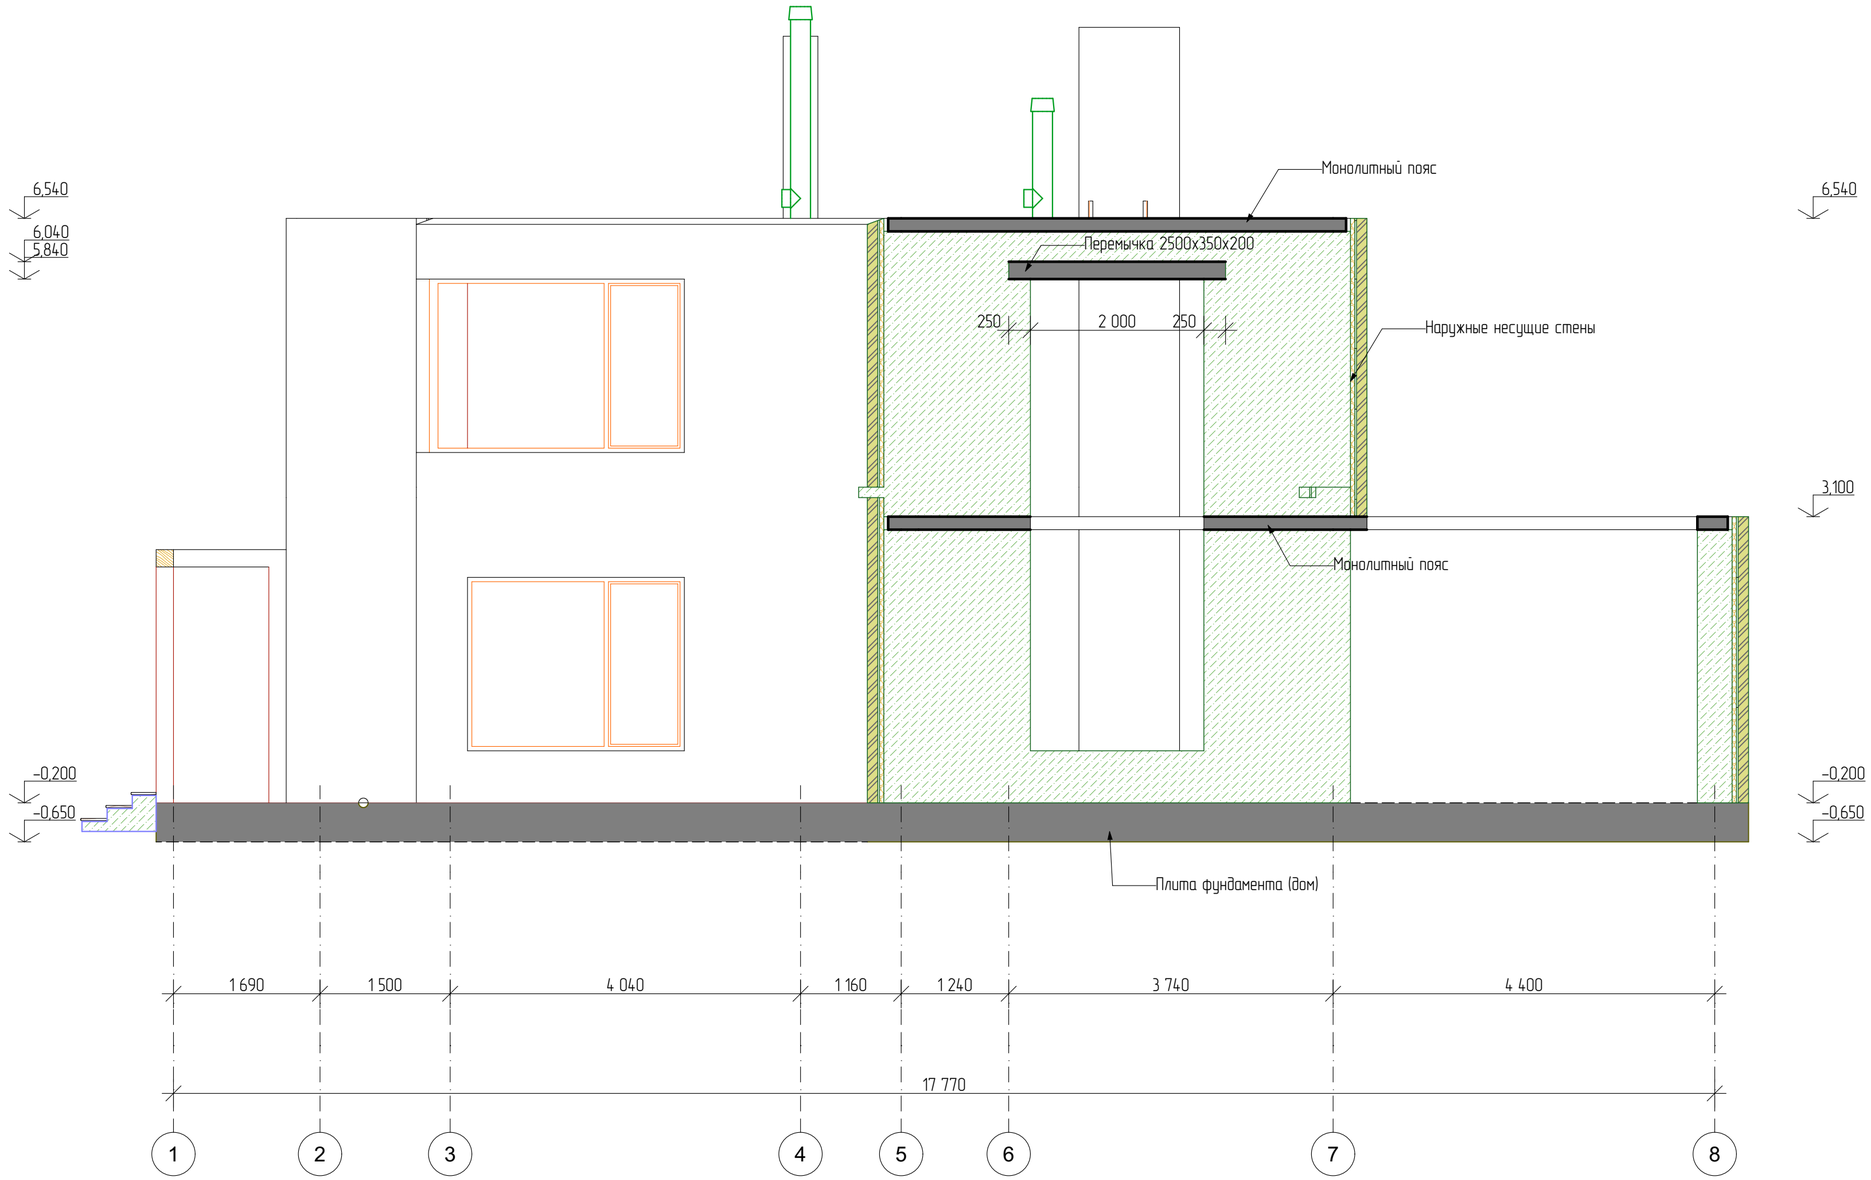

						#ID Проекта
						кадастровый номер Россия
Изм.	Кол.уч.	Лист	№Док.	Подп.	Дата	
Разраб.						Индивидуальный жилой дом
ГАП						

Стадия	Лист	Листов
#Стадия Проекта	84	

Р2

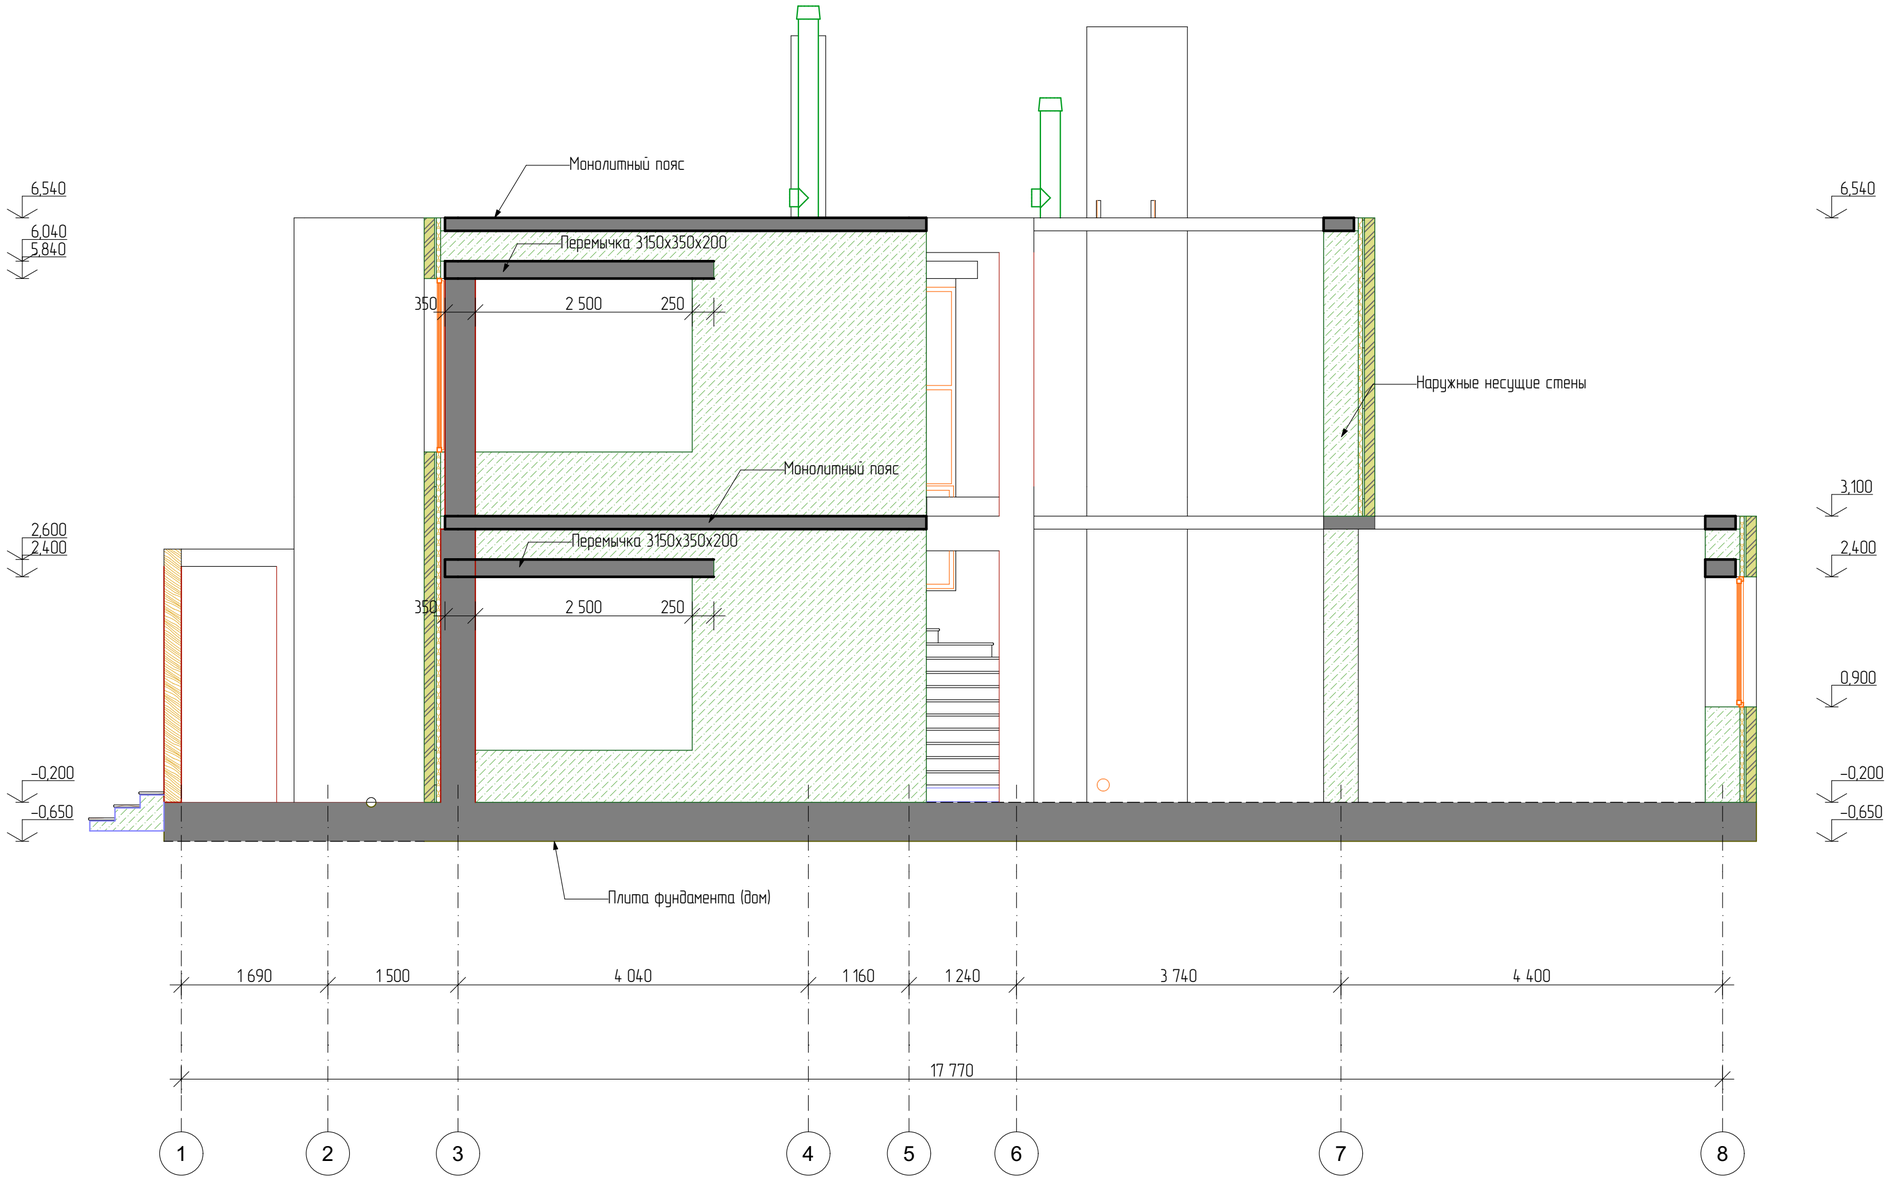

						#ID Проекта	
						кадастровый номер Россия	
Изм.	Кол.уч.	Лист	№Док.	Подп.	Дата		
Разраб.						Индивидуальный жилой дом	Стадия: #Стадия Проекта; Лист: 85; Листов:
ГАП							
						Р3	

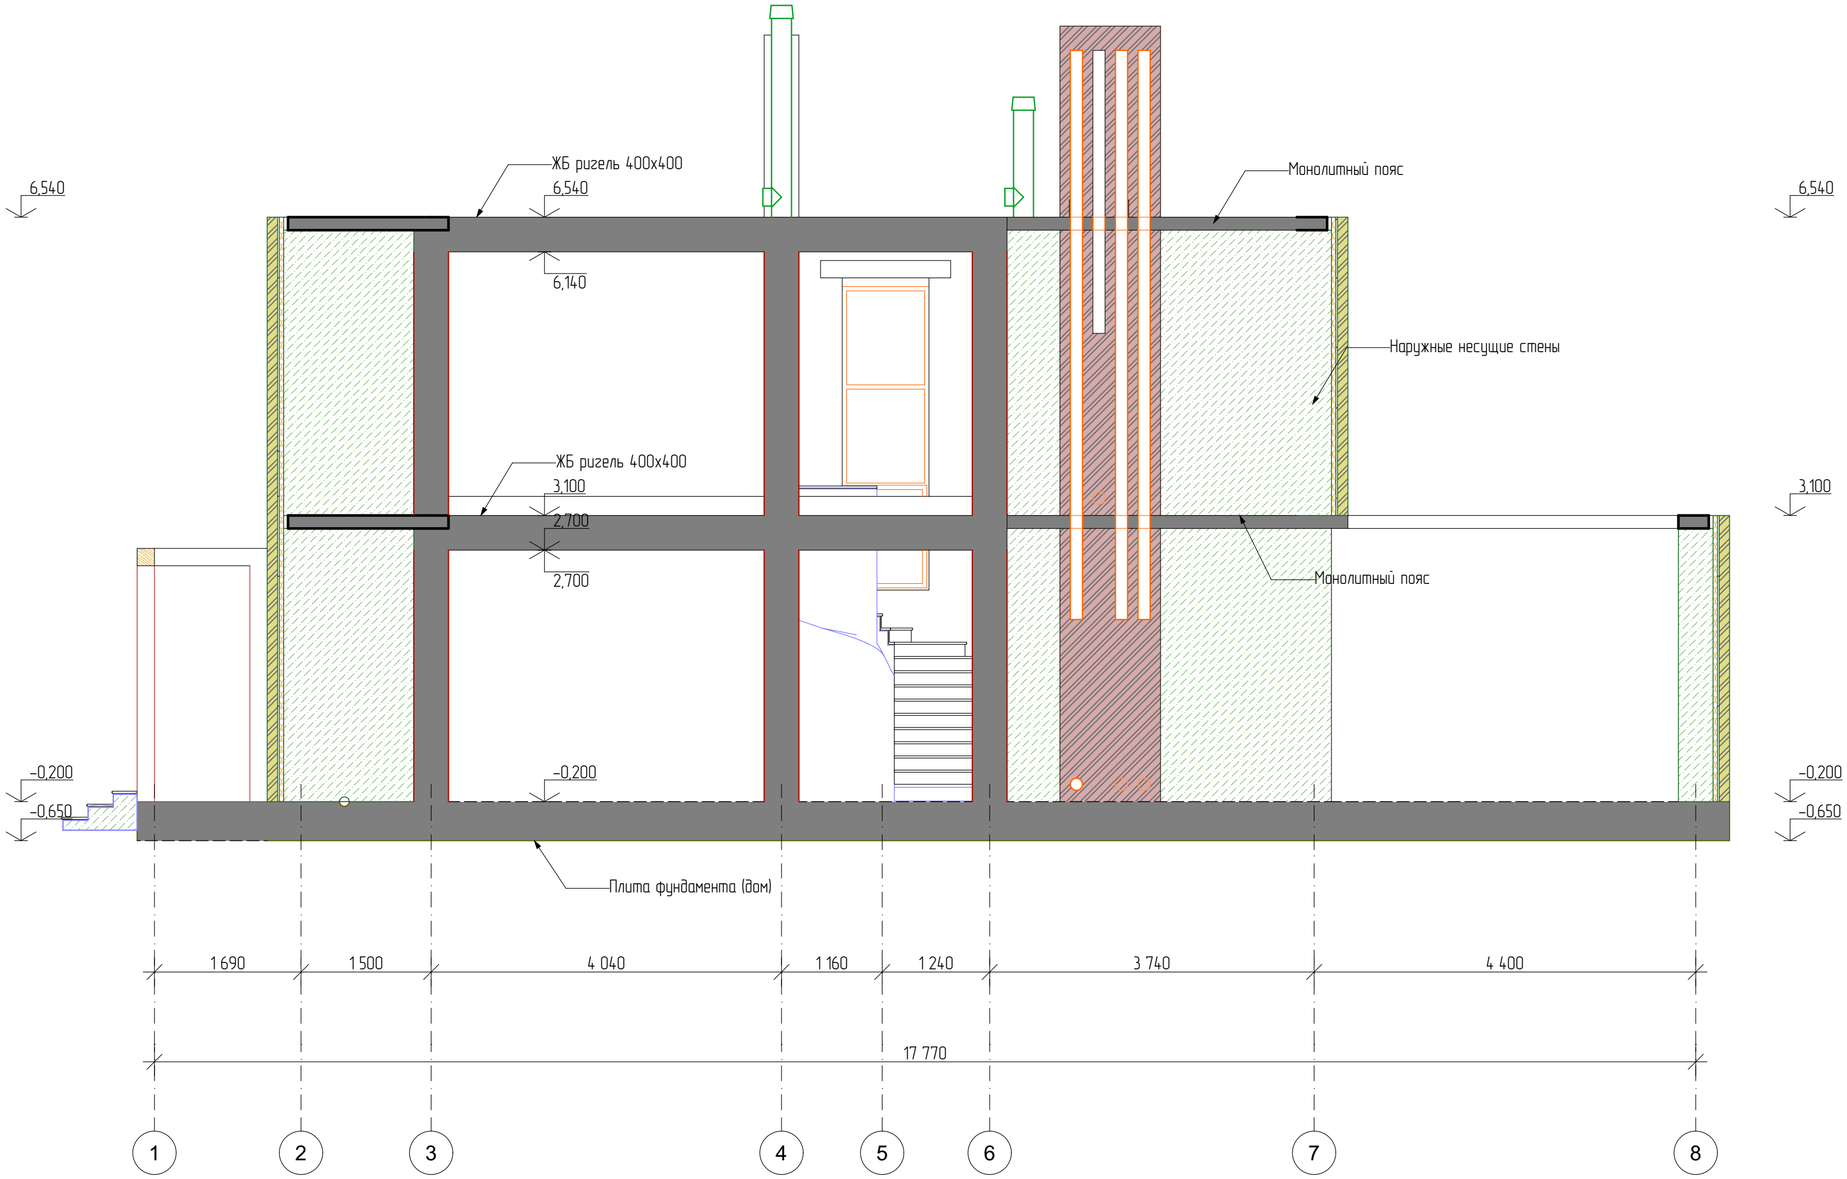

							#ID Проекта
							кадастровый номер Россия
Изм.	Колуч.	Лист	№Док.	Подп.	Дата		
Разраб.						Индивидуальный жилой дом	Стадия: #Стадия Проекта; Лист: 86; Листов:
ГАП							
Р4							

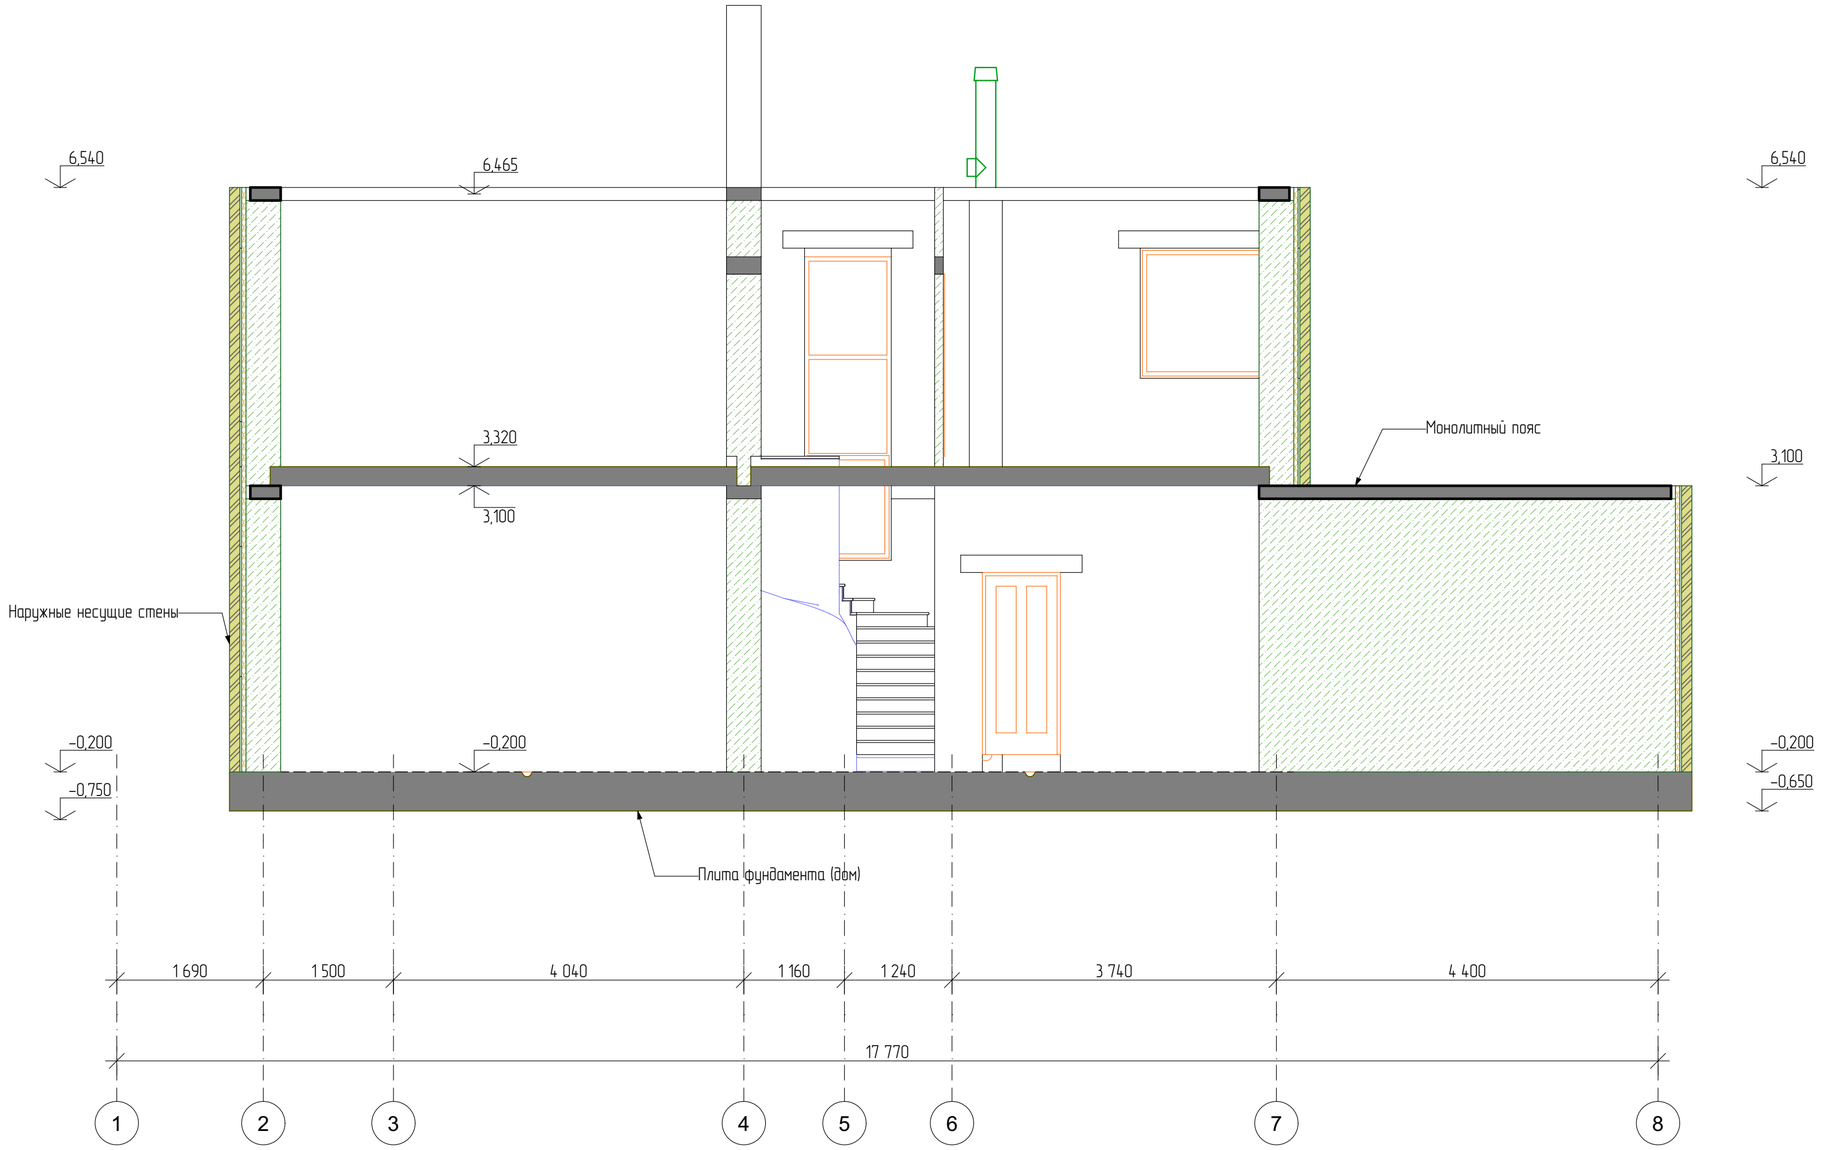

						#ID Проекта	
						кадастровый номер Россия	
Изм.	Кол.уч.	Лист	№Док.	Подп.	Дата		
Разраб.						Индивидуальный жилой дом	Стадия: #Стадия Проекта; Лист: 87; Листов:
ГАП							
						Р5	

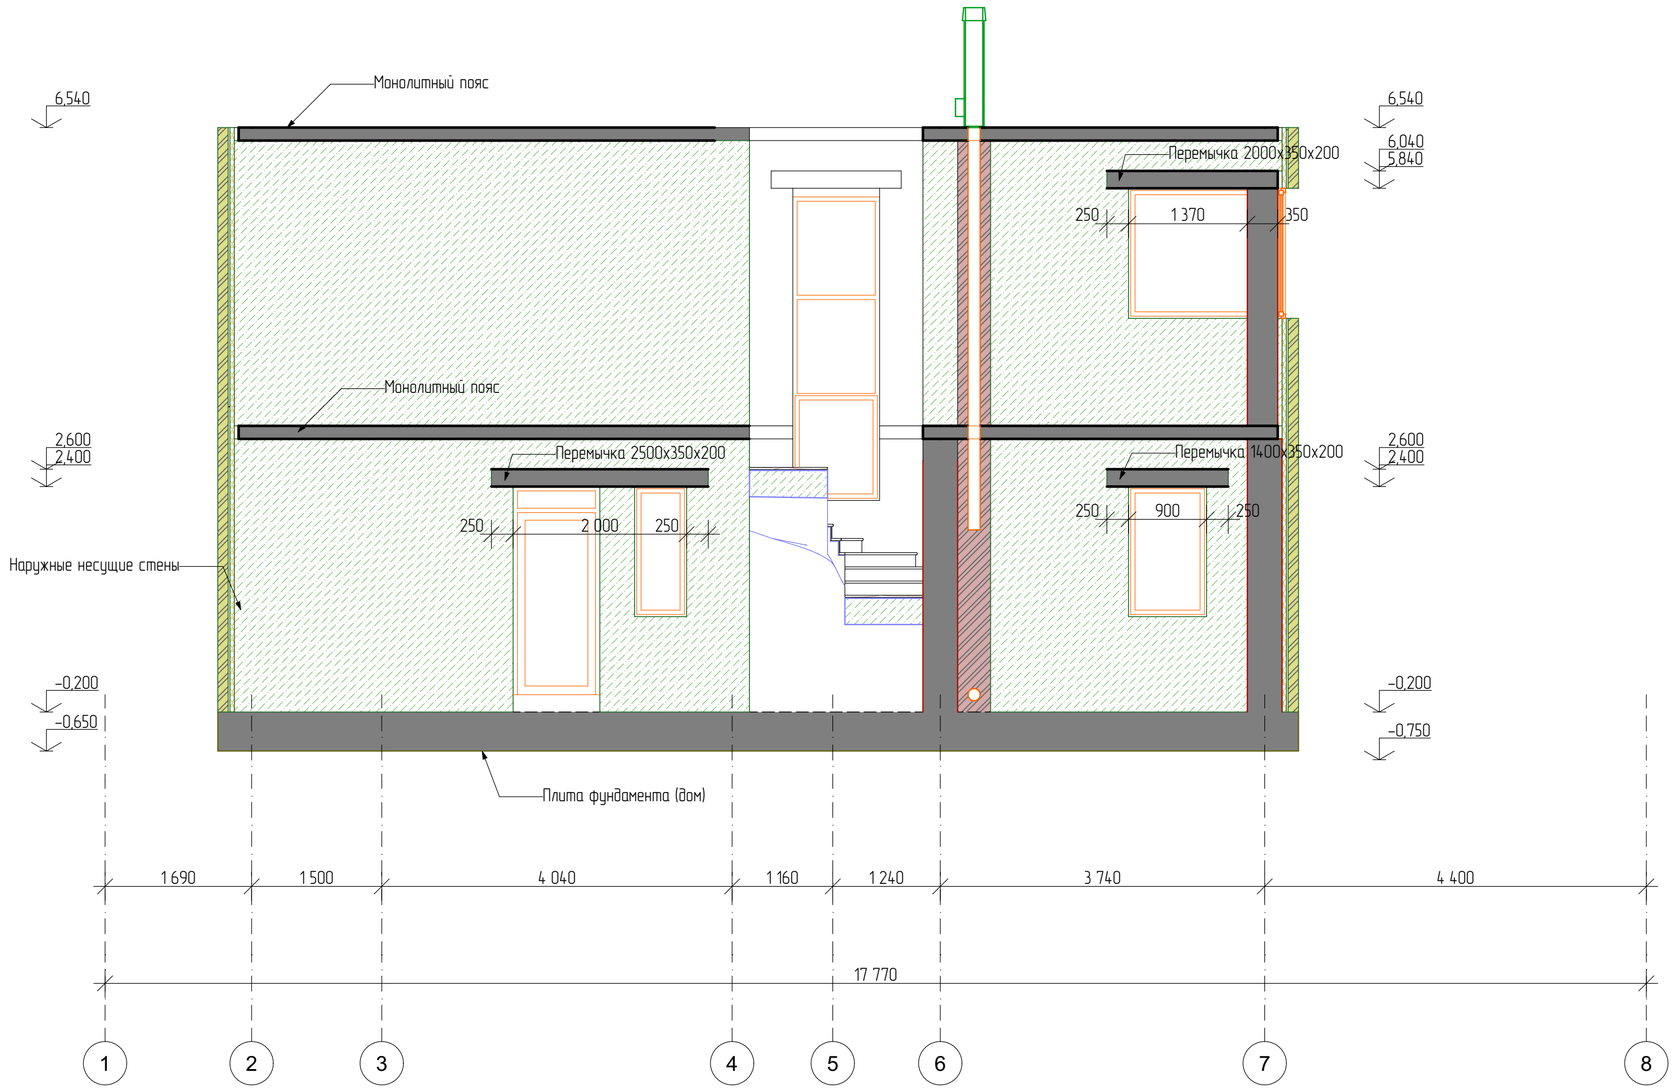

						#ID Проекта	
						кадастровый номер Россия	
Изм.	Колуч.	Лист	№Док.	Подп.	Дата		
Разраб.						Индивидуальный жилой дом	Стадия: #Стадия Проекта; Лист: 88; Листов:
ГАП							
Р6							

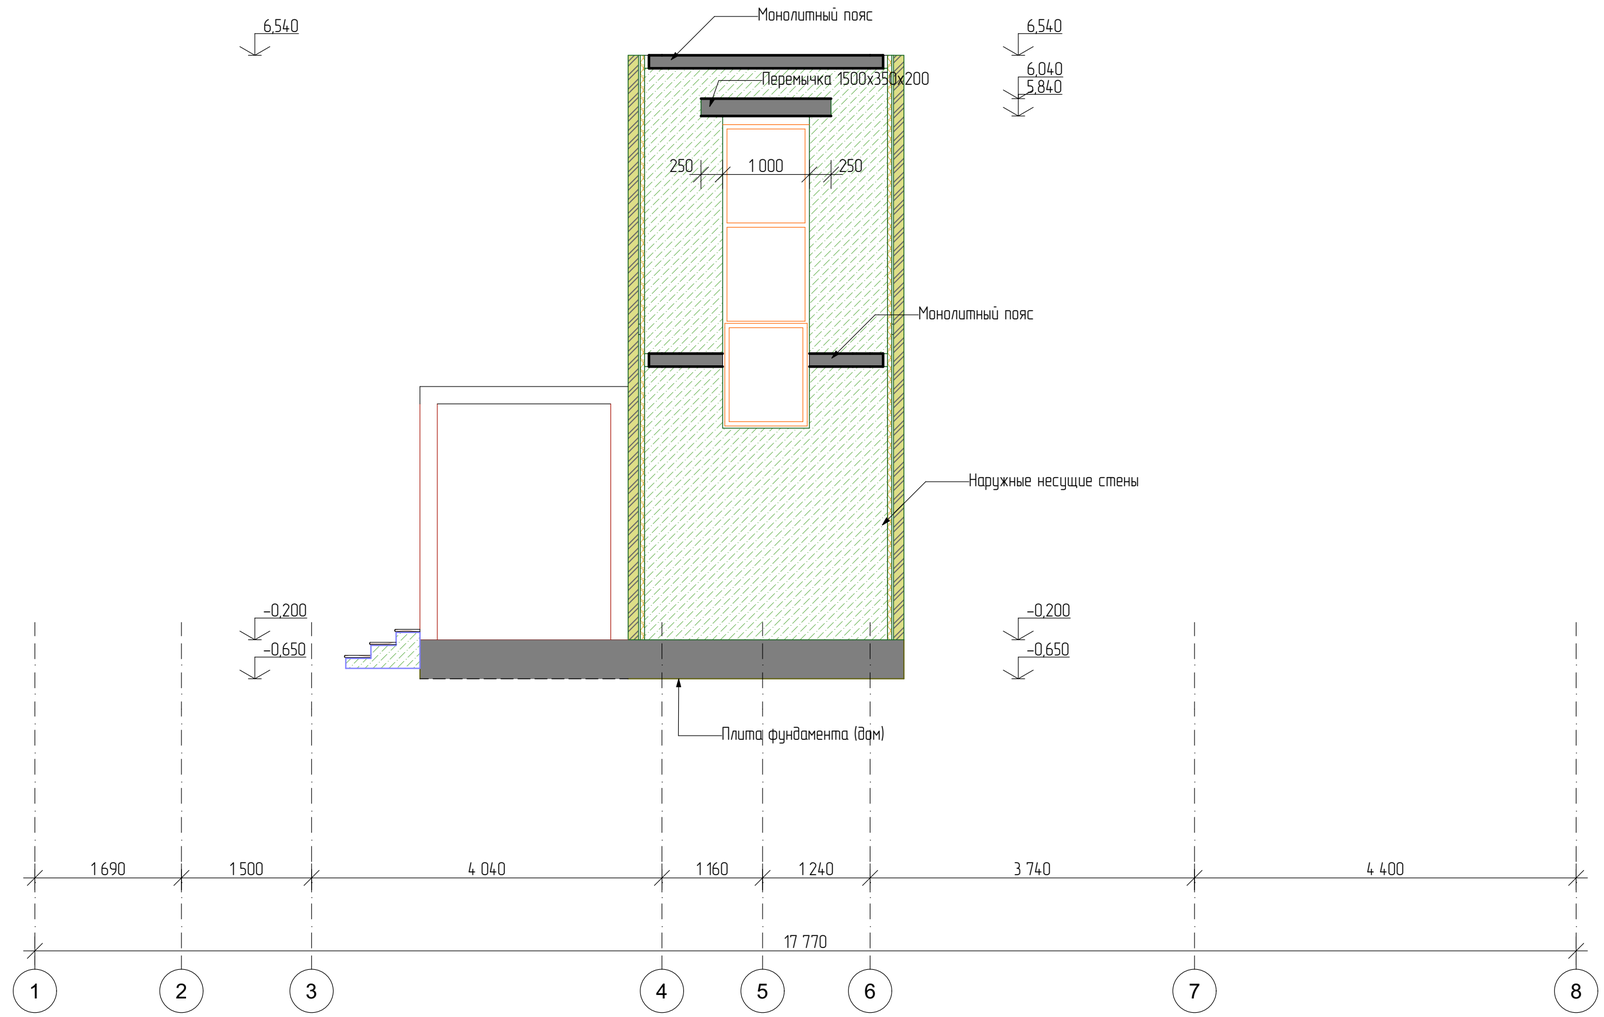

						#ID Проекта	
						кадастровый номер Россия	
Изм.	Кол.уч.	Лист	№Док.	Подп.	Дата		
Разраб.						Индивидуальный жилой дом	Стадия: #Стадия Проекта; Лист: 89; Листов:
ГАП							
Р7							

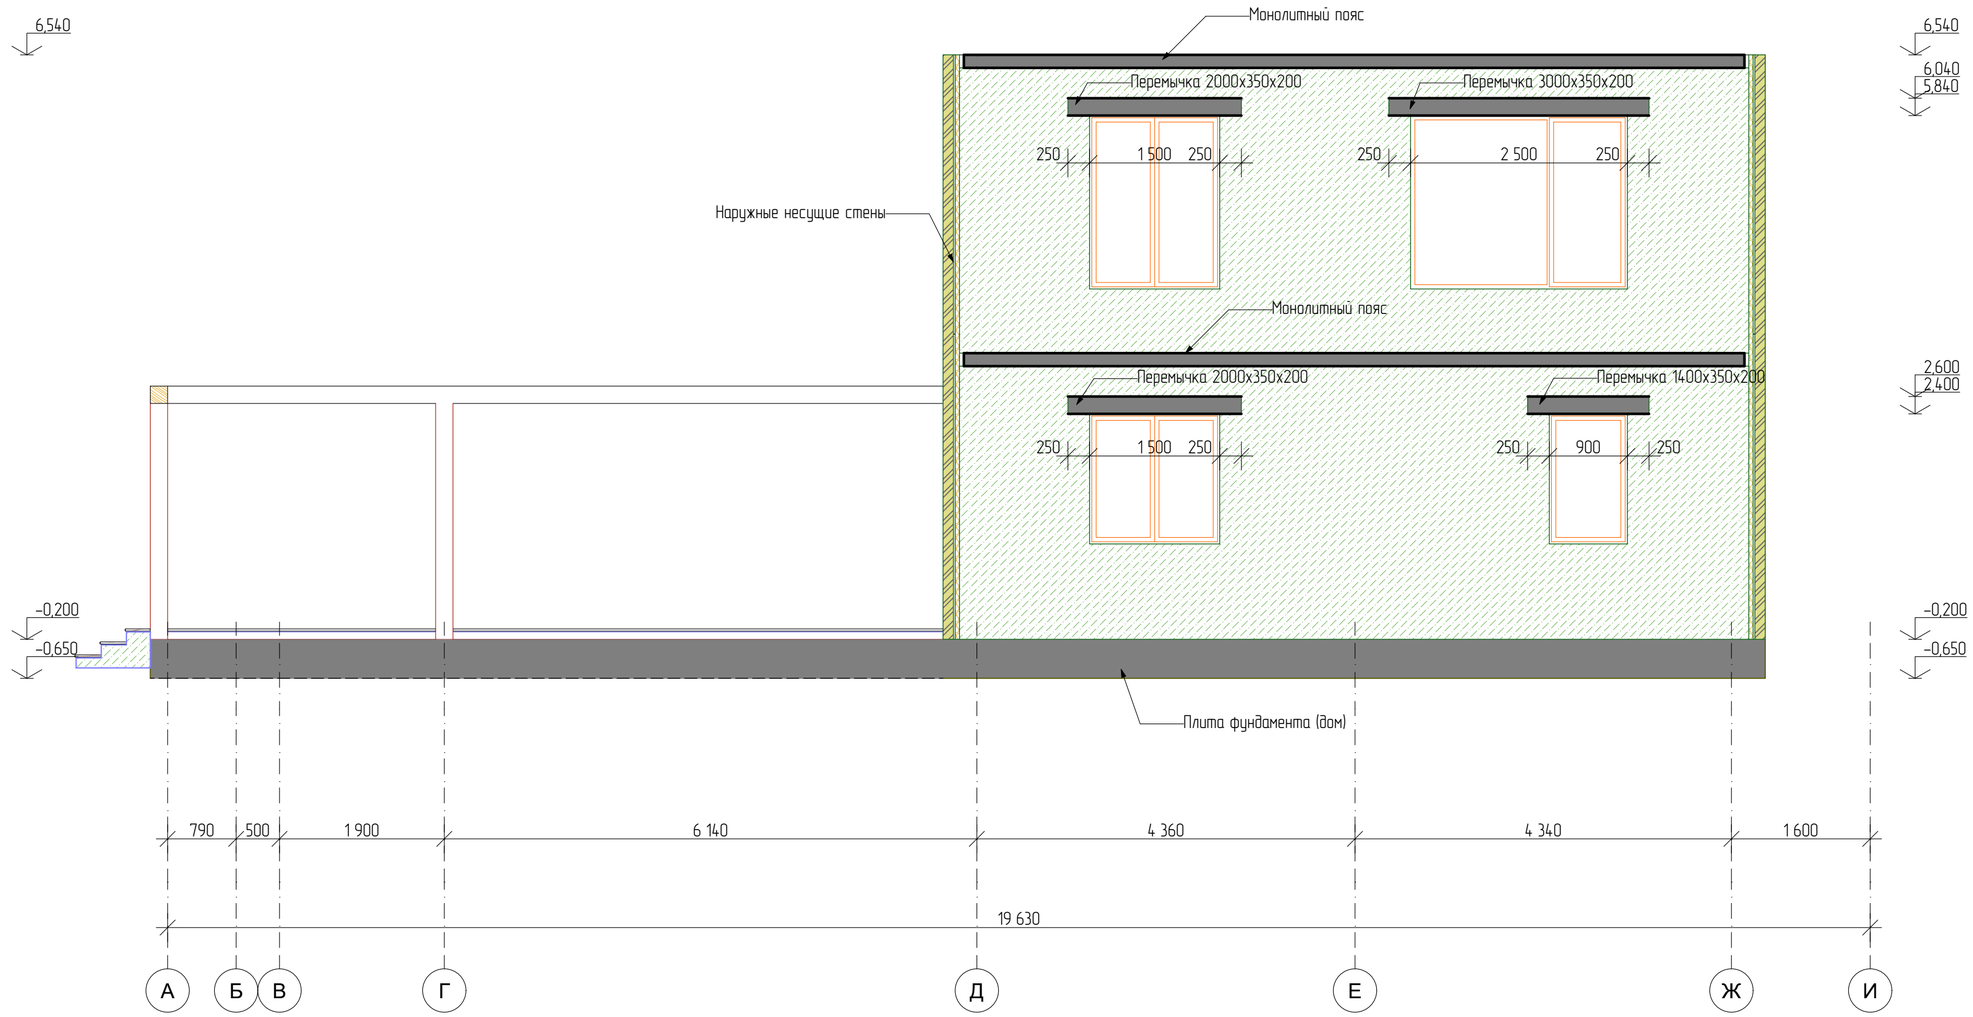

						#ID Проекта	
						кадастровый номер Россия	
Изм.	Колуч.	Лист	№Док.	Подп.	Дата		
Разраб.						Индивидуальный жилой дом	Стадия: #Стадия Проекта; Лист: 90; Листов:
ГАП							
Р8							

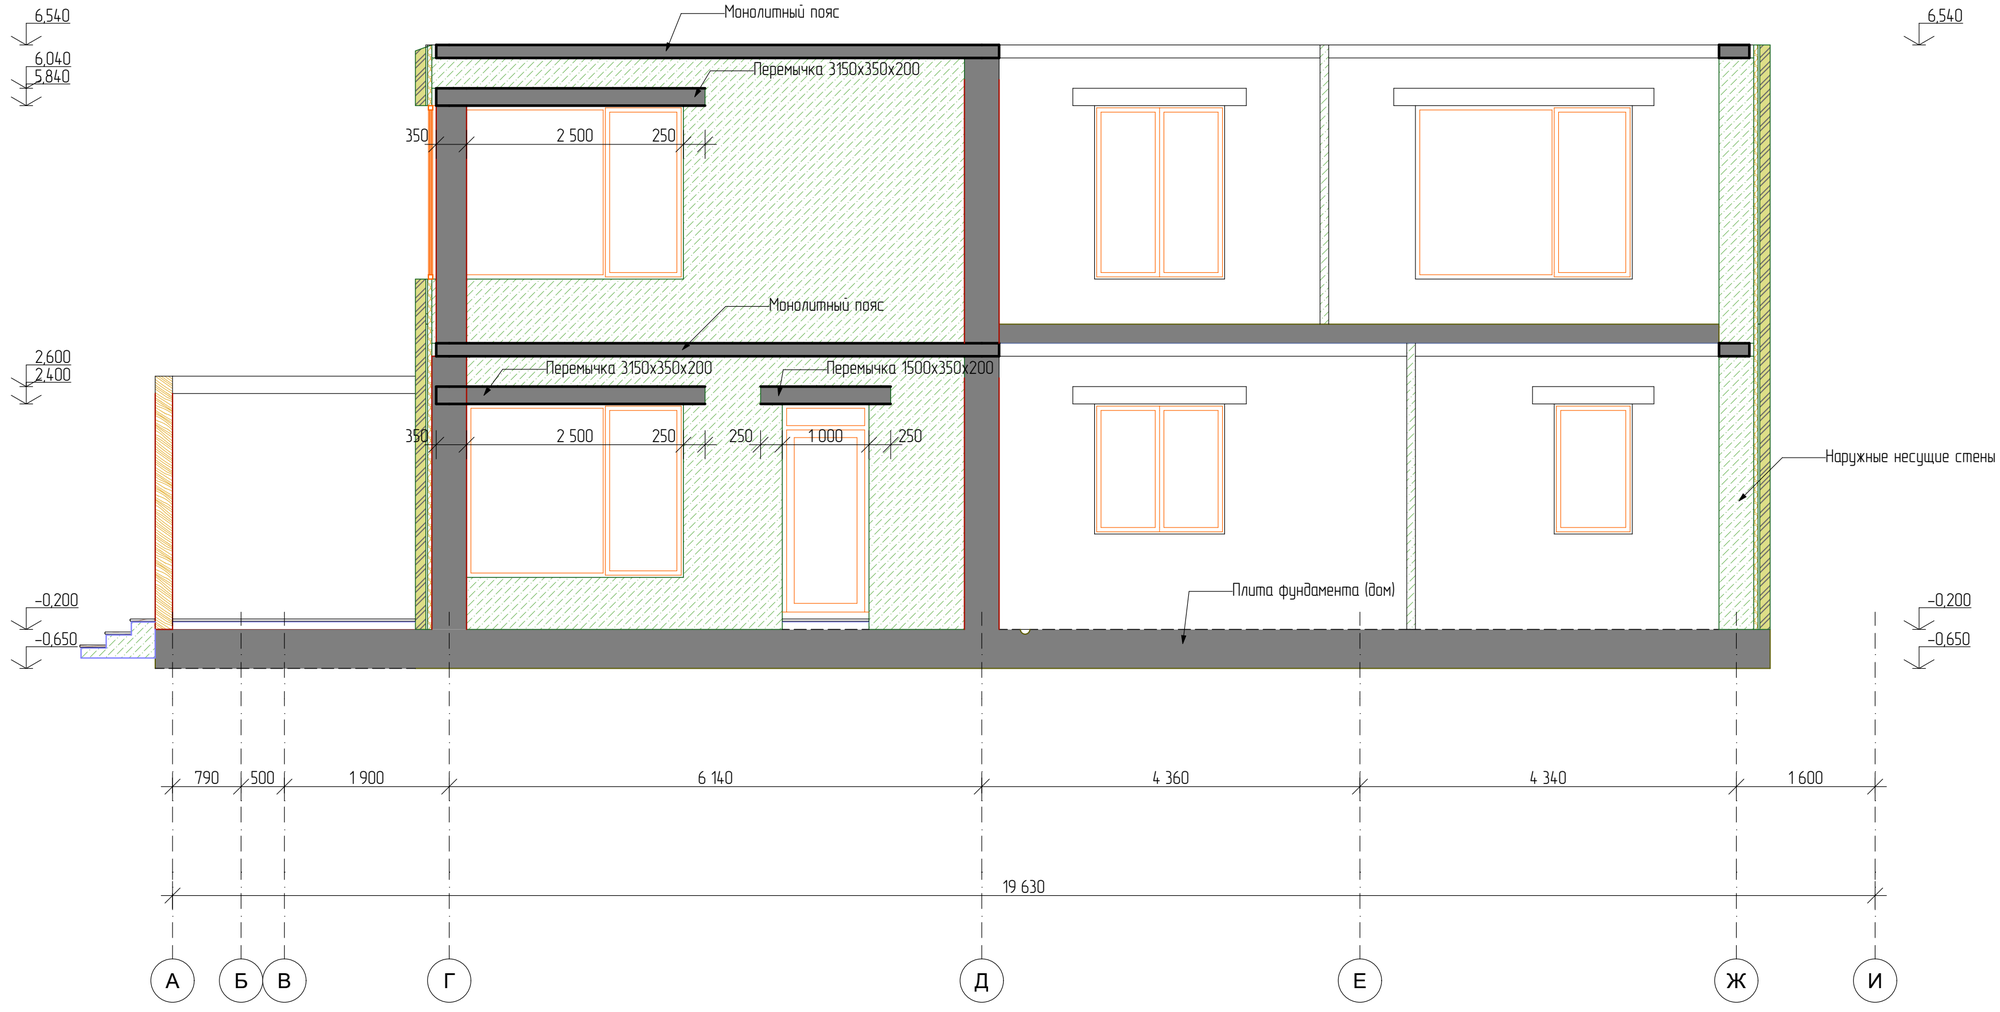

						#ID Проекта	
						кадастровый номер Россия	
Изм.	Колуч.	Лист	№Док.	Подп.	Дата		
Разраб.						Индивидуальный жилой дом	Стадия: #Стадия Проекта; Лист: 91; Листов:
ГАП							
Р9							

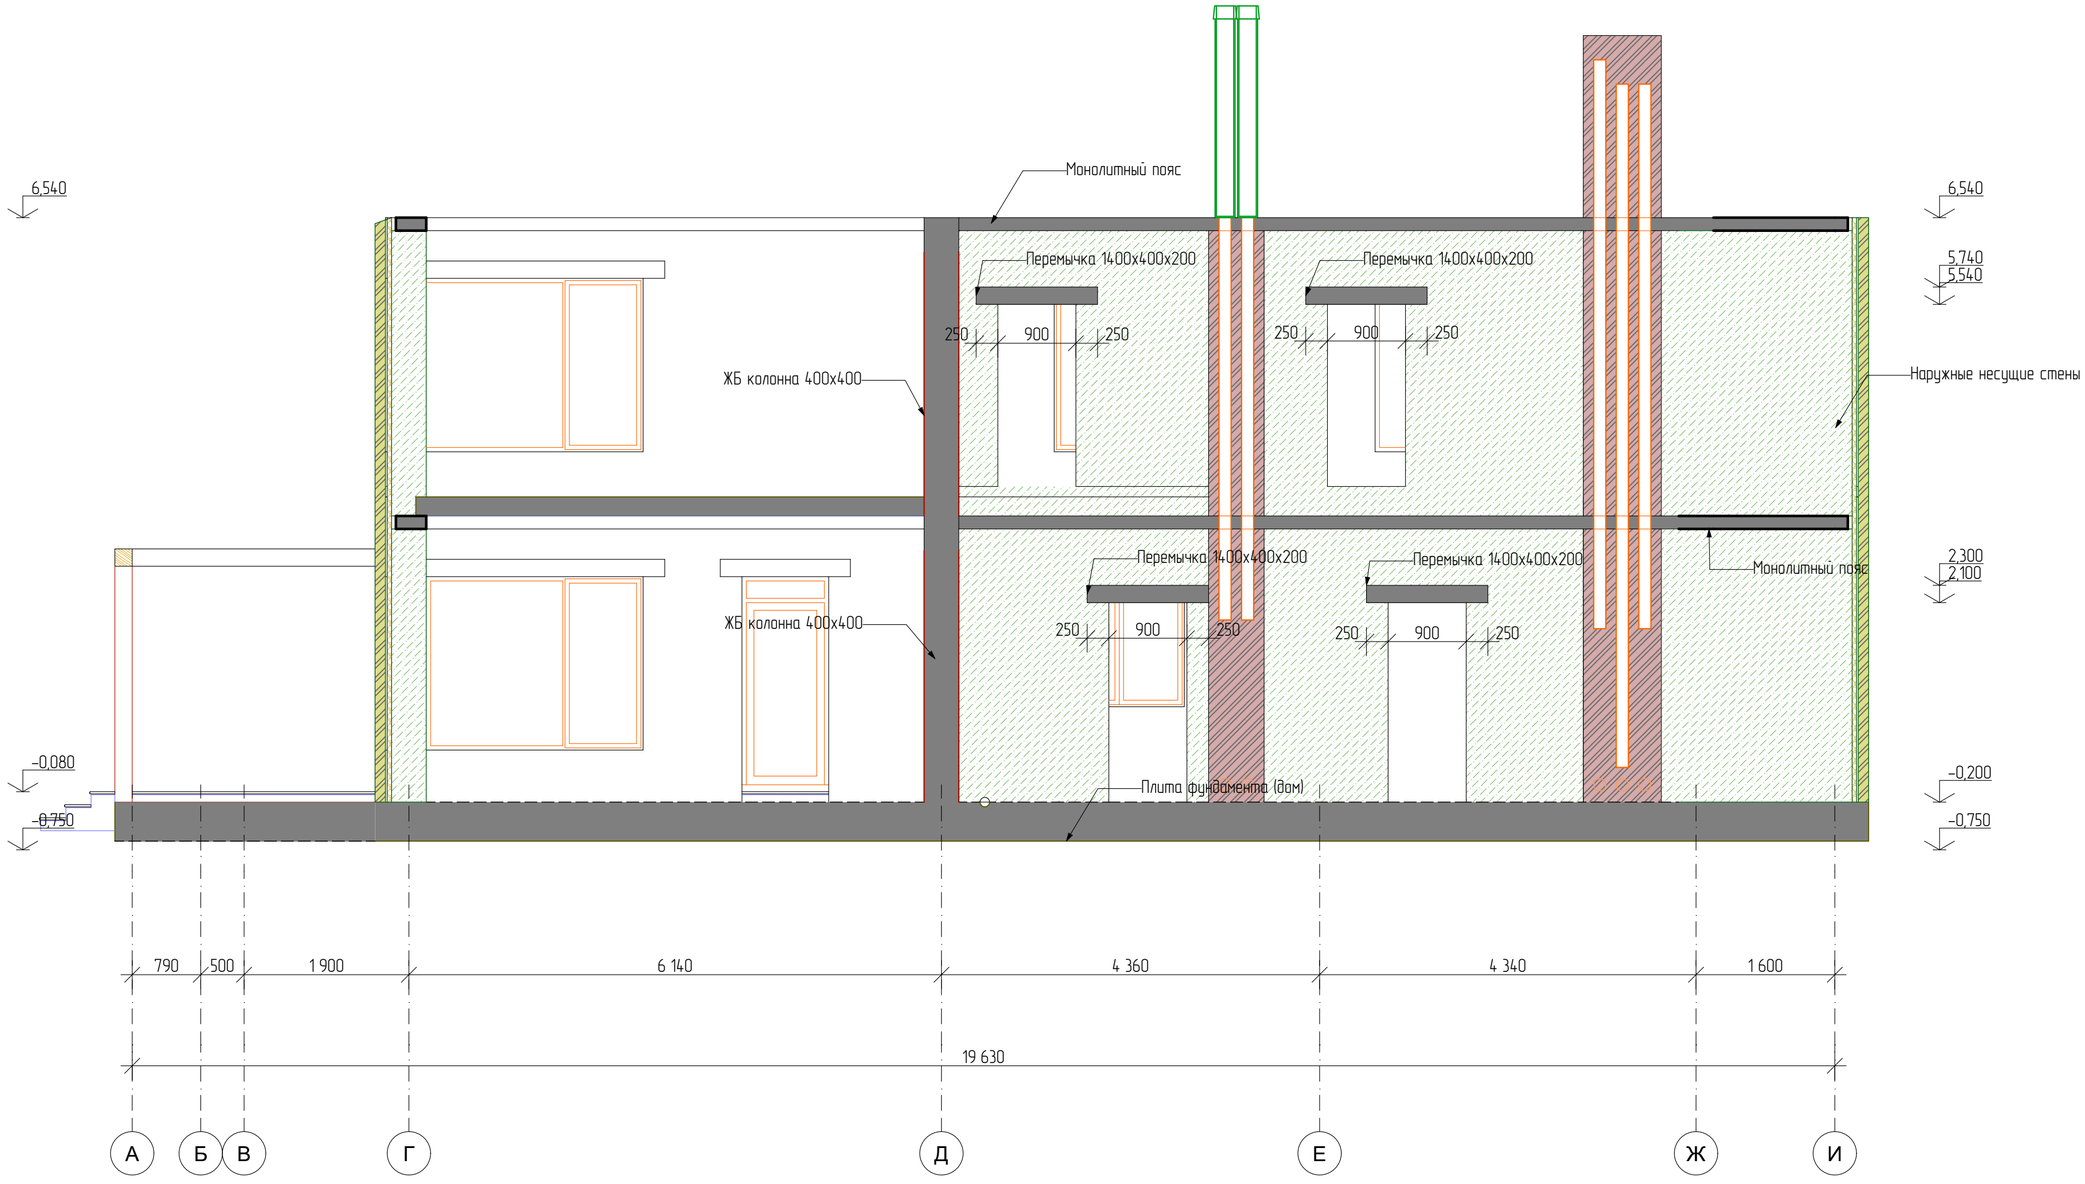

						#ID Проекта	
						кадастровый номер Россия	
Изм.	Кол.уч.	Лист	№Док.	Подп.	Дата		
Разраб.						Индивидуальный жилой дом	Стадия: #Стадия Проекта; Лист: 92; Листов:
ГАП							
Р10							

						#ID Проекта	
						кадастровый номер Россия	
Изм.	Кол.уч.	Лист	№Док.	Подп.	Дата		
Разраб.						Индивидуальный жилой дом	Стадия: #Стадия Проекта; Лист: 93; Листов:
ГАП							
						Р11	

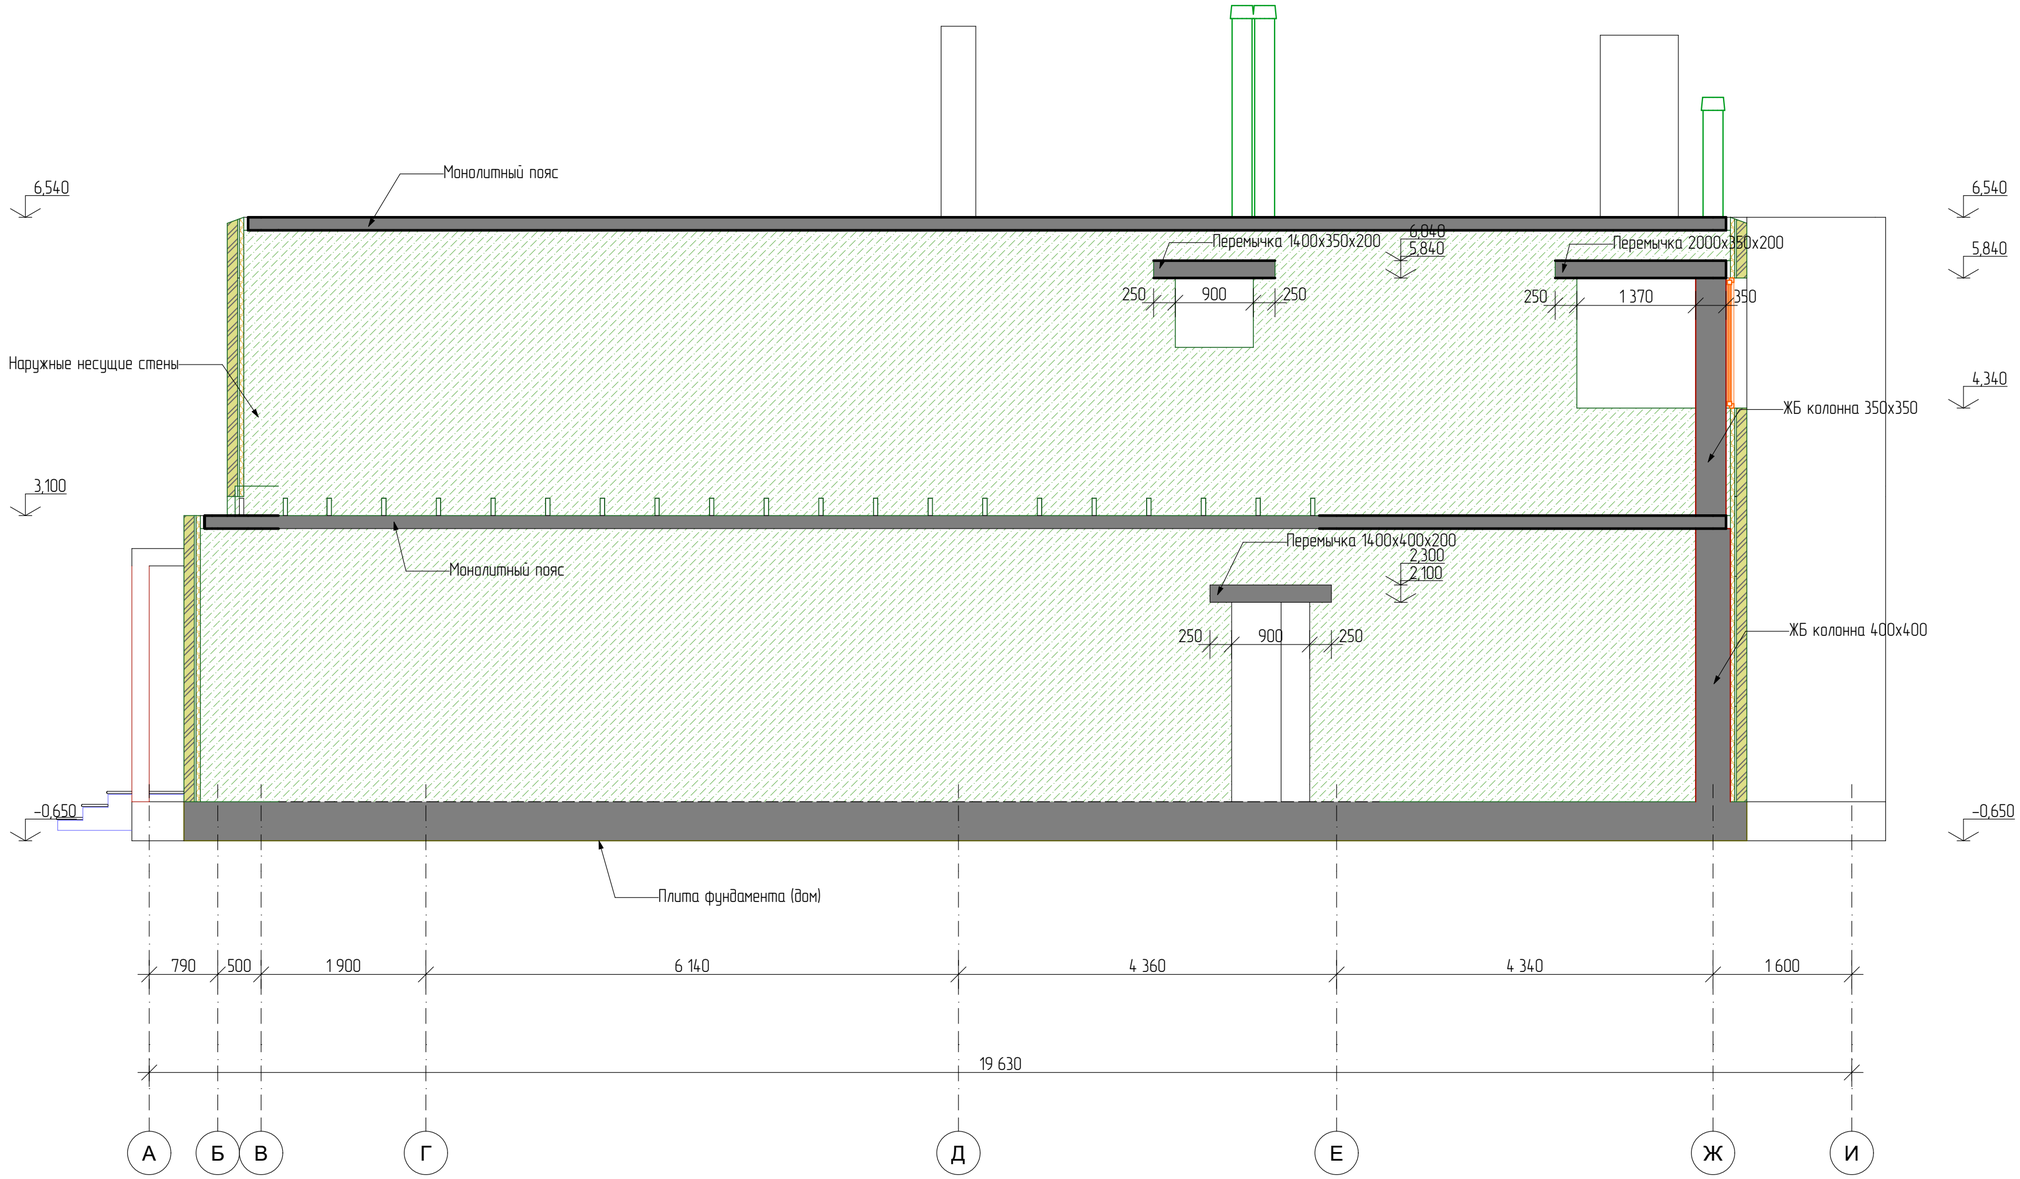

						#ID Проекта	
						кадастровый номер Россия	
Изм.	Колуч.	Лист	№Док.	Подп.	Дата		
Разраб.						Индивидуальный жилой дом	Стадия: #Стадия Проекта; Лист: 94; Листов:
ГАП							
Р12							

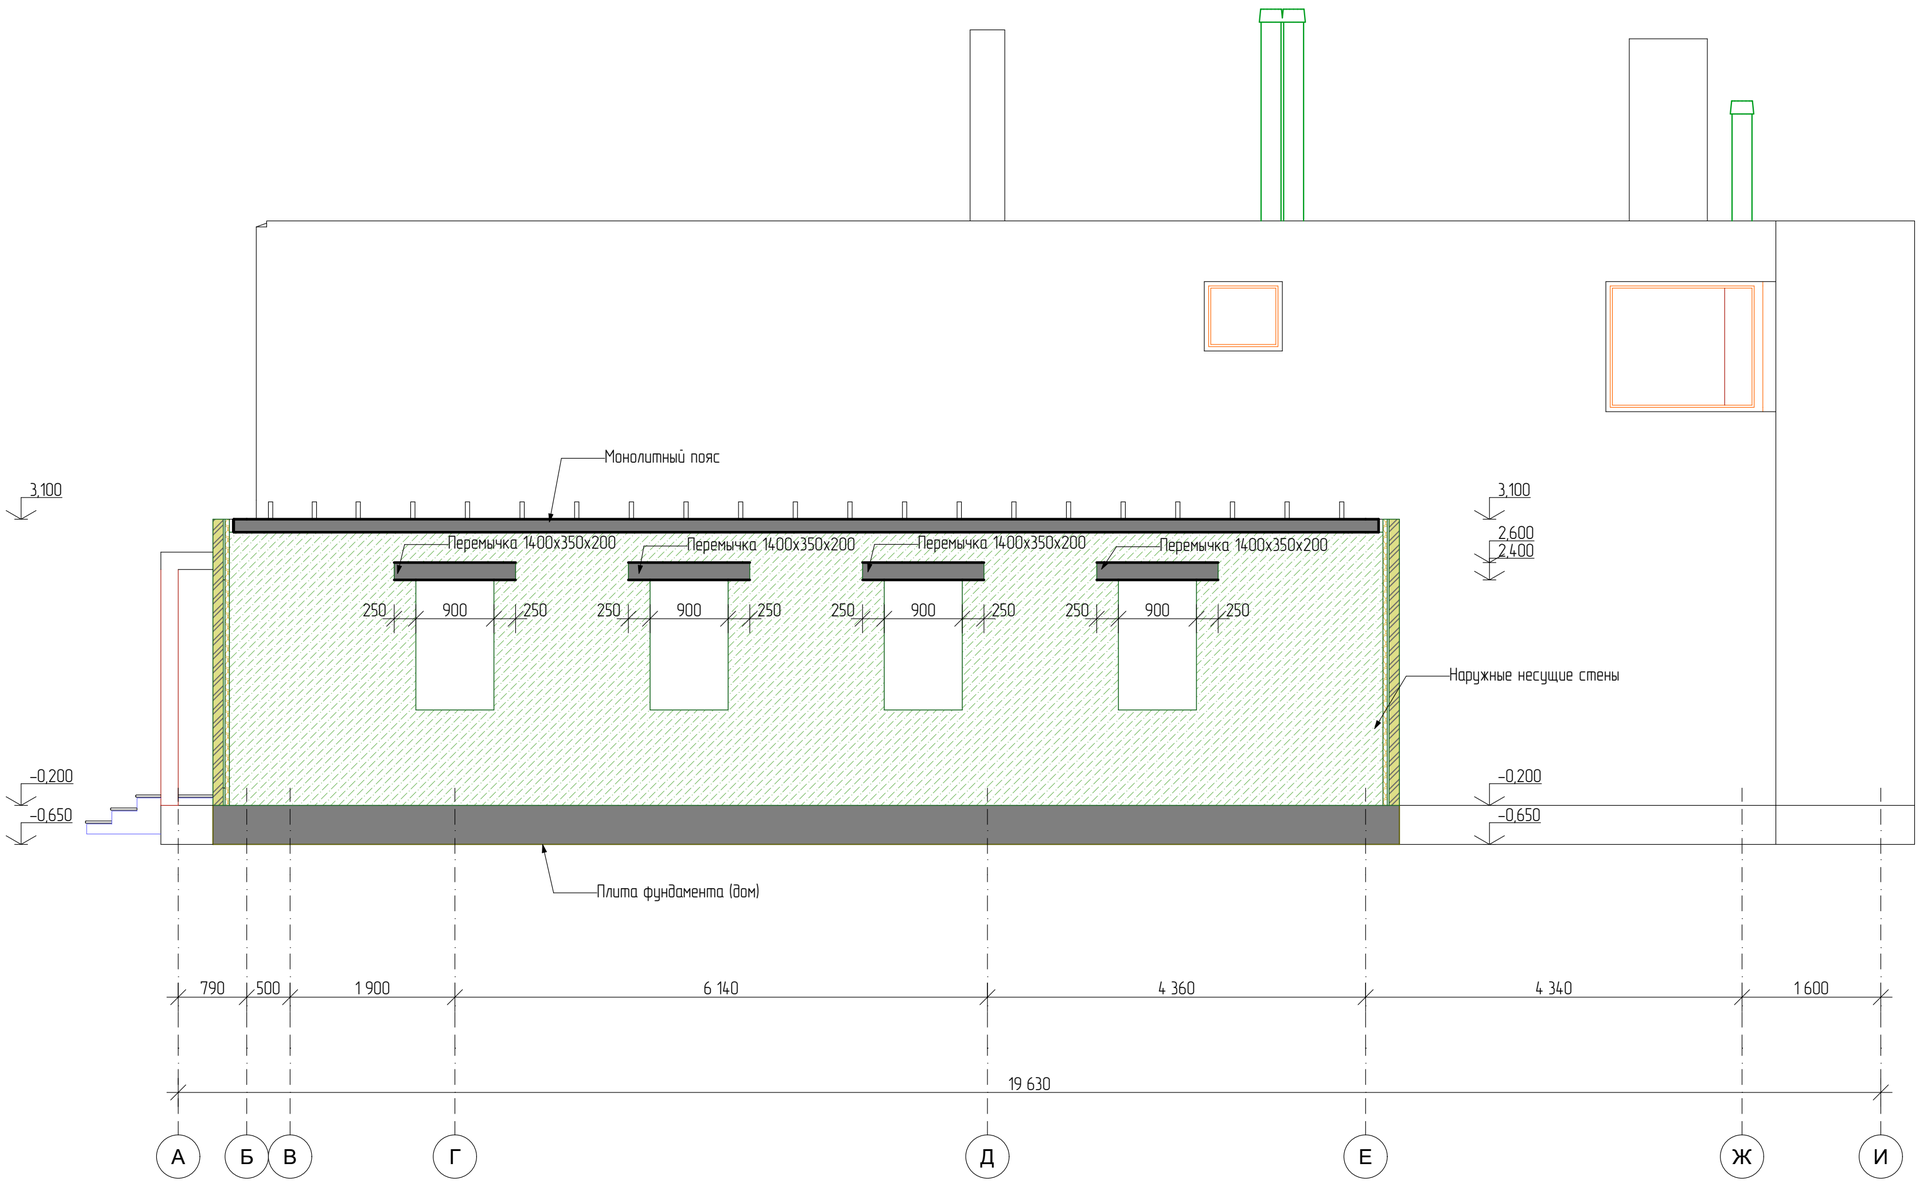

						#ID Проекта	
						кадастровый номер Россия	
Изм.	Кол.уч.	Лист	№Док.	Подп.	Дата		
Разраб.						Индивидуальный жилой дом	Стадия: #Стадия Проекта; Лист: 95; Листов:
ГАП							
Р13							