ПРОЕКТНАЯ ДОКУМЕНТАЦИЯ

Индивидуальный жилой дом

кадастровый номер Россия



Разработал Салыкова В.

2024

Ведомость листов	
Наименование	Лист
Обложка	
Общие данные	02
Сводная ведомость материалов	03
Схема организации участка	04
3D Виды	05
План фундамента	06
План фундамента с закладными	07
План 1 этажа	08
Маркировочный план 1 этаж	09
Каталог дверных проемов	10
Каталог оконных проемов	11
Разрез 1 - 1	12
Разрез 2 - 2	13
Разрез по стене	14
План перекрытий на отм 3,050	15
Монолитный пояс на отм 2,800	16
План кровли на отм. 3,312	17
Схема расположения стропил на отм. 3...	18
3Д Вид стропильной системы	19
План расстановки мебели 1 этаж	20
Экспликация помещений 1- го этажа	21
Фасад в осях 1-2	22
Фасад в осях В-А	23
Фасад в осях А-В	24
Фасад в осях 2-1	25

Изм.	Кол.уч.	Лист	№Док.	Подп.	Дата	кадастровый номер Россия			
Разраб.		Салыкова В				Индивидуальный жилой дом	Стадия	Лист	Листов
							#Стадия Проекта	02	
						Общие данные			

Ведомость перекрытия	
Наименование	Объем

Балка деревянная 200х50	0,96

ИКК-03 Кровля	
Наименование	Площадь, м2
Кровля	53,32

ИКК-03 Стропильная система	
Наименование	Объем, м3
Коньковый брус 200х100	0,18
Мауэрлат 100х200	0,18
Стропильная нога 200х50	0,90

ВЕДОМОСТЬ НА МОНОЛИТНЫЙ ПОЯС 1-ГО ЭТАЖА	
Наименование	Объем, м3
	3,50
Монолитный пояс из U-блоков	3,50


ВЕДОМОСТЬ БЛОКА ДЛЯ СТЕН	
ID Элемента	Объем, м3
Несущие 400мм	45,98
Перегородки 100мм	2,50


ВЕДОМОСТЬ НА УТЕПЛИТЕЛЬ ДЛЯ СТЕН, ПОЛА ПЕРВОГО ЭТАЖА, РОСТВЕРКА			
Наименование	**Компоненты**		
	Толщина [м]	**Объем [м3]**	**Площадь [м2]**
Изоляция - Минеральная Жесткая			
	20	0,12	5,83
	100	3,38	33,80
	200	8,42	42,12
Изоляция - ЭППС			
	50	0,52	10,33
	100	4,63	46,26


Отделочные материалы		
Наименование	**Компоненты**	
	Толщина [м]	**Площадь [м2]**
Штукатурка - фасадная		
	10	117,22

ВЕДОМОСТЬ БЕТОНА	
Наименование	Объем, м3
Плита фундамента	21,47

Изм.	Кол.уч.	Лист	№Док.	Подп.	Дата	кадастровый номер Россия			
Разраб.		Салыкова Е.				Индивидуальный жилой дом	Стадия	Лист	Листов
							#Стадия Проекта	03	
						Сводная ведомость материалов			

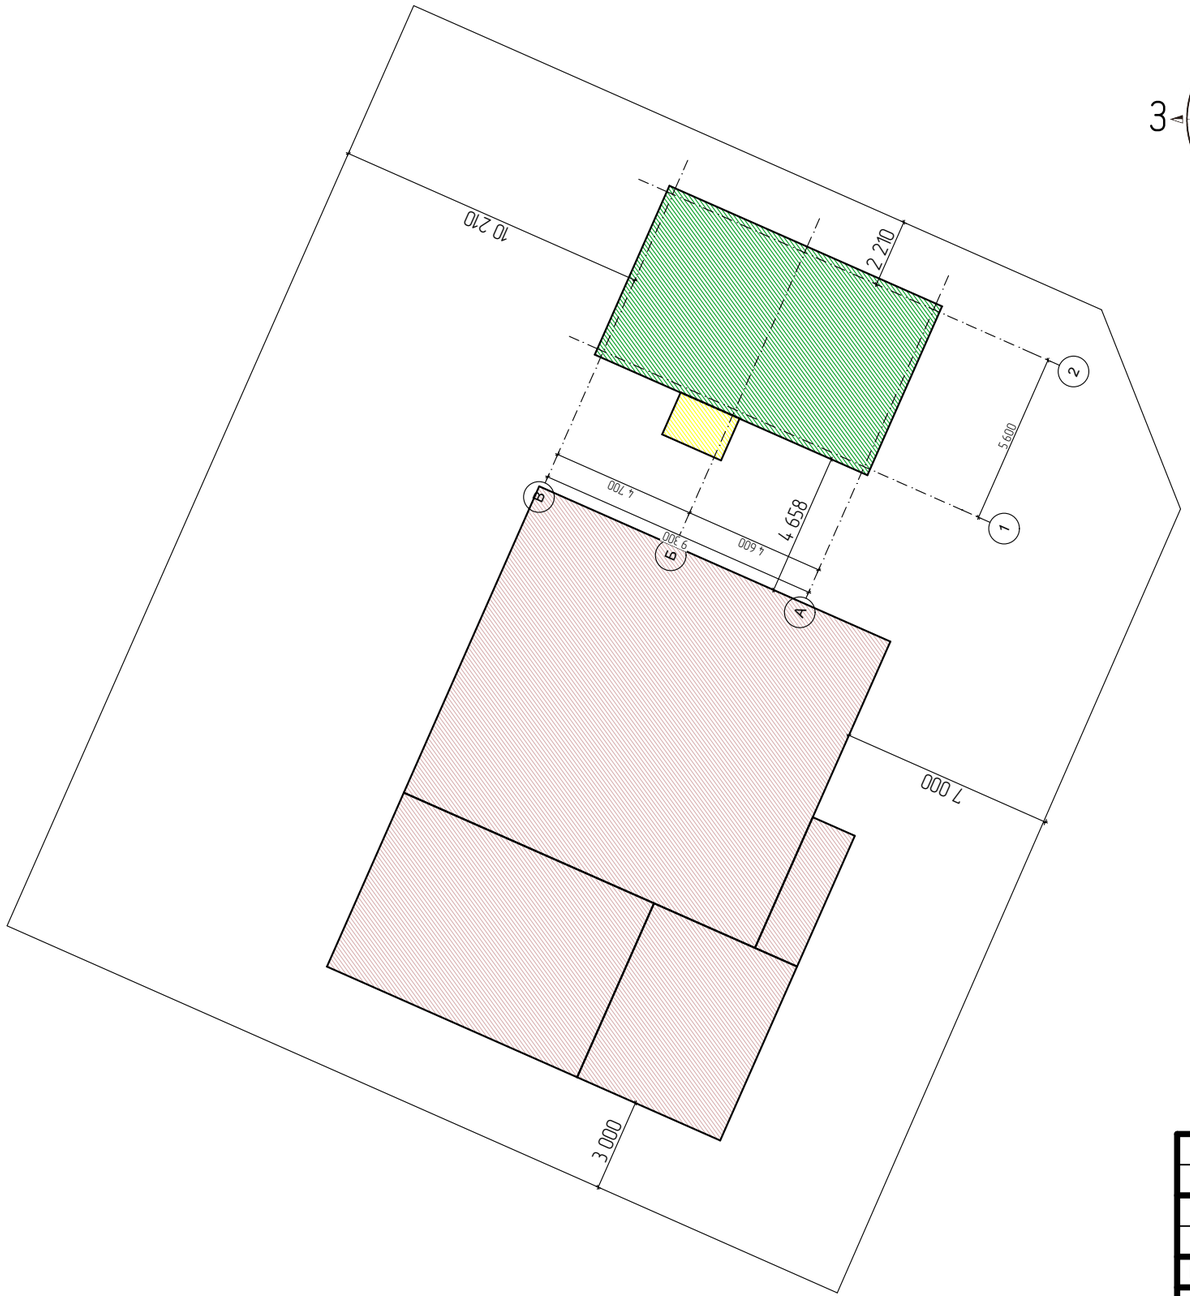

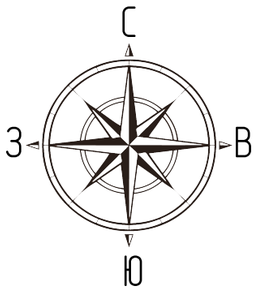

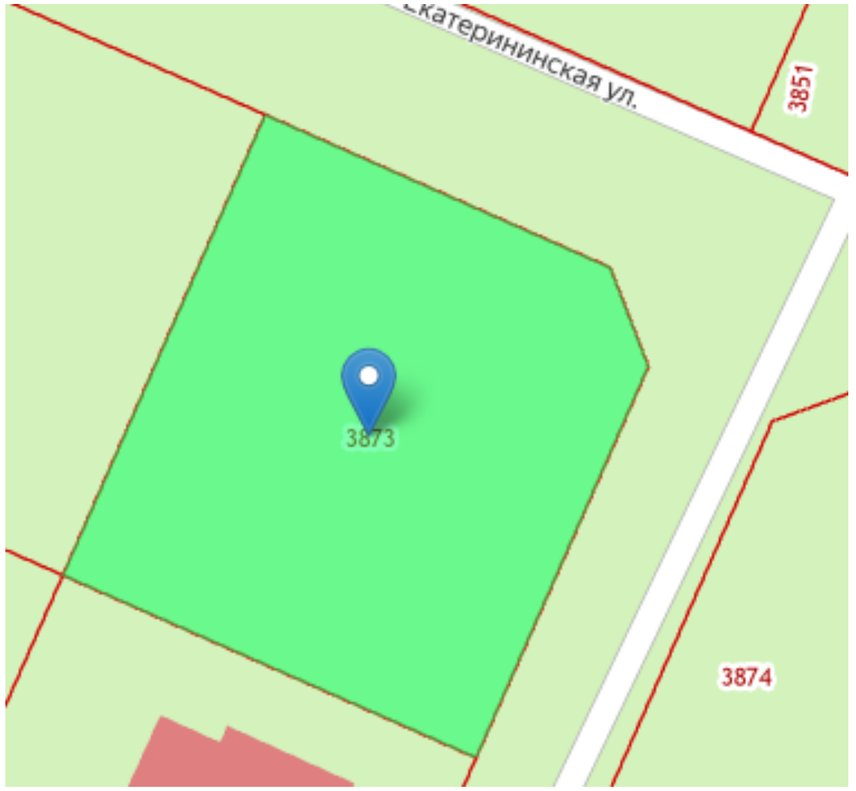

Баня


Дом


Крыльцо

Изм.	Кол.уч.	Лист	№Док.	Подп.	Дата	
Разраб.		Салыкова В.				

кадастровый номер Россия


Индивидуальный жилой дом	Стадия	Лист	Листов
	#Стадия Проекта	04	
Схема организации участка			

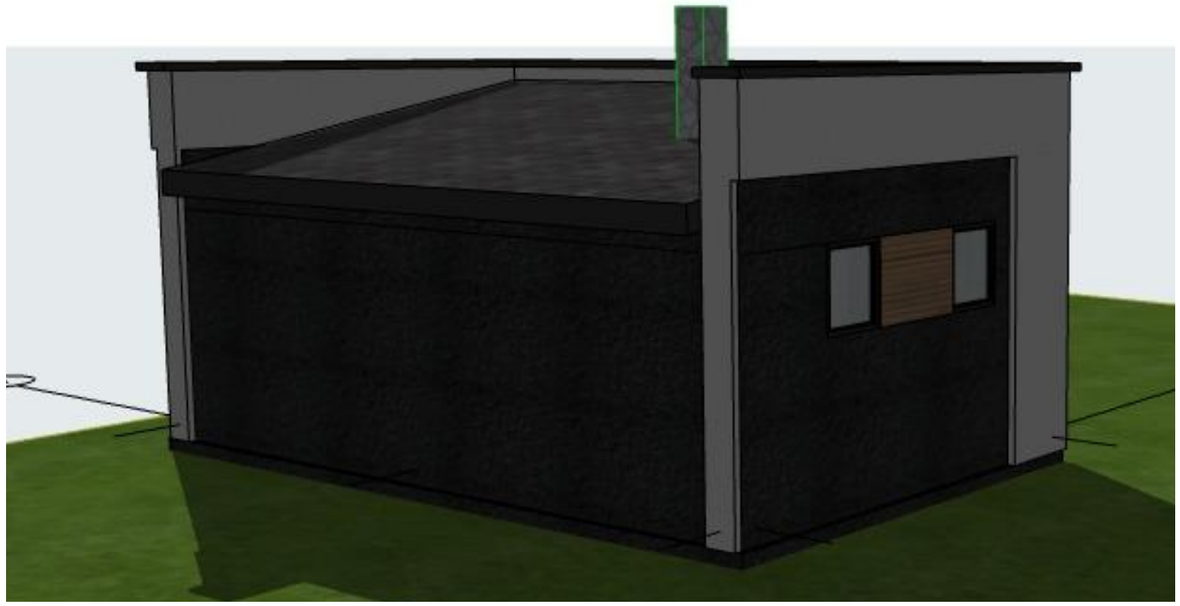

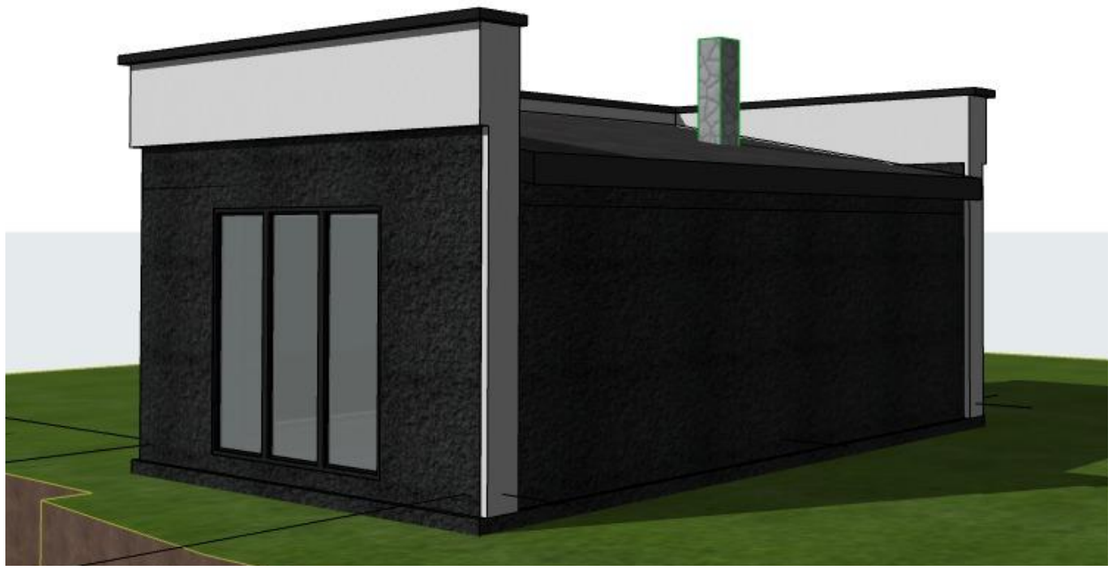




						кадастровый номер Россия		
Изм.	Кол.уч.	Лист	№Док.	Подп.	Дата			
Разраб.		Салыкова Е.				Индивидуальный жилой дом	Стадия	Лист	Листов
							#Стадия Проекта	05	
						3D Виды			

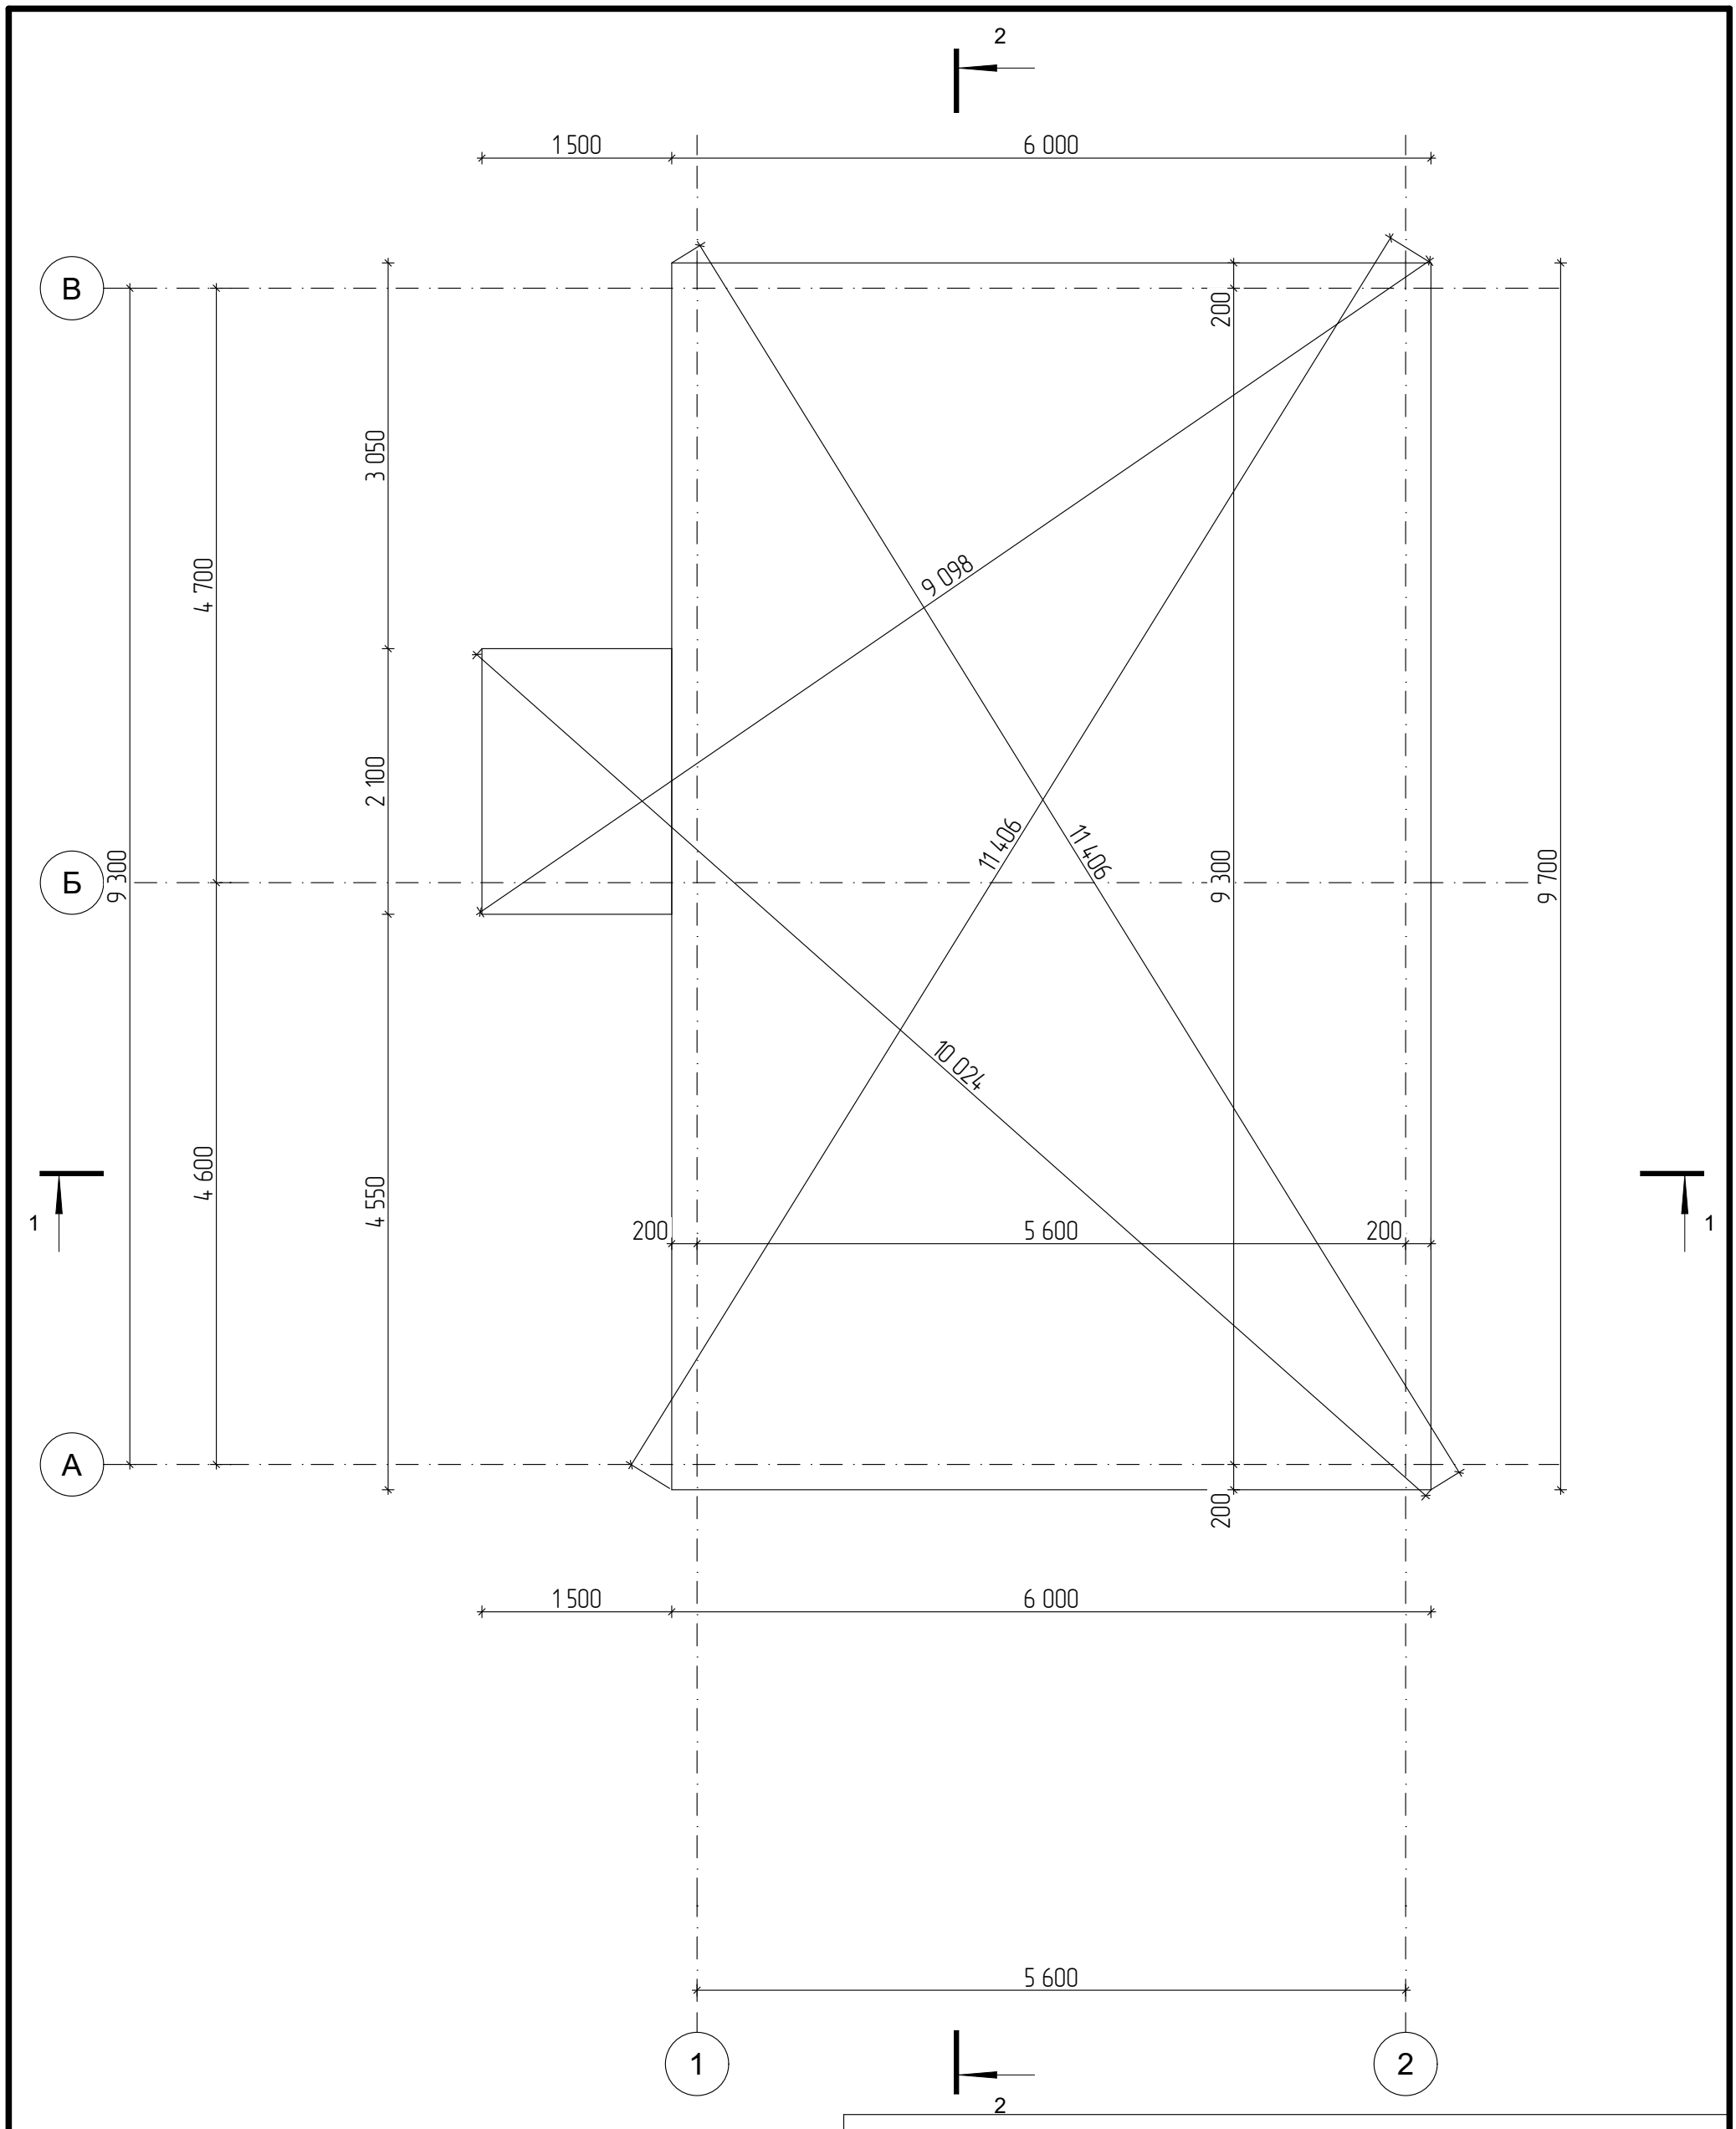


ВЕДОМОСТЬ БЕТОНА

Наименование	Объем, м3
Плита фундамента	21,47

Изм.	Кол.уч.	Лист	№Док.	Подп.	Дата				
						кадастровый номер Россия			
Разраб.		Салыкова Е.				Индивидуальный жилой дом	Стадия	Лист	Листов
							#Стадия Проекта	06	
						План фундамента			

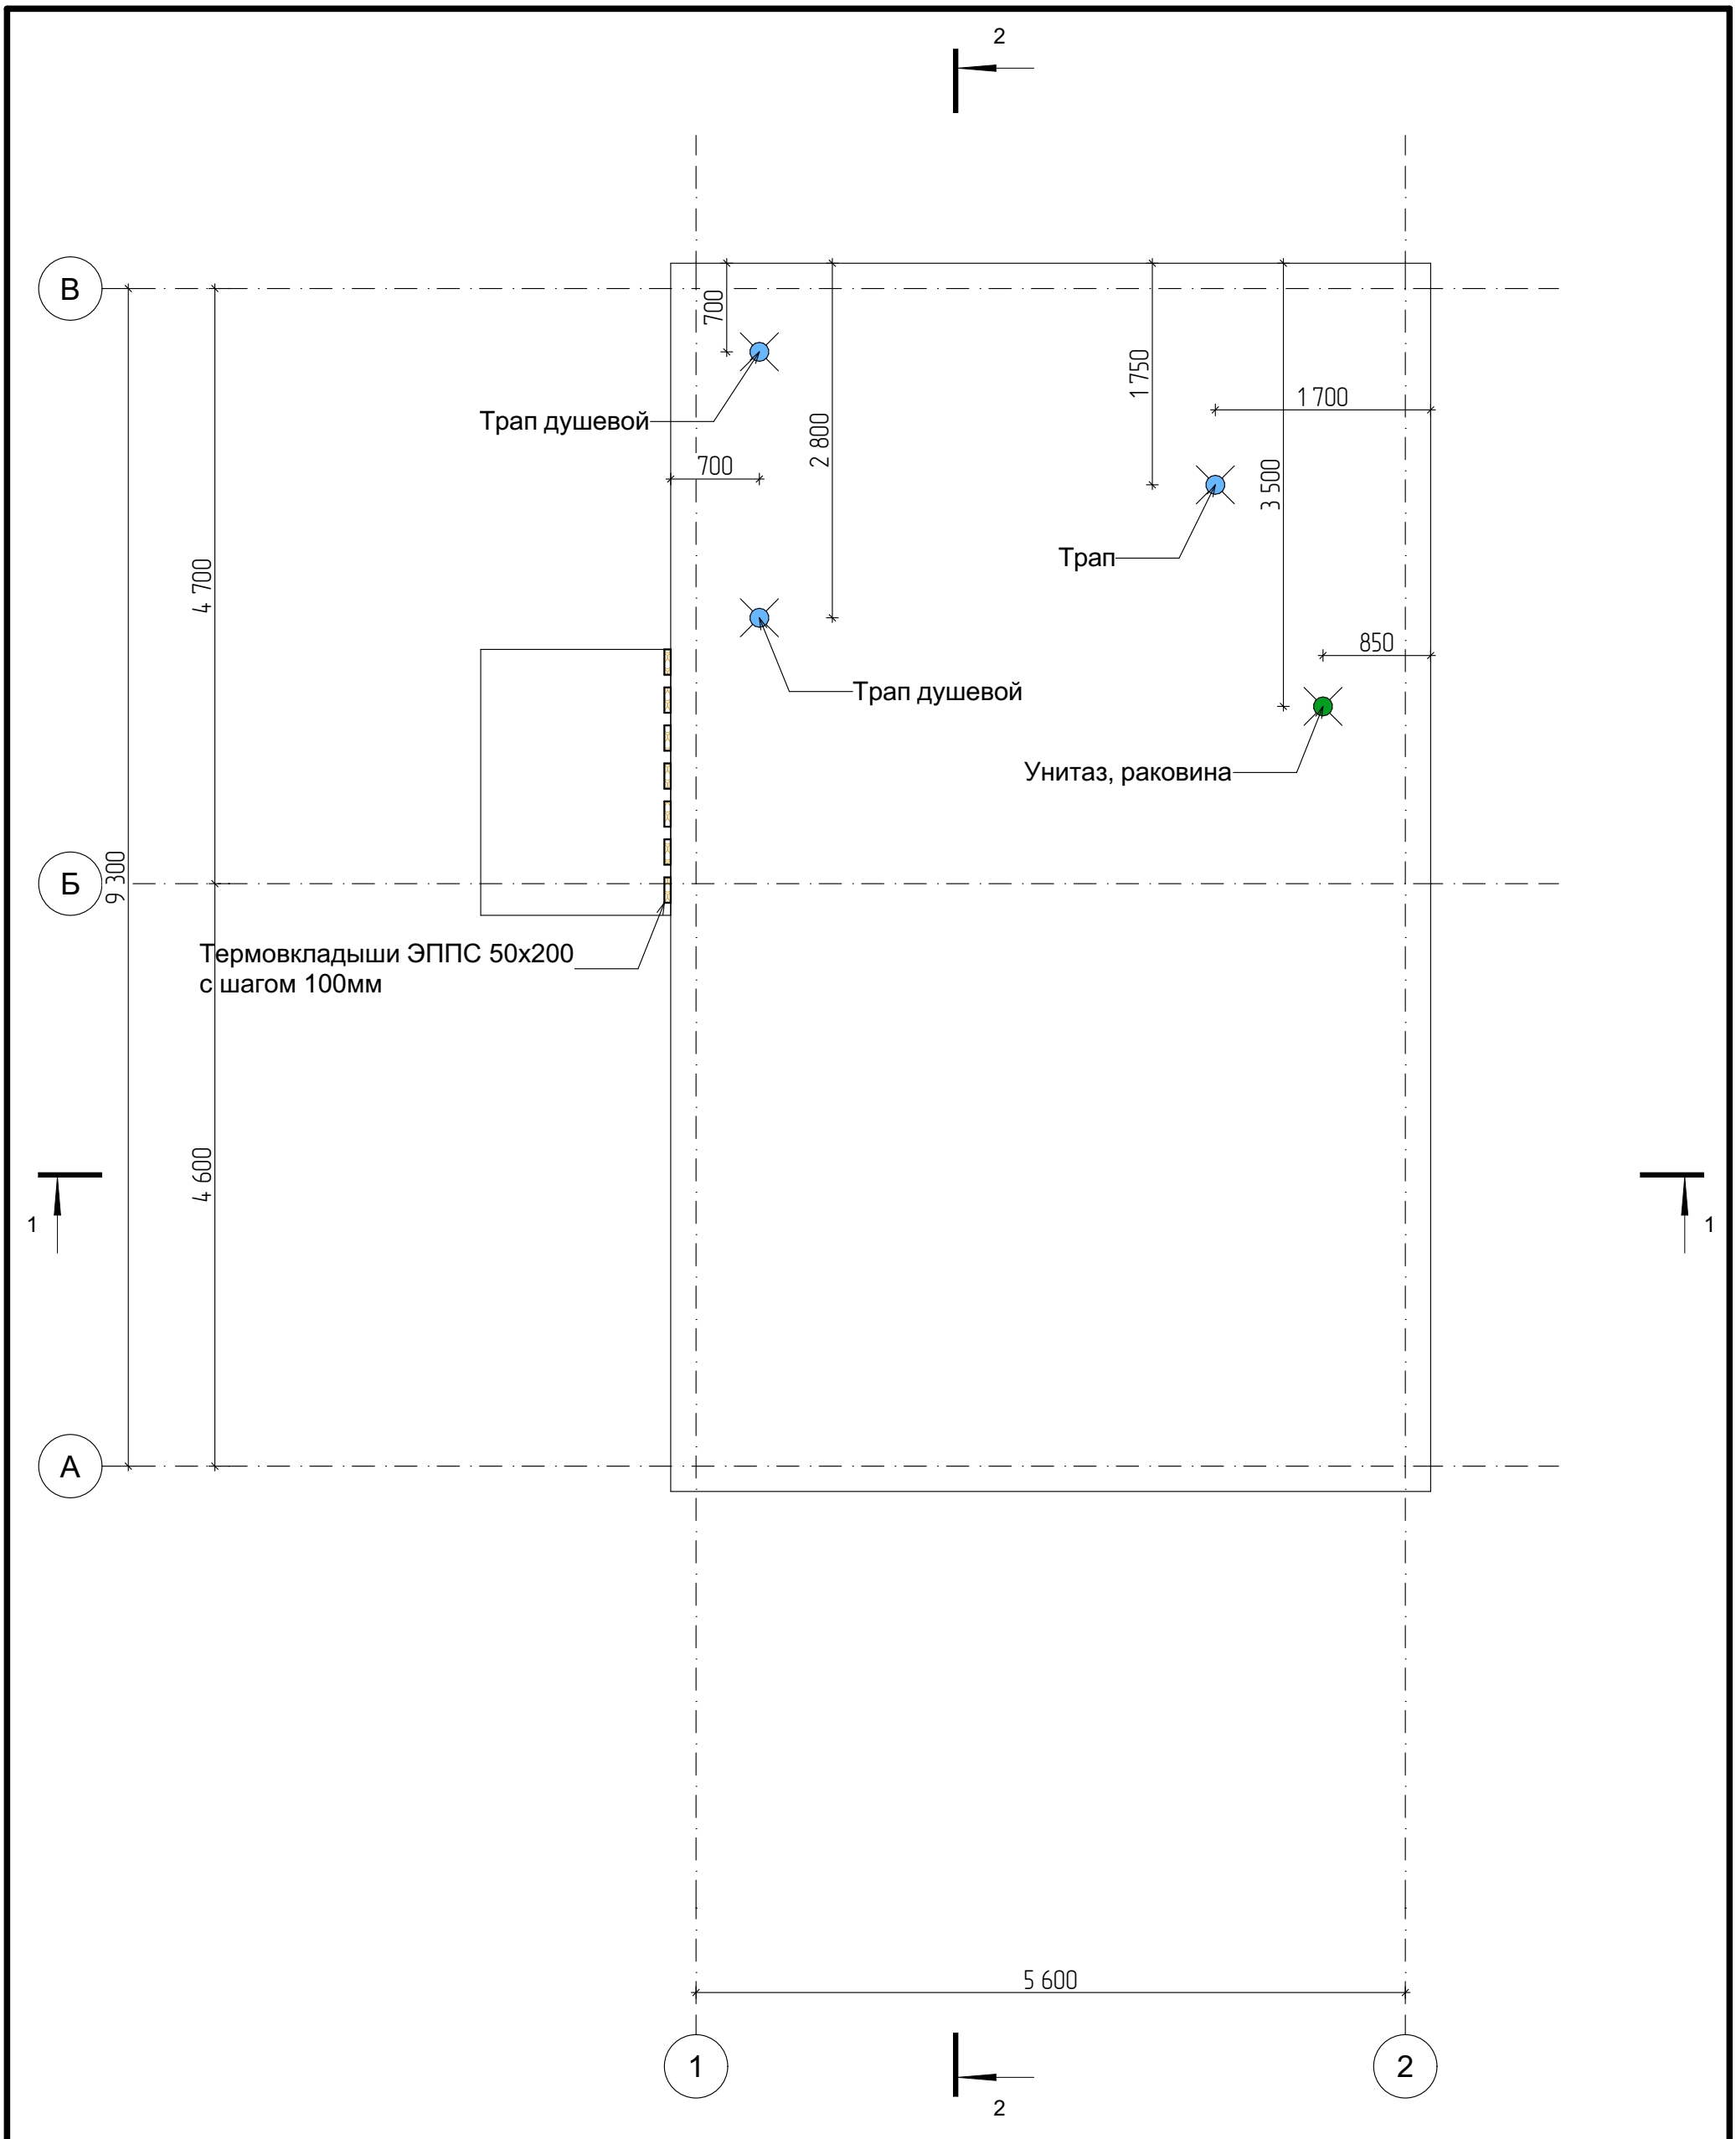


Изм.	Кол.уч.	Лист	№Док.	Подп.	Дата	кадастровый номер Россия			
Разраб.		Салыкова Е.				Индивидуальный жилой дом	Стадия	Лист	Листов
							#Стадия Проекта	07	
						План фундамента с закладными			

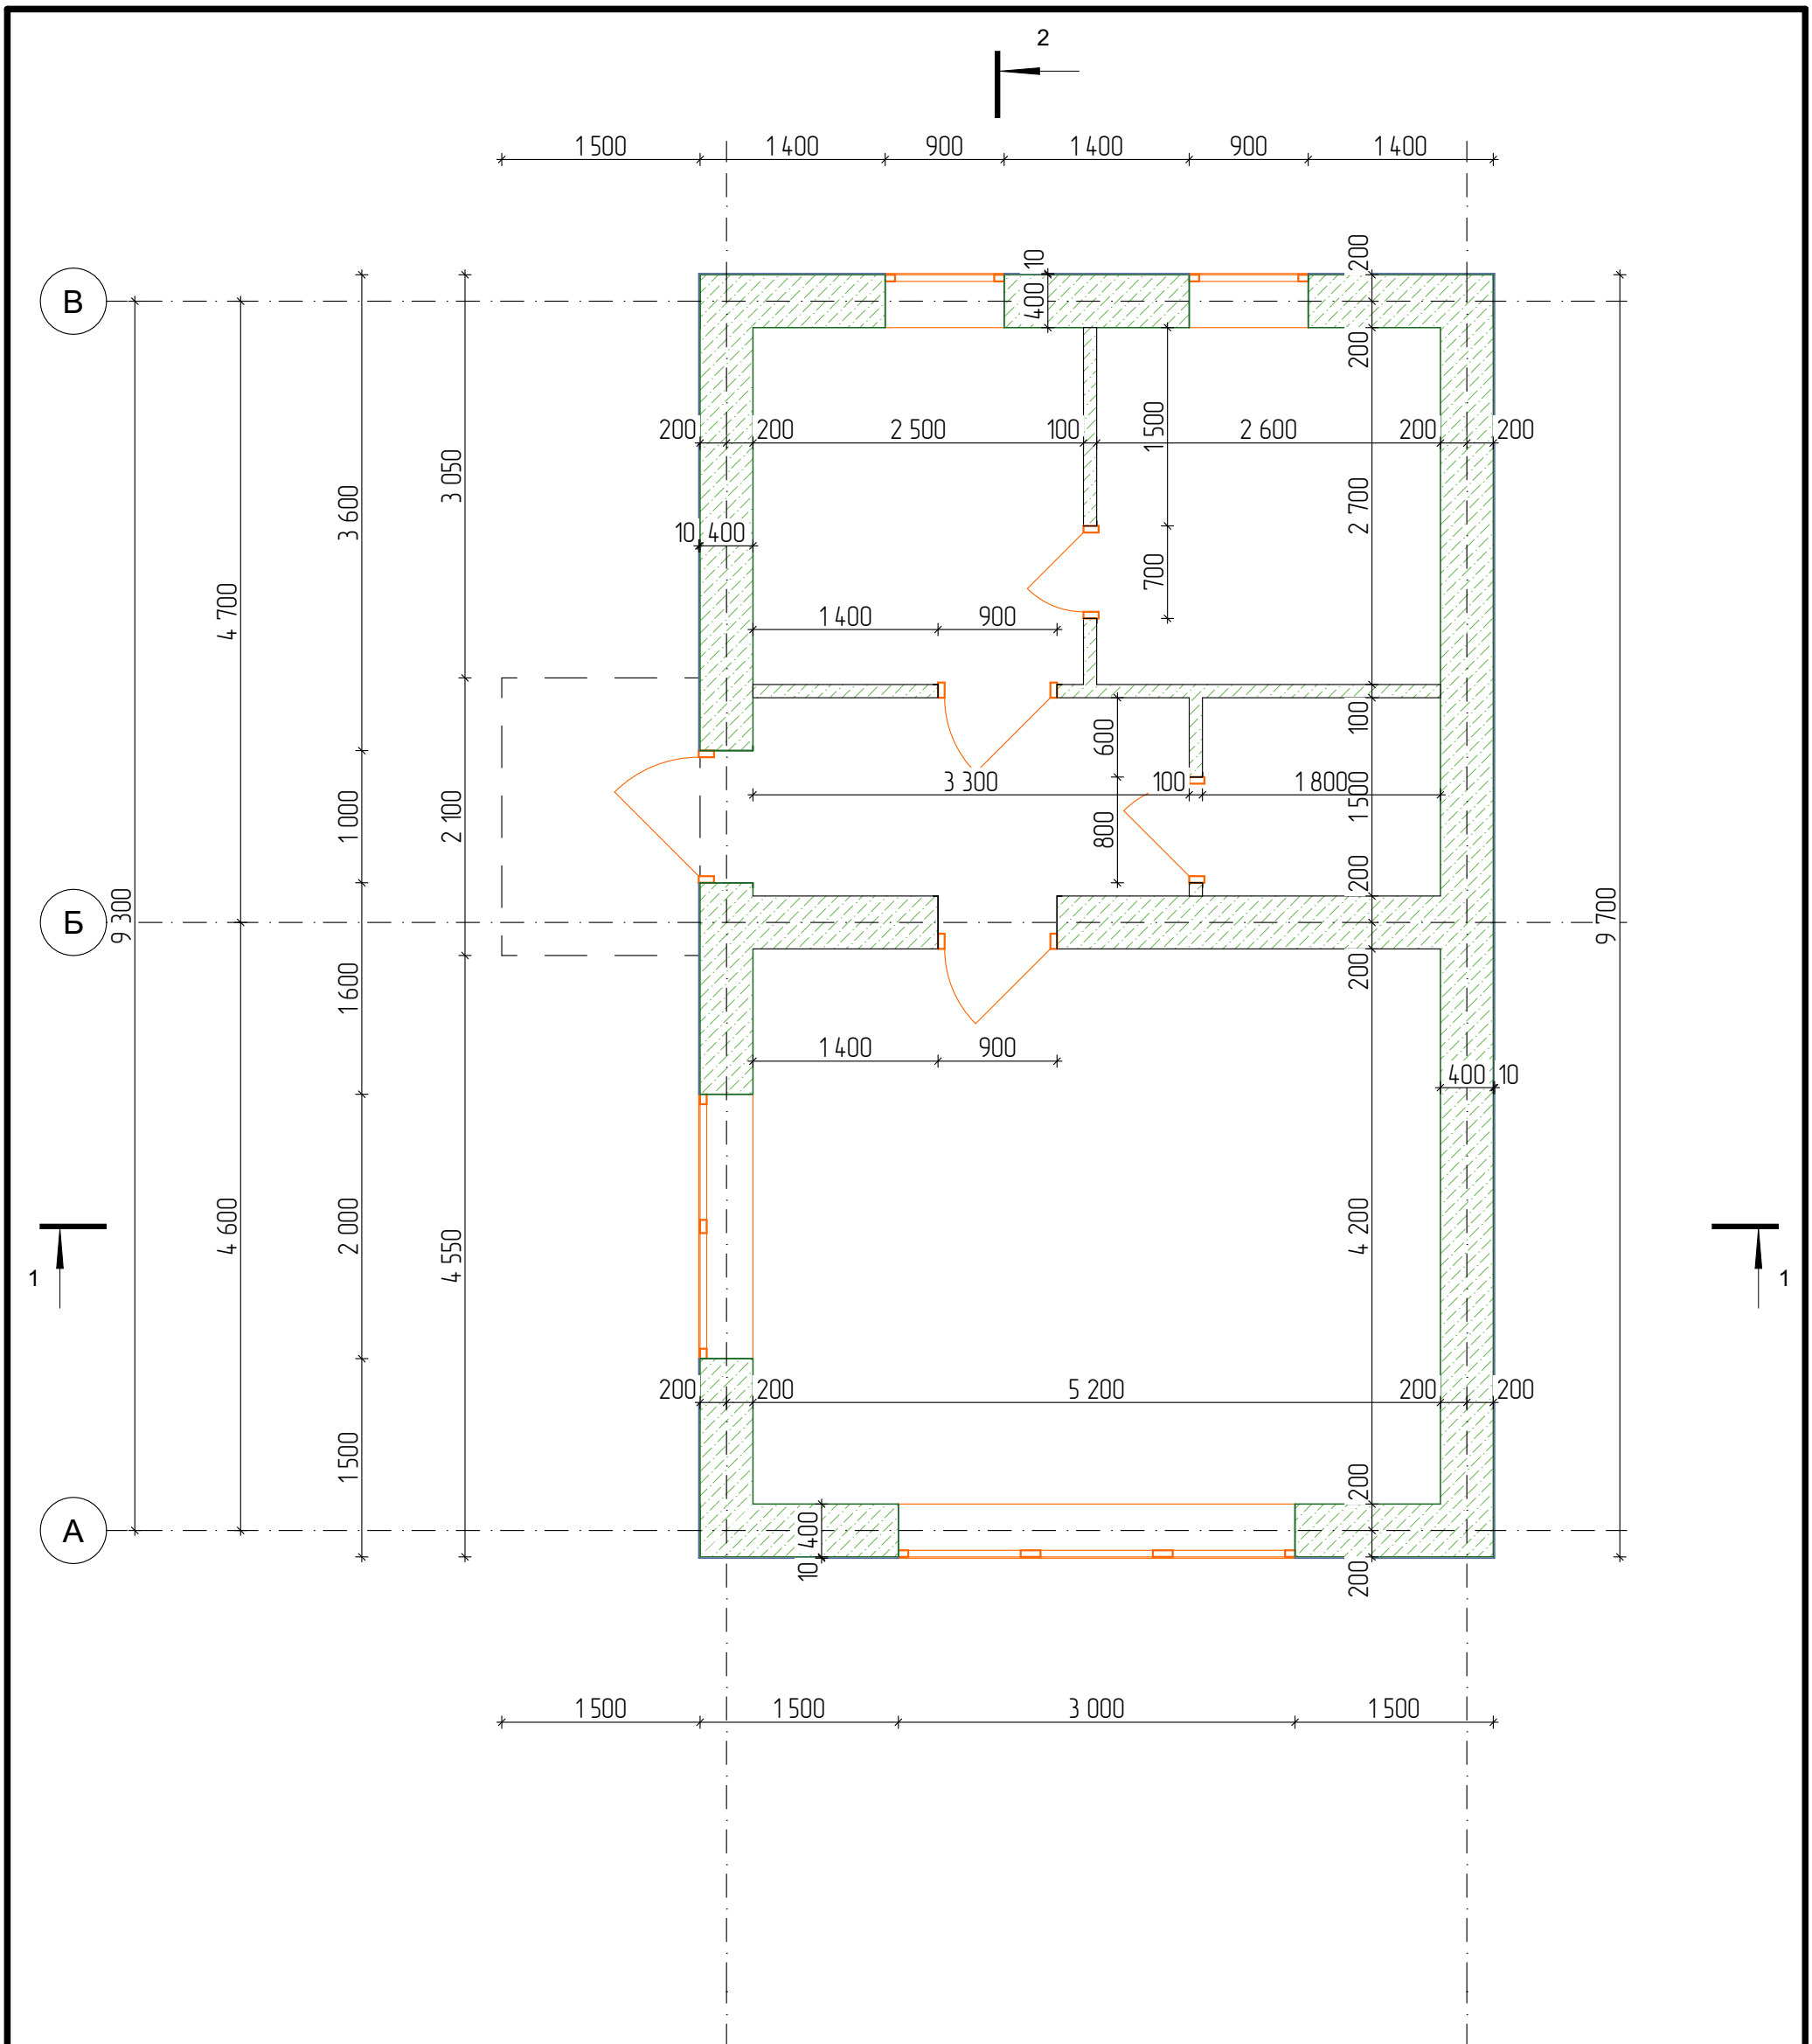




ВЕДОМОСТЬ БЛОКА ДЛЯ СТЕН	
ID Элемента	Объем, м3
Несущие 400мм	45,98
Перегородки 100мм	2,50

Изм.	Кол.уч.	Лист	№Док.	Подп.	Дата	кадастровый номер Россия			
Разраб.		Салыкова Е.				Индивидуальный жилой дом	Стадия	Лист	Листов
							#Стадия Проекта	08	
						План 1 этажа			


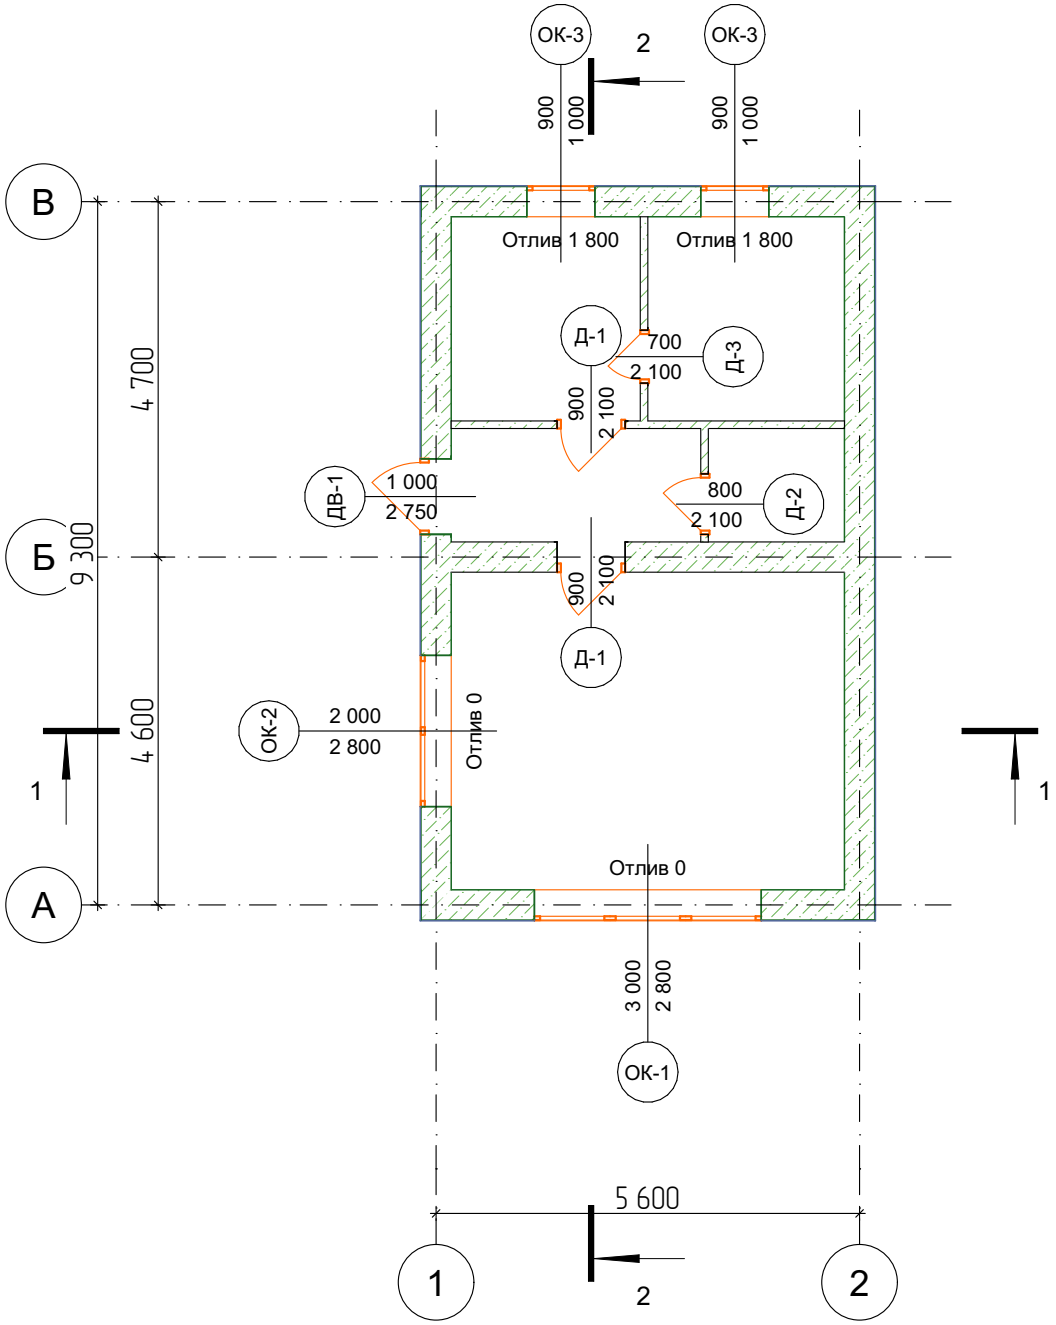


						кадастровый номер Россия		
Изм.	Кол.уч.	Лист	№Док.	Подп.	Дата			
Разраб.		Салыкова В				Индивидуальный жилой дом	Стадия: #Стадия Проекта	Лист: 09 / Листов:
						Маркировочный план 1 этаж		


Каталог Дверей

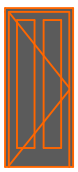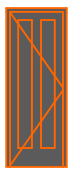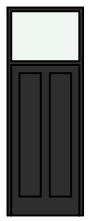Полный ID Элемента	Д-1	Д-2	Д-3	ДВ-1
D по Классификации	Дверь -1	Дверь -2	Дверь -3	Дверь -1
Наименование Двери	Однопольная Дверь 27	Однопольная Дверь 27	Однопольная Дверь 27	Однопольная Дверь с Фрамугой 27
Количество	2	1	1	1
Размер Ш х В	900×2 100	800×2 100	700×2 100	1 000×2 750
Ориентация	П	П	Л	П
Высота Порога Двери	0	0	0	0
Высота Перемычки Двери	2 100	2 100	2 100	2 750
2D-символ				
Вид со Стороны, Противоположной Стороне Открывания				

Изм.	Кол.уч.	Лист	№Док.	Подп.	Дата	кадастровый номер Россия			
Разраб.		Салыкова В				Индивидуальный жилой дом	Стадия	Лист	Листов
							#Стадия Проекта	10	
						Каталог дверных проемов			

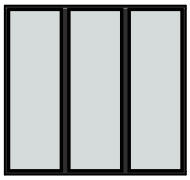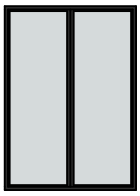
Каталог Окон			
Полный ID Элемента	ОК-1	ОК-2	ОК-3
Наименование Окна	Трехстворчатое Окно 27	Раздвижное Двустворчатое Окно 27	Окно 27
Количество	1	1	2
Размер Ш x В	3 000×2 800	2 000×2 800	900×1 000
Высота Подоконника Окна	0	0	1 800
Высота Перемычки Окна	2 800	2 800	2 800
2D-символ			
Вид со Стороны, Противоположной Стороне Открывания			

Изм.	Кол.уч.	Лист	№Док.	Подп.	Дата	кадастровый номер Россия			
Разраб.		Салыкова В				Индивидуальный жилой дом	Стадия	Лист	Листов
							#Стадия Проекта	11	
						Каталог оконных проемов			

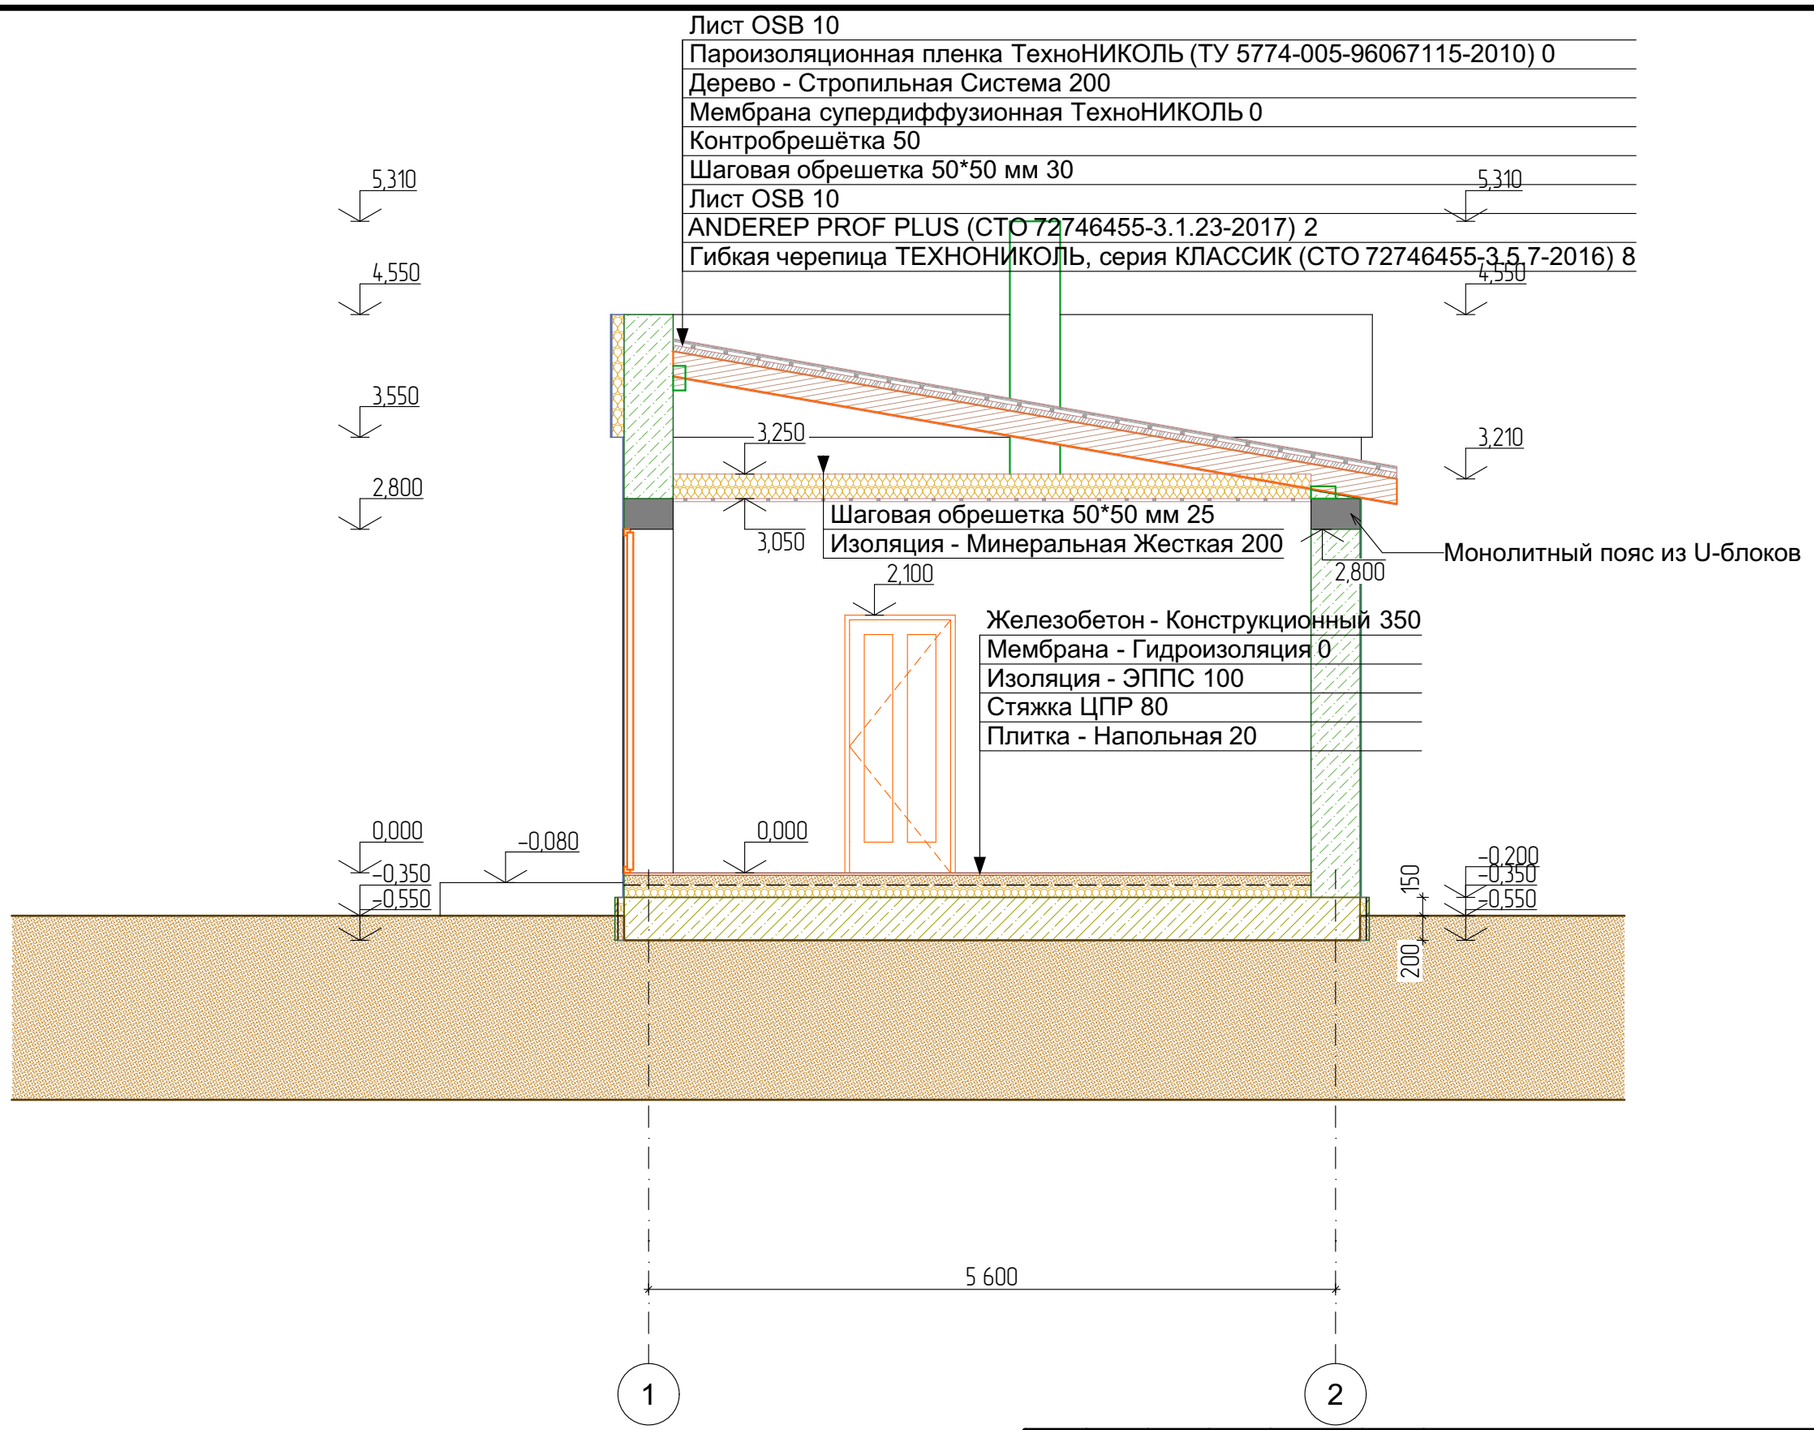

Изм.	Кол.уч.	Лист	№Док.	Подп.	Дата	
						кадастровый номер Россия
Разраб.		Салыкова Е.				Индивидуальный жилой дом
						Разрез 1 - 1

Стадия	Лист	Листов
#Стадия Проекта	12	

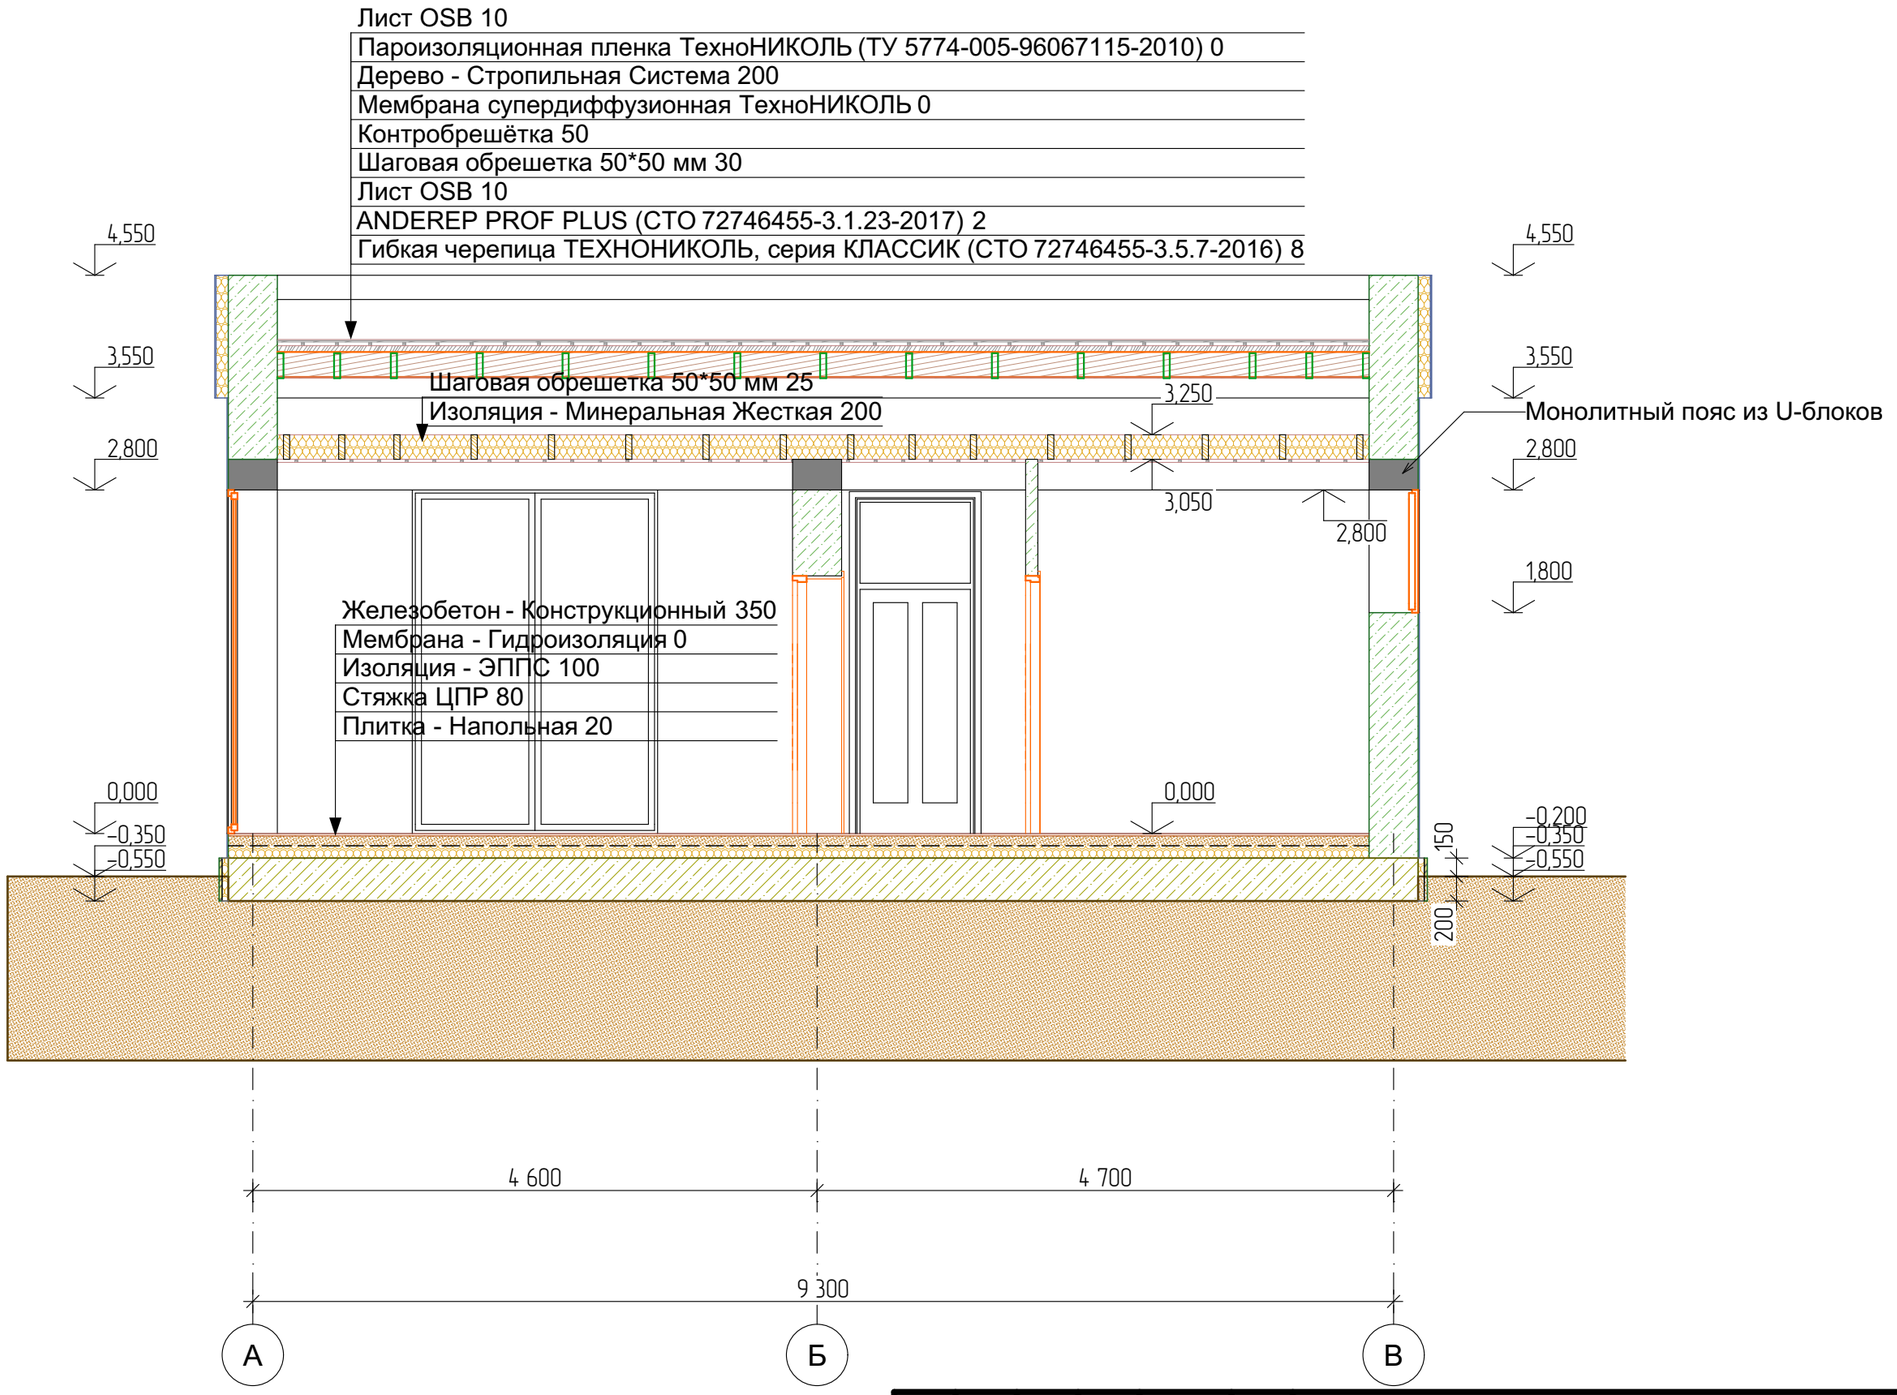

Изм.	Кол.уч.	Лист	№Док.	Подп.	Дата	кадастровый номер Россия			
Разраб.		Салыкова Е.				Индивидуальный жилой дом	Стадия	Лист	Листов
							#Стадия Проекта	13	
						Разрез 2 - 2			

Лист OSB 10
Пароизоляционная пленка ТехноНИКОЛЬ (ТУ 5774-005-96067115-2010) 0
Дерево - Стропильная Система 200
Мембрана супердиффузионная ТехноНИКОЛЬ 0
Контробрешётка 50
Шаговая обрешетка 50*50 мм 30
Лист OSB 10
ANDEREP PROF PLUS (СТО 72746455-3.1.23-2017) 2
Гибкая черепица ТЕХНОНИКОЛЬ, серия КЛАССИК (СТО 72746455-3.5.7-2016) 8

Мауэрлат 100x200

3,312

3,250

200

3,050

25

Шаговая обрешетка 50*50 мм 25
Изоляция - Минеральная Жесткая 200

13
12
2,800
11
Монолитный пояс из U-блоков
10
9
8
400
10
7
6
5
4
3
2
1

3 025


Железобетон - Конструкционный 350
Мембрана - Гидроизоляция 0
Изоляция - ЭППС 100
Стяжка ЦПР 80
Плитка - Напольная 20

0,000

20
80
100
350
50
25
350

-0,200
-0,550

Изм.	Кол.уч.	Лист	№Док.	Подп.	Дата	кадастровый номер Россия			
Разраб.		Салыкова Е.				Индивидуальный жилой дом	Стадия	Лист	Листов
							#Стадия Проекта	14	
						Разрез по стене			

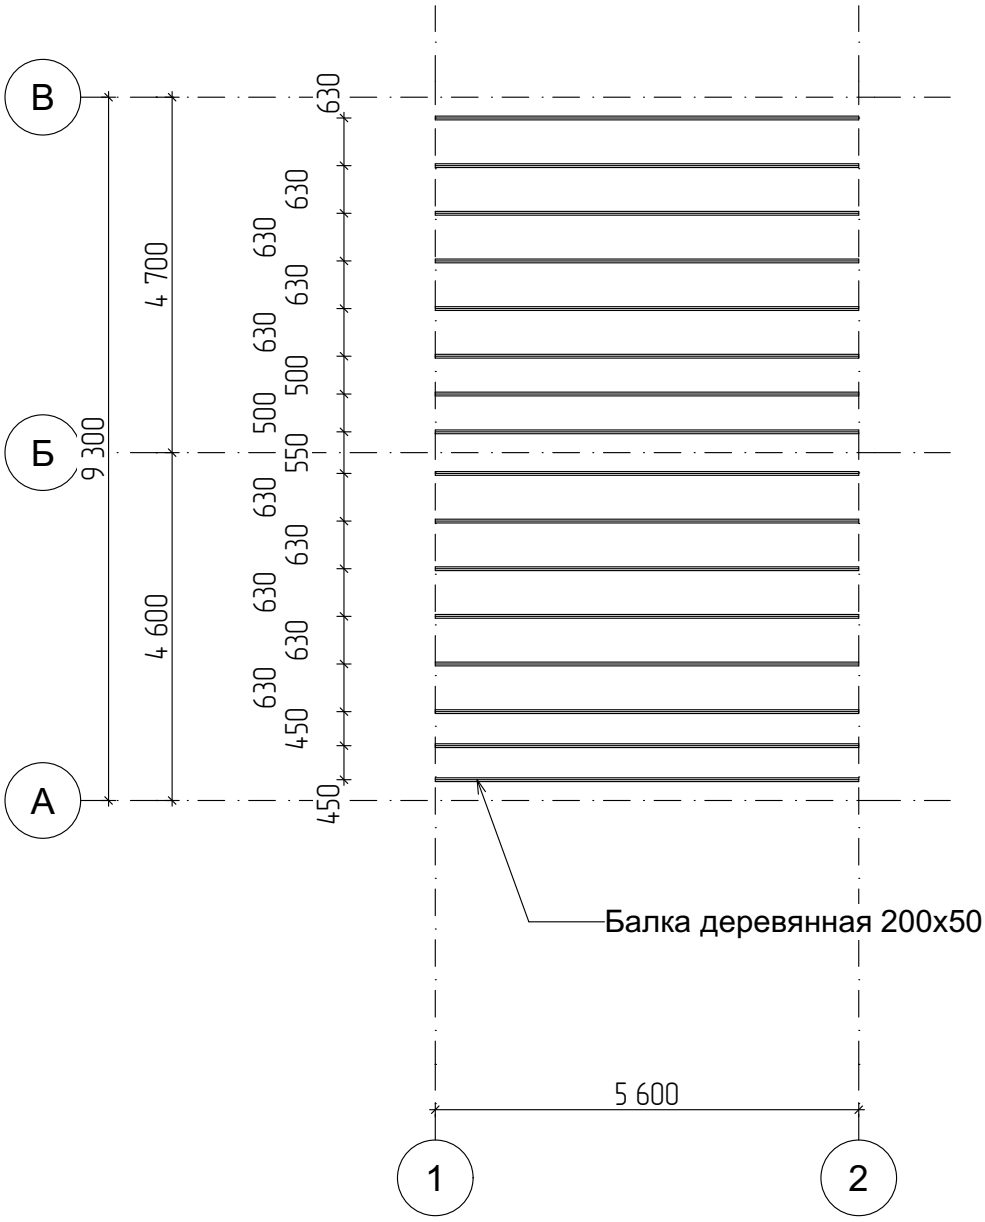


Ведомость перекрытия	
Наименование	Объем

Балка деревянная 200х50	0,96

Изм.	Кол.уч.	Лист	№Док.	Подп.	Дата	
Разраб.		Салыкова В				


кадастровый номер Россия

	Стадия	Лист	Листов
Индивидуальный жилой дом	#Стадия Проекта	15	
План перекрытий на отм 3,050			

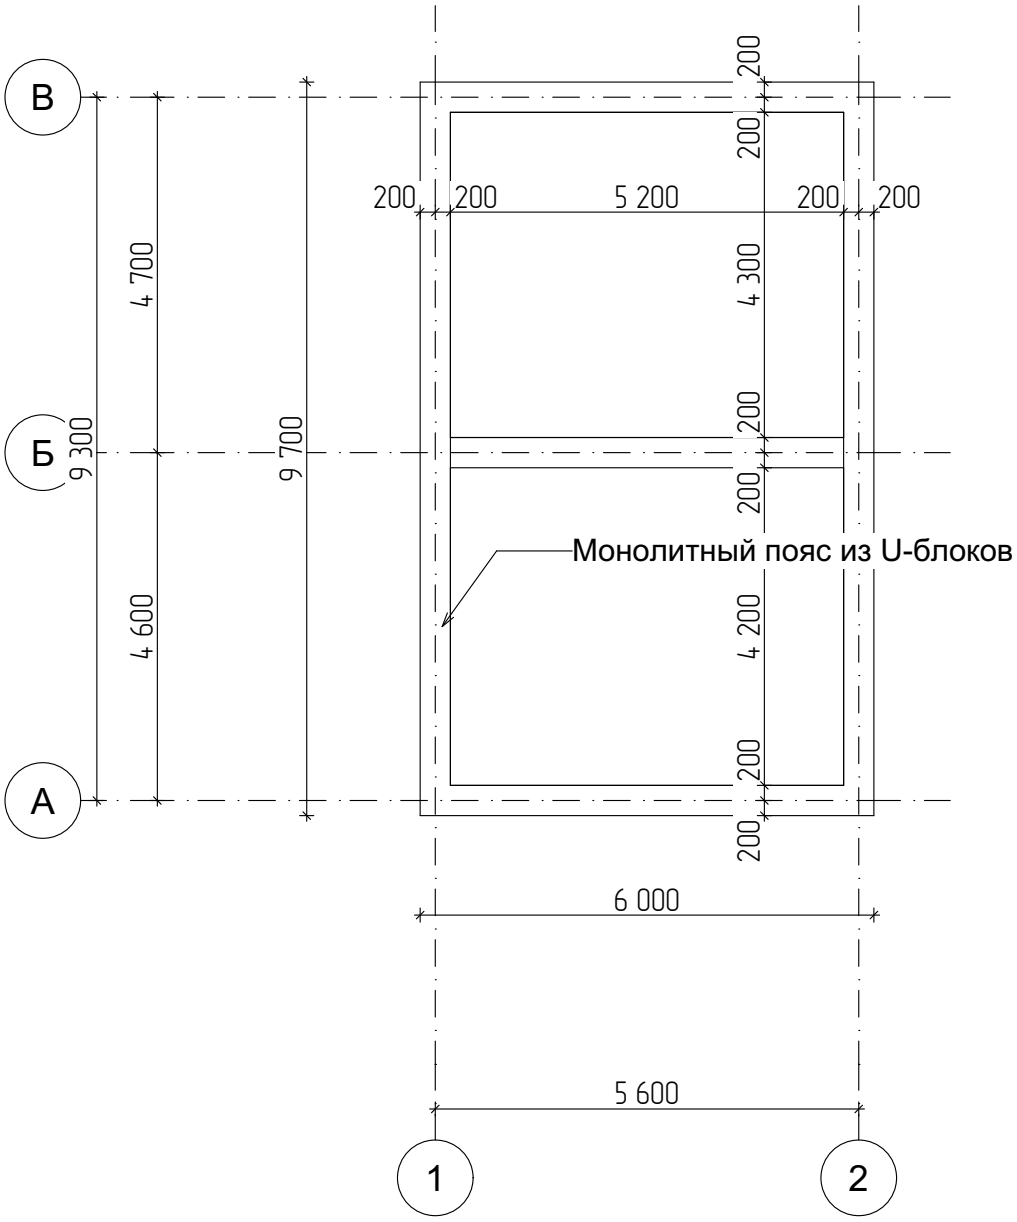

ВЕДОМОСТЬ НА МОНОЛИТНЫЙ ПОЯС 1-ГО ЭТАЖА	
Наименование	Объем, м3
	3,50
Монолитный пояс из U-блоков	3,50


						кадастровый номер Россия	
Изм.	Кол.уч.	Лист	№Док.	Подп.	Дата		
Разраб.		Салыкова В				Индивидуальный жилой дом	Стадия: #Стадия Проекта; Лист: 16; Листов:
						Монолитный пояс на отм 2,800	

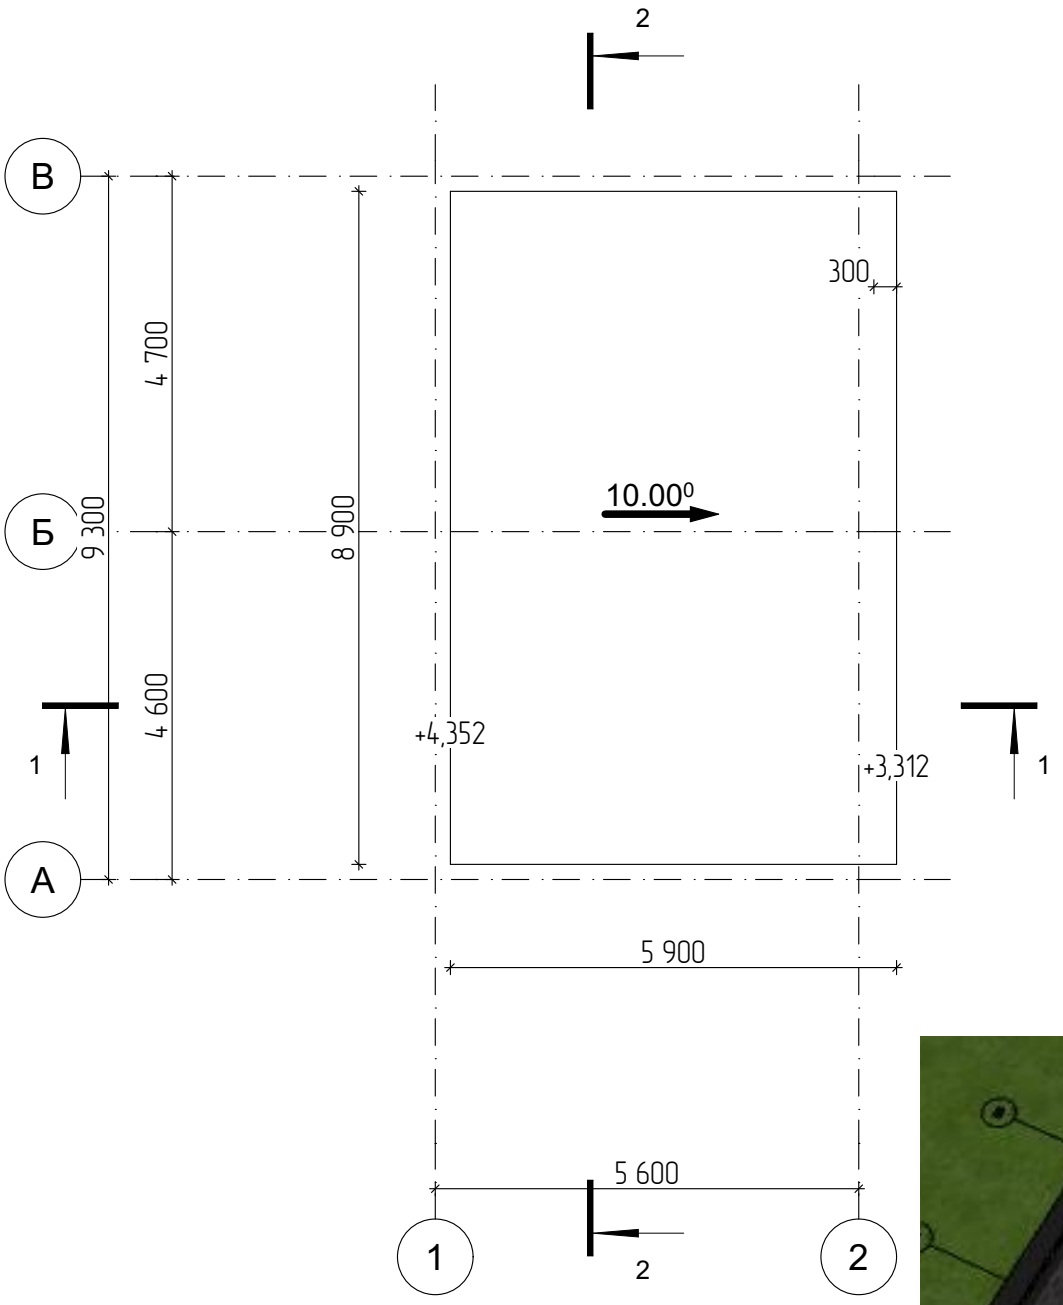




ИКК-03 Кровля	
Наименование	Площадь, м2
Кровля	53,32

Изм.	Кол.уч.	Лист	№Док.	Подп.	Дата	кадастровый номер Россия			
Разраб.		Салыкова В				Индивидуальный жилой дом	Стадия	Лист	Листов
							#Стадия Проекта	17	
						План кровли на отм. 3,312			

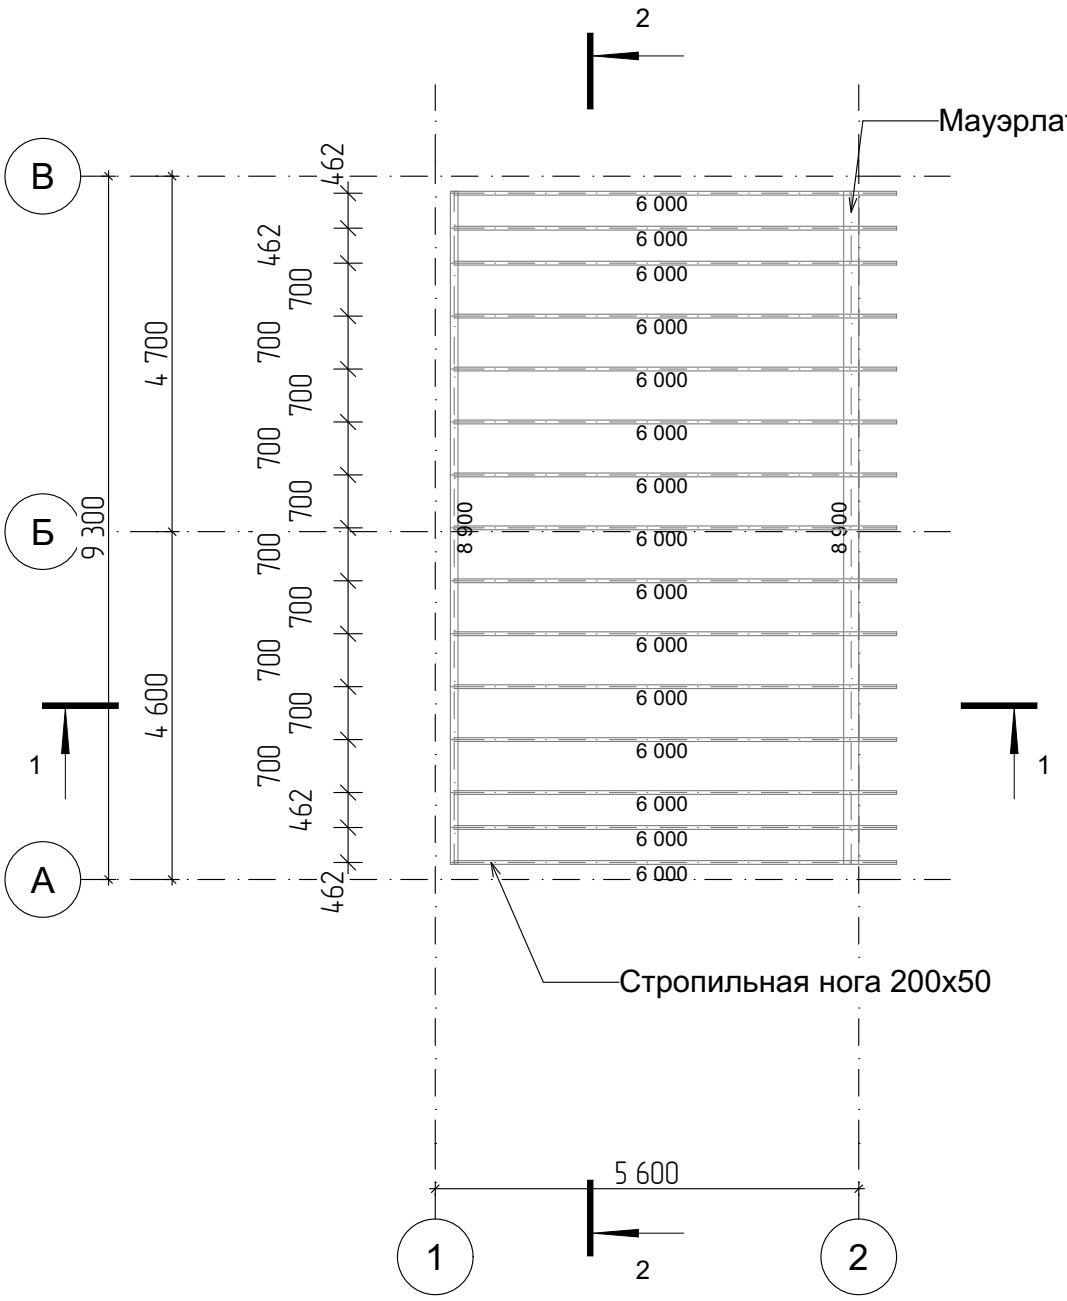


ИКК-03 Стропильная система	
Наименование	Объем, м3
Коньковый брус 200х100	0,18
Мауэрлат 100х200	0,18
Стропильная нога 200х50	0,90

Изм.	Кол.уч.	Лист	№Док.	Подп.	Дата	кадастровый номер Россия			
Разраб.		Салыкова В				Индивидуальный жилой дом	Стадия	Лист	Листов
							#Стадия Проекта	18	
						Схема расположения стропил на отм. 3,312			

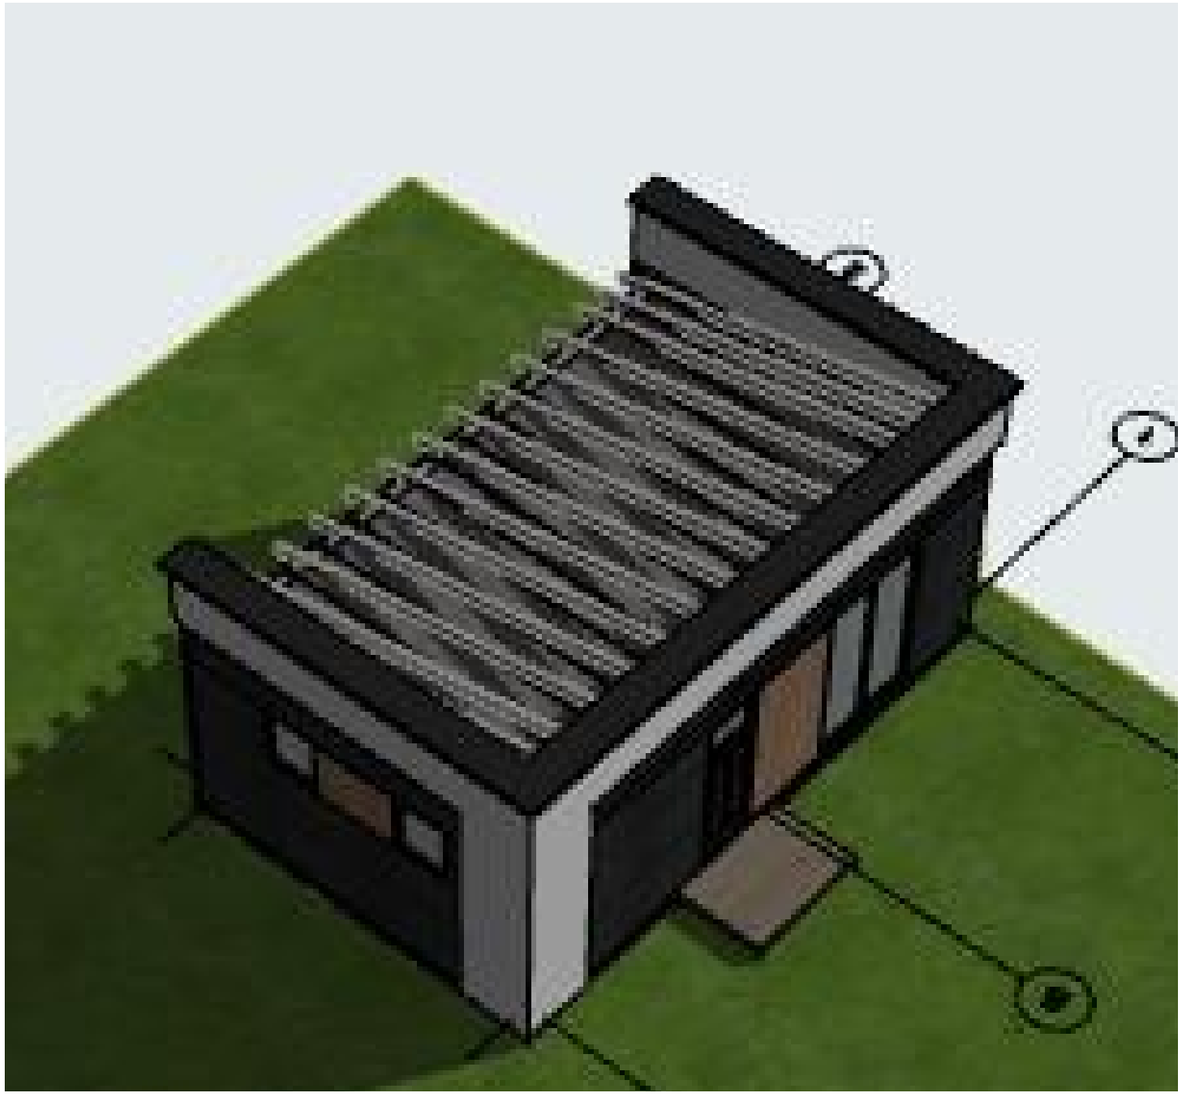




						кадастровый номер Россия		
Изм.	Кол.уч.	Лист	№Док.	Подп.	Дата			
Разраб.		Салыкова В.				Индивидуальный жилой дом	Стадия	Лист	Листов
							#Стадия Проекта	19	
						3Д Вид стропильной системы			

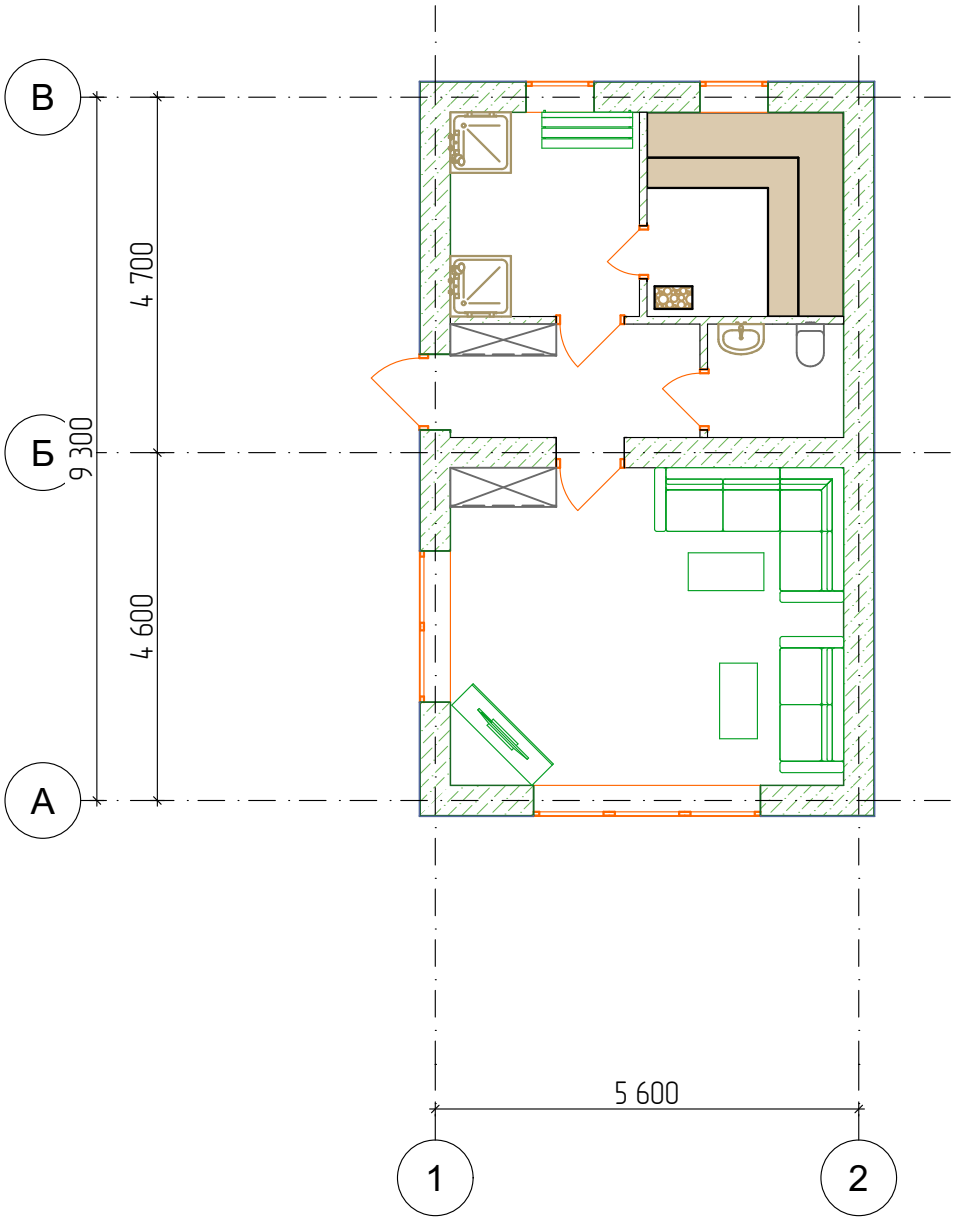


						кадастровый номер Россия		
Изм.	Кол.уч.	Лист	№Док.	Подп.	Дата			
Разраб.		Салыкова В				Индивидуальный жилой дом	Стадия: #Стадия Проекта	Лист: 20 / Листов:
						План расстановки мебели 1 этаж		

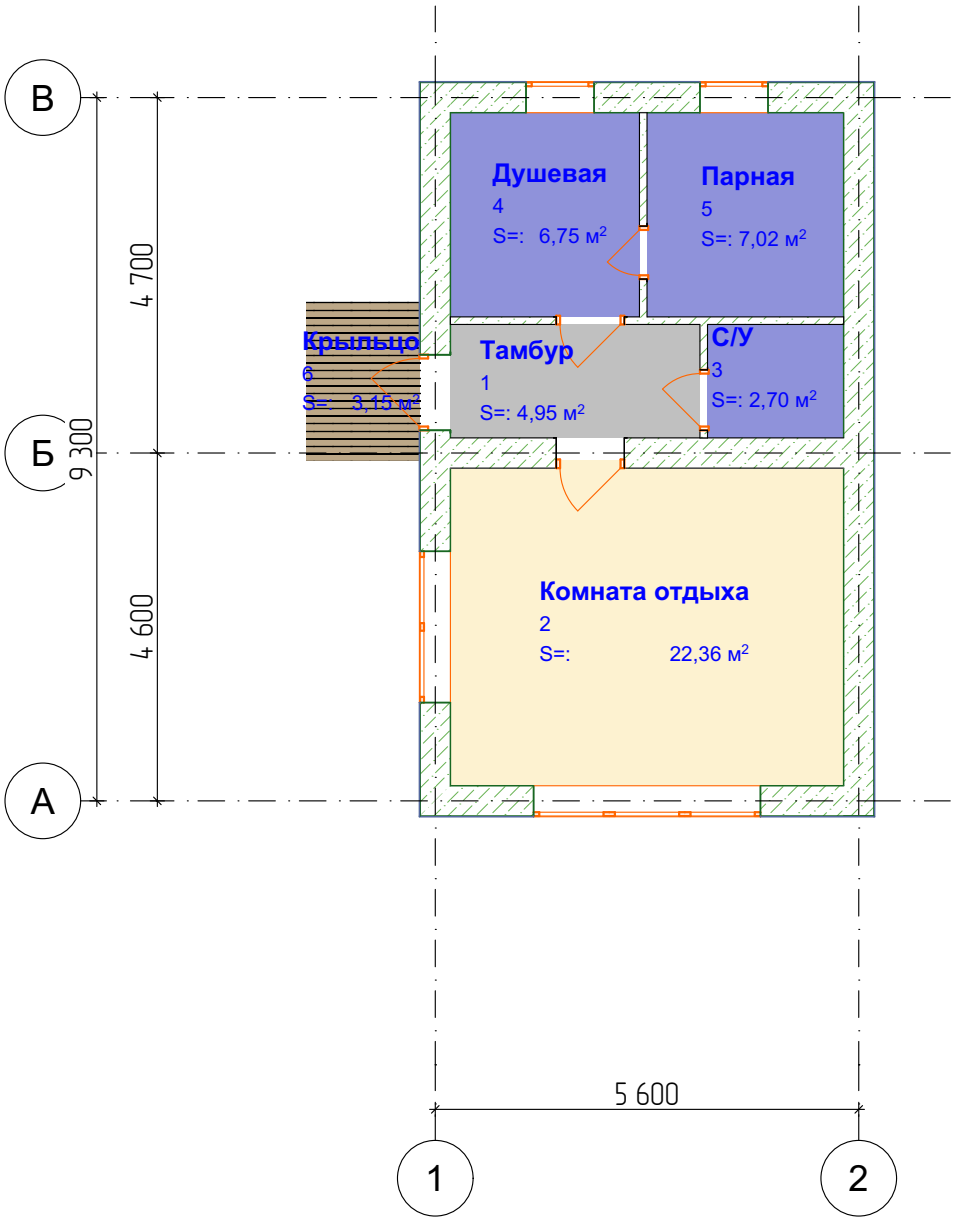


№	Наименование	Площадь
1	Тамбур	4,95
2	Комната отдыха	22,36
3	С/У	2,70
4	Душевая	6,75
5	Парная	7,02
6	Крыльцо	3,15
		46,93 м²

Изм.	Кол.уч.	Лист	№Док.	Подп.	Дата	кадастровый номер Россия			
Разраб.		Салыкова В				Индивидуальный жилой дом	Стадия	Лист	Листов
							#Стадия Проекта	21	
						Экспликация помещений 1- го этажа			

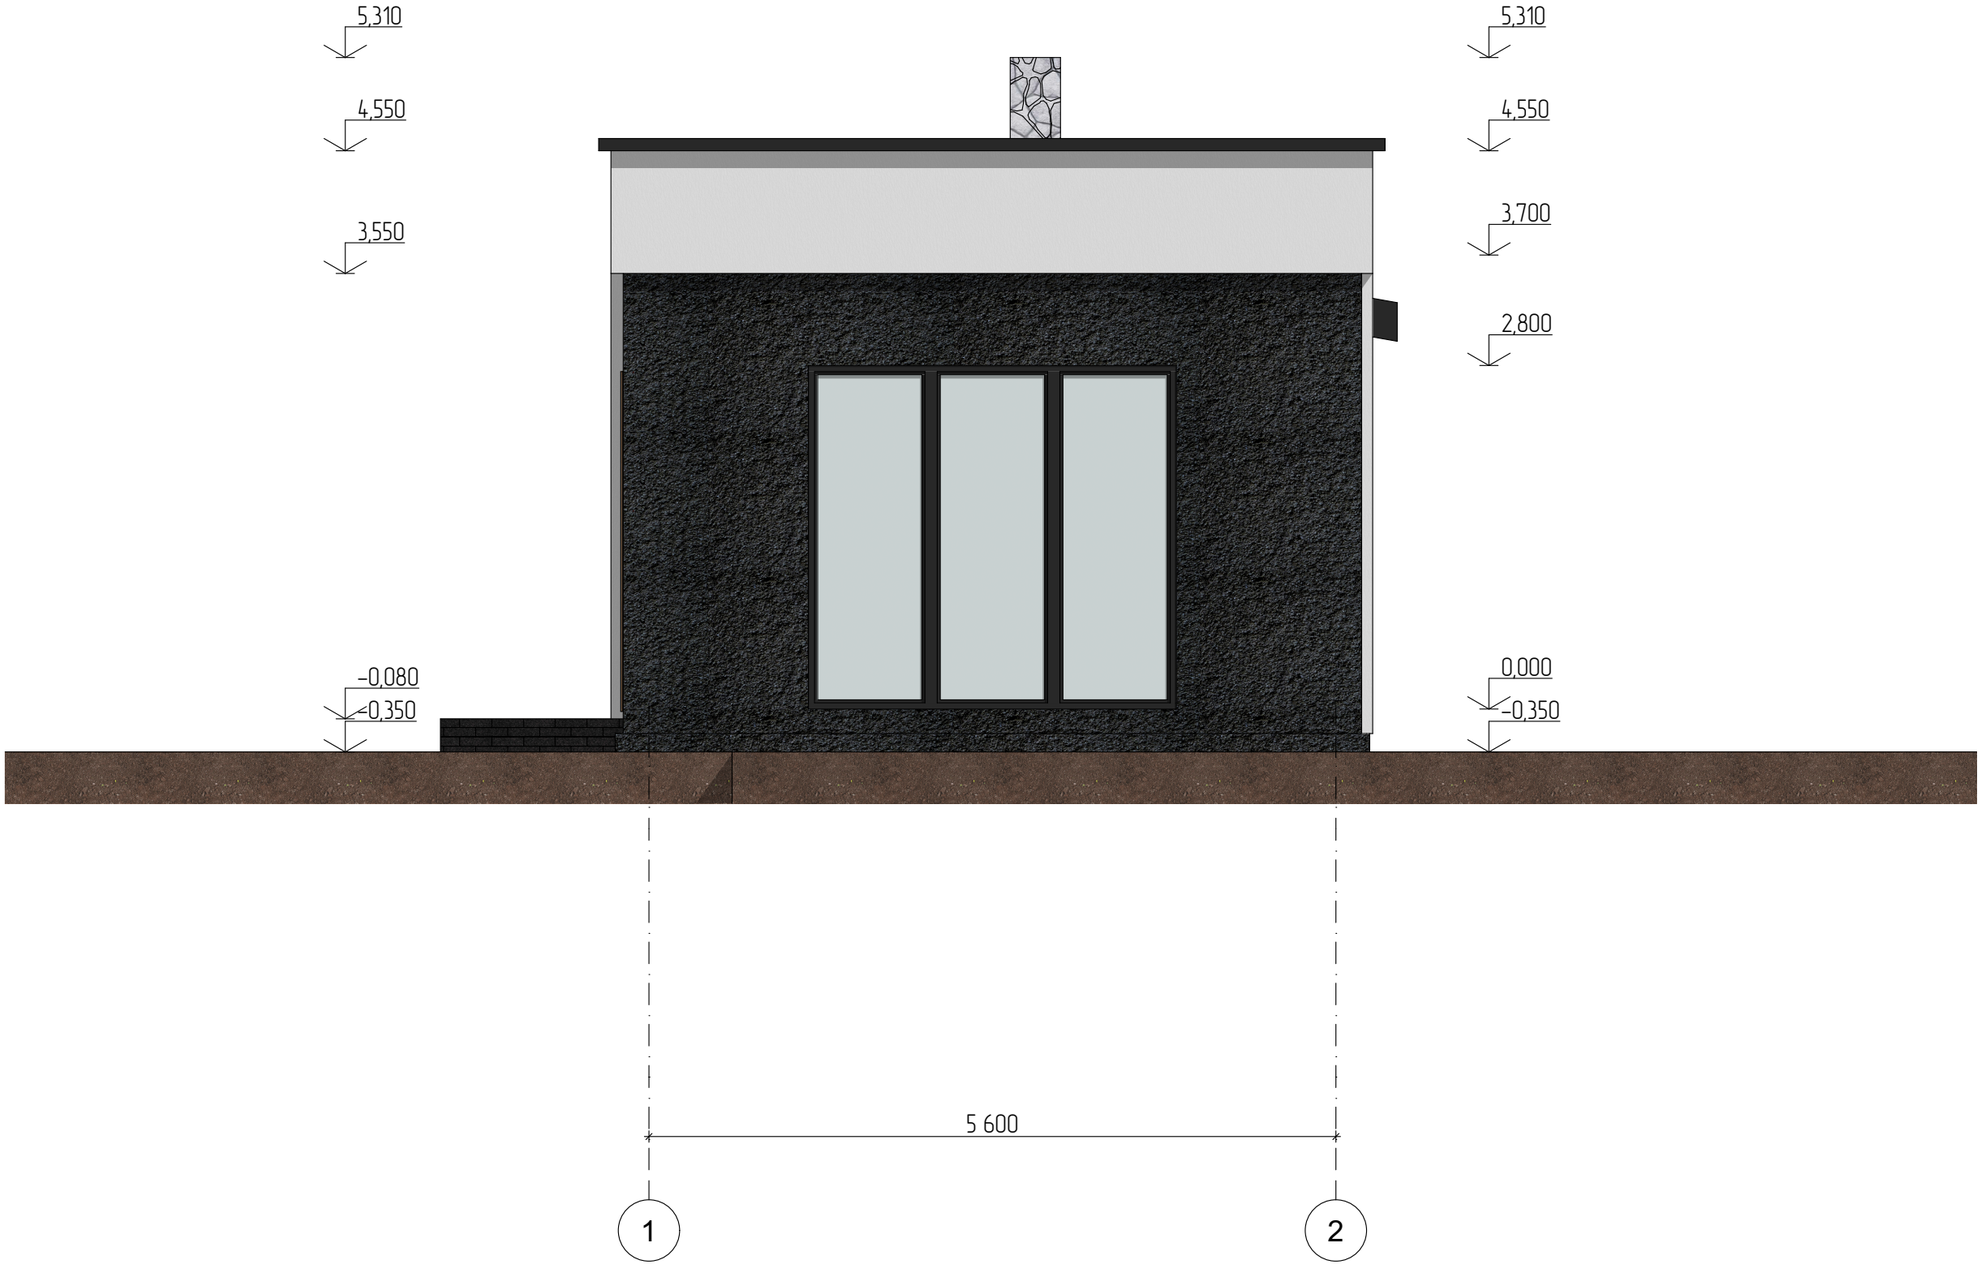


						кадастровый номер Россия
Изм.	Кол.уч.	Лист	№Док.	Подп.	Дата	
Разраб.		Салыкова Е.				Индивидуальный жилой дом
						Фасад в осях 1-2

Стадия	Лист	Листов
#Стадия Проекта	22	

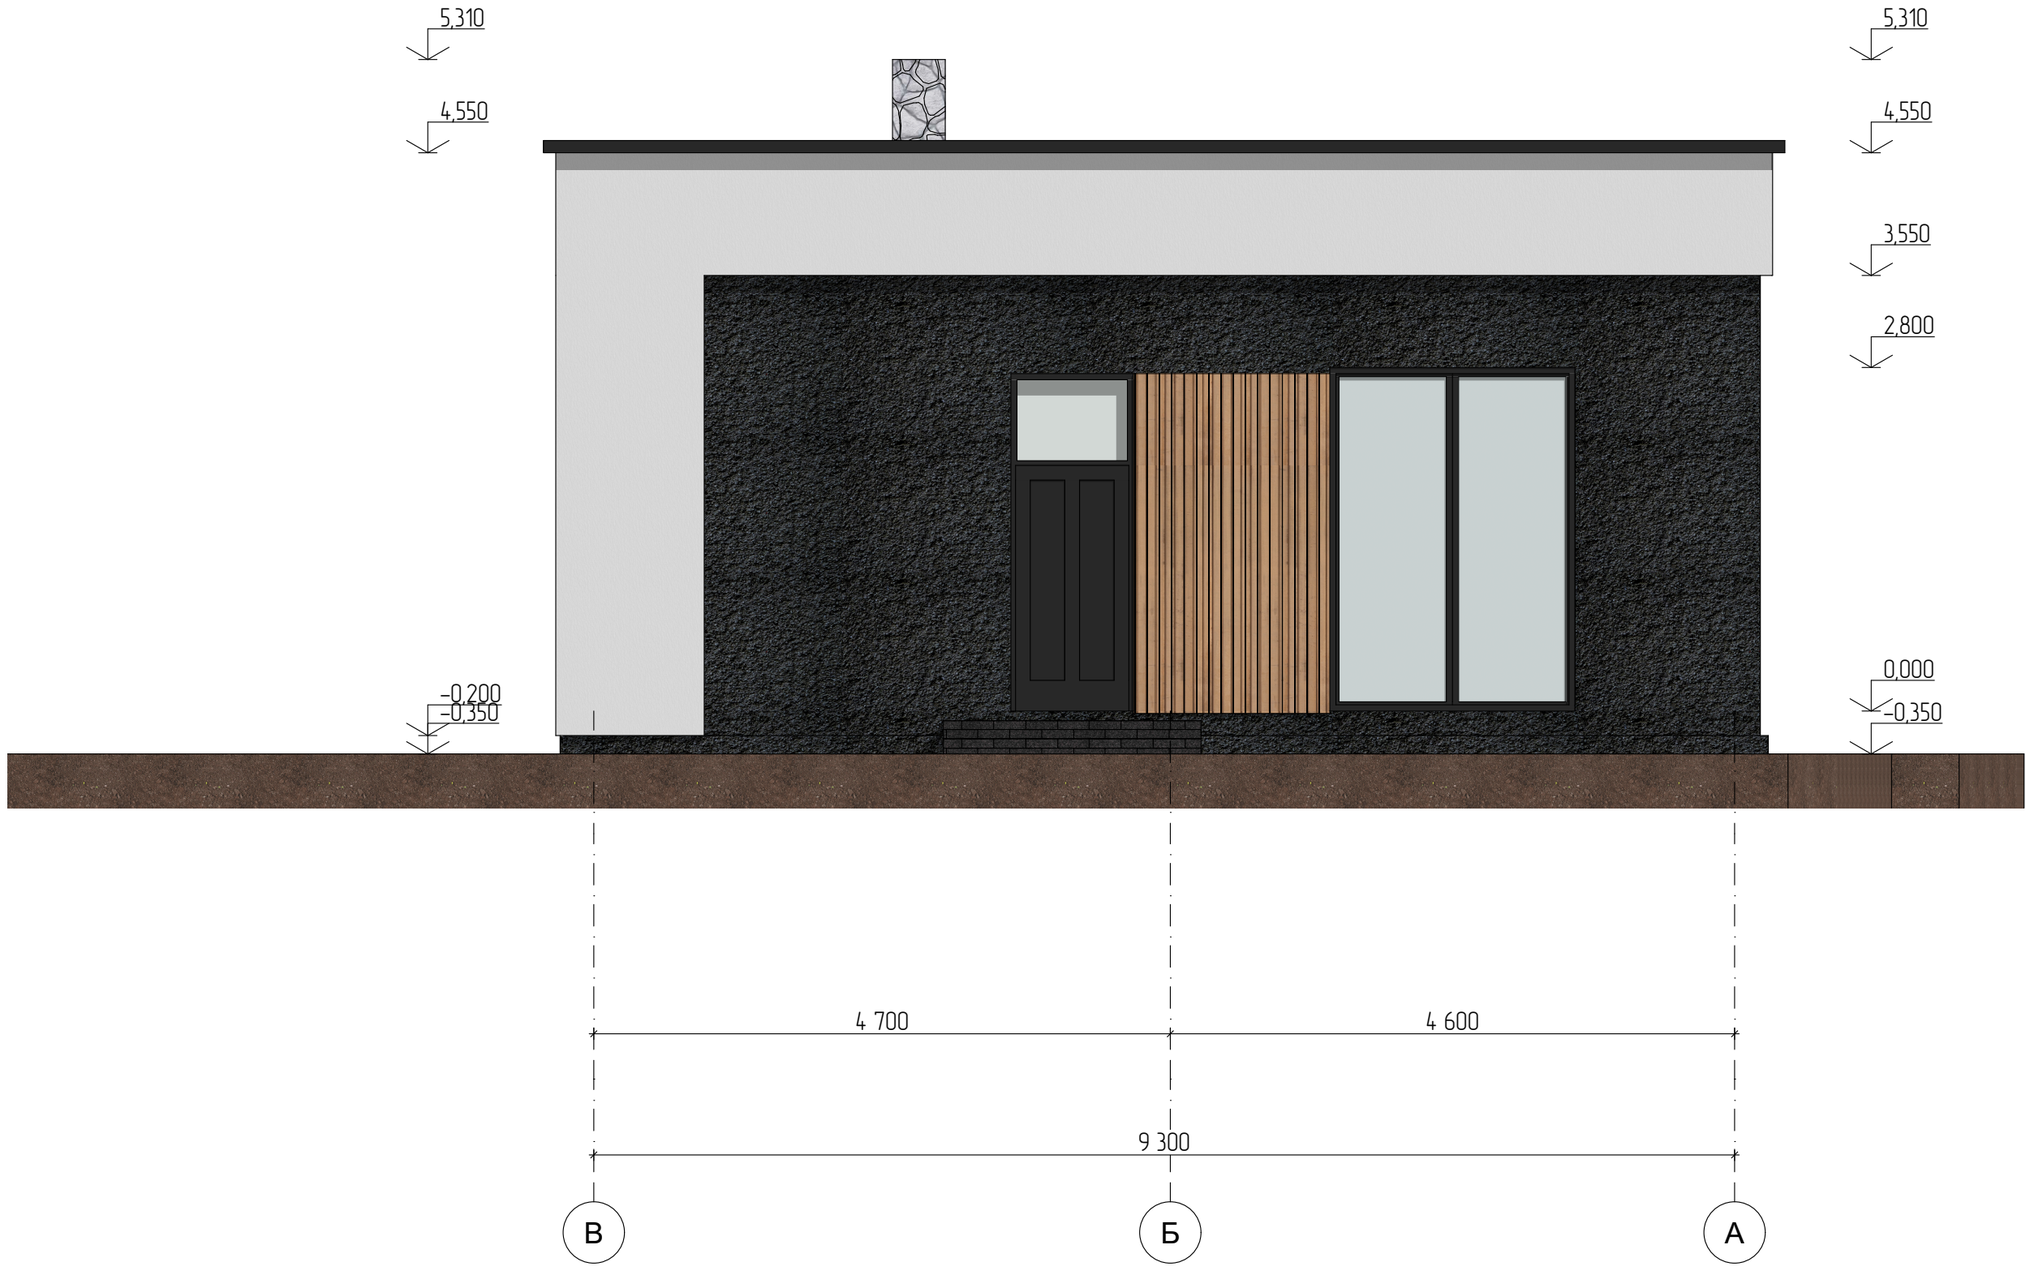


Изм.	Кол.уч.	Лист	№Док.	Подп.	Дата	кадастровый номер Россия			
Разраб.		Салыкова Е.				Индивидуальный жилой дом	Стадия	Лист	Листов
							#Стадия Проекта	23	
						Фасад в осях В-А			

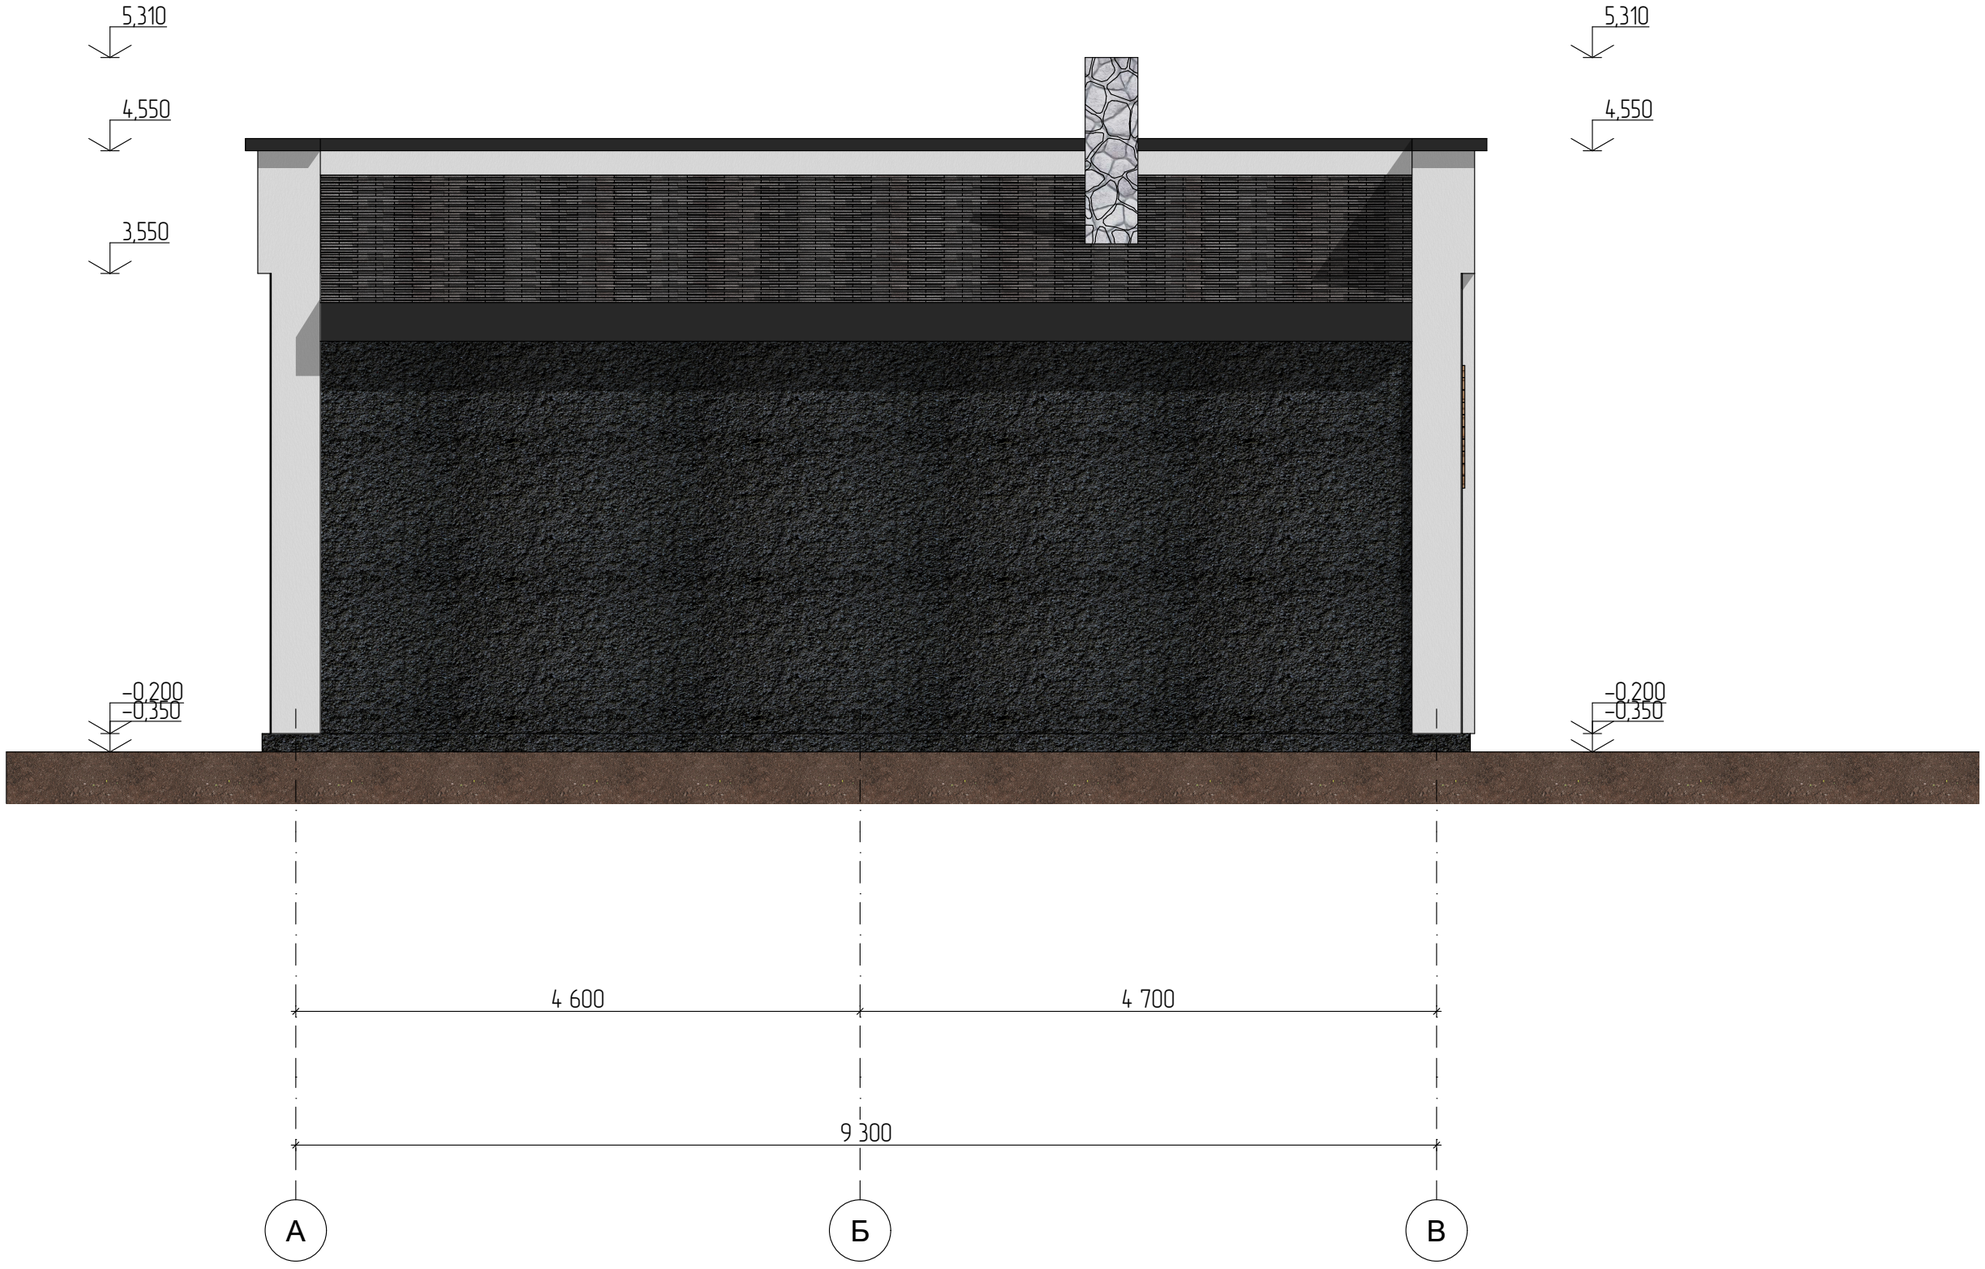

						кадастровый номер Россия
Изм.	Кол.уч.	Лист	№Док.	Подп.	Дата	
Разраб.		Салыкова Е.				Индивидуальный жилой дом
						Фасад в осях А-В

Стадия	Лист	Листов
#Стадия Проекта	24	

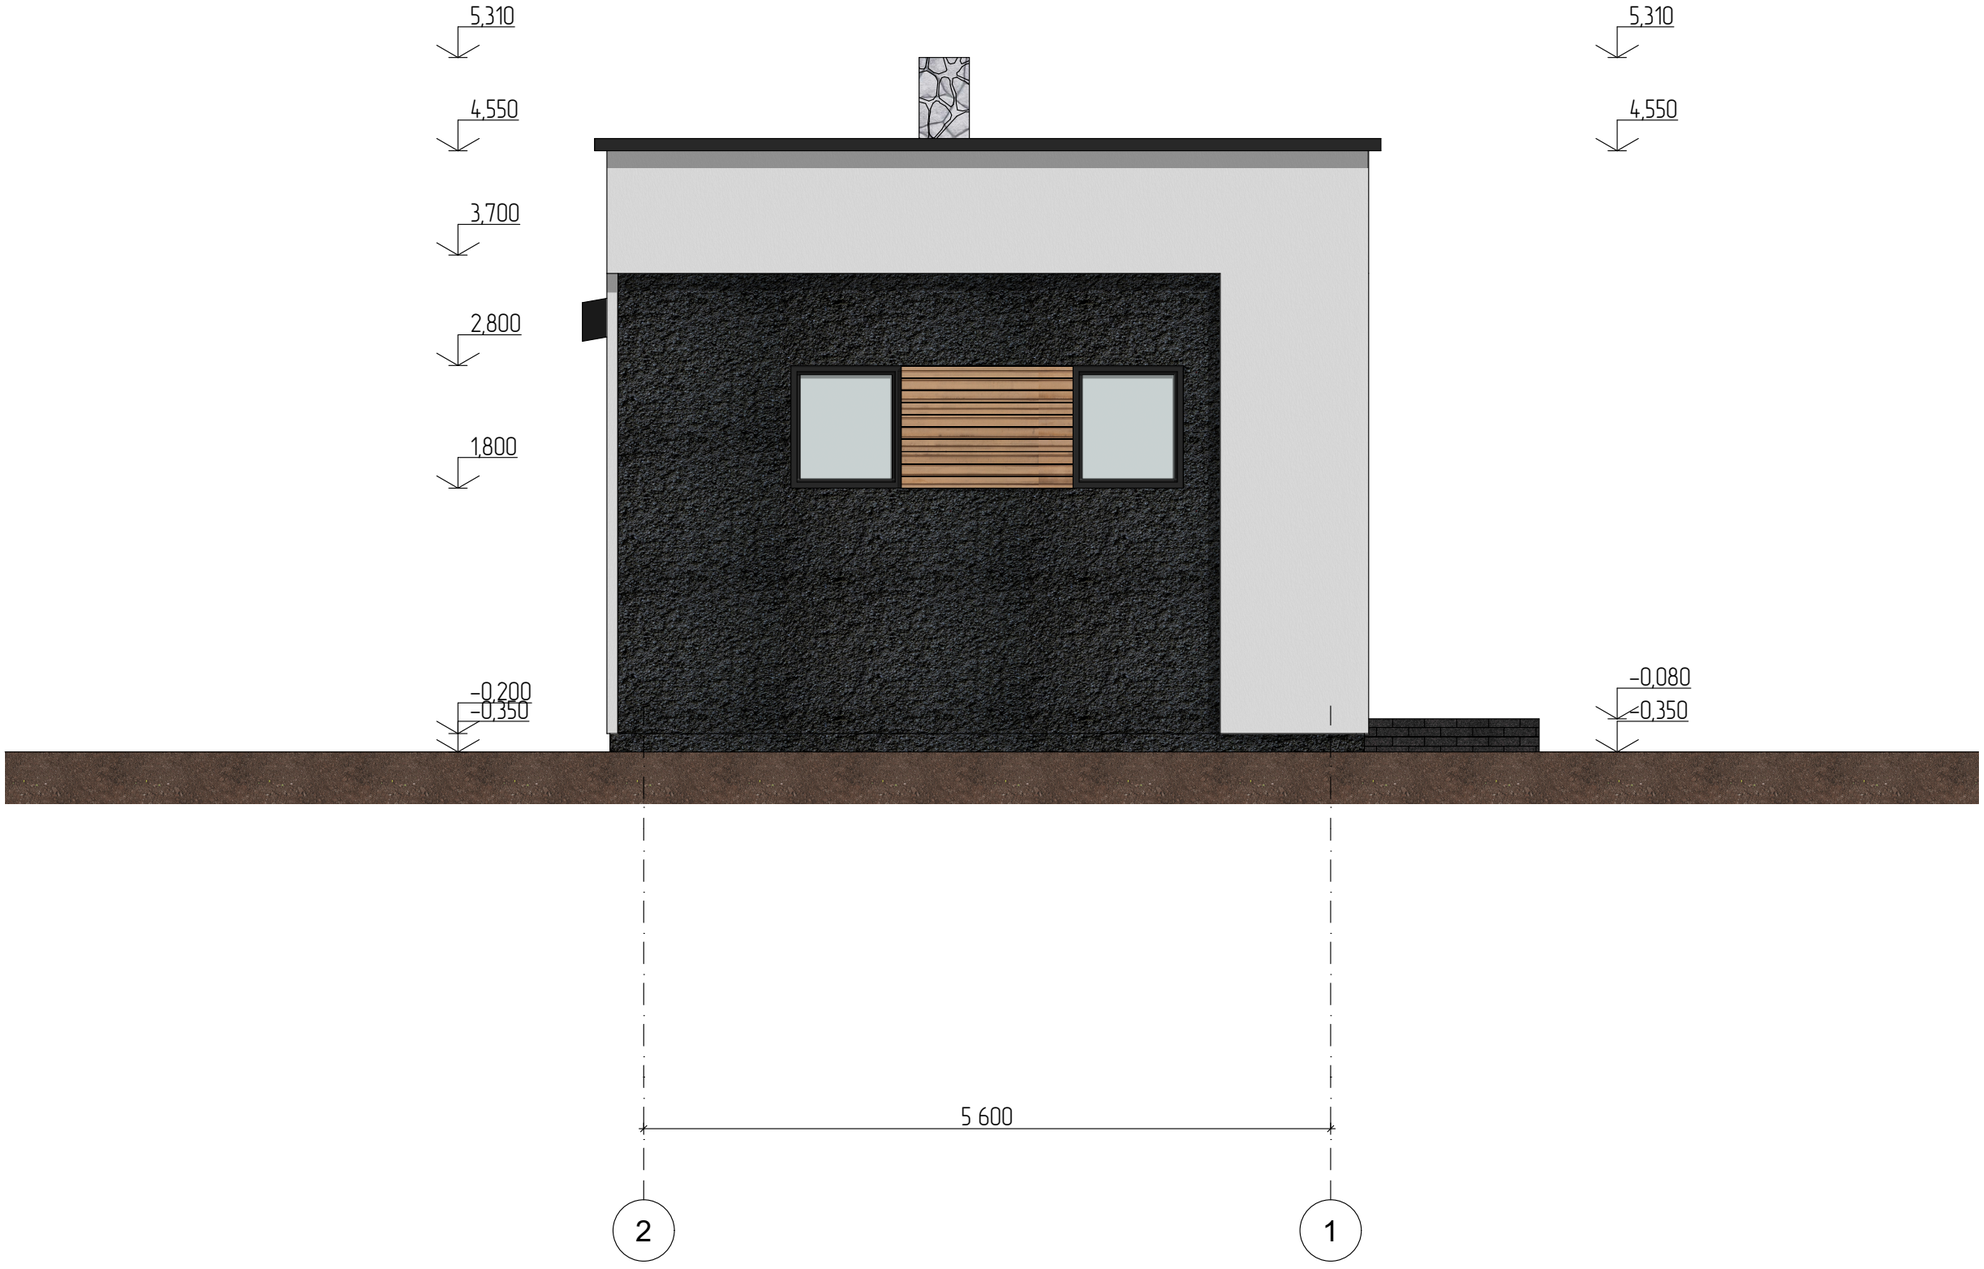

						кадастровый номер Россия
Изм.	Кол.уч.	Лист	№Док.	Подп.	Дата	
Разраб.		Салыкова Е.				Индивидуальный жилой дом
						Фасад в осях 2-1

Стадия	Лист	Листов
#Стадия Проекта	25	