






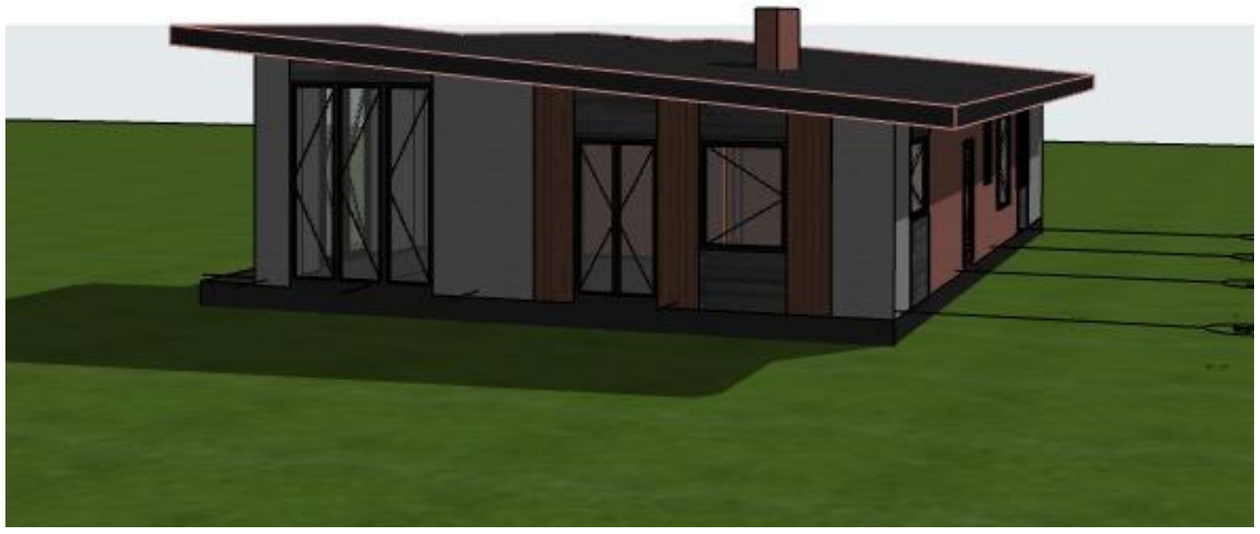

						#ID Проекта	
						кадастровый номер Россия	
Изм.	Кол.уч.	Лист	№Док.	Подп.	Дата		
Разраб.						Индивидуальный жилой дом	Стадия: ЭП; Лист: 05; Листов:
						3D Виды	

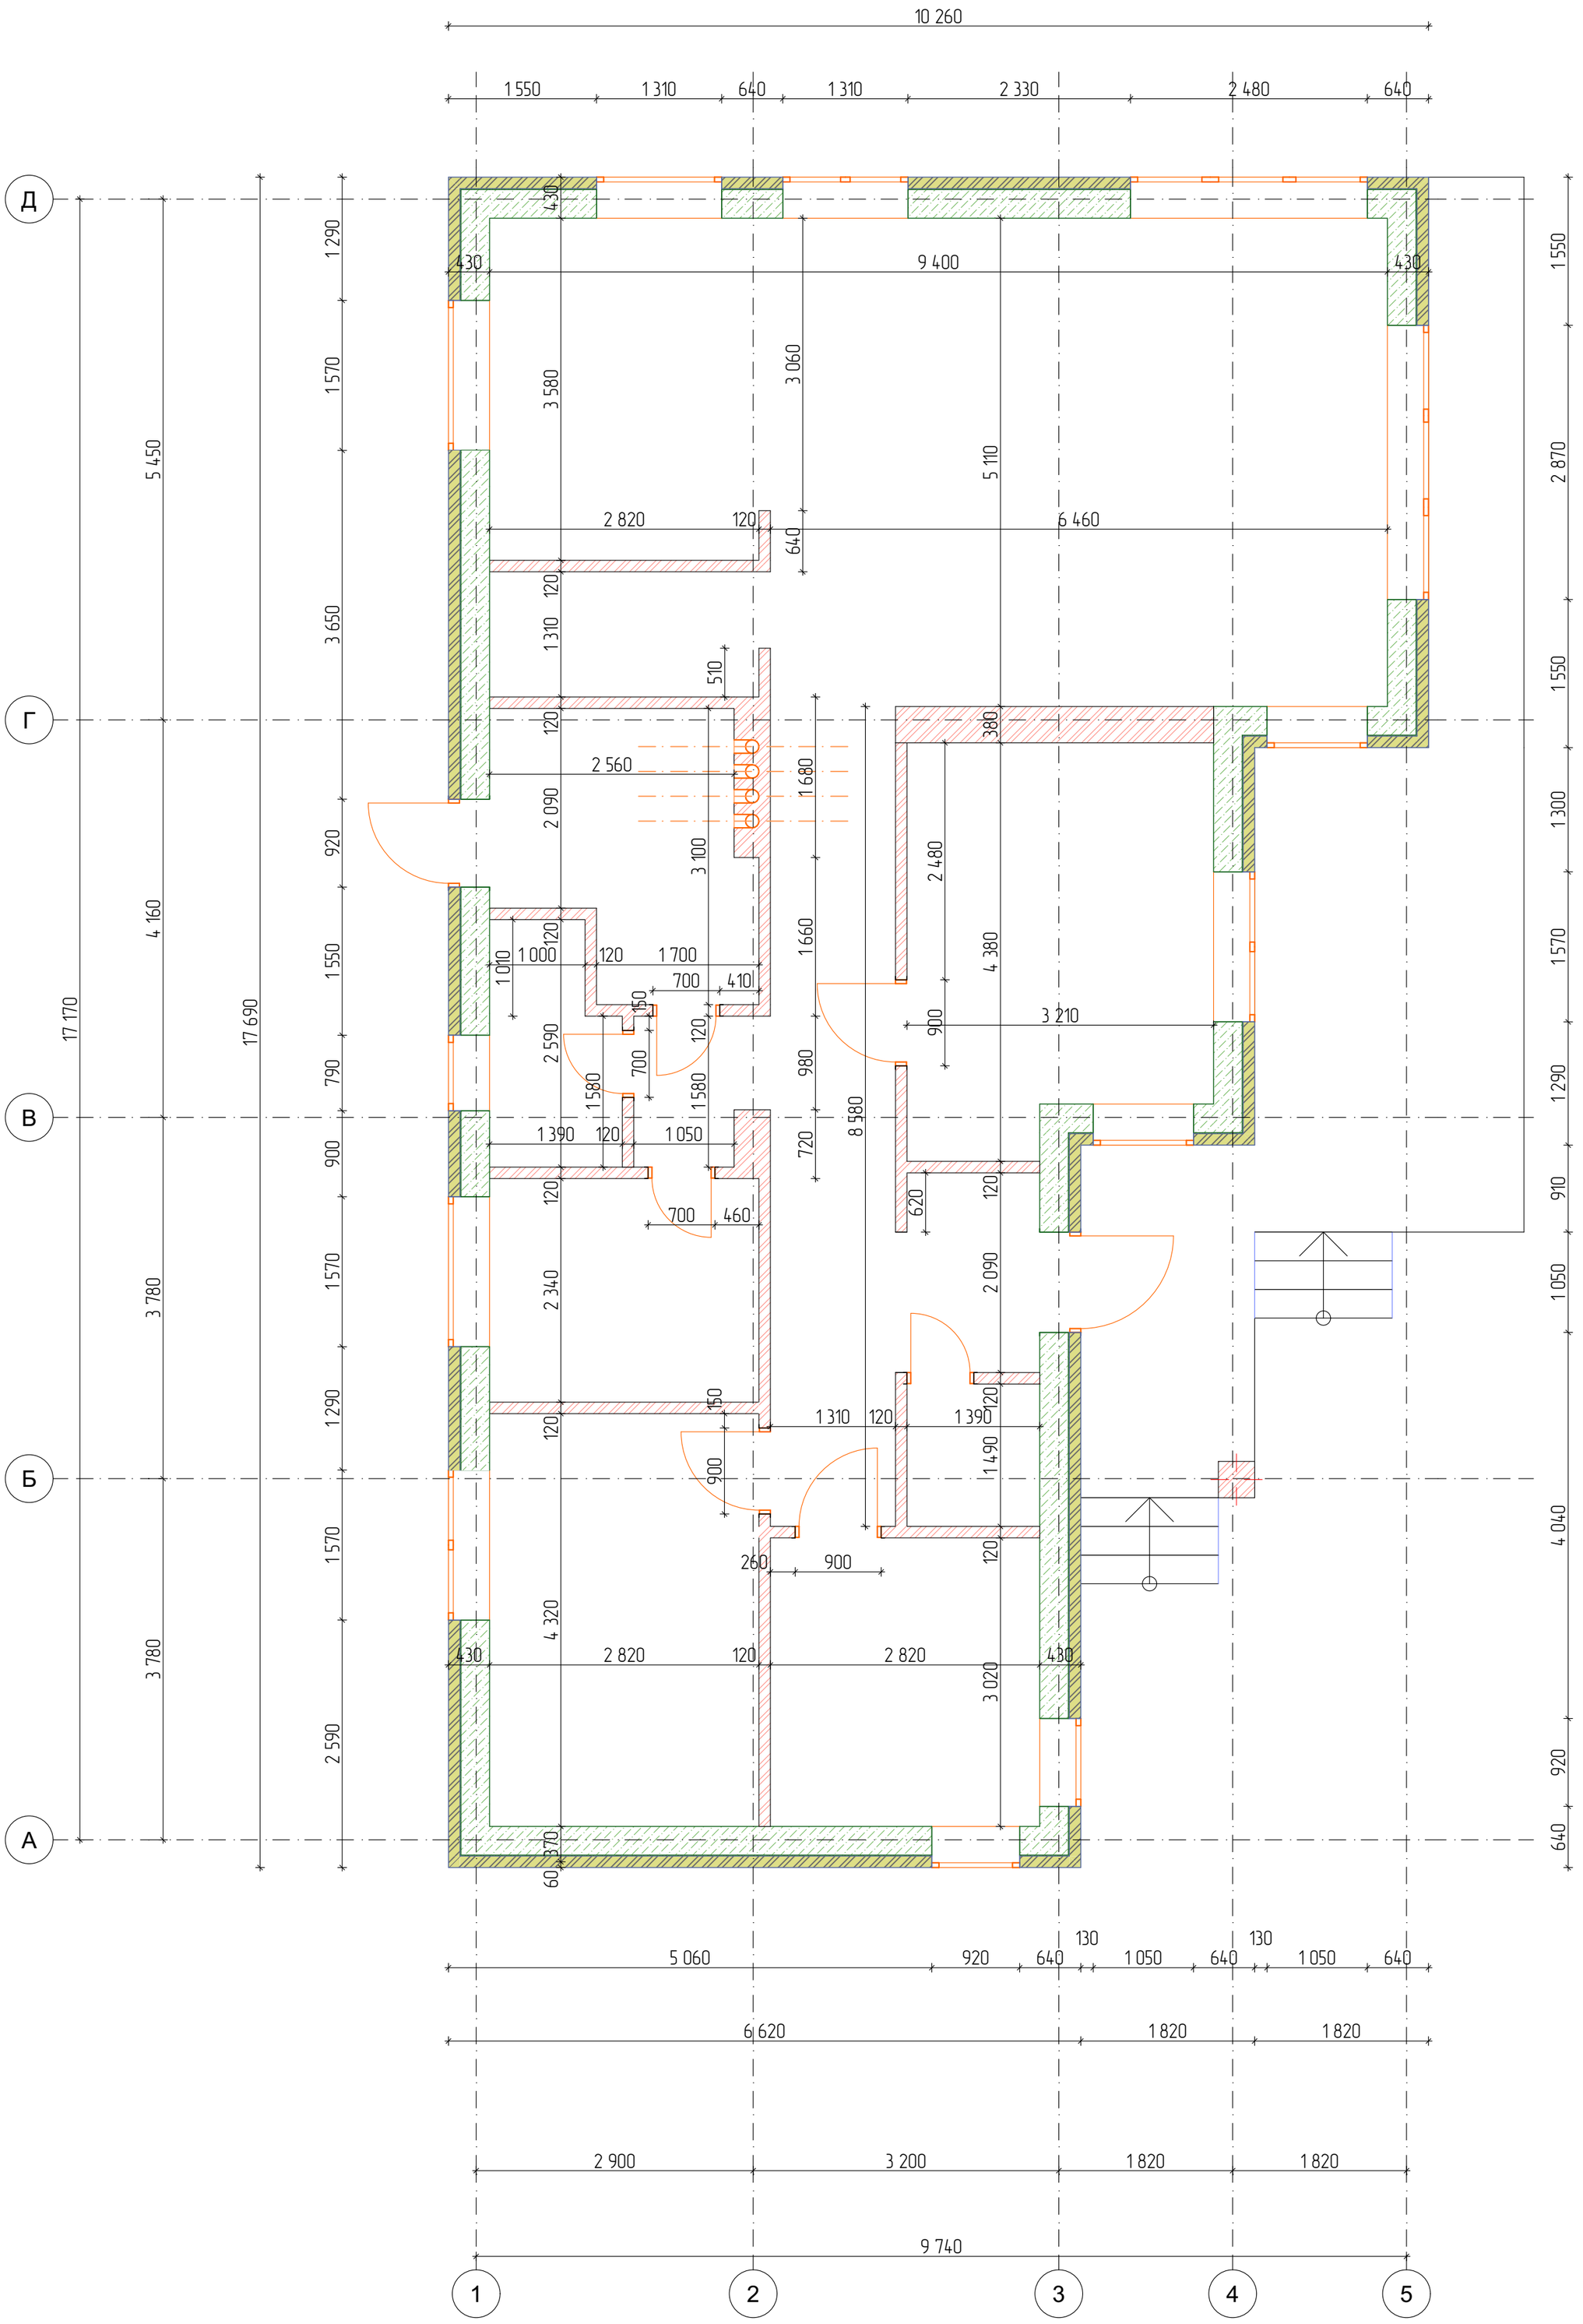


						#ID Проекта	
						кадастровый номер Россия	
Изм.	Кол.уч.	Лист	№Док.	Подп.	Дата		
Разраб.						Индивидуальный жилой дом	Стадия: ЭП; Лист: 07; Листов:
						План 1 этажа	

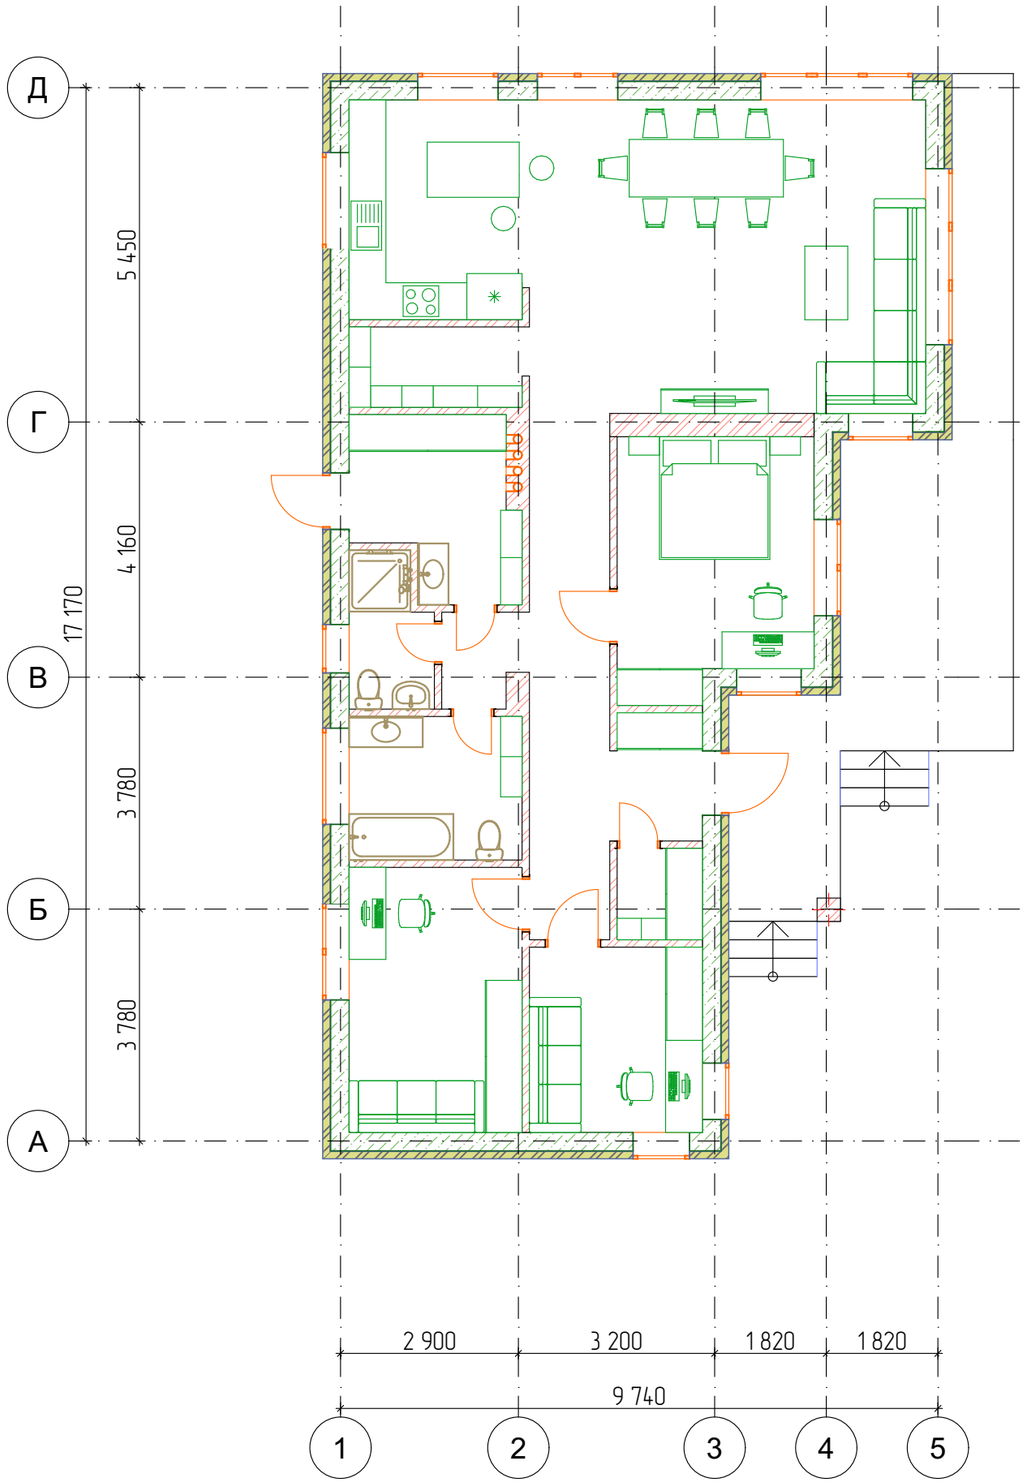


						#ID Проекта
						кадастровый номер Россия
Изм.	Кол.уч.	Лист	№Док.	Подп.	Дата	
Разраб.						Индивидуальный жилой дом
						План расстановки мебели 1 этаж

Стадия	Лист	Листов
ЭП	25	

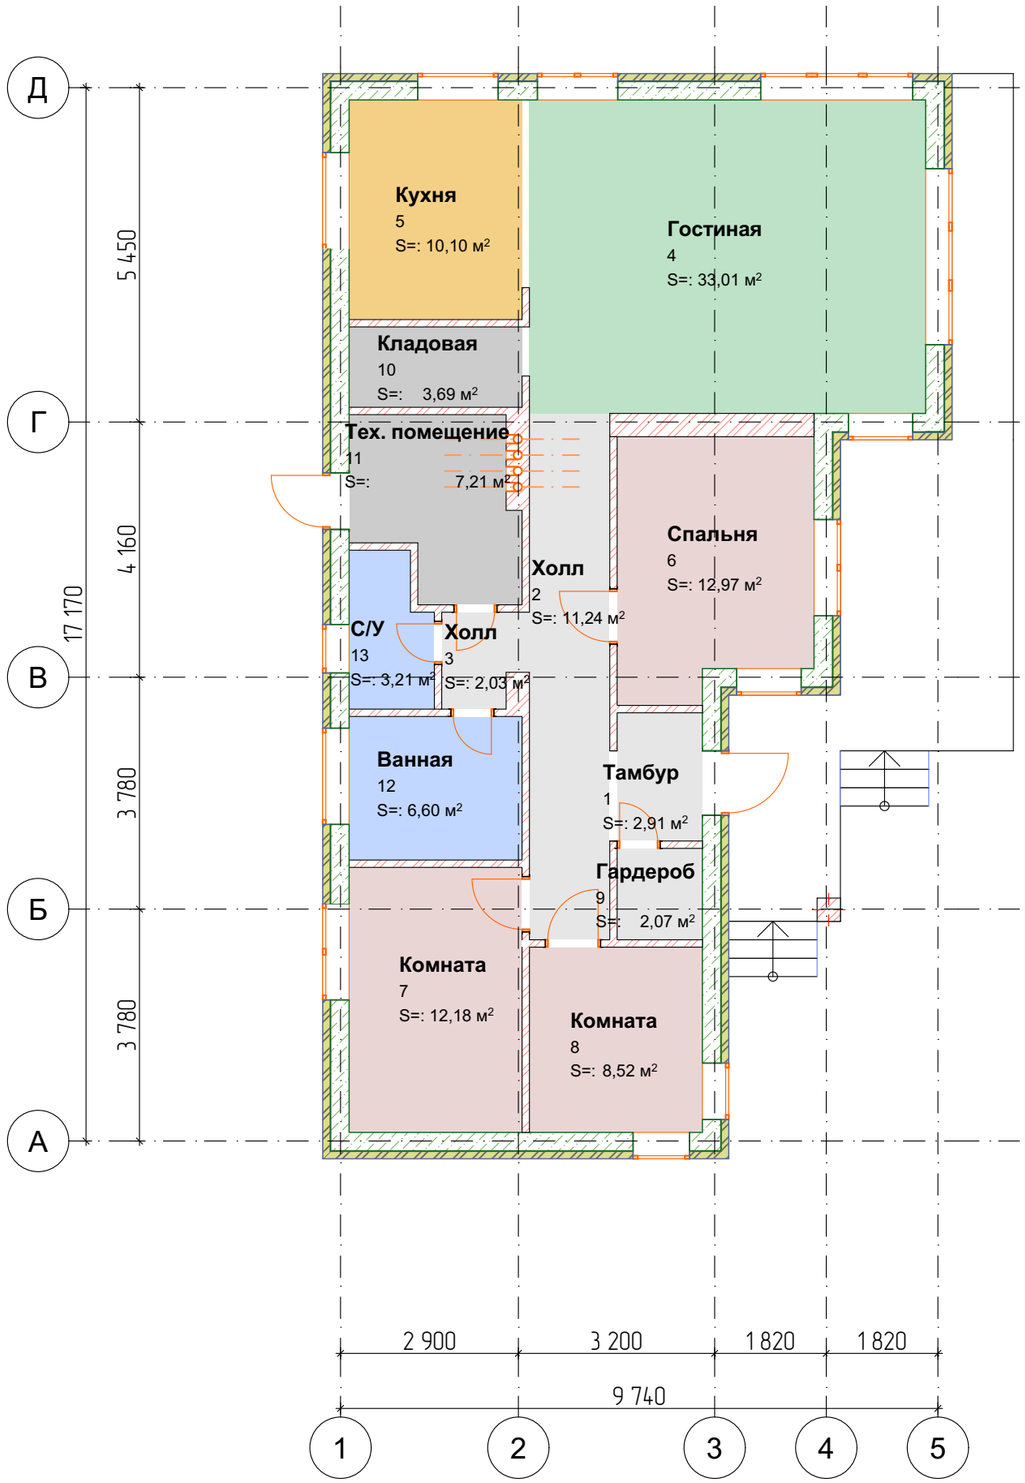


№	Наименование	Площадь
1	Тамбур	2,91
2	Холл	11,24
3	Холл	2,03
4	Гостиная	33,01
5	Кухня	10,10
6	Спальня	12,97
7	Комната	12,18
8	Комната	8,52
9	Гардероб	2,07
10	Кладовая	3,69
11	Тех. помещение	7,21
12	Ванная	6,60
13	С/У	3,21
		115,74 м²

Изм.	Кол.уч.	Лист	№Док.	Подп.	Дата	#ID Проекта			
						кадастровый номер Россия			
Разраб.						Индивидуальный жилой дом	Стадия	Лист	Листов
							ЭП	28	
						Экспликация помещений 1- го этажа			

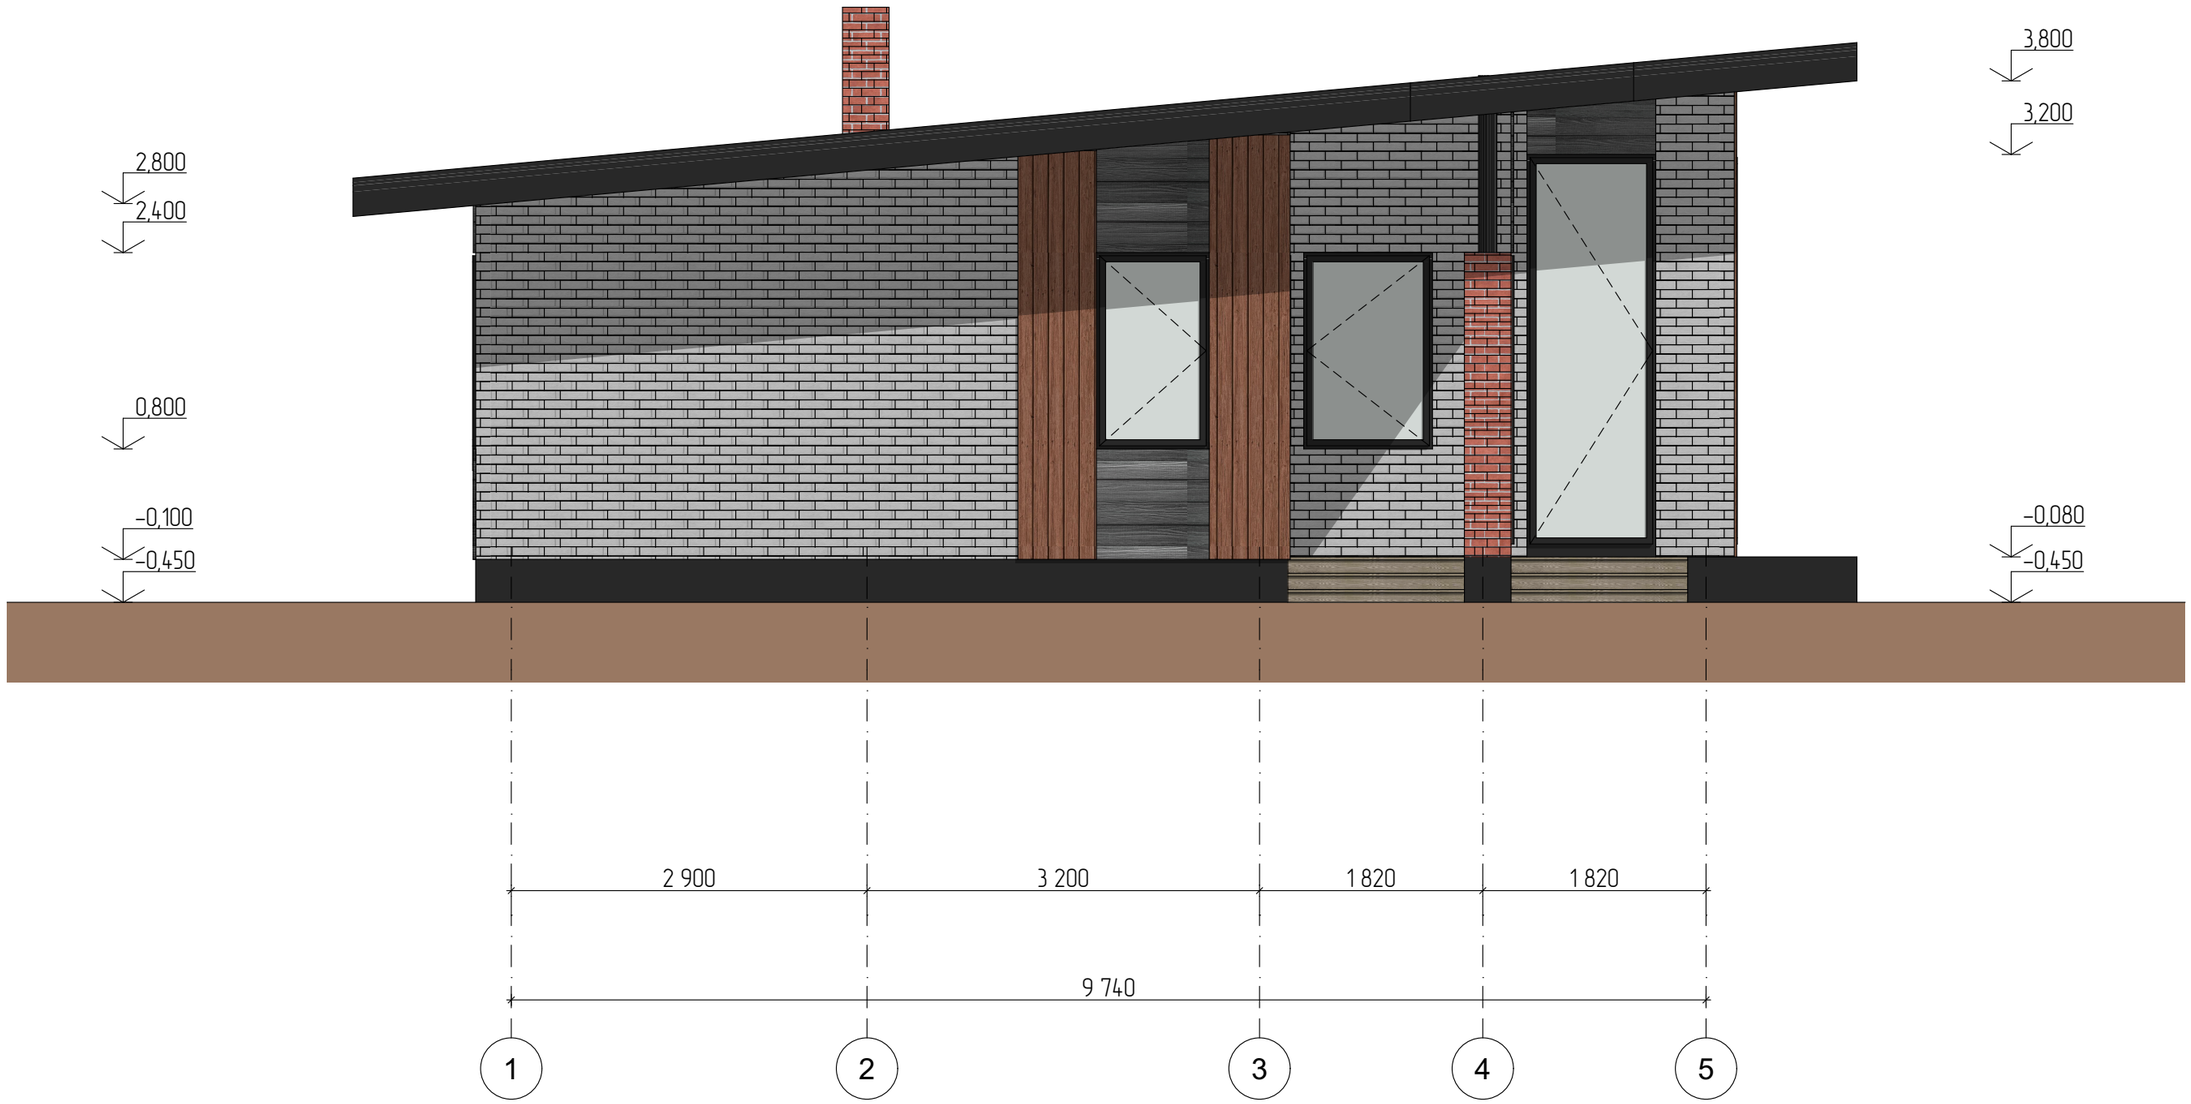

						#ID Проекта
						кадастровый номер Россия
Изм.	Кол.уч.	Лист	№Док.	Подп.	Дата	
Разраб.						Индивидуальный жилой дом
						Фасад в осях 1-5


Стадия	Лист	Листов
ЭП	31	

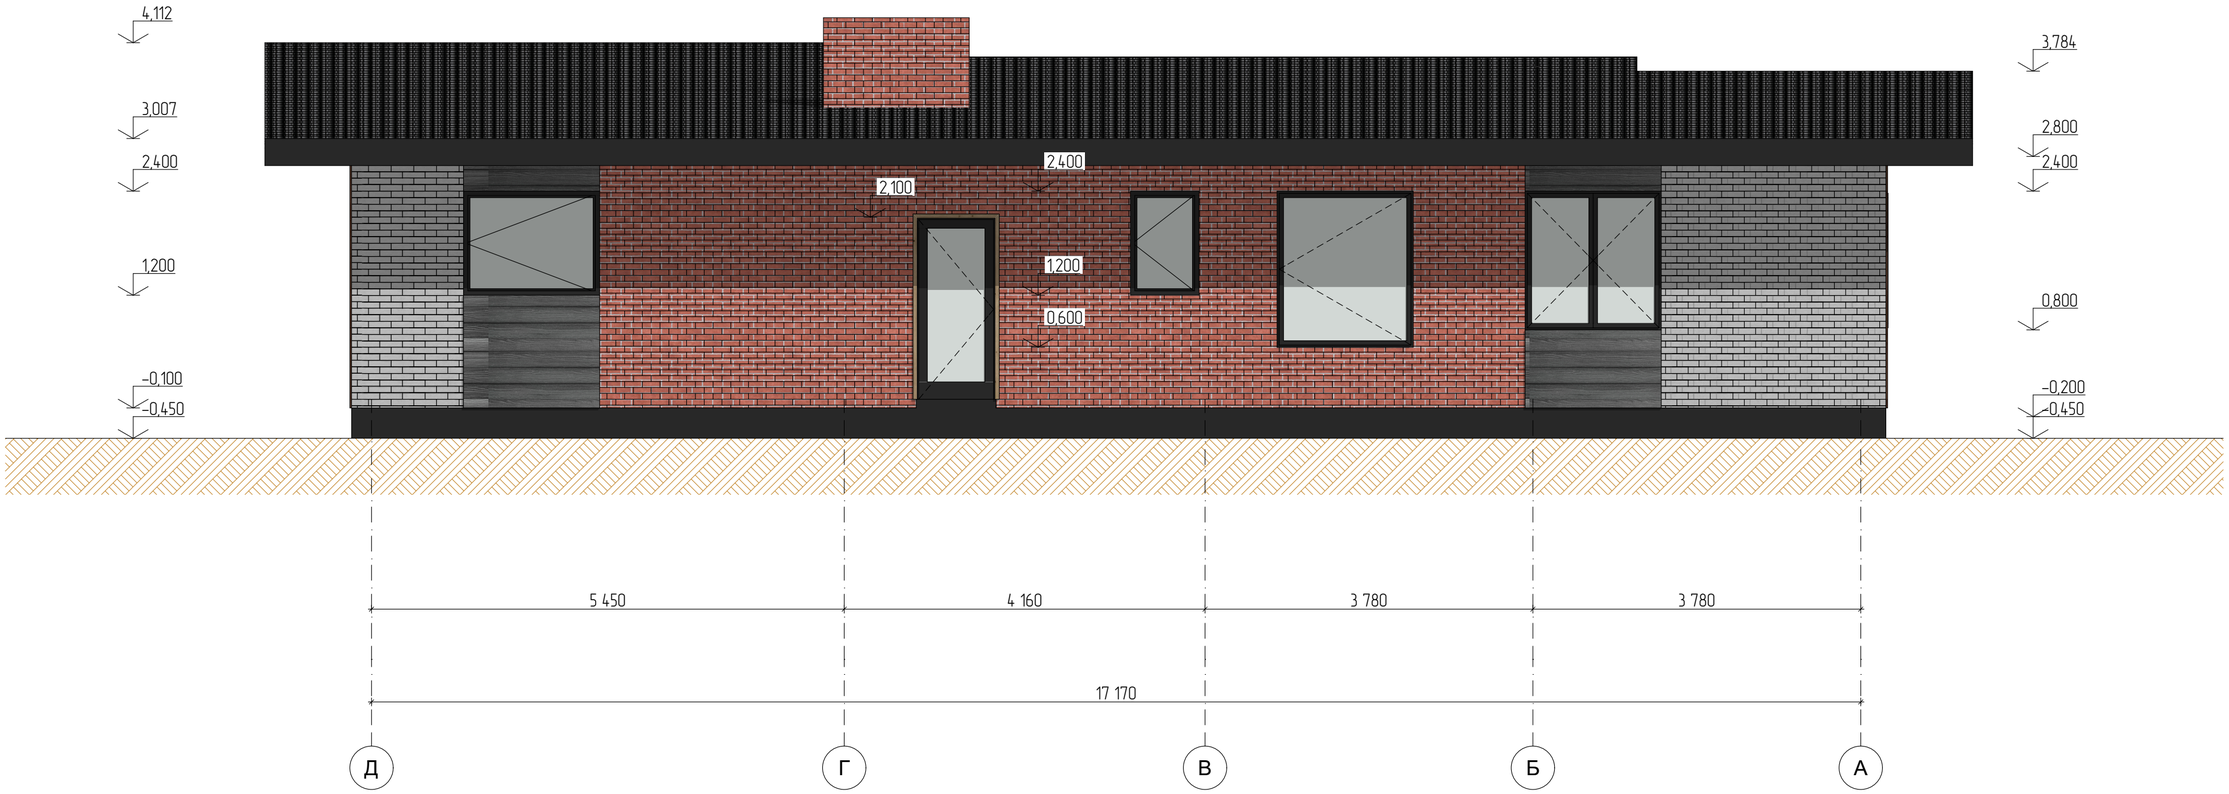

						#ID Проекта	
						кадастровый номер Россия	
Изм.	Кол.уч.	Лист	№Док.	Подп.	Дата		
Разраб.						Индивидуальный жилой дом	Стадия: ЭП; Лист: 32; Листов:
						Фасад в осях Д-А	



						#ID Проекта	
						кадастровый номер Россия	
Изм.	Колуч.	Лист	№Док.	Подп.	Дата		
Разраб.						Индивидуальный жилой дом	Стадия: ЭП; Лист: 33; Листов:
						Фасад в осях А-Д	

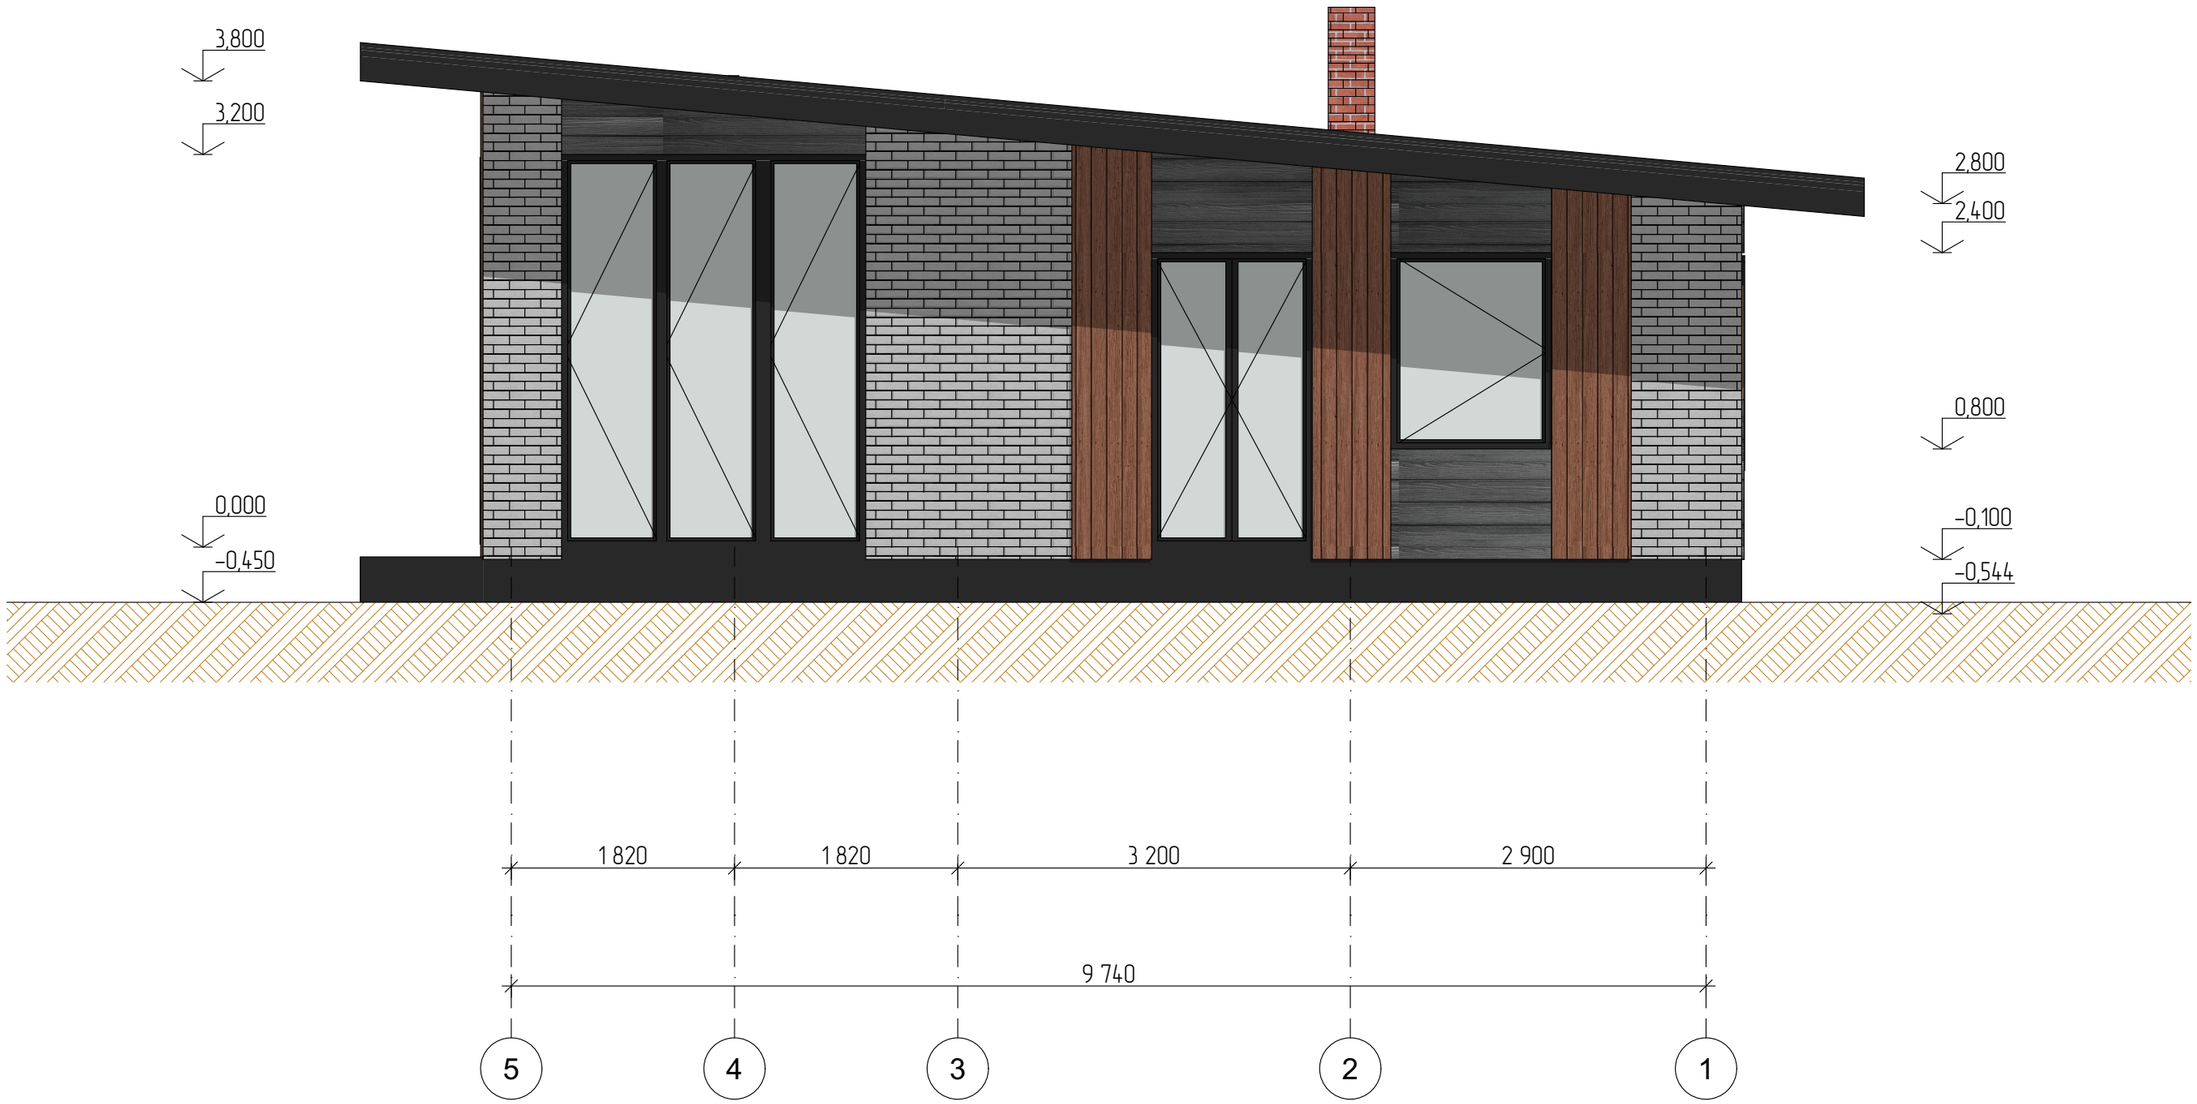

						#ID Проекта
						кадастровый номер Россия
Изм.	Кол.уч.	Лист	№Док.	Подп.	Дата	
Разраб.						Индивидуальный жилой дом
						Фасад в осях 5-1

Стадия	Лист	Листов
ЭП	34	