

М 1:100

Кладочный план 1 этаж



17 700
1 275
1 800
1 550
1 800
1 275
ОК-4
ОК-4
5 000
1 500
900
1 200
200
900
5 000
2 500
3 900
150
2 900
2 870
1 870
250
Д-2
Д-2
ОК-3
4 625
250
780
4 890
250
250
780
ОК-5
3 510
2 475
150
2 000
К-2
К-1
К-2
К-1
К-2
575
960
330
Д-1
ДН-1П
950
940
660
630
940
2 550
Д-1
П/П
П/П
940
940
670
600
2 300
Д-1
ДН-1
ДН-2
К-2
К-2
К-1
К-2
565
3 120
4 625
ОК-3
3 350
250
3 350
ОК-5
ОК-2
ОК-2
6 950
1 125
3 140
735
735
3 140
1 125
435
435
ОК-1
ОК-1
810
2 640
800
2 640
810
5 000
7 700
5 000
1 400
5 000
3 750
3 750
5 000
1 400
20 300
13 900
12 700
8 950
9 200
9 700
2 600
2 150
2 600
1 500
1 400
1 500
1 500
1 500


М 1:150

Кладочный план_диагонали

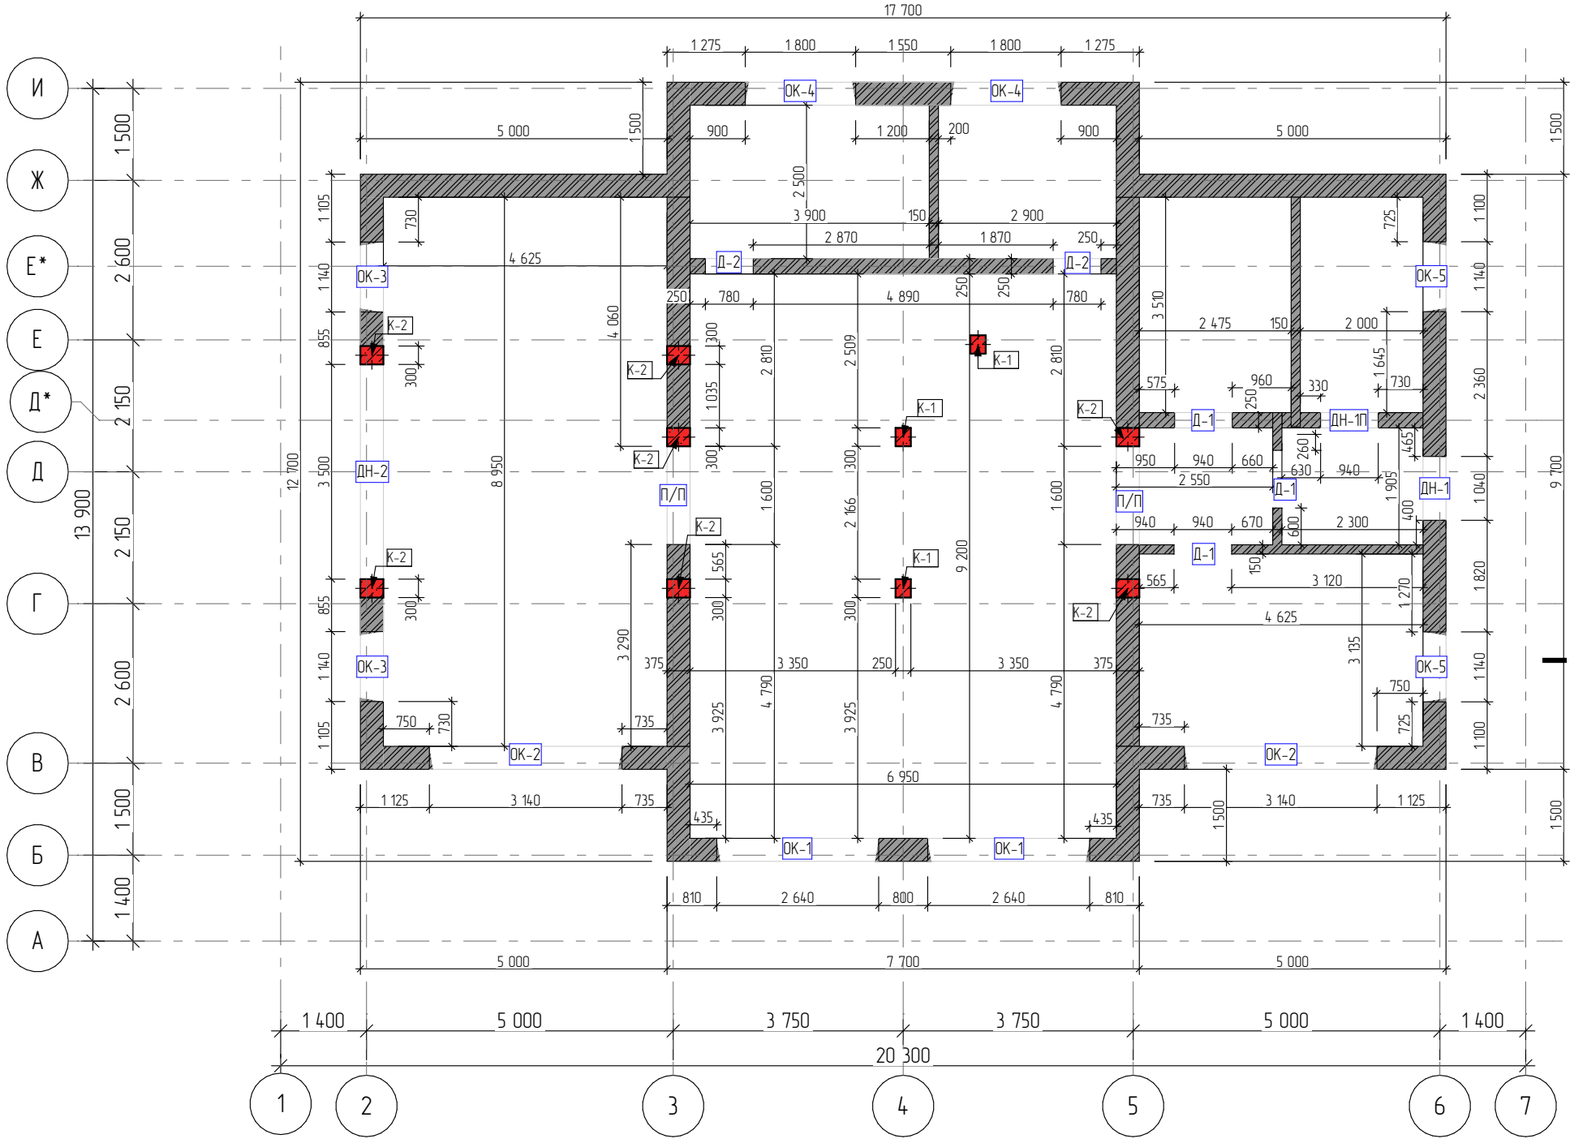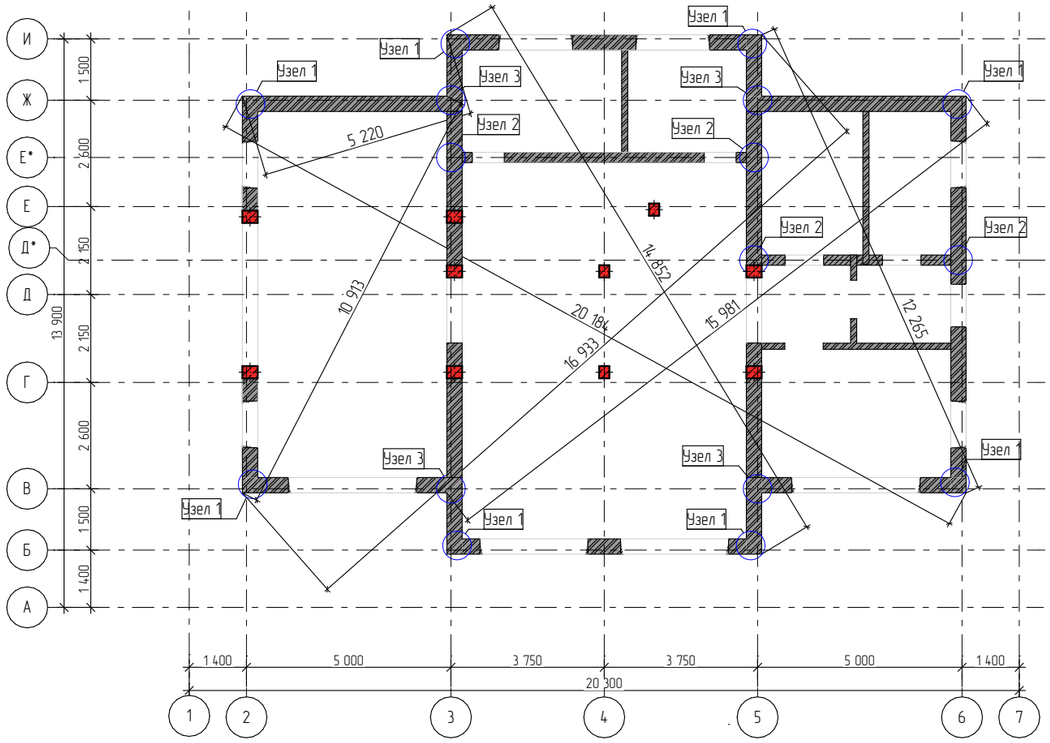



Узел 1

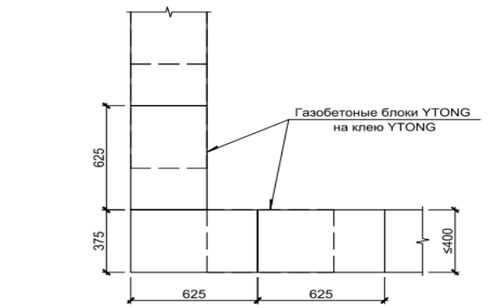

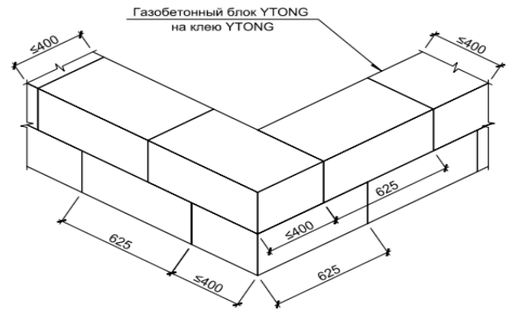


Узел 2

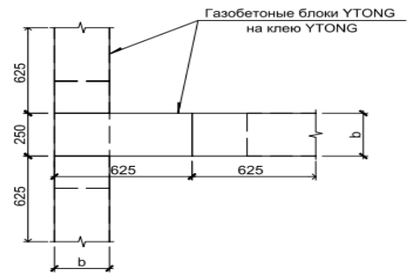

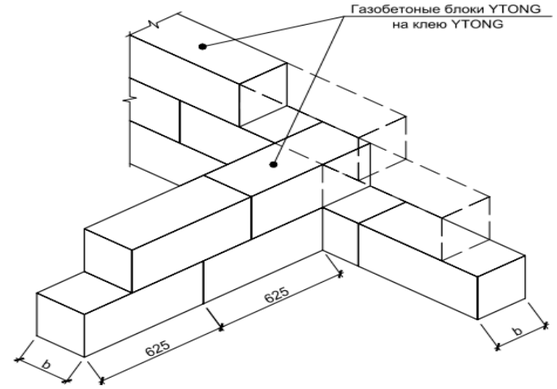


Узел 3

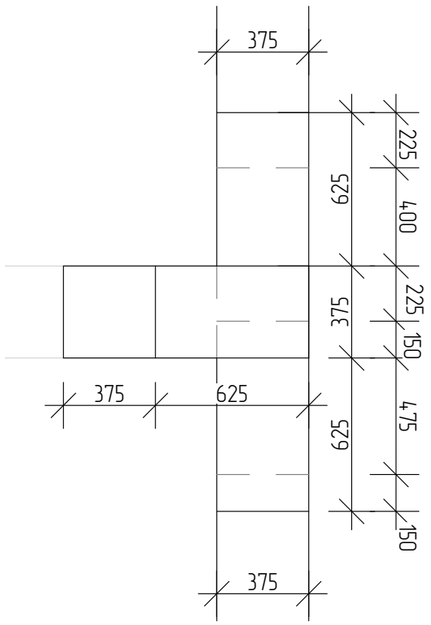


М 1:100

Кладка (вид1)

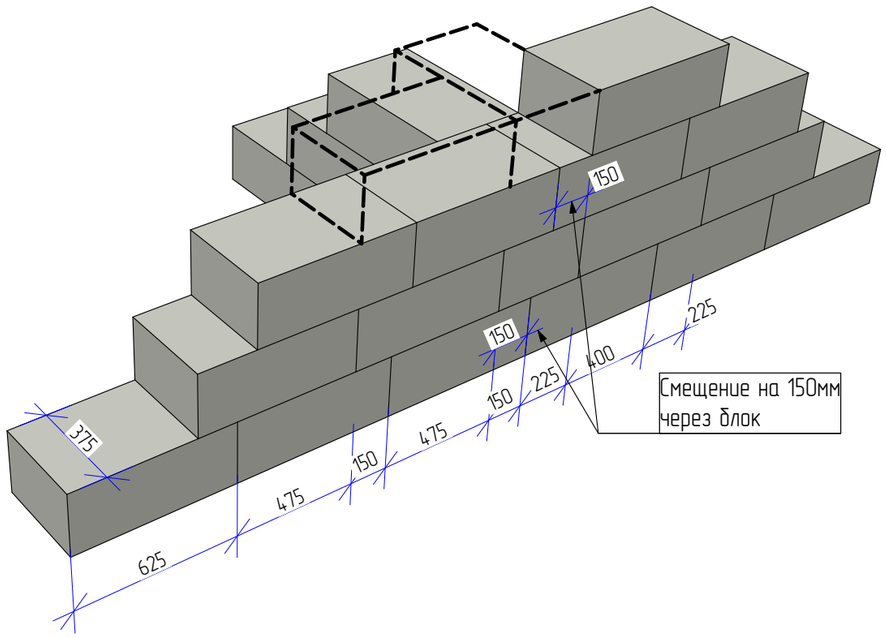

М 1:100

Кладка (вид2)

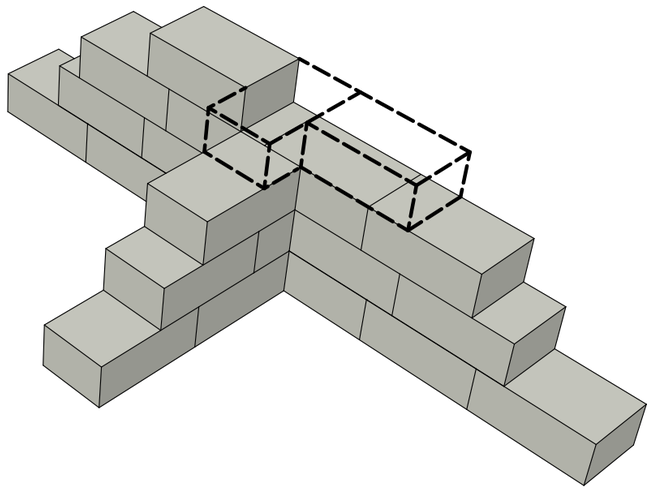

Согласовано

Взам инв. №

Подпись и дата

Инв. № подл


Кладочный план_диагонали

Лист

2


М 1:100

ЖБ плита межэтажная

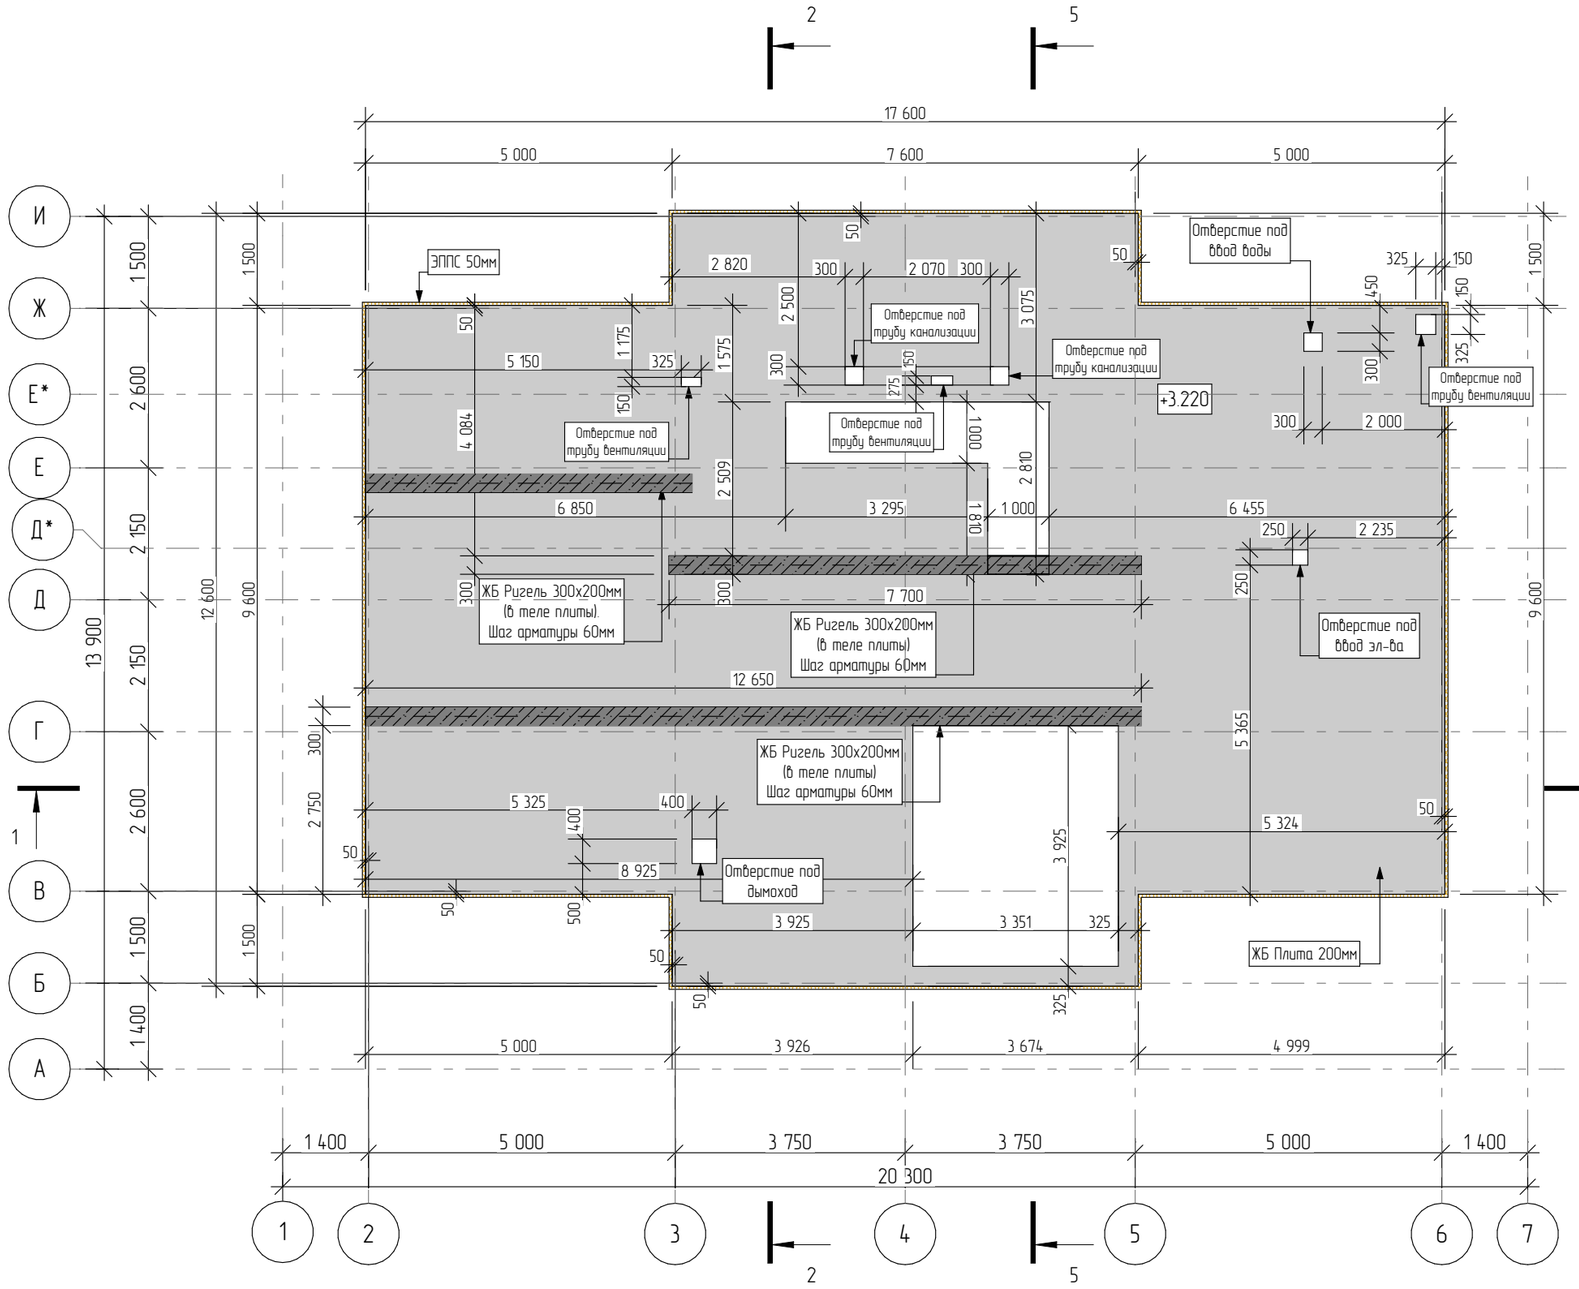

ЖБ Ригель 300х200мм (в теле плиты)

М 1:10

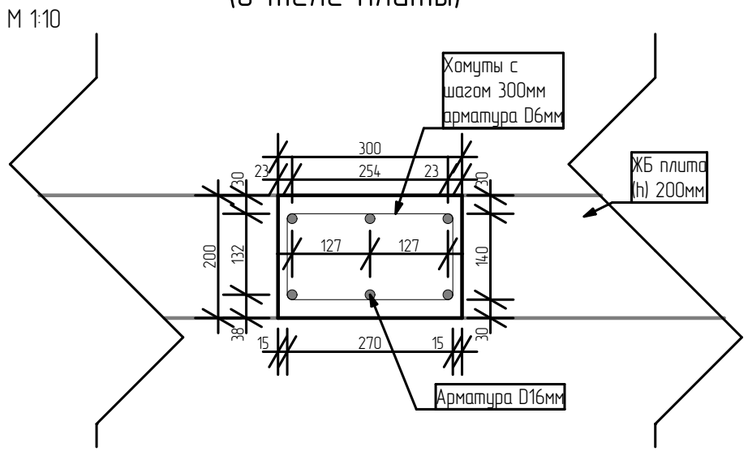

Согласовано:

Взам. инв. №

Подпись и дата

Инв. № подл.

					2021
Изм.	Кол.уч	Лист	№док.	Подпись	Дата
Архитектор		Салыкова В.Г.			
Заказчик		#Обращение к Заказчику			


#ID Проекта

Адрес: #Полный Адрес Участка


Индивидуальный жилой дом	стадия	лист	листов
	РП	.3	
Межэтажная ЖБ плита М 1:100			

М 1:50

Стена 2

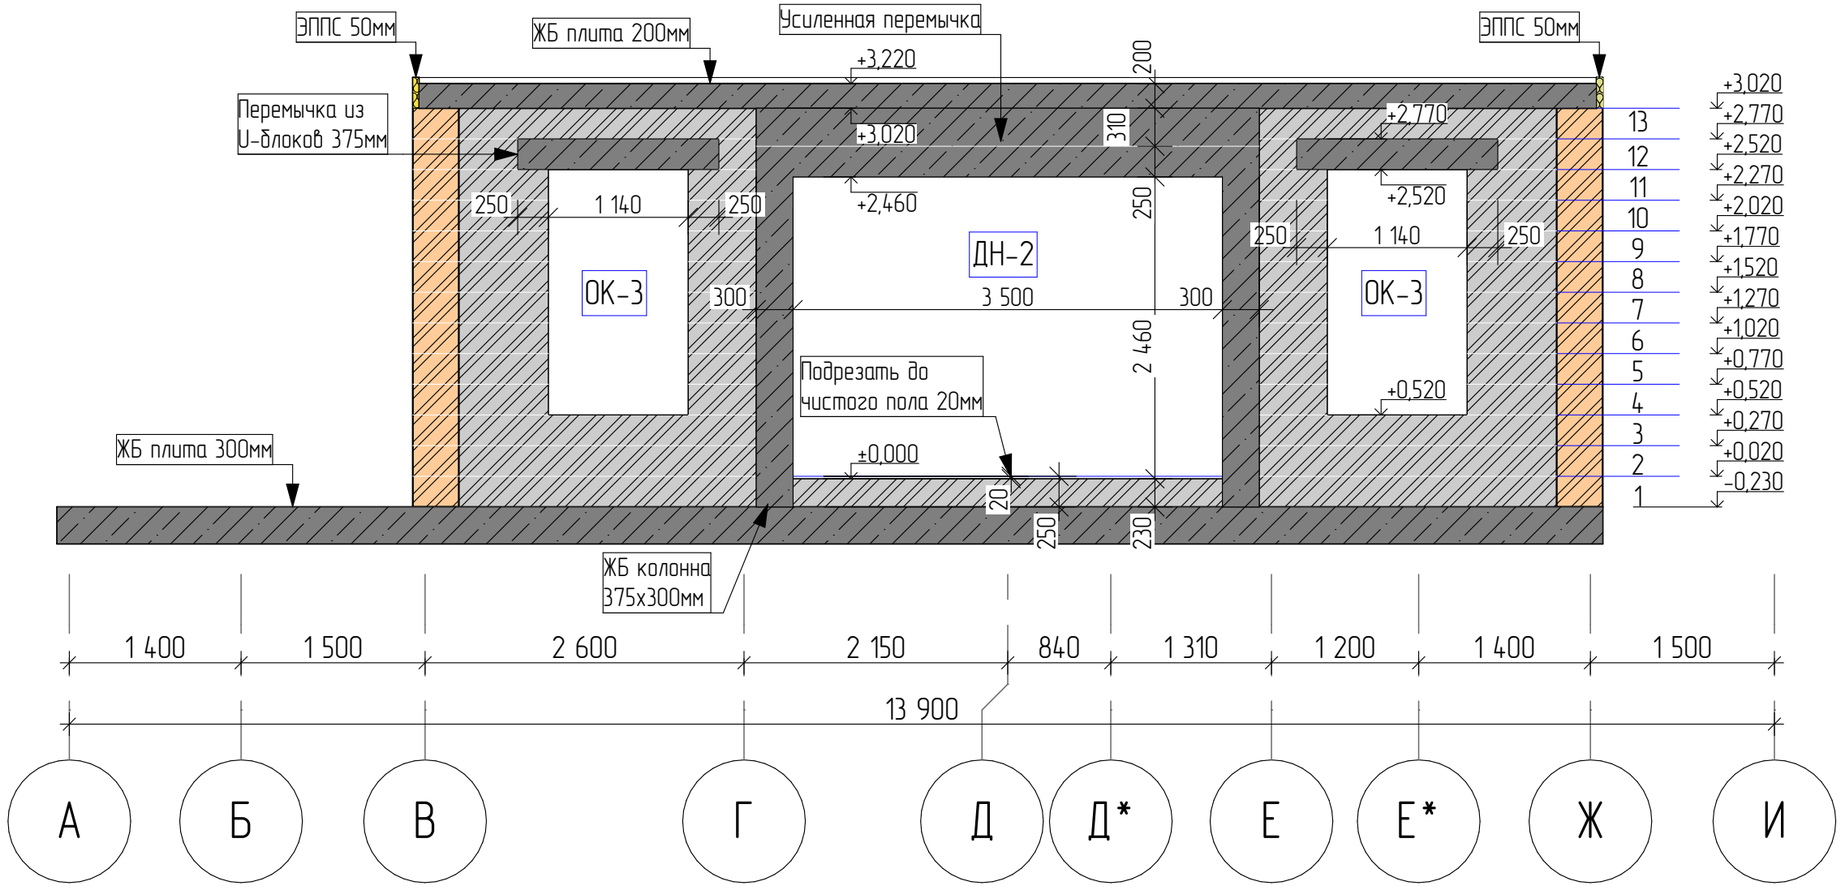

Усиленная перемычка

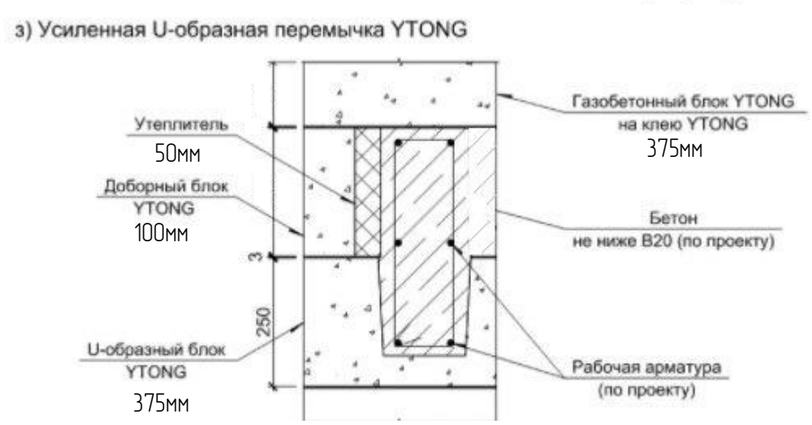

Согласовано

Взам. инв. №


Подпись и дата

Инв. № подл.


Стена 2	Лист 4

М 1:50

Стена 3

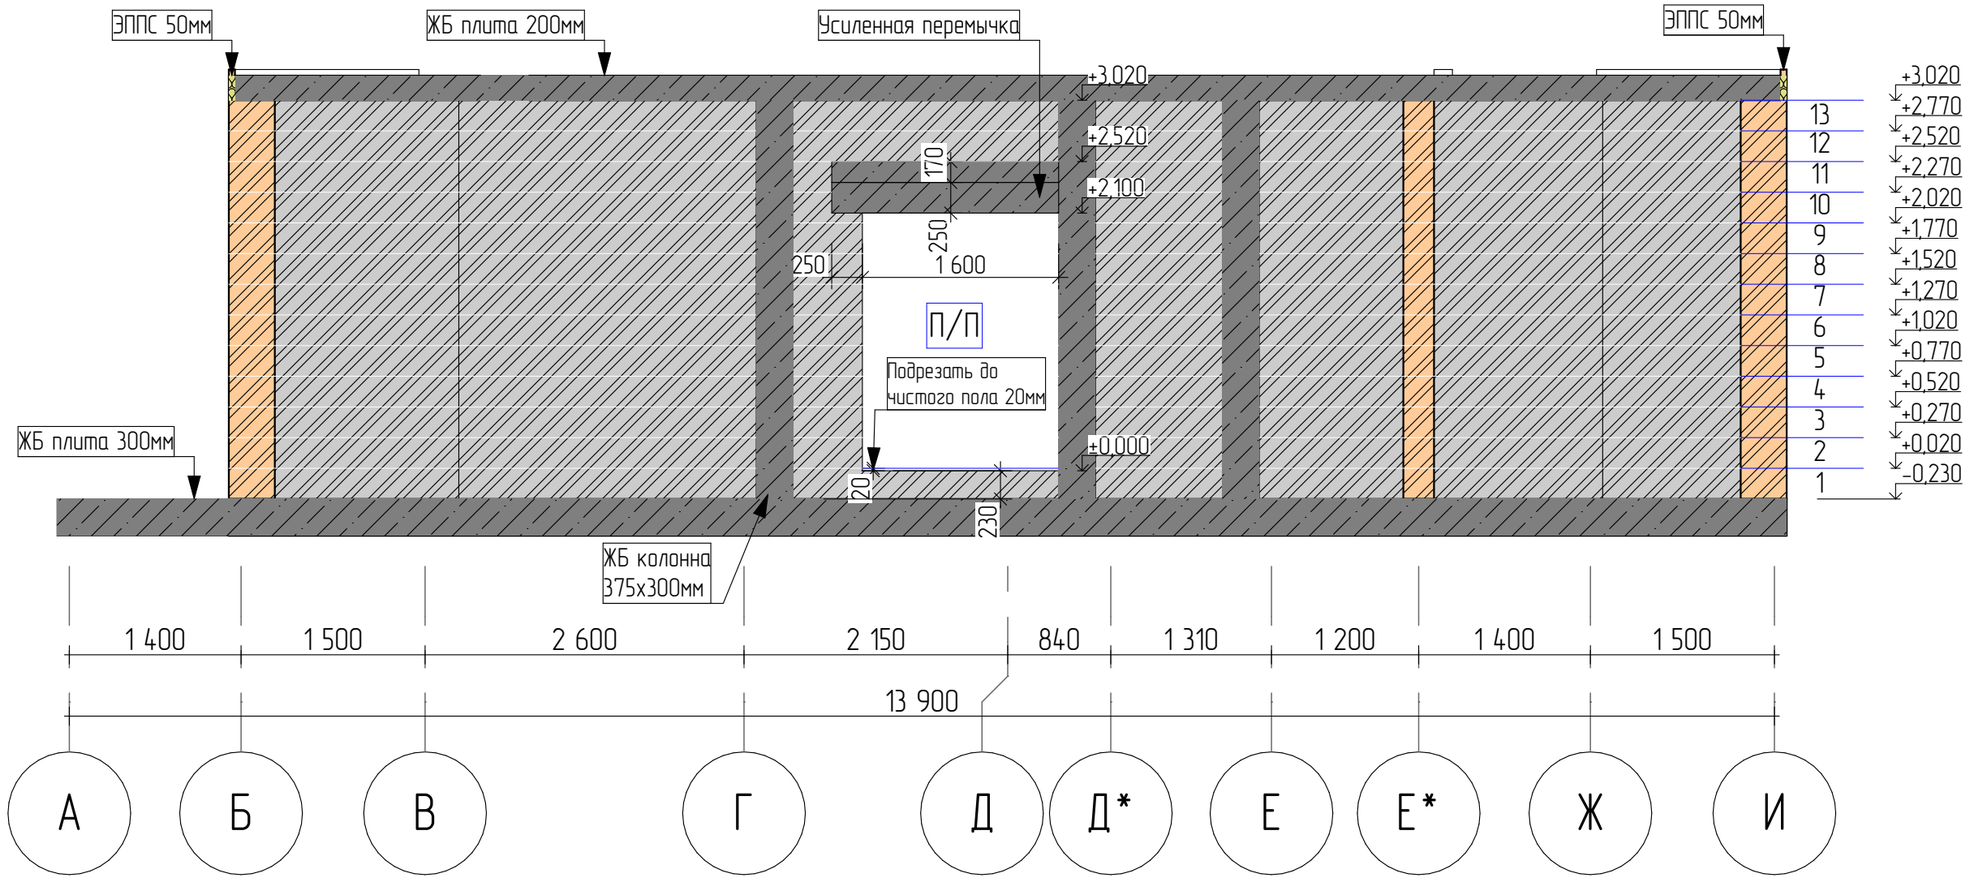

Усиленная перемычка

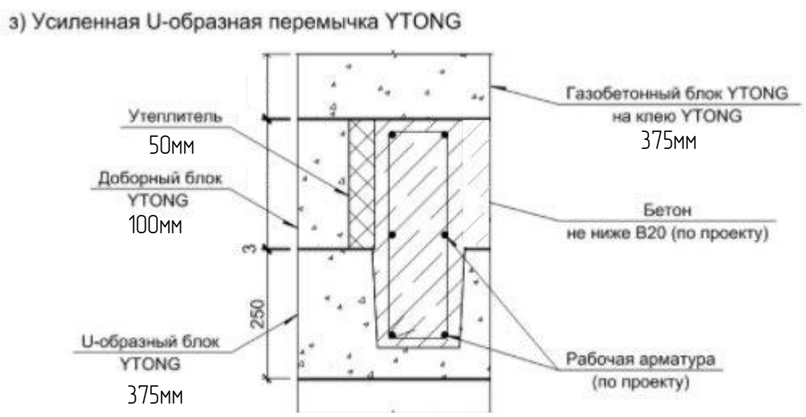

Согласовано

Взам. инв. №


Подпись и дата

Инв. № подл.

Стена 3	Лист 5


М 1:50

Стена 5

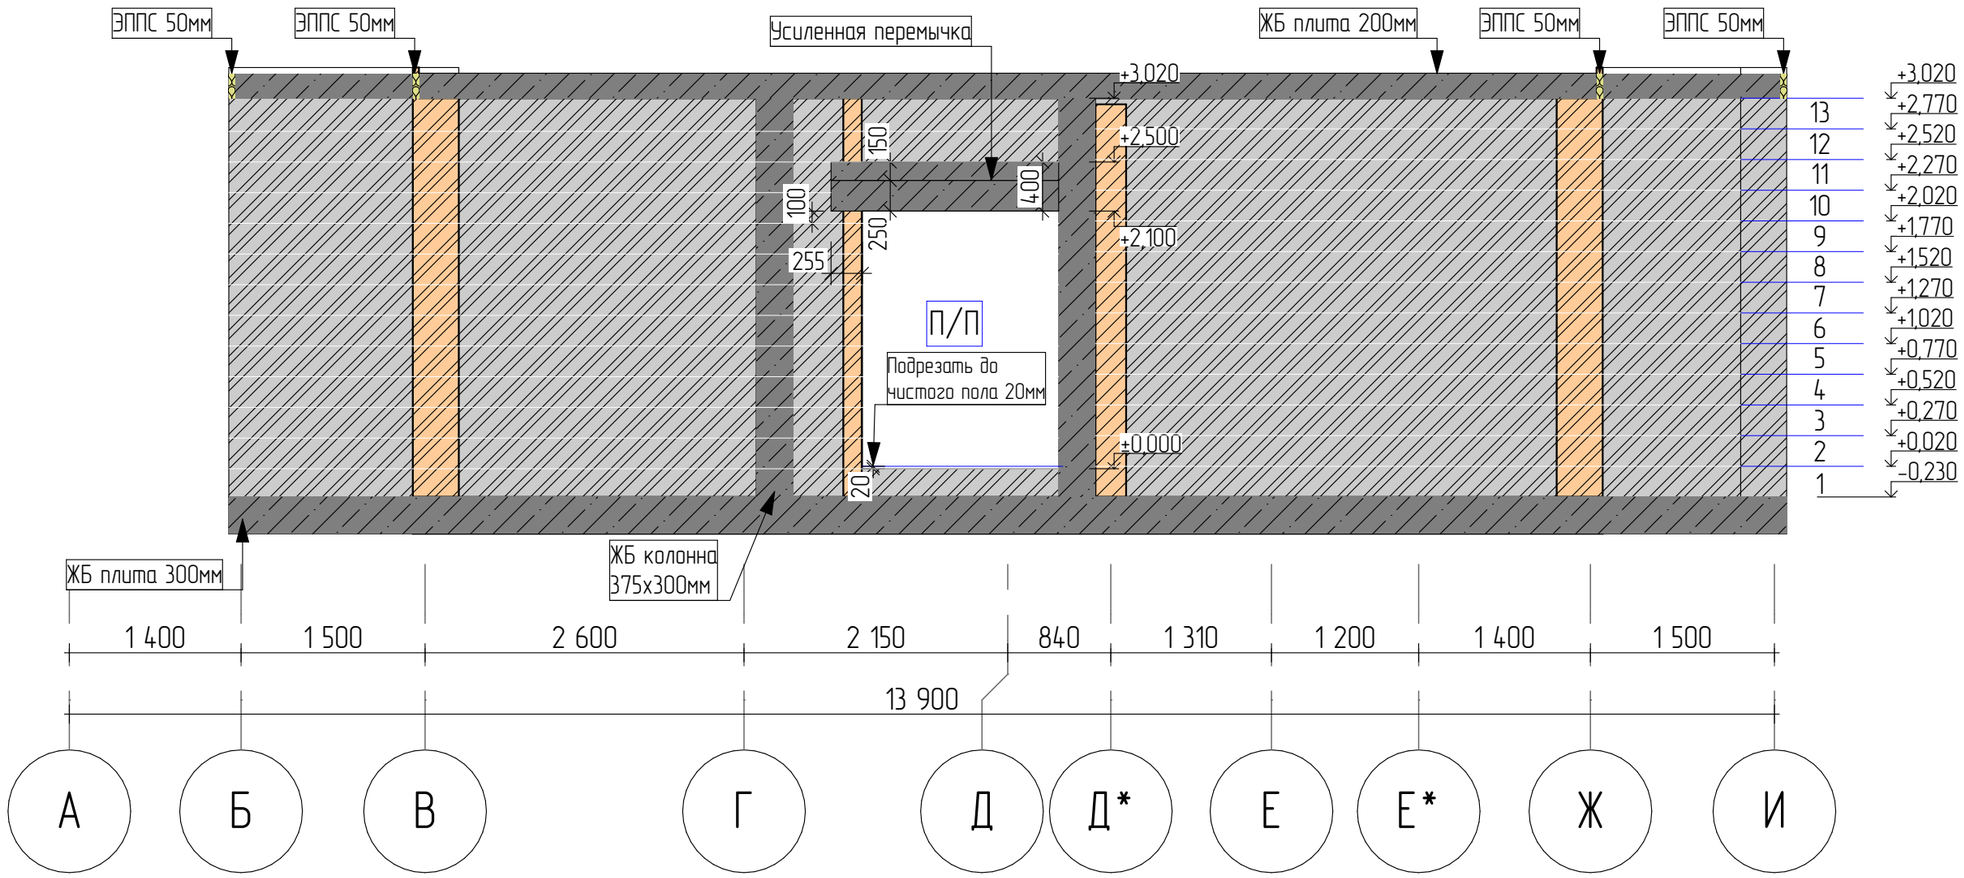

Усиленная перемычка

з) Усиленная U-образная перемычка YTONG

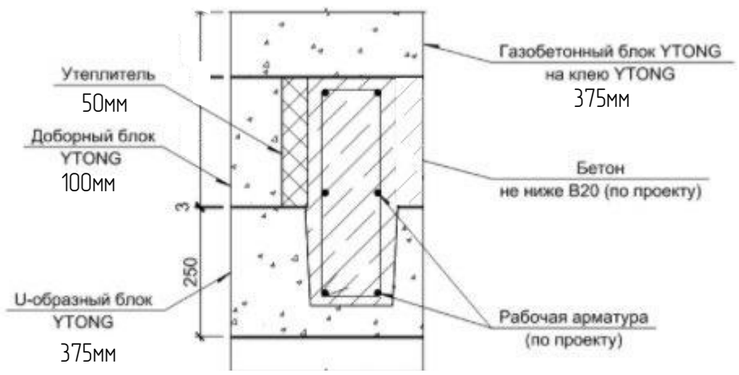

Согласовано

Взам. инв. №

Подпись и дата

Инв. № подл.


Стена 5


Лист

6

М 1:50

Стена 6

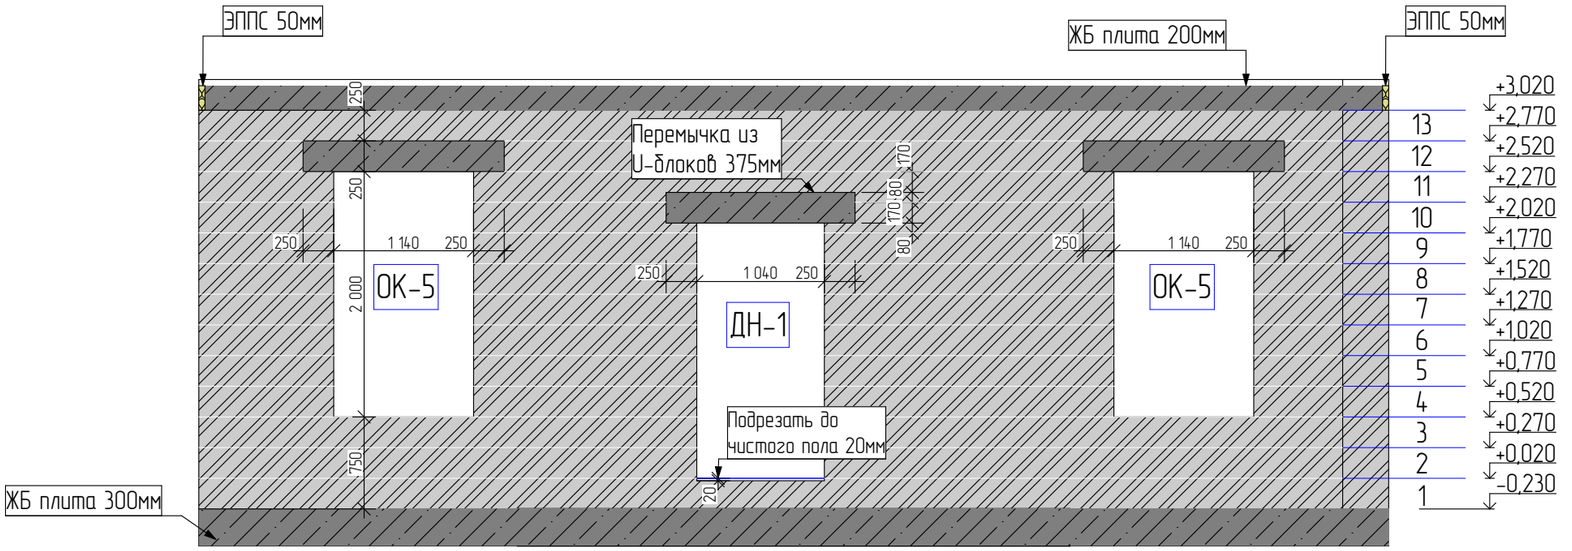

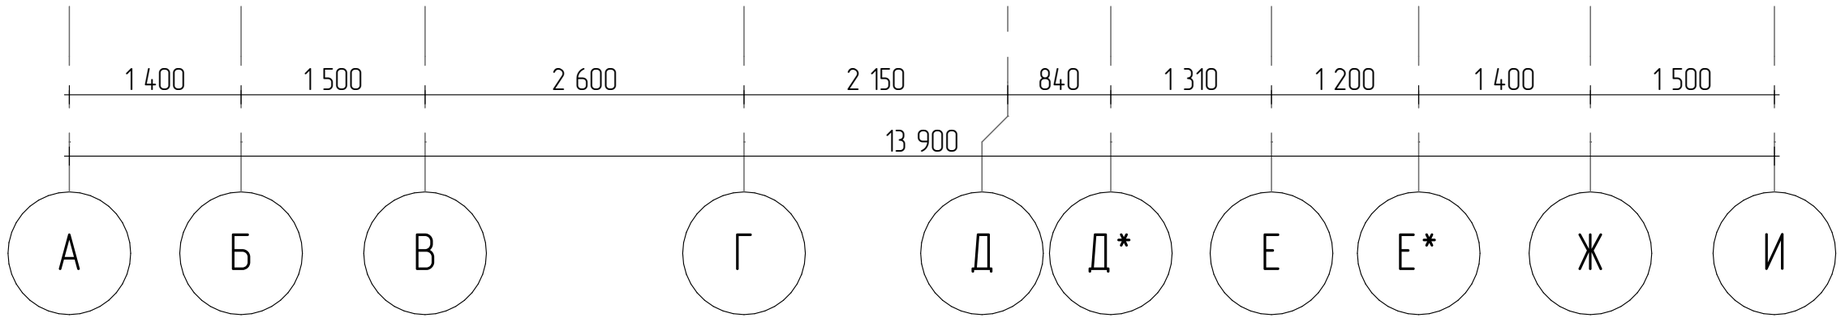

Согласовано


Взам. инв. №

Подпись и дата


Инв. № подл.

М 1:75

Стена Б

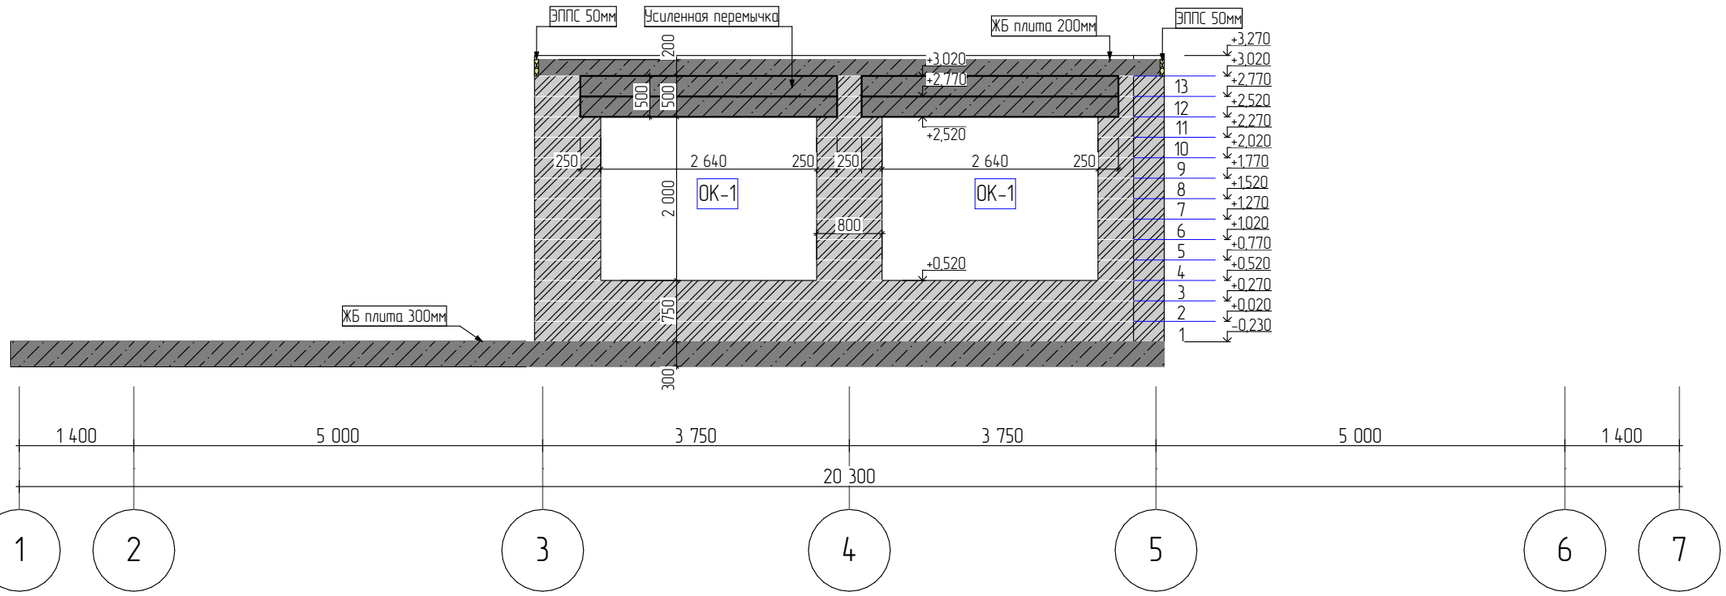

Усиленная перемычка

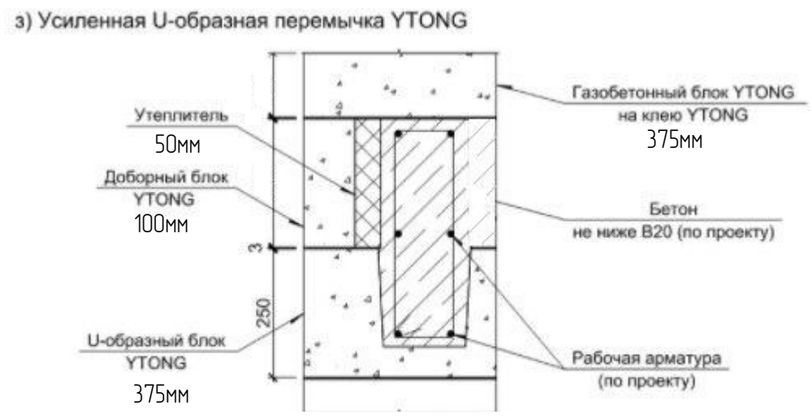

Согласовано

Взам. инв. №


Подпись и дата

Инв. № подл.


Стена Б	Лист 8

М 1:75

Стена В

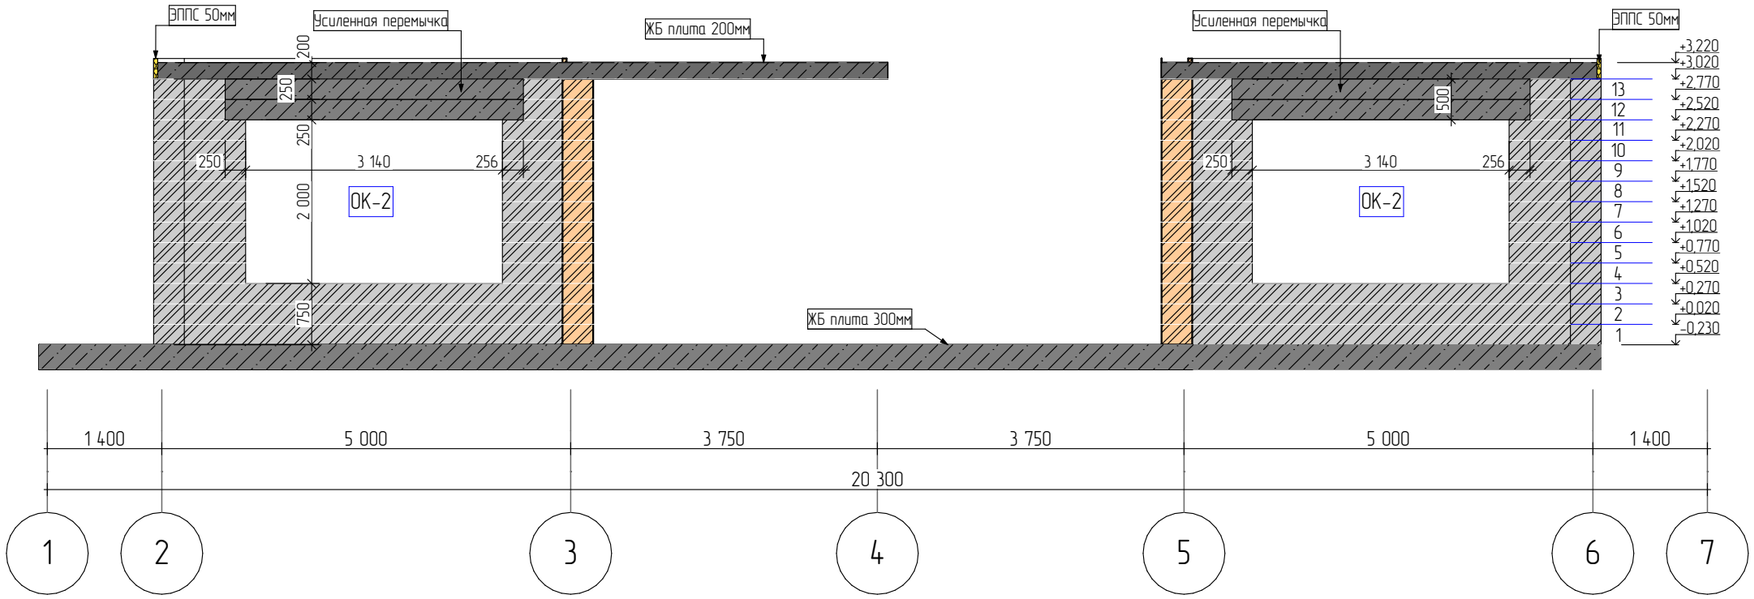

Усиленная перемычка

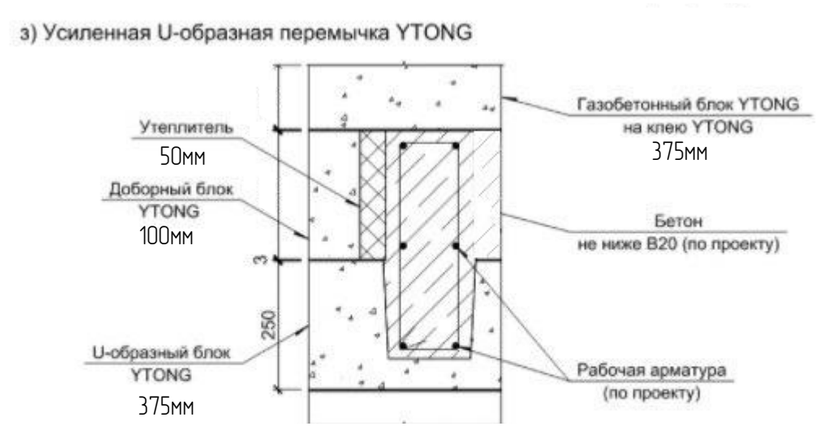

Согласовано

Взам. инв. №


Подпись и дата

Инв. № подл.

Стена В	Лист 9

М 1:75

Стена Д*

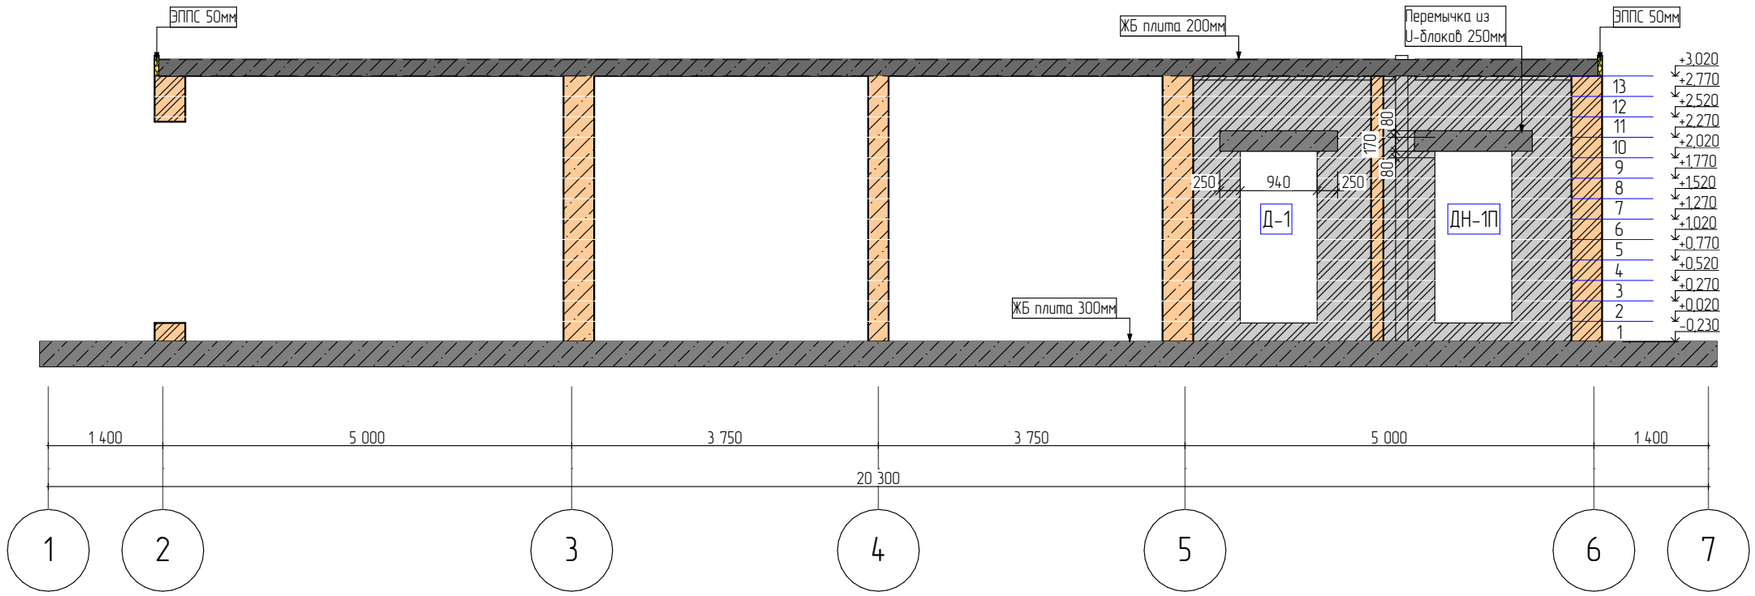

Согласовано

Взам. инв. №


Подпись и дата

Инв. № подл.

Стена Д*	Лист 10

М 1:75

Стена Е*

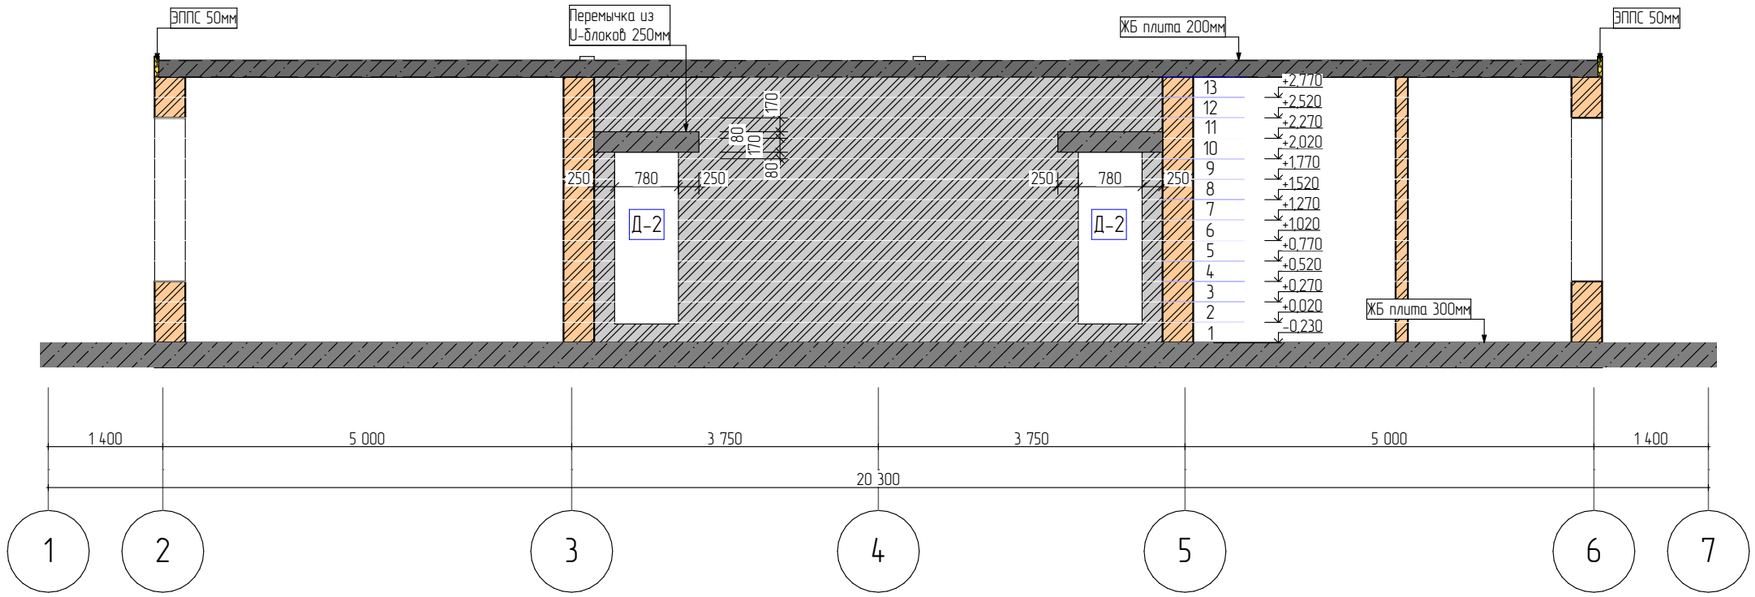

Согласовано

Взам. инв. №

Подпись и дата

Инв. № подл.


Стена Е*

Лист

11

М 1:75

Стена Ж

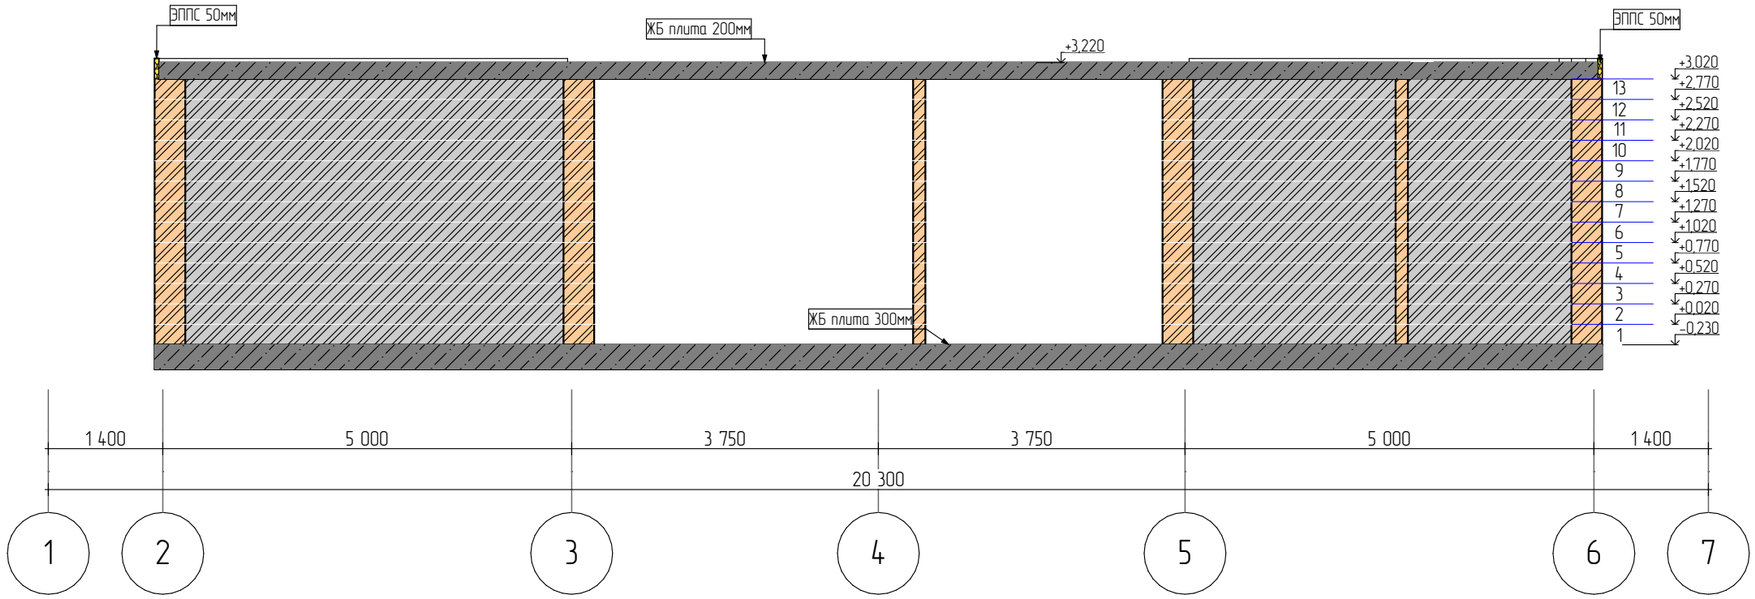

Согласовано

Взам. инв. №

Подпись и дата

Инв. № подл.


Стена Ж


Лист

12

М 1:75

Стена И

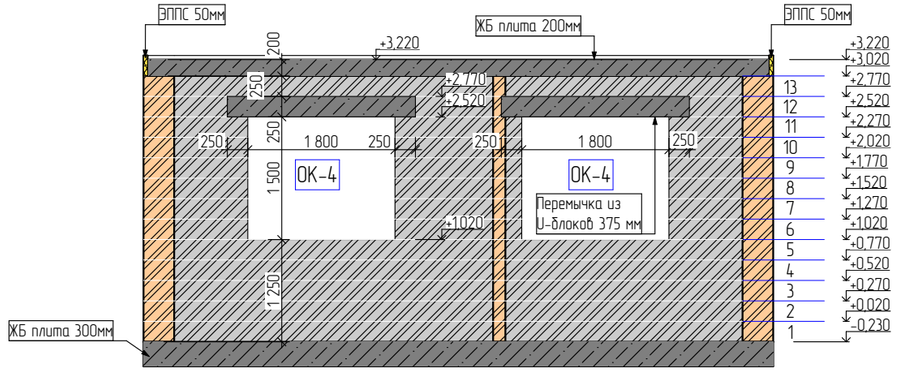

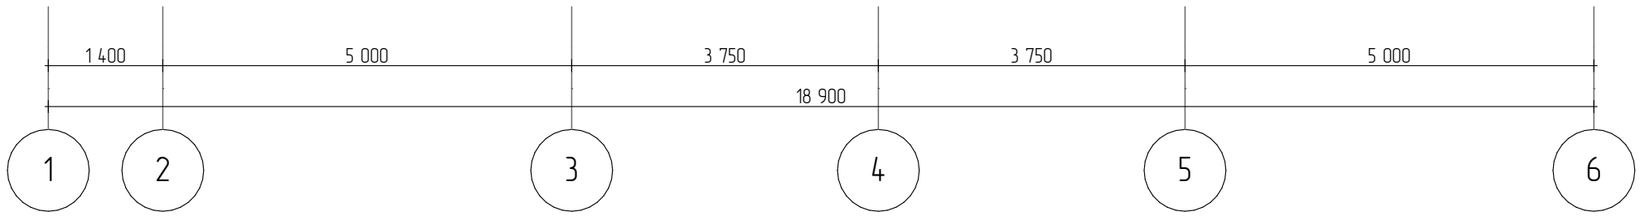

Согласовано

Взам. инв. №

Подпись и дата

Инв. № подл.

Стени И

Лист

13

ОБЪЕКТ ИНДИВИДУАЛЬНОГО ЖИЛИЩНОГО СТРОИТЕЛЬСТВА



РАБОЧИЙ ПРОЕКТ

ШИФР: #ID ПРОЕКТА

АРХИТЕКТУРНЫЕ РЕШЕНИЯ

САНКТ-ПЕТЕРБУРГ 2021

ОБЪЕКТ: ОБЪЕКТ ИНДИВИДУАЛЬНОГО ЖИЛИЩНОГО СТРОИТЕЛЬСТВА

ПО АДРЕСУ: #ПОЛНЫЙ АДРЕС УЧАСТКА; К/Н; #ID УЧАСТКА

ЗАКАЗЧИК: _____#ОБРАЩЕНИЕ К ЗАКАЗЧИКУ

АРХИТЕКТОР _____САЛЫКОВА В.Г.

РАБОЧИЙ ПРОЕКТ

ШИФР: #ID ПРОЕКТА

АРХИТЕКТУРНЫЕ РЕШЕНИЯ

САНКТ-ПЕТЕРБУРГ 2021

Согласовано:

Взам. инв. №

Подпись и дата

Инв. № подл.

Ведомость чертежей

Лист	Наименование	Примечание
	Обложка	
	Общие виды	
	Титульный лист	
2	Общие данные (начало)	
3	Общие данные (окончание)	
4	Схема организации участка М 1:300	
5	План 1 этажа с расстановкой мебели М 1:100	
6	План 2 этажа с расстановкой мебели М 1:100	
7	Фасады М 1:100	
8	Фасады М 1:100	
9	Разрез 1-1 М 1:75	
10	Разрез 2-2 М 1:75	
11	План ЖБ плиты М 1:100	
12	План ЖБ плиты с закладными М 1:100	
13	Межэтажная ЖБ плита М 1:100	
14	Подкладочный ряд 2 этажа М 1:100	
15	План 1 этажа с размерами М 1:100	
16	План 2 этажа с размерами М 1:100	
17	Маркировочный план 1 этажа М 1:100	
18	Маркировочный план 2 этажа М 1:100	
19	План кровли М 1:100	
20	Фрагменты разрезов М 1:100	
21	Схема устройства ЖБ лестницы М 1:100	
22	Спецификация заполнения оконных проёмов	
23	Спецификация заполнения дверных проёмов	
24	Общий вид крыши	
26	Общие виды (поэтажные)	

Пояснительная записка /начало/

Проект разработан на основании техзадания, предоставленного заказчиком, соответствует установленным общегосударственным нормам и требованиям малоэтажному строительству в соответствии со СП 55.13330.2011 "Дома жилые одноквартирные". Актуализированная редакция СНиП 31-02-2001; СП 131.13330.2018 "Строительная климатология", ГОСТ 21.501-2011 "Система проектной документации для строительства. Правила выполнения рабочей документации архитектурных и конструктивных решений". СП 63.13330.2012 «Бетонные и железобетонные конструкции», СП 64.13330.2017 "Деревянные конструкции", ГОСТ 8486-86 "Пиломатериалы хвойных пород", СП 15.13330.2012 "Каменные и армокаменные конструкции".

Нормативное значение равномено-распределенной временной нагрузки на перекрытие согласно СП 20.13330.2016 «Нагрузки и воздействия» равно 150,0кг/м2.

Производство работ должно выполняться в строгом соответствии с тербованиями Подрядчика.
Обязательно выполнение работ по водоотведению - дренажных работ с монтажом смотровых колодцев, отмостки и других работ, направленных на отведение воды от пятна застройки. Выполняется в объеме, определенном сметой.

Гарантия на фундаментные работы осуществляется только при условии надлежащей системы водоотведения и ее эксплуатации.

Данные о фактических размерах участка, габаритов его границ, наличие заборов, крупных растений, близость соседских построек, различных ограничений, схемы с точной привязкой их расположения на территории участка предоставляет заказчик. Точность вышеописанных сведений лежит на Заказчике. Подрядчиком не проводятся работы по межеванию и он основывается на данных, предоставленных Заказчиком.

Характеристика проектируемого объекта:

- этажность - 2 этажа
- класс функциональной пожарной опасности здания - Ф 1,4 (по СП 112.13330.2011)

Строительно-климатический район IIВ в соответствии с СП 131.13330.2018 со следующими характеристиками условий:
- температура наружного воздуха наиболее холодных суток - -32оС
- температура наружного воздуха наиболее холодной пятидневки - -28оС
- рассчетная снеговая нагрузка по району - 180кг/м2
- нормативное давление ветра - 23кгс/м2

					2021	#ID Проекта
						Адрес: #Полный Адрес Участка
Изм.	Кол.уч	Лист	№док.	Подпись	Дата	
						Индивидуальный жилой дом
Архитектор		Салыкова В.Г.				
Заказчик		#Обращение к Заказчику				Общие данные (начало)

стадия	лист	листов
РП	2	

Пояснительная записка /окончание/

Архитектурно-планировочные решения:

Проектируемый коттедж одноквартирный, двухэтажный . Размеры в осях 13,9х20,3 м.

На первом этаже дома размещаются помещения: Тамбур, 2 Холла, Котельная, Санузел, Гардероб, Тренажерный зал, Кухня, Столовая, Гостиная, Гостевая комната, Крыльцо, Терраса.

На втором этаже размещаются: 4 спальных комнаты, Гардеобная, 2 с/у, Холл, 2 балкона.

Дом без чердака. За отм. 0,000 принят уровень чистого пола первого этажа дома. За отм. 3,350 принят уровень чистого пола второго этажа дома. Покрытие кровли – согласно смете. Водосточная система – водосточные трубы и желоба , цвет индивидуальный. Окна – ПВХ или деревянные, 2– камерные стеклопакеты, индивидуального изготовления. Двери наружные – металлические, сендвич, внутренняя сторона МДФ или индивидуального изготовления. Двери внутренние – деревянные по индивидуальному проекту. Отмостка –утепленная, бетонная толщ.100мм из бетона Кл.В7.5 по гравийно-песчаному основанию шириной 1000мм.

Конструктивные решения:

Фундамент представляет собой монолитную железобетонную плиту 300мм.
Полы первого этажа, (крыльца и террасы) выполнены по монолитной ЖБ плите.
Межэтажное перекрытие: по монолитной ж/б плите толщиной 200мм.
Наружние несущие стены 1-го этажа выполнены из газобетонных блоков
-Ytong 1/625x375x250/D400/B2,5/F100 ГОСТ 31360-2007.
Внутренние несущие стены 1-го этажа выполнены из газобетонных блоков
-Ytong 1/625x250x250/D500/B3,5/F100 ГОСТ 31360-2007 .
Перегородки 1-го этажа выполнены из газобетонных блоков
- Ytong 1/625x150x250
Кладка из газобетонных блоков может эксплуатироваться без отделки. Обязательной является только защита от намокания мест потенциального переувлажнения: подоконных зон, примыкания к отмостке, козырькам – мест, где возможно образование снеговых карманов, потоков и пр. Для наружной отделки, наносимой непосредственно на поверхность кладки (штукатурка, окраска, наклейка плитки или каменных плит), существуют дополнительные ограничения. Слой такой отделки должен обладать достаточной паропроницаемостью, т.е.обеспечивать удаление из кладки начальной технологической влаги и не вызывать значительного увлажнения кладки за отделкой в отопительный сезон.

Несущие стены 2-го этажа. выполнены из клееного профилированного бруса 200х260(255)(h)мм. Материал строительства – клееный брус соответствует техническим условиям, опряделяемыми строительной компанией подрядчиком. Перегородки 2-го этажа- деревянный каркас – стойки с шагом 600 мм, между ними расположен утеплитель. Внешняя и внутренняя обшивка имитацией бруса, во влажных помещениях отделка влагостойким ГВЛ, либо иными материалами по согласованию сторон.

Номинальные, проектные линейные и высотные размеры отдельных применяемых материалов строения могут отличаться от фактических в силу технических и технологических особенностей, выполняемых работ и применяемых материалов, технологической усадки стенового комплекта, нормативных допусков и отклонений от предельных размеров строения и материалов в частности, сезонности и влажности, погодных явлений и других обстоятельств.

Крыша – двускатная из деревянных наслонных стропил с обрешеткой, покрытие согласно смете. Между стропилами укладывается утеплитель толщ.200мм.

Стропила- сухая строганая доска сухая строганная 100х200мм.

Материалы, технология работ и способы исполнения, гарантийные обязательства, способы эксплуатации и другое, связанное с использованием строения, а также его монтажом регулируется ТУ 16.23.19-001-17010764-2018

ТЕХНИКО-ЭКОНОМИЧЕСКИЕ ПОКАЗАТЕЛИ:	
Наименование	Площадь, м2
Площадь застройки	229,59
Жилая площадь	220,62
	Объем, м3
Строительный объем	1355,18

*Площадь помещений указана без учета отделочных материалов и понижающего коэффициента

Проект строительства жилого дома разработан в соответствии с действующими строительными, технологическими и санитарными нормами и правилами, предусматривает мероприятия, обеспечивающие конструктивную надежность, врзрывопожарную и пожарную безопасность объекта, защиту окружающей природной среды при его эксплуатации и отвечает требованиям законодательства Российской Федерации в области капитального строительства.

Архитектор проекта _____ Салыкова В.Г.


					2021	#ID Проекта		
						Адрес: #Полный Адрес Участка		
Изм.	Кол.уч	Лист	№док.	Подпись	Дата			
						Индивидуальный жилой дом	стадия	лист	листов
							РП	3	
Архитектор		Салыкова В.Г.							
						Общие данные (окончание)			
Заказчик		#Обращение к Заказчику							

Согласовано

Взам. инв. №

Подпись и дата

Инв. № подл.

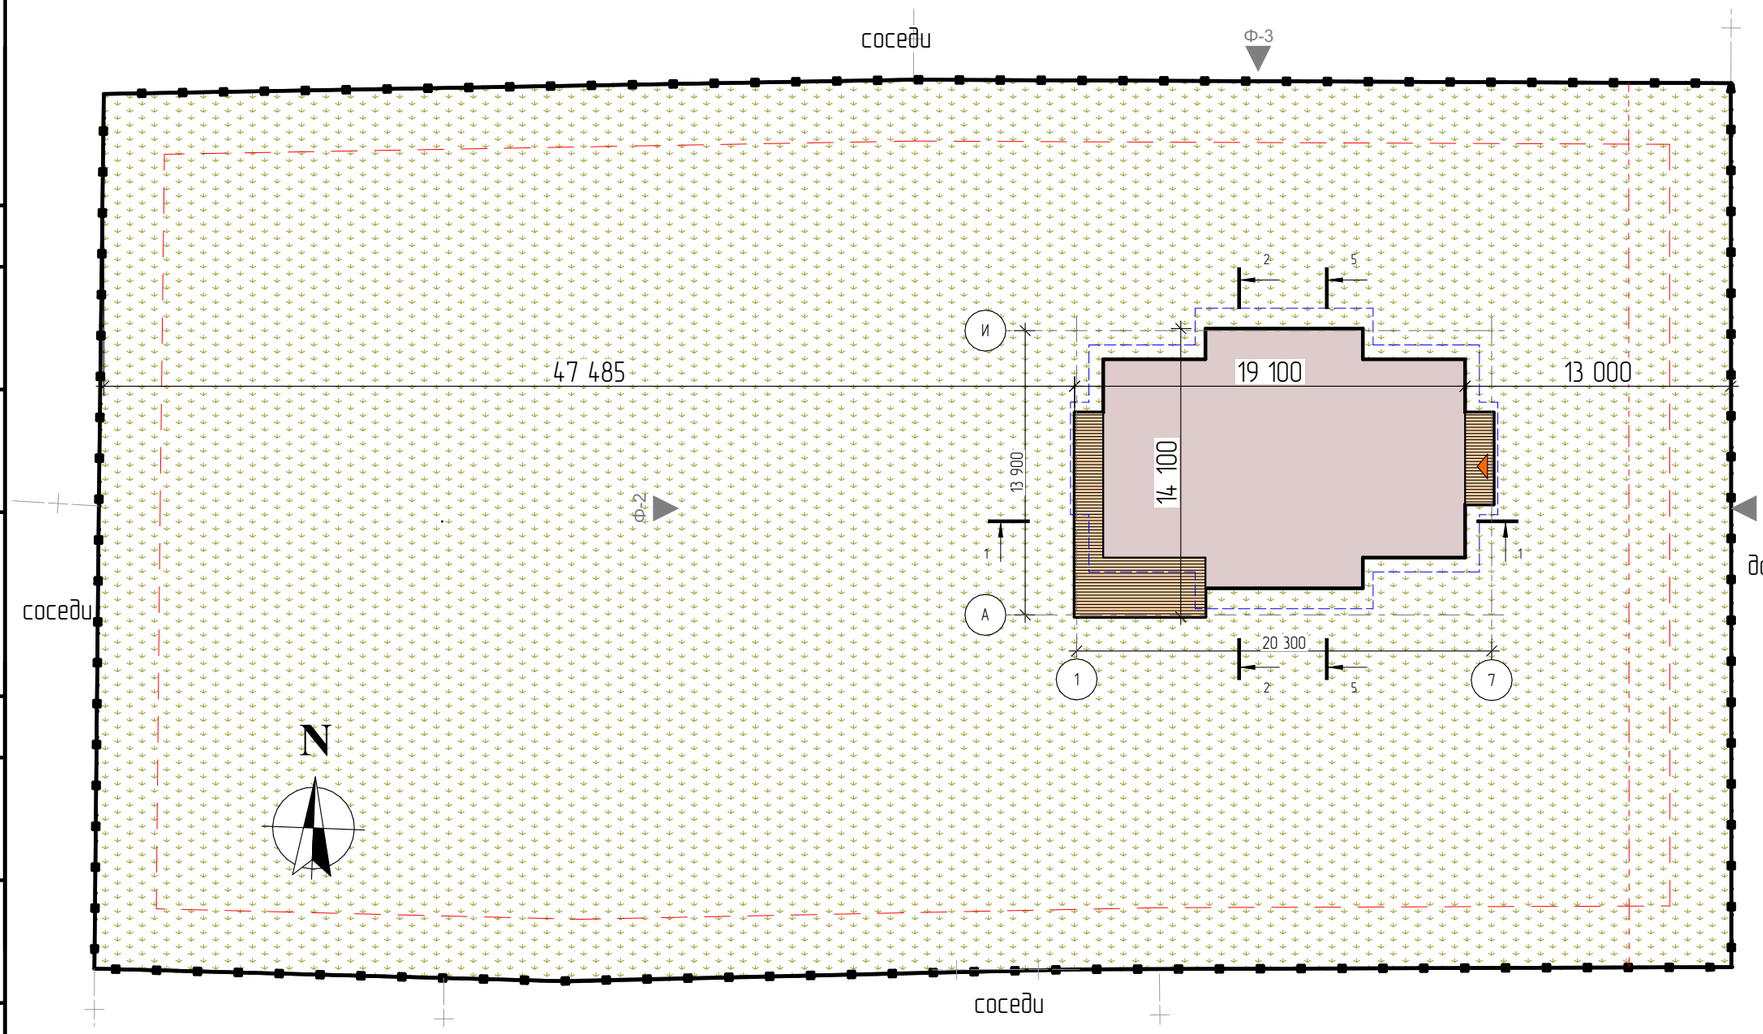


Условные обозначения:

- Проектируемое здание
- Терраса/крыльцо/веранда
- Вход
- Контур кровли
- Зона отступа от края участка (красной линии улицы) = 5,0 м
- Зона отступа от края участка = 3,0 м
- Граница участка



#ID Участка

Инсоляция по временам года

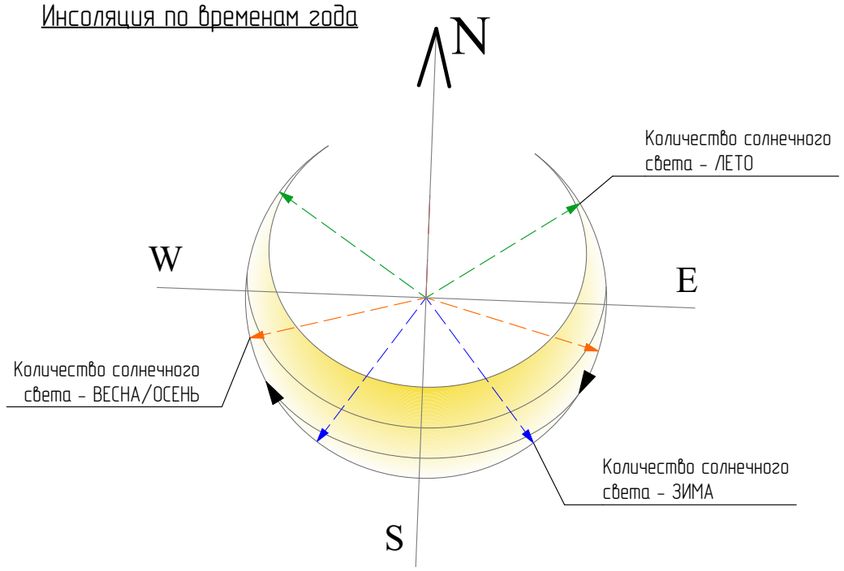

Примечание:
1) Расположение дома показано от забора до края фундамента.
2) Привязка показана условно. Скорректировать по месту.
3) При расположении дома учитывать требования по противопожарным расстояниям между строениями на соседних участках в соответствии с СП 53.13330.2011
4) Монтаж и расположение наружных сетей согласовывается с инженером по месту.

					2021	#ID Проекта		
						Адрес: #Полный Адрес Участка		
Изм.	Кол.уч	Лист	№док.	Подпись	Дата			
						Индивидуальный жилой дом	стадия	лист	листов
							РП	4	
Архитектор		Салыкова В.Г.							
Заказчик		#Обращение к Заказчику				Схема организации участка М 1:300			

Согласовано:


Взам. инв. №

Подпись и дата

Инв. № подл.

М 1:100

План 1 этажа с расстановкой мебели

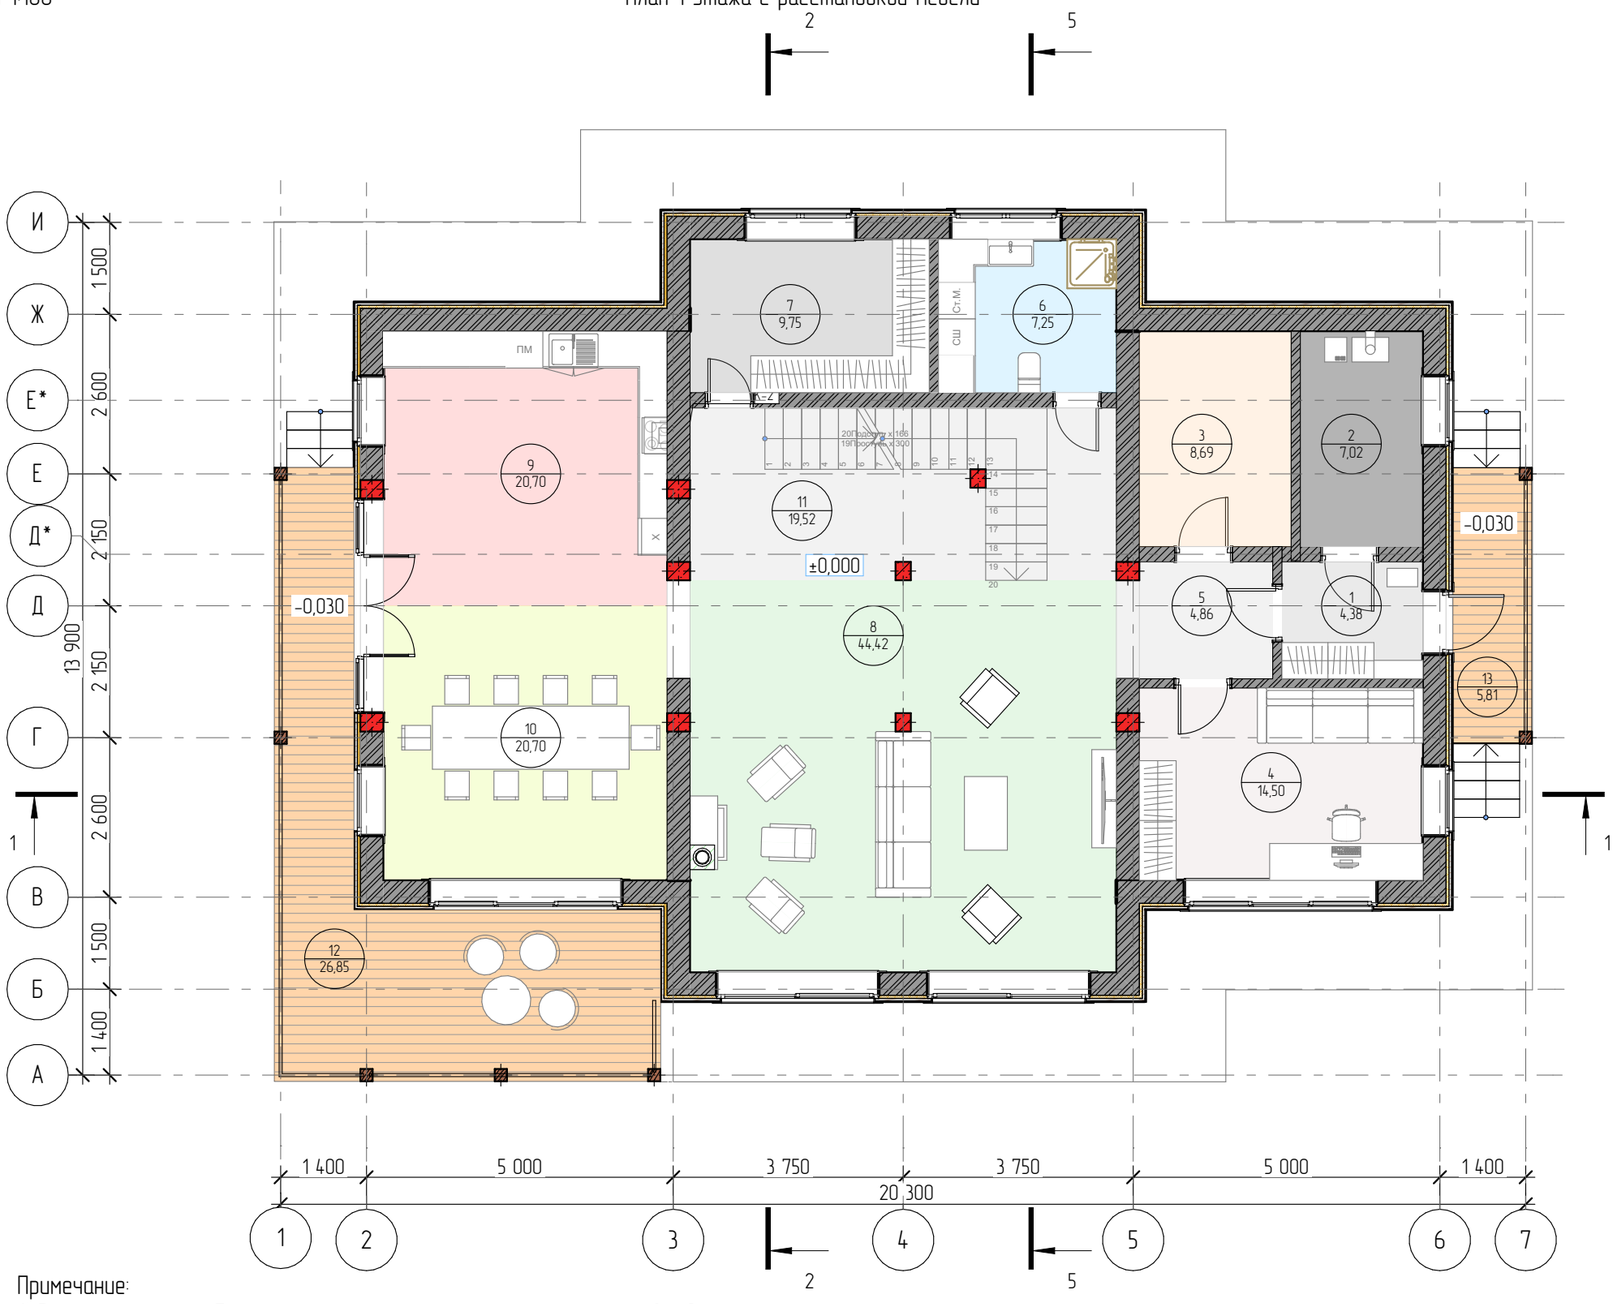

Экспликация 1 этажа

Расположение поещений	№ п/п	Наименование	Площадь, м2
Внутр. пом.			
	1	Тамбур	4,38
	2	Котельная	7,02
	3	Тренажерный зал	8,69
	4	Гостевая Комната	14,50
	5	Холл 1	4,86
	6	Санузел	7,25
	7	Гардероб	9,75
	8	Гостиная	44,42
	9	Кухня	20,70
	10	Столовая	20,70
	11	Холл 2	19,52
			161,79 м²
Наружн. пом.			
	12	Терраса	26,85
	13	Крыльцо	5,81
			32,66 м²
			194,45 м²

Примечание:

1) Вся показанная мебель, а также назначение комнат носят условный характер
2) Расположение сан.технических приборов не подлежит перемещению.
3) Площадь помещений показана без учета отделочных материалов и понижающего коэффициента по периметру пола.
4) Все декоративные элементы подлежат дополнительному сметному согласованию.
5) За отметку 0,000 принята отметка чистового пола второго этажа
6) Габаритные размеры и расположение печи/камина могут измениться в процессе строительства
7) Расположение вентиляционных коммуникаций и прочих инженерных систем показано условно. Проект инженерных коммуникаций будет разрабатываться при заключении договора на инженерные работы. Количество и наличие вентиляционных, фановых и дымовых труб определяется дополнительным согласованием в сметном расчёте на этапе отделочных работ.
8) Ответственность за конструктивное решение и расположение печи/камина относительно несущих деревянных конструкций, фундамента, а также соблюдение мер пожарной безопасности при сооружении и эксплуатации печи/камина, полностью лежат на Заказчике

Изм.	Кол.уч	Лист	№док.	Подпись	Дата
					2021
Архитектор		Салыкова В.Г.			
Заказчик		#Обращение к Заказчику			

#ID Проекта

Адрес: #Полный Адрес Участка

Индивидуальный жилой дом

стадия	лист	листов
РП	5	

План 1 этажа с расстановкой мебели
М 1:100

Согласовано:


Взам. инв. №

Подпись и дата

Инв. № подл.

М 1:100

План 2 этажа с расстановкой мебели

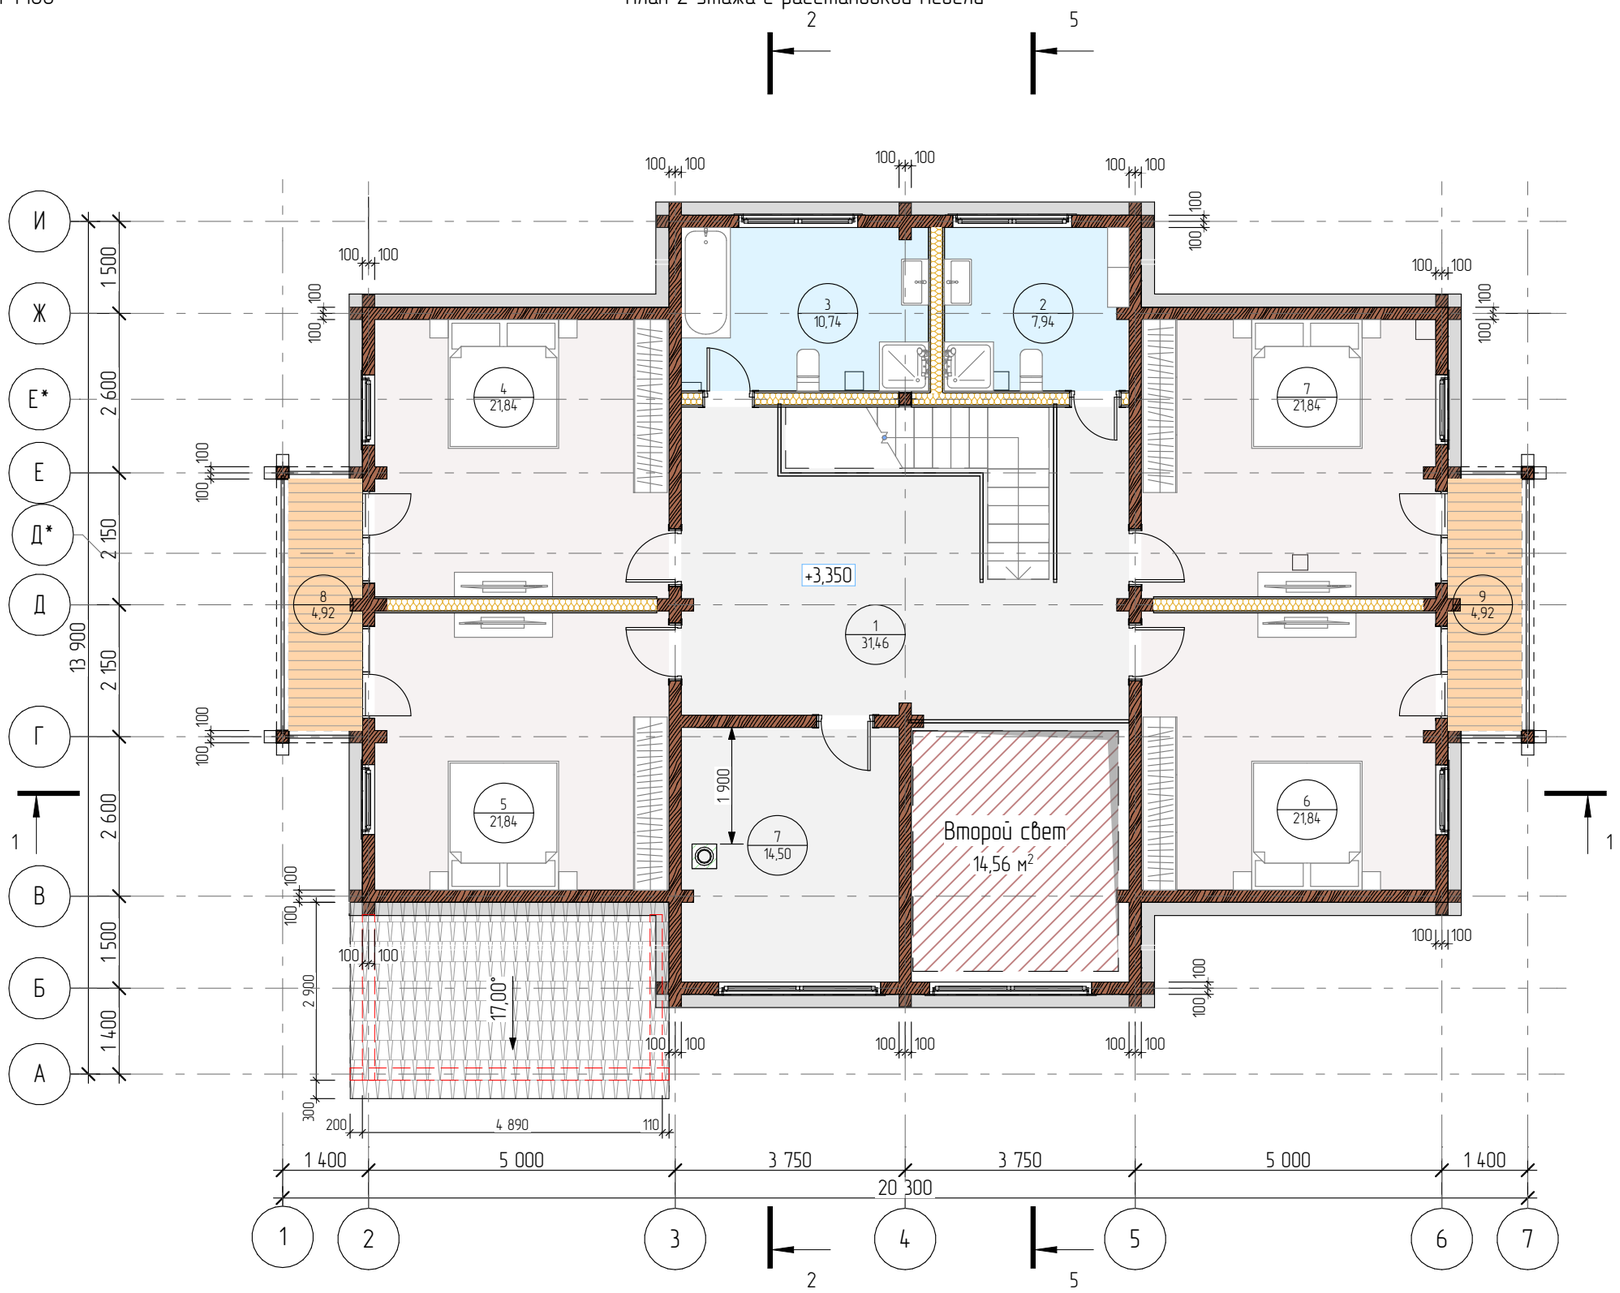

Примечание:

1) Вся показанная мебель, а также назначение комнат носят условный характер
2) Расположение сан.технических приборов не подлежит перемещению.
3) Площадь помещений показана без учета отделочных материалов и понижающего коэффициента по периметру пола.
4) Все декоративные элементы подлежат дополнительному сметному согласованию.
5) За отметку +3,350 принята отметка чистового пола второго этажа
6) Габаритные размеры и расположение печи/камина могут измениться в процессе строительства
7) Расположение вентиляционных коммуникаций и прочих инженерных систем показано условно. Проект инженерных коммуникаций будет разрабатываться при заключении договора на инженерные работы. Количество и наличие вентиляционных, фановых и дымовых труб определяется дополнительным согласованием в сметном расчёте на этапе отделочных работ.
8) Ответственность за конструктивное решение и расположение печи/камина относительно несущих деревянных конструкций, фундамента, а также соблюдение мер пожарной безопасности при сооружении и эксплуатации печи/камина, полностью лежат на Заказчике

Экспликация 2 этажа

Расположение поещений	№ п/п	Наименование	Площадь, м2
Внутр. пом.			
	1	Холл	31,46
	2	Санузел 1	7,94
	3	Санузел 2	10,74
	4	Спальня 1	21,84
	5	Спальня 2	21,84
	6	Спальня 3	21,84
	7	Спальня 4	21,84
	7	Гардероб	14,50
			152,00 м²
Наружн. пом.			
	8	Балкон 1	4,92
	9	Балкон 2	4,92
			9,84 м²
			161,84 м²

Изм.	Кол.уч	Лист	№док.	Подпись	Дата
					2021
Архитектор		Салыкова В.Г.			
Заказчик		#Обращение к Заказчику			

#ID Проекта

Адрес: #Полный Адрес Участка

Индивидуальный жилой дом

стадия	лист	листов
РП	6	

План 2 этажа с расстановкой мебели
М 1:100

Согласовано:

Взам. инв. №

Подпись и дата

Инв. № подл.

Фасад 1-5



Фасад Д-А



Примечание:
1) За отметку +0,000 принята отметка чистового пола первого этажа
2) За отметку +3,350 принята отметка чистового пола второго этажа
3) Номинальные высотные размеры могут отличаться от фактических в силу технологической усадки стенового комплекта и принимаемых отделочных материалов.
4) Несущие перевязки из бревен могут быть ниже основного уровня потолка
5) Все декоративные элементы показаны условно.

					2021	#ID Проекта
						Адрес: #Полный Адрес Участка; к/н: #ID Участка
Изм.	Кол.уч	Лист	№док.	Подпись	Дата	
						Индивидуальный жилой дом
Архитектор		Салыкова В.Г.				
Заказчик		#Обращение к Заказчику				Фасады М 1:100

стадия	лист	листов
ЭП	7	


Согласовано:

Взам. инв. №


Подпись и дата

Инв. № подл.

Фасад 5-1

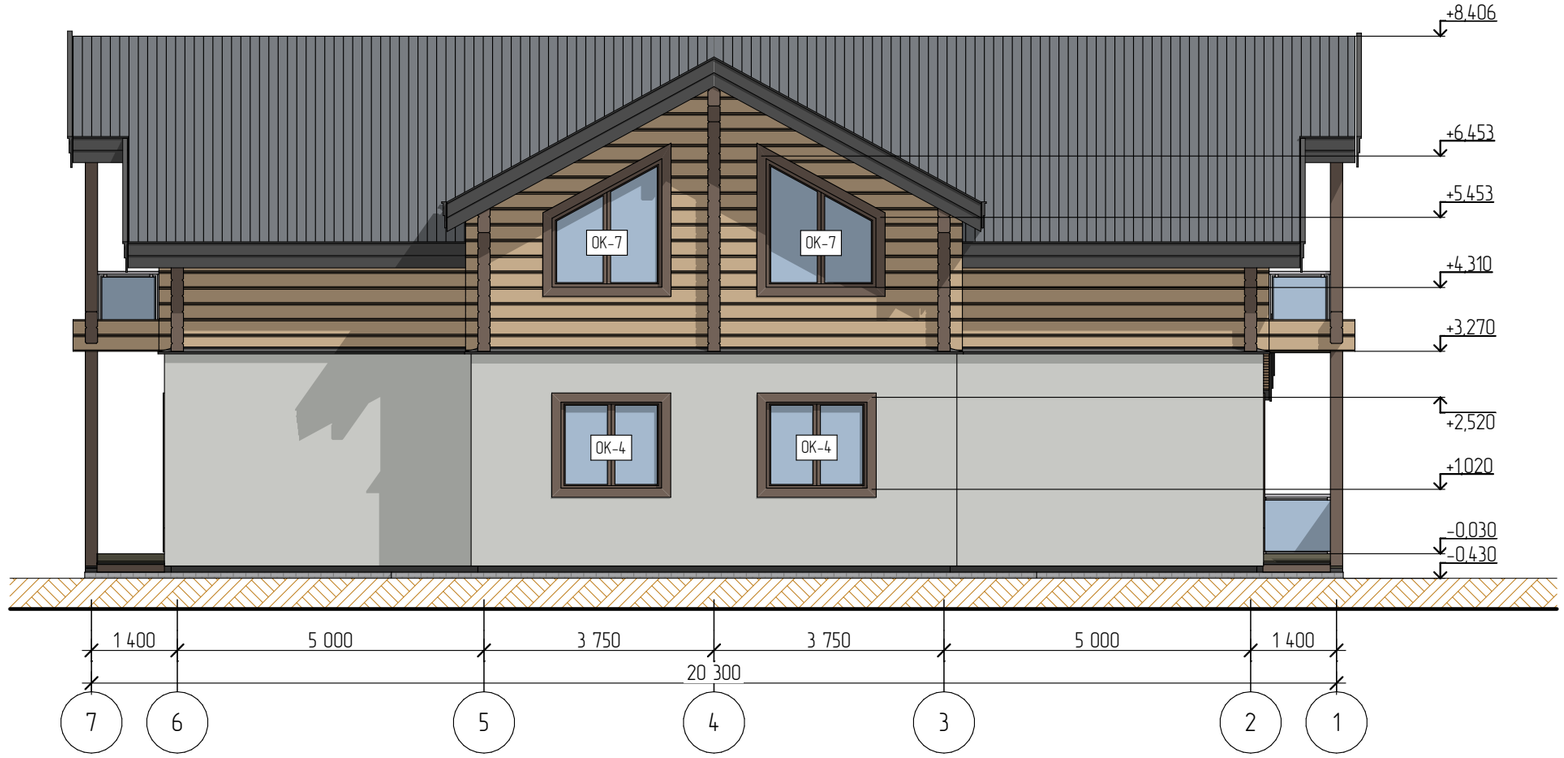

Фасад А-Д

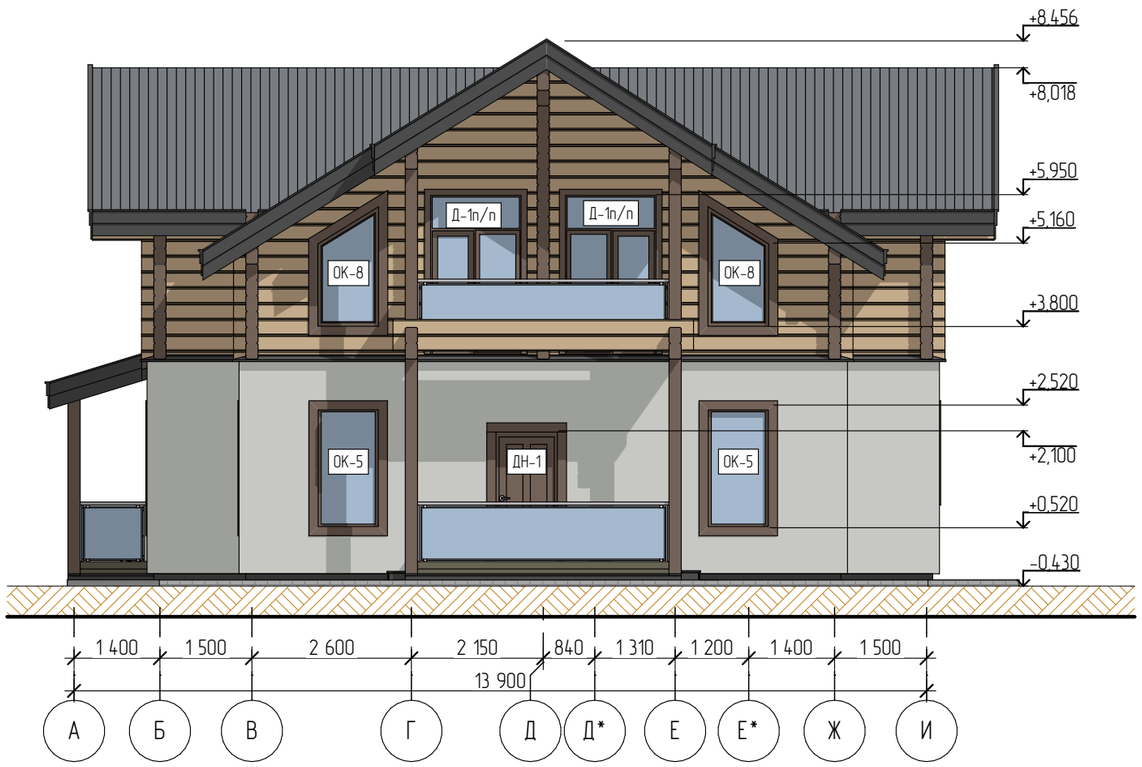

Примечание:
1) За отметку +0,000 принята отметка чистового пола первого этажа
2) За отметку +3,350 принята отметка чистового пола второго этажа
3) Номинальные высотные размеры могут отличаться от фактических в силу технологической усадки стенового комплекта и принимаемых отделочных материалов.
4) Несущие перевязки из бруса могут быть ниже основного уровня потолка
5) Все декоративные элементы показаны условно.

					2021	#ID Проекта		
						Адрес: #Полный Адрес Участка; к/н: #ID Участка		
Изм.	Кол.уч	Лист	№док.	Подпись	Дата			
						Индивидуальный жилой дом	стадия	лист	листов
							ЭП	8	
Архитектор		Салыкова В.Г.							
Заказчик		#Обращение к Заказчику				Фасады М 1:100			

Согласовано:


Взам. инв. №

Подпись и дата

Инв. № подл.

1:75

Разрез 1-1

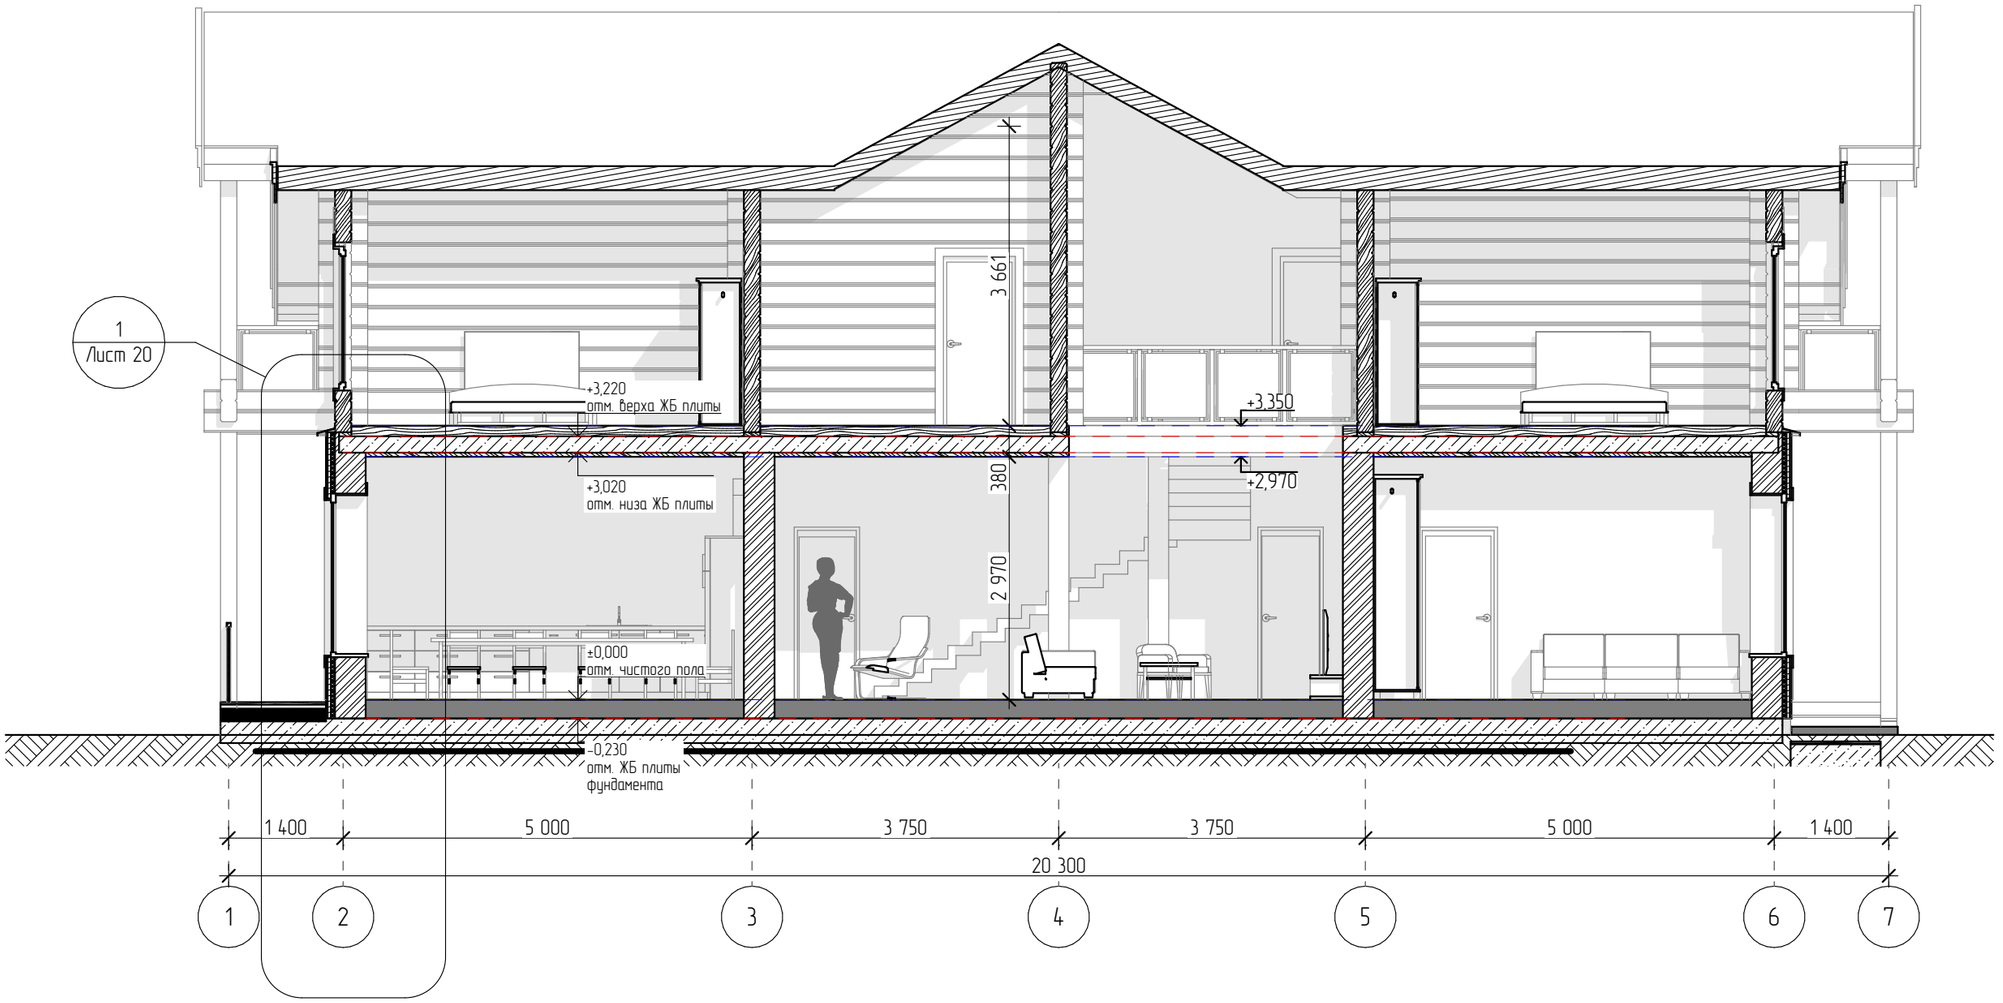

Примечание:

1) За отметку +0,000 принята отметка чистового пола первого этажа
2) За отметку +3,350 принята отметка чистового пола второго этажа
3) Номинальные высотные размеры могут отличаться от фактических в силу технологической усадки стенового комплекта и принимаемых отделочных материалов.
4) Несущие перевязки из бруса могут быть ниже основного уровня потолка
5) Высота фундамента дана без учета перепада. Замер перепада производится на участке при выезде инженера. Изменение габаритов и типа фундаментов согласовывается дополнительным согласованием по смете.
6) Все декоративные элементы показаны условно.

					2021	#ID Проекта			
						Адрес: #Полный Адрес Участка			
Изм.	Кол.уч	Лист	№док.	Подпись	Дата				
						Индивидуальный жилой дом	стадия	лист	листов
							РП	9	
Архитектор		Салыкова В.Г.							
Заказчик		#Обращение к Заказчику				Разрез 1-1 М 1:75			

Согласовано


Взам. инв. №

Подпись и дата

Инв. № подл.

1:75

Разрез 2-2

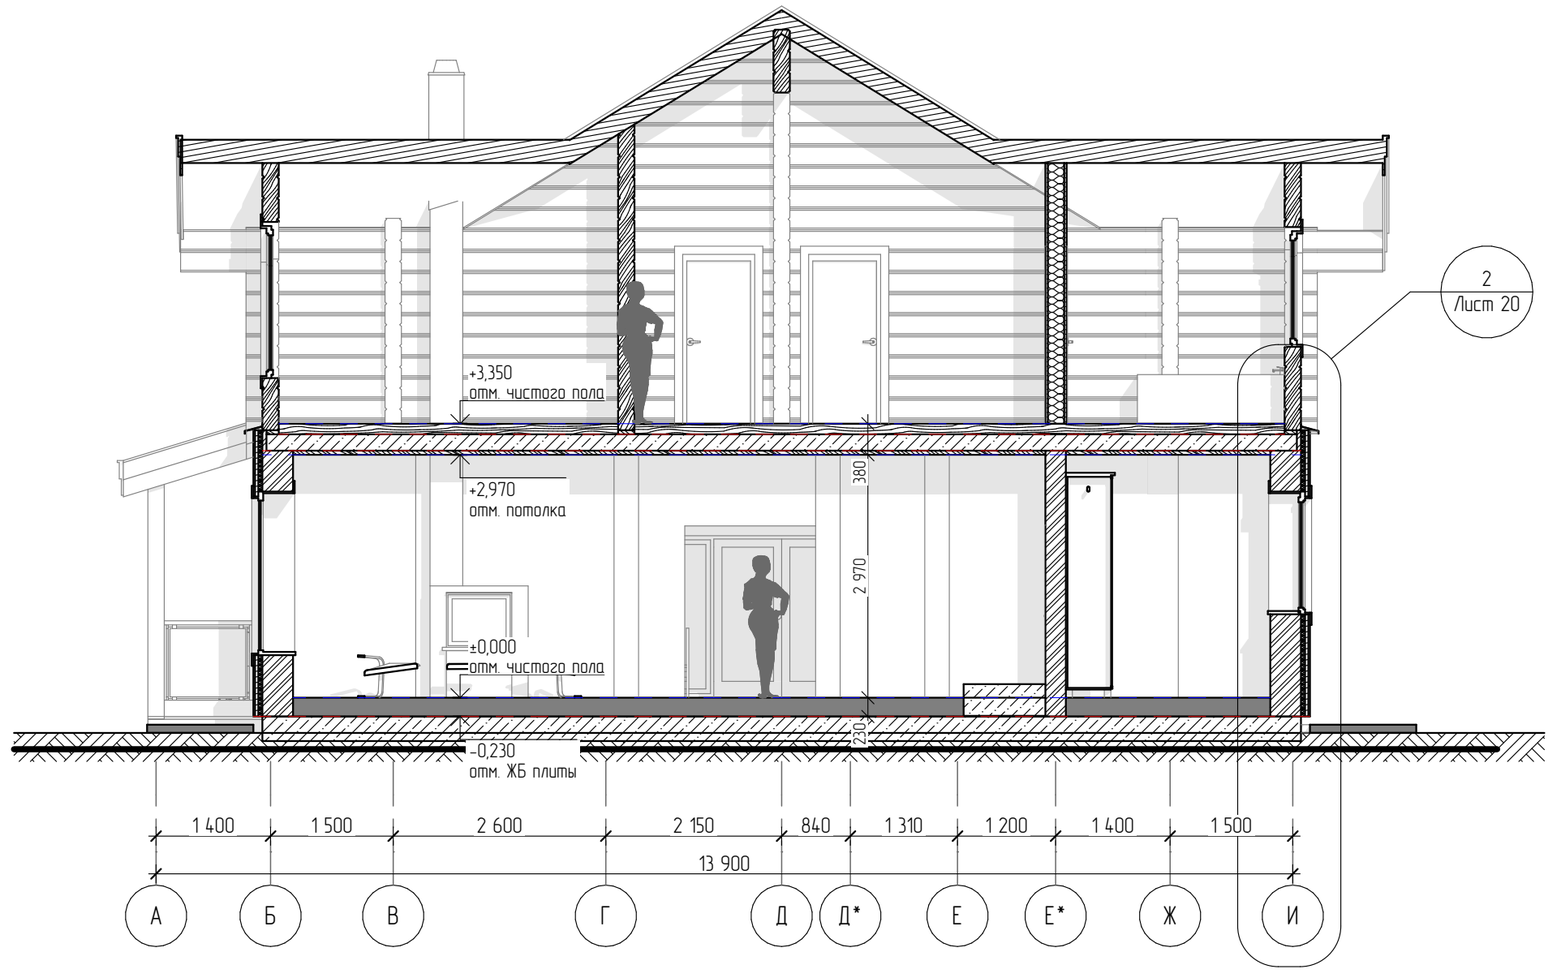

Примечание:

1) За отметку +0,000 принята отметка чистового пола первого этажа
2) За отметку +3,350 принята отметка чистового пола второго этажа
3) Номинальные высотные размеры могут отличаться от фактических в силу технологической усадки стенового комплекта и принимаемых отделочных материалов.
4) Несущие перевязки из бруса могут быть ниже основного уровня потолка
5) Высота фундамента дана без учета перепада. Замер перепада производится на участке при выезде инженера. Изменение габаритов и типа фундаментов согласовывается дополнительным согласованием по смете.
6) Все декоративные элементы показаны условно.

					2021	#ID Проекта			
						Адрес: #Полный Адрес Участка			
Изм.	Кол.уч	Лист	№док.	Подпись	Дата	Индивидуальный жилой дом	стадия	лист	листов
							РП	10	
Архитектор		Салыкова В.Г.				Разрез 2-2 М 1:75			
Заказчик		#Обращение к Заказчику							

Согласовано:


Взам. инв. №

Подпись и дата

Инв. № подл.

М 1:100

План ЖБ плиты

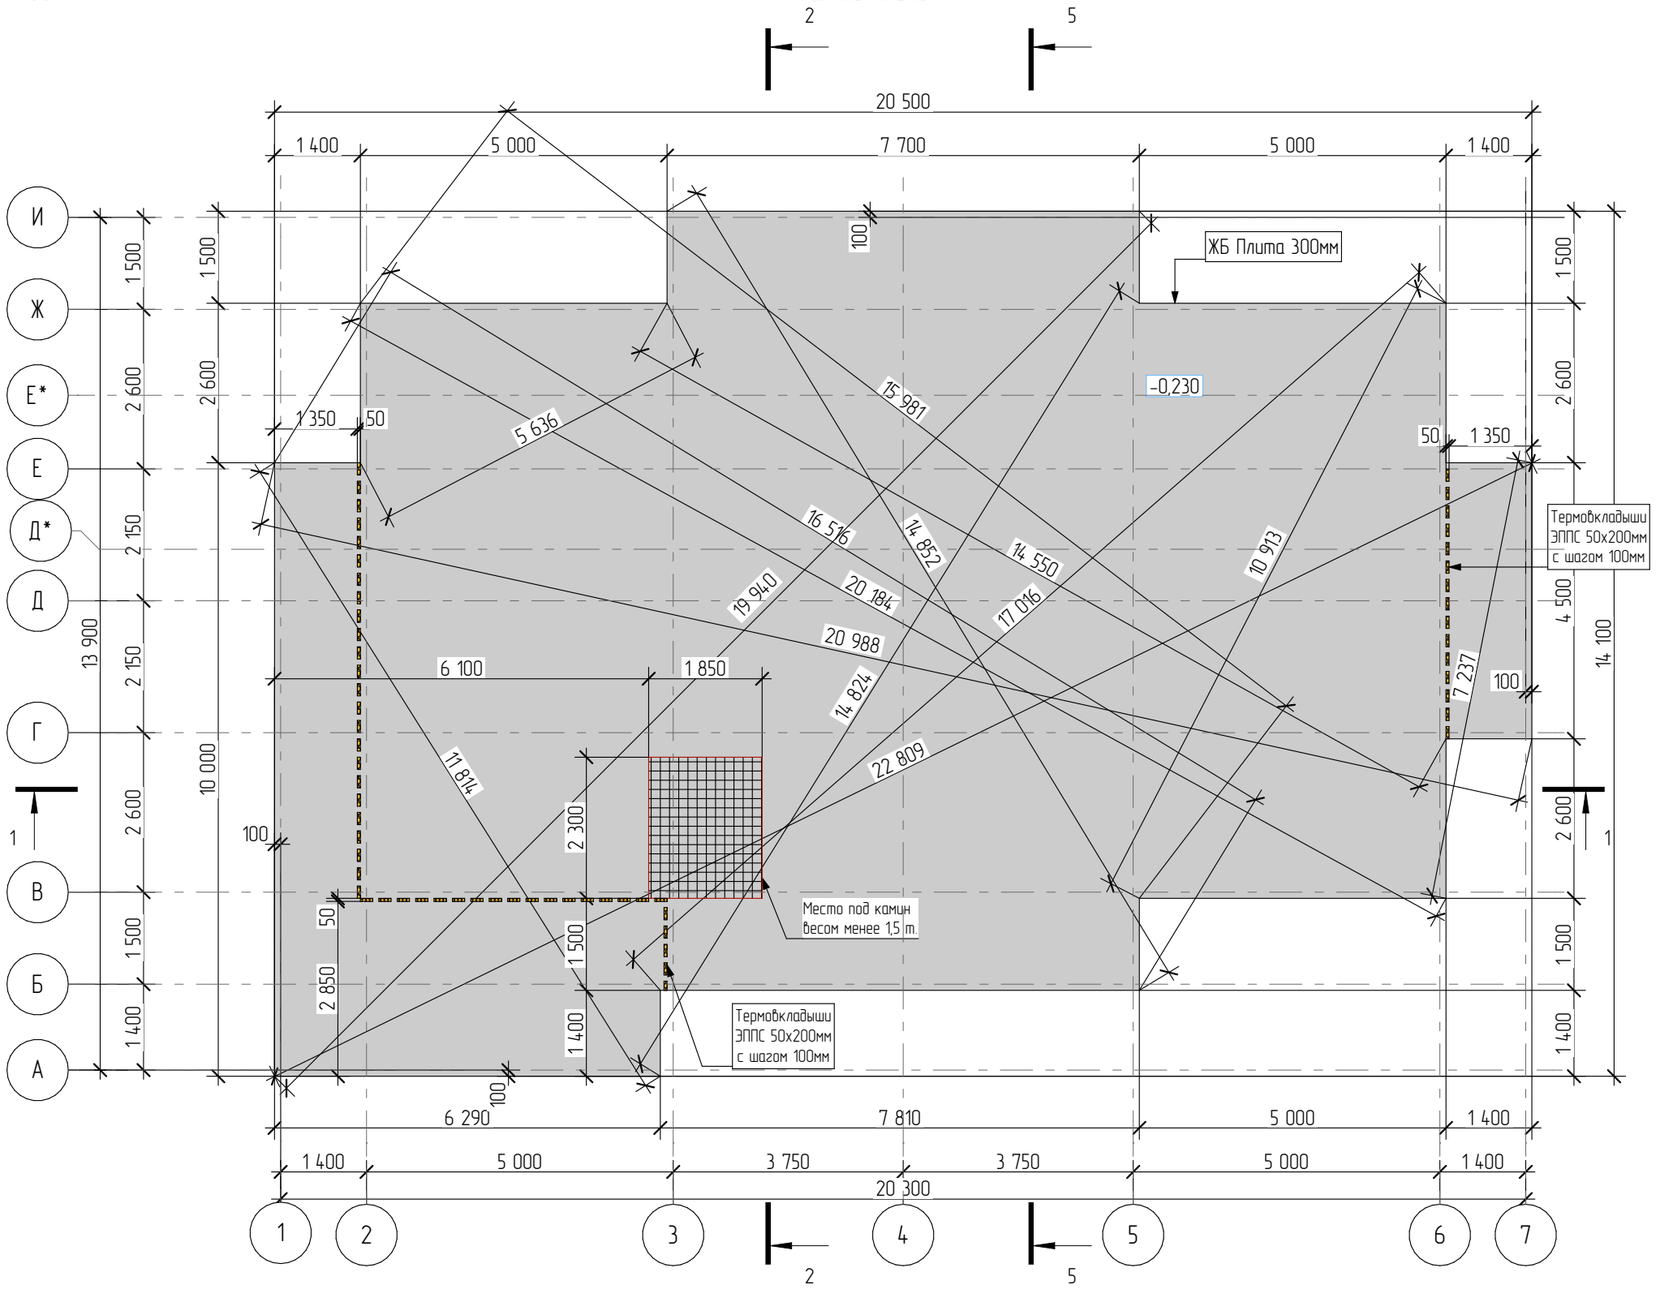

Примечание:

1) Отметка 0,000 задана по верху чистого пола первого этажа
2) Диагональная привязка фундамента осуществляется по наружной грани фундамента

					2021	#ID Проекта			
						Адрес: #Полный Адрес Участка			
Изм.	Кол.уч	Лист	№док.	Подпись	Дата				
						Индивидуальный жилой дом	стадия	лист	листов
Архитектор		Салыкова В.Г.					РП	11	
Заказчик		#Обращение к Заказчику				План ЖБ плиты М 1:100			

Согласовано:


Взам. инв. №

Подпись и дата

Инв. № подл.

М 1:100

Плита фундамента закладные

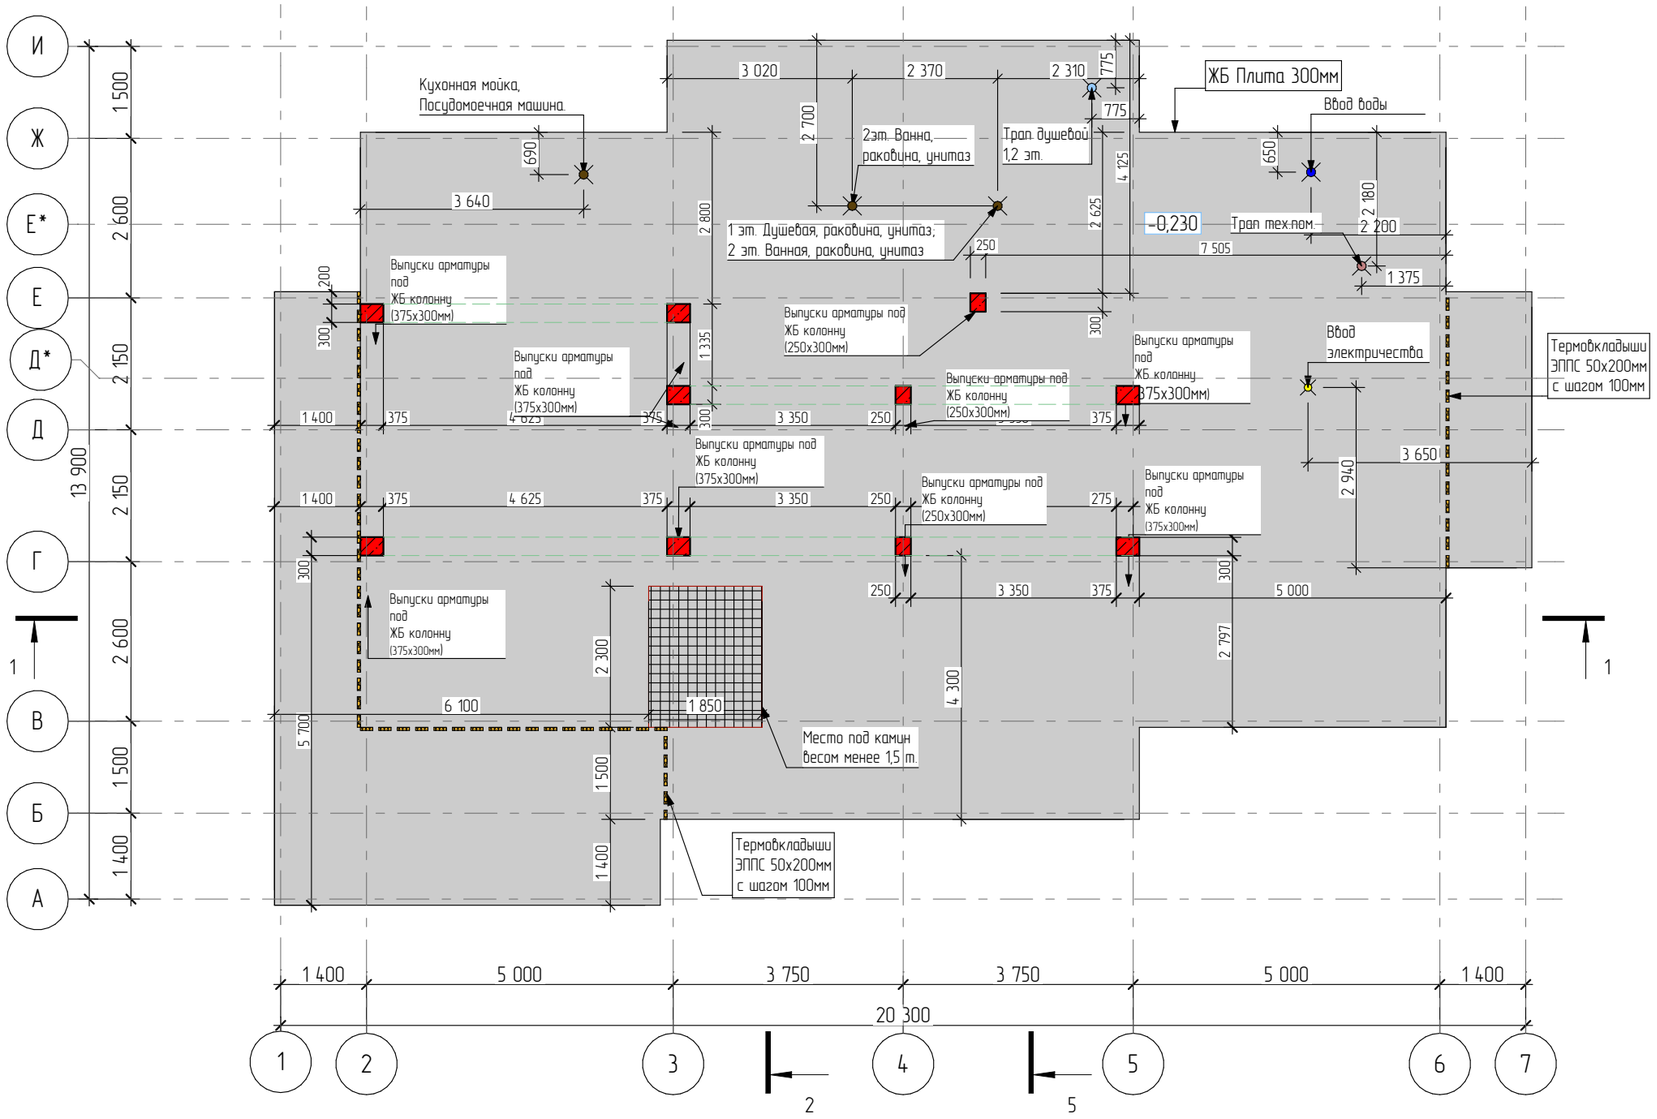

Примечание:

1) Отметка 0,000 задана по верху чистого пола первого этажа
2) Закладные в железобетонной плите перекрытия устанавливаются в соответствии с расположением сантехнических приборов во время заливки жб плиты.
3) Рекомендуется к разработке проект инженерных коммуникаций. Количество и наличие вентиляционных, фановых и дымовых труб определяется дополнительным согласованием в сметном расчёте.
4) Выпуски арматуры пож жб колонны 400-500мм.

					2021	#ID Проекта			
						Адрес: #Полный Адрес Участка			
Изм.	Кол.уч	Лист	№док.	Подпись	Дата	Индивидуальный жилой дом	стадия	лист	листов
							РП	12	
Архитектор		Салыкова В.Г.				План ЖБ плиты с закладными М 1:100			
Заказчик		#Обращение к Заказчику							

Согласовано


Взам. инв. №

Подпись и дата

Инв. № подл.

М 1:100

ЖБ плита межэтажная

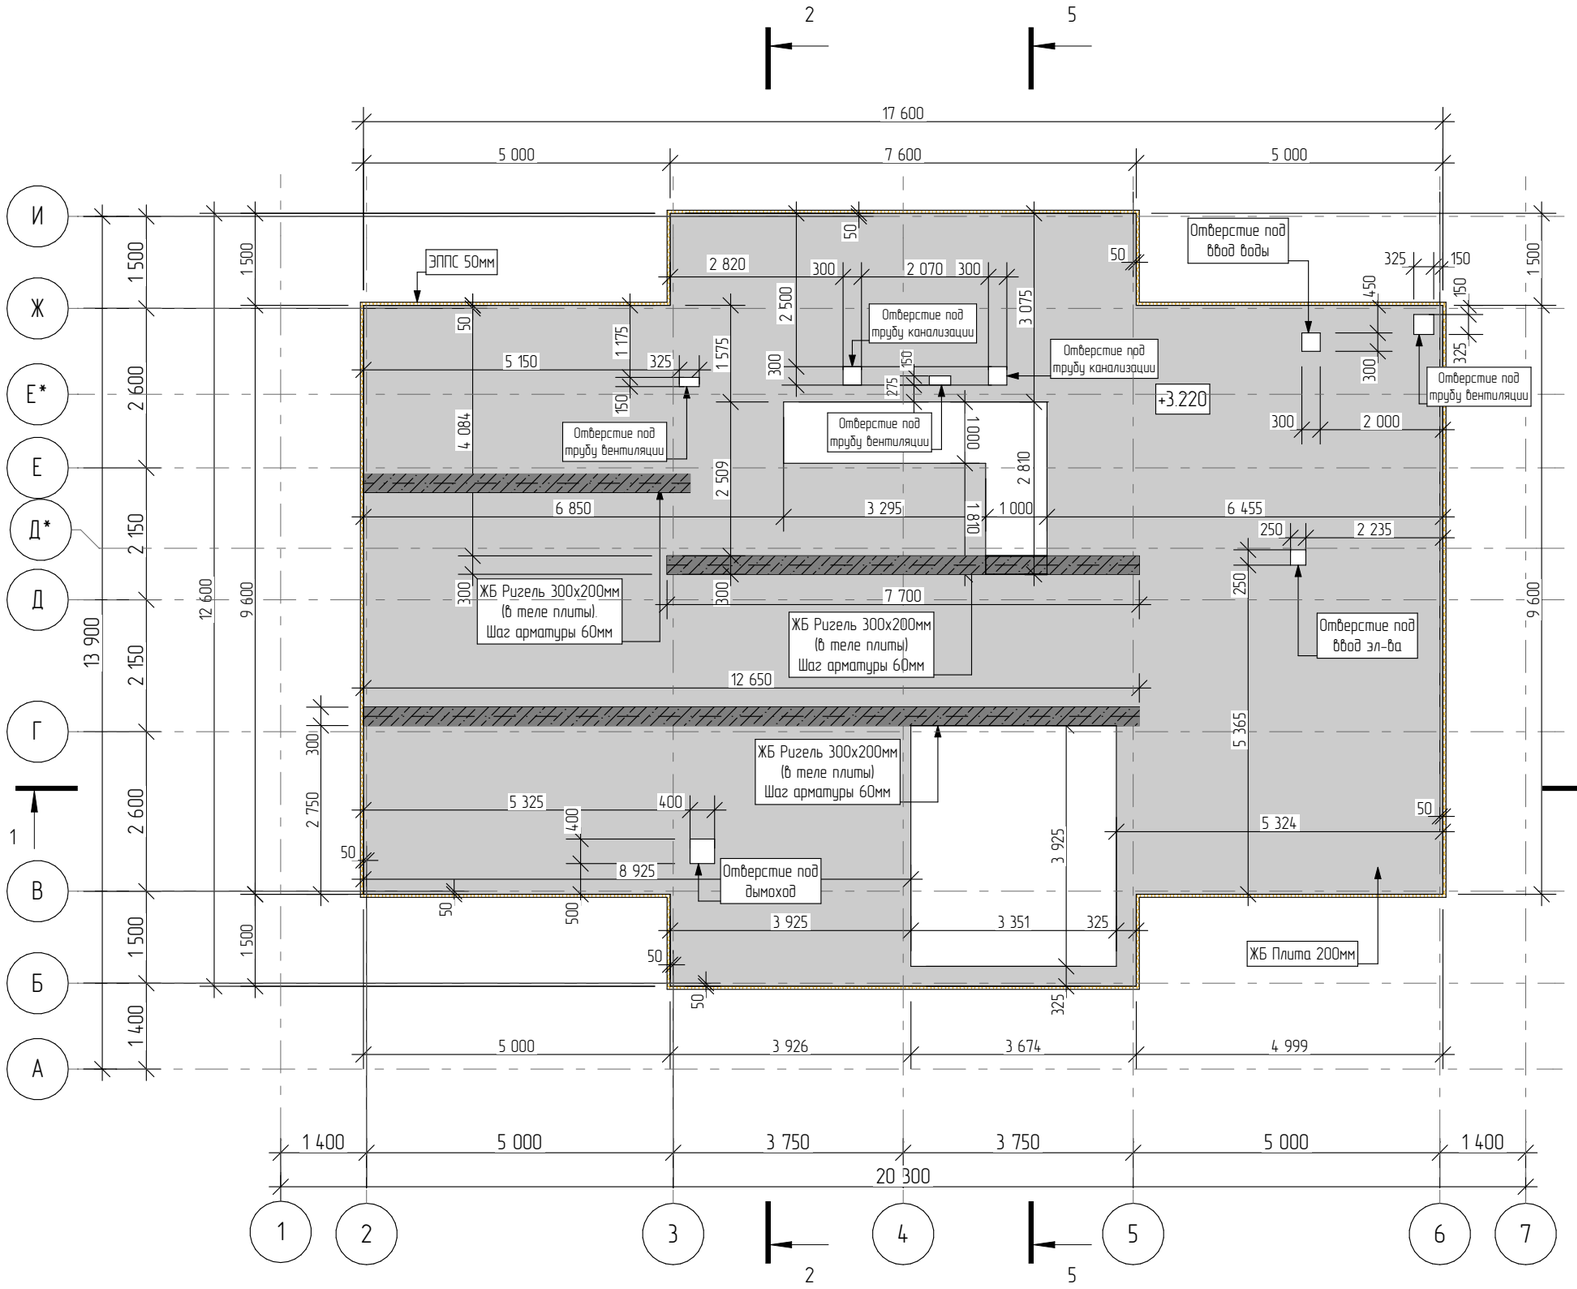

					2021	#ID Проекта
						Адрес: #Полный Адрес Участка
Изм.	Кол.уч	Лист	№док.	Подпись	Дата	
						Индивидуальный жилой дом
Архитектор		Салыкова В.Г.				Межэтажная ЖБ плита М 1:100
Заказчик		#Обращение к Заказчику				

стадия	лист	листов
РП	13	

Согласовано:


Взам. инв. №

Подпись и дата

Инв. № подл.

М 1:100

Подкладочный ряд 2 этажа

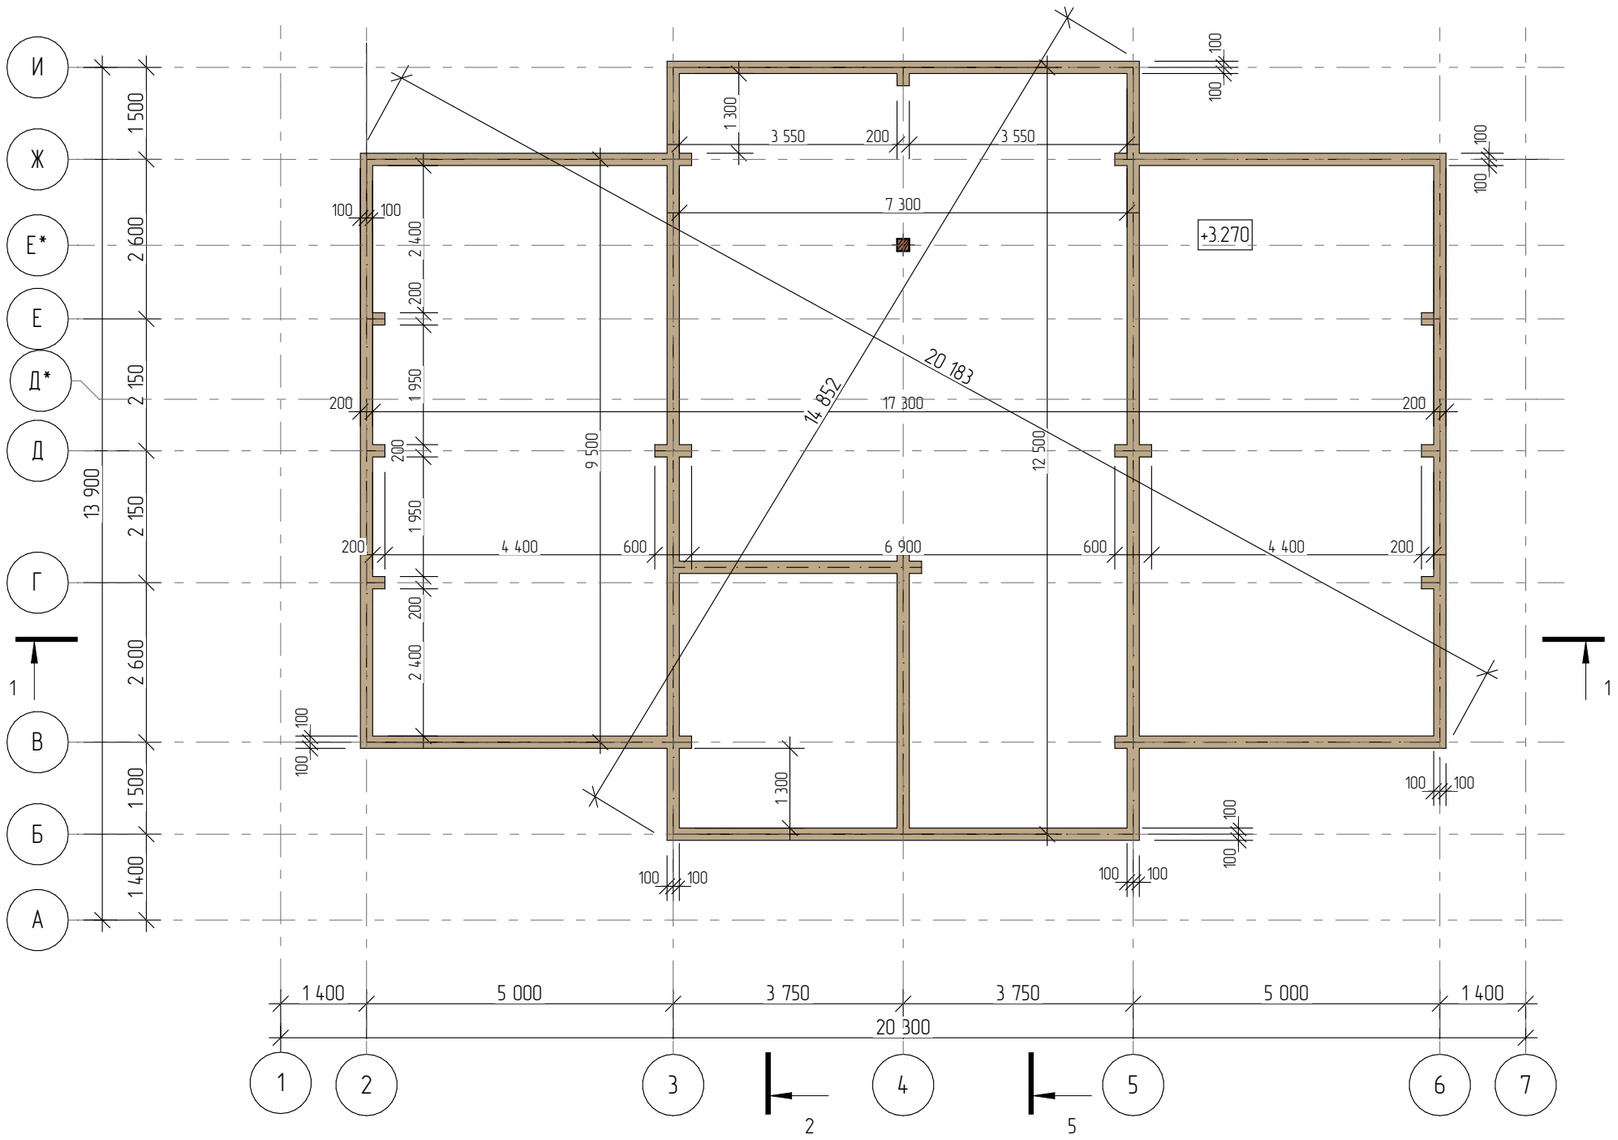

Примечание:

1) Обвязочный брус – обрезная доска 50х200(+/- 10мм), естеств. влажности, сосна или ель.
2) Сечение обвязочного ряда определяется сметным расчётом

					2021	#ID Проекта			
						Адрес: #Полный Адрес Участка			
Изм.	Кол.уч	Лист	№док.	Подпись	Дата				
						Индивидуальный жилой дом	стадия	лист	листов
Архитектор		Салыкова В.Г.					РП	14	
Заказчик		#Обращение к Заказчику				Подкладочный ряд 2 этажа М 1:100			

Согласовано:


Взам. инв. №

Подпись и дата

Инв. № подл.

М 1:100

Монтажный план 1 этажа

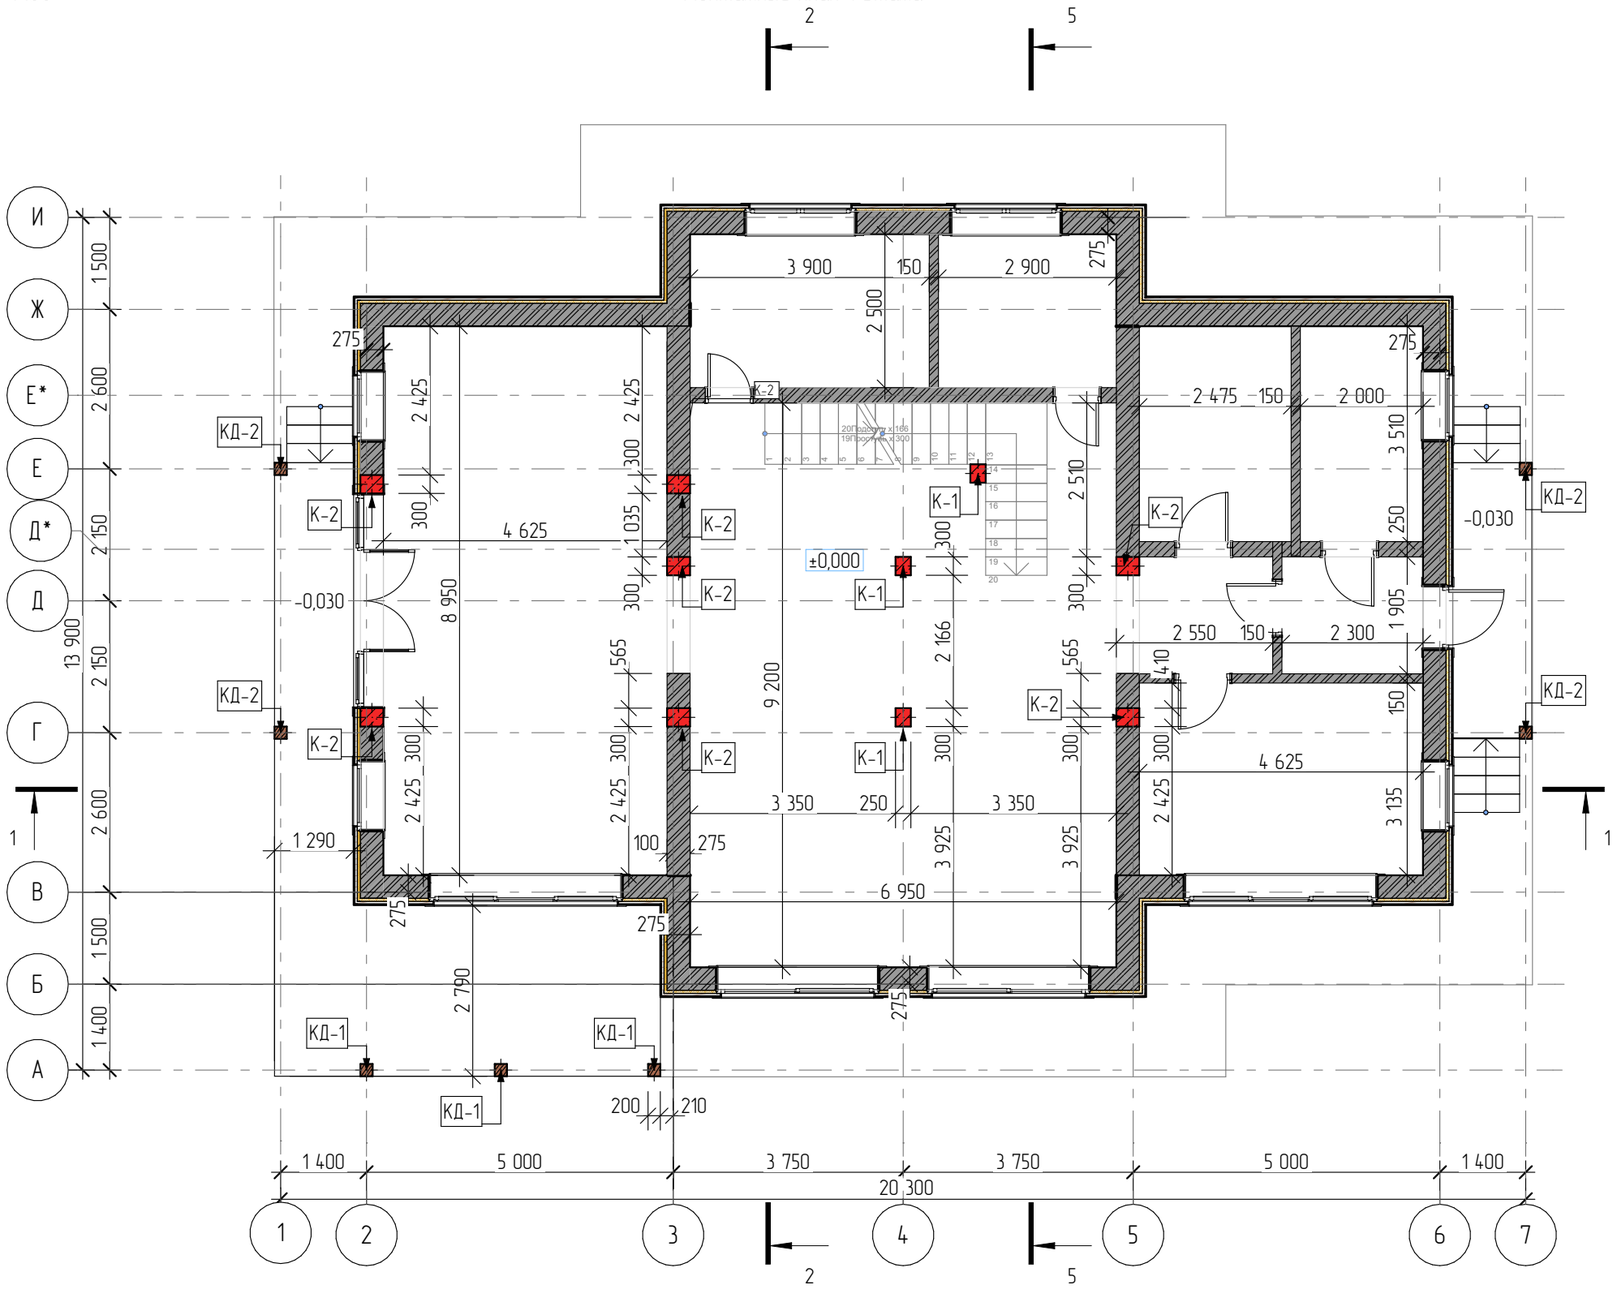

Примечание:

1) За отметку +-0,000 принята отметка чистового пола первого этажа
2) Расположение вентиляционных коммуникаций и прочих инженерных систем показано условно. Проект инженерных коммуникаций будет разрабатываться при заключении договора на инженерные работы. Количество и наличие вентиляционных, фановых и дымовых труб определяется дополнительным согласованием в сметном расчёте на этапе отделочных работ.
3) Габаритные размеры и расположение печи/камина могут измениться в процессе строительства
4) Ответственность за конструктивное решение и расположение печи/камина относительно несущих деревянных конструкций, фундамента, а также соблюдение мер пожарной безопасности при сооружении и эксплуатации печи/камина, полностью лежат на Заказчике

					2021
Изм.	Кол.уч	Лист	№док.	Подпись	Дата
Архитектор		Салыкова В.Г.			
Заказчик		#Обращение к Заказчику			

#ID Проекта

Адрес: #Полный Адрес Участка

Индивидуальный жилой дом	стадия	лист	листов
	РП	15	
План 1 этажа с размерами М 1:100			

Согласовано


Взам. инв. №

Подпись и дата

Инв. № подл.

М 1:100

Монтажный план 2 этажа

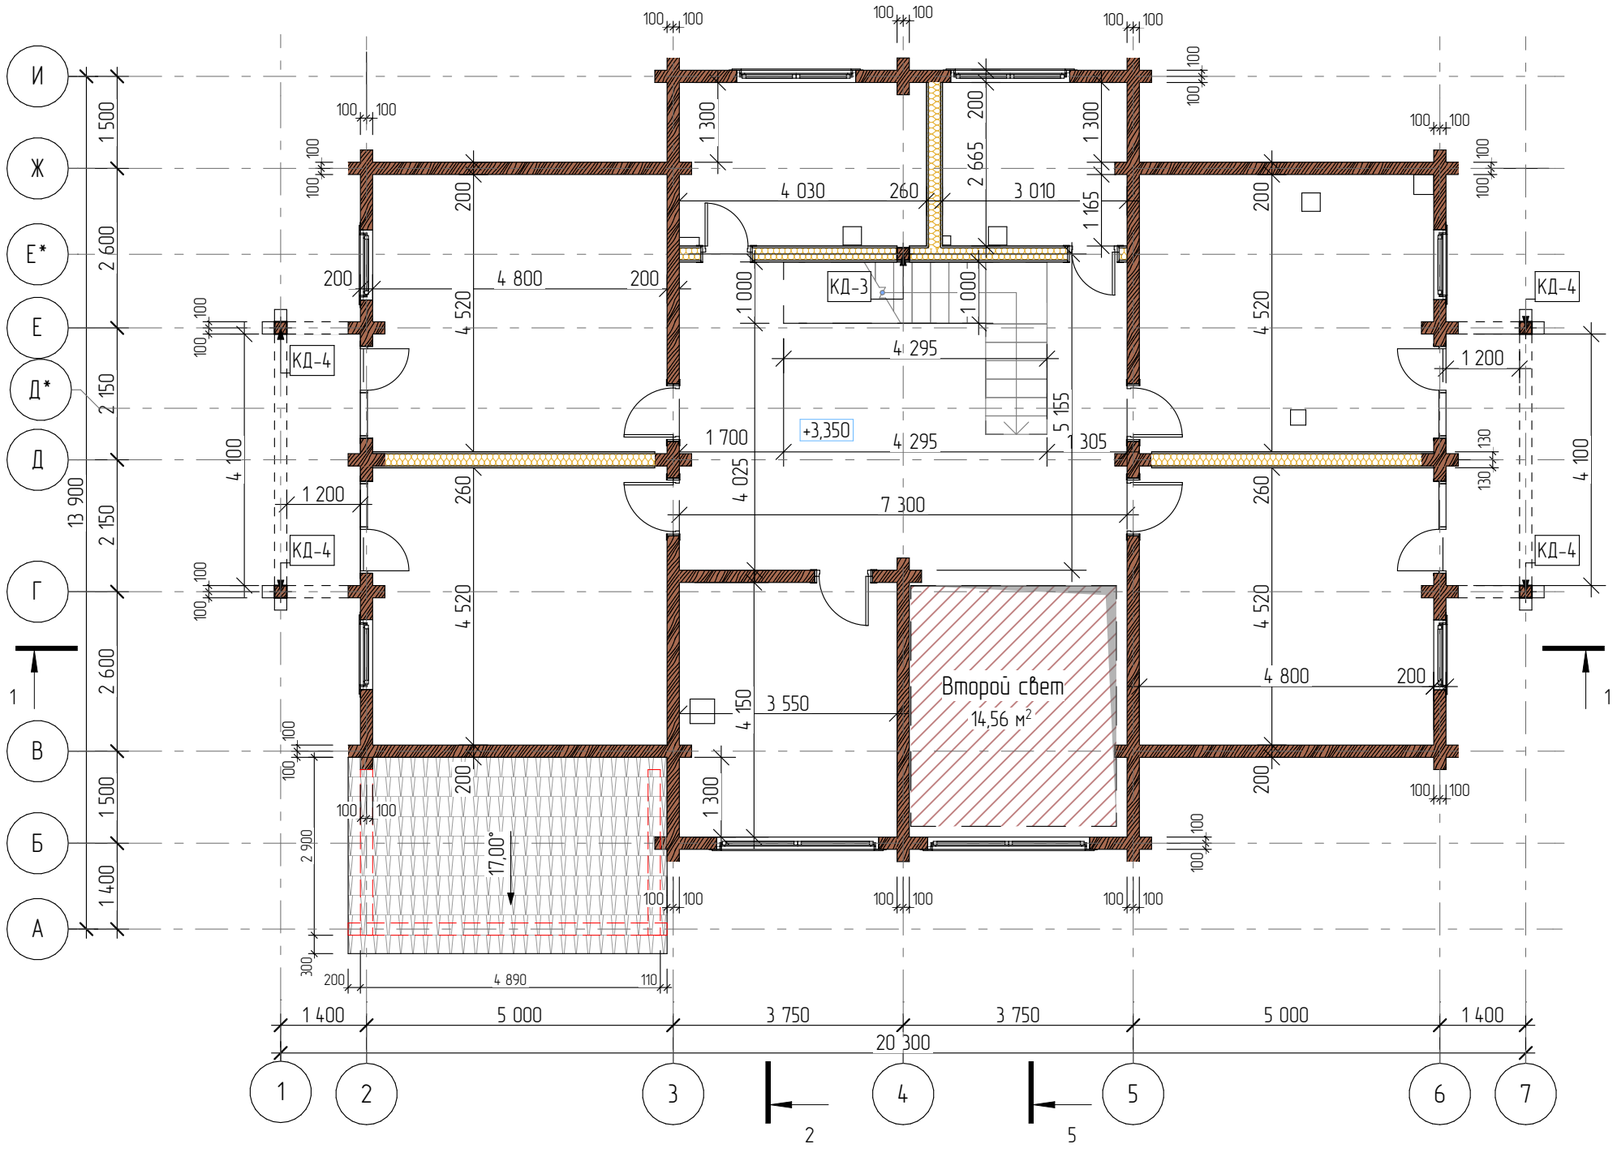

Примечание:

1) За отметку +3,350 принята отметка чистового пола второго этажа
2) Толщина каркасных перегородок показана без учета отделочных материалов
3) Расположение вентиляционных коммуникаций и прочих инженерных систем показано условно. Проект инженерных коммуникаций будет разрабатываться при заключении договора на инженерные работы. Количество и наличие вентиляционных, фановых и дымовых труб определяется дополнительным согласованием в сметном расчёте на этапе отделочных работ.
4) Габаритные размеры и расположение печи/камина могут измениться в процессе строительства
5) Ответственность за конструктивное решение и расположение печи/камина относительно несущих деревянных конструкций, фундамента, а также соблюдение мер пожарной безопасности при сооружении и эксплуатации печи/камина, полностью лежат на Заказчике

					2021	#ID Проекта		
						Адрес: #Полный Адрес Участка		
Изм.	Кол.уч	Лист	№док.	Подпись	Дата			
						Индивидуальный жилой дом	стадия	лист	листов
							РП	16	
Архитектор		Салыкова В.Г.				План 2 этажа с размерами М 1:100			
Заказчик		#Обращение к Заказчику							

Согласовано:


Взам. инв. №

Подпись и дата

Инв. № подл.

М 1:100

Маркировочный план 1 этажа

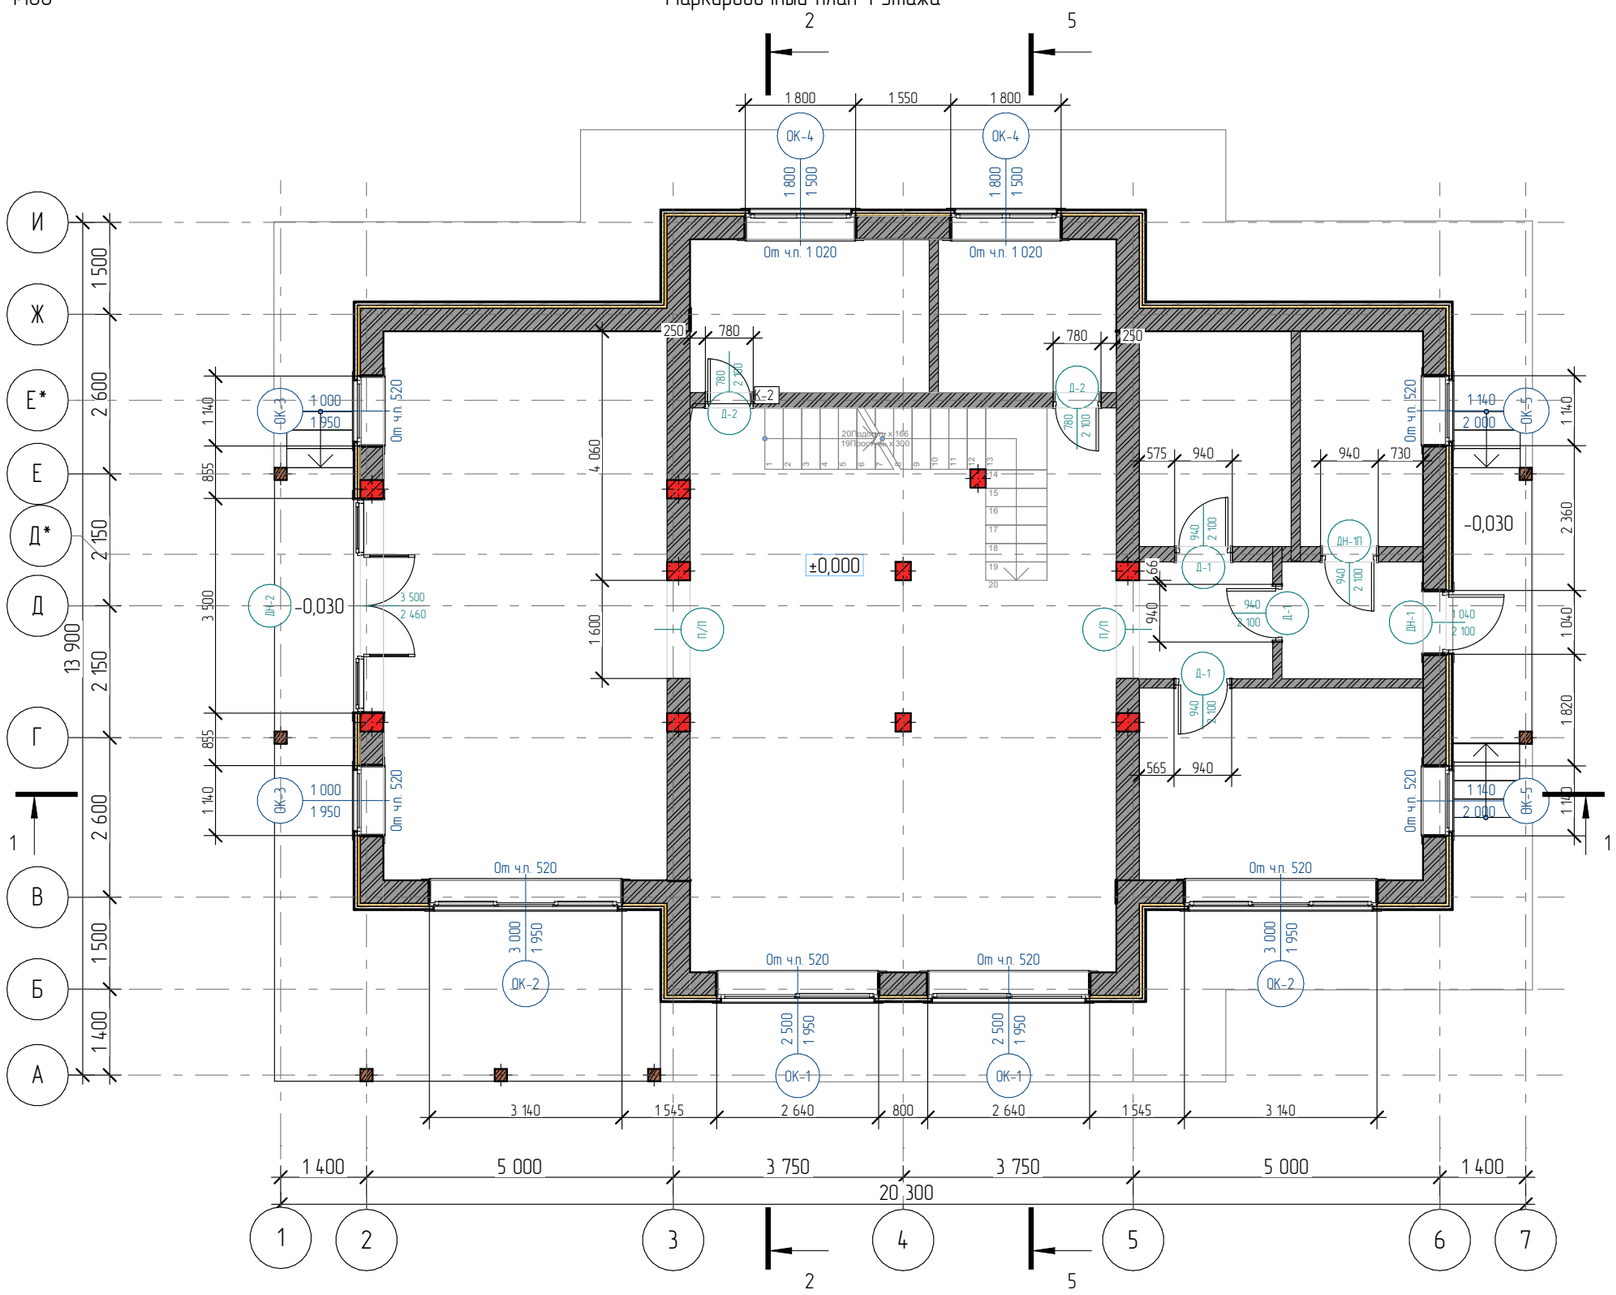

Условные обозначения

ОК-3	Маркировка Окна; См. спецификацию заполнения оконных проемов
ДН-1	Дверь наружняя. См. спецификацию заполнения дверных проемов
Д-1	Дверь межкомнатная
ДН-1П	Дверь противопожарная

Согласовано:

Взам. инв. №


Подпись и дата

Инв. № подл.

					2021	#ID Проекта		
						Адрес: #Полный Адрес Участка		
Изм.	Кол.уч	Лист	№док.	Подпись	Дата			
						Индивидуальный жилой дом	стадия	лист	листов
							РП	17	
Архитектор		Салыкова В.Г.				Маркировочный план 1 этажа М 1:100			
Заказчик		#Обращение к Заказчику							

М 1:100

Маркировочный план 2 этажа

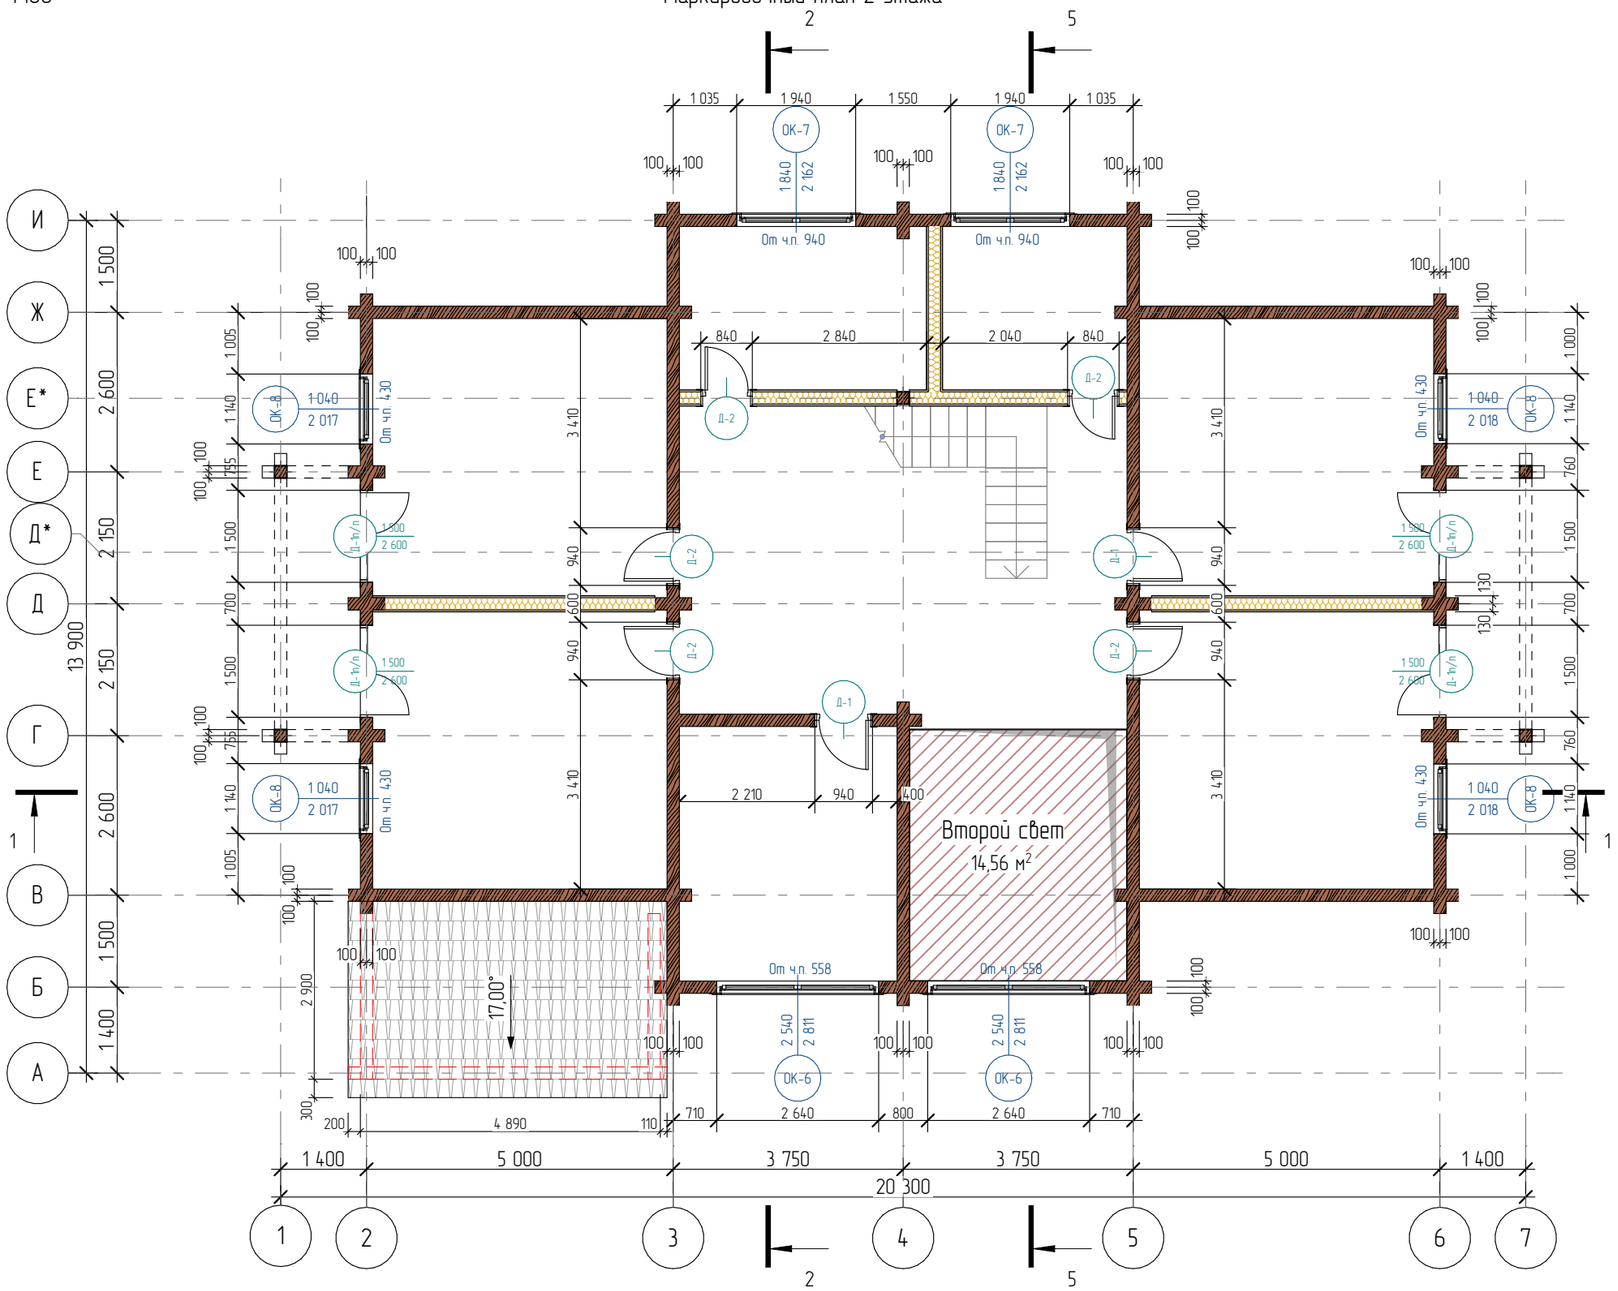

Условные обозначения

ОК-8 — Маркировка Окна; См. спецификацию заполнения оконных проемов

Д-1 — Дверь межкомнатная

Примечание:

1) Привязка проёмов окон и дверей в клееном брусе указывается с учетом обсады

					2021	#ID Проекта	
						Адрес: #Полный Адрес Участка	
Изм.	Кол.уч	Лист	№док.	Подпись	Дата		
						Индивидуальный жилой дом	стадия: РП; лист: 18; листов:
Архитектор		Салыкова В.Г.					
Заказчик		#Обращение к Заказчику				Маркировочный план 2 этажа М 1:100	

Согласовано:


Взам. инв. №

Подпись и дата

Инв. № подл.

М 1:100

План кровли

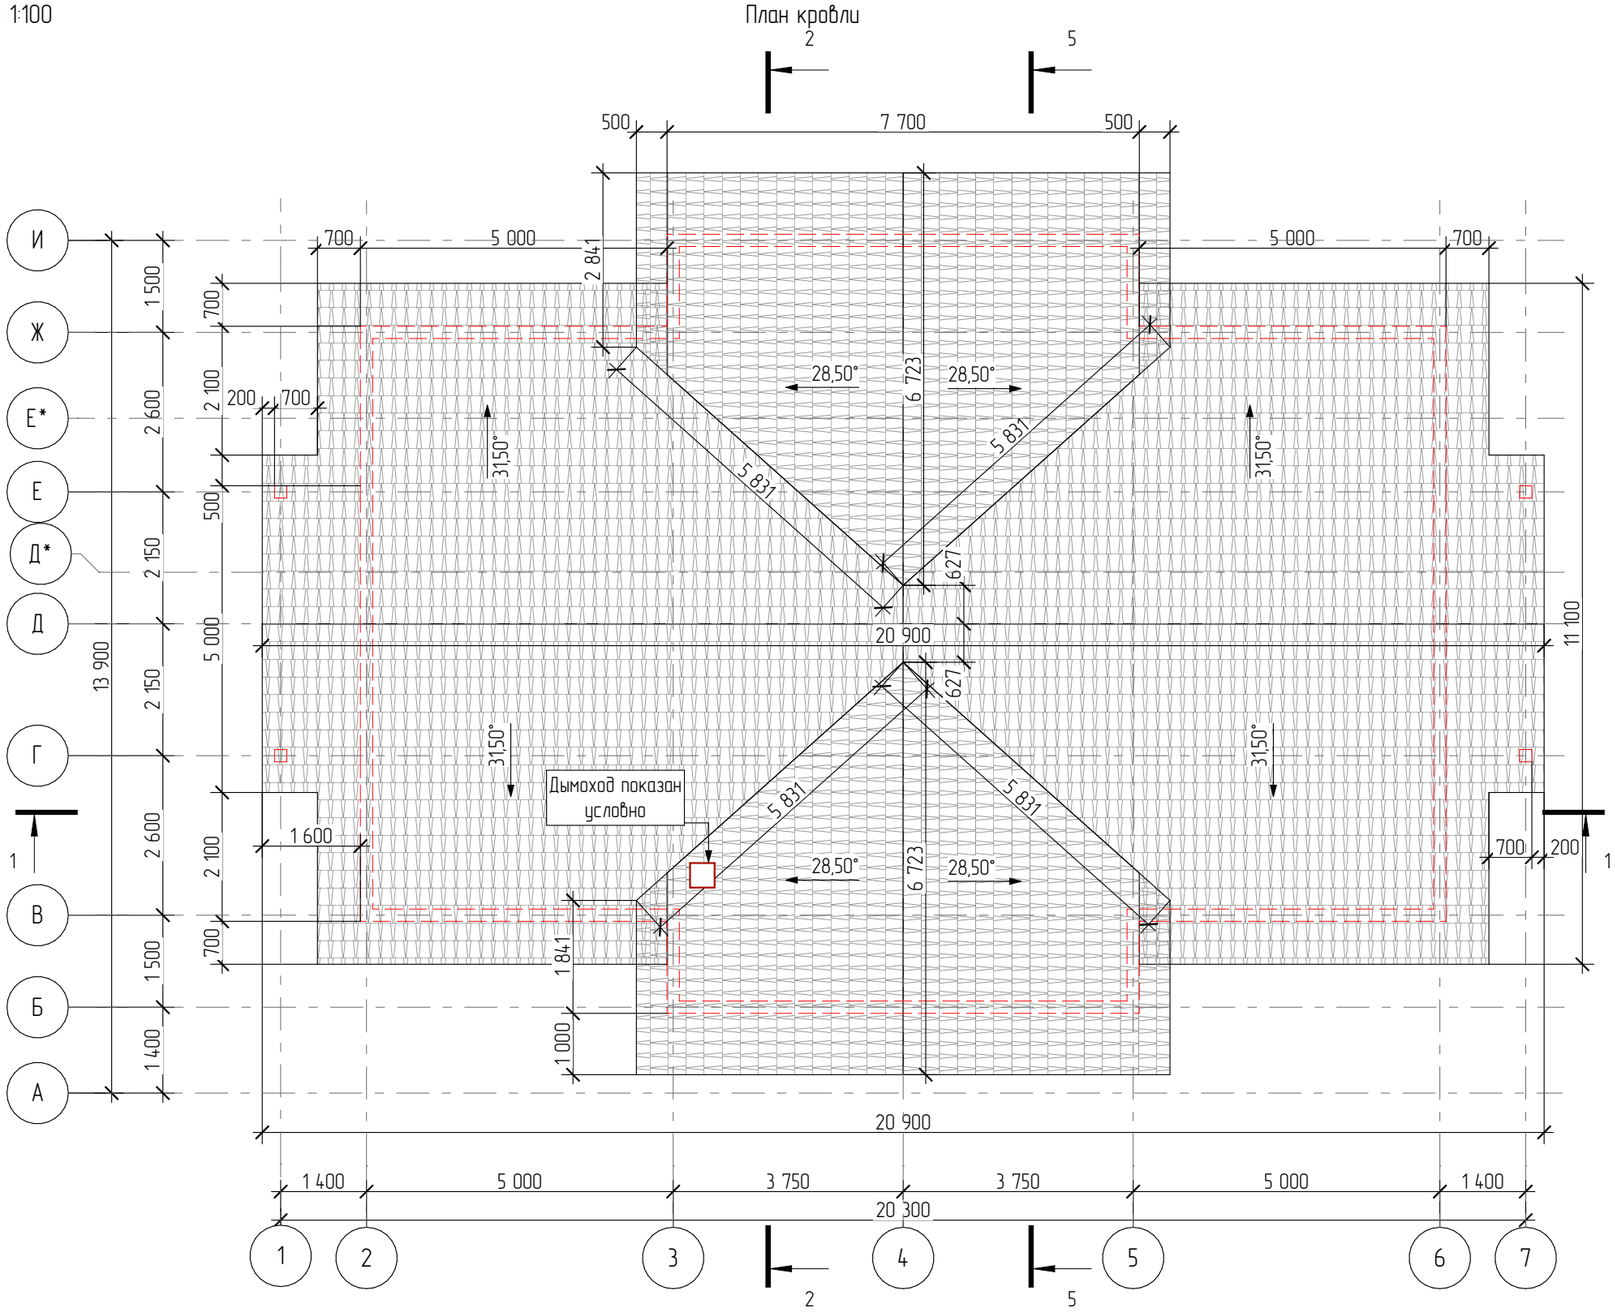

Условные обозначения:

- - - - - - контур наружной стены

Примечание:

1) Все размеры даны в горизонтальной проекции
2) Наличие снегозадержателей и водосточной системы определяется сметным расчётом.
3) Погрешность монтажа вент выхода по горизонтали 16см а по длине волны 38 (при монтаже в металлочерепицу или Брас)
4) Монтаж кровельного покрытия выполнять в соответствии с инструкциями завода-изготовителя.
5) Расположение вентиляционных коммуникаций и прочих инженерных систем показано условно. Проект инженерных коммуникаций будет разрабатываться при заключении договора на инженерные работы. Количество и наличие вентиляционных, фановых и дымовых труб определяется дополнительным согласованием в сметном расчёте на этапе отделочных работ.

					2021
Изм.	Кол.уч	Лист	№док.	Подпись	Дата
Архитектор		Салыкова В.Г.			
Заказчик		#Обращение к Заказчику			

#ID Проекта

Адрес: #Полный Адрес Участка

Индивидуальный жилой дом	стадия	лист	листов
	РП	19	

План кровли М 1:100

Согласовано


Взам. инв. №

Подпись и дата


Инв. № подл.

М 1:25

1

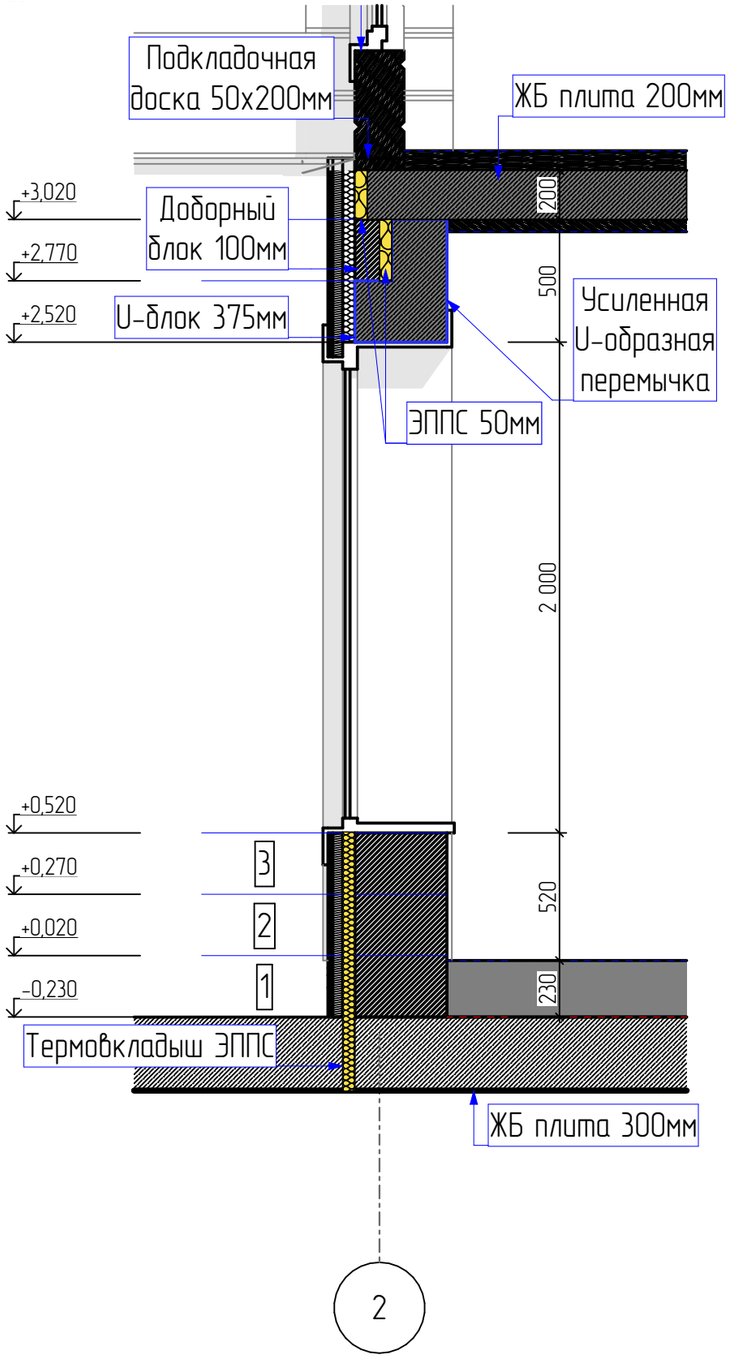


Усиленная U-образная перемычка

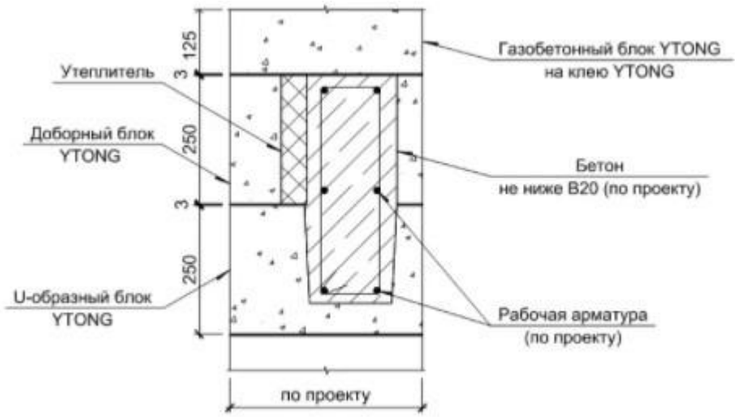

М 1:25

2

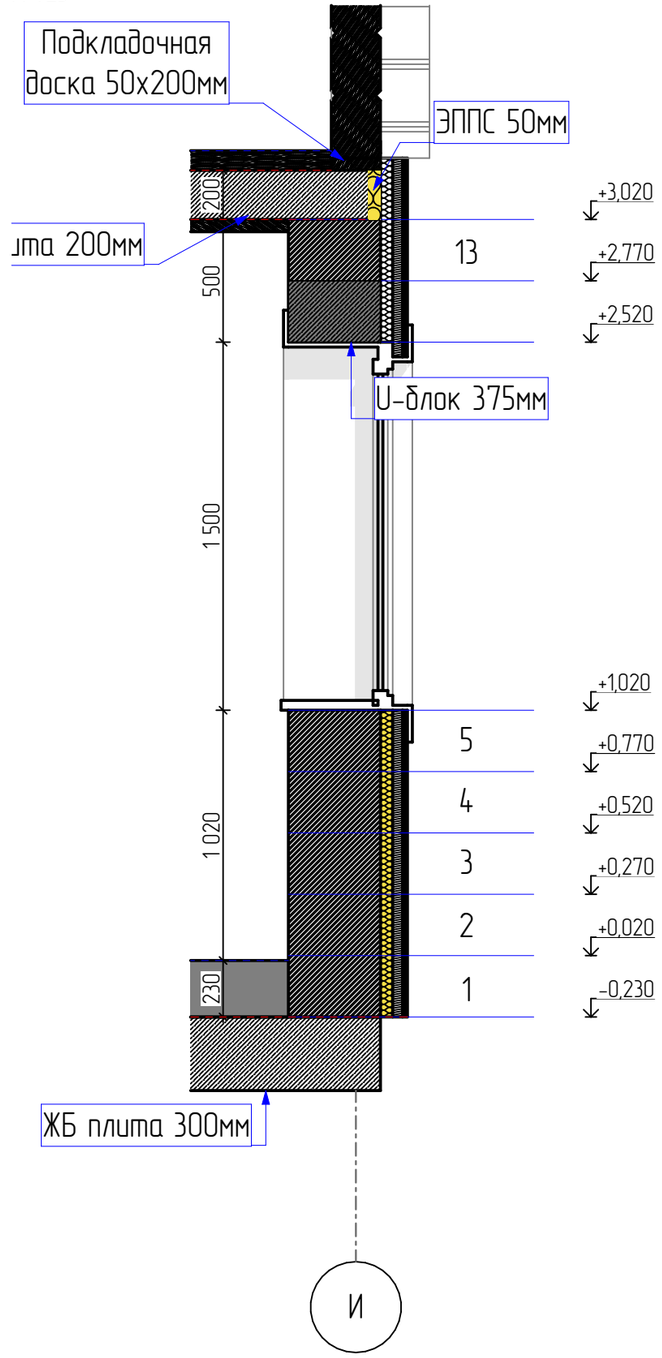

Согласовано

Взам. инв. №


Подпись и дата

Инв. № подл.


					2021	#ID Проекта		
						Адрес: #Полный Адрес Участка		
Изм.	Кол.уч	Лист	№док.	Подпись	Дата			
						Индивидуальный жилой дом	стадия	лист	листов
							РП	20	
Архитектор		Салыкова В.Г.				Фрагменты разрезов М 1:100			
Заказчик		#Обращение к Заказчику							

М 1:100


Лестница

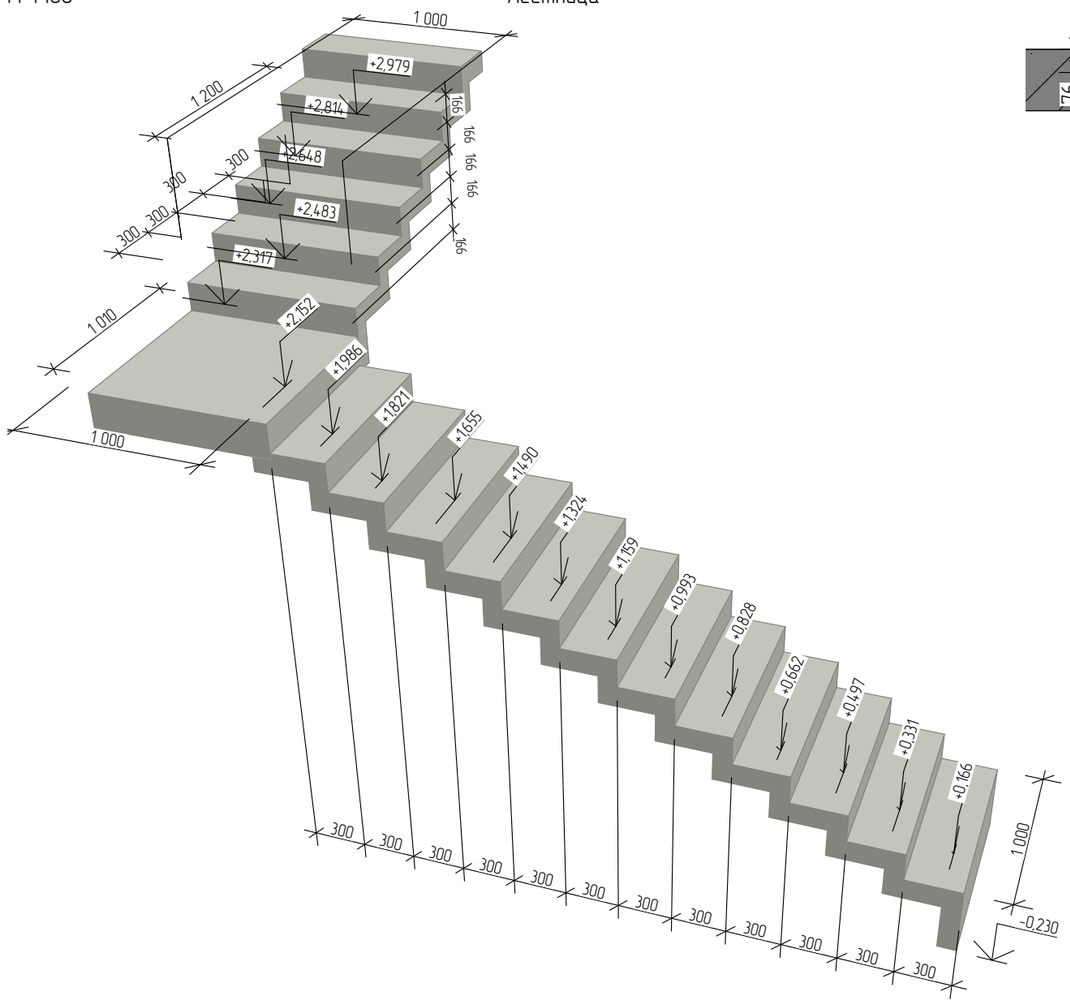

М 1:20

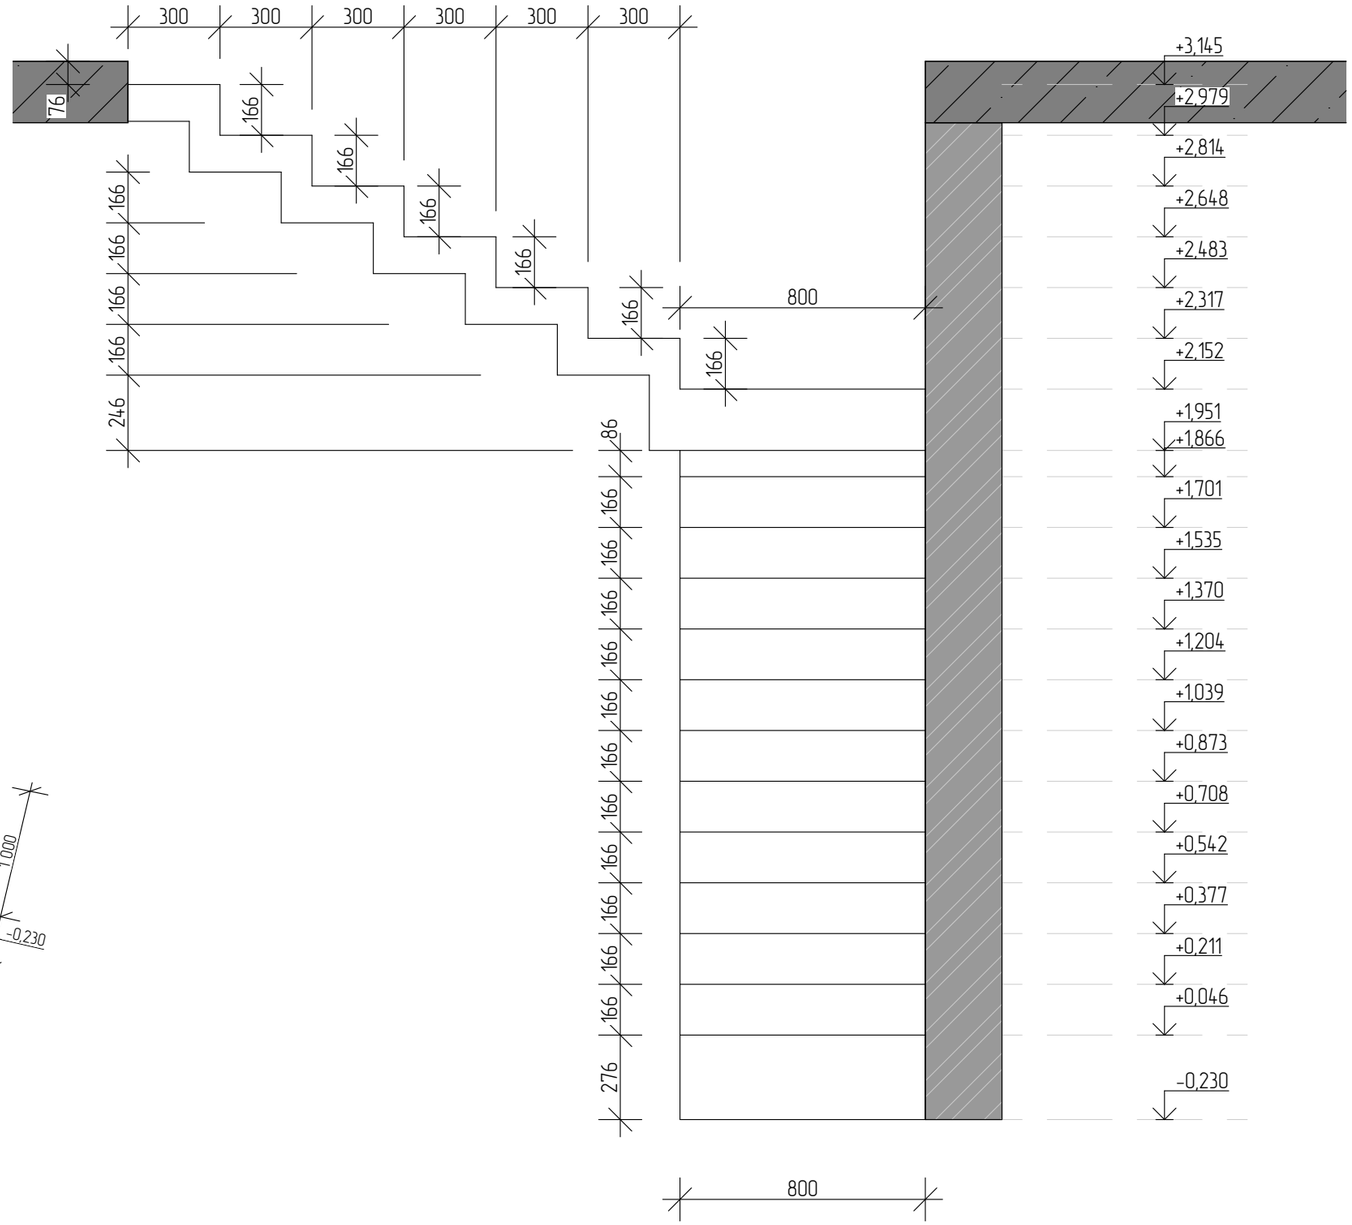

М 1:50

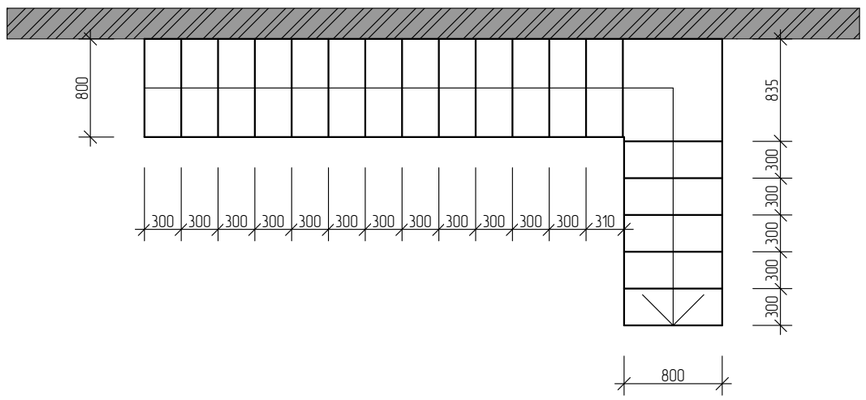










					2021	#ID Проекта	
						Адрес: #Полный Адрес Участка	
Изм.	Кол.уч	Лист	№док.	Подпись	Дата		
						Индивидуальный жилой дом	стадия: РП; лист: 21; листов:
Архитектор		Салыкова В.Г.					
Заказчик		#Обращение к Заказчику				Схема устройства ЖБ лестницы М 1:100	

Согласовано:

Взам. инв. №

Подпись и дата

Инв. № подл.

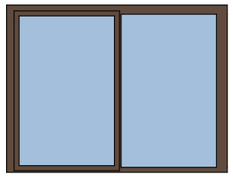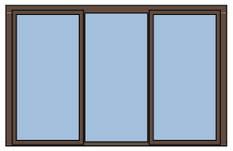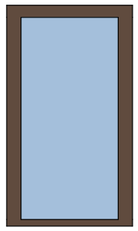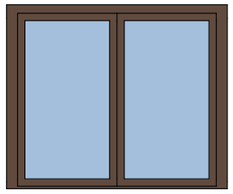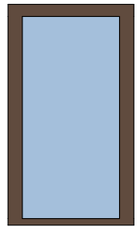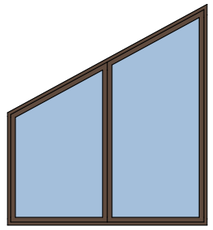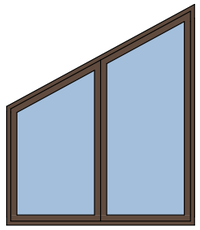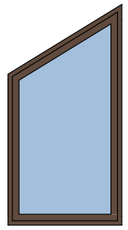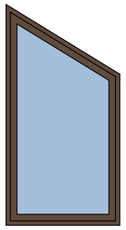Поз.	ОК-1	ОК-2	ОК-3	ОК-4
Общий вид				
Размеры Блока	2 500×1 950	3 000×1 950	1 000×1 950	1 660×1 450
Поз.	ОК-5	ОК-6	ОК-7	ОК-8
Общий вид				
Размеры Блока	1 000×1 950	2 500×2 771	1 800×2 122	1 000×1 977
Поз.	ОК-8			
Общий вид				
Размеры Блока	1 000×1 978			

Спецификация оконных проемов и заполнений

Поз.	Обозначение	Размеры проема, мм.	Размеры блока, мм.	Кол-во, шт	Этаж	Примечание
ОК-1		2 640×2 000	2 500×1 950	2	1 этаж	
ОК-2		3 140×2 000	3 000×1 950	2	1 этаж	
ОК-3		1 140×2 000	1 000×1 950	2	1 этаж	
ОК-4		1 800×1 500	1 660×1 450	2	1 этаж	
ОК-5		1 140×2 000	1 000×1 950	2	1 этаж	
ОК-6		2 540×2 811	2 500×2 771	2	Кровля	
ОК-7		1 840×2 162	1 800×2 122	2	Кровля	
ОК-8		1 040×2 017	1 000×1 977	2	2 этаж	
ОК-8		1 040×2 018	1 000×1 978	2	2 этаж	

Примечание:

1) Открывание окон, итоговые размеры оконных/дверных проемов и блоков, и их конструкции, расположение, кол-во, наличие шпросов, а также доп. декоративных и конструктивных элементов согласовывается с фирмой производителем/Подрядчиком.

2) Окна показаны снаружи.

3) Итоговый материал изготовления окон определяется сметным расчётом

4) В габариты оконных проемов включен размер обсадной коробки.

5) Оконный проем (фактический размер окна отличается на размер обсадной коробки и технологического зазора на установку. Ориентировочно размер изделия будет меньше на 15 см на всю ширину и высоту окна)





					2021	#ID Проекта		
						Адрес: #Полный Адрес Участка		
Изм.	Кол.уч	Лист	№док.	Подпись	Дата			
						Индивидуальный жилой дом	стадия	лист	листов
							РП	22	
Архитектор		Салыкова В.Г.							
						Спецификация заполнения оконных проёмов			
Заказчик		#Обращение к Заказчику							



Согласовано:

Взам. инв. №

Подпись и дата

Инв. № подл.

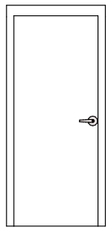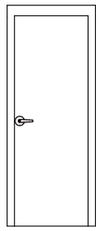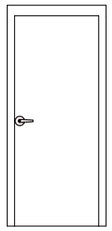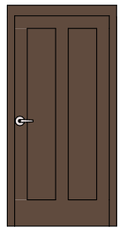Поз.	Д-1	Д-2	Д-2	ДН-1
Общий вид				
Размеры Блока	880×2 040	780×2 040	880×2 040	980×2 040

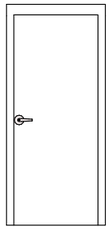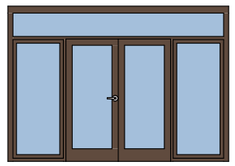Поз.	ДН-1П	ДН-2
Общий вид		
Размеры Блока	880×2 040	3 440×2 400

Спецификация дверных проемов и заполнений

Поз.	Откр.	Размеры проема	Размеры Блока	Кол-во, шт	Этаж	Примечание
Д-1	Л	940×2 100	880×2 040	3	1 этаж	
Д-1	П	940×2 100	880×2 040	1	2 этаж	
Д-1	Л	940×2 100	880×2 040	1	2 этаж	
Д-2	П	780×2 100	780×2 040	2	1 этаж	
Д-2	П	840×2 100	780×2 040	2	2 этаж	
Д-2	П	940×2 100	880×2 040	2	2 этаж	
Д-2	Л	940×2 100	880×2 040	1	2 этаж	
ДН-1	П	1 040×2 100	980×2 040	1	1 этаж	
ДН-1П	П	940×2 100	880×2 040	1	1 этаж	
ДН-2	Л	3 500×2 460	3 440×2 400	1	1 этаж	

Примечание:

1) Открывание дверных проемов; расположение, количество и наличие шпросов согласовывается с фирмой производителем в отдельной спецификации.

2) Двери показаны снаружи.

3) Итоговый материал изготовления дверей определяется сметным расчётом

4) Двери с маркировкой кб. Пример Д-1кб даны на плане с размерами с учетом обсады в стенах из клееного бруса. Проемы по высоте выпиливаются по месту. В спецификации указан размер с деревянной коробкой.

5) Дверной проем (фактический размер двери в стене из клееного бруса отличается на размер обсадной коробки и технологического зазора на установку по ширине. Ориентировочно размер изделия будет меньше на 10 см на всю ширину двери, по высоте проем выбирается по месту)


Согласовано:

Взам. инв. №

Подпись и дата

Инв. № подл.

					2021	#ID Проекта			
						Адрес: #Полный Адрес Участка			
Изм.	Кол.уч	Лист	№док.	Подпись	Дата				
						Индивидуальный жилой дом	стадия	лист	листов
							РП	23	
Архитектор		Салыкова В.Г.				Спецификация заполнения дверных проёмов			
Заказчик		#Обращение к Заказчику							

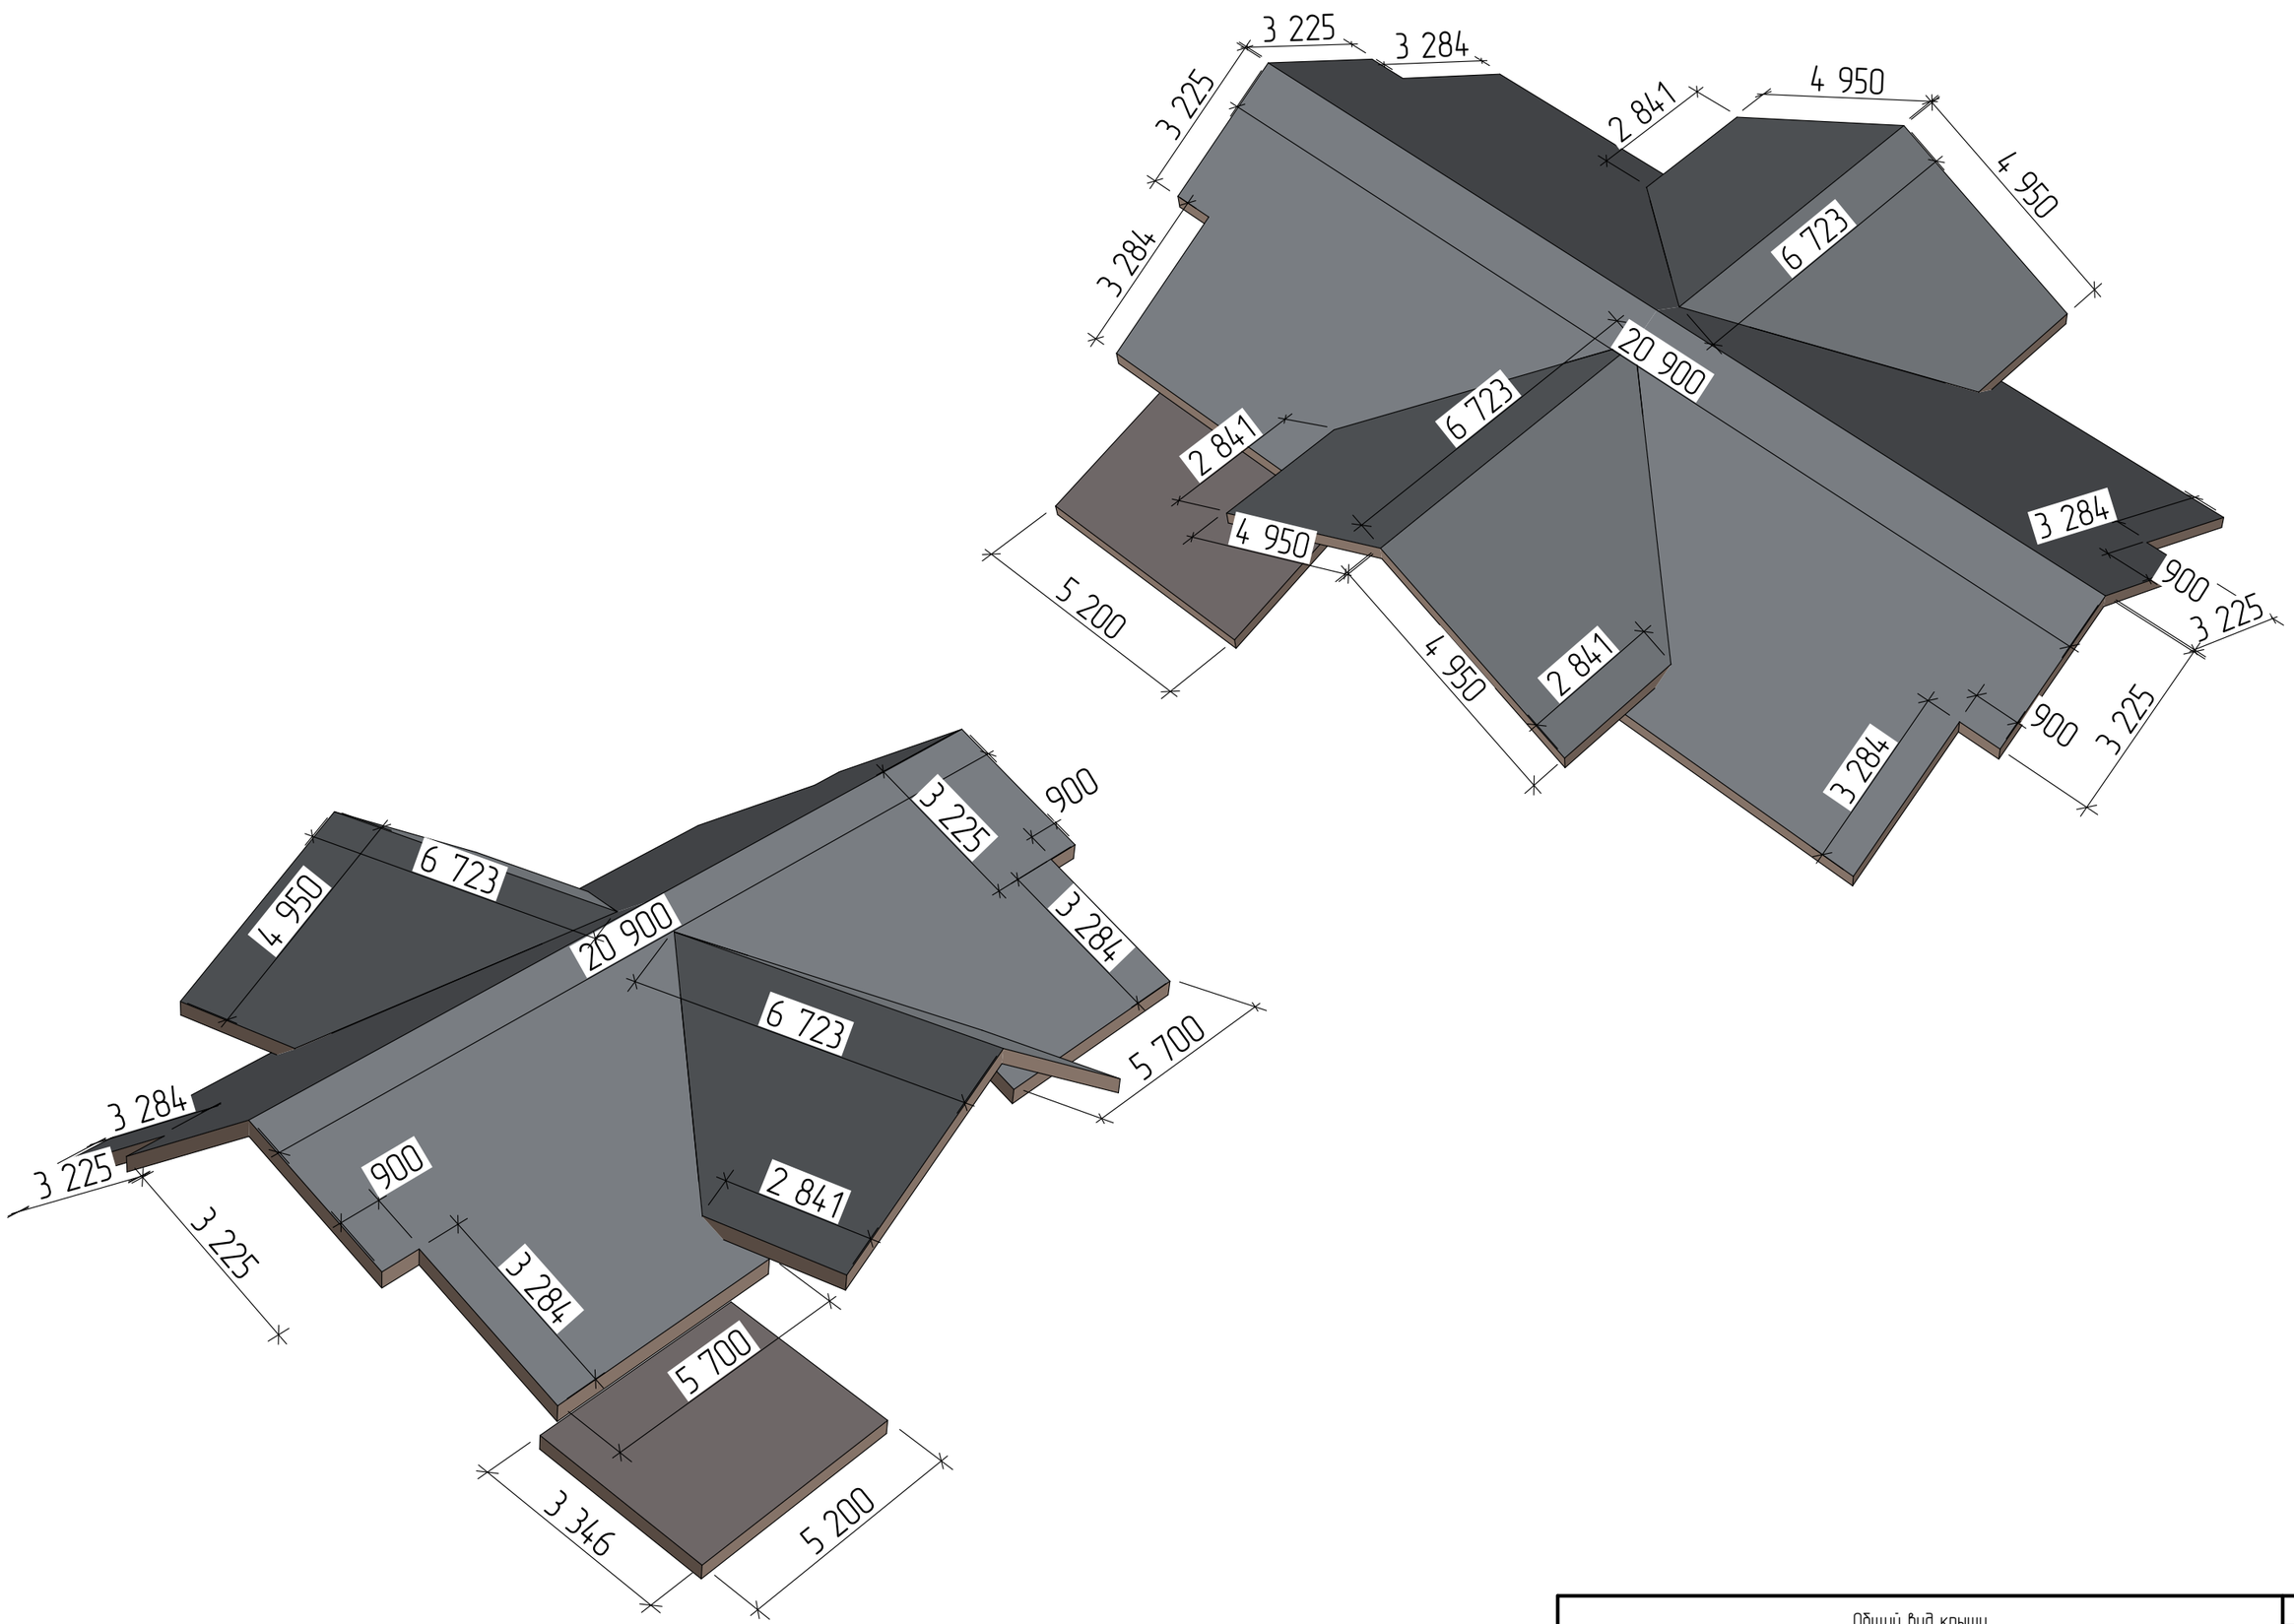

Согласовано

Взам. инв. №

Подпись и дата

Инв. № подл.

Общий вид крыши

Лист 24

Общий вид 1



Общий вид 2



Общий вид 3



Общий вид 4



Общие виды

Лист

Согласовано

Взам. инв. №

Подпись и дата

Инв. № подл.


Общий вид 1 этаж



Общий вид 1 этаж



Общий вид 2 этаж

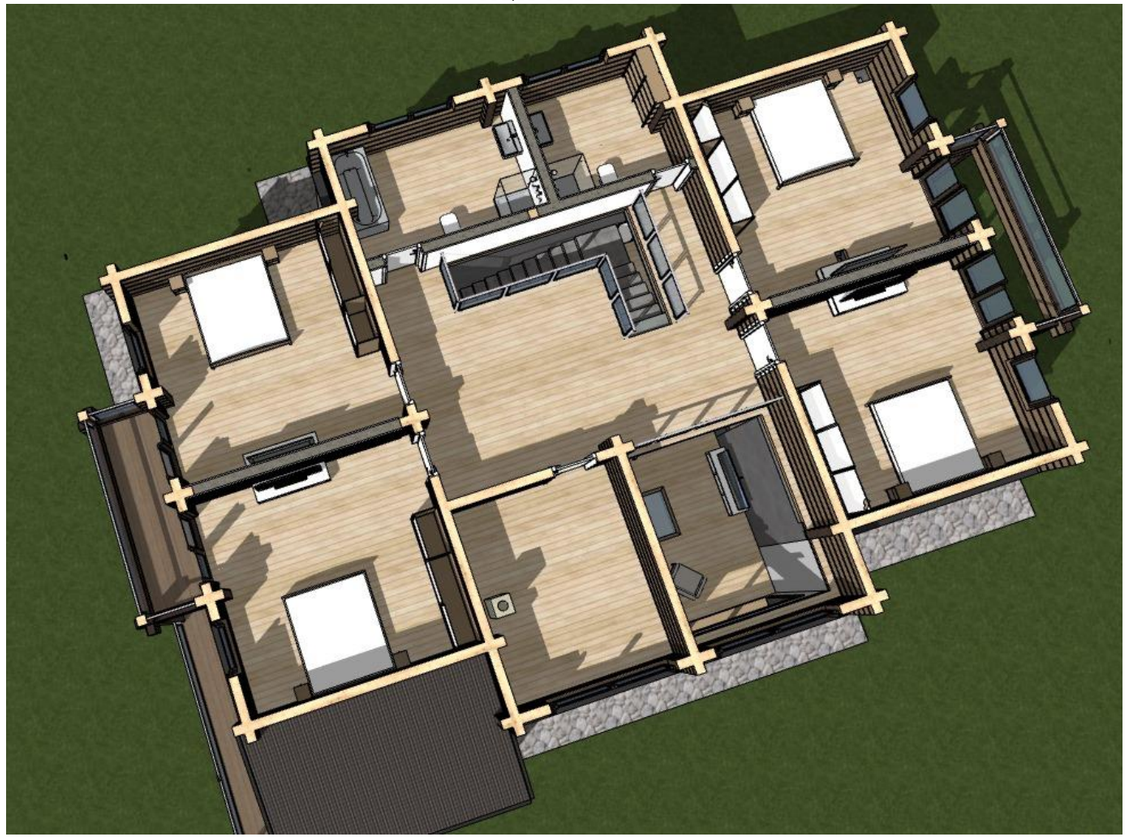

Общий вид 2 этаж



Согласовано

Взам. инв. №

Подпись и дата

Инв. № подл.

Общие виды (поэтажные)

Лист

26

ОБЪЕКТ ИНДИВИДУАЛЬНОГО ЖИЛИЩНОГО СТРОИТЕЛЬСТВА



ЭСКИЗНЫЙ ПРОЕКТ


ШИФР: #ID ПРОЕКТА

АРХИТЕКТУРНЫЕ РЕШЕНИЯ

САНКТ-ПЕТЕРБУРГ 2021

М 1:100

План 1 этажа с расстановкой мебели

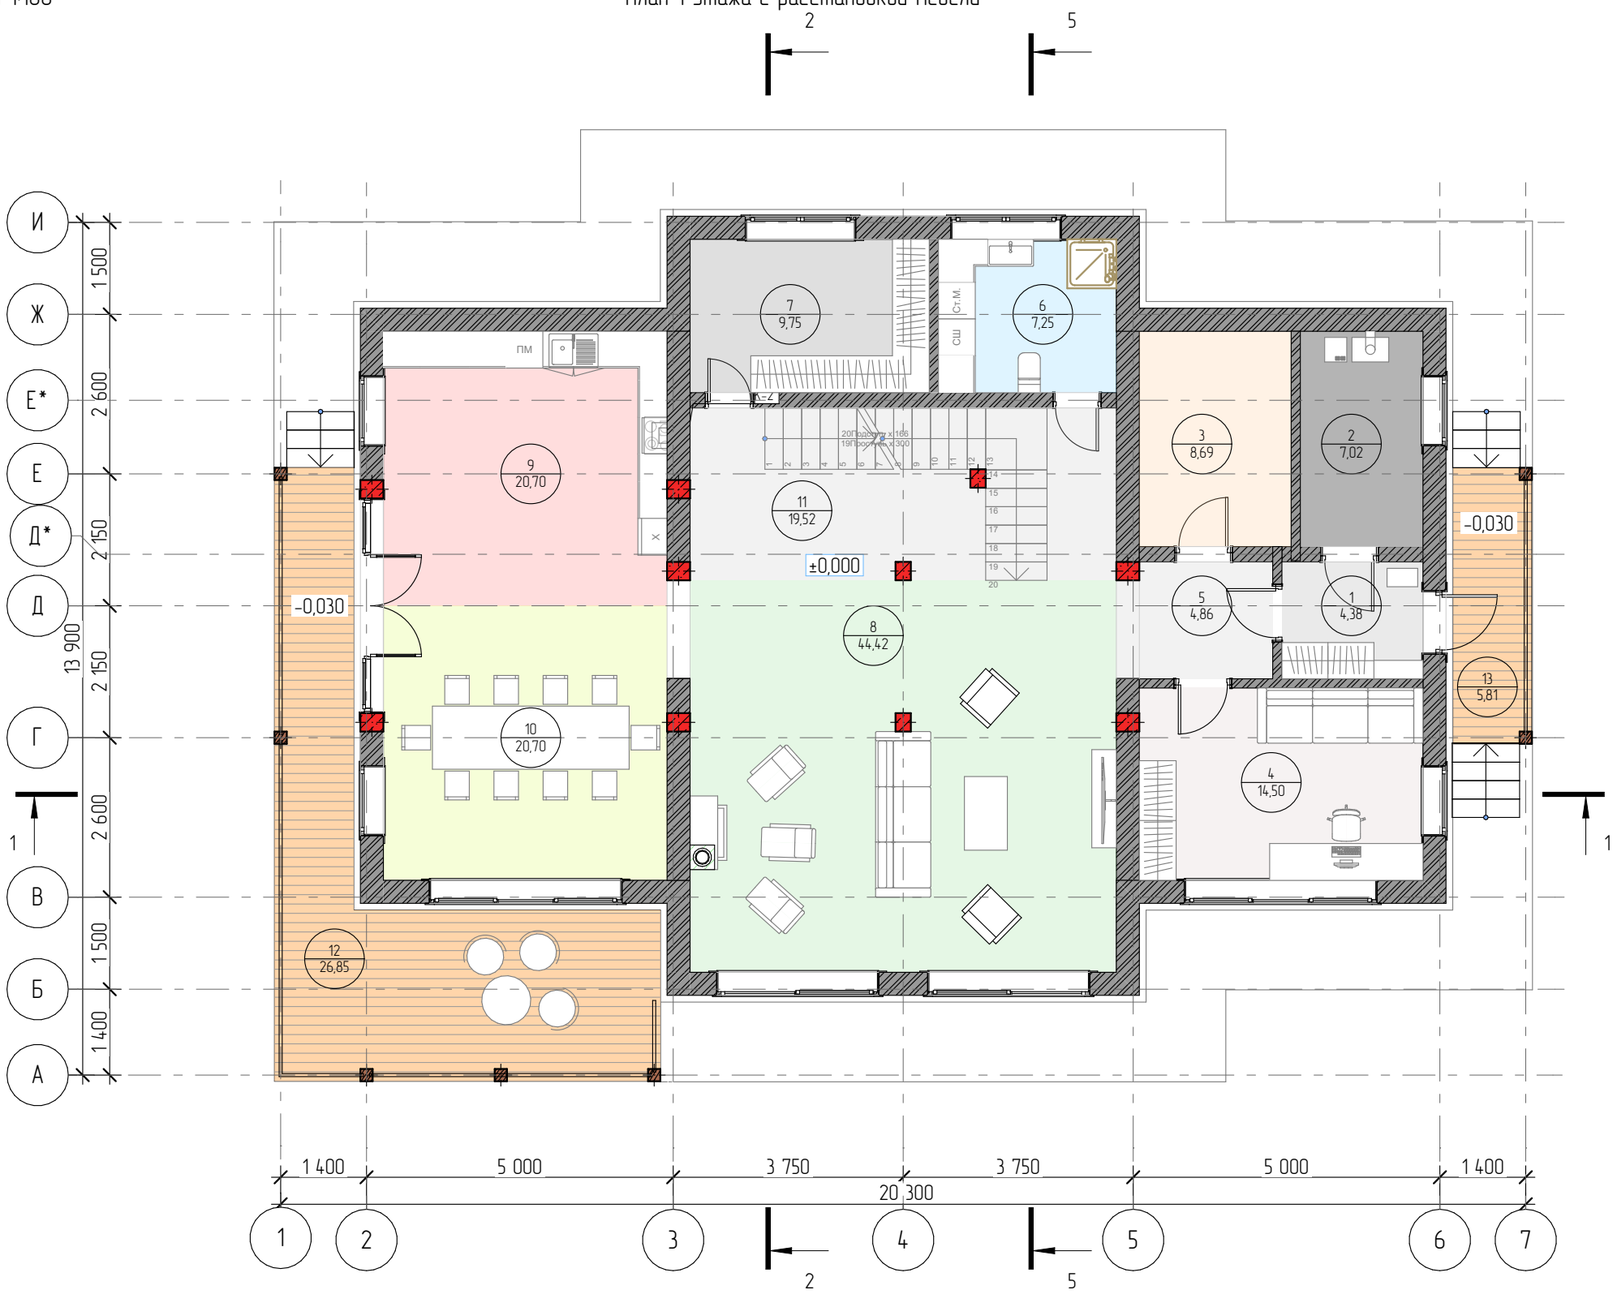

Экспликация 1 этажа

Расположение поиещений	№ п/п	Наименование	Площадь, м2
Внутр. пом.			
	1	Тамбур	4,38
	2	Котельная	7,02
	3	Тренажерный зал	8,69
	4	Гостевая Комната	14,50
	5	Холл 1	4,86
	6	Санузел	7,25
	7	Гардероб	9,75
	8	Гостиная	44,42
	9	Кухня	20,70
	10	Столовая	20,70
	11	Холл 2	19,52
			161,79 м²
Наружн. пом.			
	12	Терраса	26,85
	13	Крыльцо	5,81
			32,66 м²
			194,45 м²

Примечание:
1) Вся показанная мебель, а также назначение комнат носят условный характер
2) Расположение сан.технических приборов не подлежит перемещению.
3) Площадь помещений показана без учета отделочных материалов и понижающего коэффициента по периметру пола.
4) Все декоративные элементы подлежат дополнительному сметному согласованию.

Изм.	Кол.уч	Лист	№док.	Подпись	Дата
Архитектор		Салыкова В.Г.			
Заказчик		#Обращение к Заказчику			

2021

#ID Проекта

Адрес: #Полный Адрес Участка;
к/н: #ID Участка

Индивидуальный жилой дом

стадия	лист	листов
ЭП	1	

План 1 этажа с расстановкой мебели
М 1:100

Согласовано


Взам. инв. №

Подпись и дата

Инв. № подл.

М 1:100

План 2 этажа с расстановкой мебели

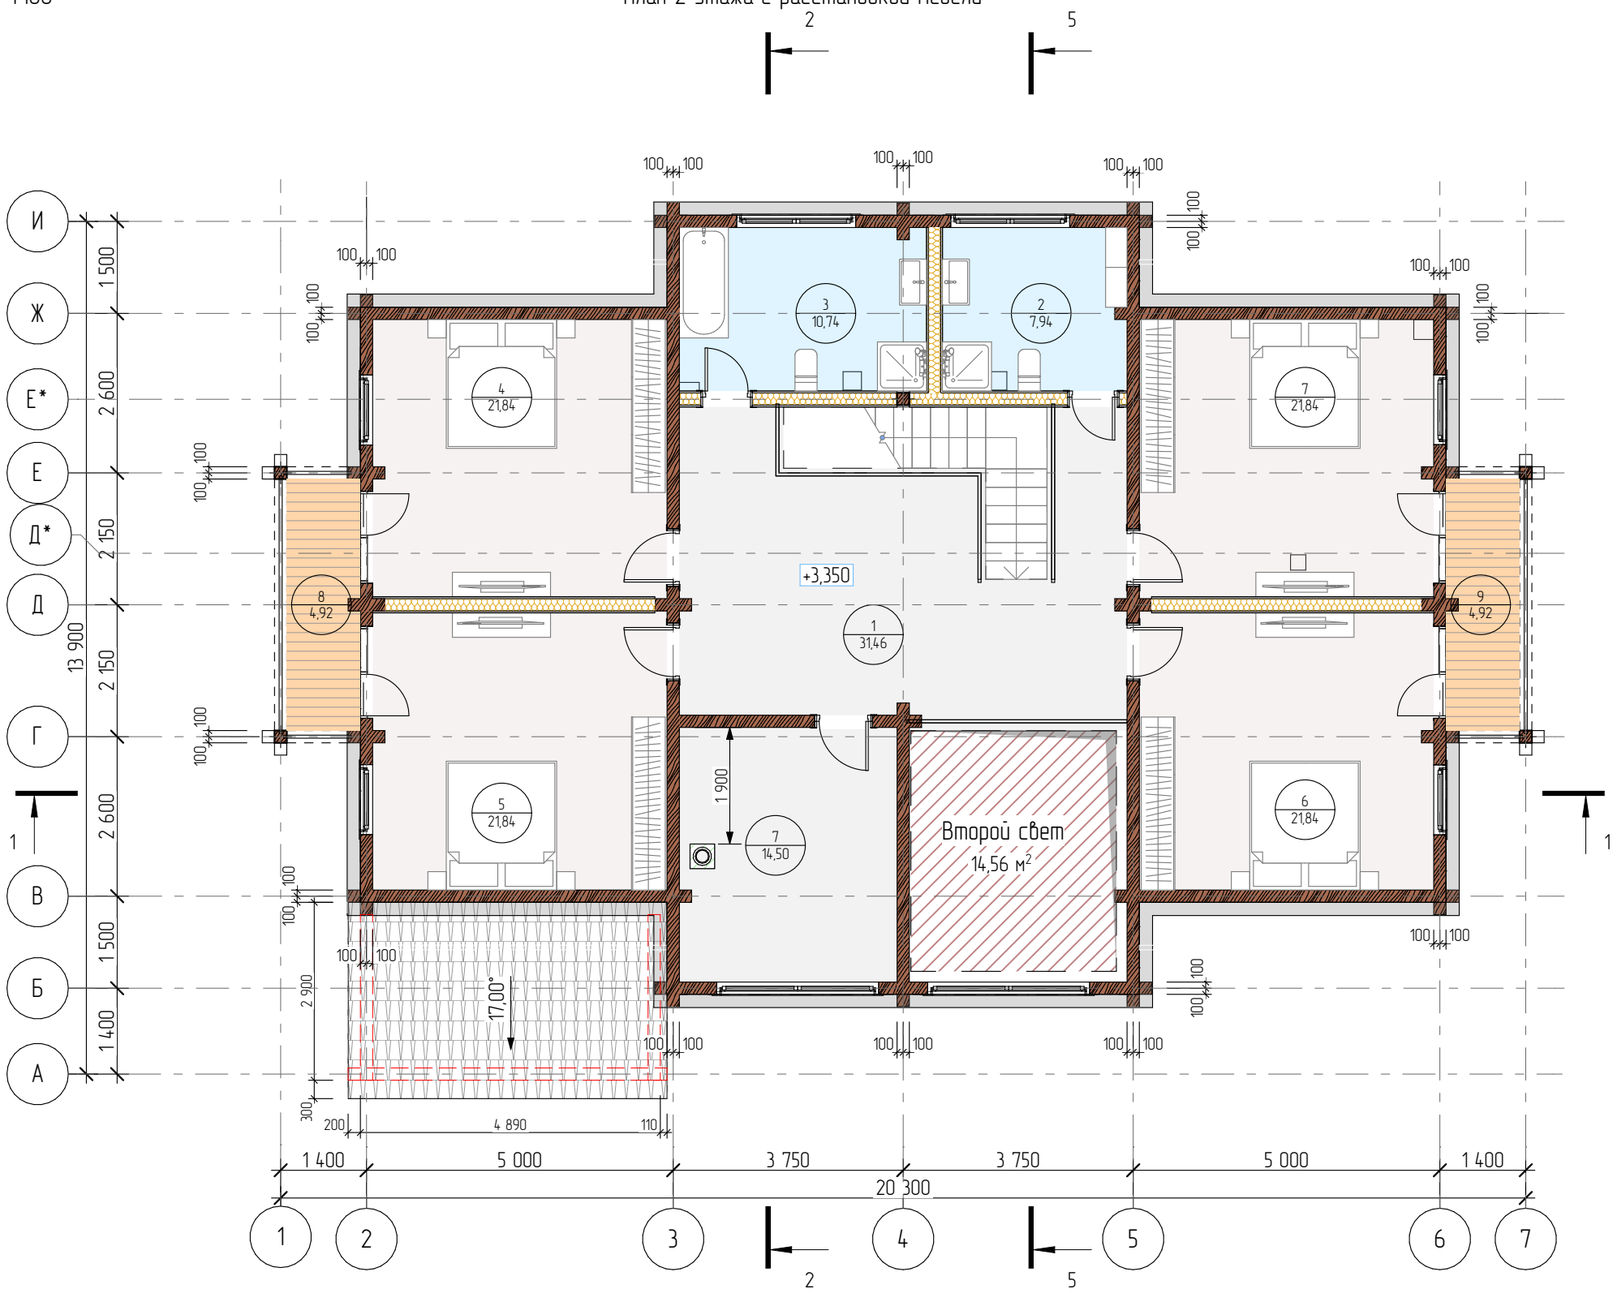

Примечание:
1) Вся показанная мебель, а также назначение комнат носят условный характер
2) Расположение сан.технических приборов не подлежит перемещению.
3) Площадь помещений показана без учета отделочных материалов и понижающего коэффициента по периметру пола.
4) Все декоративные элементы подлежат дополнительному сметному согласованию.

Экспликация 2 этажа

Расположение поиещений	№ п/п	Наименование	Площадь, м2
Внутр. пом.			
	1	Холл	31,46
	2	Санузел 1	7,94
	3	Санузел 2	10,74
	4	Спальня 1	21,84
	5	Спальня 2	21,84
	6	Спальня 3	21,84
	7	Спальня 4	21,84
	7	Гардероб	14,50
			152,00 м²
Наружн. пом.			
	8	Балкон 1	4,92
	9	Балкон 2	4,92
			9,84 м²
			161,84 м²

Согласовано:

Взам. инв. №

Подпись и дата

Инв. № подл.

Изм.	Кол.уч	Лист	№док.	Подпись	Дата
Архитектор		Салыкова В.Г.			
Заказчик		#Обращение к Заказчику			

2021

#ID Проекта

Адрес: #Полный Адрес Участка;
к/н: #ID Участка

Индивидуальный жилой дом

стадия	лист	листов
ЭП	2	

План 2 этажа с расстановкой мебели
М 1:100

Фасад 1-5



Фасад Д-А



Примечание:
1) За отметку +0,000 принята отметка чистового пола первого этажа
2) За отметку +3,350 принята отметка чистового пола второго этажа
3) Номинальные высотные размеры могут отличаться от фактических в силу технологической усадки стенового комплекта и принимаемых отделочных материалов.
4) Несущие перевязки из бревен могут быть ниже основного уровня потолка
5) Все декоративные элементы показаны условно.

					2021	#ID Проекта		
						Адрес: #Полный Адрес Участка; к/н: #ID Участка		
Изм.	Кол.уч	Лист	№док.	Подпись	Дата			
						Индивидуальный жилой дом	стадия	лист	листов
							ЭП	3	
Архитектор		Салыкова В.Г.							
Заказчик		#Обращение к Заказчику				Фасады М 1:100			


Согласовано:

Взам. инв. №


Подпись и дата

Инв. № подл.

Фасад 5-1

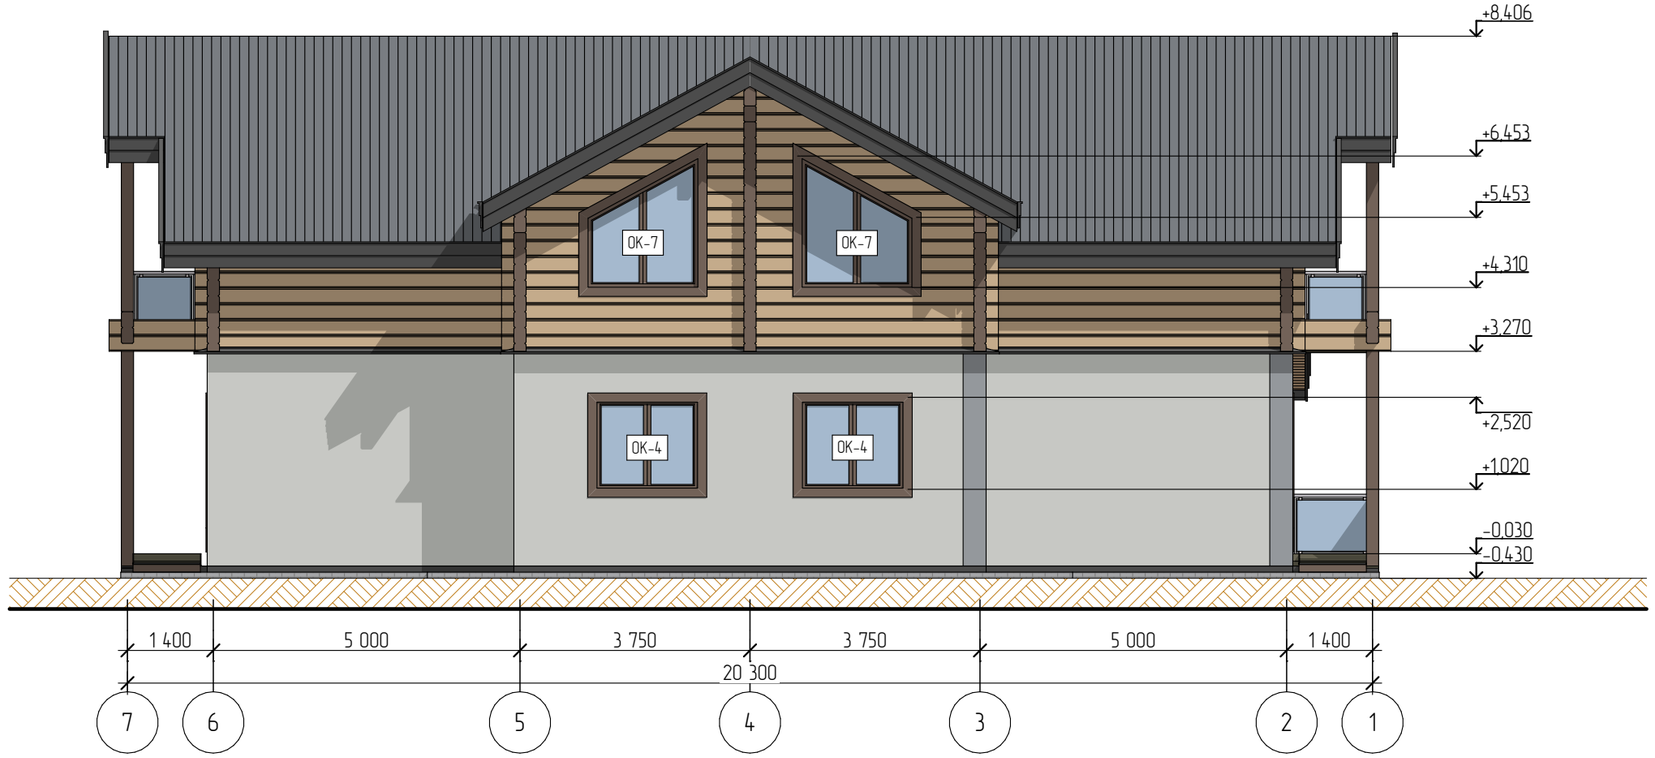

Фасад А-Д

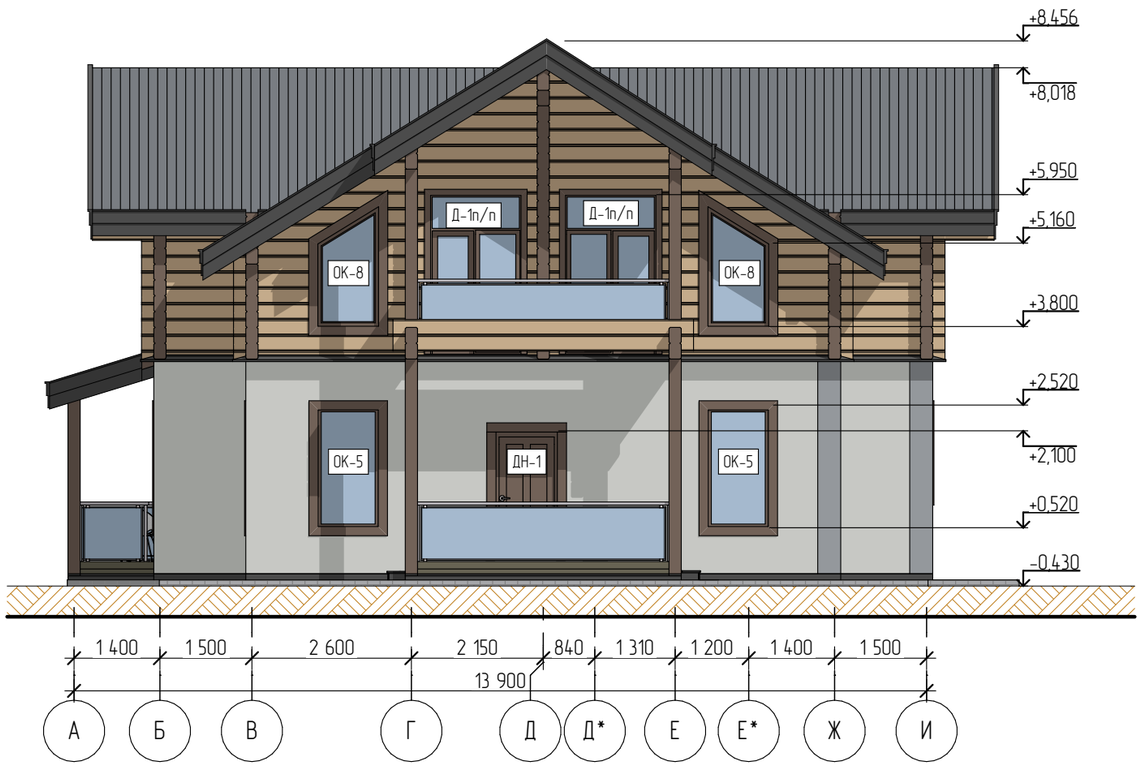

Примечание:
1) За отметку +0,000 принята отметка чистового пола первого этажа
2) За отметку +3,350 принята отметка чистового пола второго этажа
3) Номинальные высотные размеры могут отличаться от фактических в силу технологической усадки стенового комплекта и принимаемых отделочных материалов.
4) Несущие перевязки из бруса могут быть ниже основного уровня потолка
5) Все декоративные элементы показаны условно.

					2021	#ID Проекта		
						Адрес: #Полный Адрес Участка; к/н: #ID Участка		
Изм.	Кол.уч	Лист	№док.	Подпись	Дата			
						Индивидуальный жилой дом	стадия	лист	листов
							ЭП	4	
Архитектор		Салыкова В.Г.							
Заказчик		#Обращение к Заказчику				Фасады М 1:100			

Согласовано:


Взам. инв. №

Подпись и дата

Инв. № подл.

1:75

Разрез 1-1

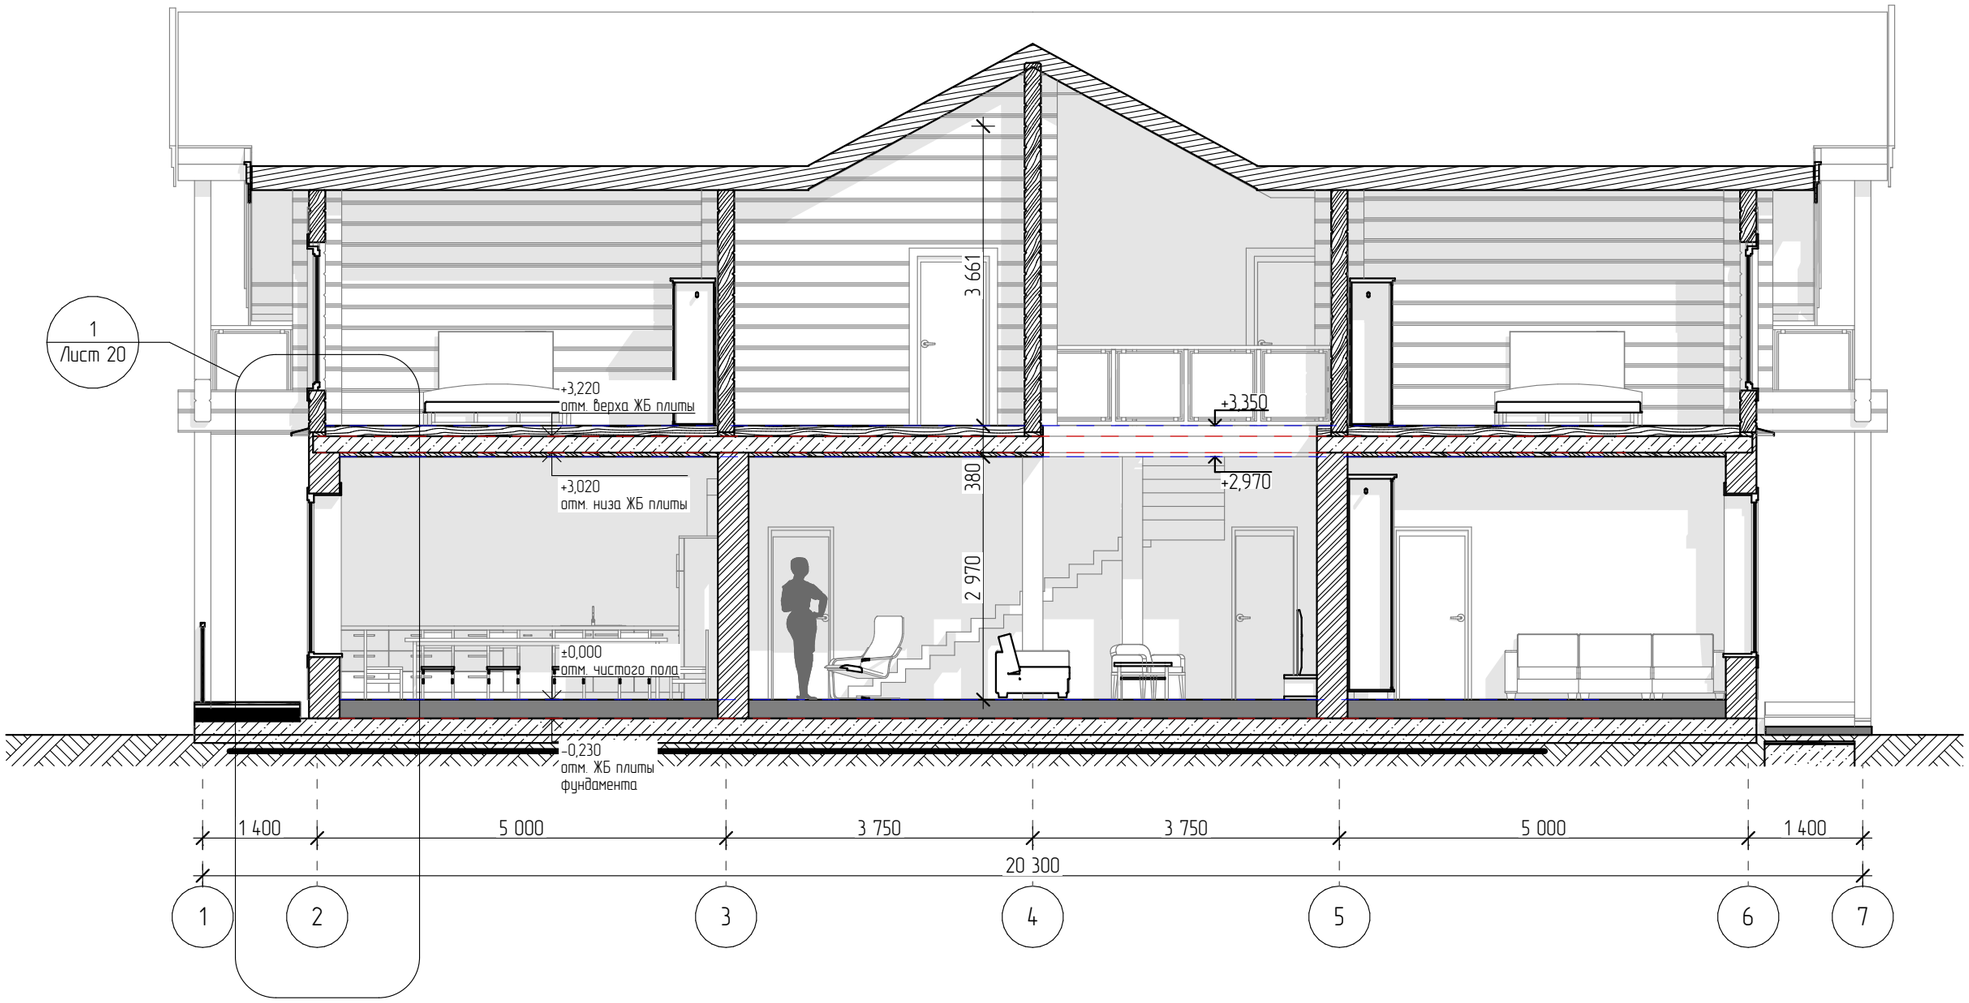

Примечание:

1) За отметку +0,000 принята отметка чистового пола первого этажа
2) За отметку +3,350 принята отметка чистового пола второго этажа
3) Номинальные высотные размеры могут отличаться от фактических в силу технологической усадки стенового комплекта и принимаемых отделочных материалов.
4) Высота фундамента дана без учета перепада. Замер перепада производится на участке при выезде инженера. Изменение габаритов и типа фундаментов согласовывается дополнительным согласованием по смете.
5) Все декоративные элементы показаны условно.

					2021	#ID Проекта			
						Адрес: #Полный Адрес Участка; к/н: #ID Участка			
Изм.	Кол.уч	Лист	№док.	Подпись	Дата				
						Индивидуальный жилой дом	стадия	лист	листов
Архитектор		Салыкова В.Г.					ЭП	5	
Заказчик		#Обращение к Заказчику				Разрез 1-1 М 1:75			

Согласовано:


Взам. инв. №

Подпись и дата

Инв. № подл.

М 1:75

Разрез 2-2

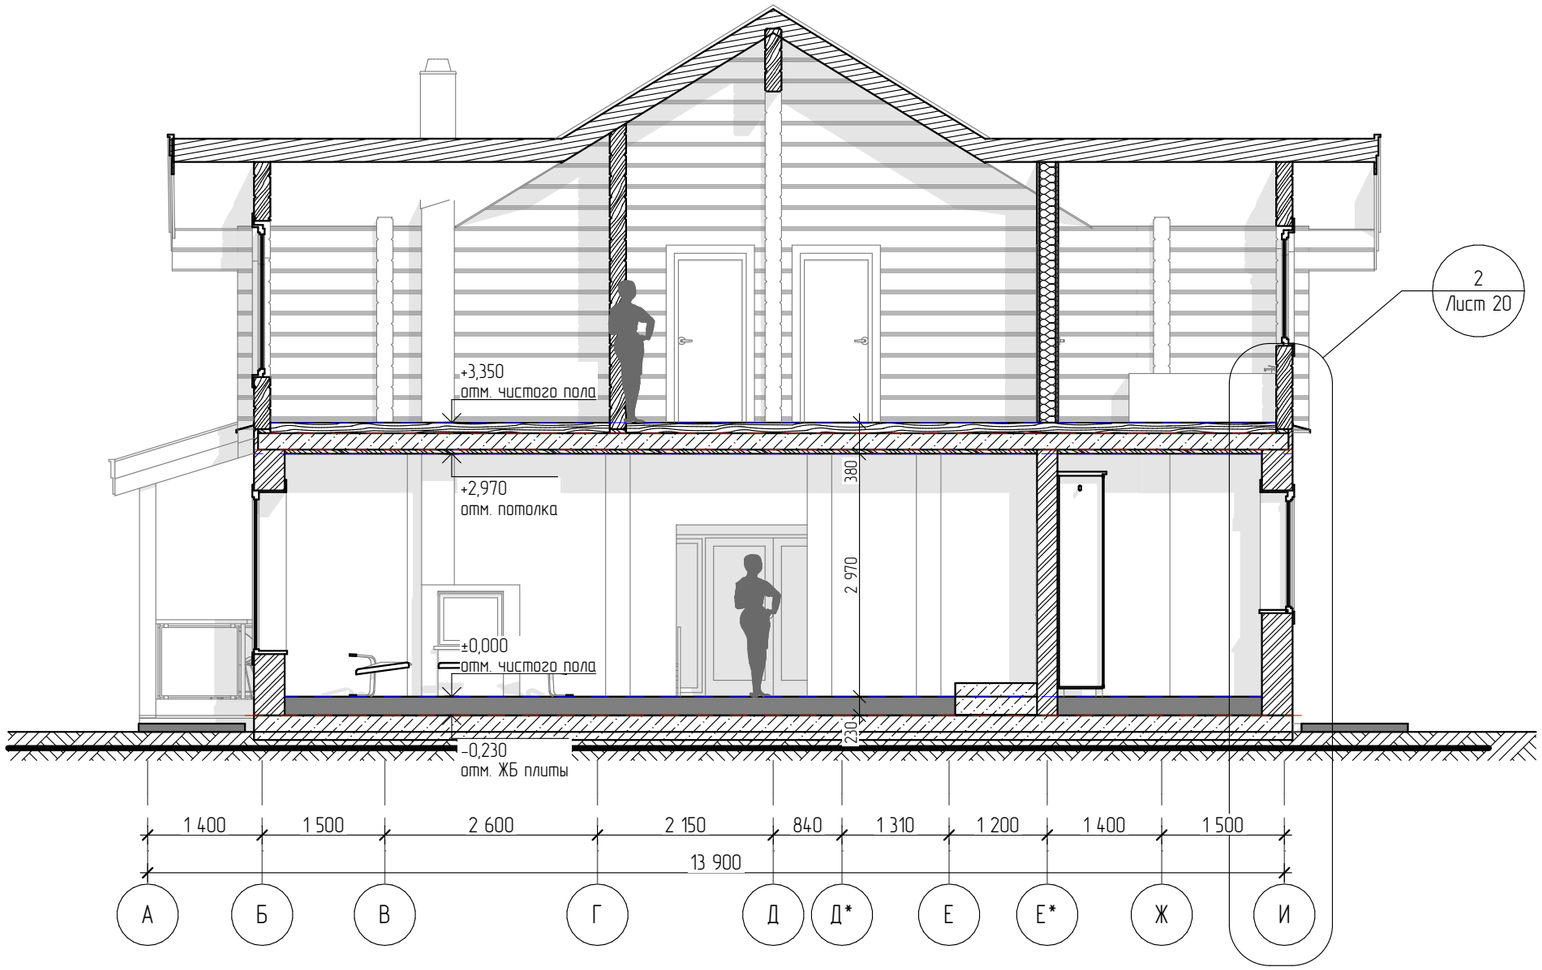

Примечание:

1) За отметку +0,000 принята отметка чистового пола первого этажа
2) За отметку +3,350 принята отметка чистового пола второго этажа
3) Номинальные высотные размеры могут отличаться от фактических в силу технологической усадки стенового комплекта и принимаемых отделочных материалов.
4) Высота фундамента дана без учета перепада. Замер перепада производится на участке при выезде инженера. Изменение габаритов и типа фундаментов согласовывается дополнительным согласованием по смете.
5) Все декоративные элементы показаны условно.

					2021	#ID Проекта			
						Адрес: #Полный Адрес Участка; к/н: #ID Участка			
Изм.	Кол.уч	Лист	№док.	Подпись	Дата				
						Индивидуальный жилой дом	стадия	лист	листов
							ЭП	6	
Архитектор		Салыкова В.Г.							
Заказчик		#Обращение к Заказчику				Разрез 2-2 М 1:75			

Согласовано:

Взам. инв. №

Подпись и дата

Инв. № подл.

Общий вид 1



Общий вид 2



Общий вид 3



Общий вид 4



Общие виды

Лист 7

Согласовано

Взам. инв. №

Подпись и дата

Инв. № подл.

Общий вид 1 этаж



Общий вид 1 этаж



Общий вид 2 этаж



Общий вид 2 этаж



Согласовано

Взам. инв. №

Подпись и дата

Инв. № подл.


Общие виды (поэтажные)

Лист

8

М 1:100

План раскладки стропил 1 уровень

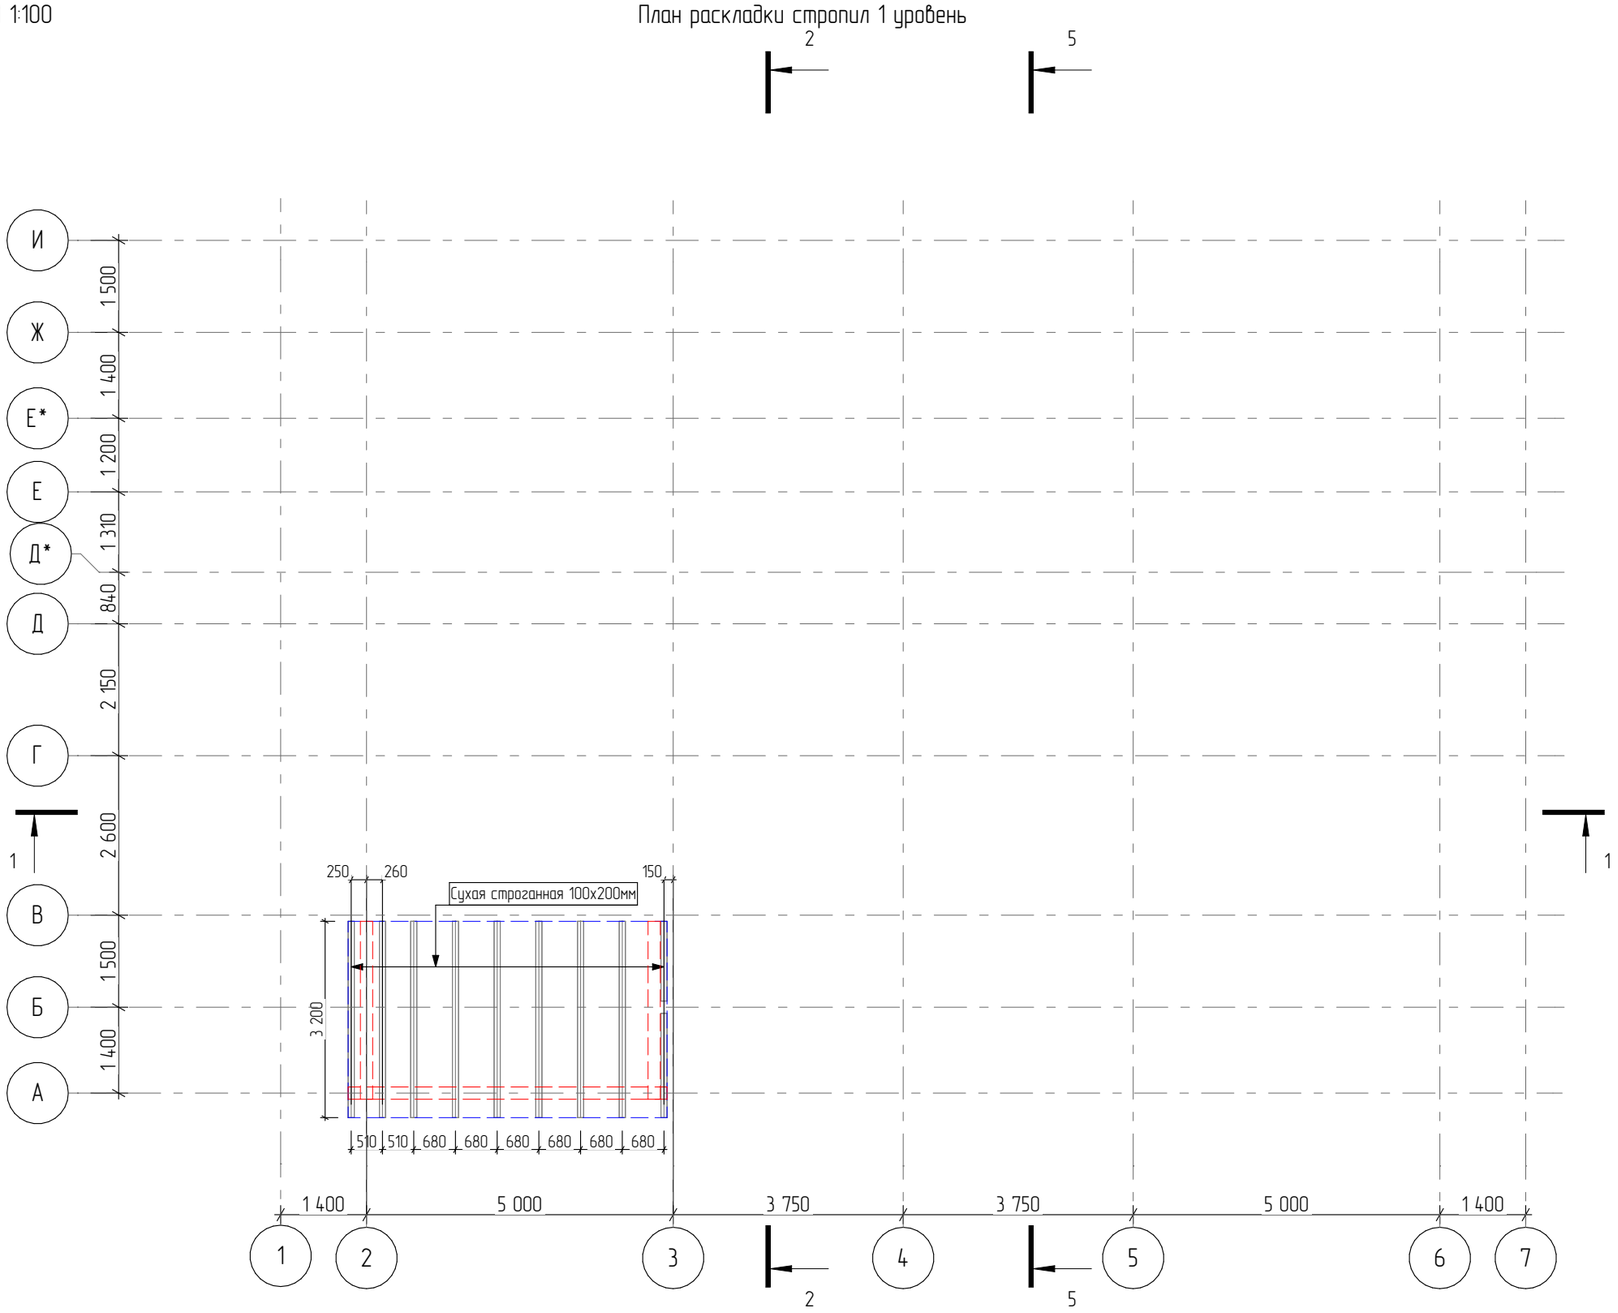

Согласовано

Взам. инв. №

Подпись и дата


Инв. № подл

Стропила 1 уровень

Лист

М 1:100

План раскладки стропил 2 уровень

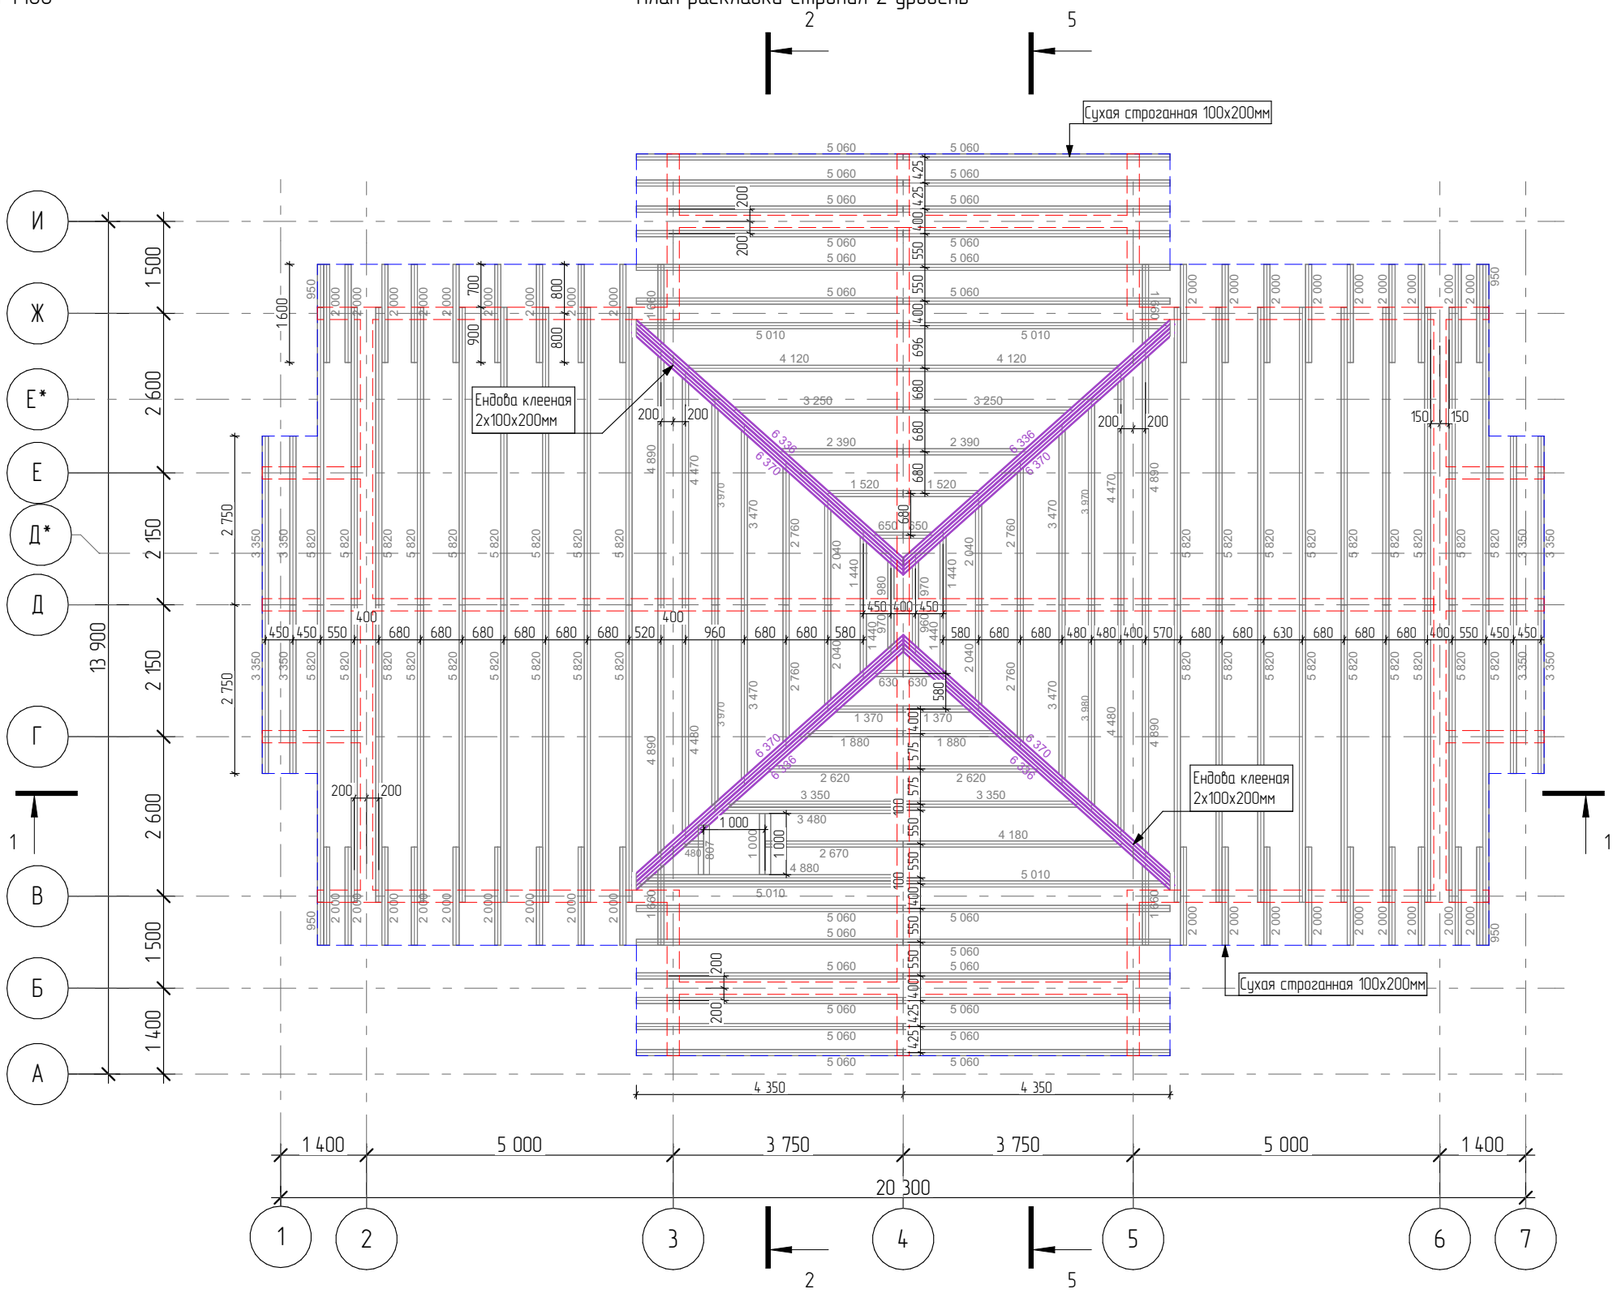

Согласовано:

Взам. инв. №

Подпись и дата

Инв. № подл.

					2021	#ID Проекта			
						Адрес: #Полный Адрес Участка			
Изм.	Кол.уч	Лист	№док.	Подпись	Дата				
						Индивидуальный жилой дом	стадия	лист	листов
							РП		
Архитектор		Салыкова В.Г.							
Заказчик		#Обращение к Заказчику				Стропила 2 уровень			

Общий вид КД - 1



Согласовано

Взам инв. №

Подпись и дата

Инв. № подл.

Общие виды

Лист

2



Вид 2


Общие виды

Лист 3

Инв. № подл.	Подпись и дата	Взам. инв. №

Лист 4

Общие виды

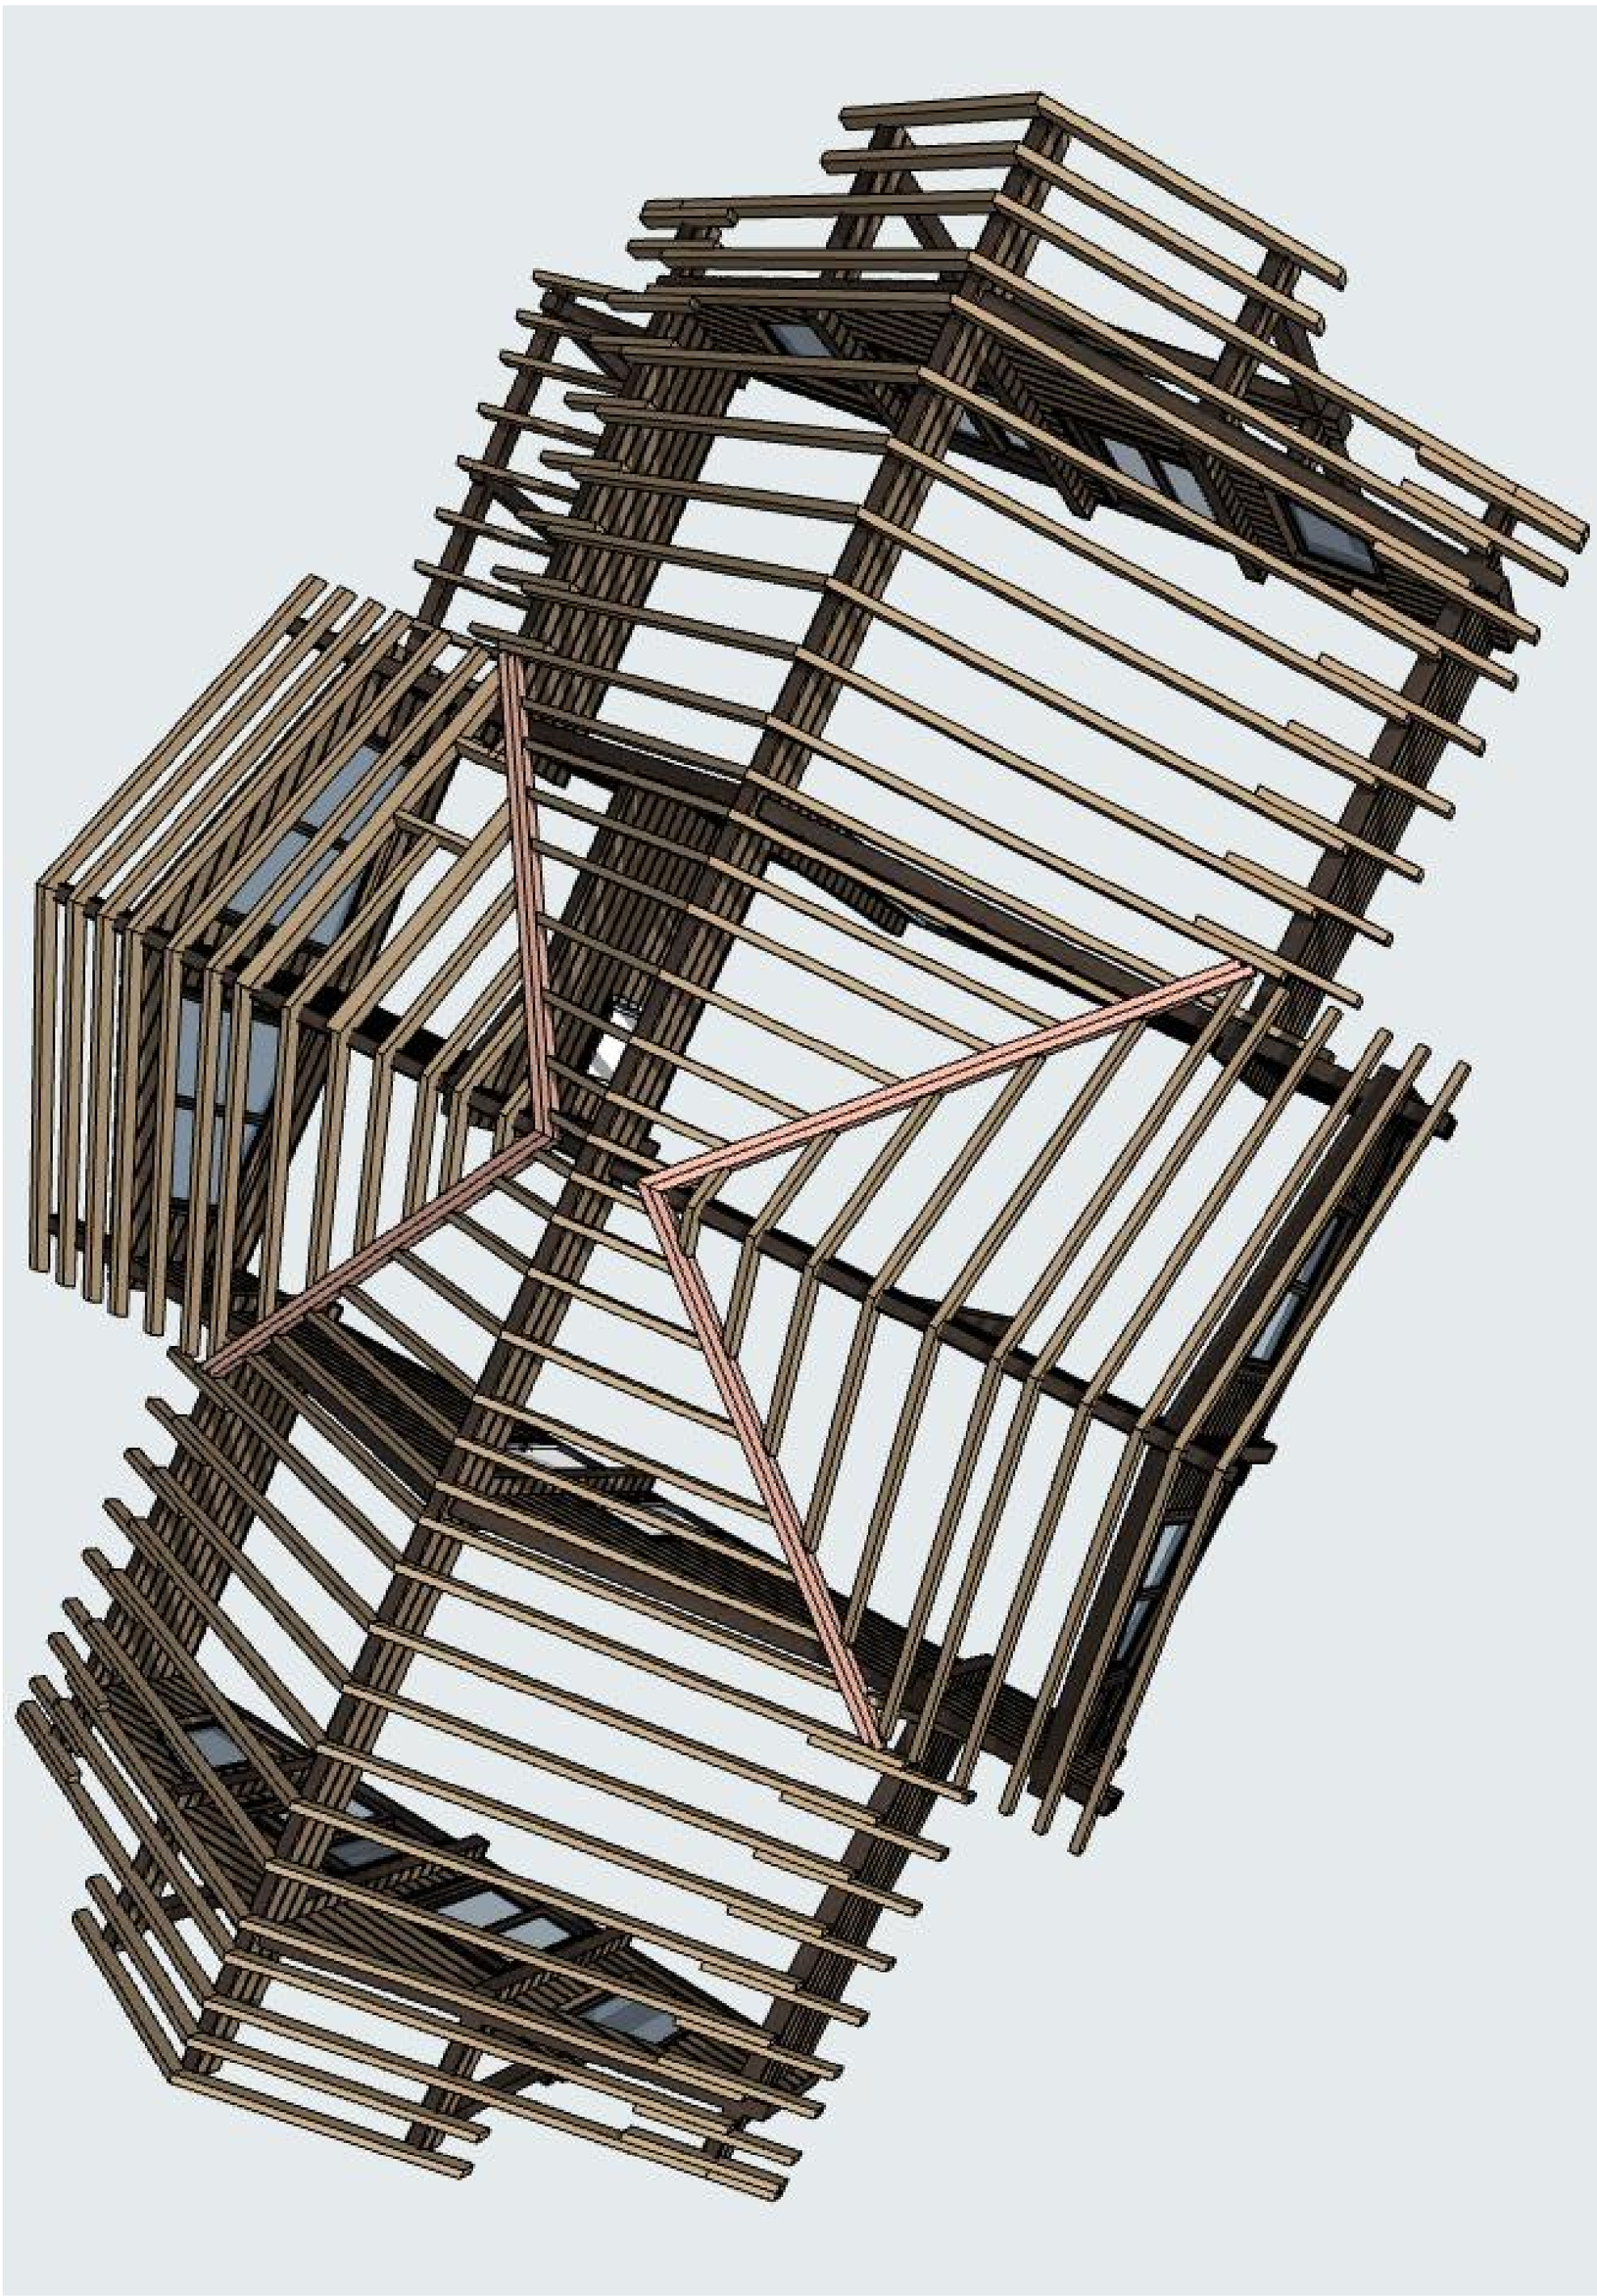

Вид 3

Согласовано							

Инв. № подл.	Подпись и дата	Взам. инв. №


Вид 4



Общие виды

М 1:100

Схема штробления под электрику 2 этаж

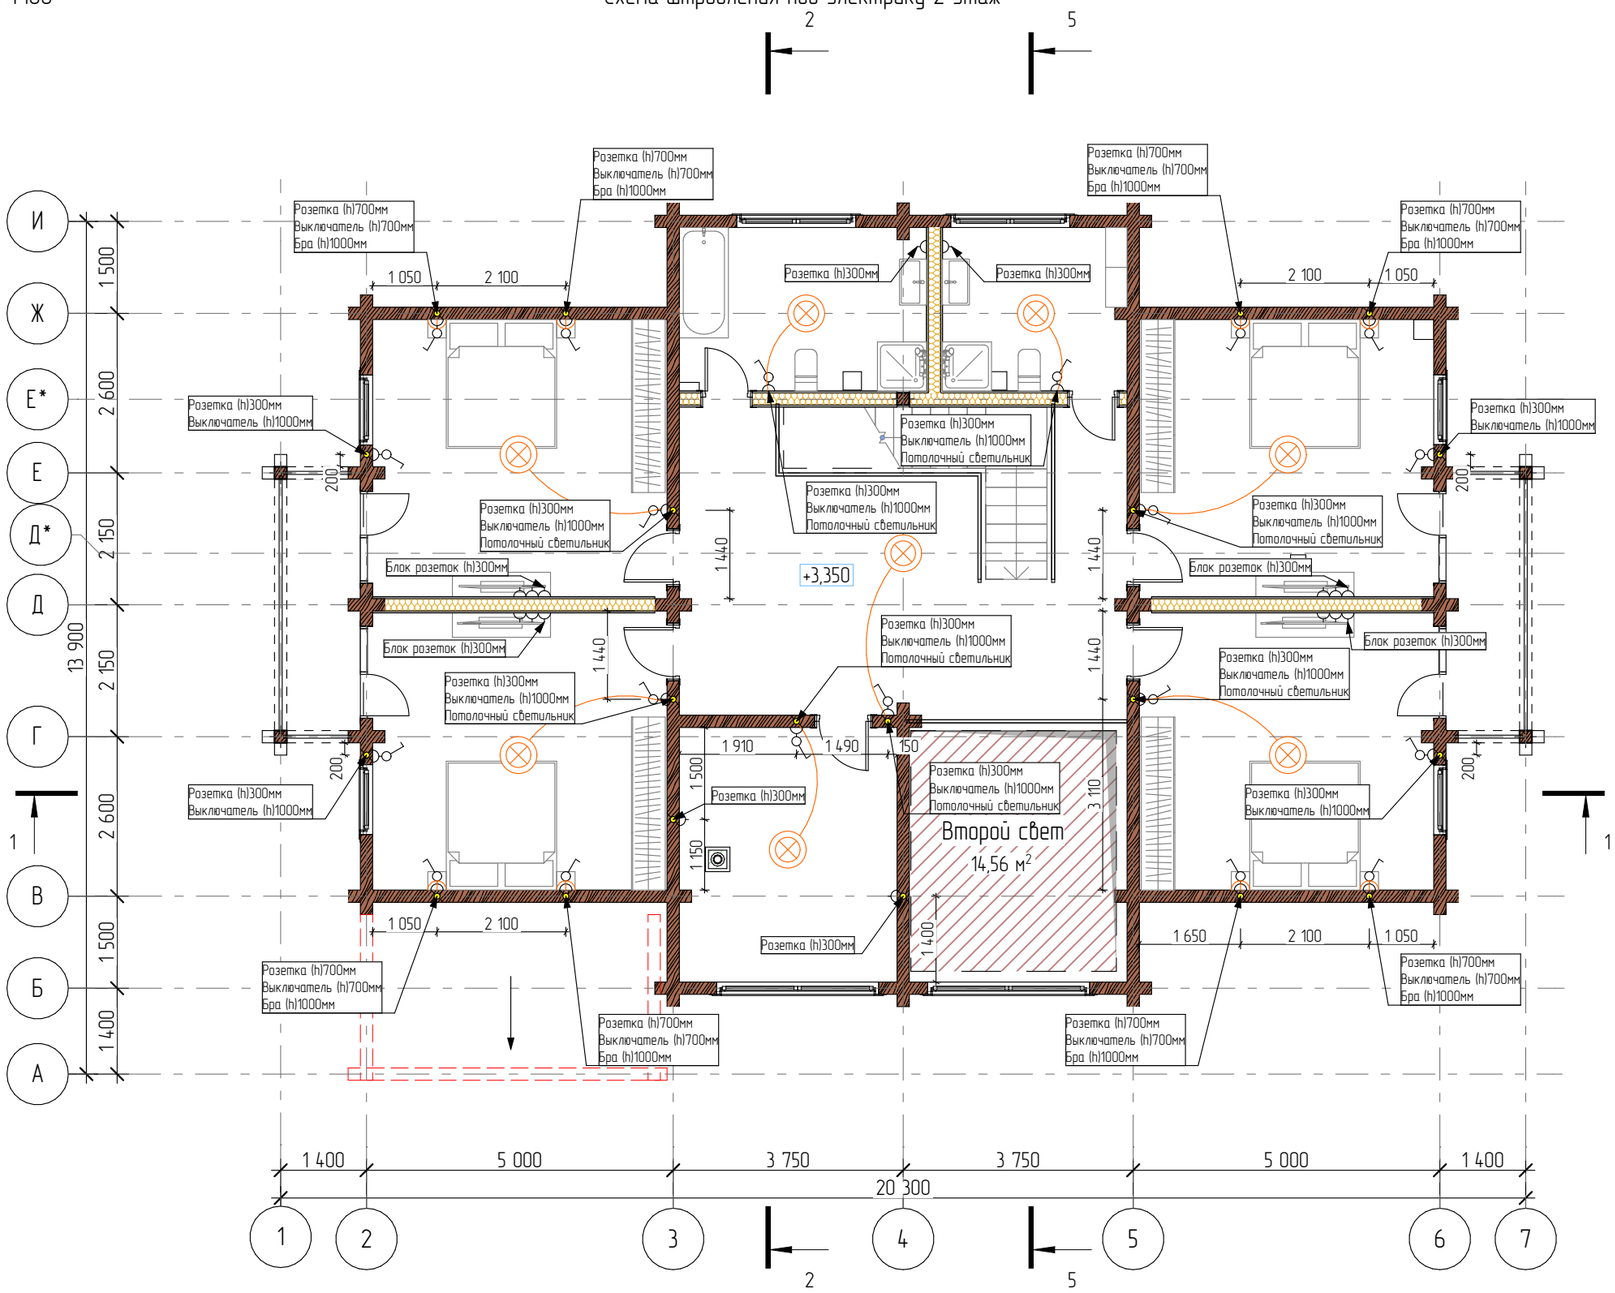

Условные обозначения:	
	Электрическая розетка
	Выключатель одноклавишный
	Подвесной/встраиваемый светильник потолочный
	Бра
1000	Размеры в мм
h=100мм	Размеры в мм от чистого пола

Согласовано:

Взам. инв. №

Подпись и дата

Инв. № подл.

						2021	ДСП № 14.09.2021-КБ
							Адрес: Ленинградская область, Гатчинский муниципальный район, Вырицкое городское поселение, г. п. Вырица, ул. Елизаветинская
Изм.	Кол.уч	Лист	№док.	Подпись	Дата		
							Индивидуальный жилой дом
Архитектор		Салыкова В.Г.					
Заказчик		Кондрашов Д.В.					Схема штробления под электрику

стадия	лист	листов
РП	.2	

АПС ДСК™ ДОМОСТРОИТЕЛЬНЫЙ КОМБИНАТ