

М 1:100

Кладочный план 1 этаж



17 700
1 275
1 800
1 550
1 800
1 275
ОК-4
ОК-4
5 000
1 500
900
1 200
200
900
5 000
2 500
3 900
150
2 900
2 870
1 870
250
Д-2
Д-2
ОК-3
4 625
250
780
4 890
250
250
780
ОК-5
3 510
2 475
150
2 000
К-2
К-1
К-2
К-1
К-2
575
960
330
Д-1
ДН-1П
950
940
660
630
940
2 550
Д-1
П/П
П/П
940
940
670
600
2 300
Д-1
ДН-1
ДН-2
К-2
К-2
К-1
К-2
565
3 120
4 625
ОК-3
3 350
250
3 350
ОК-5
ОК-2
ОК-2
6 950
1 125
3 140
735
735
3 140
1 125
435
435
ОК-1
ОК-1
810
2 640
800
2 640
810
5 000
7 700
5 000
1 400
5 000
3 750
3 750
5 000
1 400
20 300
13 900
12 700
8 950
9 200
9 700
2 600
2 150
2 600
1 500
1 400
1 500
1 500
1 500


М 1:150

Кладочный план_диагонали

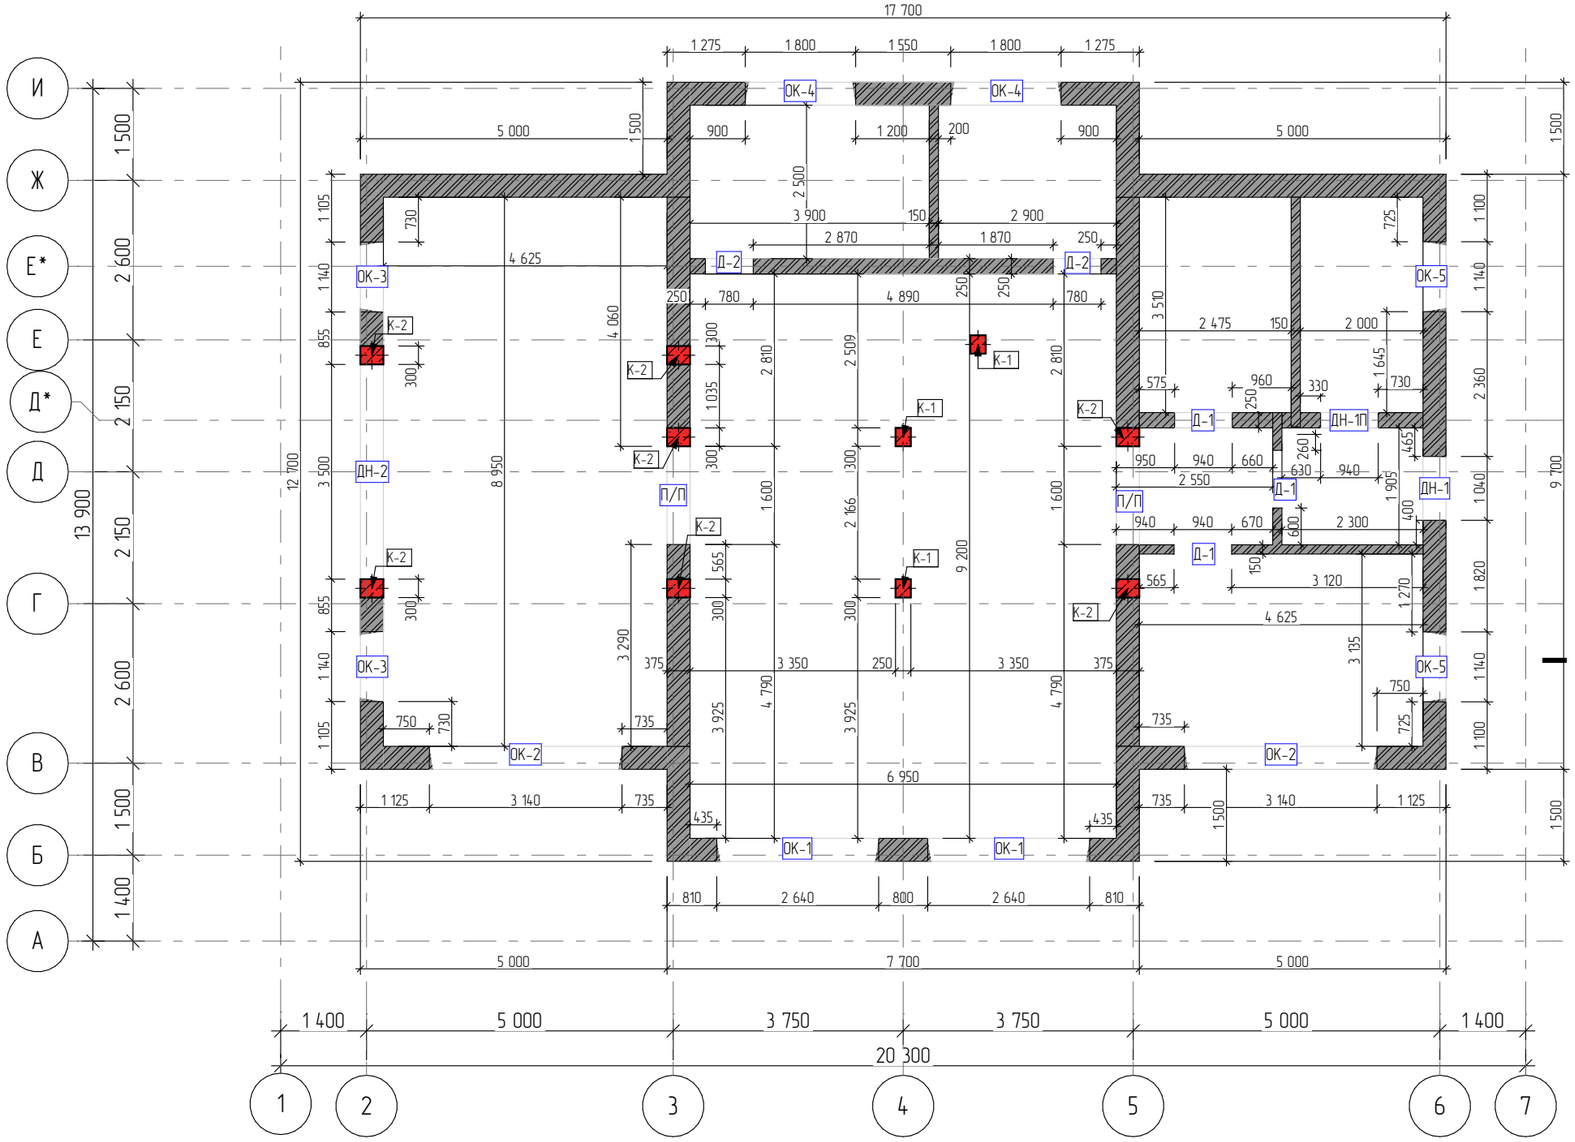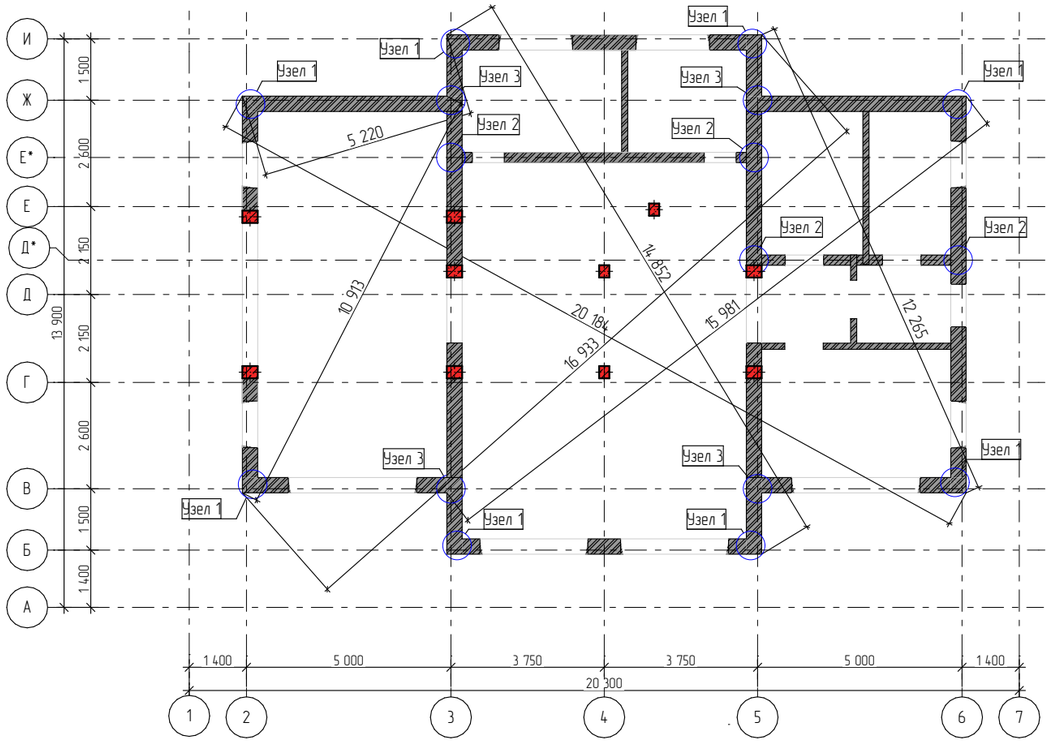



Узел 1

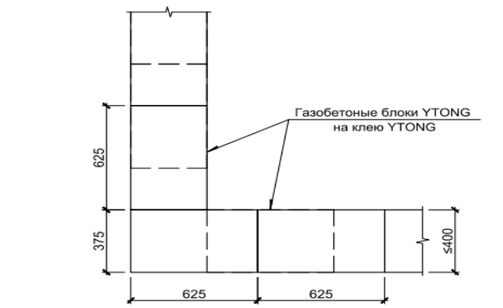

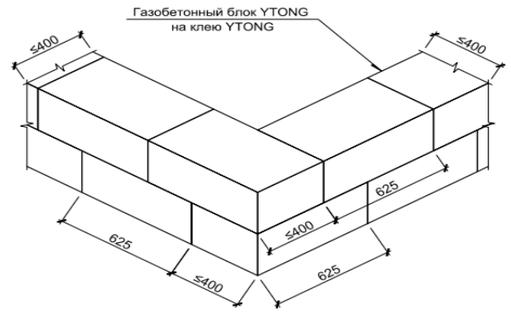


Узел 2

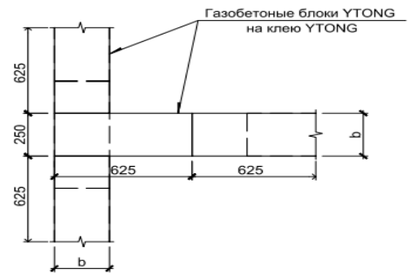

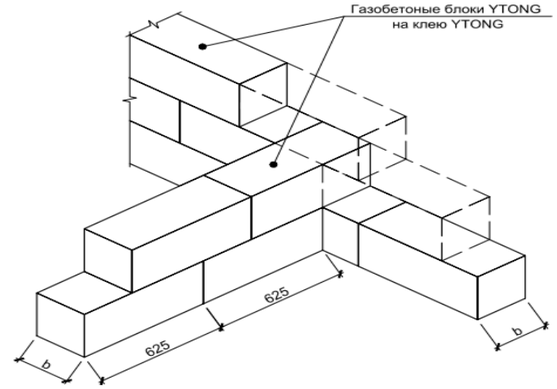


Узел 3

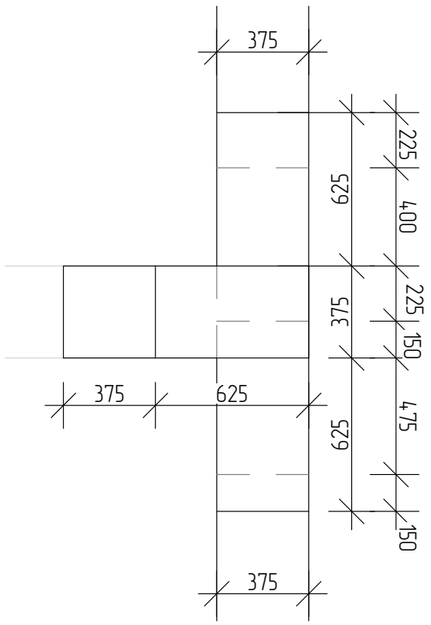


М 1:100

Кладка (вид1)

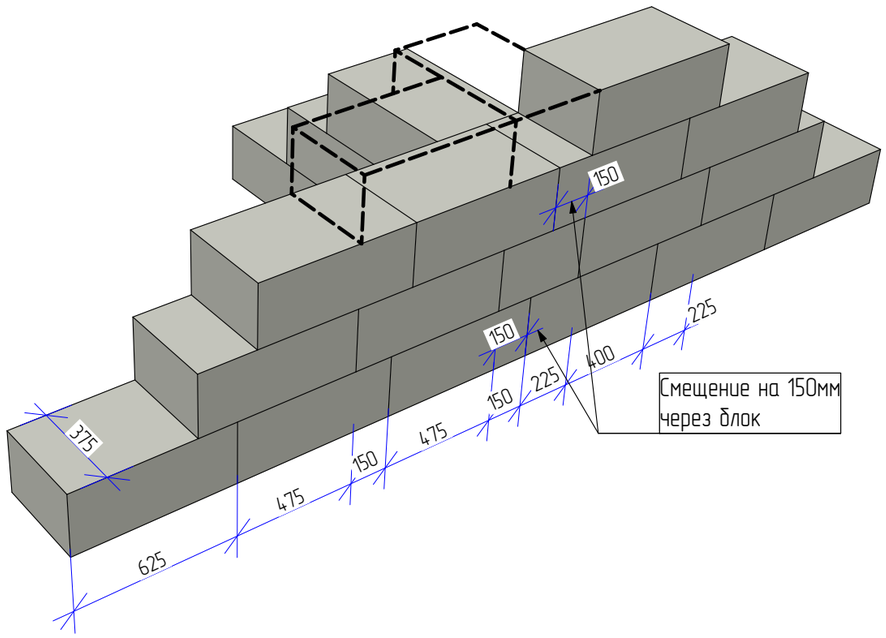

М 1:100

Кладка (вид2)

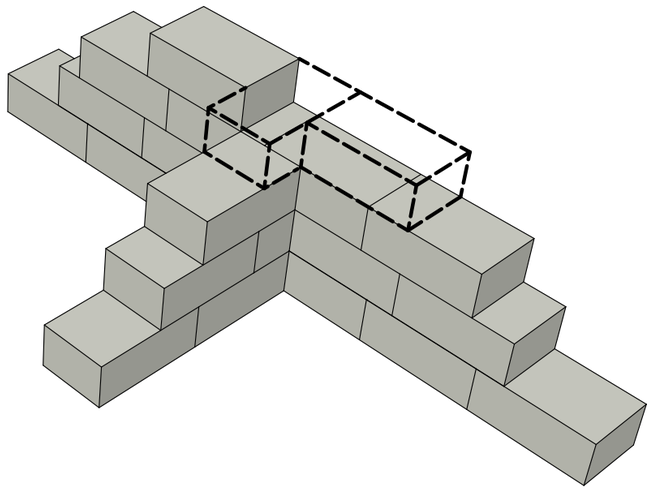

Согласовано

Взам инв. №

Подпись и дата

Инв. № подл


Кладочный план_диагонали

Лист

2


М 1:100

ЖБ плита межэтажная

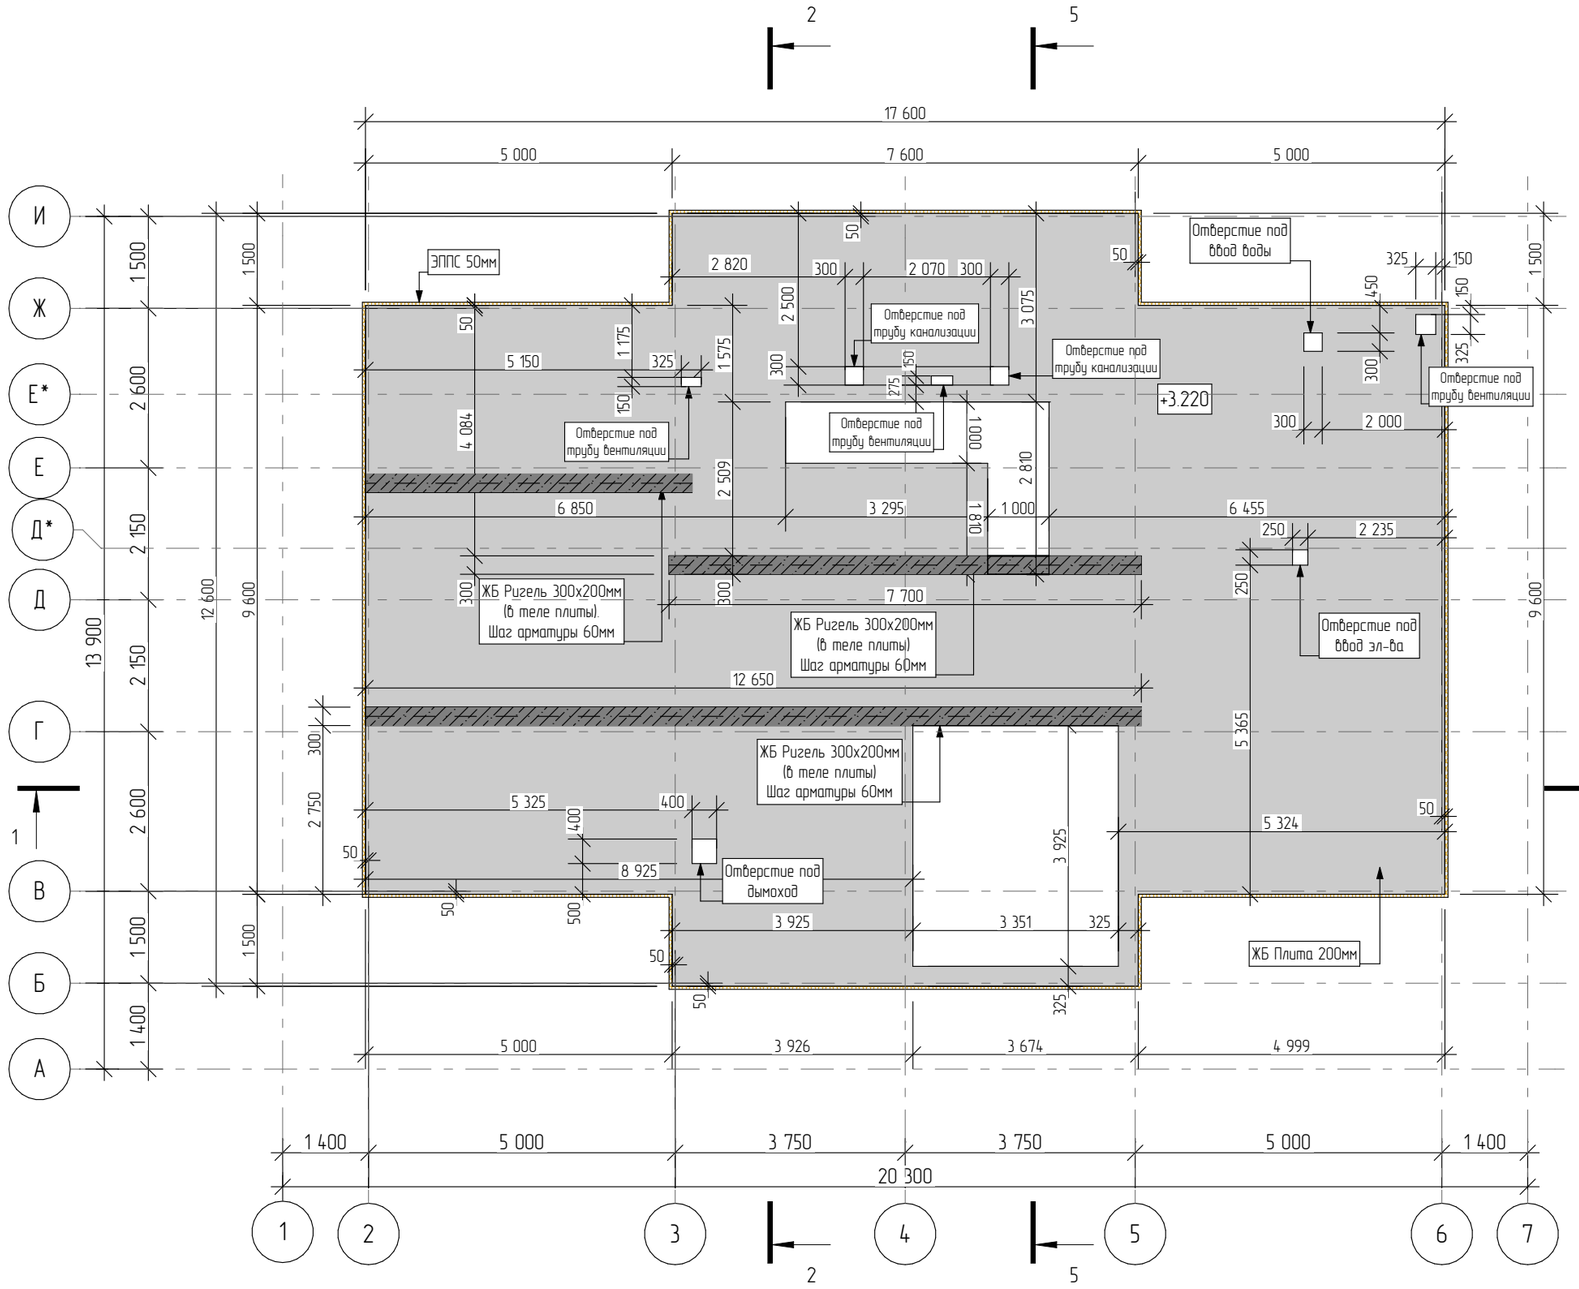

ЖБ Ригель 300х200мм (в теле плиты)

М 1:10

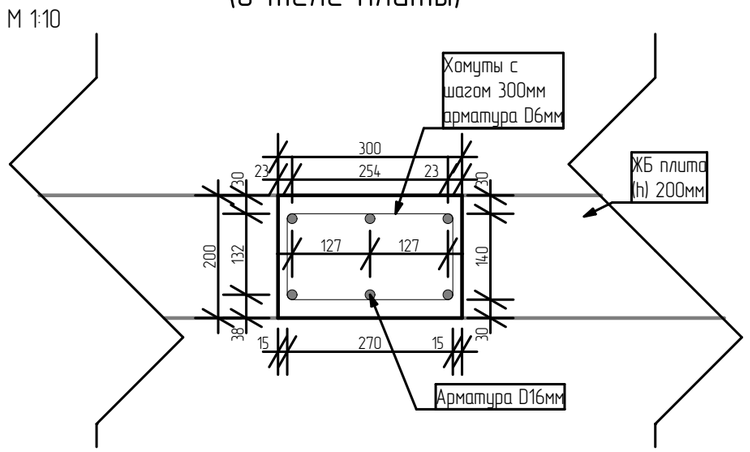

Согласовано:

Взам. инв. №

Подпись и дата

Инв. № подл.

					2021
Изм.	Кол.уч	Лист	№док.	Подпись	Дата
Архитектор		Салыкова В.Г.			
Заказчик		#Обращение к Заказчику			


#ID Проекта

Адрес: #Полный Адрес Участка


Индивидуальный жилой дом	стадия	лист	листов
	РП	.3	
Межэтажная ЖБ плита М 1:100			

М 1:50

Стена 2

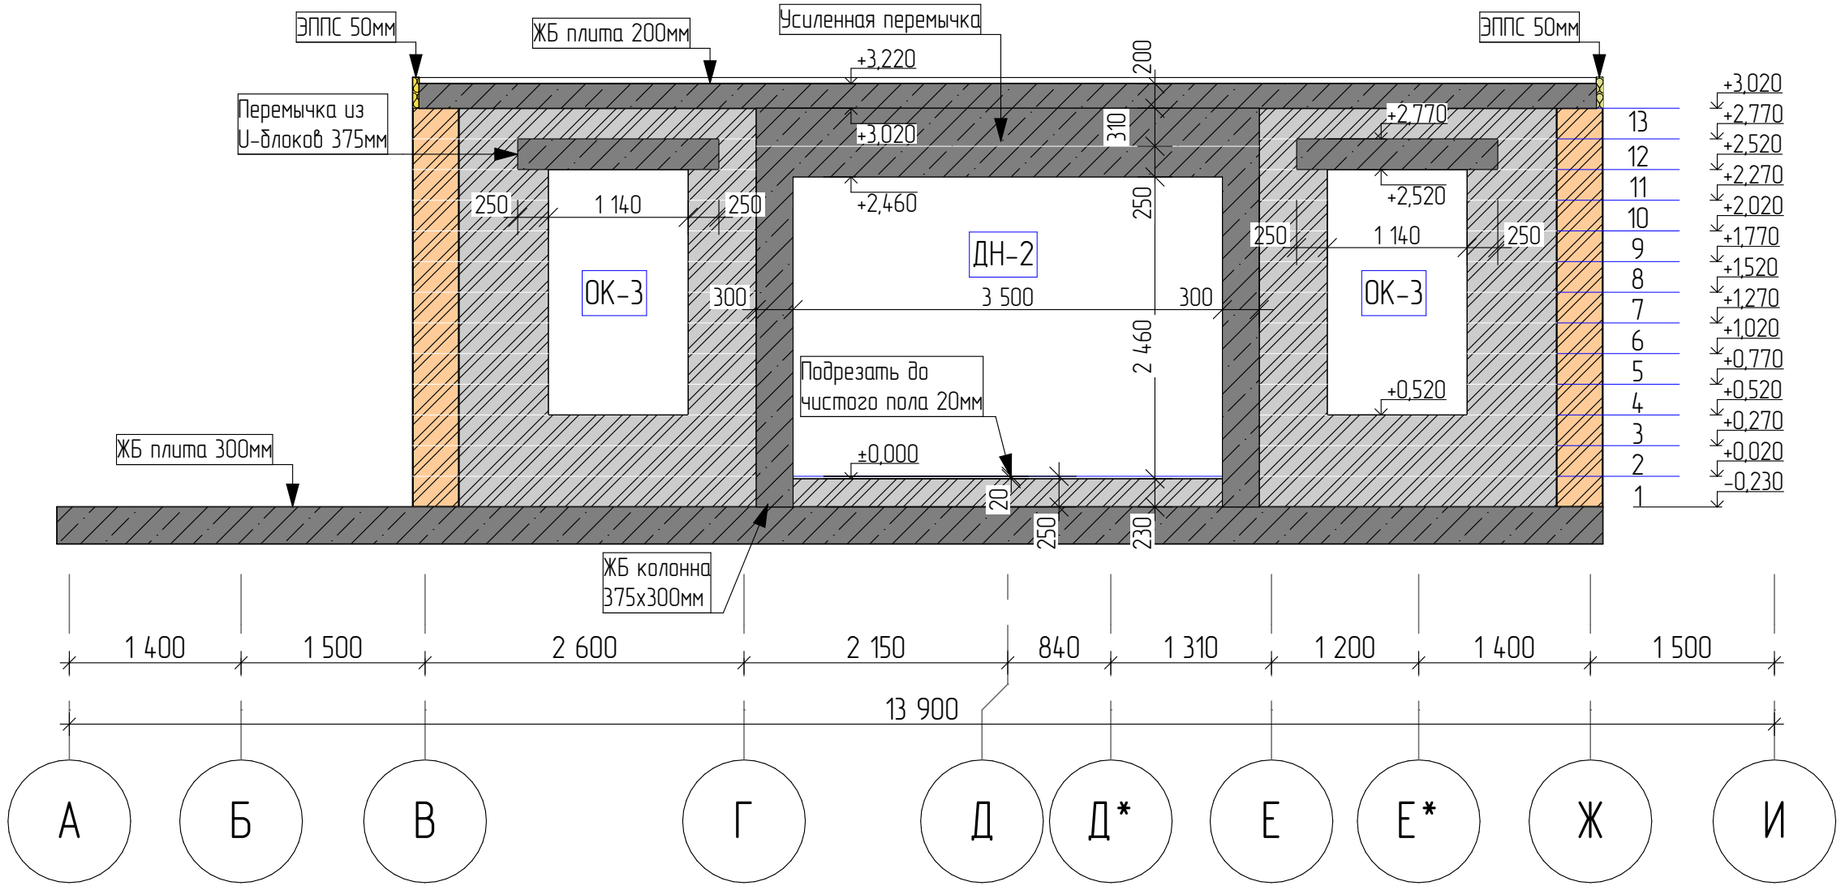

Усиленная перемычка

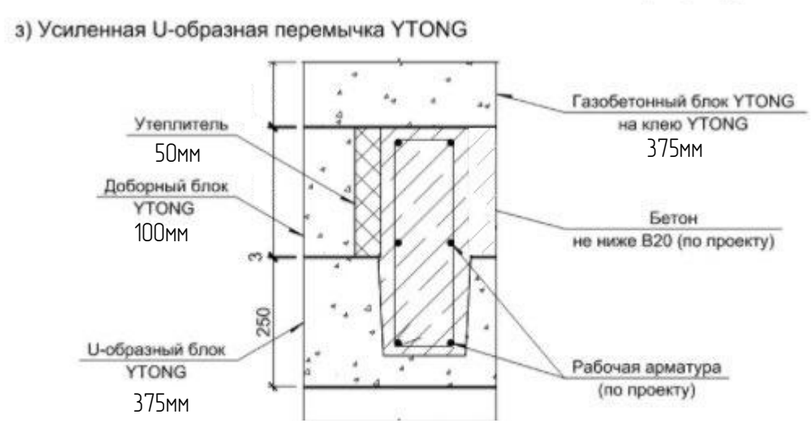

Согласовано

Взам. инв. №


Подпись и дата

Инв. № подл.


Стена 2	Лист 4

М 1:50

Стена 3

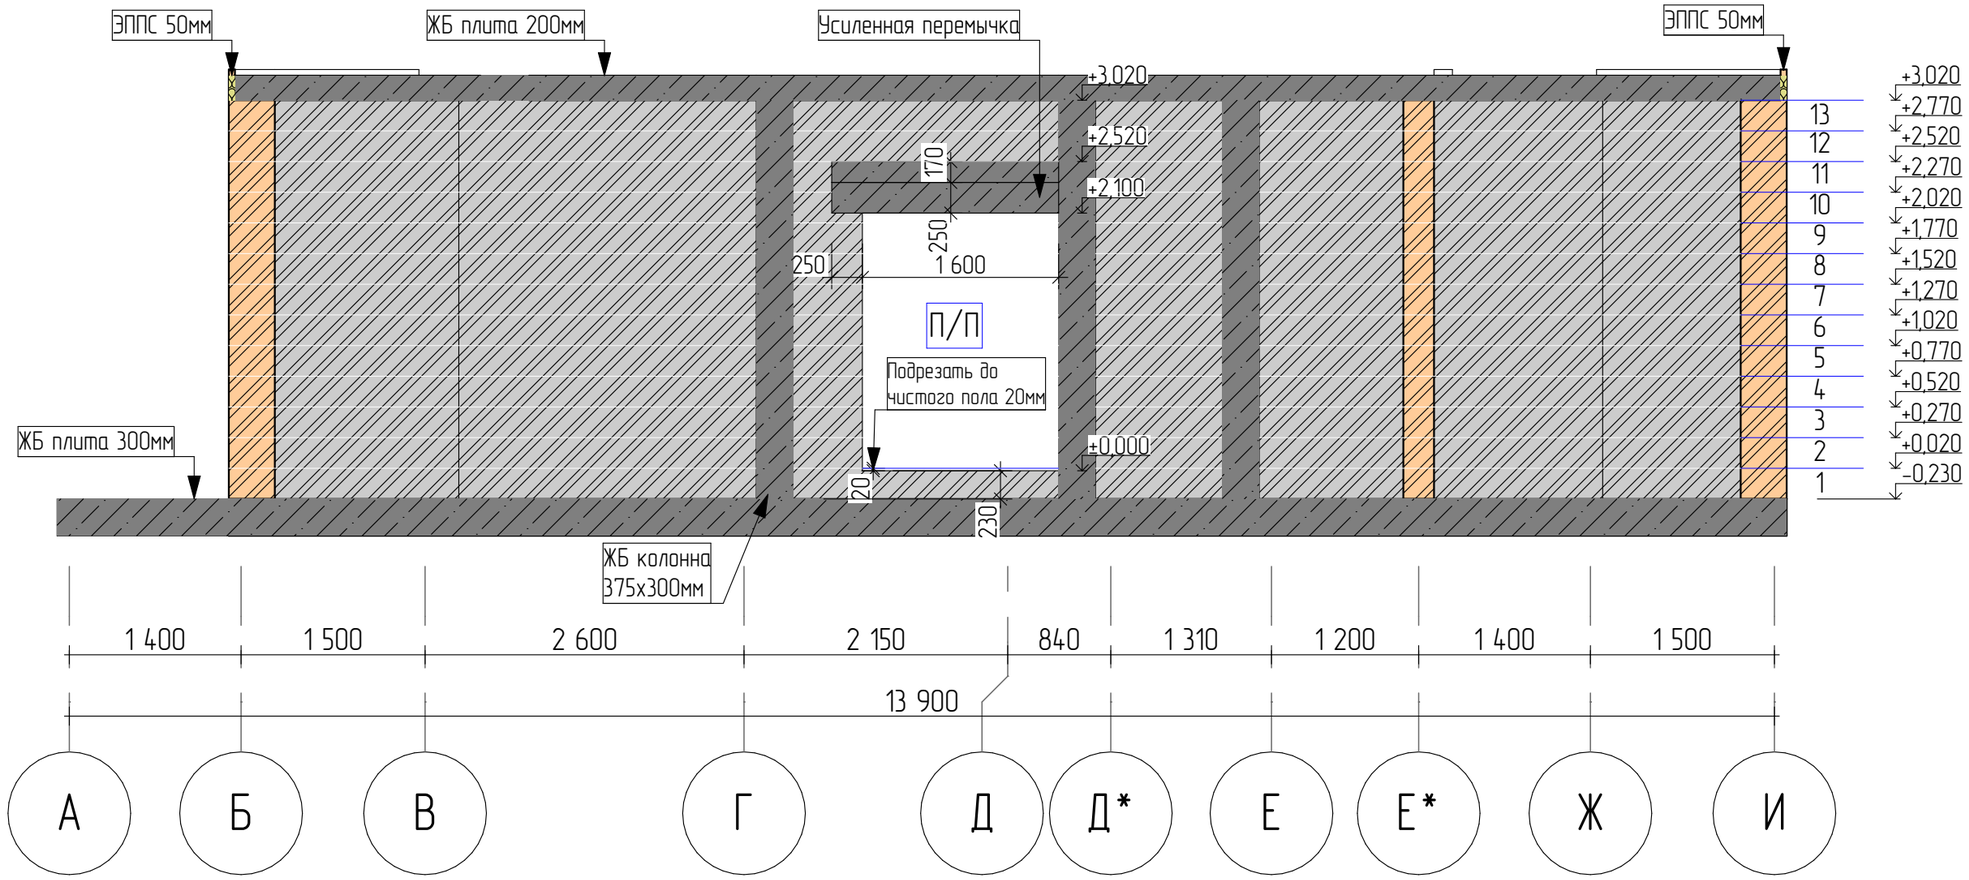

Усиленная перемычка

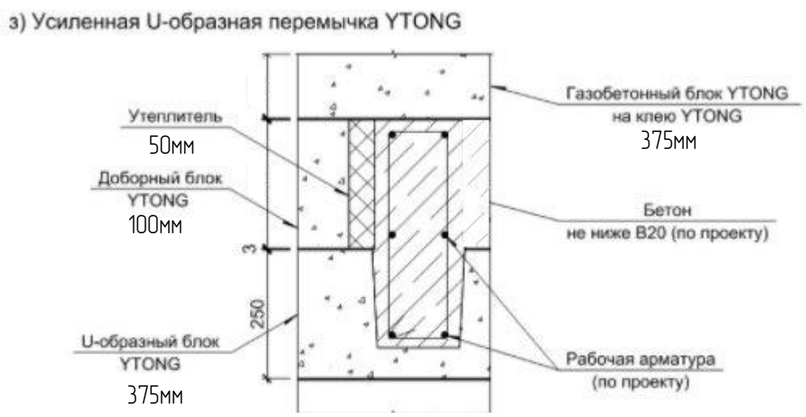

Согласовано

Взам. инв. №


Подпись и дата

Инв. № подл.

Стена 3	Лист 5


М 1:50

Стена 5

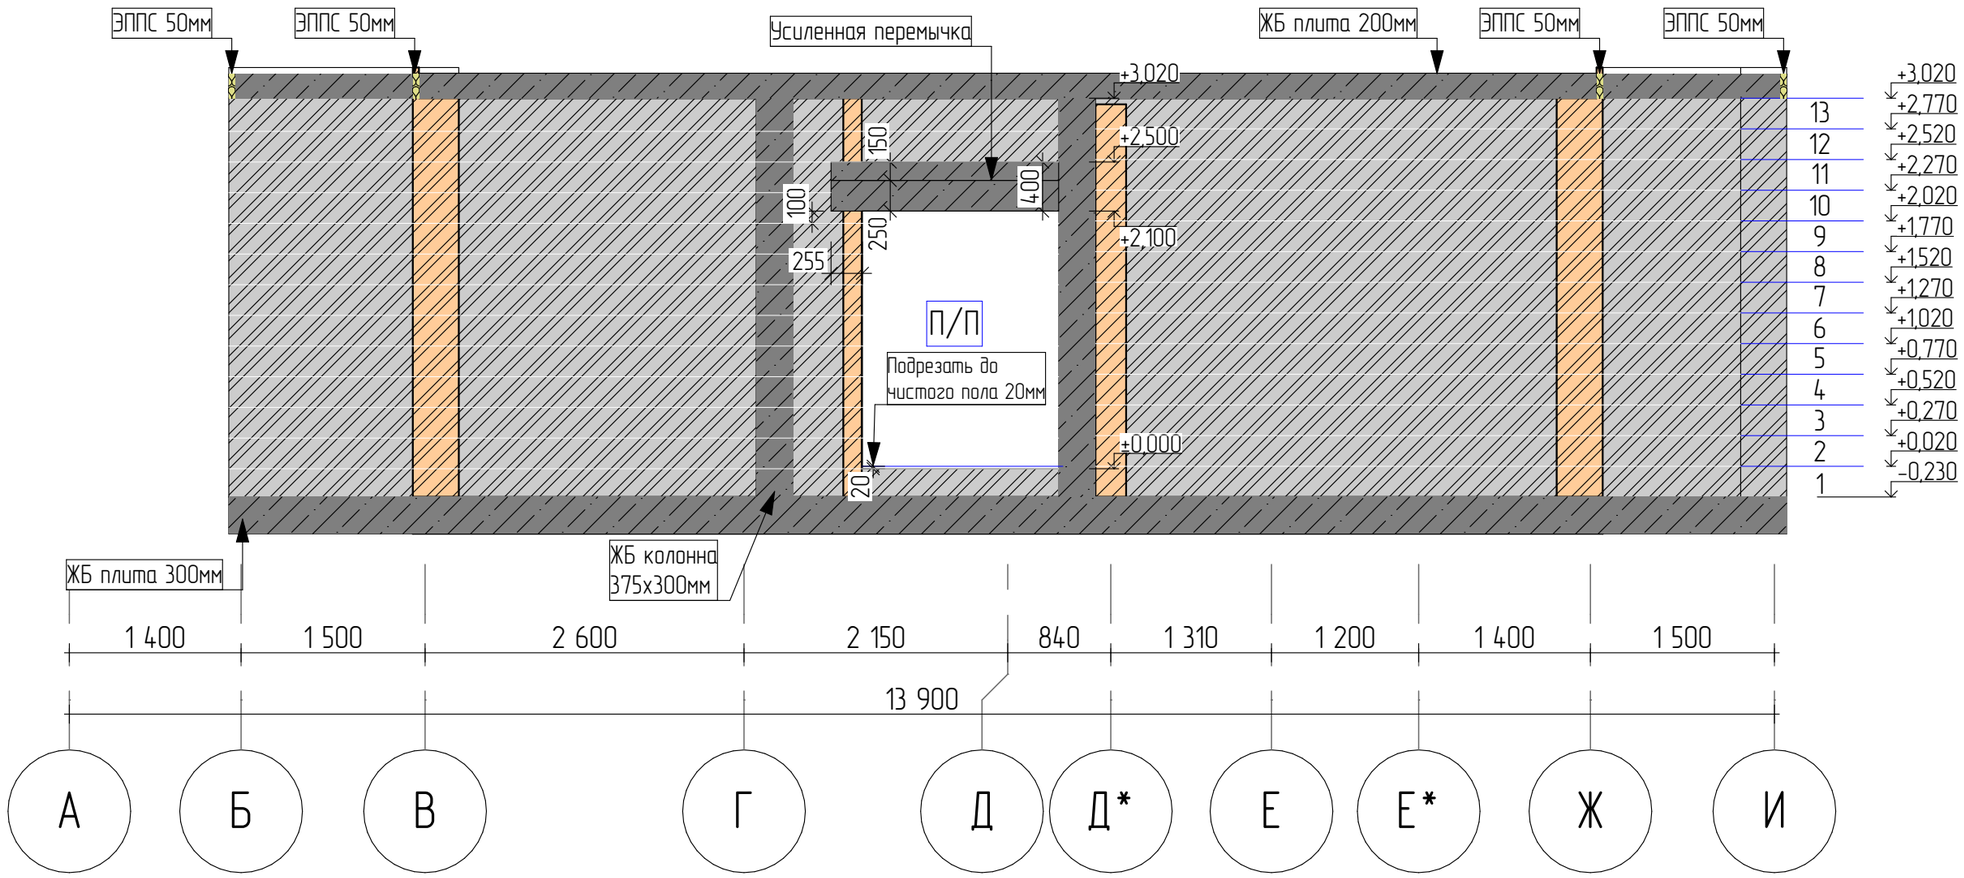

Усиленная перемычка

з) Усиленная U-образная перемычка YTONG

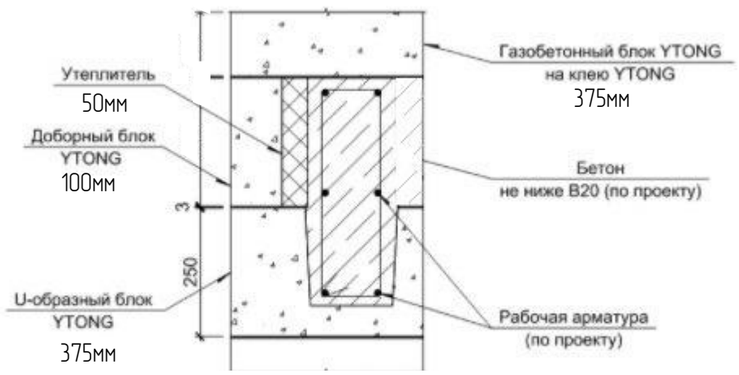

Согласовано

Взам. инв. №

Подпись и дата

Инв. № подл.


Стена 5


Лист

6

М 1:50

Стена 6

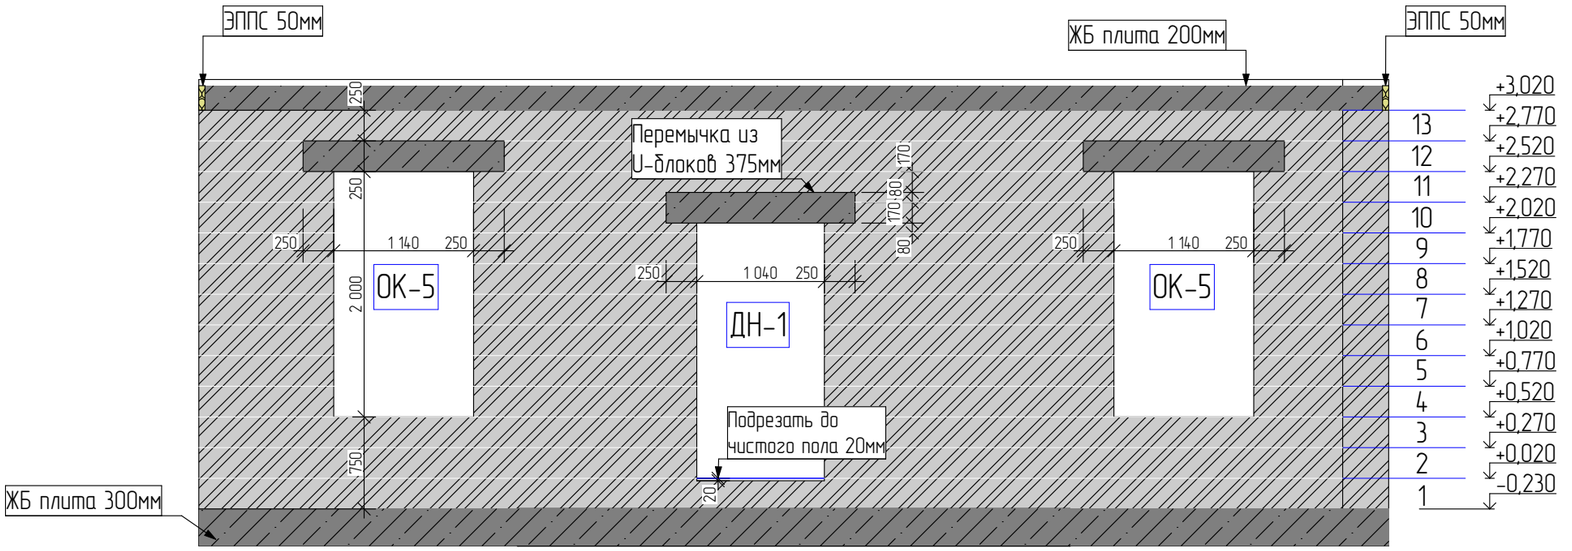

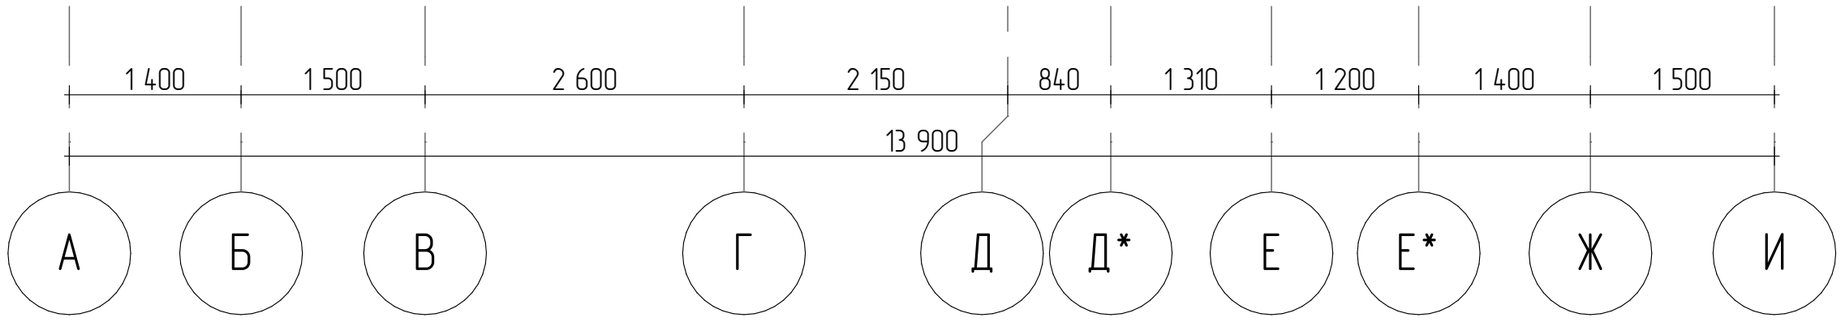

Согласовано


Взам. инв. №

Подпись и дата


Инв. № подл.

М 1:75

Стена Б

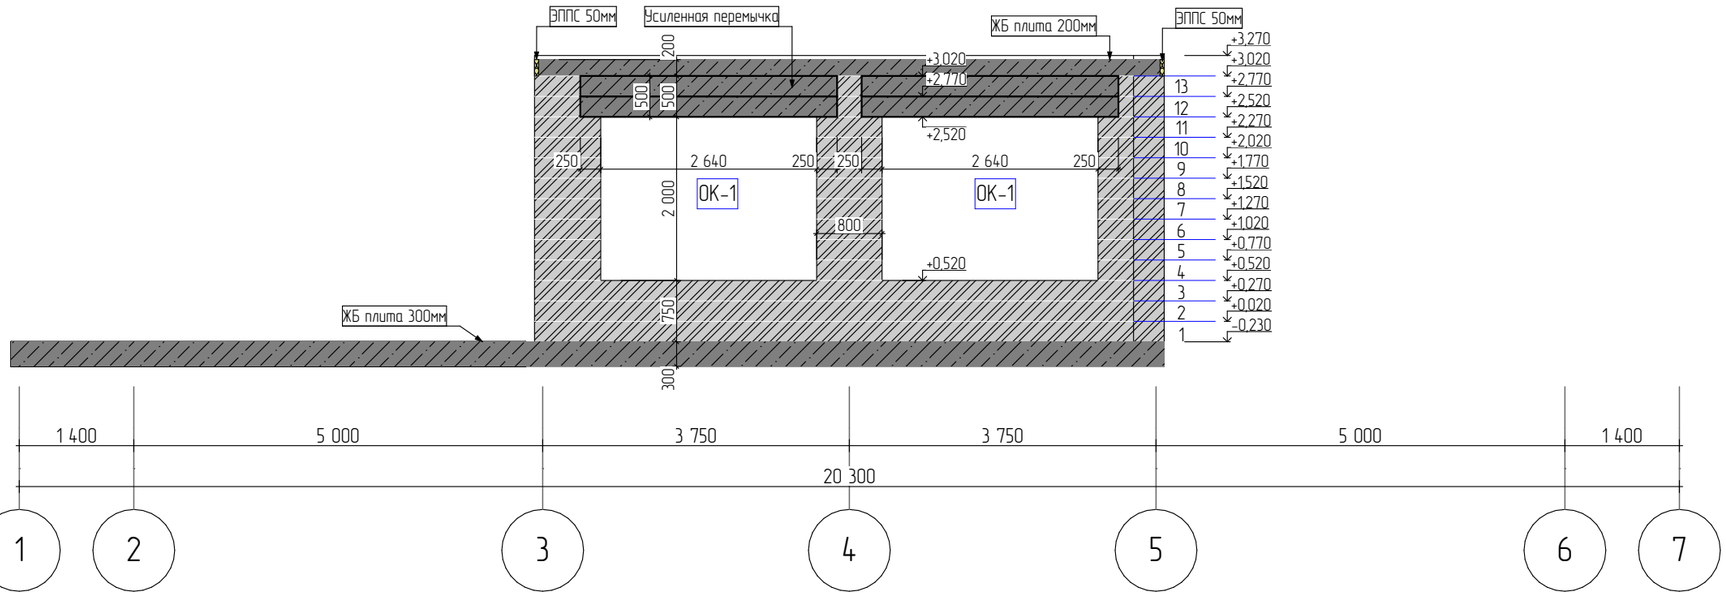

Усиленная перемычка

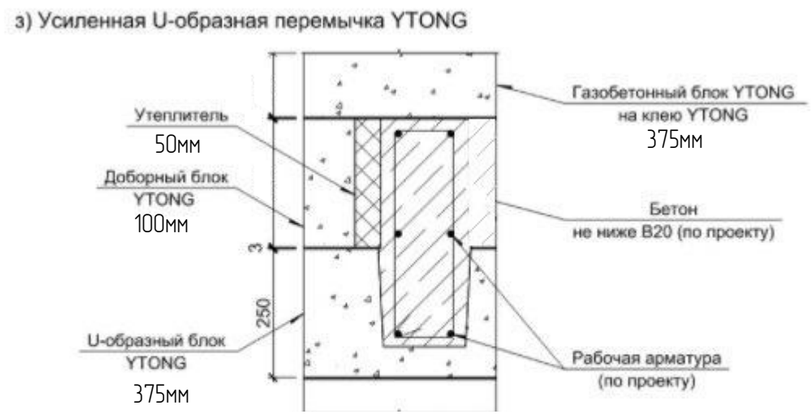

Согласовано

Взам. инв. №


Подпись и дата

Инв. № подл.


Стена Б	Лист 8

М 1:75

Стена В

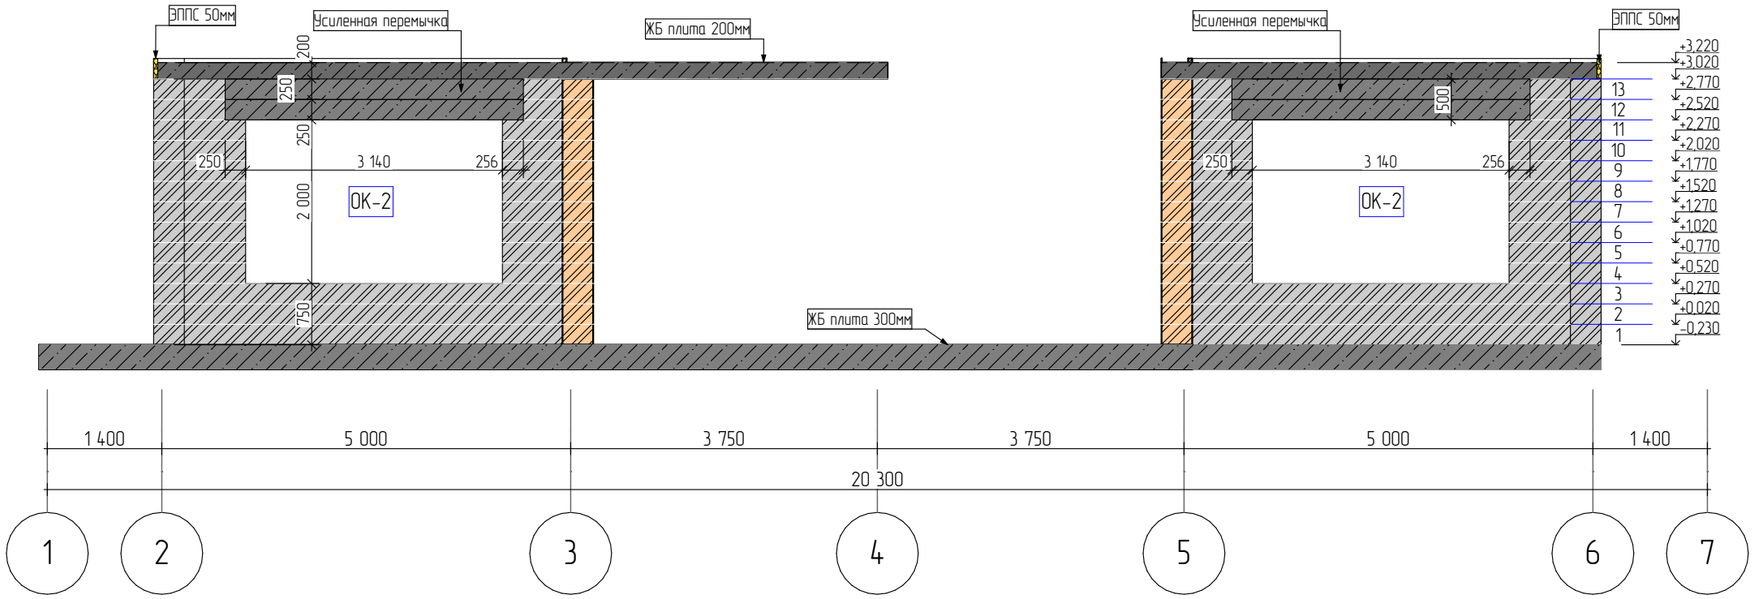

Усиленная перемычка

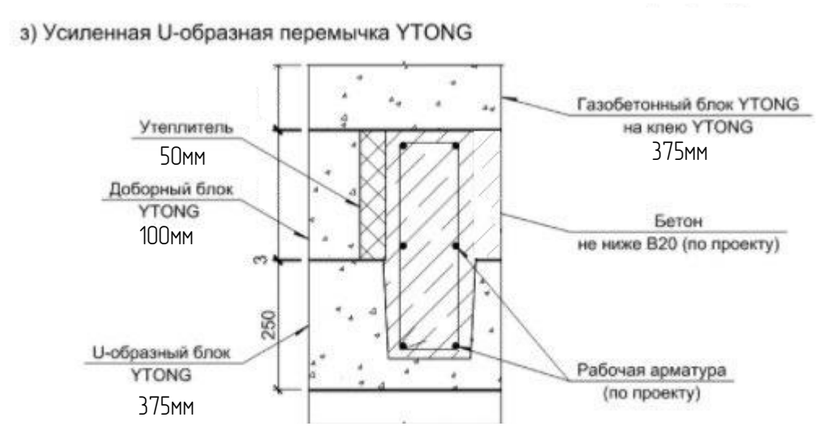

Согласовано

Взам. инв. №


Подпись и дата

Инв. № подл.

Стена В	Лист 9

М 1:75

Стена Д*

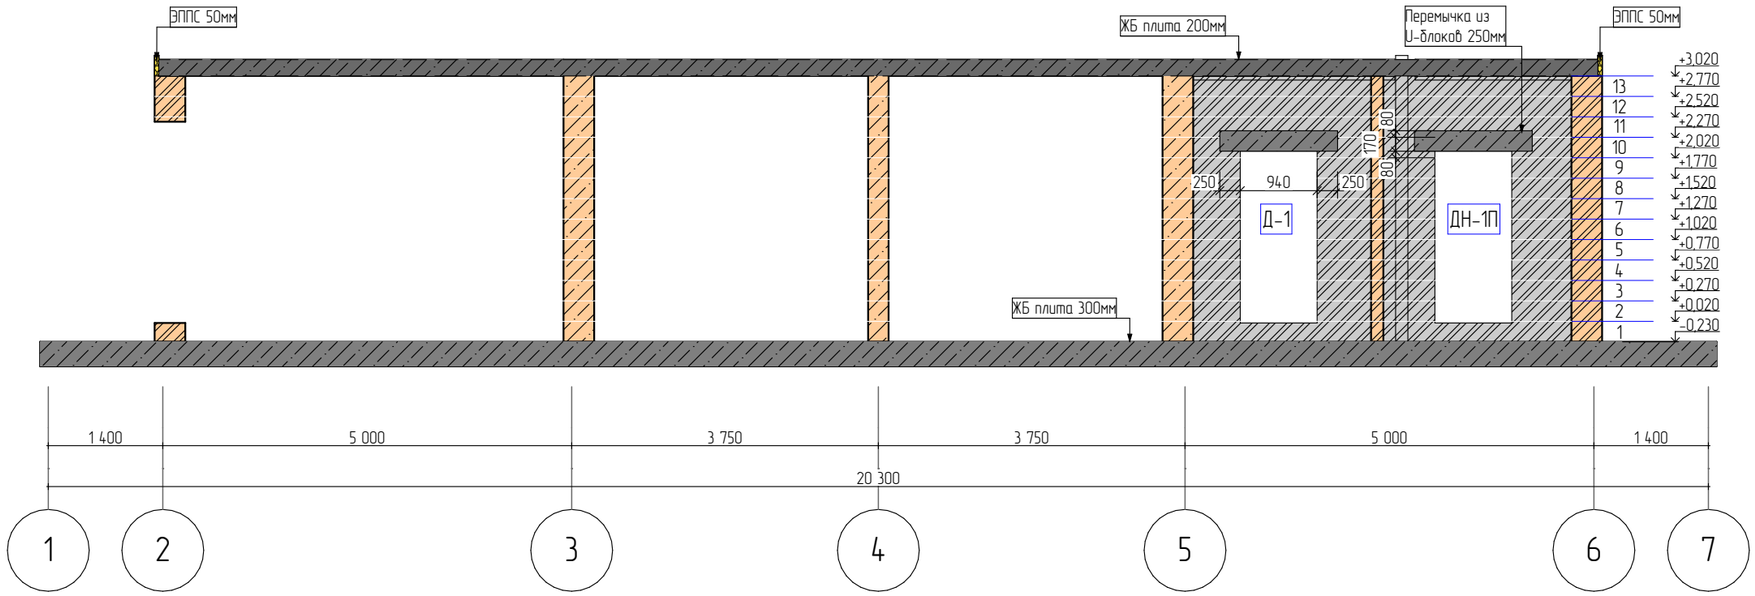

Согласовано

Взам. инв. №


Подпись и дата

Инв. № подл.

Стена Д*	Лист 10

М 1:75

Стена Е*

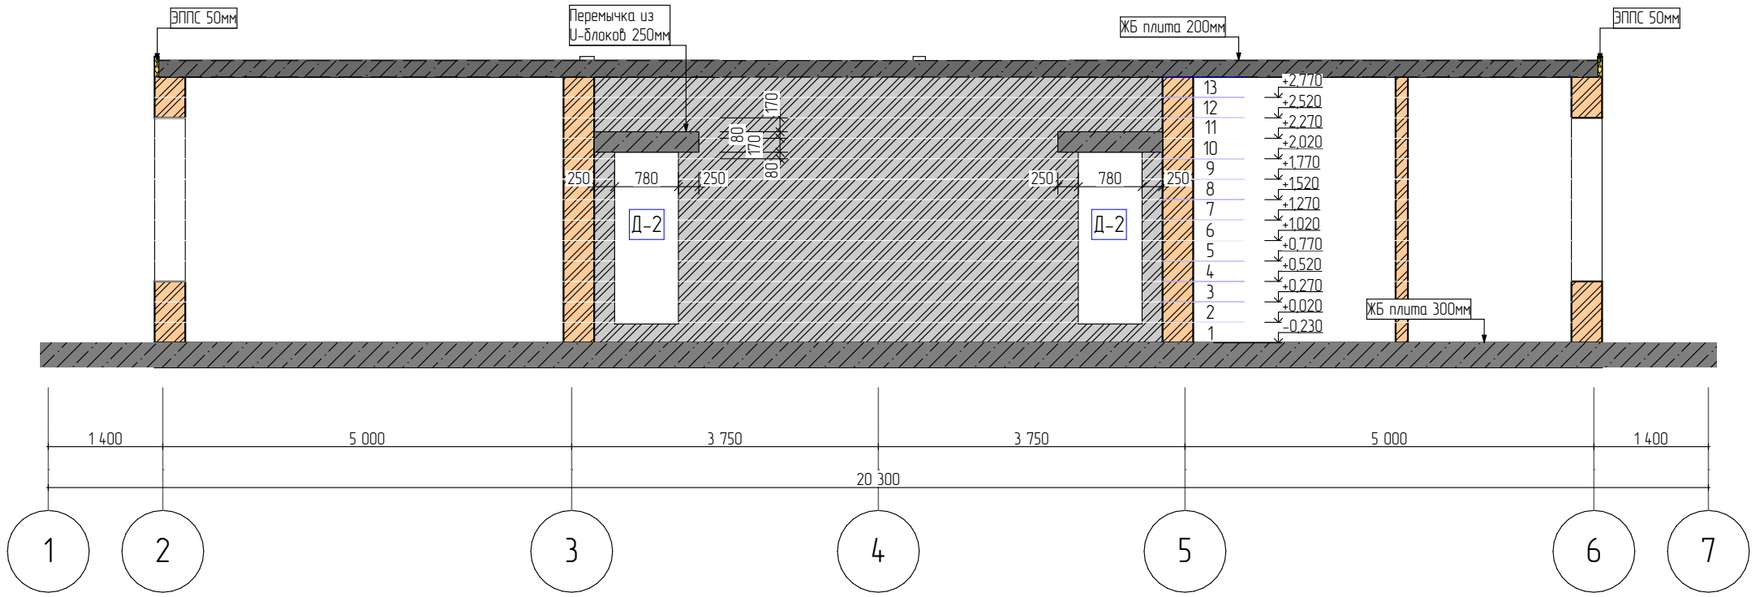

Согласовано

Взам. инв. №

Подпись и дата

Инв. № подл.


Стена Е*

Лист

11

М 1:75

Стена Ж

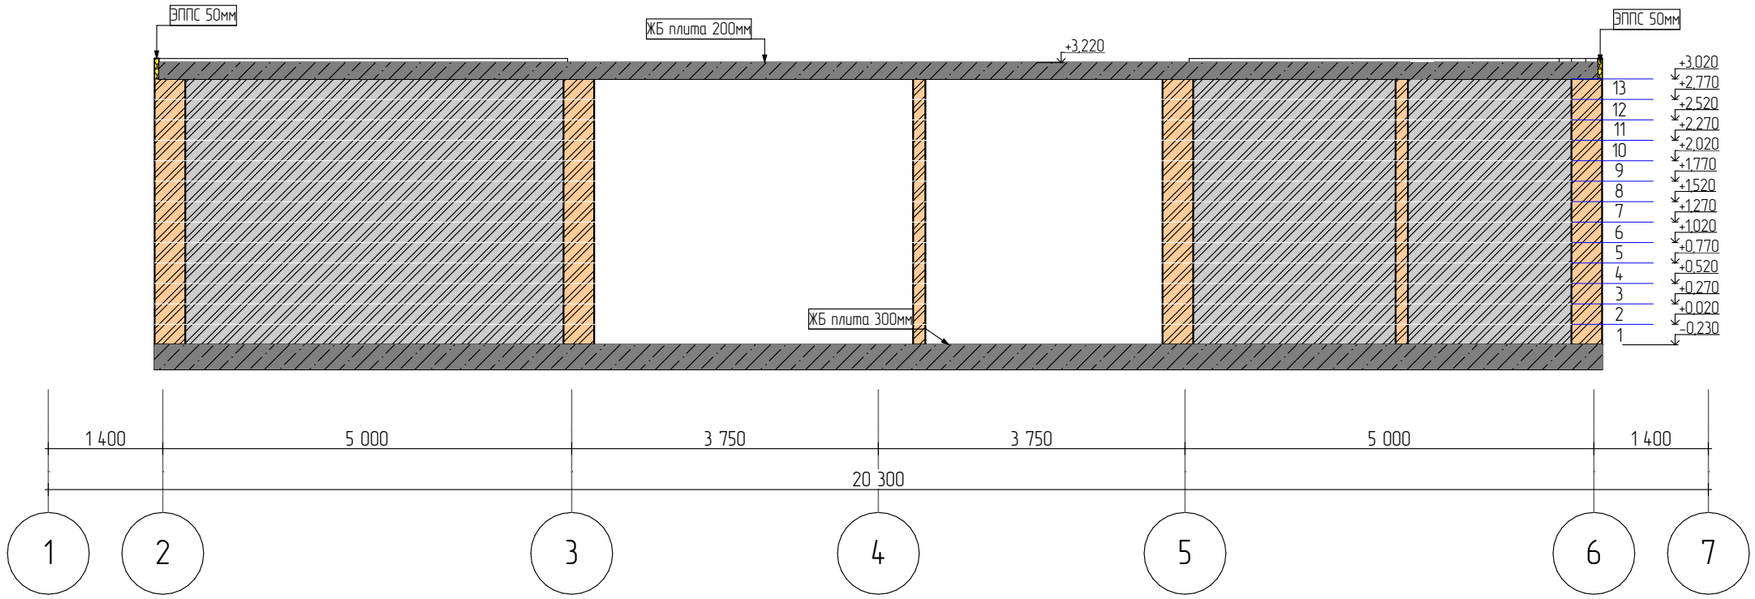

Согласовано

Взам. инв. №

Подпись и дата

Инв. № подл.


Стена Ж


Лист

12

М 1:75

Стена И

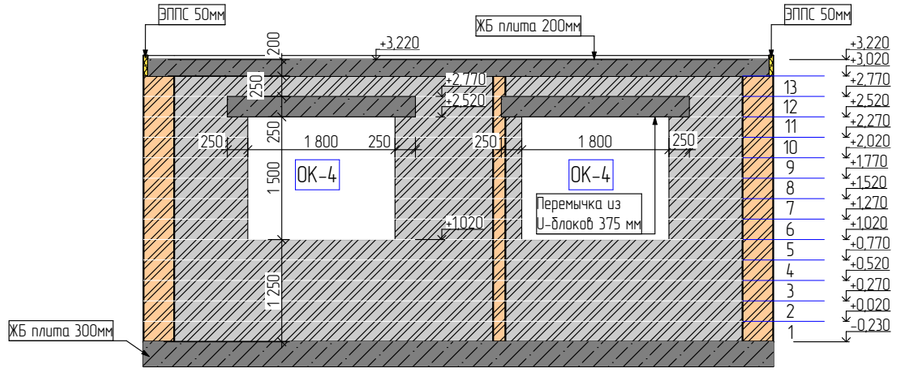

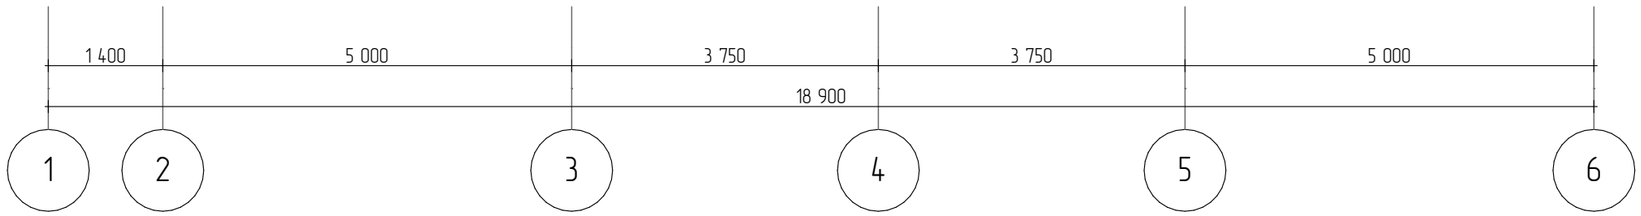

Согласовано

Взам. инв. №

Подпись и дата

Инв. № подл.

Стени И

Лист

13