ОБЪЕКТ ИНДИВИДУАЛЬНОГО ЖИЛИЩНОГО СТРОИТЕЛЬСТВА



ЭСКИЗНЫЙ ПРОЕКТ


ШИФР: #ID ПРОЕКТА

АРХИТЕКТУРНЫЕ РЕШЕНИЯ

САНКТ-ПЕТЕРБУРГ 2021

М 1:100

План 1 этажа с расстановкой мебели

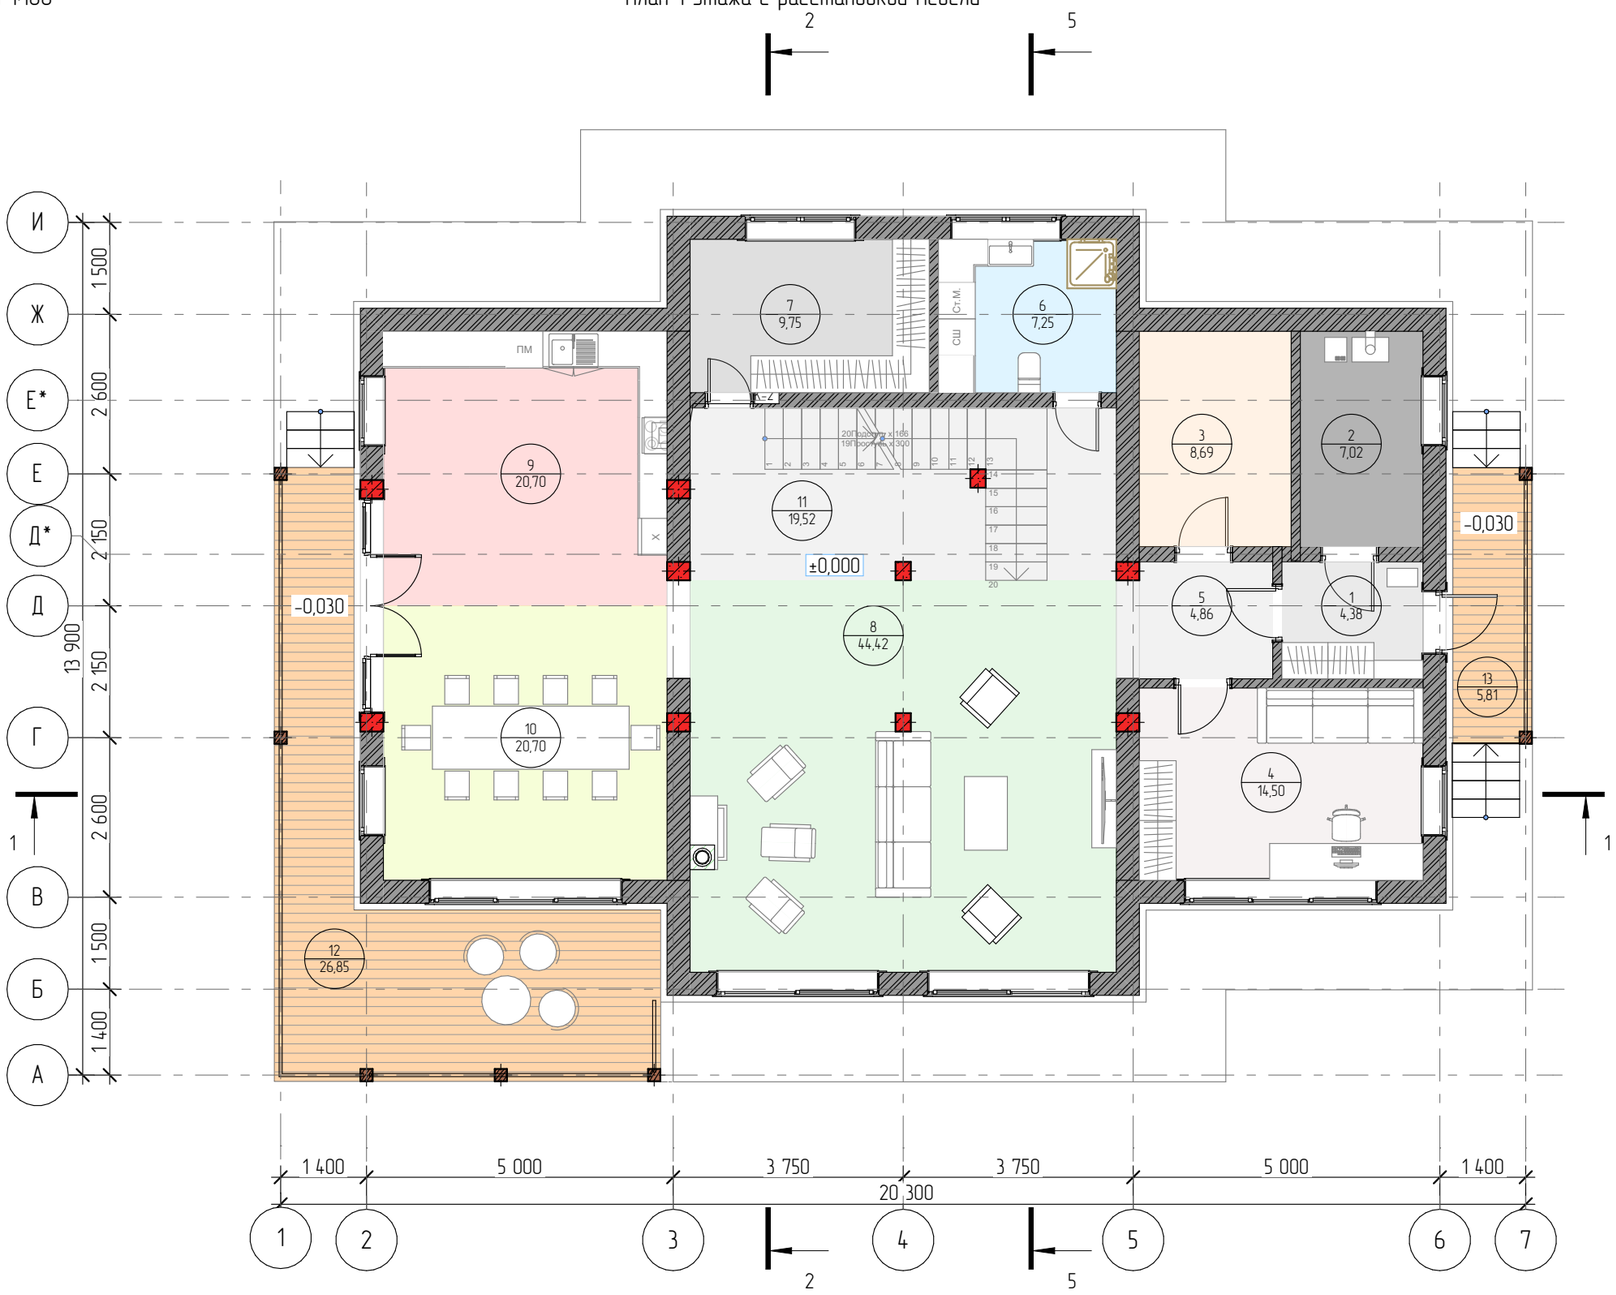

Экспликация 1 этажа

Расположение поиещений	№ п/п	Наименование	Площадь, м2
Внутр. пом.			
	1	Тамбур	4,38
	2	Котельная	7,02
	3	Тренажерный зал	8,69
	4	Гостевая Комната	14,50
	5	Холл 1	4,86
	6	Санузел	7,25
	7	Гардероб	9,75
	8	Гостиная	44,42
	9	Кухня	20,70
	10	Столовая	20,70
	11	Холл 2	19,52
			161,79 м²
Наружн. пом.			
	12	Терраса	26,85
	13	Крыльцо	5,81
			32,66 м²
			194,45 м²

Примечание:
1) Вся показанная мебель, а также назначение комнат носят условный характер
2) Расположение сан.технических приборов не подлежит перемещению.
3) Площадь помещений показана без учета отделочных материалов и понижающего коэффициента по периметру пола.
4) Все декоративные элементы подлежат дополнительному сметному согласованию.

Изм.	Кол.уч	Лист	№док.	Подпись	Дата
Архитектор		Салыкова В.Г.			
Заказчик		#Обращение к Заказчику			

2021

#ID Проекта

Адрес: #Полный Адрес Участка;
к/н: #ID Участка

Индивидуальный жилой дом

стадия	лист	листов
ЭП	1	

План 1 этажа с расстановкой мебели
М 1:100

Согласовано


Взам. инв. №

Подпись и дата

Инв. № подл.

М 1:100

План 2 этажа с расстановкой мебели

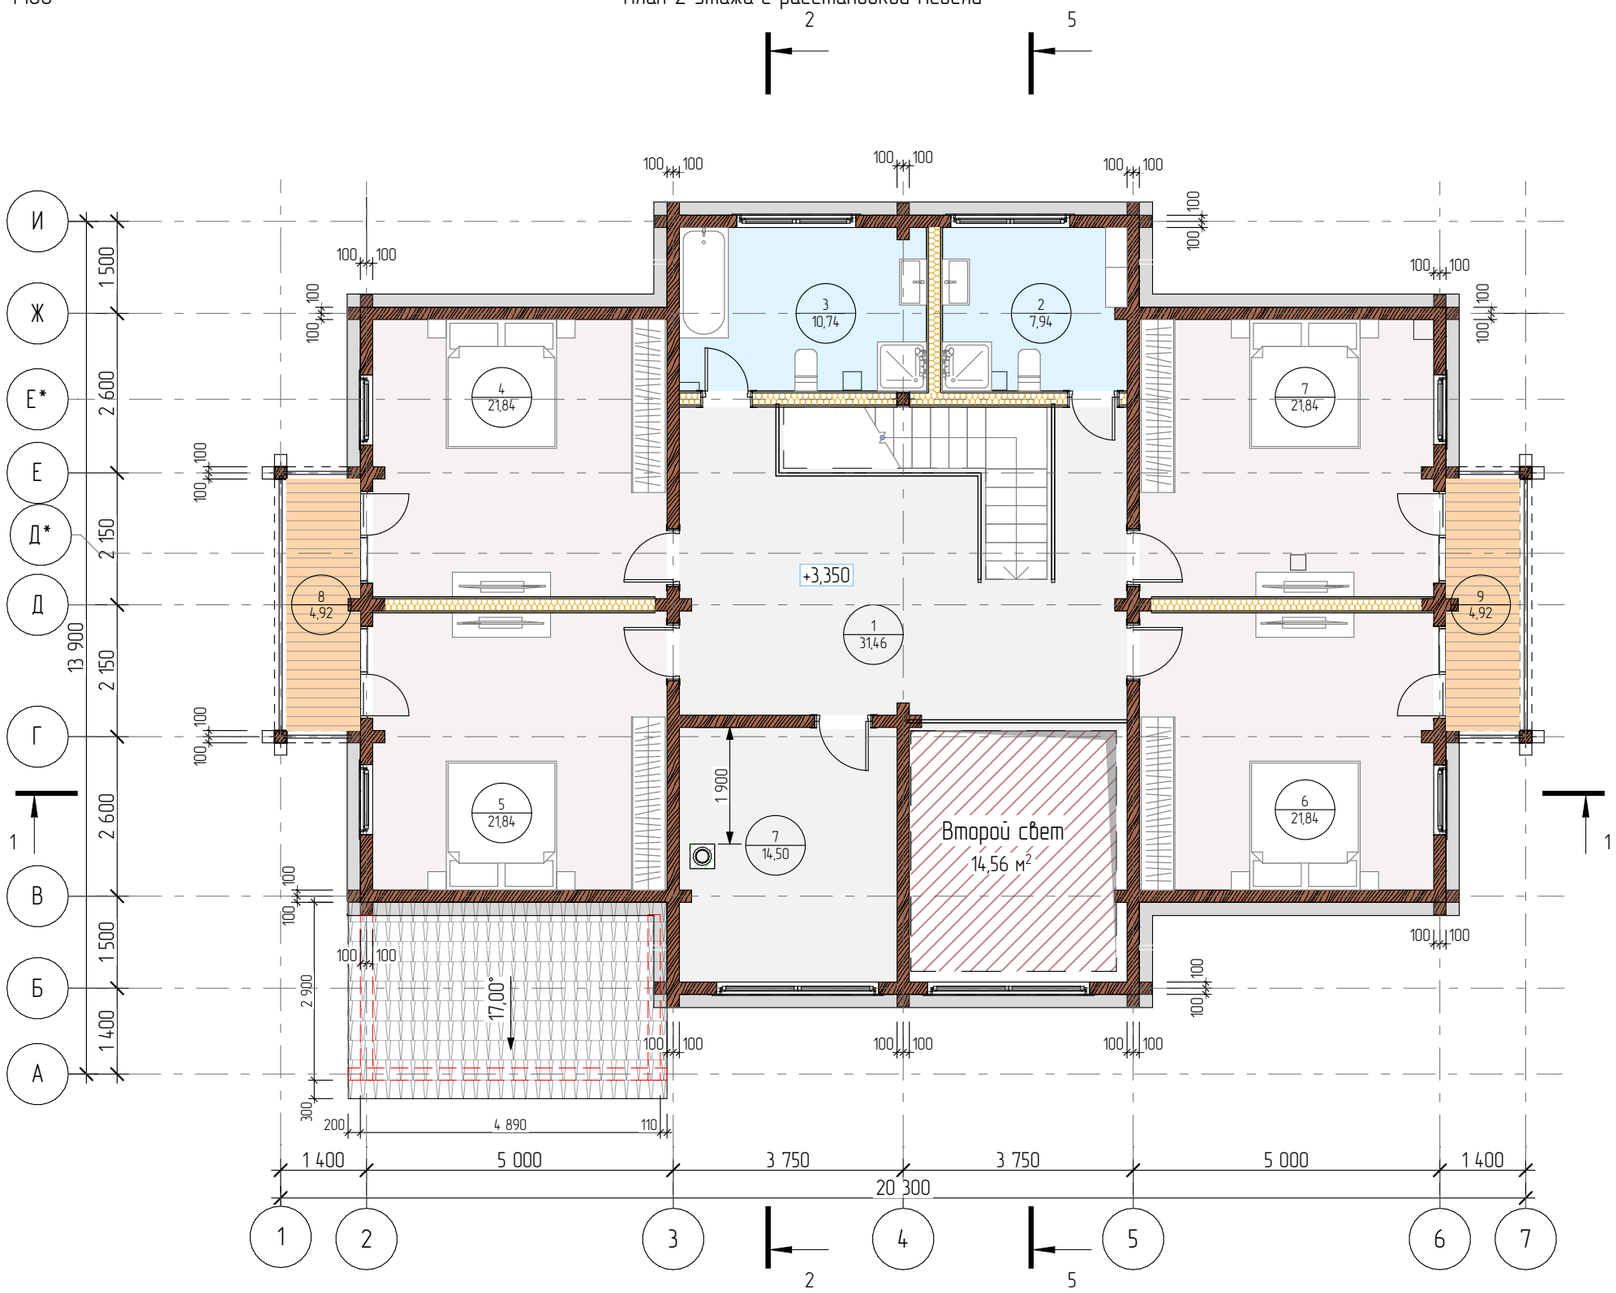

Примечание:
1) Вся показанная мебель, а также назначение комнат носят условный характер
2) Расположение сан.технических приборов не подлежит перемещению.
3) Площадь помещений показана без учета отделочных материалов и понижающего коэффициента по периметру пола.
4) Все декоративные элементы подлежат дополнительному сметному согласованию.

Экспликация 2 этажа

Расположение поиещений	№ п/п	Наименование	Площадь, м2
Внутр. пом.			
	1	Холл	31,46
	2	Санузел 1	7,94
	3	Санузел 2	10,74
	4	Спальня 1	21,84
	5	Спальня 2	21,84
	6	Спальня 3	21,84
	7	Спальня 4	21,84
	7	Гардероб	14,50
			152,00 м²
Наружн. пом.			
	8	Балкон 1	4,92
	9	Балкон 2	4,92
			9,84 м²
			161,84 м²

Согласовано:

Взам. инв. №

Подпись и дата

Инв. № подл.

Изм.	Кол.уч	Лист	№док.	Подпись	Дата
Архитектор		Салыкова В.Г.			
Заказчик		#Обращение к Заказчику			

2021

#ID Проекта

Адрес: #Полный Адрес Участка;
к/н: #ID Участка

Индивидуальный жилой дом

стадия	лист	листов
ЭП	2	

План 2 этажа с расстановкой мебели
М 1:100

Фасад 1-5



Фасад Д-А



Примечание:
1) За отметку +0,000 принята отметка чистового пола первого этажа
2) За отметку +3,350 принята отметка чистового пола второго этажа
3) Номинальные высотные размеры могут отличаться от фактических в силу технологической усадки стенового комплекта и принимаемых отделочных материалов.
4) Несущие перевязки из бревен могут быть ниже основного уровня потолка
5) Все декоративные элементы показаны условно.

					2021	#ID Проекта		
						Адрес: #Полный Адрес Участка; к/н: #ID Участка		
Изм.	Кол.уч	Лист	№док.	Подпись	Дата			
						Индивидуальный жилой дом	стадия	лист	листов
							ЭП	3	
Архитектор		Салыкова В.Г.							
Заказчик		#Обращение к Заказчику				Фасады М 1:100			


Согласовано:

Взам. инв. №


Подпись и дата

Инв. № подл.

Фасад 5-1

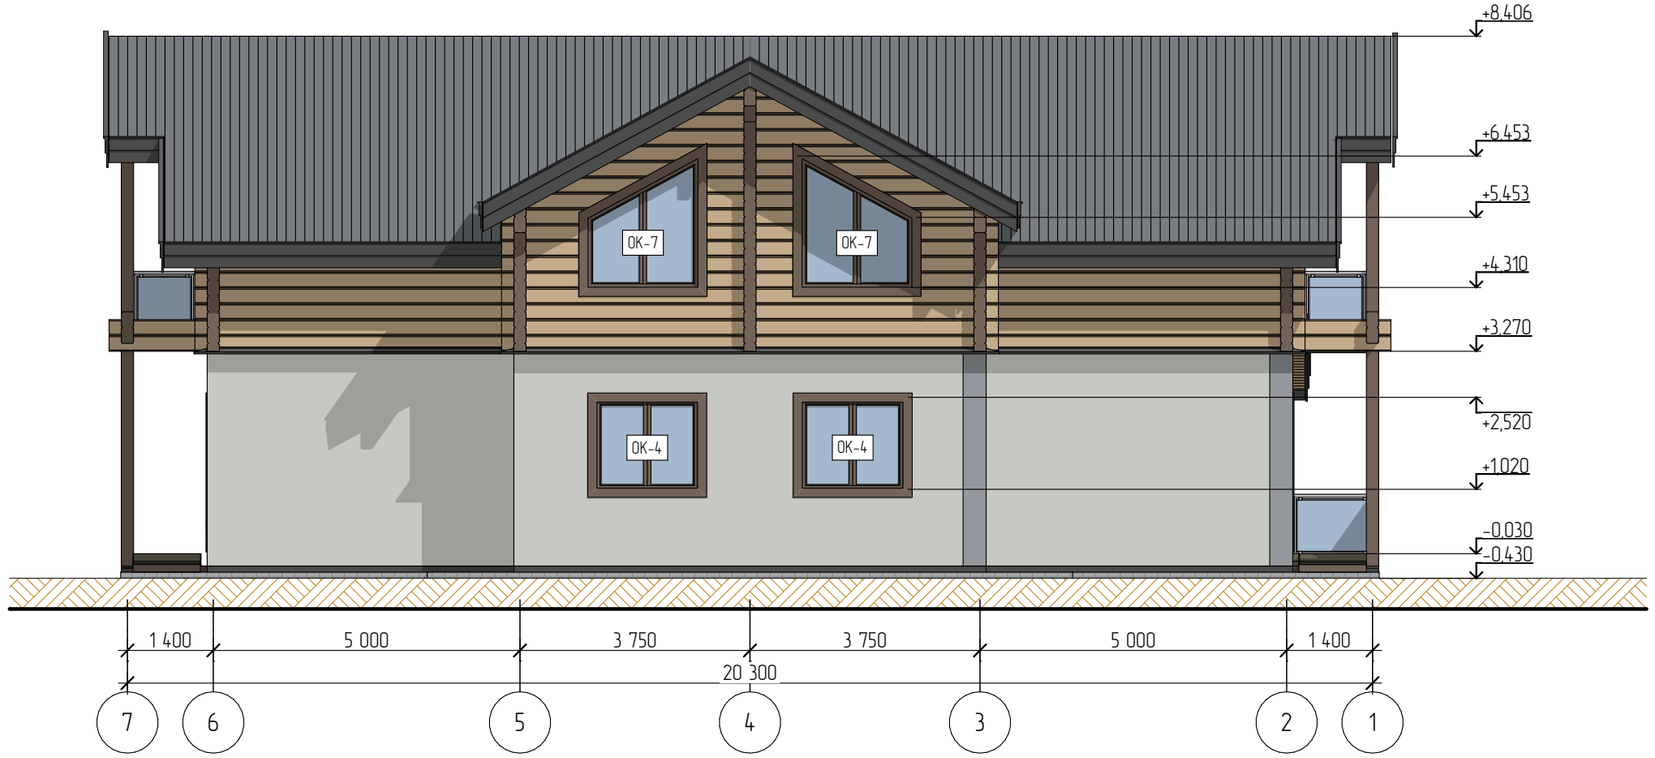

Фасад А-Д

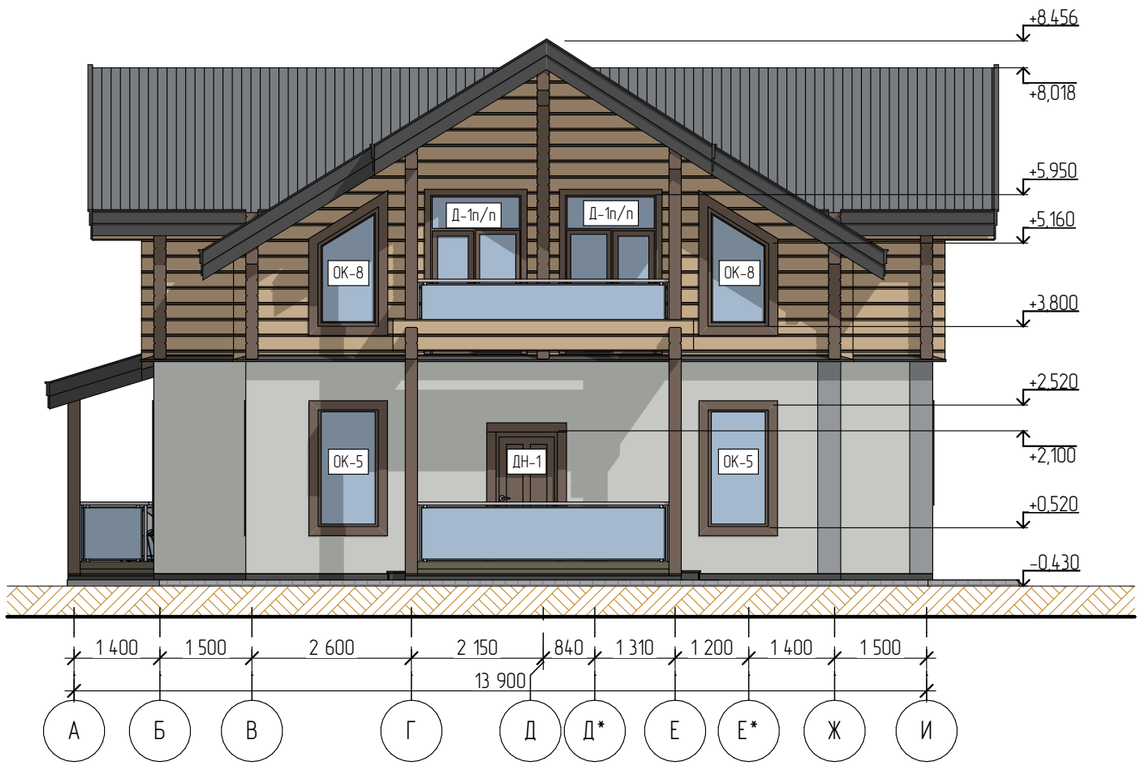

Примечание:
1) За отметку +0,000 принята отметка чистового пола первого этажа
2) За отметку +3,350 принята отметка чистового пола второго этажа
3) Номинальные высотные размеры могут отличаться от фактических в силу технологической усадки стенового комплекта и принимаемых отделочных материалов.
4) Несущие перевязки из бруса могут быть ниже основного уровня потолка
5) Все декоративные элементы показаны условно.

					2021	#ID Проекта		
						Адрес: #Полный Адрес Участка; к/н: #ID Участка		
Изм.	Кол.уч	Лист	№док.	Подпись	Дата			
						Индивидуальный жилой дом	стадия	лист	листов
							ЭП	4	
Архитектор		Салыкова В.Г.							
Заказчик		#Обращение к Заказчику				Фасады М 1:100			

Согласовано:


Взам. инв. №

Подпись и дата

Инв. № подл.

1:75

Разрез 1-1

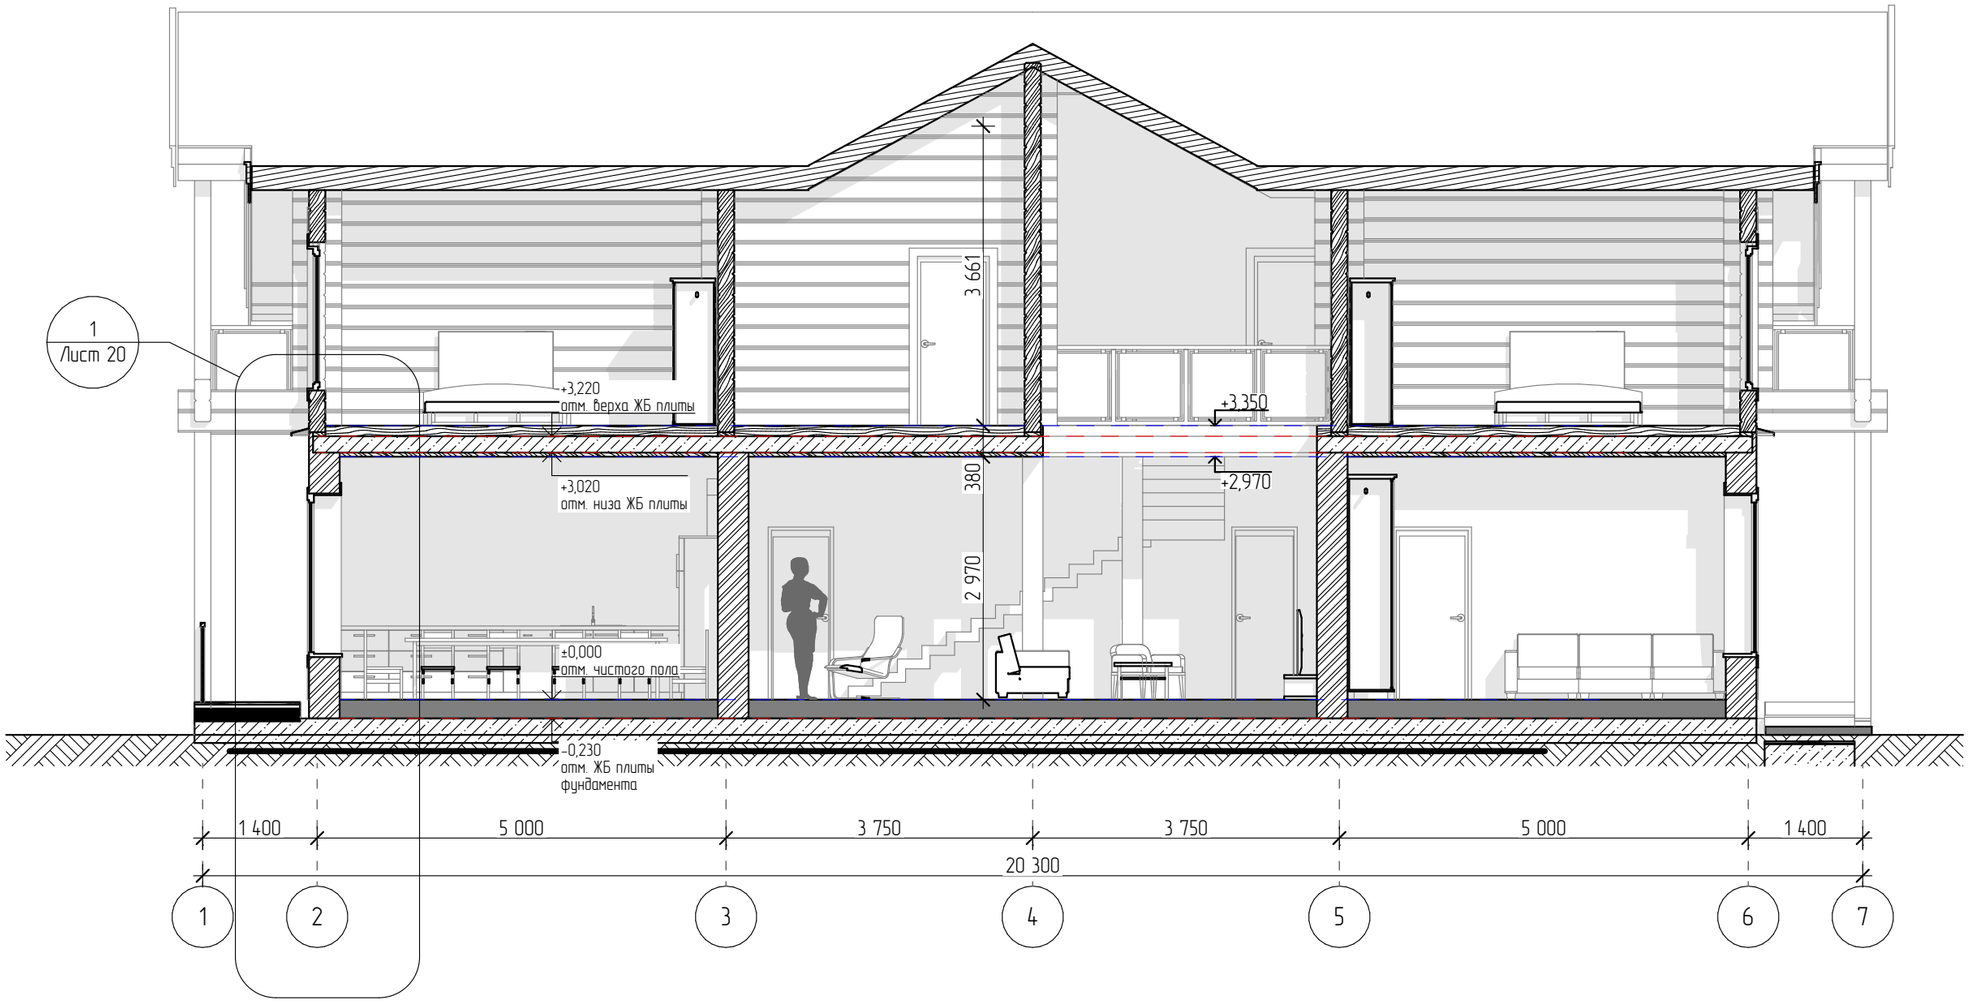

Примечание:

1) За отметку +0,000 принята отметка чистового пола первого этажа
2) За отметку +3,350 принята отметка чистового пола второго этажа
3) Номинальные высотные размеры могут отличаться от фактических в силу технологической усадки стенового комплекта и принимаемых отделочных материалов.
4) Высота фундамента дана без учета перепада. Замер перепада производится на участке при выезде инженера. Изменение габаритов и типа фундаментов согласовывается дополнительным согласованием по смете.
5) Все декоративные элементы показаны условно.

					2021	#ID Проекта			
						Адрес: #Полный Адрес Участка; к/н: #ID Участка			
Изм.	Кол.уч	Лист	№док.	Подпись	Дата				
						Индивидуальный жилой дом	стадия	лист	листов
Архитектор		Салыкова В.Г.					ЭП	5	
Заказчик		#Обращение к Заказчику				Разрез 1-1 М 1:75			

Согласовано:


Взам. инв. №

Подпись и дата

Инв. № подл.

М 1:75

Разрез 2-2

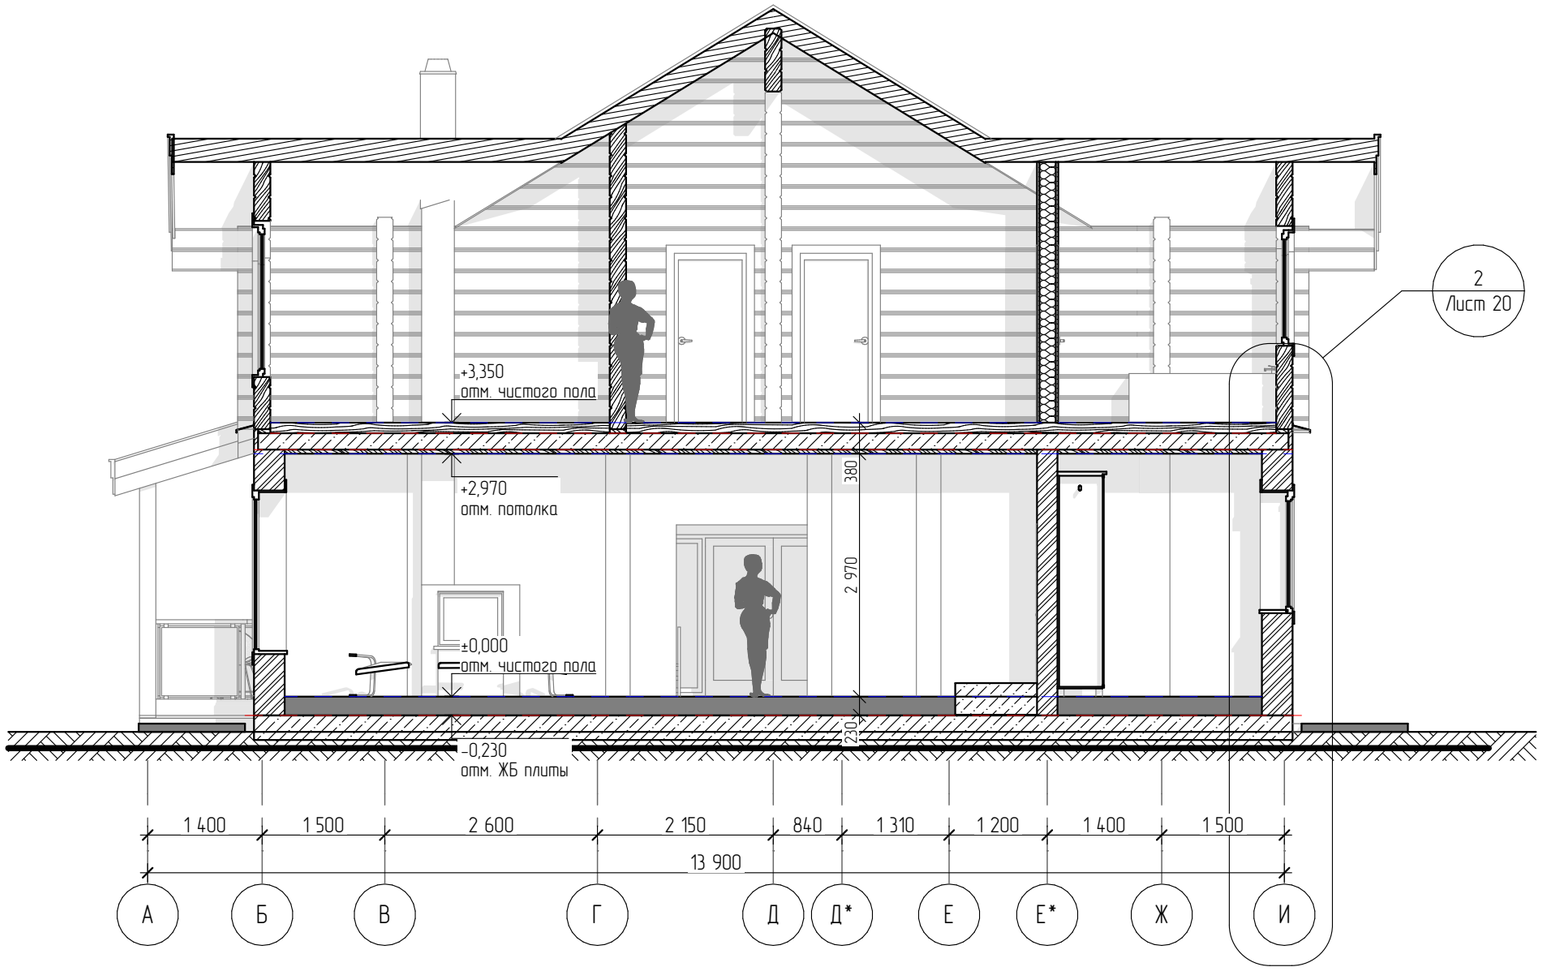

Примечание:

1) За отметку +0,000 принята отметка чистового пола первого этажа
2) За отметку +3,350 принята отметка чистового пола второго этажа
3) Номинальные высотные размеры могут отличаться от фактических в силу технологической усадки стенового комплекта и принимаемых отделочных материалов.
4) Высота фундамента дана без учета перепада. Замер перепада производится на участке при выезде инженера. Изменение габаритов и типа фундаментов согласовывается дополнительным согласованием по смете.
5) Все декоративные элементы показаны условно.

					2021	#ID Проекта			
						Адрес: #Полный Адрес Участка; к/н: #ID Участка			
Изм.	Кол.уч	Лист	№док.	Подпись	Дата				
						Индивидуальный жилой дом	стадия	лист	листов
							ЭП	6	
Архитектор		Салыкова В.Г.							
Заказчик		#Обращение к Заказчику				Разрез 2-2 М 1:75			

Согласовано:

Взам. инв. №

Подпись и дата

Инв. № подл.

Общий вид 1



Общий вид 2



Общий вид 3



Общий вид 4



Общие виды

Лист 7

Согласовано

Взам. инв. №

Подпись и дата

Инв. № подл.

Общий вид 1 этаж



Общий вид 1 этаж



Общий вид 2 этаж



Общий вид 2 этаж



Согласовано

Взам. инв. №

Подпись и дата

Инв. № подл.

Общие виды (поэтажные)

Лист

8