М 1:100

План раскладки стропил 1 уровень

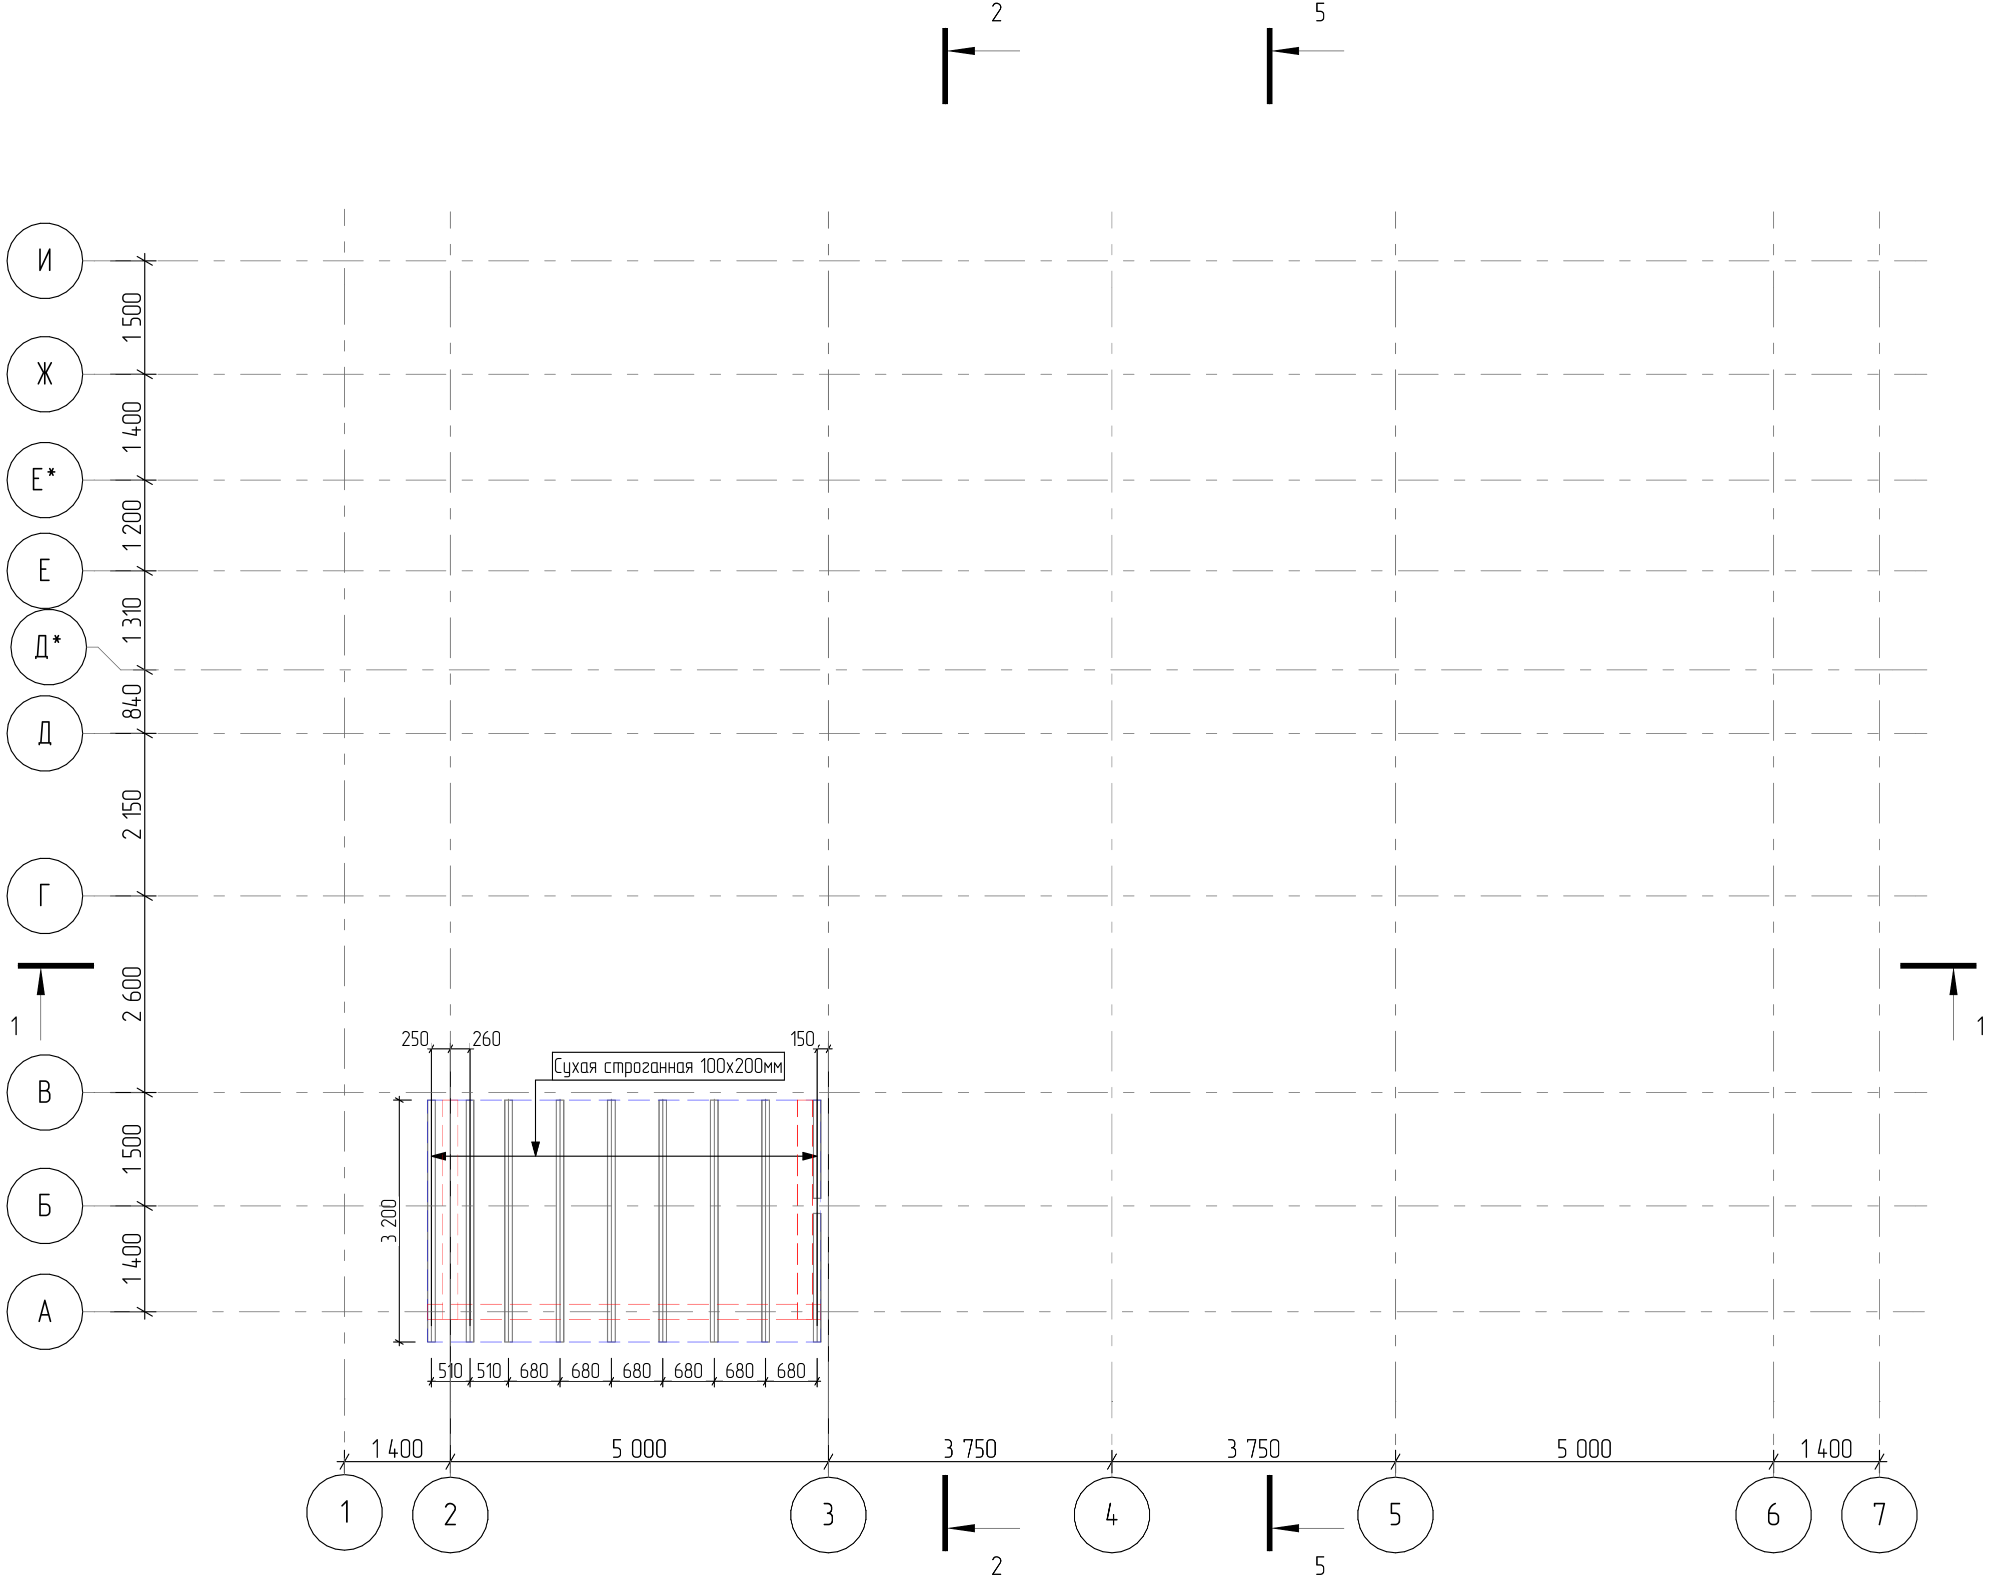

Согласовано

Взам. инв. №

Подпись и дата

Инв. № подл.

Стропила 1 уровень

Лист

М 1:100

План раскладки стропил 2 уровень

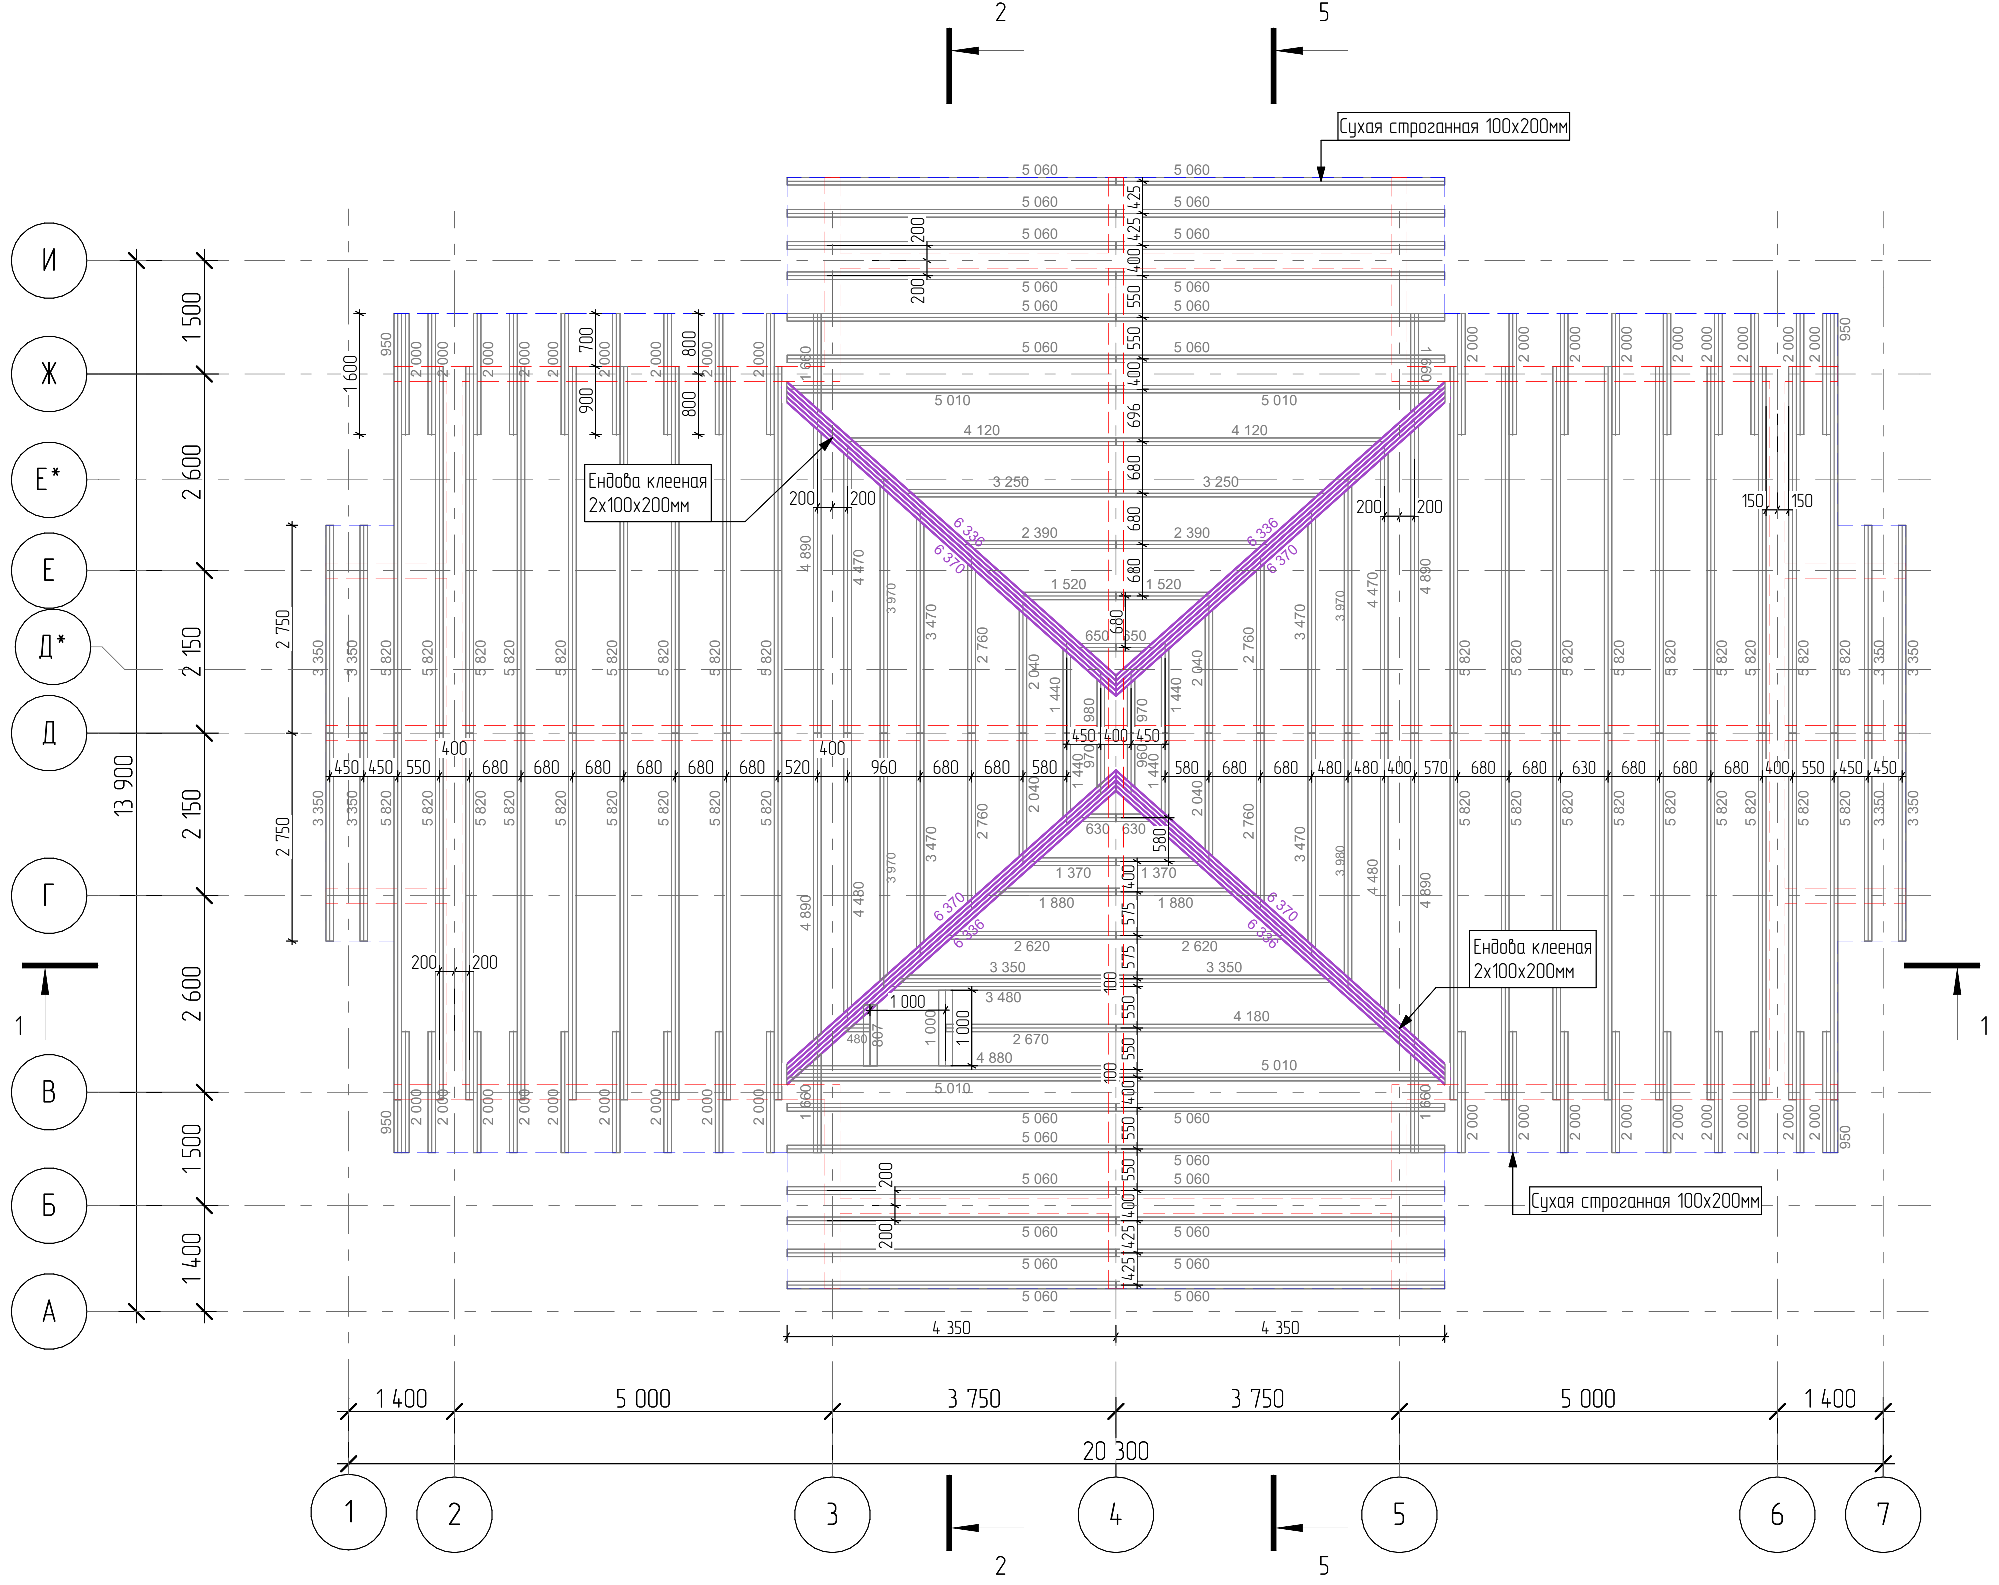

Согласовано:

Взам. инв. №

Подпись и дата

Инв. № подл.

2021

#ID Проекта

Адрес: #Полный Адрес Участка

Изм.	Кол.уч	Лист	№док.	Подпись	Дата

Архитектор Салыкова В.Г.

Заказчик #Обращение к Заказчику

Индивидуальный жилой дом

стадия	лист	листов
РП		

Стропила 2 уровень

Общий вид КД - 1

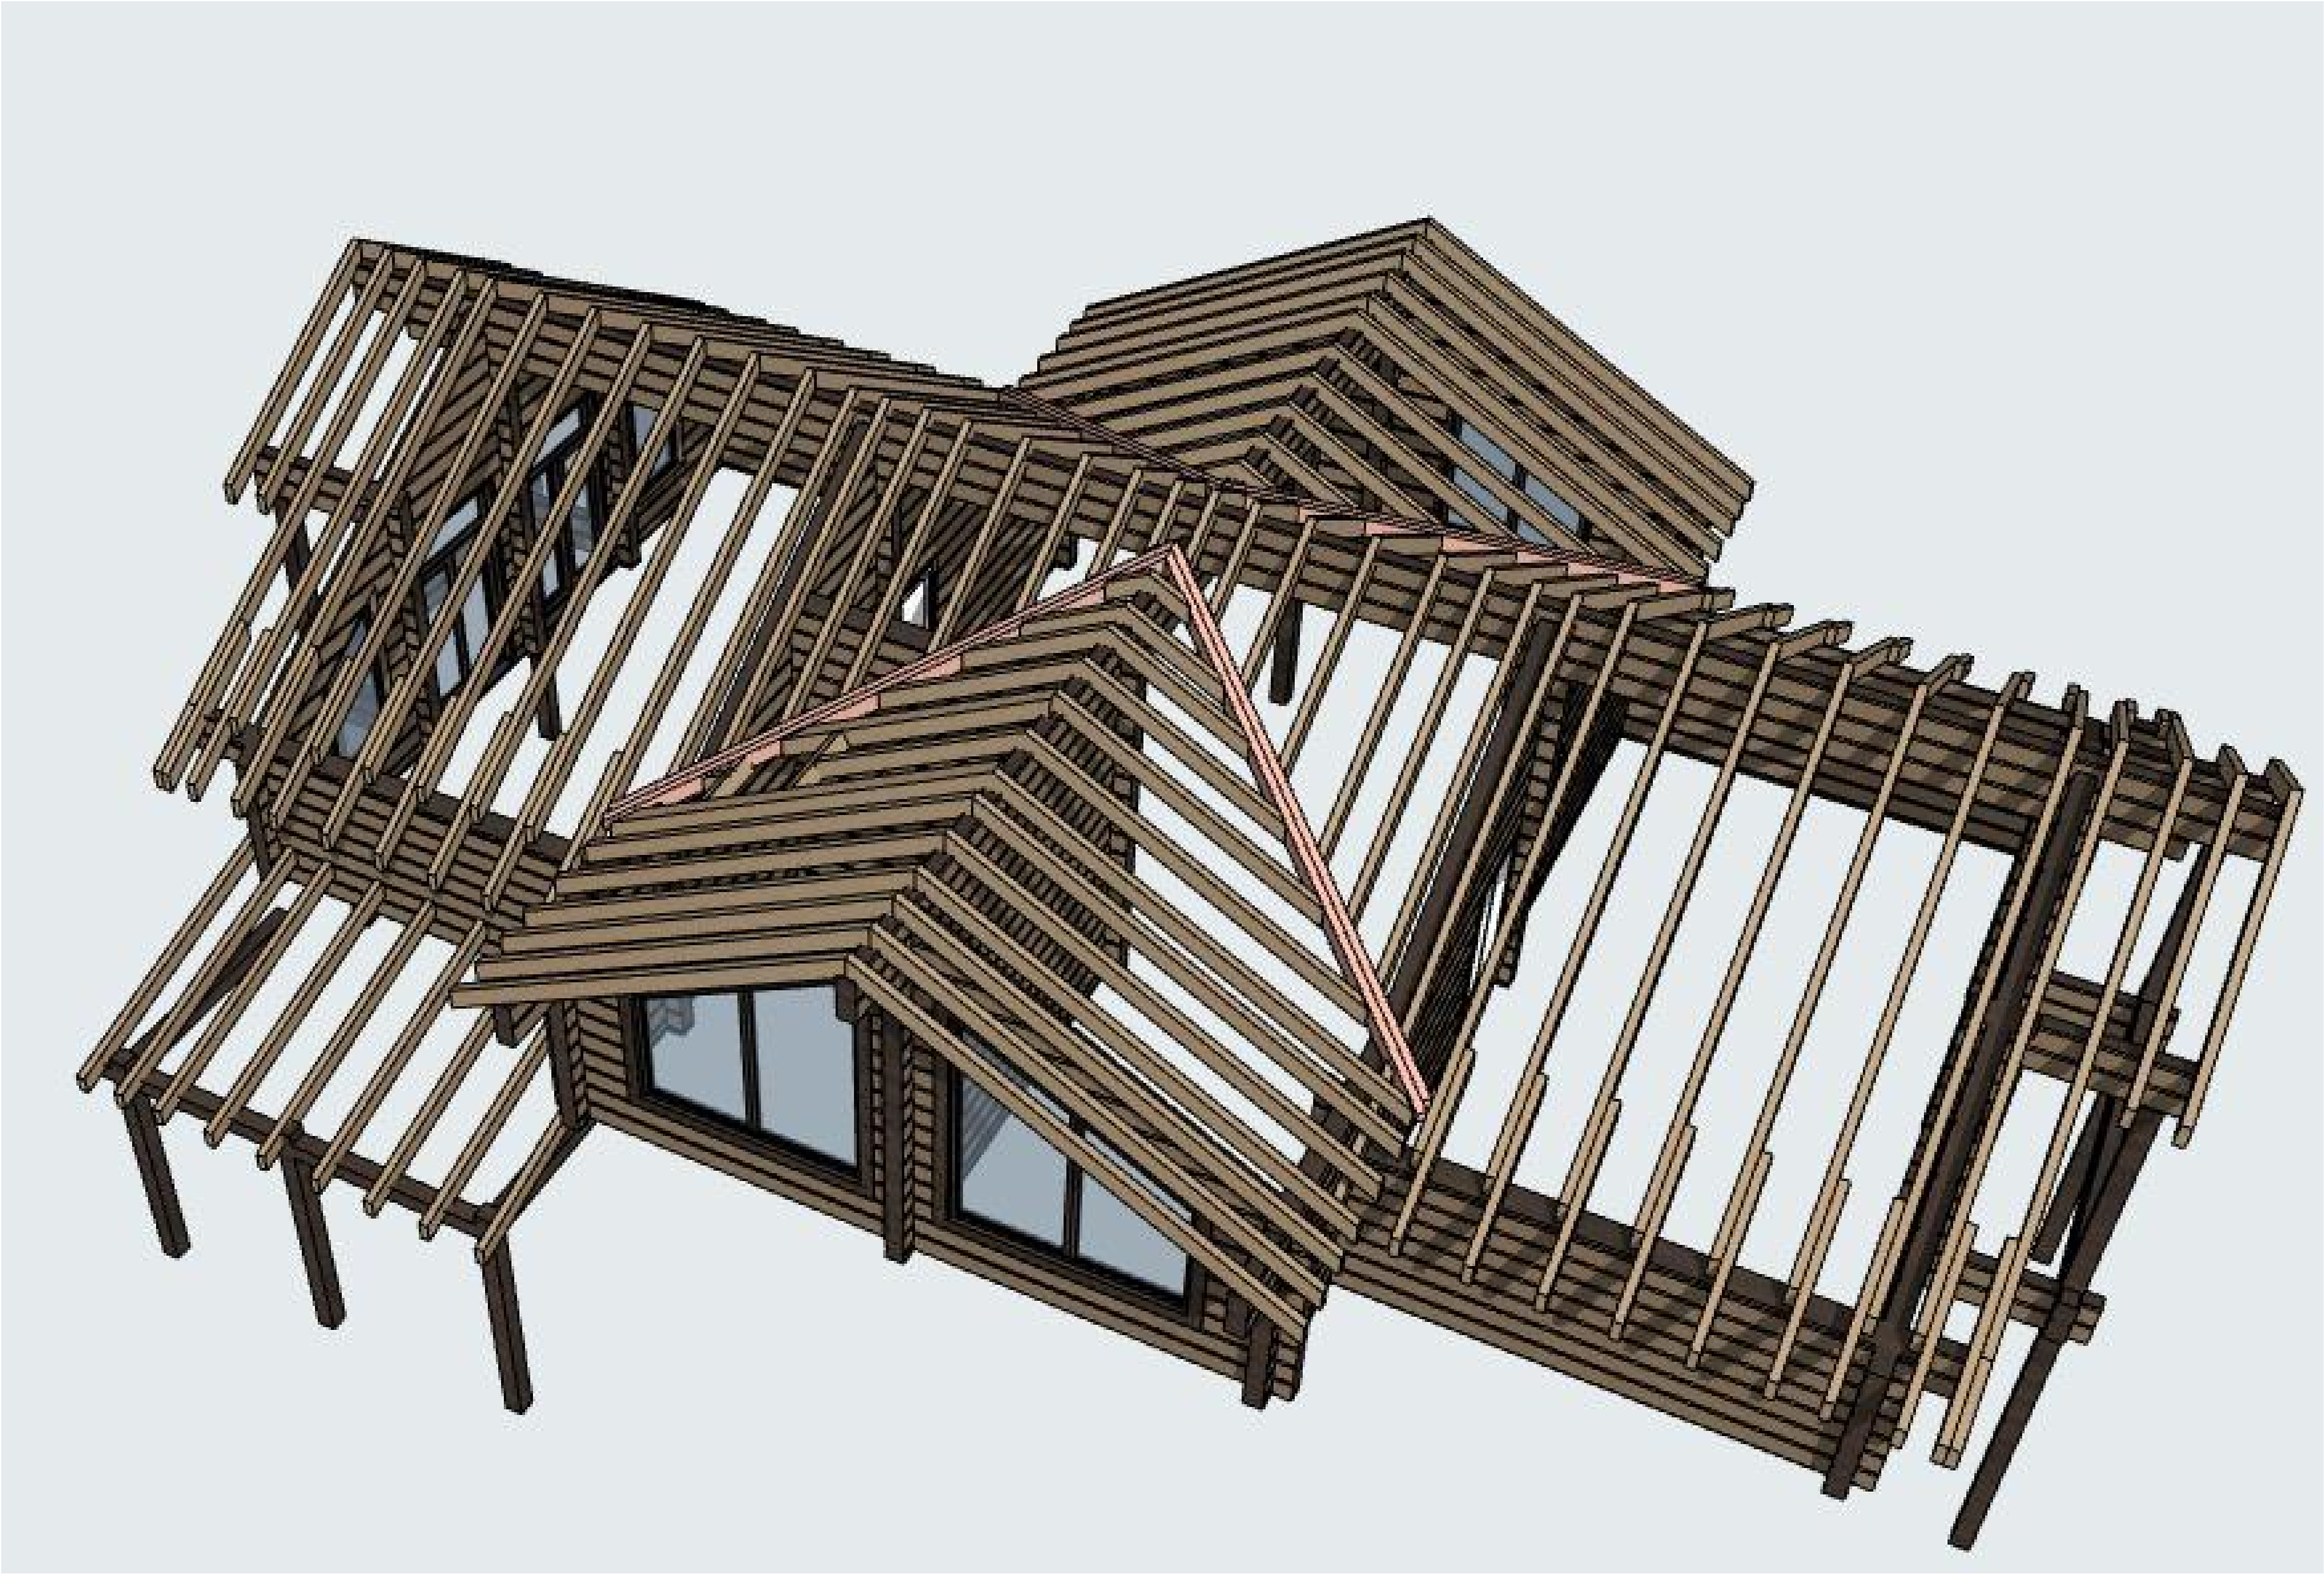

Согласовано

Взам. инв. №

Подпись и дата

Инв. № подл.

Общие виды

Вид 2

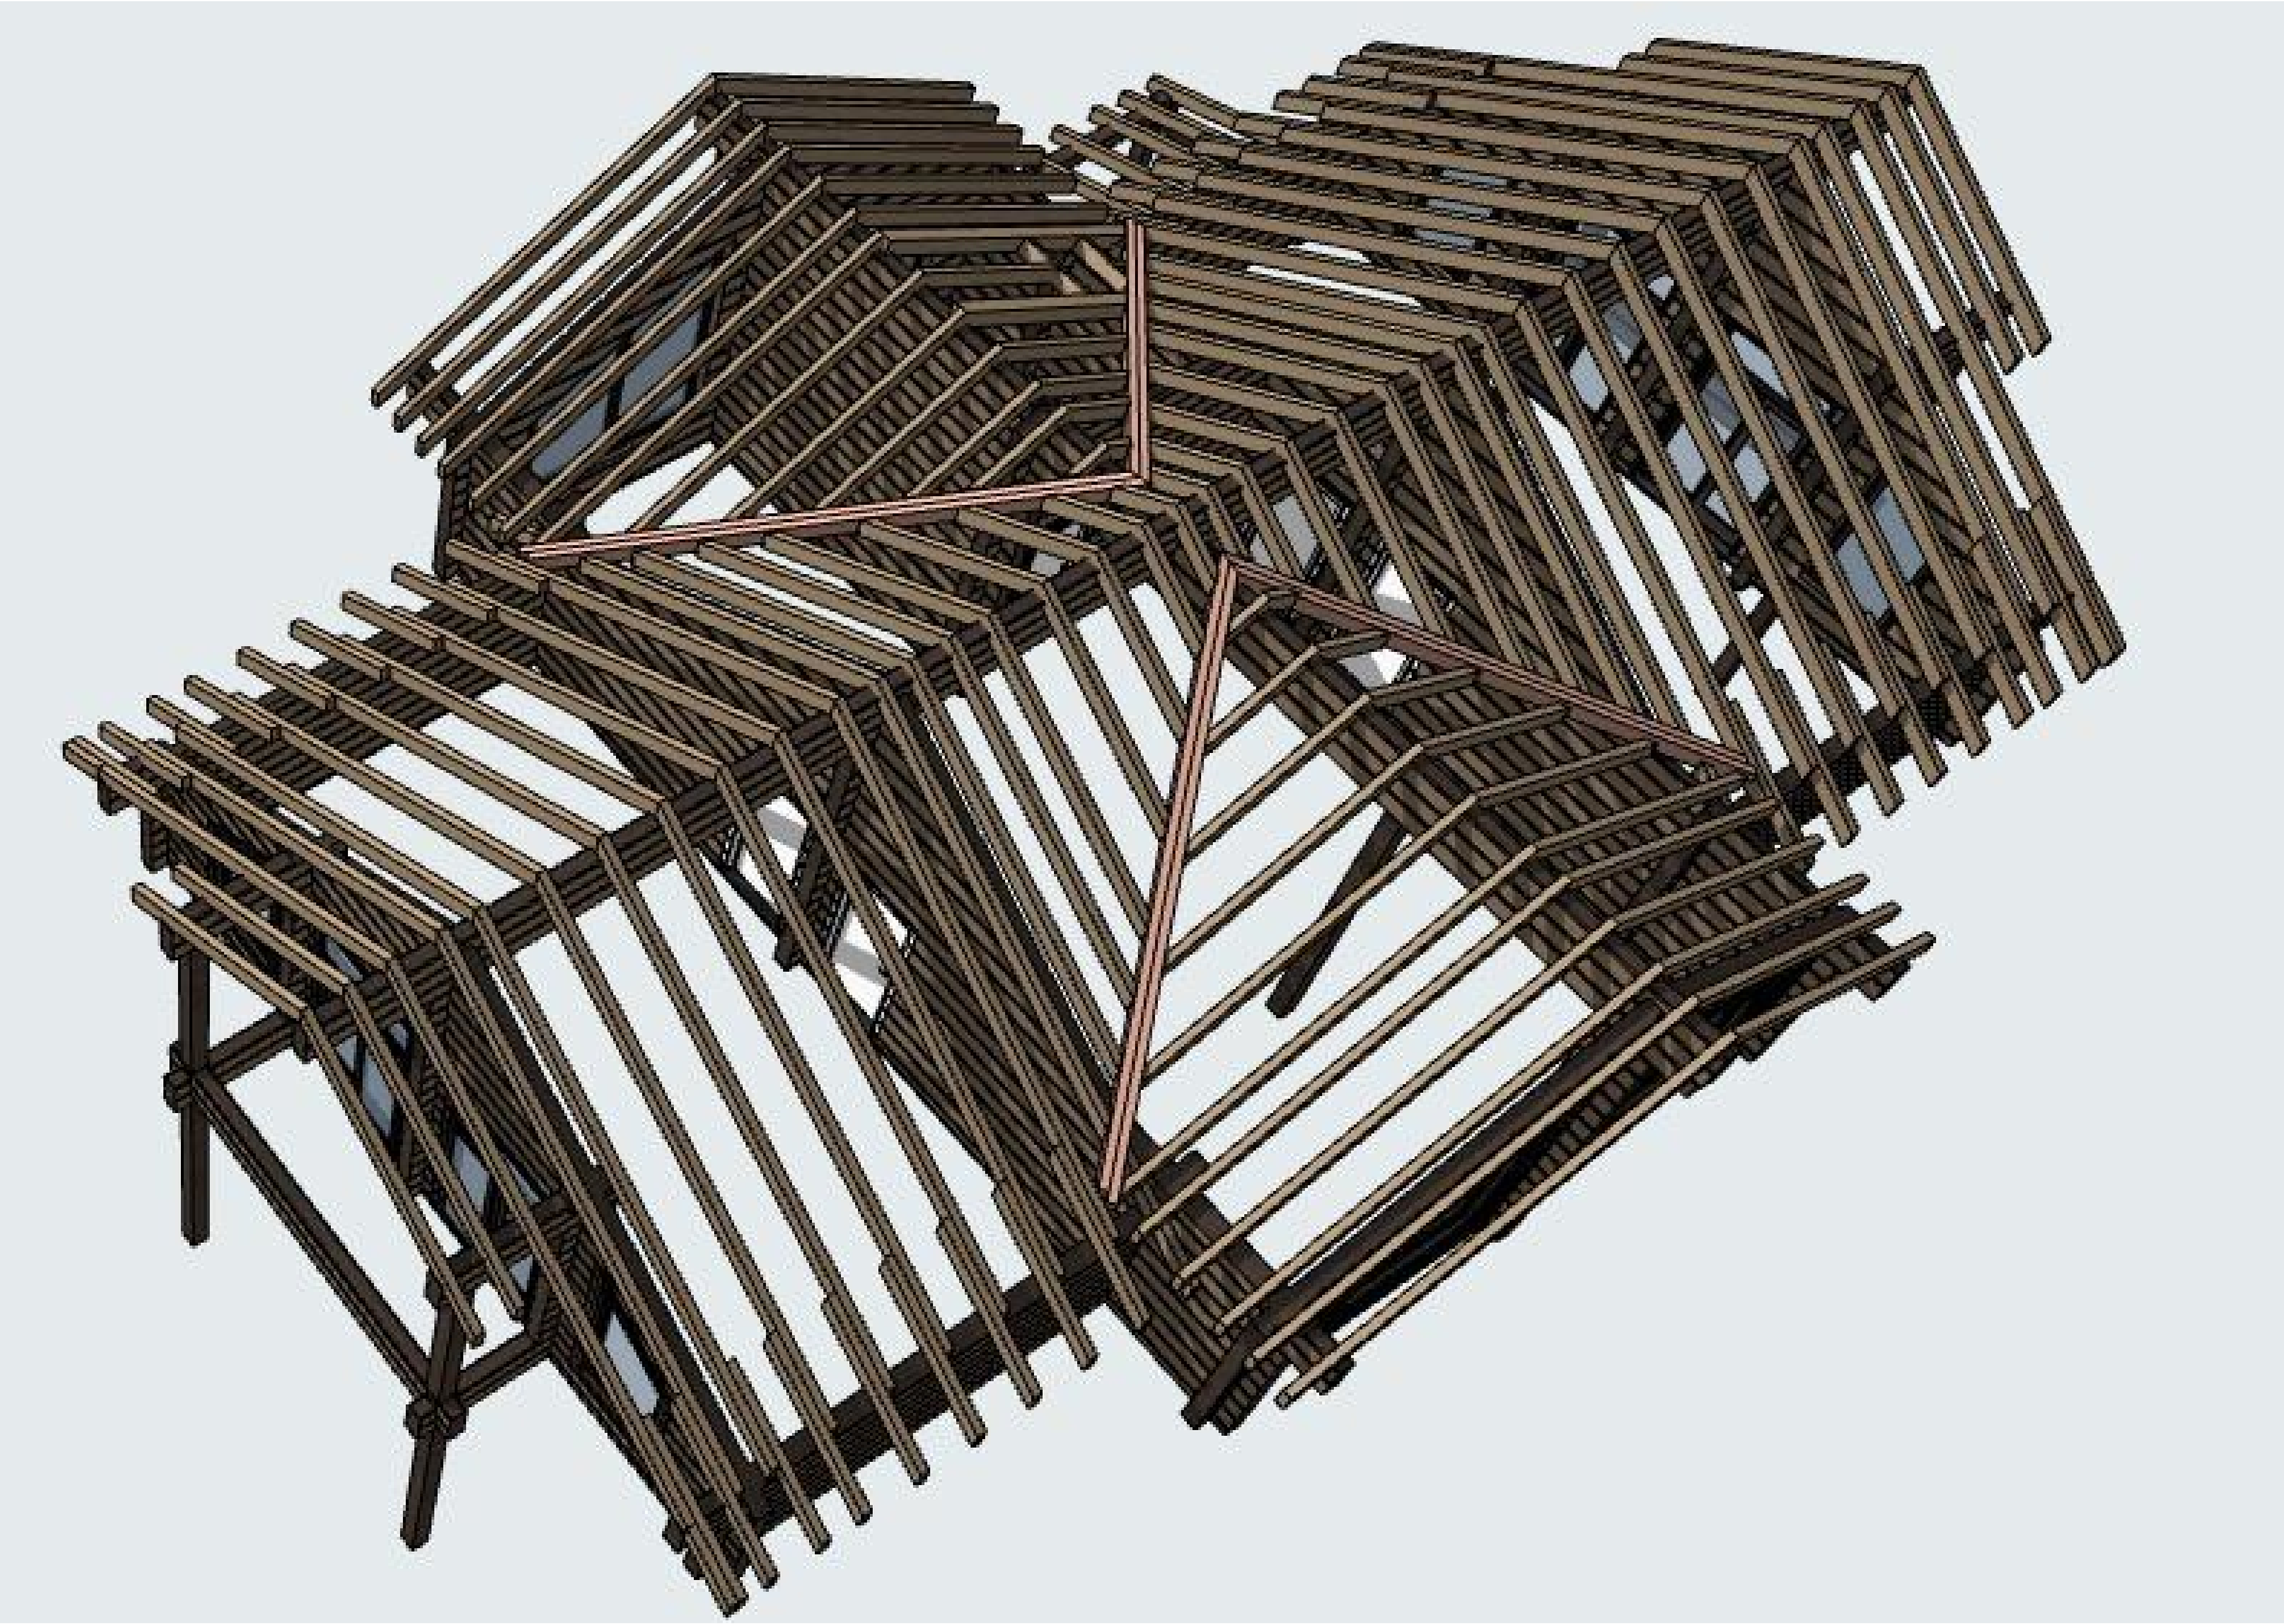

Согласовано

Взам. инв. №

Подпись и дата

Инв. № подл.

Общие виды

Вид 3

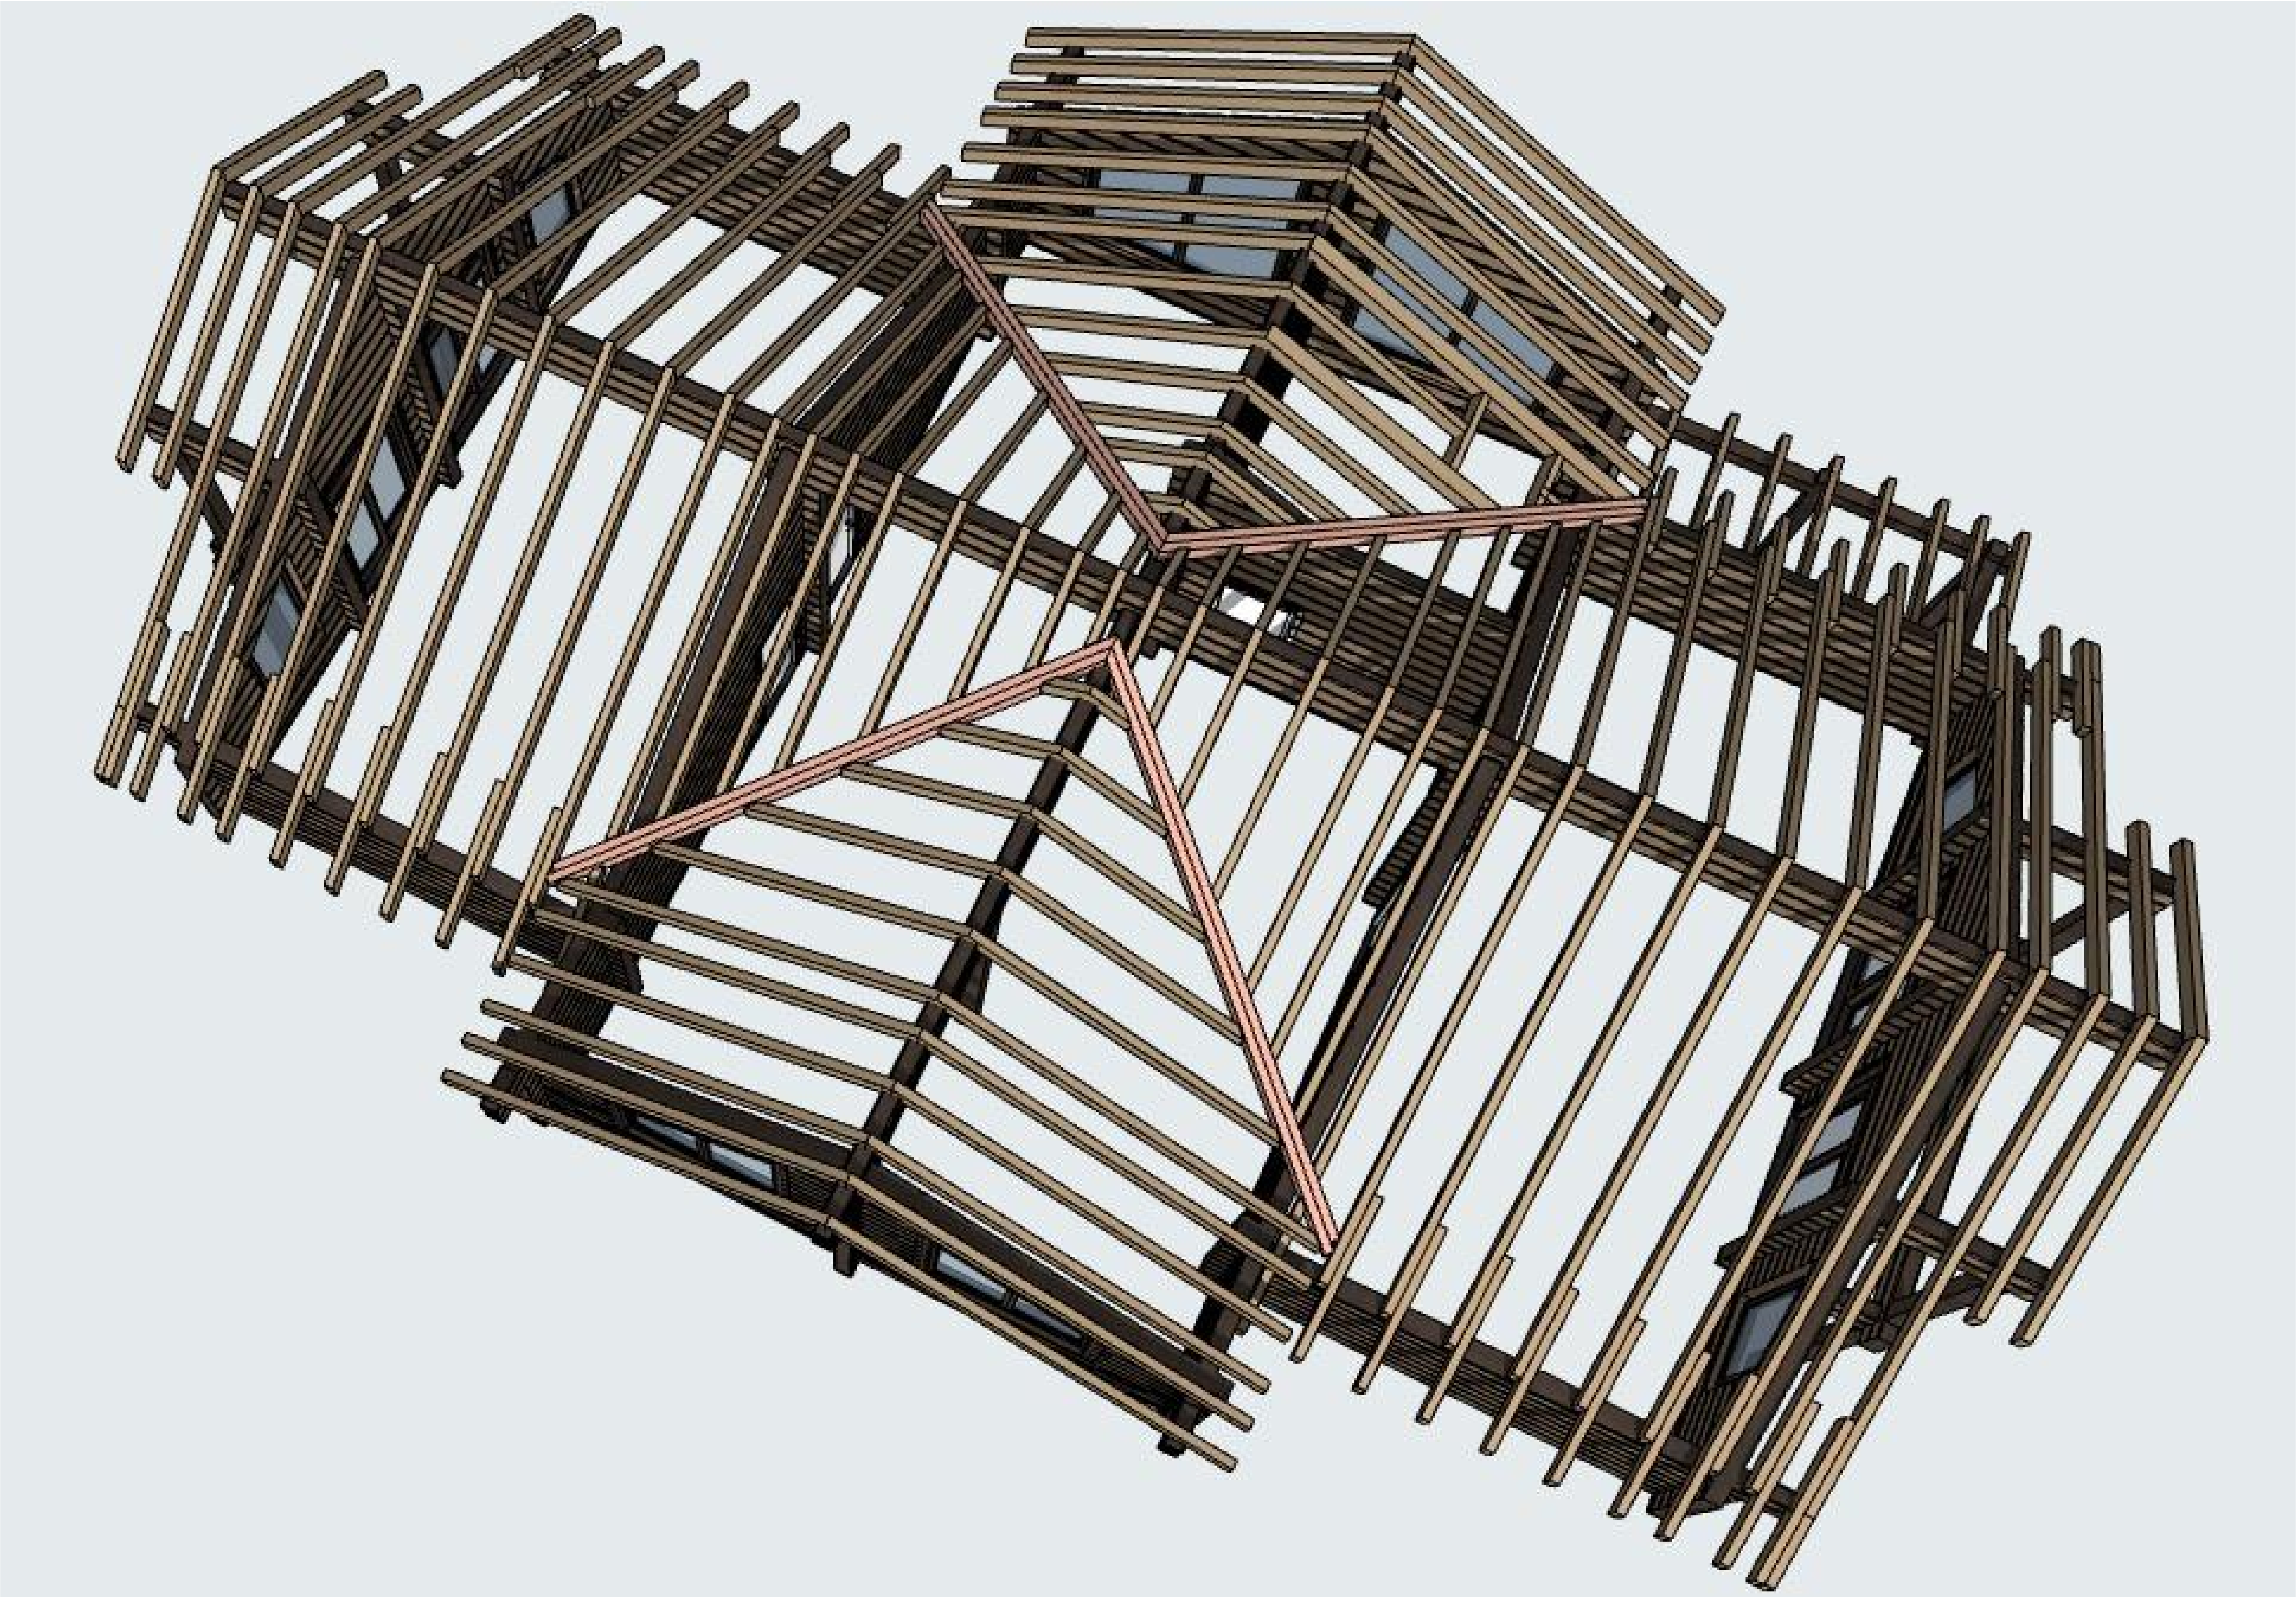

Согласовано

Взам. инв. №

Подпись и дата

Инв. № подл.

Общие виды

Вид 4

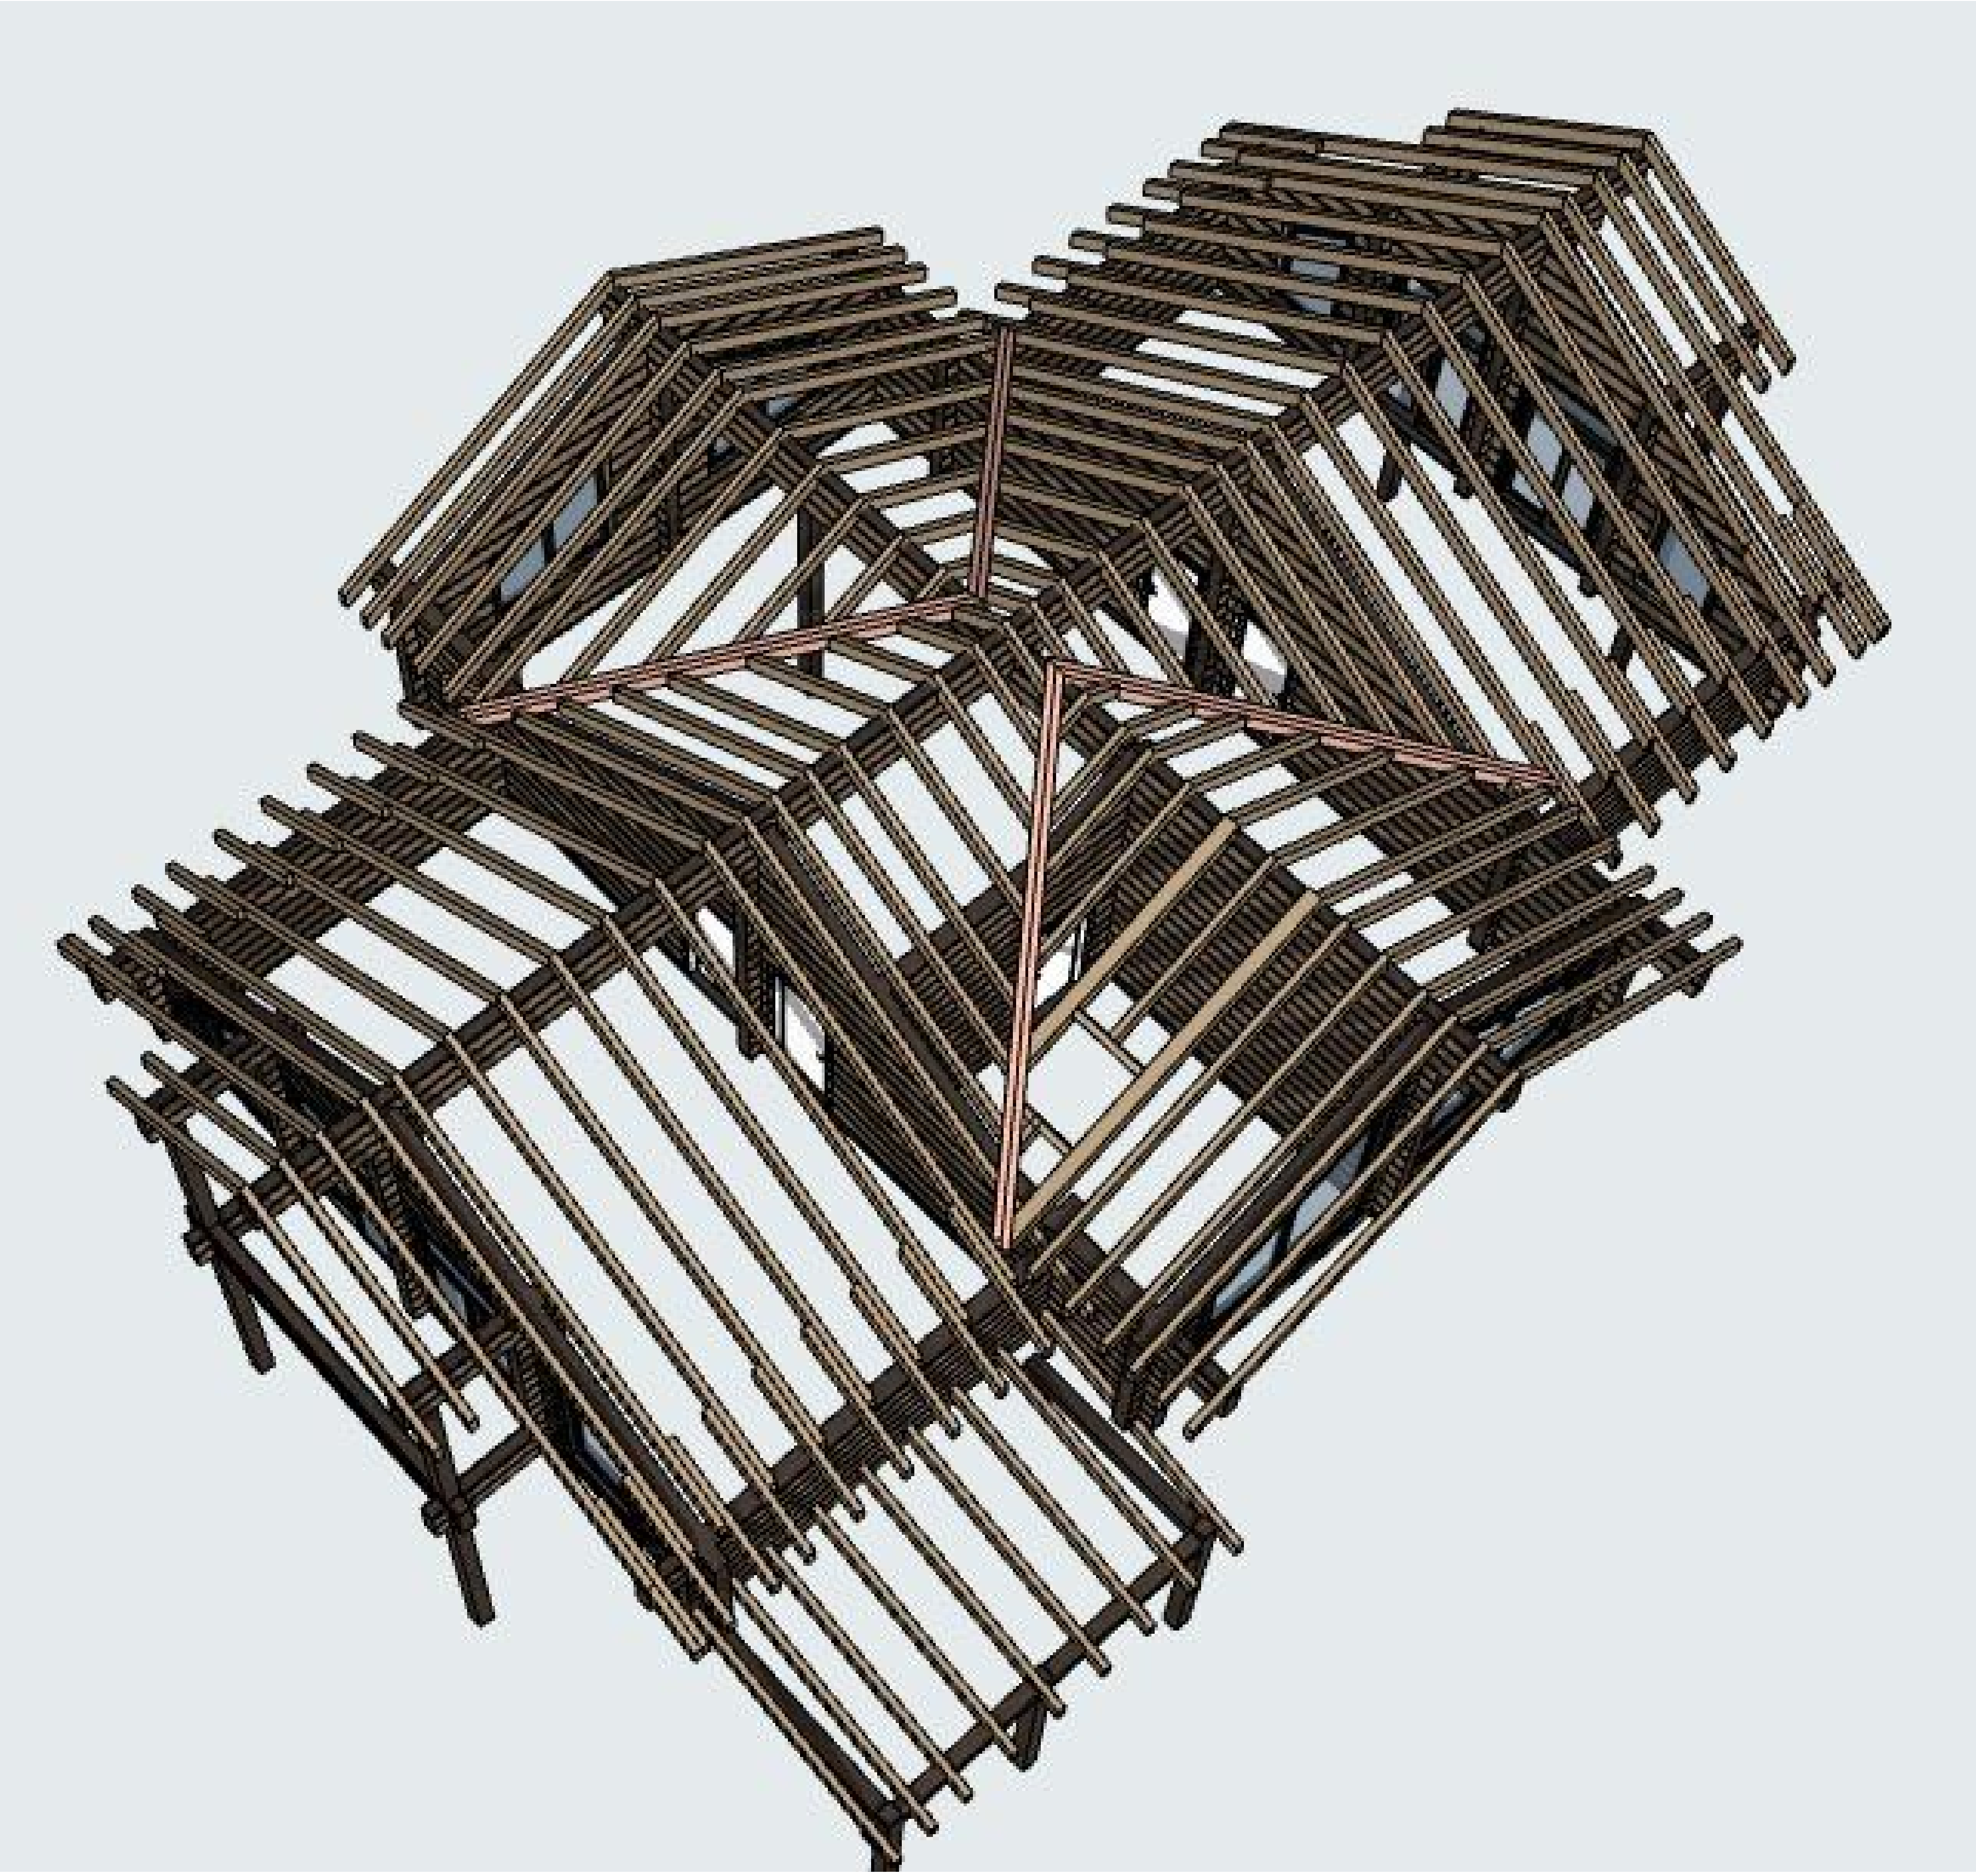

Согласовано

Взам. инв. №

Подпись и дата

Инв. № подл.

Общие виды