
М 1:100

Схема штробления под электрику 2 этаж

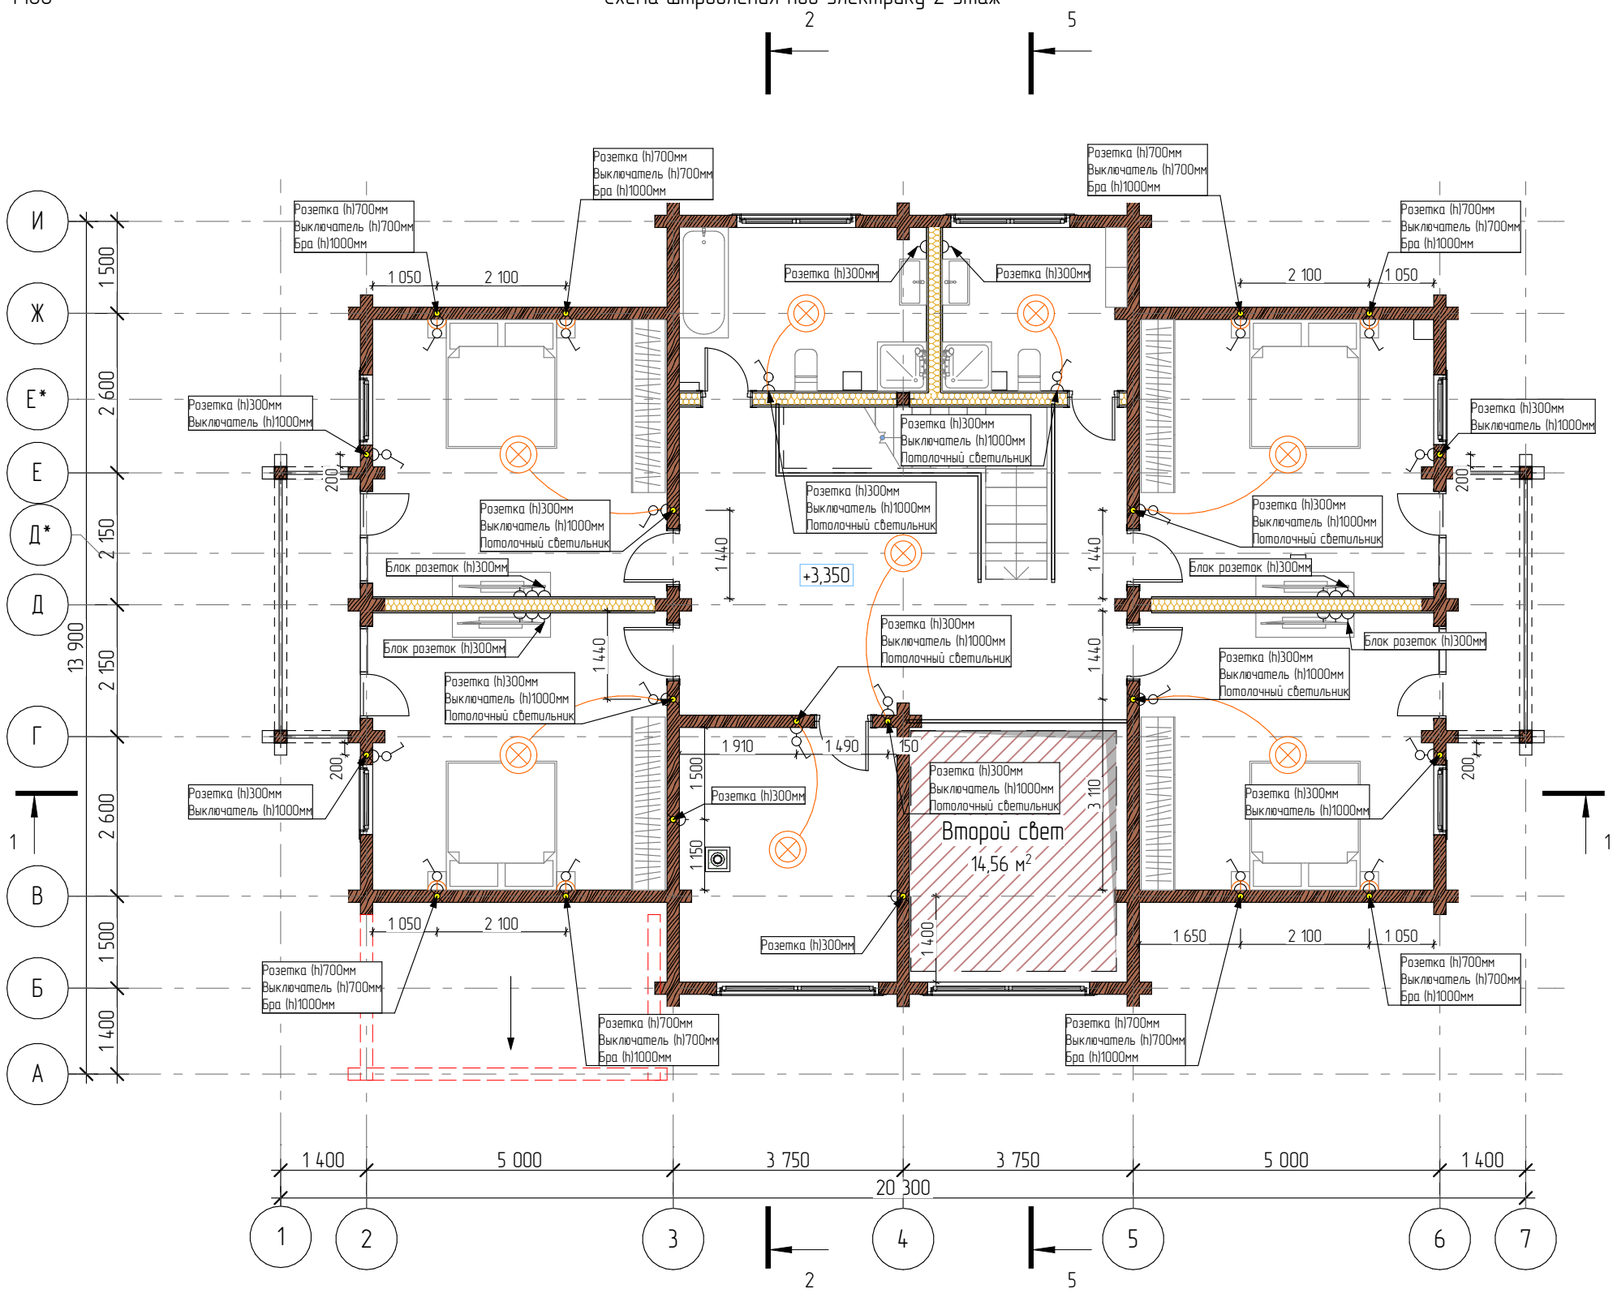

Условные обозначения:	
	Электрическая розетка
	Выключатель одноклавишный
	Подвесной/встраиваемый светильник потолочный
	Бра
1000	Размеры в мм
h=100мм	Размеры в мм от чистого пола

Согласовано:

Взам. инв. №

Подпись и дата

Инв. № подл.

						2021	ДСП № 14.09.2021-КБ
							Адрес: Ленинградская область, Гатчинский муниципальный район, Вырицкое городское поселение, г. п. Вырица, ул. Елизаветинская
Изм.	Кол.уч	Лист	№док.	Подпись	Дата		
							Индивидуальный жилой дом
Архитектор		Салыкова В.Г.					
Заказчик		Кондрашов Д.В.					Схема штробления под электрику

стадия	лист	листов
РП	.2	

АПС ДСК™ ДОМОСТРОИТЕЛЬНЫЙ КОМБИНАТ