






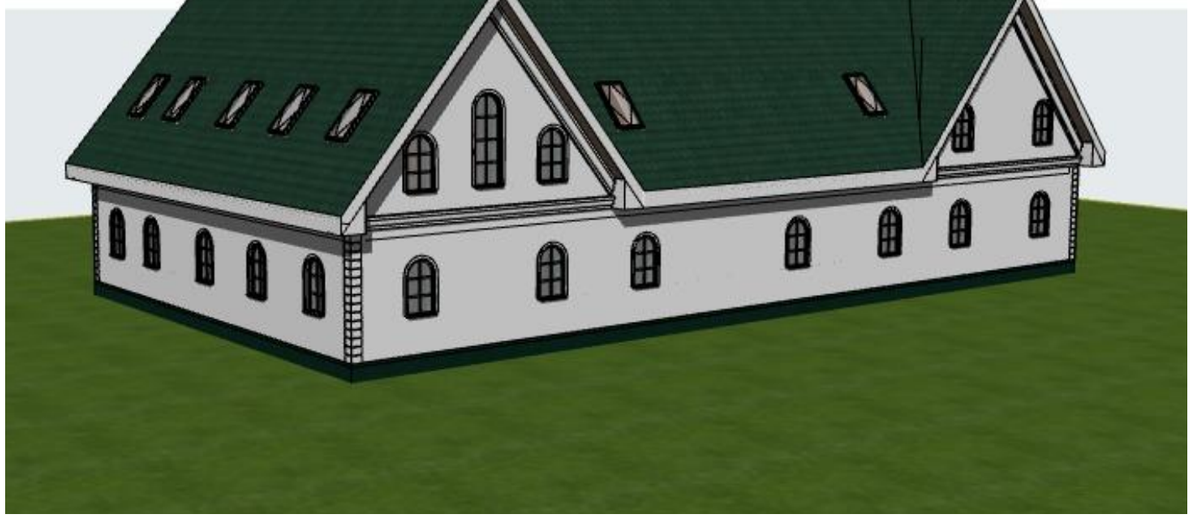

						кадастровый номер Россия			
Изм.	Кол.уч.	Лист	№Док.	Подп.	Дата				
						Индивидуальный жилой дом	Стадия	Лист	Листов
							ЭП	04	
						3D Виды			



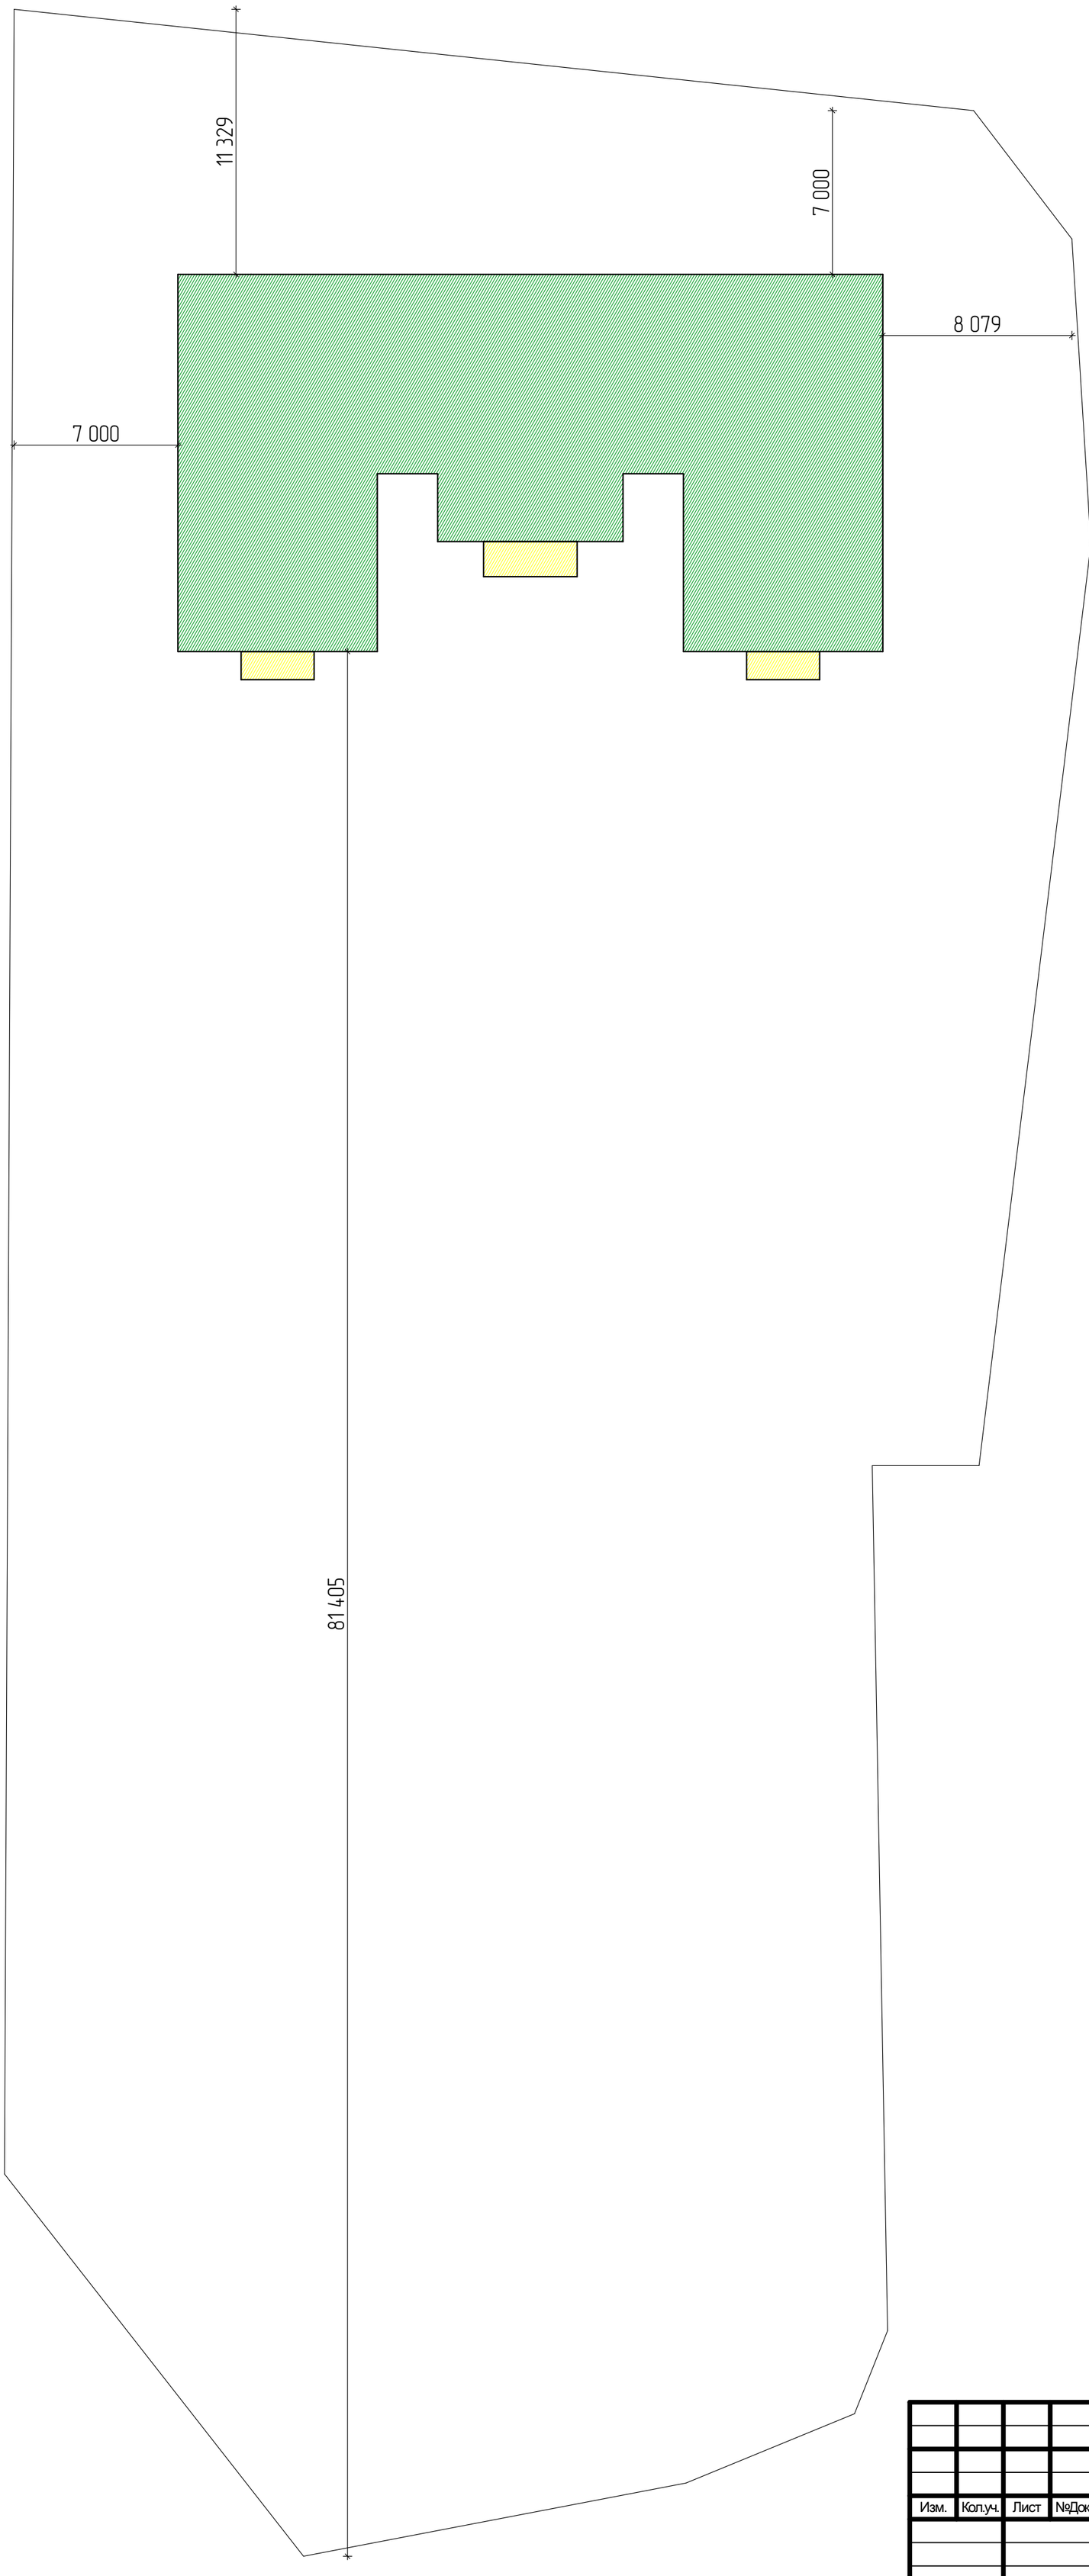


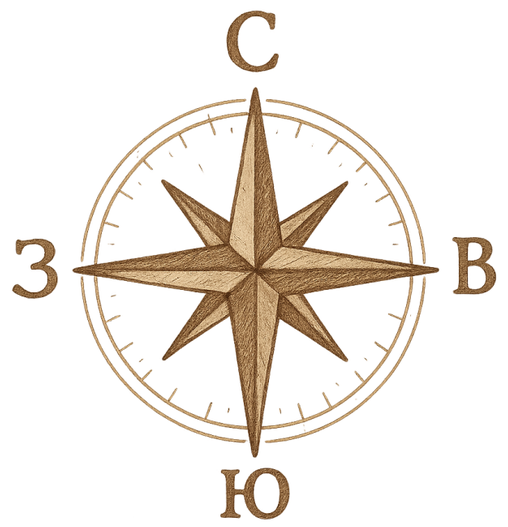


Проектируемый дом

Терраса, крыльцо


Изм.	Кол.уч.	Лист	№Док.	Подп.	Дата	кадастровый номер Россия			
						Индивидуальный жилой дом	Стадия	Лист	Листов
							ЭП	05	
						Схема расположения участка			

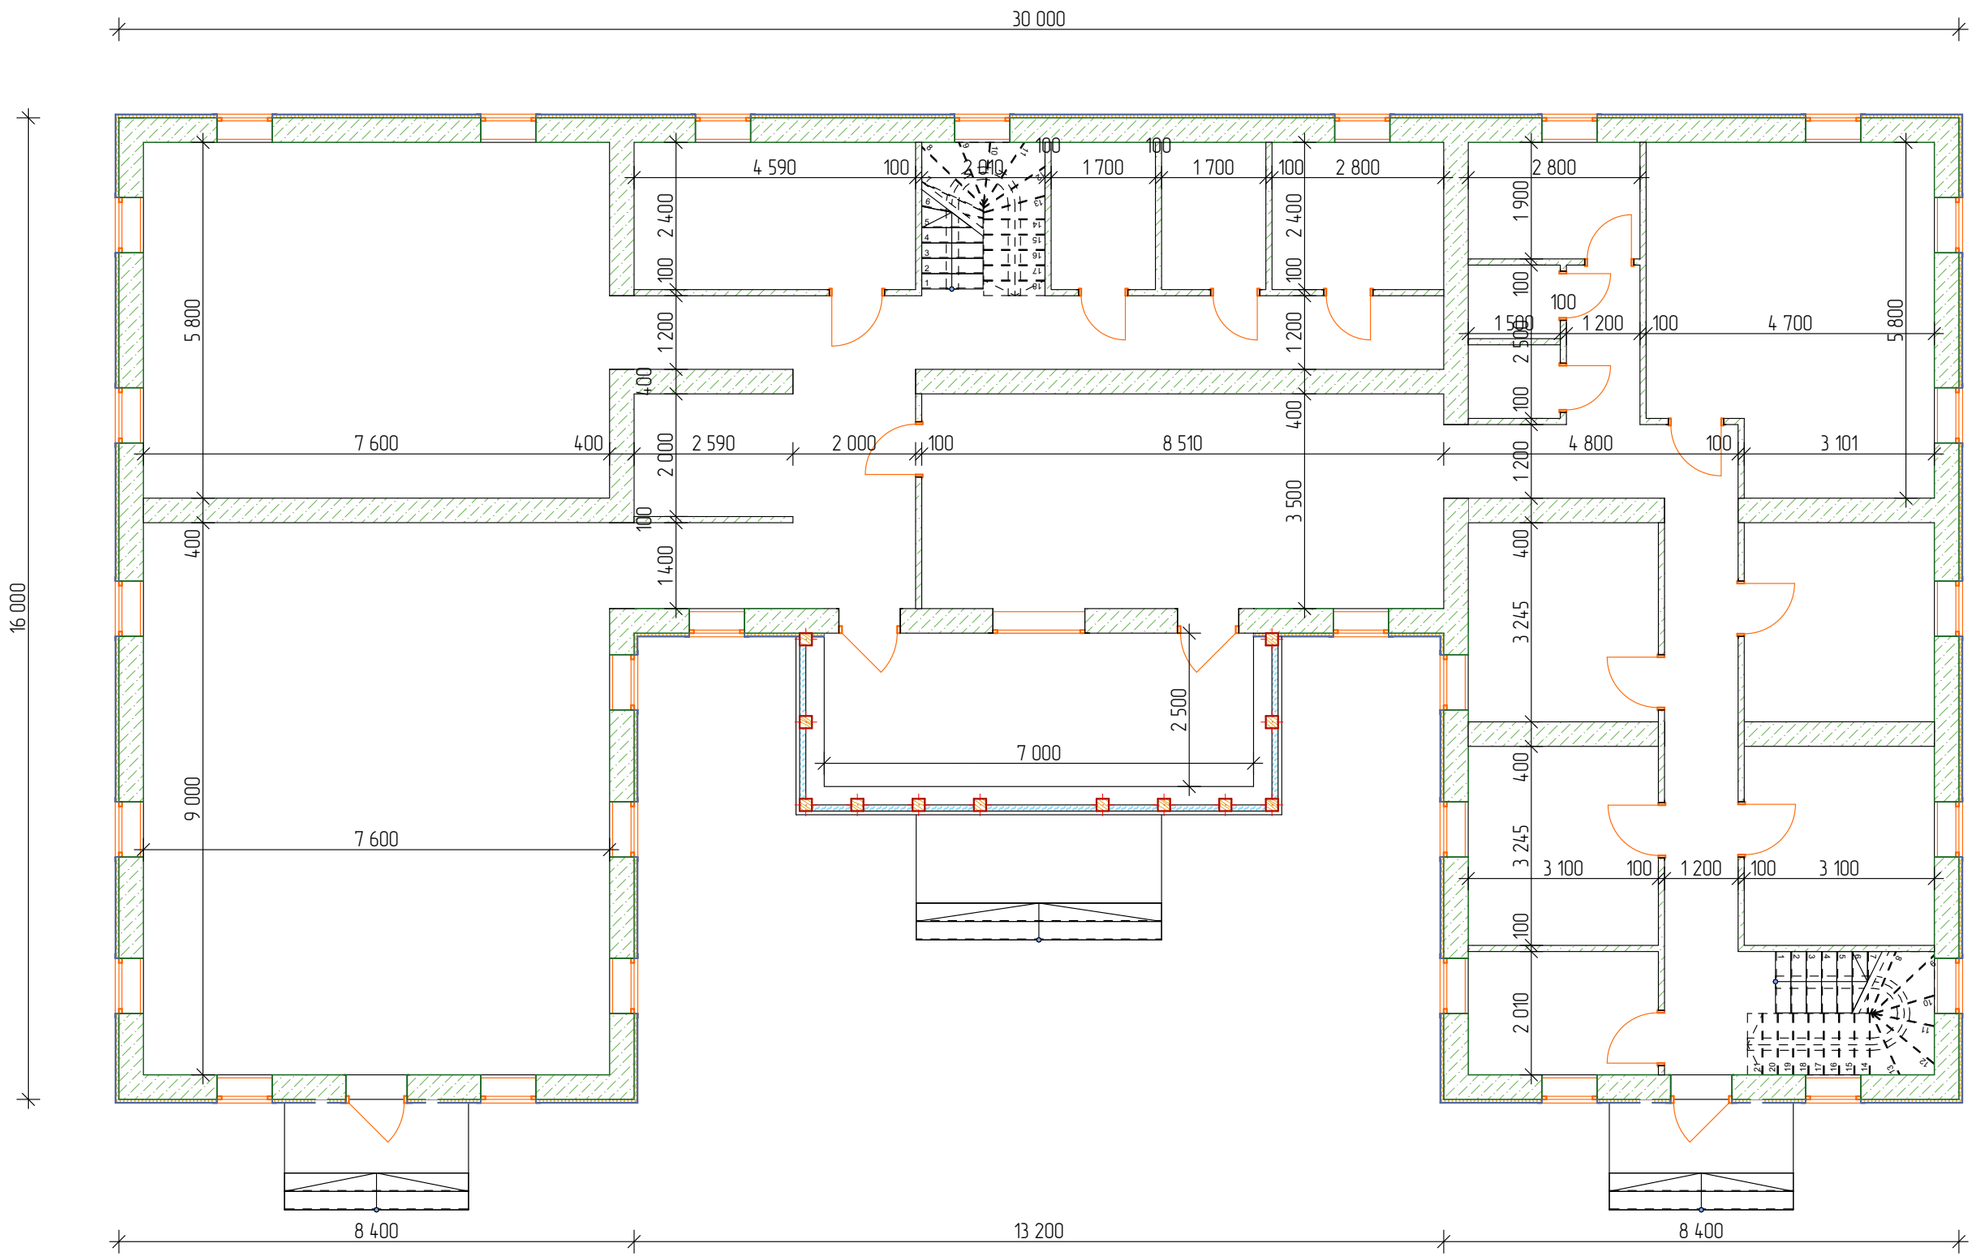


Изм.	Кол.уч.	Лист	№Док.	Подп.	Дата	кадастровый номер Россия			
						Индивидуальный жилой дом	Стадия	Лист	Листов
							ЭП	07	
						План 1 этажа			

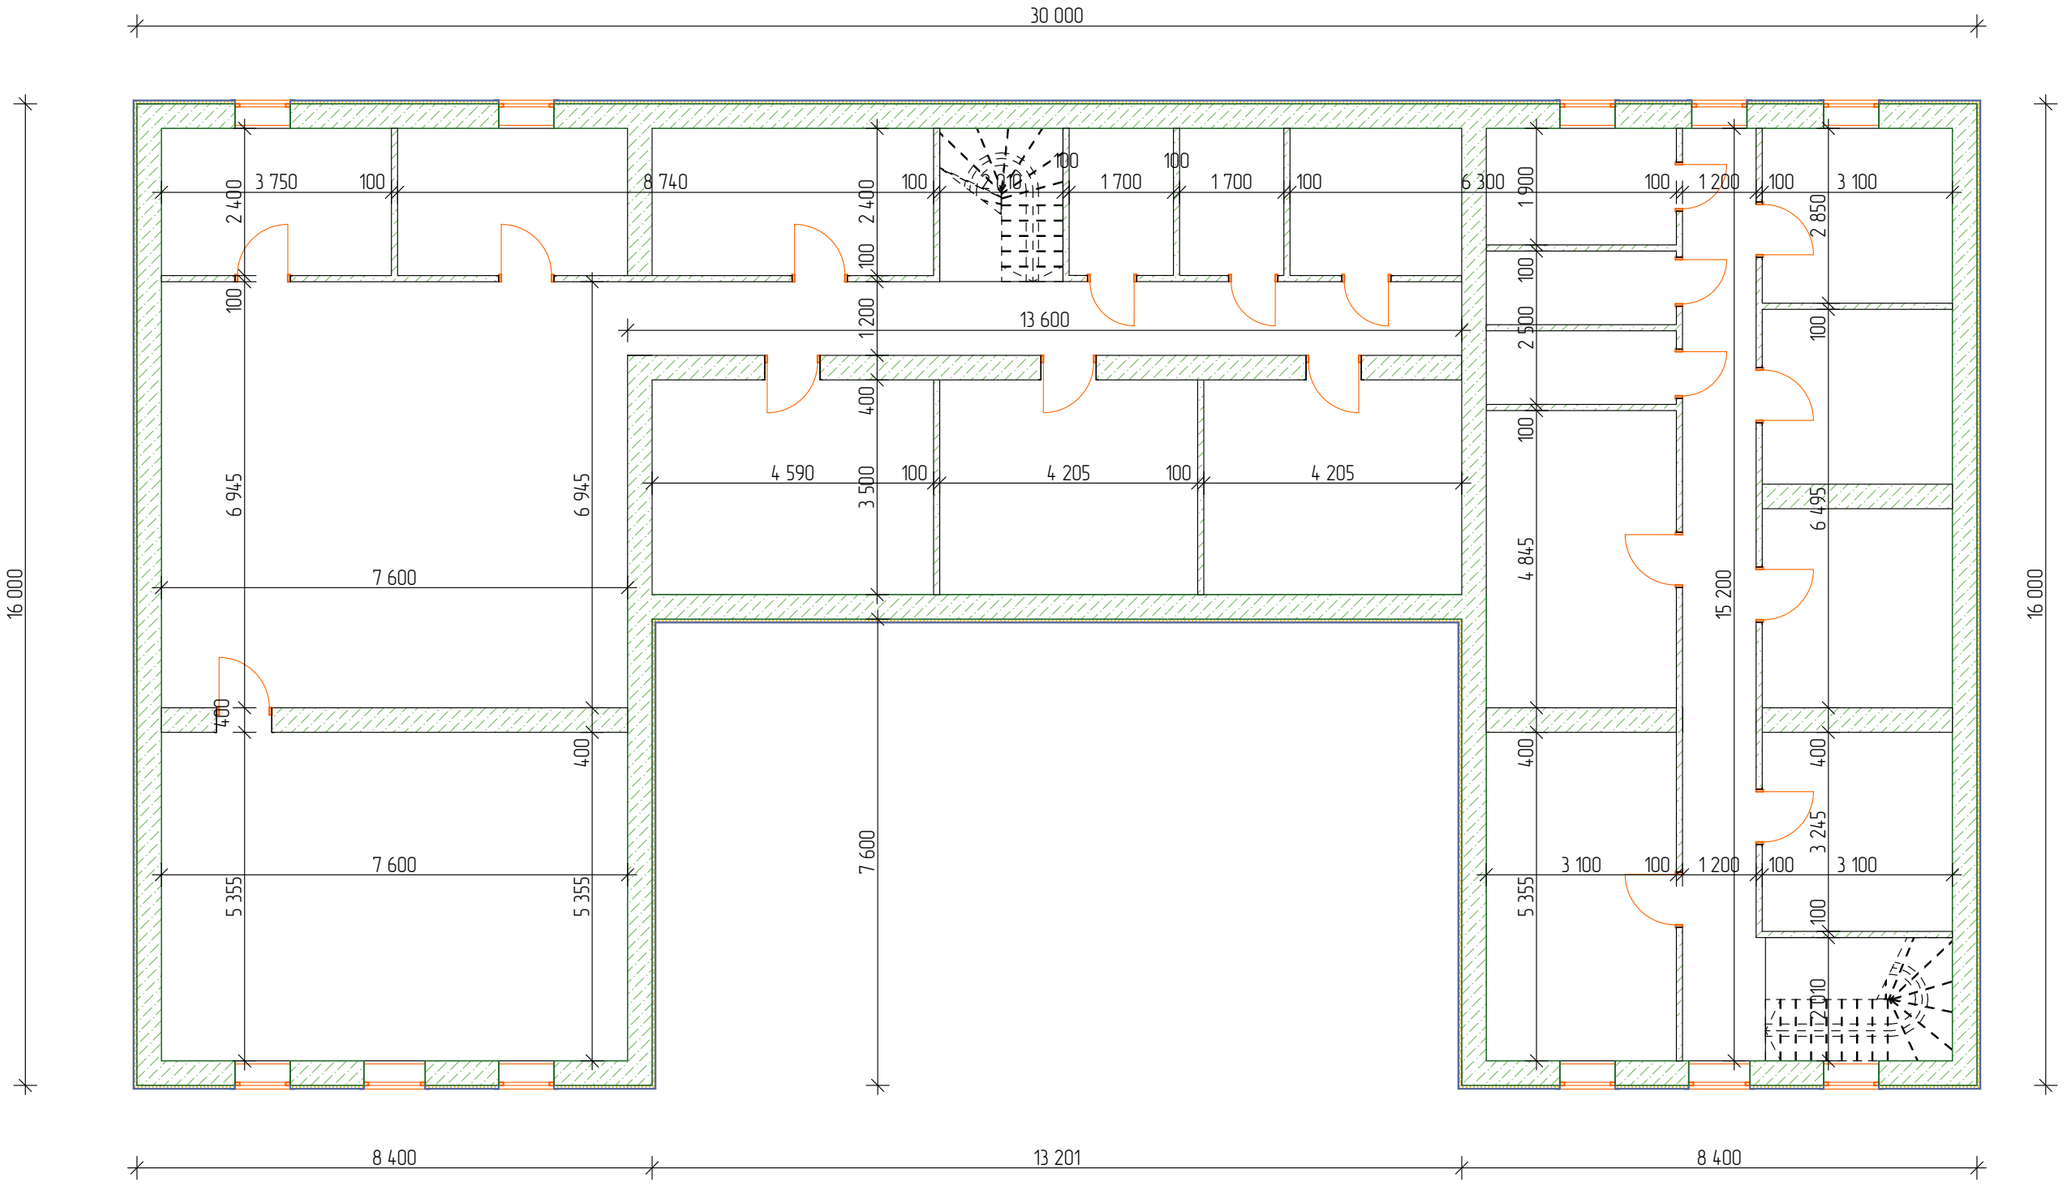

Изм.	Кол.уч.	Лист	№Док.	Подп.	Дата	кадастровый номер Россия			
						Индивидуальный жилой дом	Стадия	Лист	Листов
							ЭП	08	
						План 2 этаж			

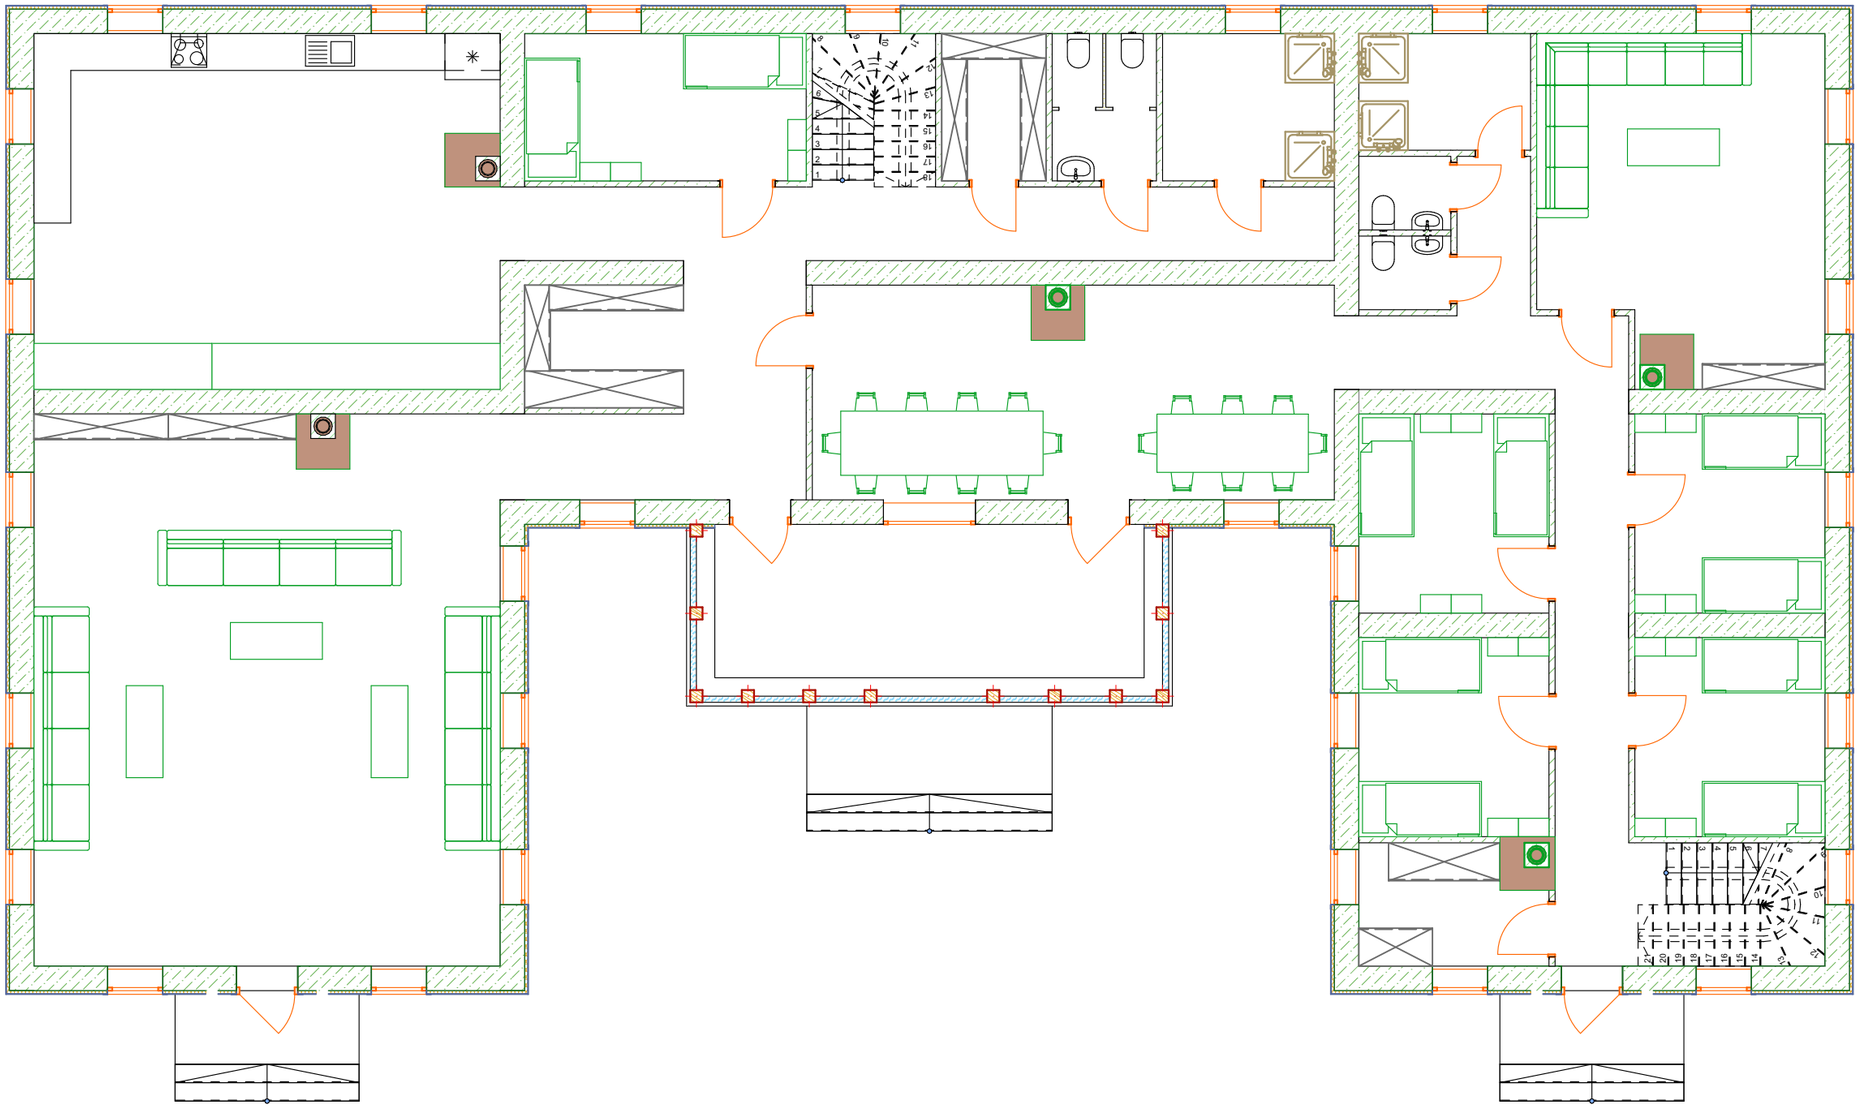

						кадастровый номер Россия	
Изм.	Кол.уч.	Лист	№Док.	Подп.	Дата		
						Индивидуальный жилой дом	Стадия: ЭП; Лист: 24; Листов:
						План расстановки мебели 1 этаж	

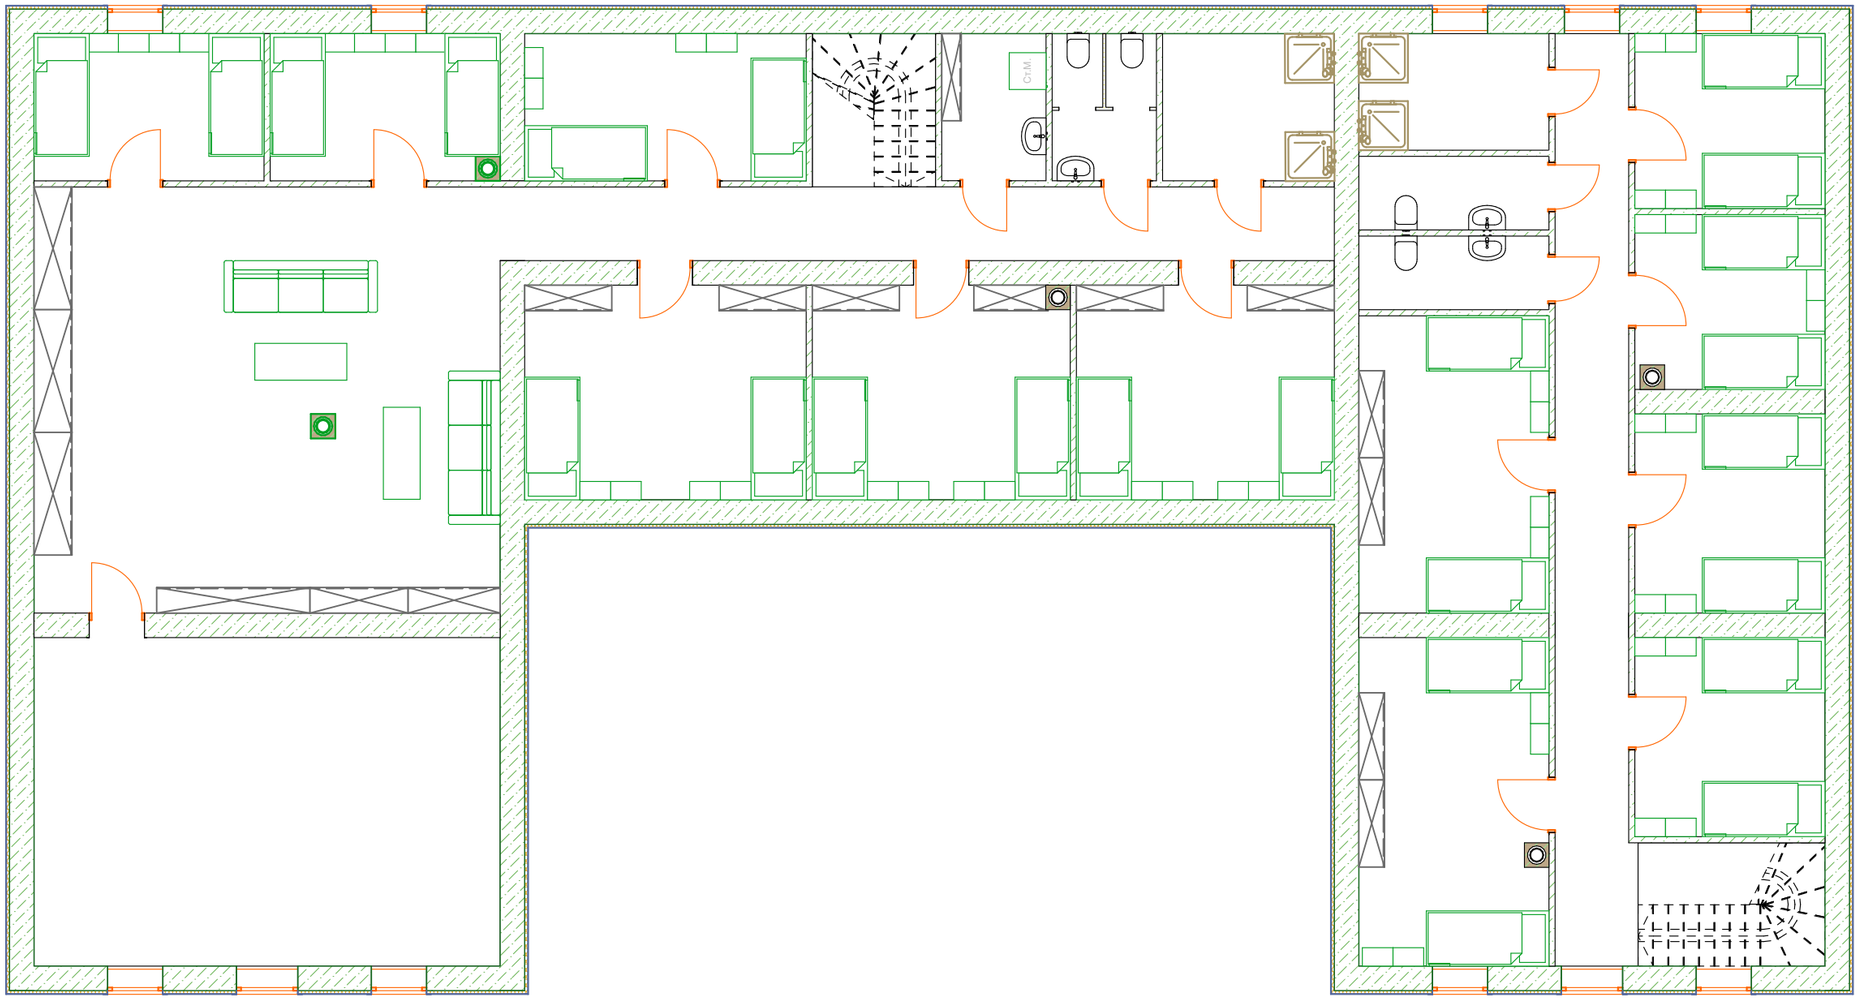


Изм.	Кол.уч.	Лист	№Док.	Подп.	Дата	

кадастровый номер Россия


Индивидуальный жилой дом	Стадия	Лист	Листов
	ЭП	25	
План расстановки мебели 2 этаж			

№	Наименование	Площадь
1	Веранда	17,50
2	Холл	27,26
3	Гардеробная	5,18
4	Гостиная	68,40
5	Кухня	44,08
6	Комната	11,01
7	Кладовая	4,08
8	С/У	4,08
9	Душевая	6,72
10	Лестница	4,62
11	Трапезная	29,79
12	Душевая	5,32
13	СУ	1,80
14	СУ	1,80
15	Гостиная	25,18
16	Холл	19,68
17	Комната	10,06
18	Комната	10,06
19	Комната	10,06
20	Комната	10,06
21	Гардероб	6,23
22	Лестница	6,43
23	Крыльцо	3,60
24	Крыльцо	3,60
25	Крыльцо	6,00
		342,60 м²

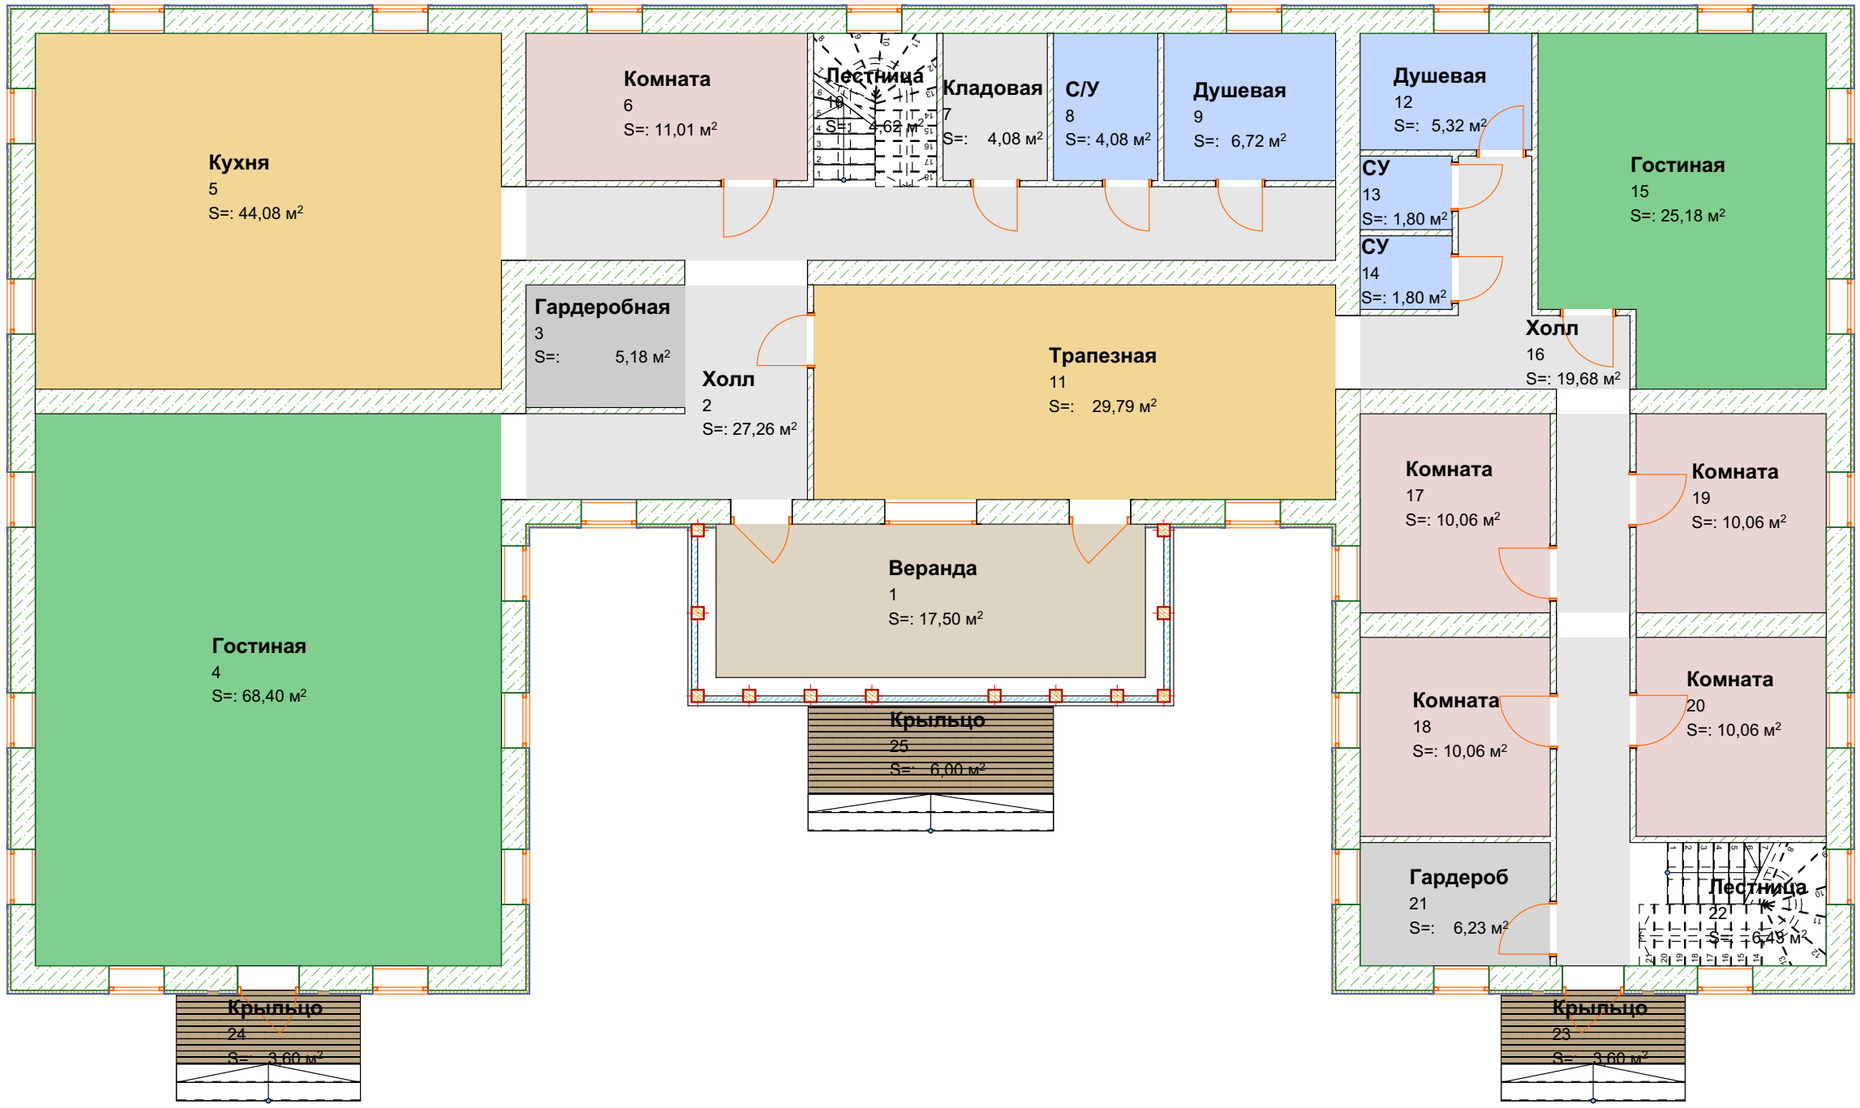

Изм.	Кол.уч.	Лист	№Док.	Подп.	Дата	кадастровый номер Россия			
						Индивидуальный жилой дом	Стадия	Лист	Листов
							ЭП	26	
						Экспликация помещений 1- го этажа			

№	Наименование	Площадь
26	Холл	15,84
27	Домашняя церковь	40,70
28	Гостиная/ библиотека	52,78
29	Комната	9,00
30	Комната	9,00
31	Комната	11,02
32	Комната	16,06
33	Комната	14,72
34	Комната	14,72
35	Прачечная	4,08
36	С/У	4,08
37	Душевая	6,72
38	Душевая	5,89
39	С/У	3,72
40	С/У	3,72
41	Комната	8,83
42	Комната	8,84
43	Комната	10,06
44	Комната	10,06
45	Комната	15,02
46	Комната	16,60
47	Холл	18,24
		299,70 м²

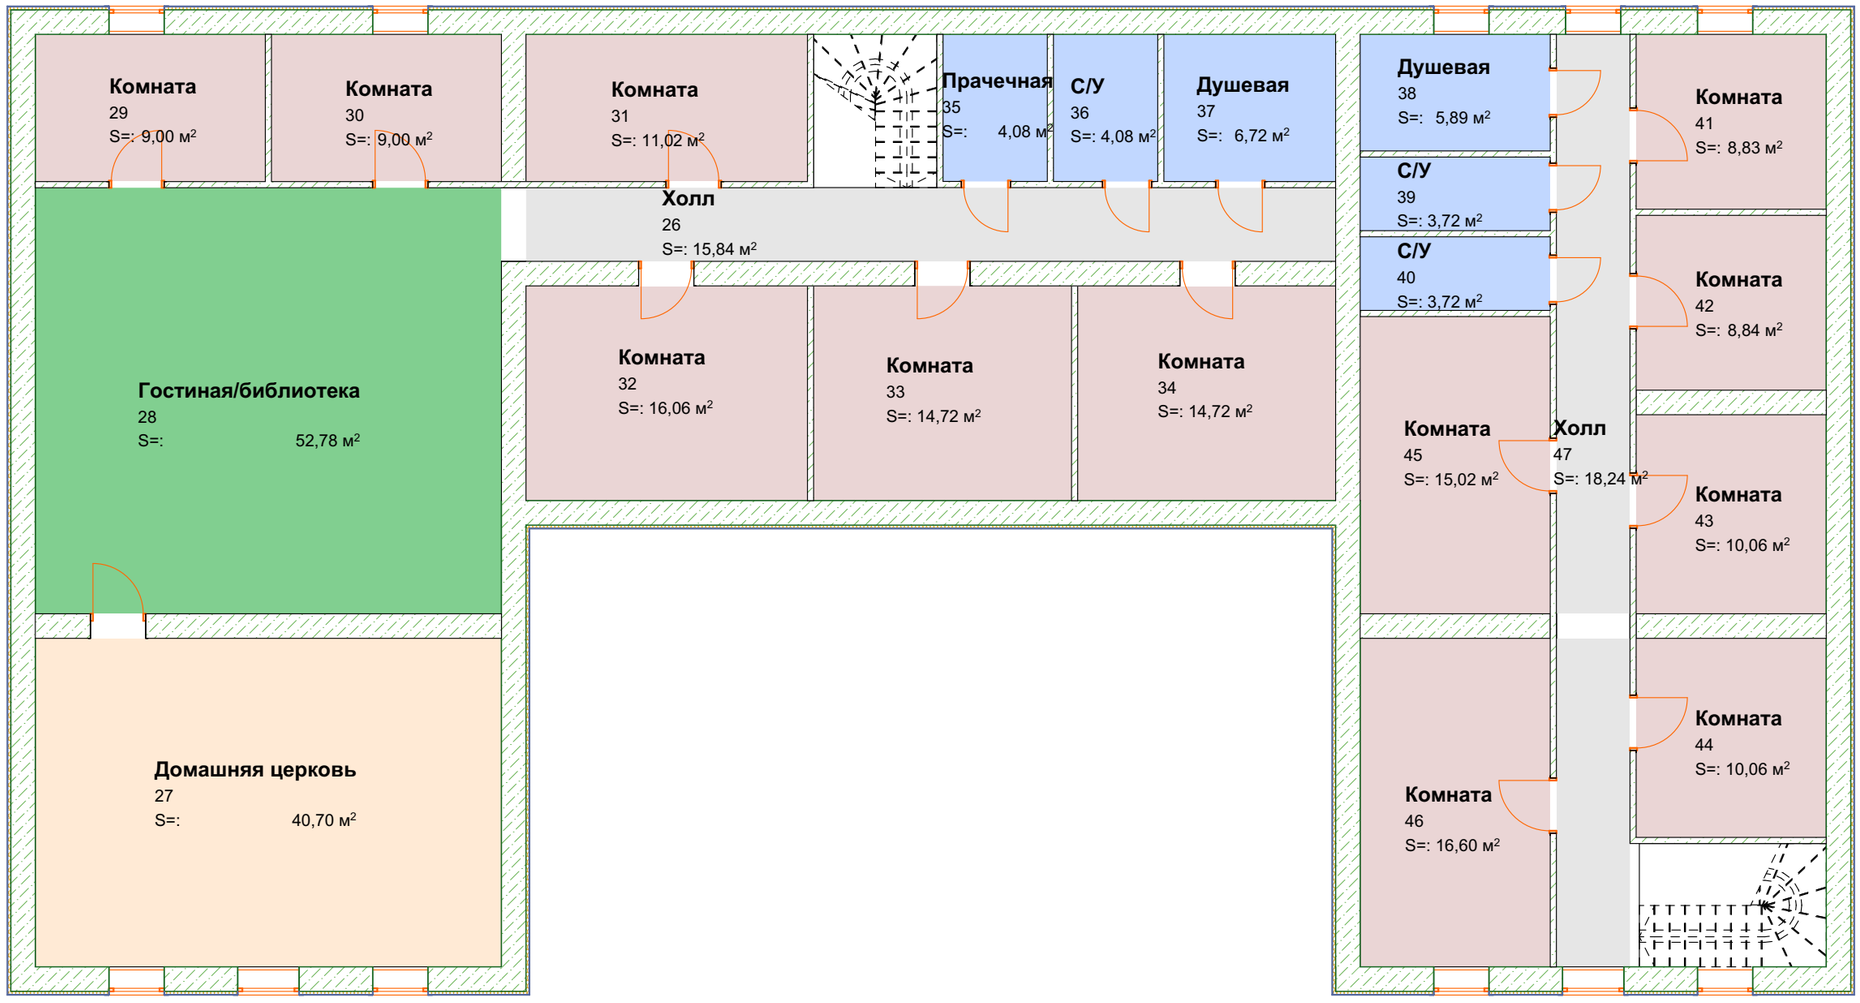


Изм.	Кол.уч.	Лист	№Док.	Подп.	Дата	кадастровый номер Россия			
						Индивидуальный жилой дом	Стадия	Лист	Листов
							ЭП	27	
						Экспликация помещений 2- го этажа			




						кадастровый номер Россия
Изм.	Кол.уч.	Лист	№Док.	Подп.	Дата	
						Индивидуальный жилой дом
						Фасад в осях 1-5


Стадия	Лист	Листов
ЭП	29	

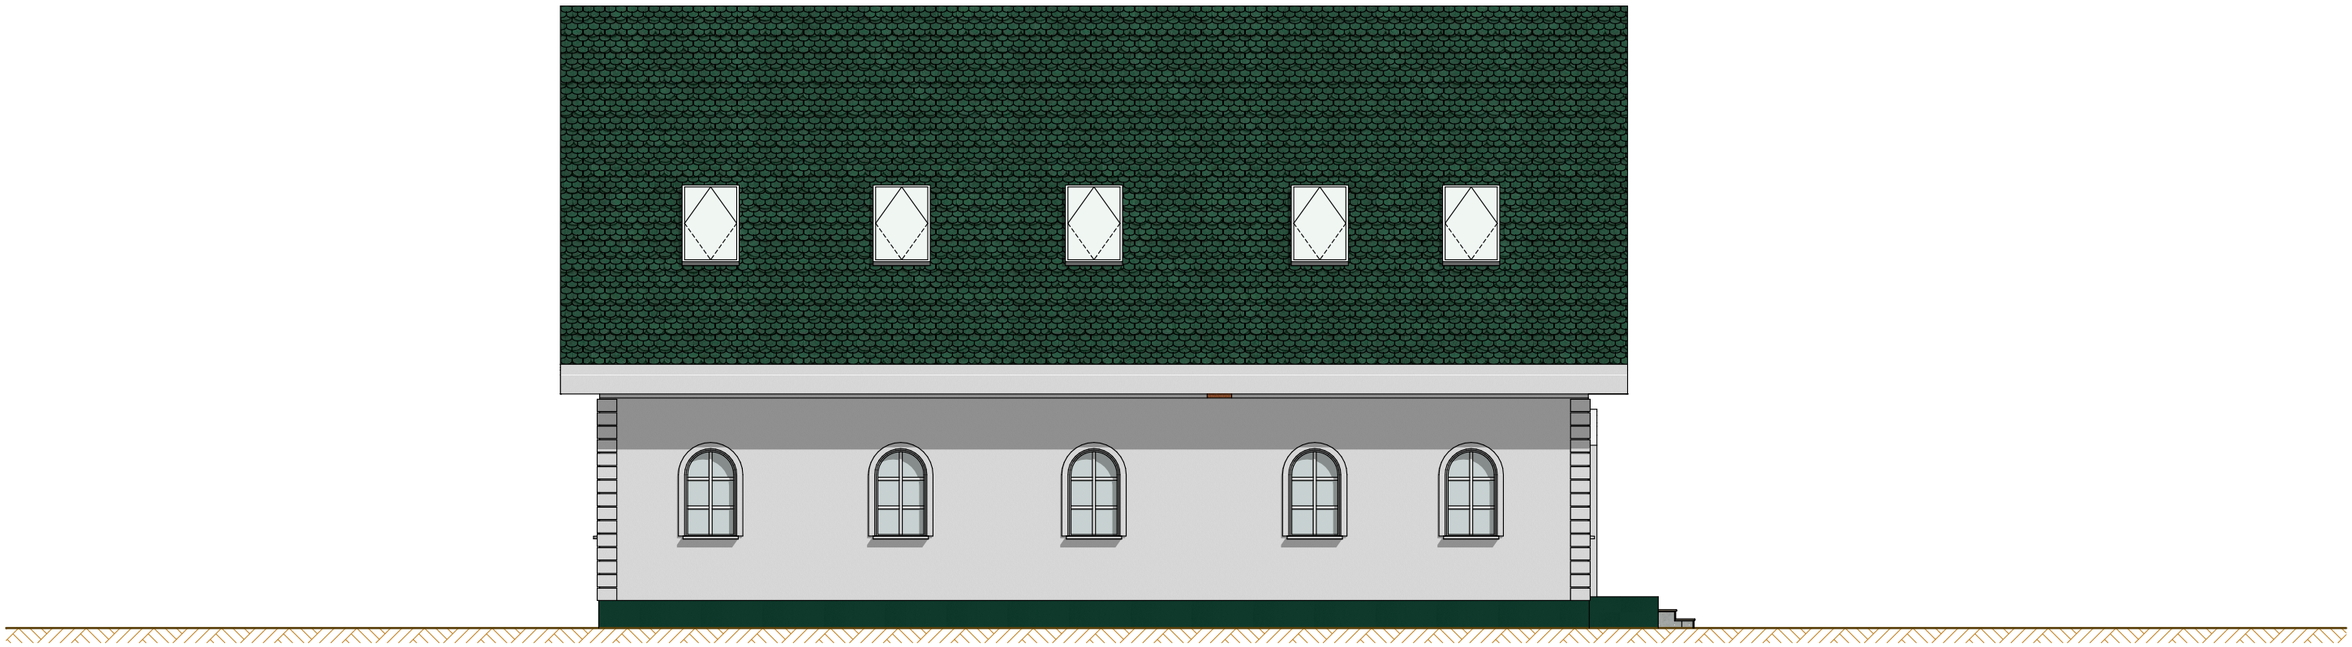

Изм.	Кол.уч.	Лист	№Док.	Подп.	Дата	кадастровый номер Россия			
						Индивидуальный жилой дом	Стадия	Лист	Листов
							ЭП	30	
						Фасад в осях В-А			

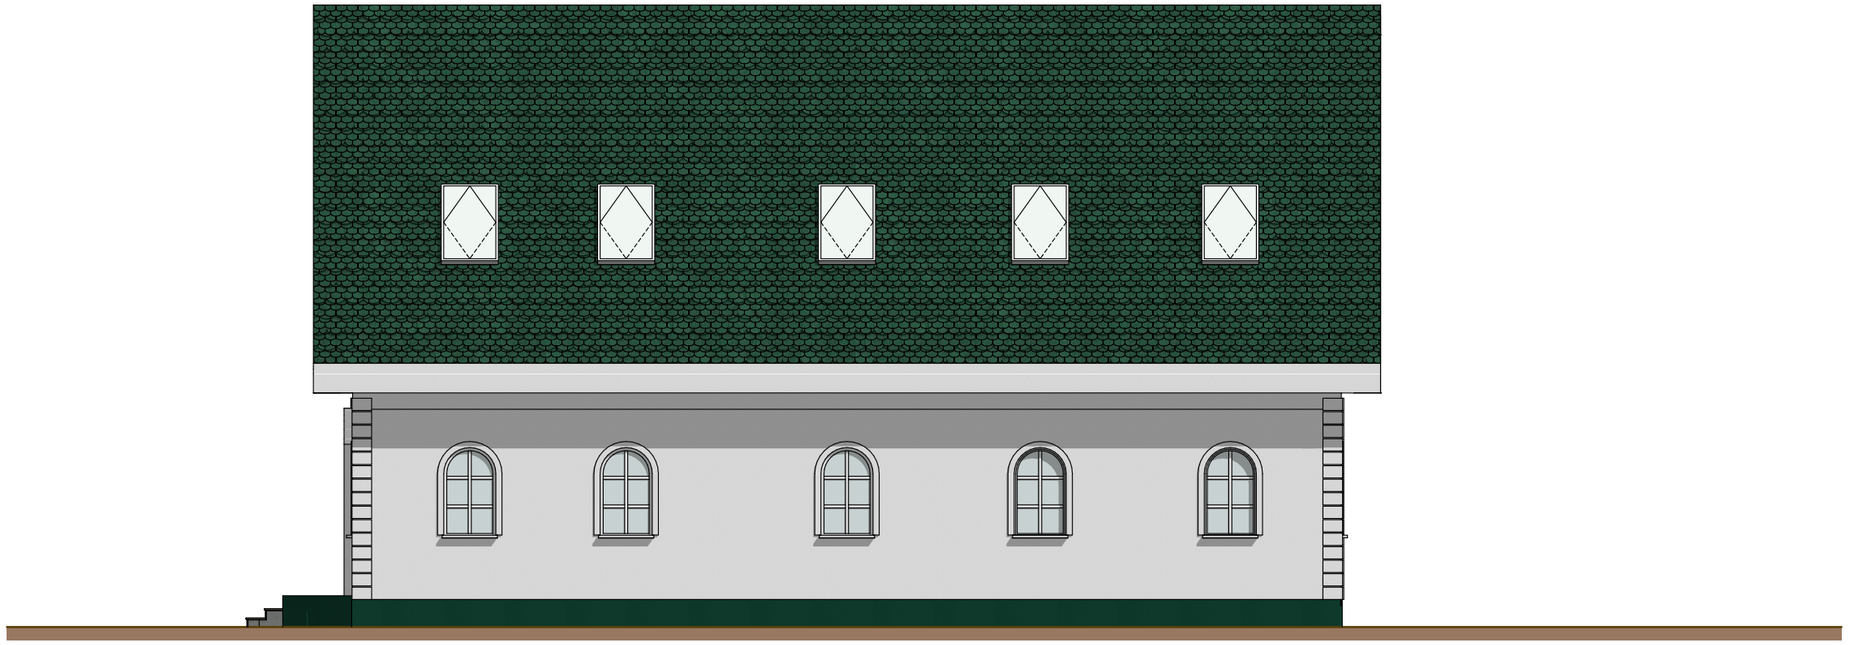

Изм.	Кол.уч.	Лист	№Док.	Подп.	Дата	кадастровый номер Россия			
						Индивидуальный жилой дом	Стадия	Лист	Листов
							ЭП	31	
						Фасад в осях А-В			

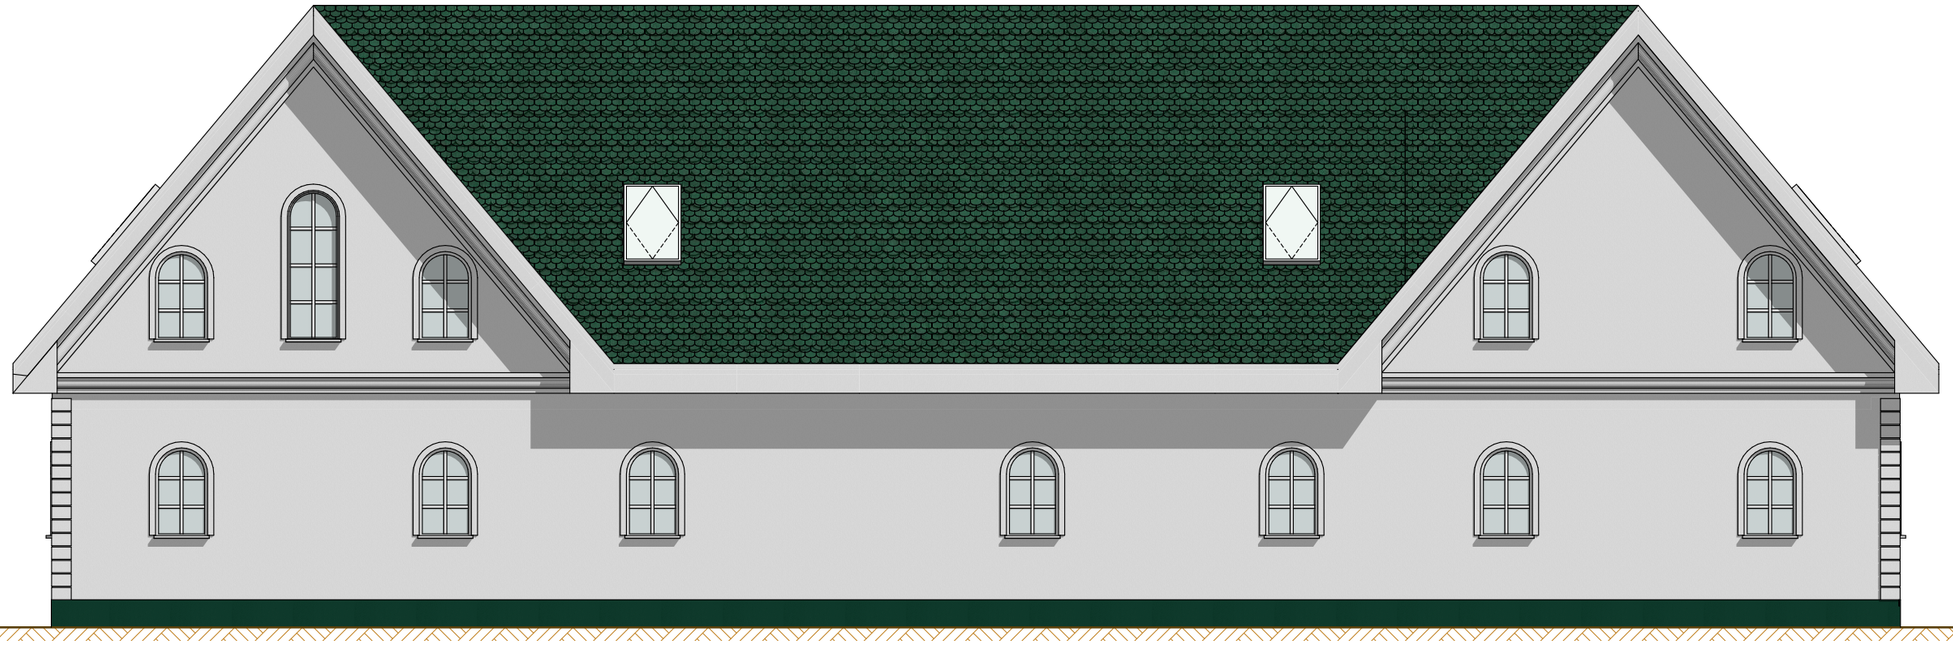

Изм.	Кол.уч.	Лист	№Док.	Подп.	Дата	кадастровый номер Россия			
						Индивидуальный жилой дом	Стадия	Лист	Листов
							ЭП	32	
						Фасад в осях 5-1			