ПРОЕКТНАЯ ДОКУМЕНТАЦИЯ

Индивидуальный жилой дом

кадастровый номер Россия

#ID Проекта



РОССИЯ
2026

Ведомость листов	
Наименование	Лист
Обложка	
СОДЕРЖАНИЕ	01
Ведомость материалов - фундамент	02
Ведомость материалов - стены	03
Ведомость материалов - перекрытия	04
Ведомость материалов - кровля	05
Экспликация всех помещений	06
Генеральный план	07
ПЗ Генеральный план	08
3D Виды	09
ПЗ Фундамент	10
ПЗ Свайный фундамент (забивные сваи)	11
План свайного поля	12
План фундамента (ростверк)	13
Чертеж каркаса ростверка№ Пол 1.01 #1	14
Наружные сети	15
План коммуникаций	16
Ведомость материалов ниже отм 0.000	17
ПЗ Стены	18
ПЗ Каркасный дом	19
План на отм. ±0.000	20
План на отм +3.100	21
Ведомасть материаов стен	22
Каталог дверных проемов	23
Каталог оконных проемов	24
Маркировка оконных проемов первого этажа	25
Маркировка дверных проемов первого этажа	26
Сводная ведомость проемов	27
Разрез 1 - 1	28
Разрез 2 - 2	29
Разрез по стене	30
ПЗ - Деревянное перекрытие	31
План перекрытия +0,000	32
Чертеж каркаса перекрытия № Пол (дом) #1	33
Чертеж каркаса перекрытия № Пол (Терраса) #1	34
План перекрытий на отм 3,100	35
Чертеж каркаса перекрытия № Чердачное перек...	36
Ведомость материалов перекрытие	37
ПЗ - Скатная кровля	38
План кровли	39
Ведомость кровельного пирога	40
Схема расположения стропил	41
3Д Вид стропильной системы	42

Ведомость листов	
Наименование	Лист
Ведомость материалов (стропильная система)	43
План расстановки мебели 1 этаж	44
Экспликация помещений 1- го этажа	45
Фасад в осях 1-6	46
Фасад в осях Ж-А	47
Фасад в осях А-Ж	48
Фасад в осях 6-1	49
Ведомость отделки фасада	50
Схема расположения стен 1-го этажа	51
Схема расположения каркасов чердака	52
3Д Вид каркаса	53
3Д вид Каркаса	54
Чертеж каркаса стен № КС 1.01 #1	55
Чертеж каркаса стен № КС 1.02 #1	56
Чертеж каркаса стен № КС 1.03 #1	57
Чертеж каркаса стен № КС 1.04 #1	58
Чертеж каркаса стен № КС 1.05 #1	59
Чертеж каркаса стен № КС 1.06 #1	60
Чертеж каркаса стен № КС 1.07 #1	61
Чертеж каркаса стен № КС 1.08 #1	62
Чертеж каркаса стен № КС 1.09 #1	63
Чертеж каркаса стен № КС 1.10 #1	64
Чертеж каркаса стен № КС 1.11 #1	65
Чертеж каркаса стен № КС 2.01 #1	66
Чертеж каркаса стен № КС 2.02 #1	67
Чертеж каркаса стен № КС 2.03 #1	68
Чертеж каркаса стен № КС 2.04 #1	69
Чертеж каркаса стен № КС 2.05 #1	70

Сваи забивные	
Наиенование	Кол-во,шт
Свая 200х200	42
	42

Конструкция пола				
	Наименование	Толщина, мм	Объем, м3	Площадь,м2
Пол (дом)				
	Дерево - Черновой настил	25	2,53	101,00
	Изоляция - Минеральная Мягкая	195	19,53	101,00
	Контробрешётка	40	4,04	101,00
	Лист OSB	22	1,97	101,00
	Мембрана - ветрозащитная диффузионная	1	0,10	101,00
	Мембрана - Пароизоляция	2	0,20	101,00
	Паркет	20	1,79	101,00
Пол (Терраса)				
	Дерево - Черновой настил	25	0,48	19,00
	Изоляция - Минеральная Мягкая	195	3,70	19,00
	Контробрешётка	40	0,75	19,00
	Лист OSB	22	0,40	19,00
	Мембрана - ветрозащитная диффузионная	1	0,02	19,00
	Мембрана - Пароизоляция	2	0,04	19,00
	Паркет	20	0,36	19,00

Коммуникации		
Назначение	Строительный Материал	Длина, мм
Водопровод	Труба ПЭ100 SDR11 d40×3,7 (PN16)	3 167
Канализация	Труба ПВХ SN4 d110×3,2 (канализация)	22 463

Стены - Каркасный дом			
Этаж	Строительный материал	Объем, м3	Площадь, м2
1-й этаж, Внутренние стены			
	Гипсокартон	0,81	81,88
		0,81 м³	
	Изоляция - Минеральная Жесткая	8,42	43,18
		8,42 м³	
	Лист OSB	0,81	82,47
		0,81 м³	
1-й этаж, Наружные стены			
	Гибкая плитка под кирпич(фасадная)	0,52	102,73
		0,52 м³	
	Гипсокартон	0,90	90,10
		0,90 м³	
	Изоляция - Минеральная Жесткая	19,33	99,13
		19,33 м³	
	Контробрешётка	7,74	193,56
		7,74 м³	
	Лист OSB	1,92	192,33
		1,92 м³	
	Мембрана - ветрозащитная диффузионная	0,25	101,69
		0,25 м³	
	Мембрана - Пароизоляция	0,24	96,81
		0,24 м³	
1-й этаж, Перегородки			
	Гипсокартон	0,94	90,54
		0,94 м³	
	Изоляция - Минеральная Жесткая	4,48	46,98
		4,48 м³	
	Лист OSB	0,94	91,14
		0,94 м³	
Чердак, Внутренние стены			
	Воздушная Прослойка	5,92	31,08
		5,92 м³	
	Гипсокартон	0,58	57,04
		0,58 м³	
	Лист OSB	0,58	57,16
		0,58 м³	

Чердак, Наружные стены			
	Гибкая плитка под кирпич(фасадная)	0,13	26,90
		0,13 м³	
	Гипсокартон	0,27	26,78
		0,27 м³	
	Изоляция - Минеральная Жесткая	5,24	26,90
		5,24 м³	
	Контробрешётка	2,14	53,80
		2,14 м³	
	Лист OSB	0,54	53,80
		0,54 м³	
	Мембрана - ветрозащитная диффузионная	0,06	26,90
		0,06 м³	
	Мембрана - Пароизоляция	0,06	26,90
		0,06 м³	
		62,82 м³	

Ведомость материалов на фасад			
Наиме...	Компоненты		Объем, м3
	Толщина, мм	Площадь, м2	
Изоляция - Минеральная Жесткая			
	95	46,98	4,48
	195	169,21	32,99

Изм.	Кол.уч.	Лист	№Док.	Подп.	Дата	#ID Проекта		
						кадастровый номер Россия		
						Индивидуальный жилой дом	Стадия: #Стадия Проекта	Лист: 03 / Листов:
Разраб.								
ГАП								
Ведомость материалов - стены								

н Ведомость перекрытий (Каркасный Дом)	
Этаж	Объем, м3
1-й этаж, Пол (дом)-01	
	0,18
1-й этаж, Пол (дом)-02	
	1,62
1-й этаж, Пол (дом)-03	
	0,00
1-й этаж, Пол (дом)-04	
	0,56
1-й этаж, Пол (дом)-05	
	0,00
1-й этаж, Пол (Терраса)-01	
	0,18
1-й этаж, Пол (Терраса)-02	
	0,36
1-й этаж, Пол (Терраса)-03	
	0,00
Чердак, Чердачное перекрытие-01	
	0,18
Чердак, Чердачное перекрытие-02	
	1,62
Чердак, Чердачное перекрытие-03	
	0,00
Чердак, Чердачное перекрытие-04	
	0,56
Чердак, Чердачное перекрытие-05	
	0,00
	5,26 м³

Состав кровли		
Элемент	Наименование	Площадь, м2
Кровля дома		
	Мембрана - Водонепроницаемая	167,84
	Черепица - Черепица	168,16
	Шаговая обрешетка 25*250	168,08


Стропильная система		
Уровень	**Наименование**	Объем, м3
Чердак		
	Контробрешетка 50х50	0,84
	Коньковый брус 200х100	0,27
	Мауэрлат 100х200	0,54
	Стропильная нога 200х50	2,52
		4,17 м³


Ведомость кровельного материала	
Наименование	Площадь, м2
Кровля дома	167,82
	167,82 м²


ВЕДОМОСТЬ НА УТЕПЛИТЕЛЬ (кровля)				
	Наименование	Компоненты		
		Толщина, мм	Объем, м3	Площадь, м2
Чердак				
	Изоляция - Минеральная Жесткая	195	5,24	26,90
	Изоляция - Минеральная Мягкая	195	19,70	101,00

						#ID Проекта	
						кадастровый номер Россия	
Изм.	Кол.уч.	Лист	№Док.	Подп.	Дата		
Разраб.						Индивидуальный жилой дом	Стадия: #Стадия Проекта; Лист: 05; Листов:
ГАП							
Ведомость материалов - кровля							

Этаж	№	Наименование	Площадь, м2
1-й этаж, ОБЩАЯ ПЛОЩАДЬ			
	1	Холл	13,15
	2	Кухня-гостиная	22,40
	3	Спальня	9,72
	4	Спальня	12,69
	5	Спальня	11,53
	6	С/У	3,36
	7	С/У	4,86
	8	Котельная	5,44
			83,15 м²
1-й этаж, Транзитные Помещения			
	9	Крыльцо	18,42
			18,42 м²
			101,57 м²

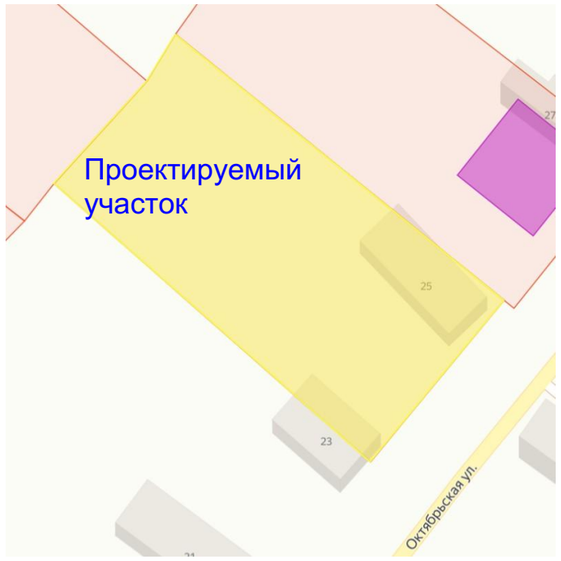

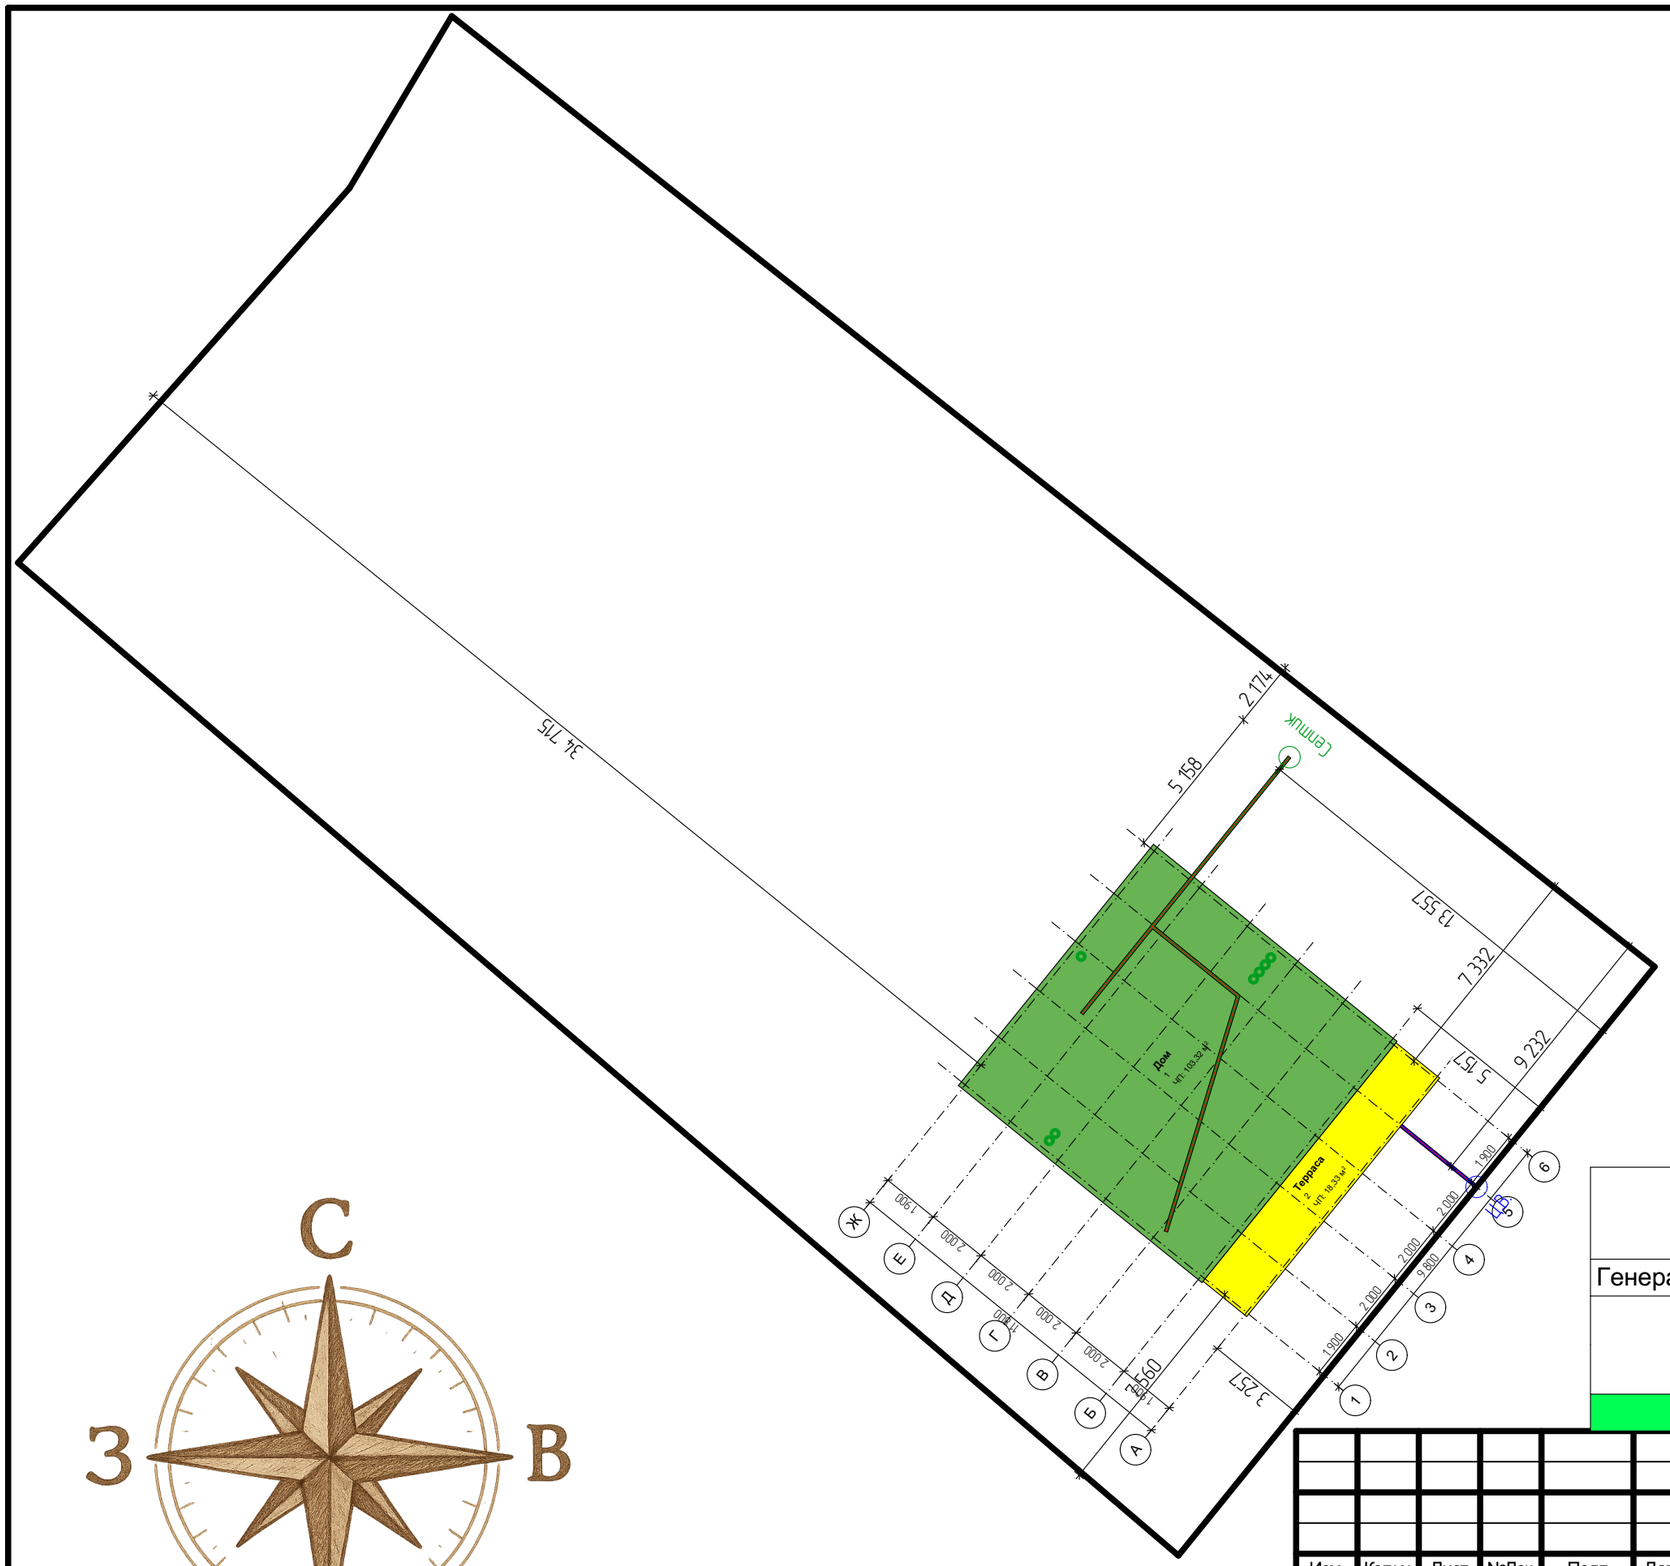

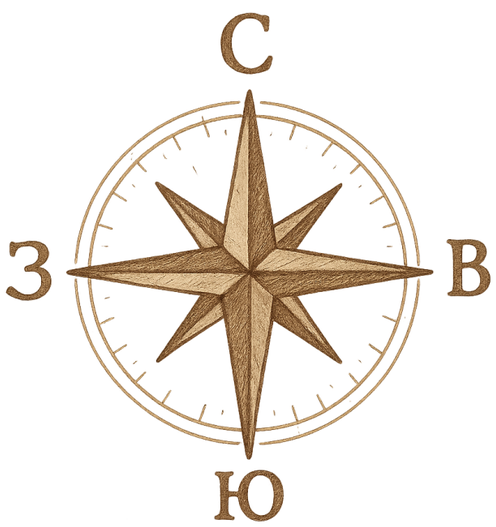

Проектируемый дом

Терраса

	№	Наименование	Площадь, м2
Генеральный план			
	1	Дом	103,32
	2	Терраса	18,33
			121,65 м²

						#ID Проекта
						кадастровый номер Россия
Изм.	Кол.уч.	Лист	№Док.	Подп.	Дата	
Разраб.						Индивидуальный жилой дом
ГАП						
Генеральный план						

Стадия	Лист	Листов
#Стадия Проекта	07	

	№	Наименование	Площадь, м2
Генеральный план			
	1	Дом	103,32
	2	Терраса	18,33
			121,65 м²

Пояснительная записка к генеральному плану

Генеральный план разработан для земельного участка, расположенного по адресу: кадастровый номер Россия.

При проектировании генерального плана соблюдены требования градостроительного и земельного законодательства Российской Федерации, а также положения СП 42.13330.2016 «Градостроительство. Планировка и застройка городских и сельских поселений». Согласно нормативам, минимальные отступы от границ земельного участка для индивидуального жилого дома должны составлять:

- от красной линии улицы – не менее 5 м;
- от границы соседнего земельного участка – не менее 3 м;
- от хозяйственных построек – не менее 1 м;
- от деревьев – не менее 4 м;
- от кустарников – не менее 1 м.

Размещение проектируемого жилого дома на участке выполнено с учетом указанных требований, а также с обеспечением удобного подъезда, инсоляции и рационального использования территории.


Вынос осей здания в натуру осуществляется геодезическими методами. На основании утверждённого генерального плана геодезист выполняет закрепление основных осей дома на местности с использованием реперов и обноски. При этом:

- на площадке устанавливаются обноски за пределами котлована;
- на обносках закрепляются гвозди/метки, соответствующие пересечению осей здания;
- натягиваются шнуры, по которым производится разметка фундамента;
- все размеры сверяются с генеральным планом и рабочей документацией.

Таким образом, проектируемое здание расположено на участке в соответствии с нормативными требованиями и может быть реализовано без нарушений действующих правил застройки.





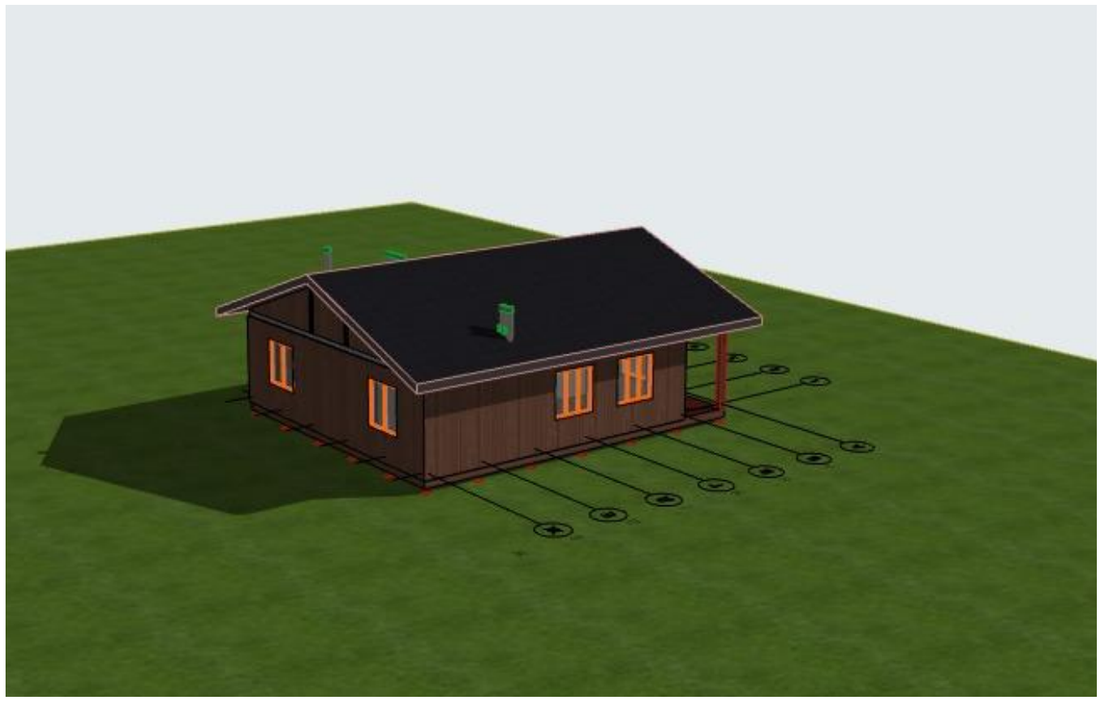

						#ID Проекта		
						кадастровый номер Россия		
Изм.	Кол.уч.	Лист	№Док.	Подп.	Дата			
Разраб.						Индивидуальный жилой дом	Стадия	Лист	Листов
ГАП							#Стадия Проекта	09	
3D Виды									

Пояснительная записка по устройству фундаментов

Фундаменты здания выполняются в соответствии с проектной документацией и действующими строительными нормами:

- СП 70.13330.2012 «Несущие и ограждающие конструкции»,
- СП 63.13330.2018 «Бетонные и железобетонные конструкции»,
- СП 28.13330.2017 «Защита строительных конструкций от коррозии»,
- СП 50.13330.2012 «Тепловая защита зданий».

Укладка бетона

Бетонная смесь доставляется на площадку в автосмесителях и укладывается в опалубку слоями толщиной не более 50 см. Укладка должна производиться без перерывов, исключающих образование рабочих швов. При необходимости перерыва поверхность бетона обрабатывается для обеспечения монолитного сцепления с последующим слоем.

Вибрирование

Каждый уложенный слой уплотняется глубинными вибраторами до прекращения выделения воздуха и появления цементного молочка на поверхности. Вибрирование выполняется равномерно, с шагом не более 1,5 радиуса действия вибратора. Недостаточное или избыточное вибрирование не допускается.

Уход за бетоном

После окончания укладки поверхности бетона должны быть защищены от пересыхания, промерзания и механических повреждений. В жаркую погоду бетон увлажняется и укрывается плёнкой, матами или геотекстилем. Снятие опалубки допускается только после достижения бетоном не менее 70 % проектной прочности.

Гидроизоляция подземных конструкций

Все подземные элементы фундаментов подлежат гидроизоляции в соответствии с СП 28.13330.2017. Для защиты от грунтовой влаги и капиллярного подсоса применяются:

- обмазочная битумная или полимерная гидроизоляция;
- рулонные материалы в два слоя с нахлёстом швов;
- проникающие составы или мембранные системы — при высоком уровне грунтовых вод.

Особое внимание уделяется узлам сопряжения вертикальной и горизонтальной гидроизоляции, а также местам ввода инженерных коммуникаций.

Дополнительные мероприятия

- Перед началом работ все материалы (цемент, арматура, гидроизоляционные составы) должны пройти входной контроль качества.
- Арматурные каркасы должны устанавливаться на фиксаторы, обеспечивающие проектные защитные слои бетона.
- Работы ведутся под контролем инженерно-технического персонала с обязательным ведением журнала бетонных работ и оформлением актов на скрытые работы.
- При устройстве фундаментов в зимнее время выполняются мероприятия по прогреву и защите бетона в соответствии с РД 34.48.201–97 и рекомендациями производителей добавок.

Пояснительная записка к устройству свайного фундамента на забивных сваях

Свайный фундамент на забивных железобетонных сваях принят исходя из расчетных нагрузок от здания и требований нормативных документов (СП 24.13330.2011 «Свайные фундаменты», СП 22.13330.2016 «Основания зданий и сооружений»).

1. Подготовительные работы

Перед началом устройства свайного поля необходимо:

- выполнить геодезическую разбивку осей здания и вынести в натуру расположение свай;
- произвести планировку строительной площадки, обеспечить доступ техники;
- устроить обноску с закреплением осей и контрольных точек.

2. Устройство свай

- В качестве свай применяются сборные железобетонные сваи заводского изготовления, размеры и тип которых принимаются по проекту.
- Забивка свай выполняется дизель-молотами, гидромолотами или вибропогружателями в зависимости от условий площадки.
- Сваи погружаются в грунт до проектной отметки или отказа, зафиксированного по данным испытаний и паспорту сваебойной установки.
- Отклонение свай по вертикали не должно превышать 1,5 % от длины сваи (СП 70.13330.2012).

3. Соединение свай с ростверком

- После погружения сваи срезаются на проектной отметке.
- Верхняя поверхность свай очищается от разрушенного бетона, оголенная арматура используется для анкеровки в тело ростверка.
- Сваи объединяются монолитным железобетонным ростверком, армирование которого принимается по проекту.
- Защитный слой бетона ростверка до рабочей арматуры — не менее 25 мм.

4. Бетонные работы (ростверк)

- Бетон — класс прочности B25, морозостойкость не ниже F150, водонепроницаемость W6.
- Укладка бетона производится слоями с обязательным виброуплотнением глубинными вибраторами.
- Поверхность бетона выравнивается, укрывается и выдерживается во влажных условиях не менее 7 суток.
- Допускаемые отклонения по высоте верха ростверка: ±10 мм на всё здание, ±5 мм на 2 м длины правила (СП 70.13330.2012).

5. Работы в зимнее время


При производстве работ в зимний период необходимо:

- при отрицательных температурах предусматривать прогрев ростверка (электродный, проводами ПНСВ или тепловыми пушками), а также утепление свежеуложенного бетона;
- применять бетонные смеси с противоморозными добавками;
- температура бетона при укладке — не ниже +5 °C, в процессе твердения поддерживается согласно СП 70.13330.2012;
- погружение свай в мерзлый грунт допускается только при применении специальных технологий (лидирующие скважины, паро- или электропрогрев).


6. Контроль качества

- Контроль точности установки свай ведется геодезическими методами.
- Отклонение свай от проектного положения в плане — не более 50 мм.
- Контроль отказа свай ведется по показаниям оборудования и актируется.
- Контроль качества бетона ростверка осуществляется лабораторными испытаниями образцов.
- Работы выполняются в соответствии с требованиями СП 24.13330.2011 «Свайные фундаменты» и СП 70.13330.2012 «Несущие и ограждающие конструкции».

						#ID Проекта		
						кадастровый номер Россия		
Изм.	Кол.уч.	Лист	№Док.	Подп.	Дата			
Разраб.						Индивидуальный жилой дом	Стадия: #Стадия Проекта	Лист: 11 / Листов:
ГАП								
ПЗ Свайный фундамент (забивные сваи)								

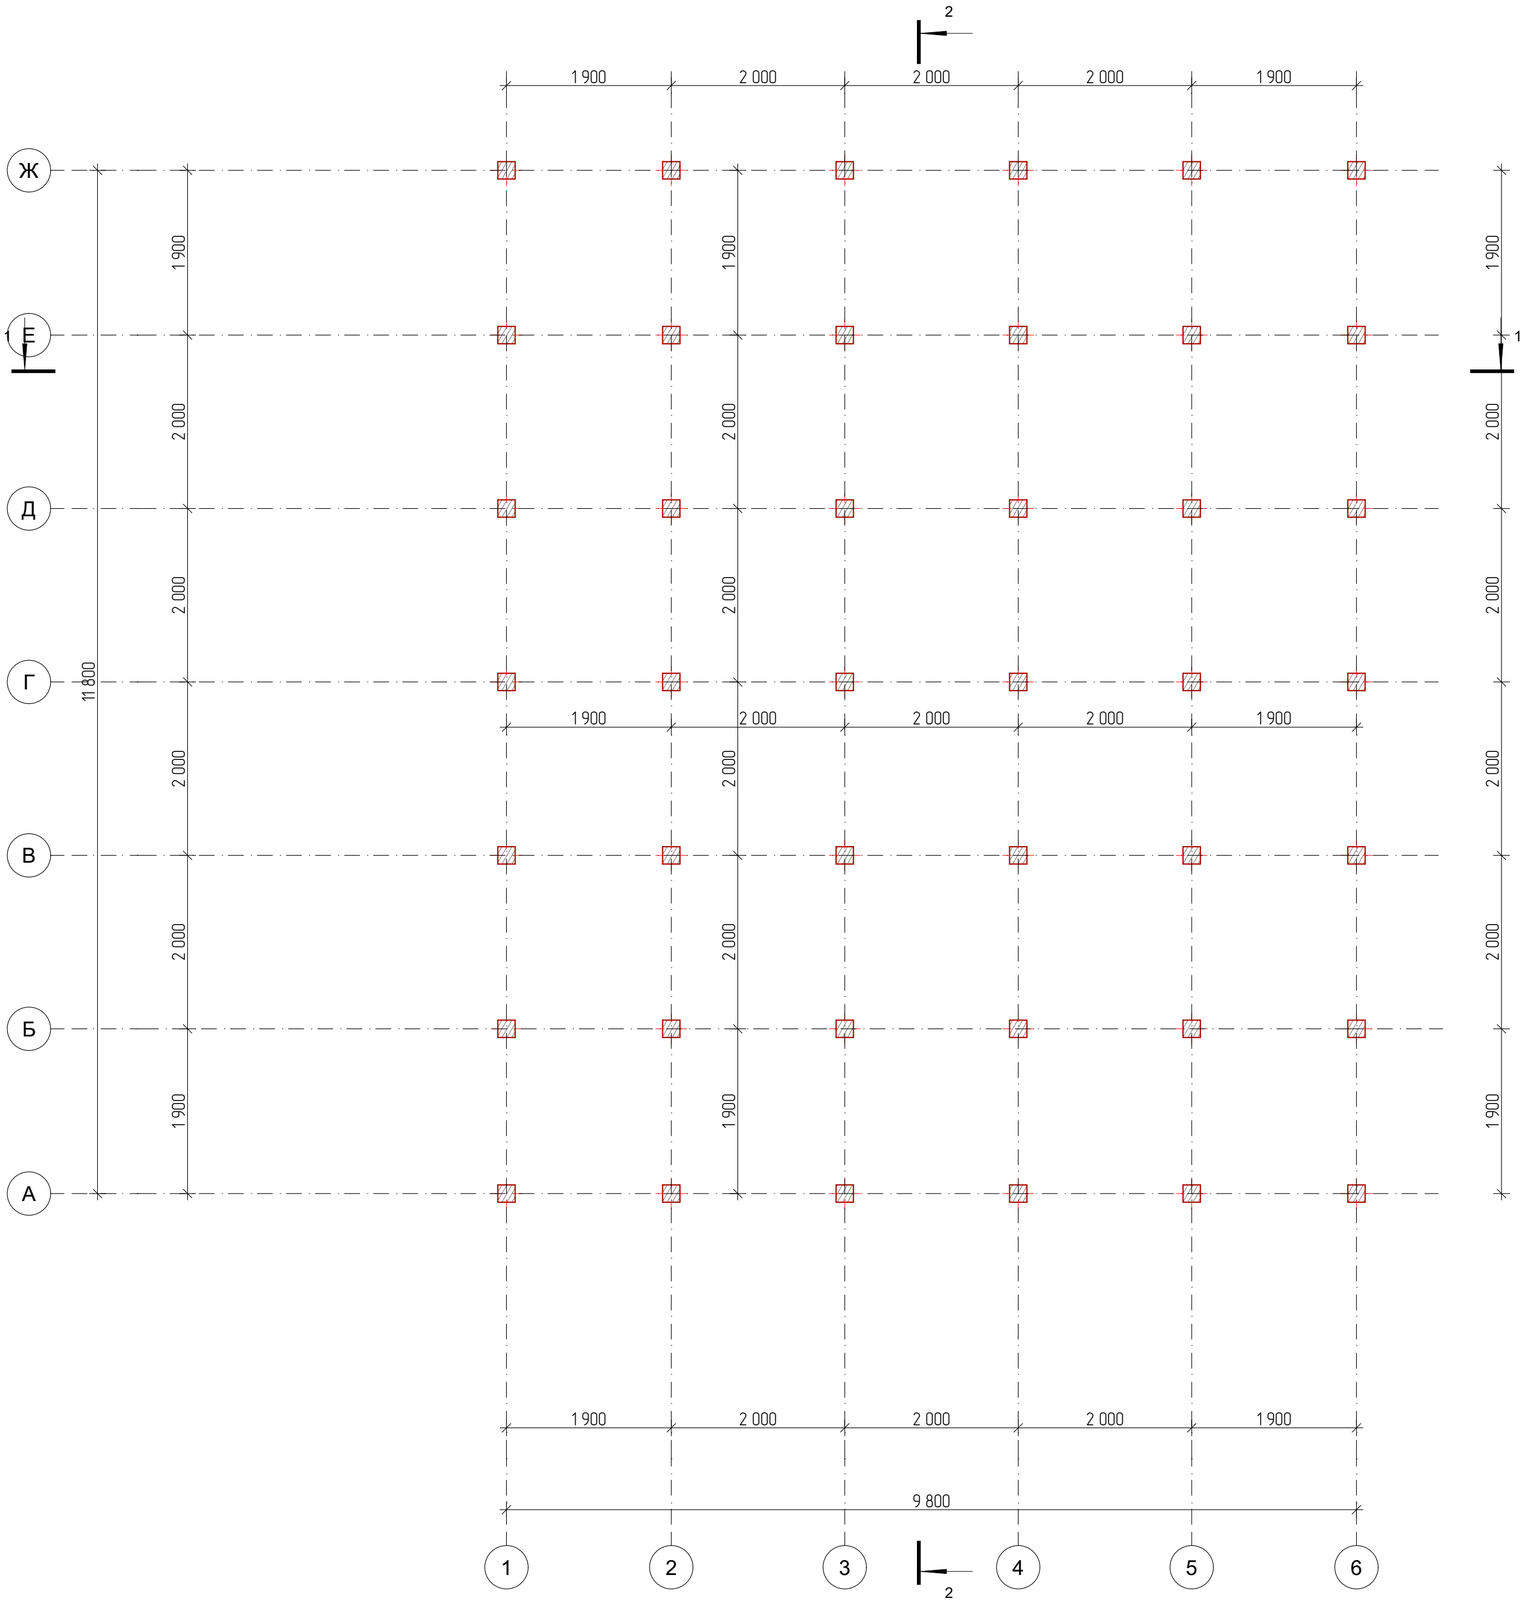


						#ID Проекта	
						кадастровый номер Россия	
Изм.	Колуч.	Лист	№Док.	Подп.	Дата		
Разраб.						Индивидуальный жилой дом	Стадия: #Стадия Проекта; Лист: 12; Листов:
ГАП							
План свайного поля							

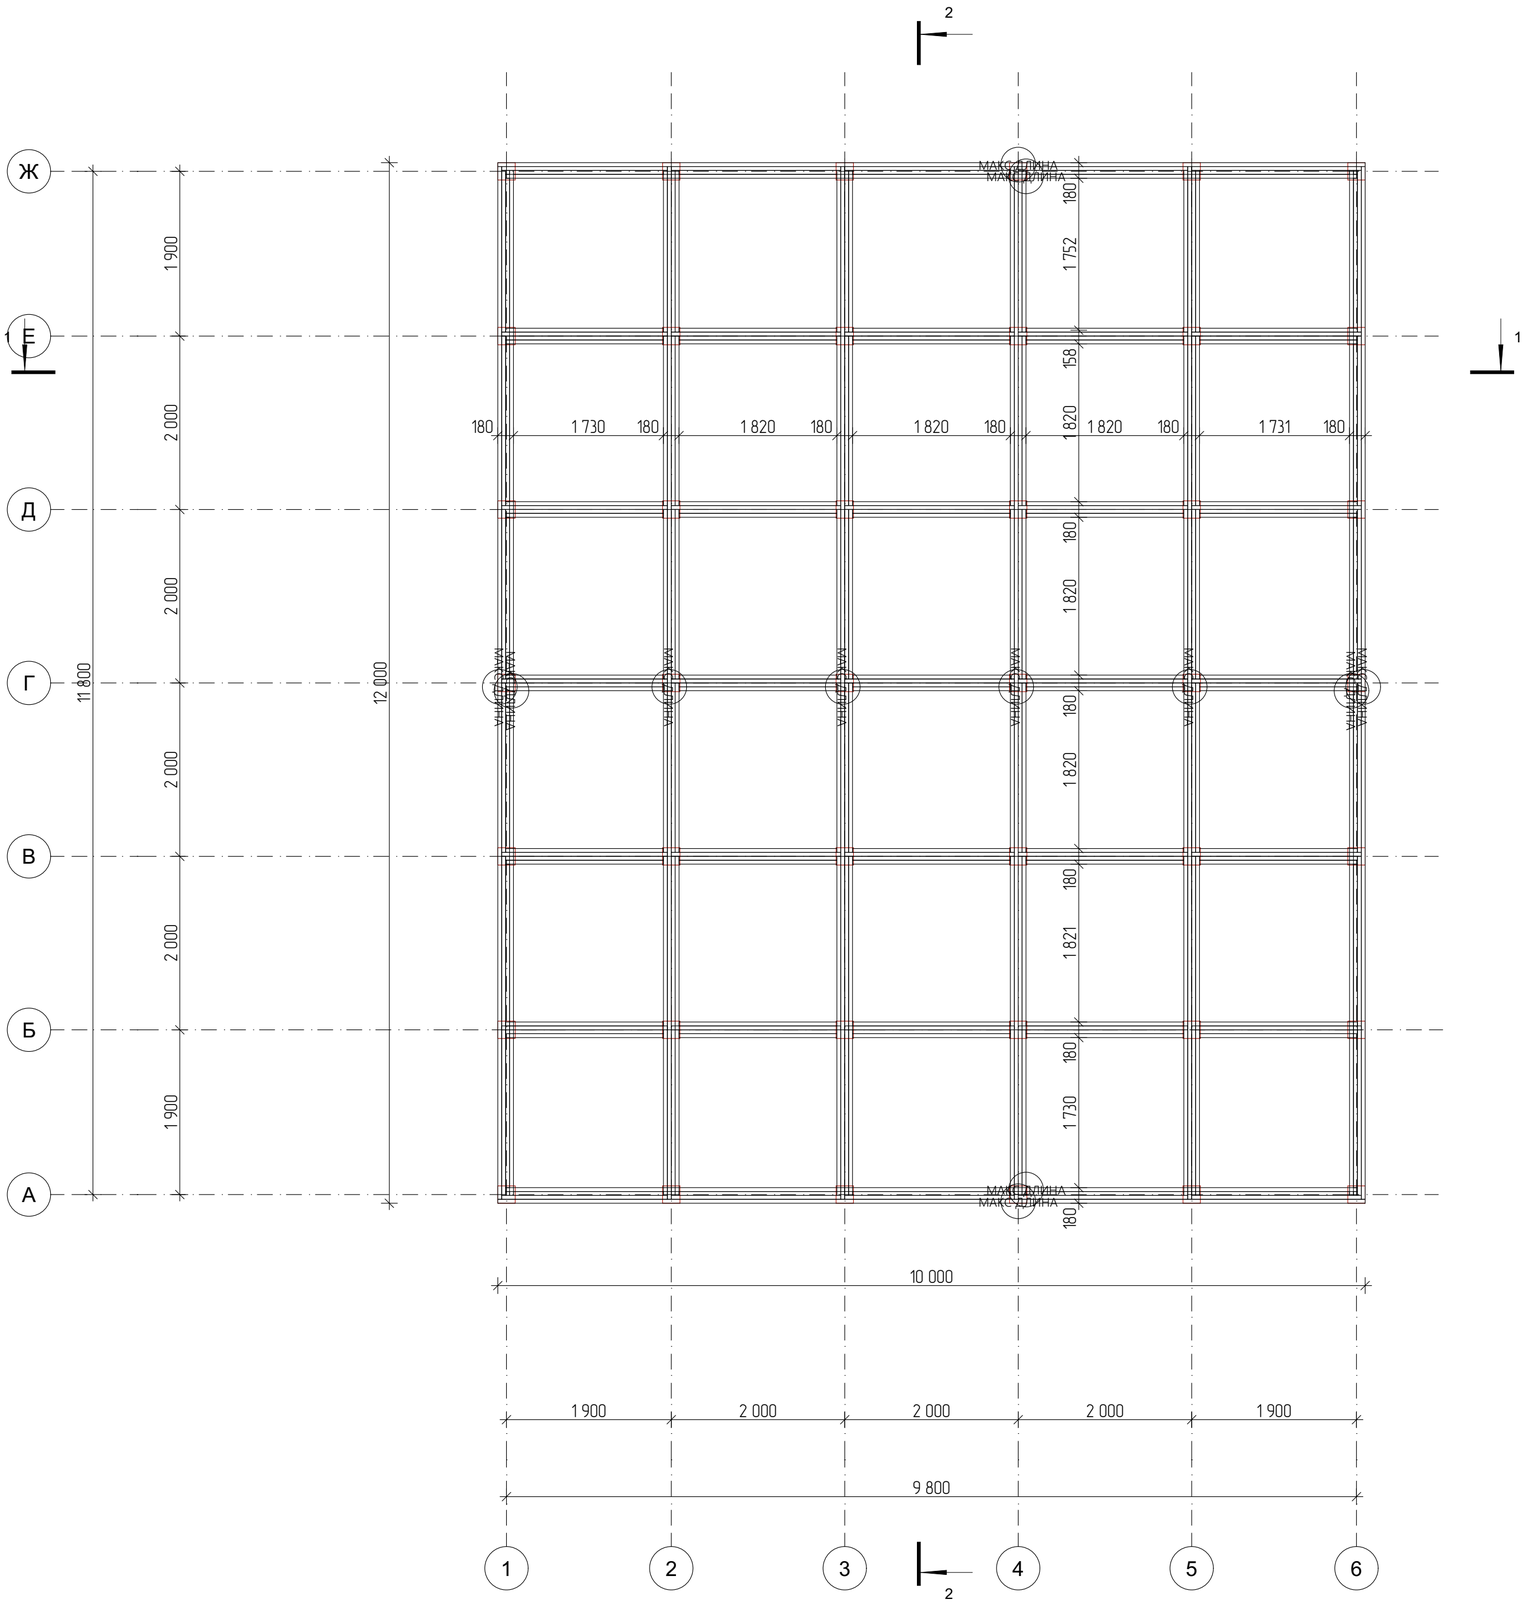

						#ID Проекта	
						кадастровый номер Россия	
Изм.	Колуч.	Лист	№Док.	Подп.	Дата		
Разраб.						Индивидуальный жилой дом	Стадия: #Стадия Проекта; Лист: 13; Листов:
ГАП							
План фундамента (ростверк)							


Вид каркаса снаружи

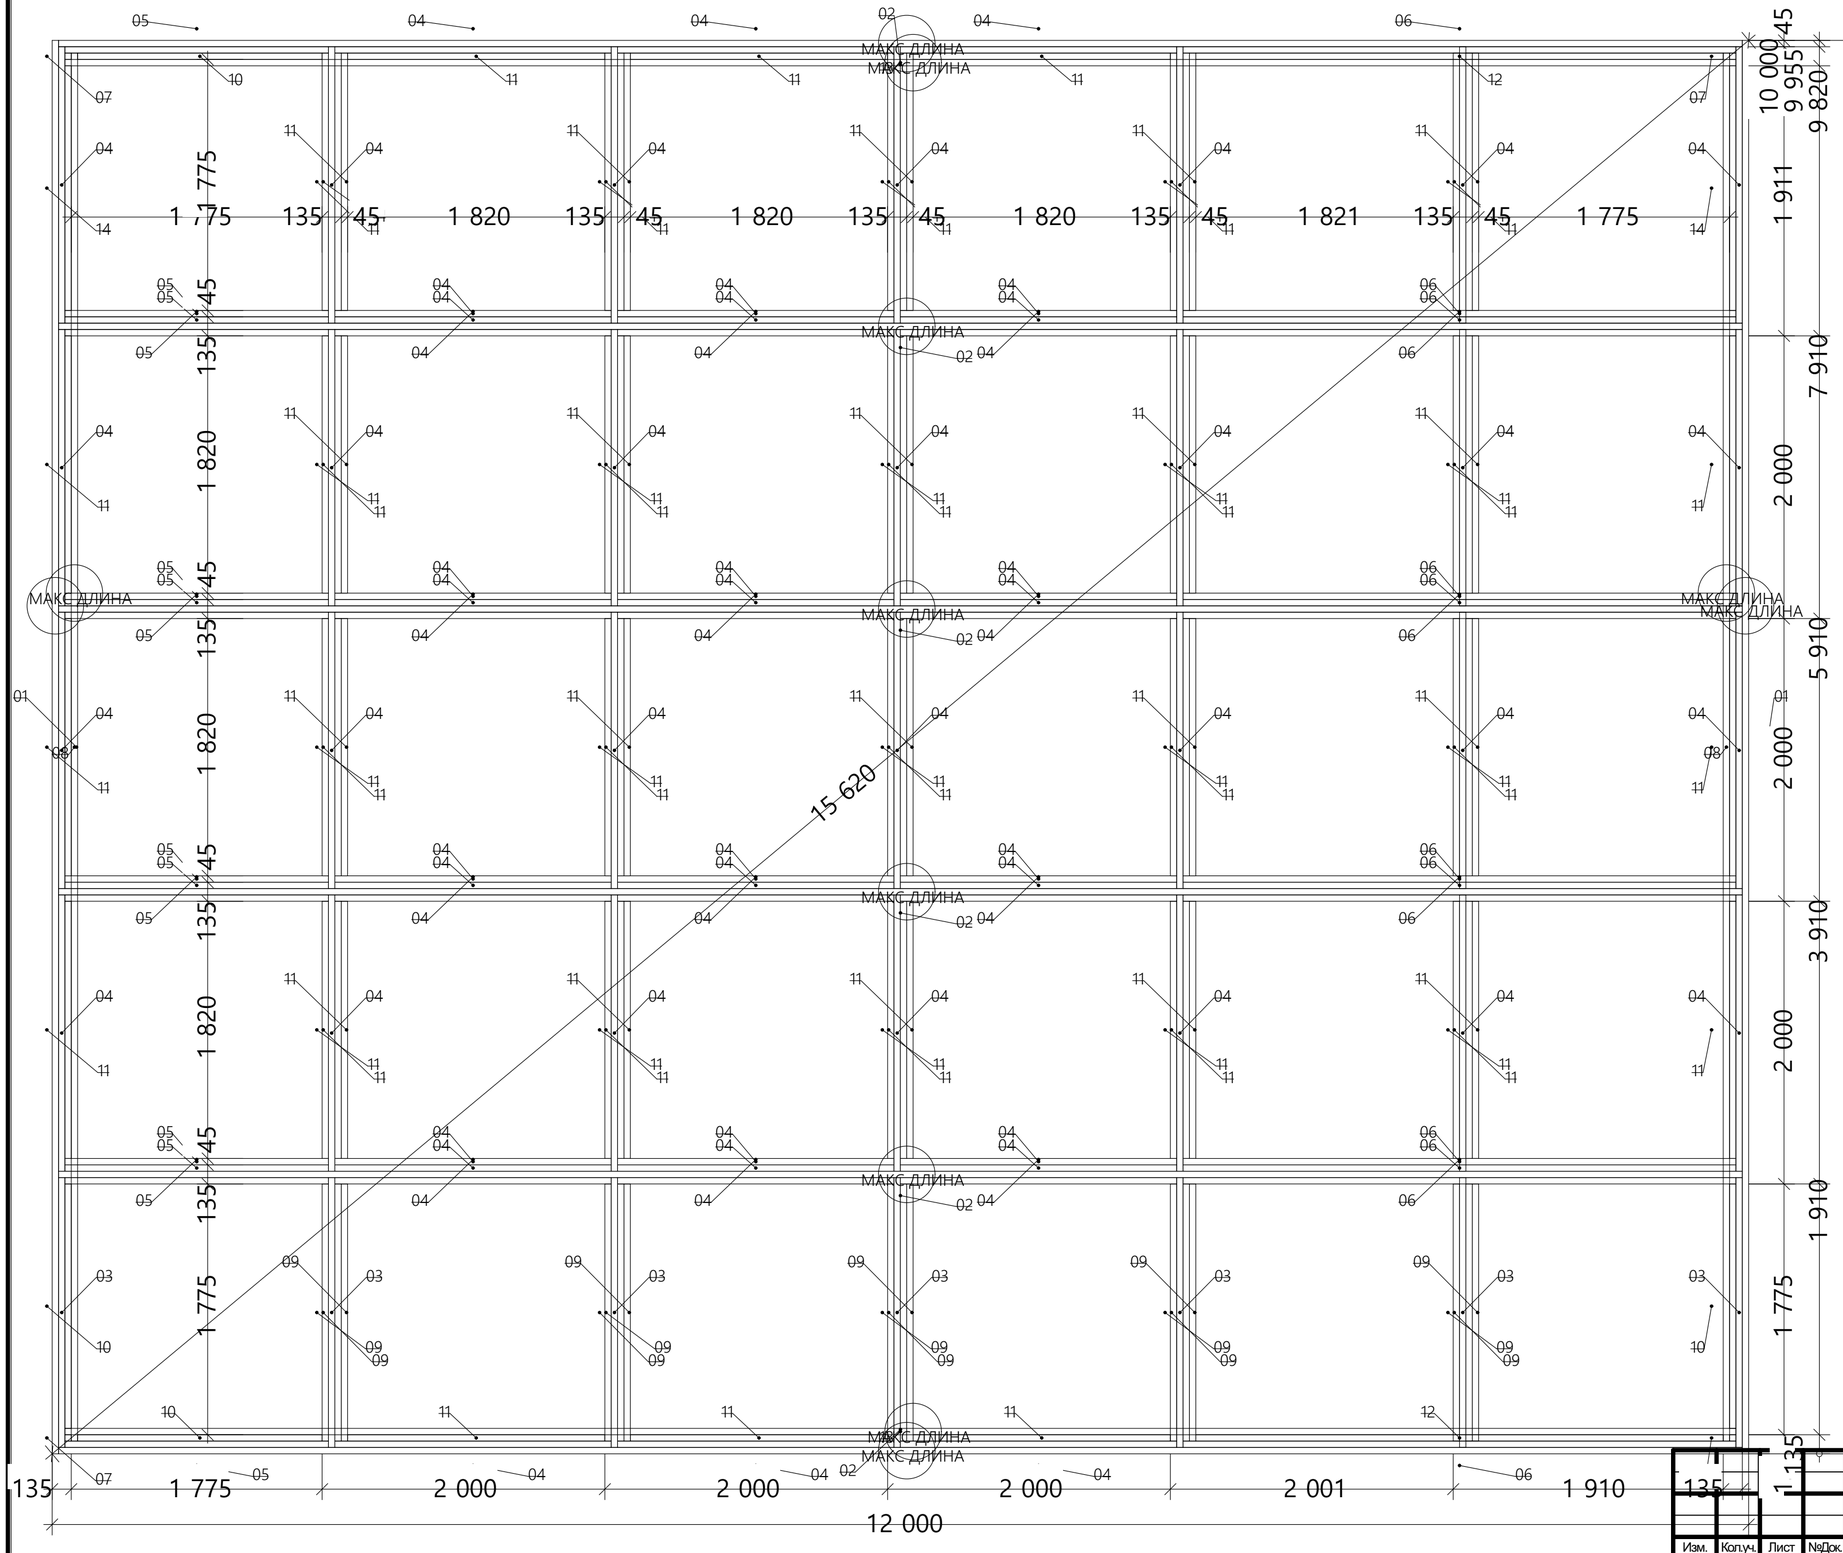


Основной каркас №Пол 1.01

Номер	Название	Сечение, мм	Длина, мм	Кол-во, шт	Объем, м3
Пол 1.01-01	Ростверк	45x195	10000	2	0.175
Пол 1.01-02	Ростверк	45x195	11910	4	0.418
Пол 1.01-02	Ростверк	45x195	11910	2	0.209
Пол 1.01-03	Ростверк	45x195	1909	7	0.117
Пол 1.01-04	Ростверк	45x195	1955	70	1.201
Пол 1.01-05	Ростверк	45x195	1864	14	0.229
Пол 1.01-06	Ростверк	45x195	3910	14	0.480
Пол 1.01-07	Ростверк	45x195	45	4	0.002
Пол 1.01-08	Ростверк	45x195	9820	2	0.172
Пол 1.01-09	Ростверк	45x195	1819	15	0.239
Пол 1.01-10	Ростверк	45x195	1730	4	0.061
Пол 1.01-11	Ростверк	45x195	1820	72	1.150
Пол 1.01-12	Ростверк	45x195	3730	2	0.065
Пол 1.01-13	Ростверк	45x195	11820	2	0.207
Пол 1.01-14	Ростверк	45x195	1730	2	0.030
			Общая сумма:	216	4.757

							#ID Проекта	
							кадастровый номер Россия	
Изм.	Колуч.	Лист	№Док.	Подп.	Дата			
Разраб.						Индивидуальный жилой дом	Стадия	Лист	Листов
ГАП							#Стадия Проекта	14	
Чертеж каркаса ростверка№ Пол 1.01 #1									

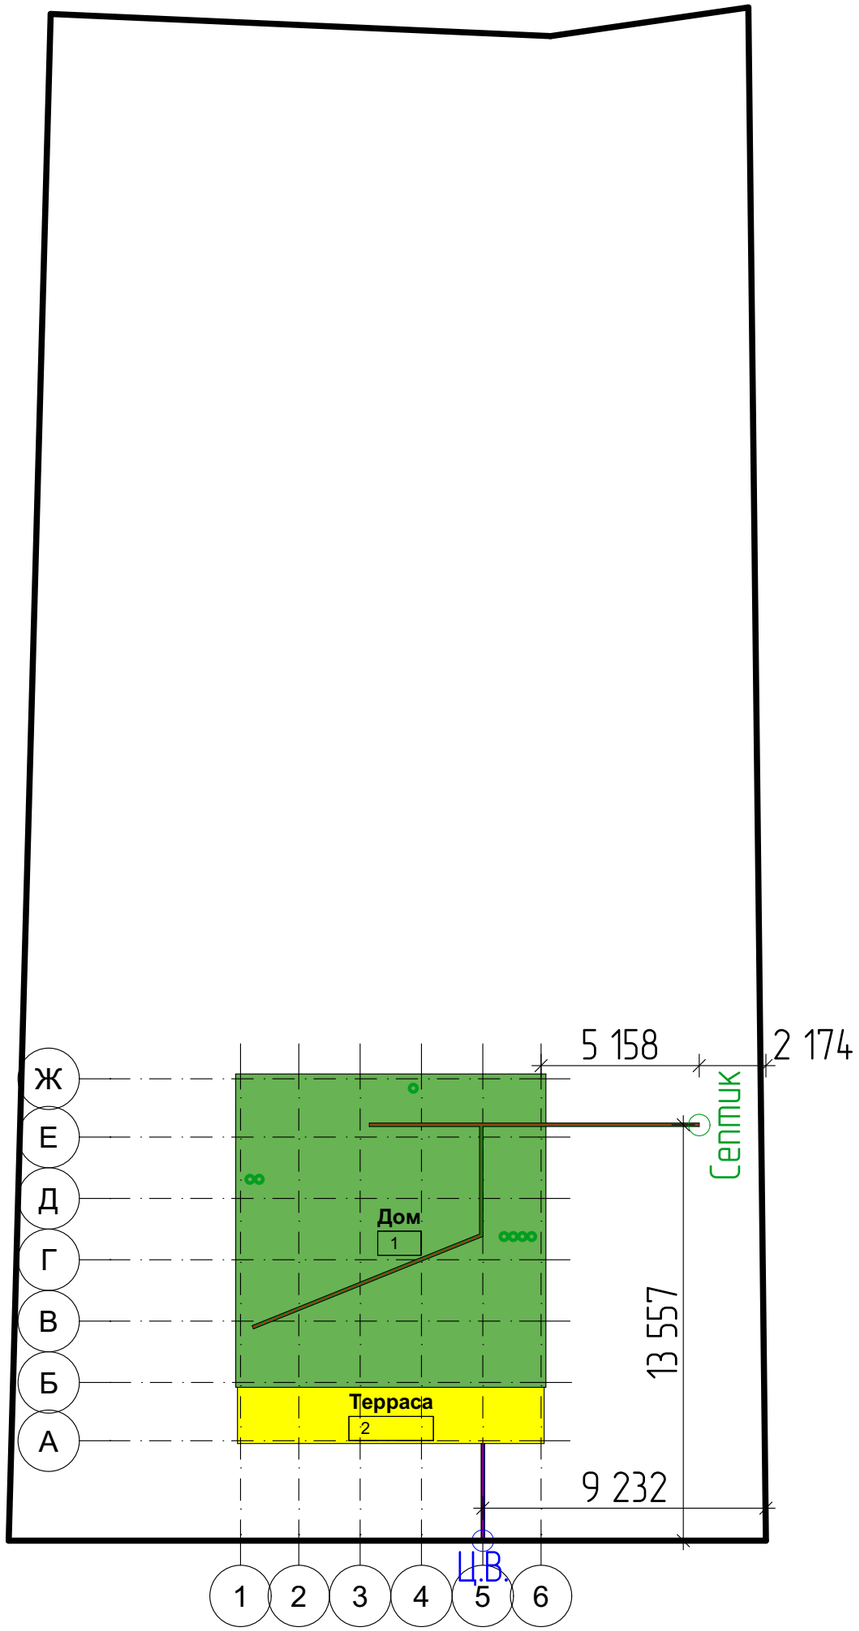

						#ID Проекта		
						кадастровый номер Россия		
Изм.	Кол.уч.	Лист	№Док.	Подп.	Дата			
Разраб.						Индивидуальный жилой дом	Стадия	Лист	Листов
ГАП							#Стадия Проекта	15	
Наружные сети									

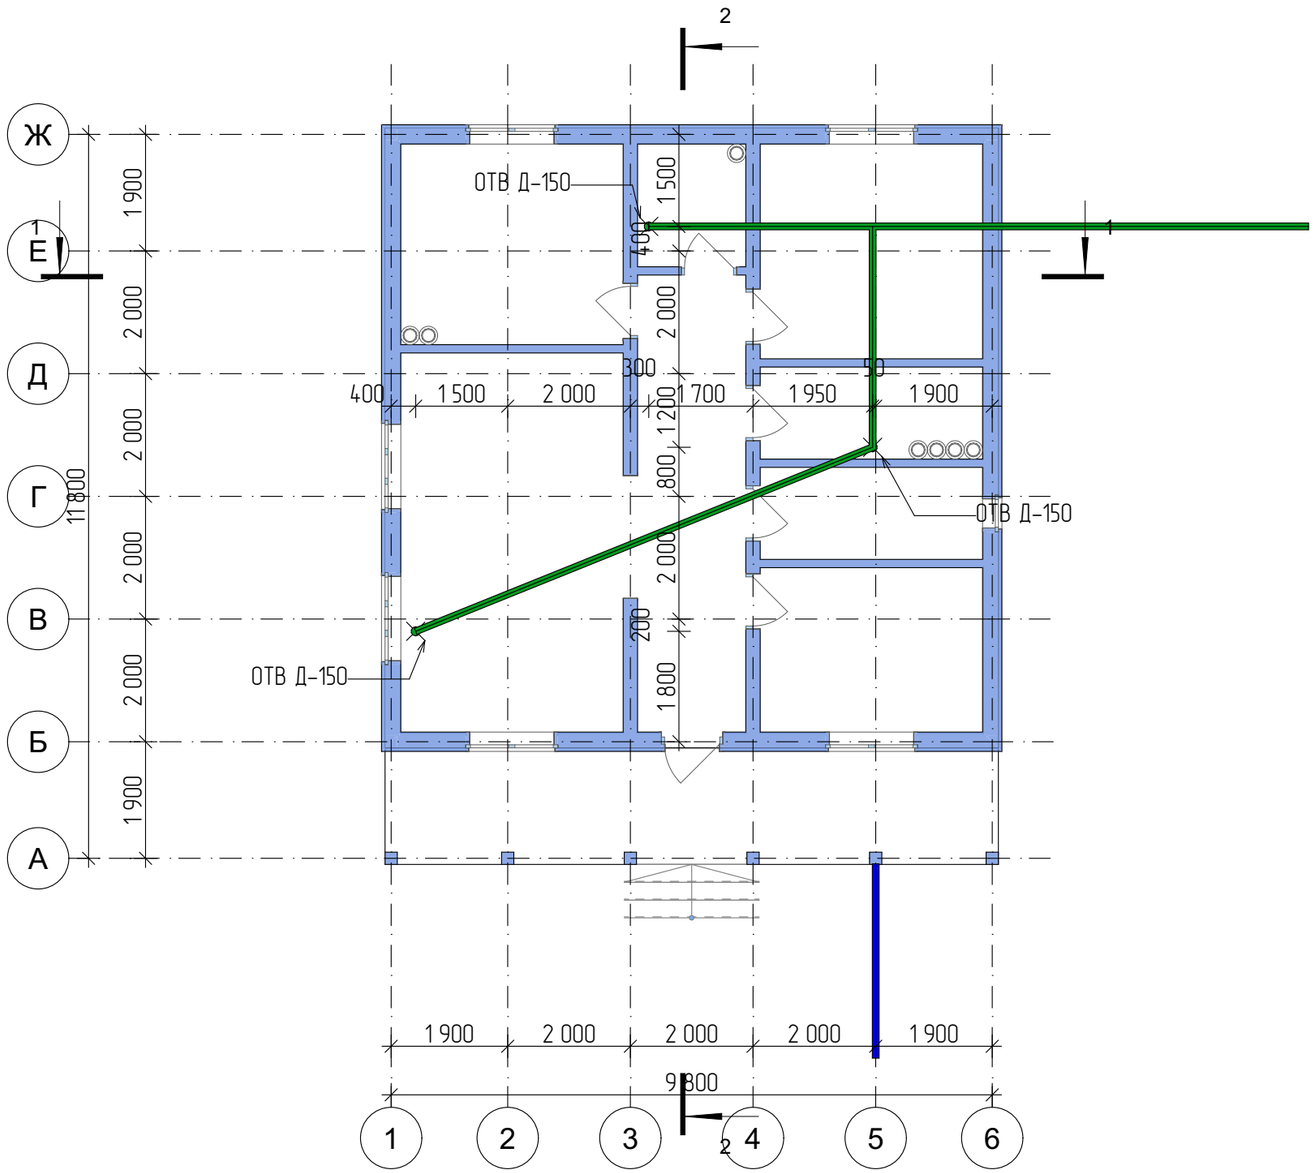

Пояснительная записка

1. Для устройства водопровода используется труба ПЭ100 SDR11 d40×3,7 (PN16), обеспечивающая подачу воды под рабочим давлением до 16 атм.

2. Для системы канализации применяется труба ПВХ SN4 d110×3,2 (канализация), предназначенная для наружной и внутренней самотечной разводки.

3. Указанные трубопроводы необходимо смонтировать в проектное положение до выполнения монолитных работ, с обеспечением прочной фиксации и защиты от повреждений.

4. На планах предусмотрены отверстия диаметром 150 мм для прокладки канализационных труб, что обеспечивает монтажный зазор и упрощает установку.

Внутренняя разводка по сантехническим приборам выполняется в толще стяжки пола и требует разработки отдельного специализированного раздела проекта. На представленных планах коммуникаций показаны только основные магистрали.

Коммуникации		
Назначение	Строительный Материал	Длина, мм
Водопровод	Труба ПЭ100 SDR11 d40×3,7 (PN16)	3 167
Канализация	Труба ПВХ SN4 d110×3,2 (канализация)	22 463

						#ID Проекта			
						кадастровый номер Россия			
Изм.	Кол.уч.	Лист	№Док.	Подп.	Дата				
Разраб.						Индивидуальный жилой дом	Стадия	Лист	Листов
ГАП							#Стадия Проекта	16	
План коммуникаций									

Конструкция пола				
	Наименование	Толщина, мм	Объем, м3	Площадь,м2
Пол (дом)				
	Дерево - Черновой настил	25	2,53	101,00
	Изоляция - Минеральная Мягкая	195	19,53	101,00
	Контробрешётка	40	4,04	101,00
	Лист OSB	22	1,97	101,00
	Мембрана - ветрозащитная диффузионная	1	0,10	101,00
	Мембрана - Пароизоляция	2	0,20	101,00
	Паркет	20	1,79	101,00
Пол (Терраса)				
	Дерево - Черновой настил	25	0,48	19,00
	Изоляция - Минеральная Мягкая	195	3,70	19,00
	Контробрешётка	40	0,75	19,00
	Лист OSB	22	0,40	19,00
	Мембрана - ветрозащитная диффузионная	1	0,02	19,00
	Мембрана - Пароизоляция	2	0,04	19,00
	Паркет	20	0,36	19,00

Сваи забивные	
Наиенование	Кол-во,шт
Свая 200х200	42
	42

Пояснительная записка по монтажу стен

Монтаж стен осуществляется после завершения устройства и набора прочности фундаментов и перекрытий. До начала работ выполняется подготовка строительной площадки: производится вынос осей здания, проверка геометрии фундамента, устройство гидроизоляции по верхней плоскости фундамента (или перекрытия), а также организация складирования строительных материалов в зоне доступности грузоподъёмной техники.

При разметке необходимо учитывать, что оси здания не совпадают с краем стены. На чертежах указаны размеры от внутренней грани стены до оси и от оси до наружной поверхности стены. Это требование принципиально важно для правильного позиционирования стен и соблюдения проектных габаритов здания. Нарушение расположения осей может привести к смещению несущих конструкций и расхождениям в размерах.

Укладка первого ряда или установка первых элементов выполняется строго по разметке осей с проверкой диагоналей, уровней и вертикали. Первый ряд задаёт правильную геометрию и точность всех последующих рядов или монтажных панелей.

Монтаж стен ведётся поэтапно, с контролем вертикальности и горизонтальности каждого ряда. Для перевязки элементов и обеспечения монолитности конструкции применяются растворы, клеевые составы или специальные соединительные элементы — в зависимости от проектного материала. По мере возведения стен предусматриваются технологические зазоры под монтаж перекрытий и оконных блоков.

В процессе работ осуществляется постоянный контроль геометрии: проверяются диагонали, отвесы, отметки по высоте, соответствие проектным размерам от осей до границ стен. При необходимости выполняется временное крепление стен или установка распорок до достижения проектной жёсткости.

По завершении возведения стен производится устройство армопояса и закладных деталей, предусмотренных проектом. В местах сопряжения стен с перекрытиями и перегородками оставляются технологические зазоры, которые заполняются согласно проектным решениям.

Все работы выполняются в соответствии с проектной документацией, строительными нормами и правилами, а также инструкциями производителей материалов.

						#ID Проекта		
						кадастровый номер Россия		
Изм.	Кол.уч.	Лист	№Док.	Подп.	Дата			
Разраб.						Индивидуальный жилой дом	Стадия: #Стадия Проекта	Лист: 18 / Листов:
ГАП								
ПЗ Стены								

Пояснительная записка к возведению каркасных стен

Возведение каркасных стен предусмотрено проектом на основании требований нормативных документов (СП 31-105-2002 «Проектирование и строительство энергоэффективных одноквартирных жилых домов с деревянным каркасом», СП 64.13330.2017 «Деревянные конструкции»).

1. Подготовительные работы

Перед началом монтажа каркаса необходимо:

проверить соответствие геометрии и отметок фундамента (ростверка, плиты или перекрытия) проектной документации;
выполнить горизонтальную гидроизоляцию по поверхности основания рулонными гидроизоляционными материалами;
нанести разметку положения наружных и внутренних несущих стен;
подготовить пиломатериалы, крепежные элементы и необходимый монтажный инструмент.

2. Монтаж каркаса

Монтаж стен выполняется из сухого строганого пиломатериала, соответствующего проектному сечению и влажности не более 18%;
стойки устанавливаются с проектным шагом и закрепляются к нижней и верхней обвязкам металлическими крепежными элементами;
все элементы каркаса выравниваются по вертикали и горизонтали, временно фиксируются до окончательного закрепления;
в местах оконных и дверных проемов устраиваются усиленные стойки, ригели и перемычки согласно проекту;
допускаемые отклонения: по вертикали — не более 10 мм на этаж, по горизонтали — не более 5 мм на 10 м длины стены (СП 70.13330.2012);
монтаж стен выполняется с обязательным устройством предусмотренных проектом укосин или плитной пространственной обшивки.

3. Устройство ограждающих конструкций

После сборки каркаса выполняется монтаж плитной обшивки, ветрозащитной мембраны и элементов пространственной жесткости;
между стойками каркаса укладывается теплоизоляционный материал без зазоров и пустот;
со стороны помещения устанавливается пароизоляционная мембрана с герметизацией стыков специализированными лентами;
наружная и внутренняя отделка выполняются в соответствии с проектной документацией.

4. Устройство перекрытий и сопряжений

Межэтажные и чердачные перекрытия опираются на верхнюю обвязку каркасных стен согласно проекту;
соединение элементов выполняется металлическими крепежными изделиями, обеспечивающими передачу расчетных нагрузок;
все узлы сопряжения стен, перекрытий и кровельных конструкций выполняются в соответствии с рабочими чертежами;
дополнительные элементы усиления устанавливаются в местах концентрации нагрузок.

5. Защита конструкций


Все деревянные элементы каркаса должны быть обработаны огнебиозащитными составами в соответствии с требованиями проектной документации;
места повреждения защитного покрытия обрабатываются повторно после монтажа;
конструкции должны быть защищены от атмосферного увлажнения до завершения устройства наружной отделки;
монтаж наружной облицовки выполняется с устройством вентиляционного зазора при необходимости, предусмотренной проектом.

6. Работы в зимнее время


При производстве монтажных работ в зимний период необходимо:

очищать конструкции и места соединений от снега, льда и наледи;
не допускать монтажа утеплителя и мембран по влажным или обледеневшим поверхностям;
крепежные соединения выполнять в соответствии с требованиями нормативных документов при отрицательных температурах;
обеспечивать защиту смонтированных конструкций от воздействия атмосферных осадков до завершения наружной отделки.

						#ID Проекта		
						кадастровый номер Россия		
Изм.	Кол.уч.	Лист	№Док.	Подп.	Дата			
Разраб.						Индивидуальный жилой дом	Стадия	Лист	Листов
ГАП							#Стадия Проекта	19	
ПЗ Каркасный дом									

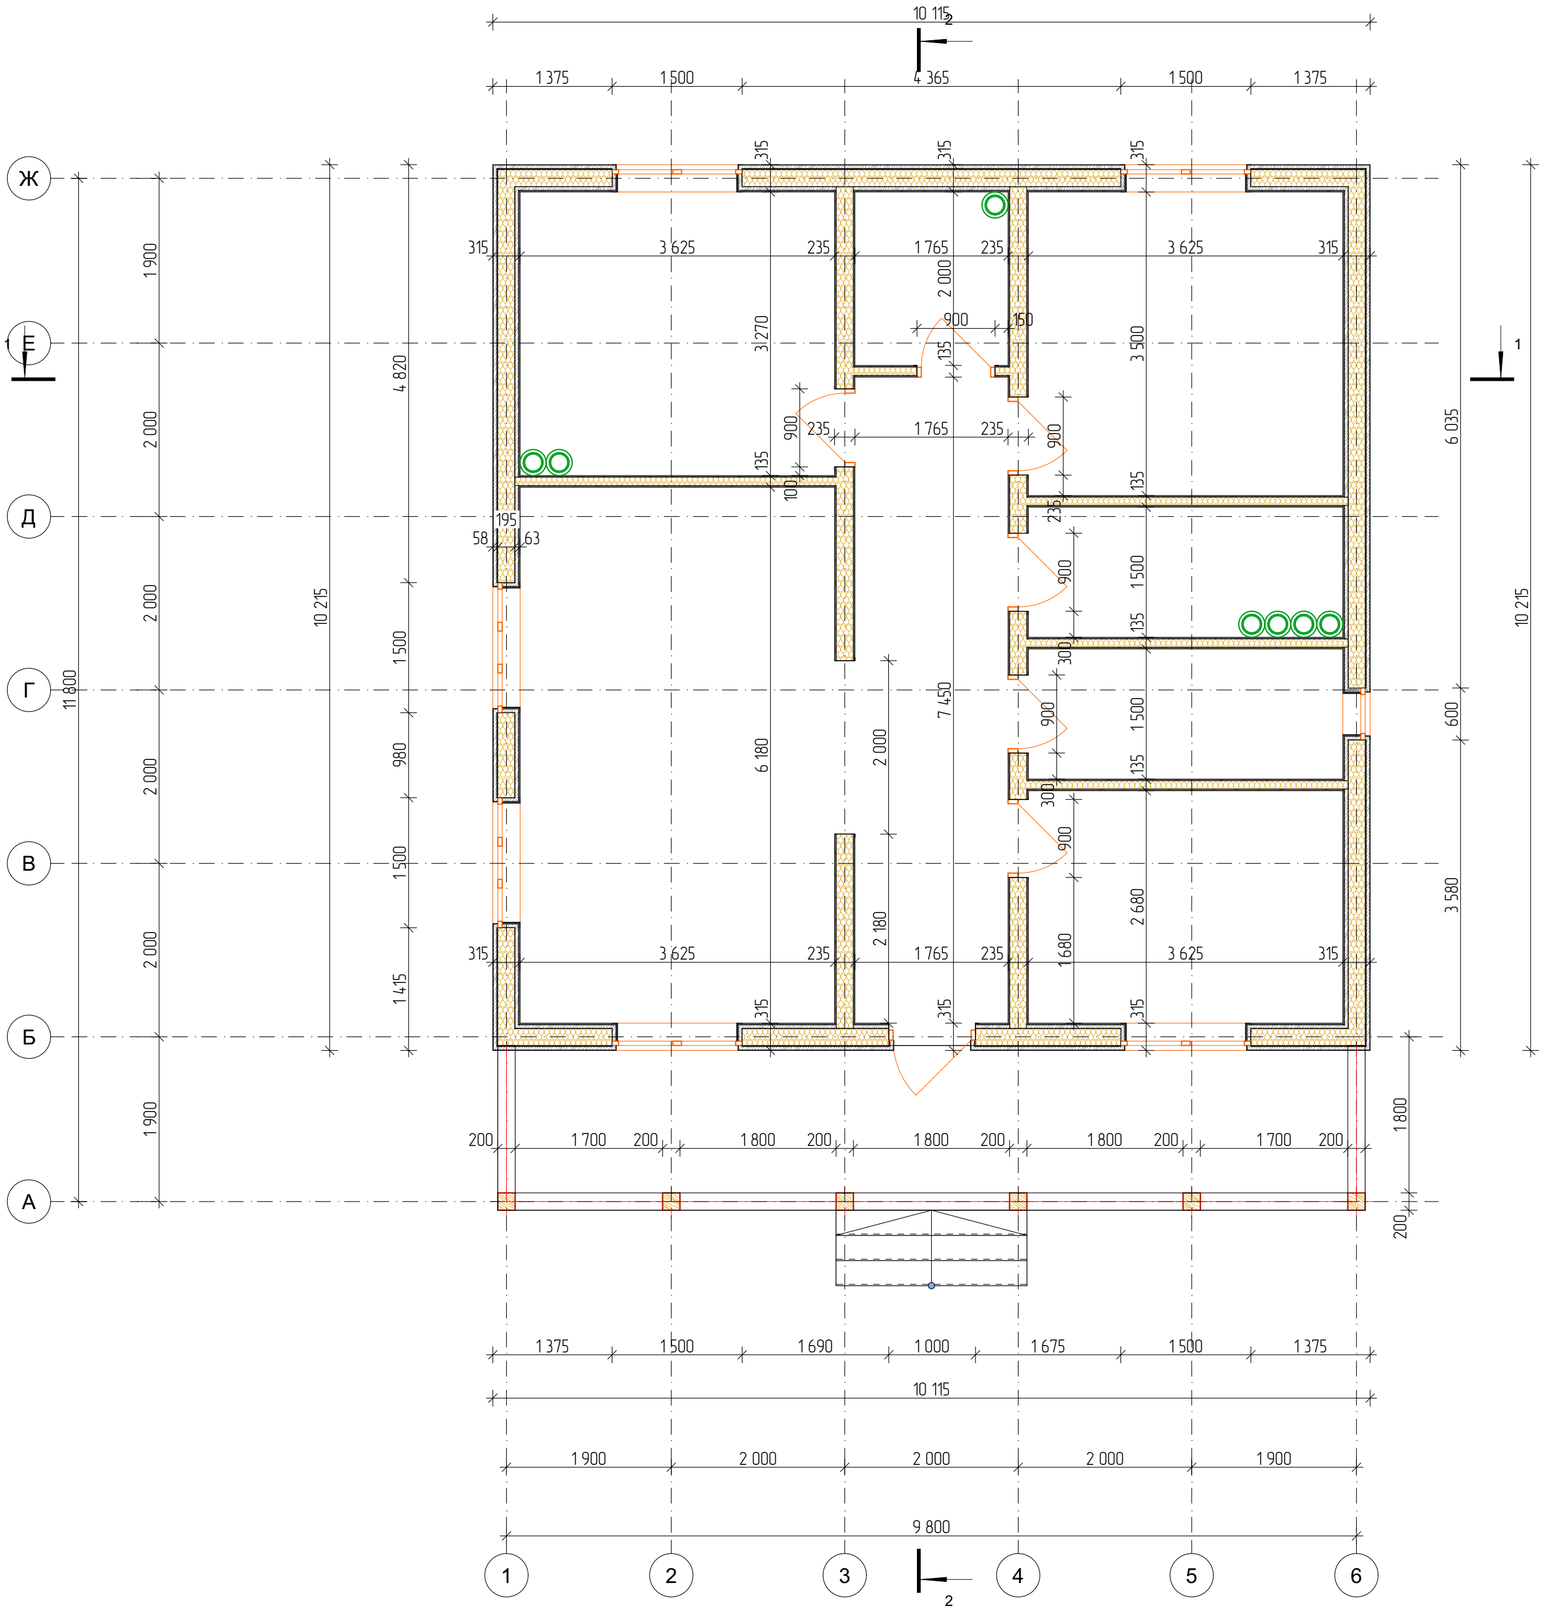

						#ID Проекта	
						кадастровый номер Россия	
Изм.	Кол.уч.	Лист	№Док.	Подп.	Дата		
Разраб.						Индивидуальный жилой дом	Стадия: #Стадия Проекта; Лист: 20; Листов:
ГАП							
План на отм. ±0.000							

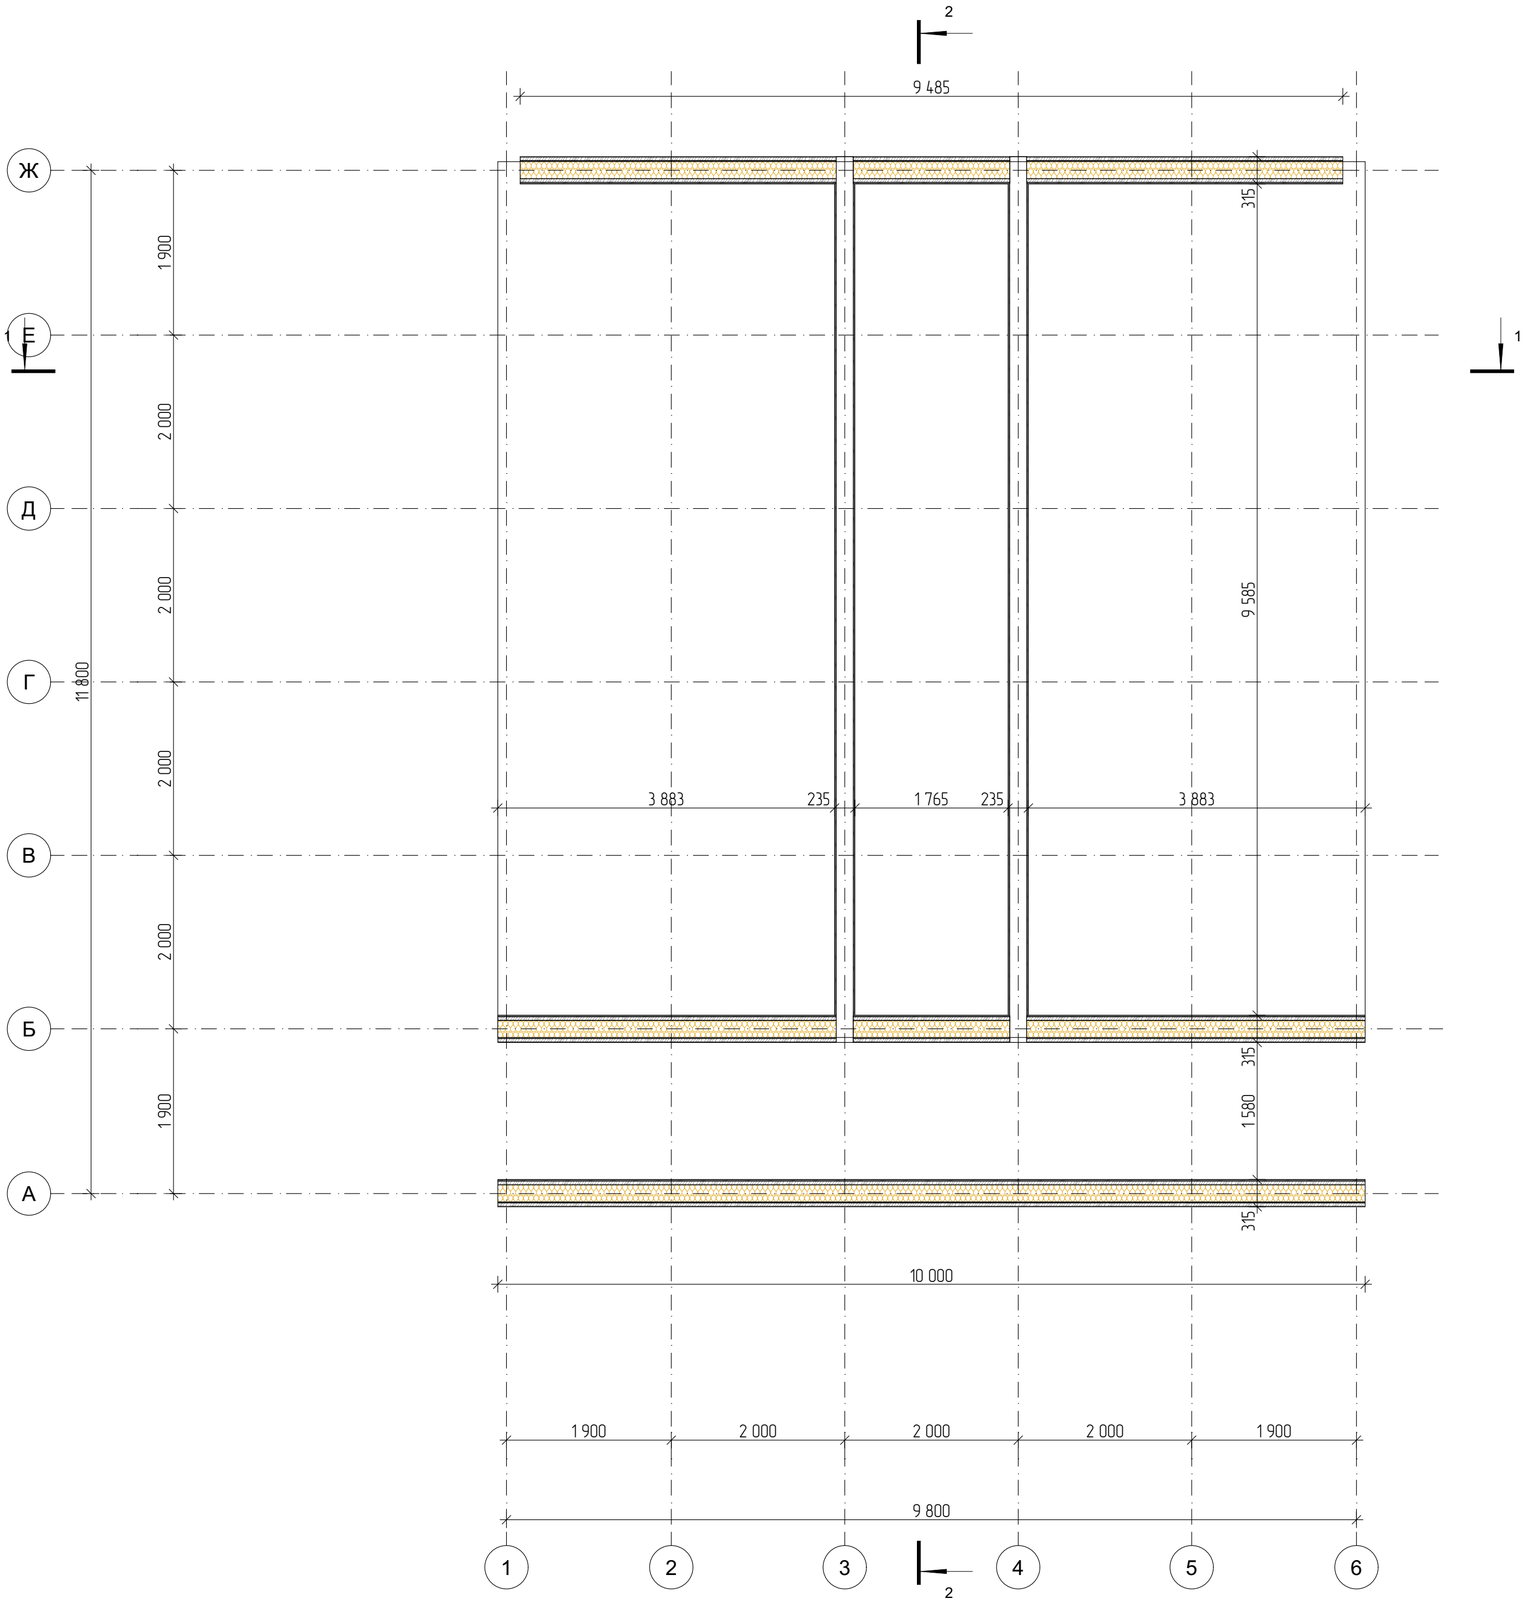



						#ID Проекта	
						кадастровый номер Россия	
Изм.	Колуч.	Лист	№Док.	Подп.	Дата		
Разраб.						Индивидуальный жилой дом	Стадия: #Стадия Проекта; Лист: 21; Листов:
ГАП							
План на отм +3.100							

Стены - Каркасный дом			
Этаж	Строительный материал	Объем, м3	Площадь, м2
1-й этаж, Внутренние стены			
	Гипсокартон	0,81	81,88
		0,81 м³	
	Изоляция - Минеральная Жесткая	8,42	43,18
		8,42 м³	
	Лист OSB	0,81	82,47
		0,81 м³	
1-й этаж, Наружные стены			
	Гибкая плитка под кирпич(фасадная)	0,52	102,73
		0,52 м³	
	Гипсокартон	0,90	90,10
		0,90 м³	
	Изоляция - Минеральная Жесткая	19,33	99,13
		19,33 м³	
	Контробрешётка	7,74	193,56
		7,74 м³	
	Лист OSB	1,92	192,33
		1,92 м³	
	Мембрана - ветрозащитная диффузионная	0,25	101,69
		0,25 м³	
	Мембрана - Пароизоляция	0,24	96,81
		0,24 м³	
1-й этаж, Перегородки			
	Гипсокартон	0,94	90,54
		0,94 м³	
	Изоляция - Минеральная Жесткая	4,48	46,98
		4,48 м³	
	Лист OSB	0,94	91,14
		0,94 м³	
Чердак, Внутренние стены			
	Воздушная Прослойка	5,92	31,08
		5,92 м³	
	Гипсокартон	0,58	57,04
		0,58 м³	
	Лист OSB	0,58	57,16
		0,58 м³	


Чердак, Наружные стены			
	Гибкая плитка под кирпич(фасадная)	0,13	26,90
		0,13 м³	
	Гипсокартон	0,27	26,78
		0,27 м³	
	Изоляция - Минеральная Жесткая	5,24	26,90
		5,24 м³	
	Контробрешётка	2,14	53,80
		2,14 м³	
	Лист OSB	0,54	53,80
		0,54 м³	
	Мембрана - ветрозащитная диффузионная	0,06	26,90
		0,06 м³	
	Мембрана - Пароизоляция	0,06	26,90
		0,06 м³	
		62,82 м³	

Ведомость материалов на фасад			
Наиме...	Компоненты		Объем, м3
	Толщина, мм	Площадь, м2	
Изоляция - Минеральная Жесткая			
	95	46,98	4,48
	195	169,21	32,99

Изм.	Кол.уч.	Лист	№Док.	Подп.	Дата	#ID Проекта			
						кадастровый номер Россия			
						Индивидуальный жилой дом	Стадия	Лист	Листов
Разраб.							#Стадия Проекта	22	
ГАП									
Ведомасть материаов стен									

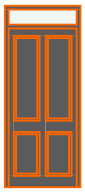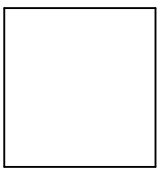
Каталог Дверей				
Полный ID Элемента	ДВ-1	ДВ-2	ДВ-2	П-1
D по Классификации	Дверь -1	Дверь -2	Дверь -2	Дверь -1
Наименование Двери	Однопольная Дверь с Фрамугой 27	Однопольная Дверь 27	Однопольная Дверь 27	Прямоугольный Дверной Проем 27
Количество	1	1	5	1
Размер Ш x В	1 000×2 400	900×2 100	900×2 100	2 000×2 100
Ориентация	П	Л	П	
Высота Порога Двери	0	0	0	0
Высота Перемычки Двери	2 400	2 100	2 100	2 100
2D-символ				
Вид со Стороны, Противоположной Стороне Открывания				

Каталог Окон			
Полный ID Элемента	ОК-1	ОК-1	ОК-2
Наименование Окна	Двустворчатое Окно 27	Трехстворчатое Окно 27	Окно 27
Количество	4	2	1
Размер Ш x В	1 500×1 500	1 500×1 500	600×1 500
Ориентация			П
Высота Подоконника Окна	900	900	900
Высота Перемычки Окна	2 400	2 400	2 400
2D-символ			
Вид со Стороны, Противоположной Стороне Открывания			

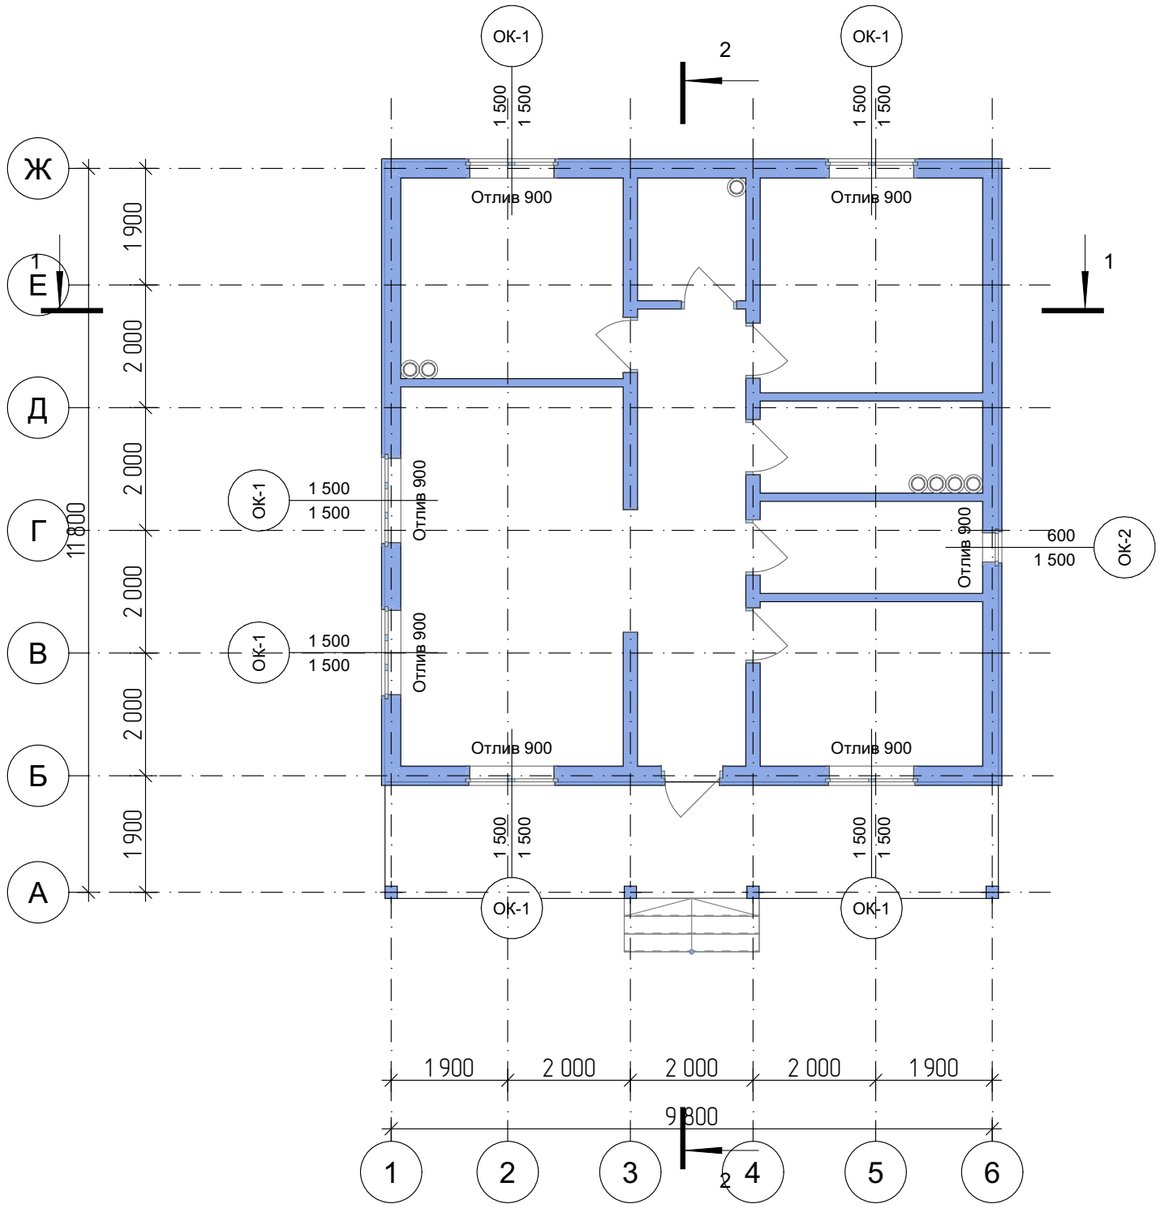

Марка, поз.	Размер проема в кладке, мм	Количество
ОК-1	1 500×1 500	6
ОК-2	600×1 500	1


						#ID Проекта		
						кадастровый номер Россия		
Изм.	Кол.уч.	Лист	№Док.	Подп.	Дата			
Разраб.						Индивидуальный жилой дом	Стадия	Лист	Листов
ГАП							#Стадия Проекта	25	
Маркировка оконных проемов первого этажа									

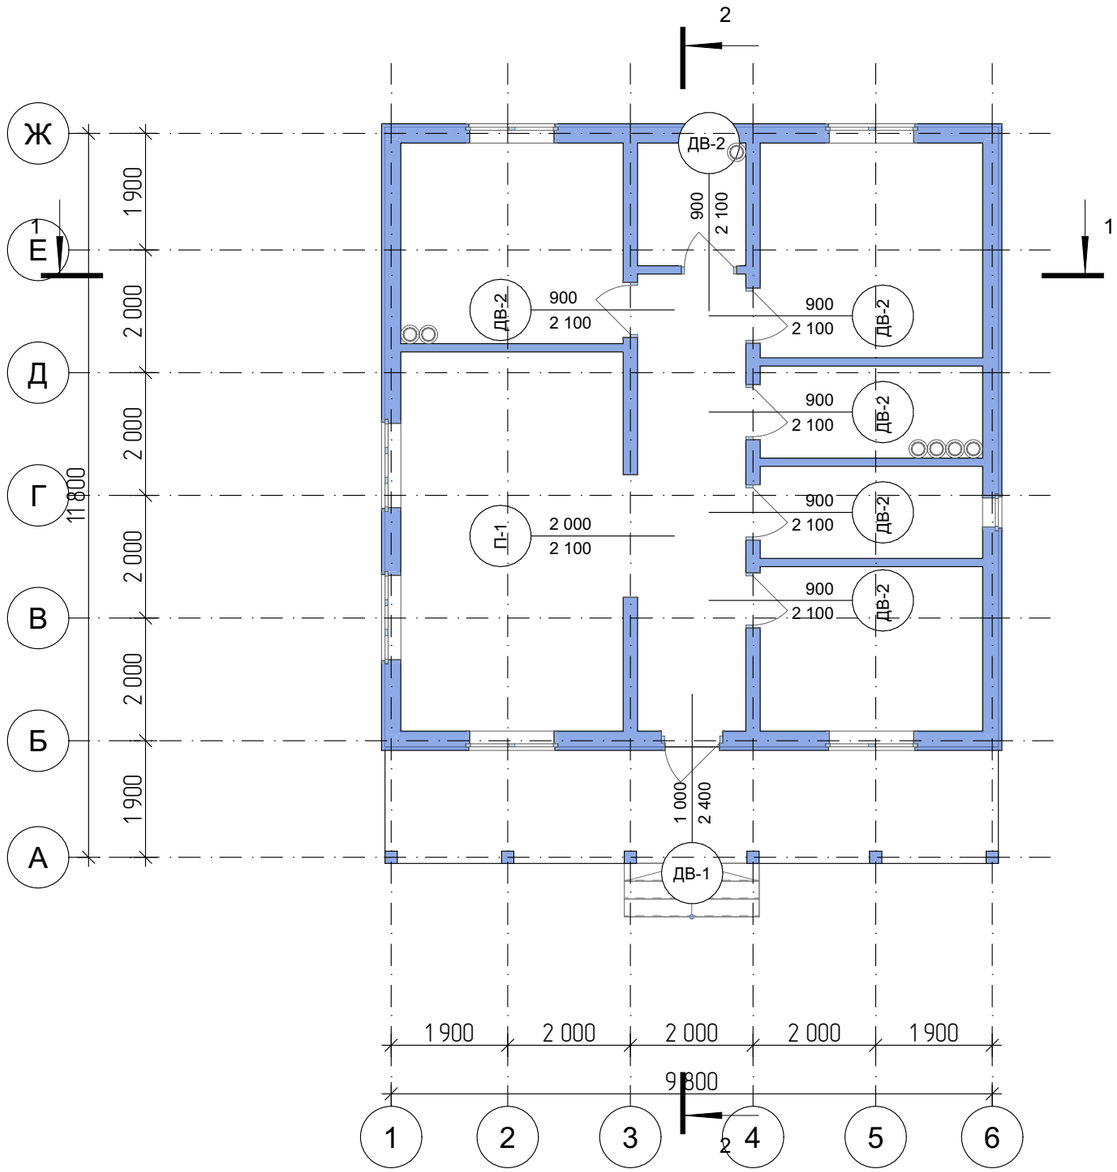


Марка, поз.	Размер проема в кладке, мм	Количество
ДВ-1	1 000×2 400	1
ДВ-2	900×2 100	6
П-1	2 000×2 100	1

						#ID Проекта		
						кадастровый номер Россия		
Изм.	Кол.уч.	Лист	№Док.	Подп.	Дата			
Разраб.						Индивидуальный жилой дом	Стадия	Лист	Листов
ГАП							#Стадия Проекта	26	
Маркировка дверных проемов первого этажа									


Тип	Марка, поз.	Размер проема в кладке, мм	Количество
Дверь, 1-й этаж			
	ДВ-1	1 000×2 400	1
	ДВ-2	900×2 100	6
	П-1	2 000×2 100	1
Окно, 1-й этаж			
	ОК-1	1 500×1 500	6
	ОК-2	600×1 500	1

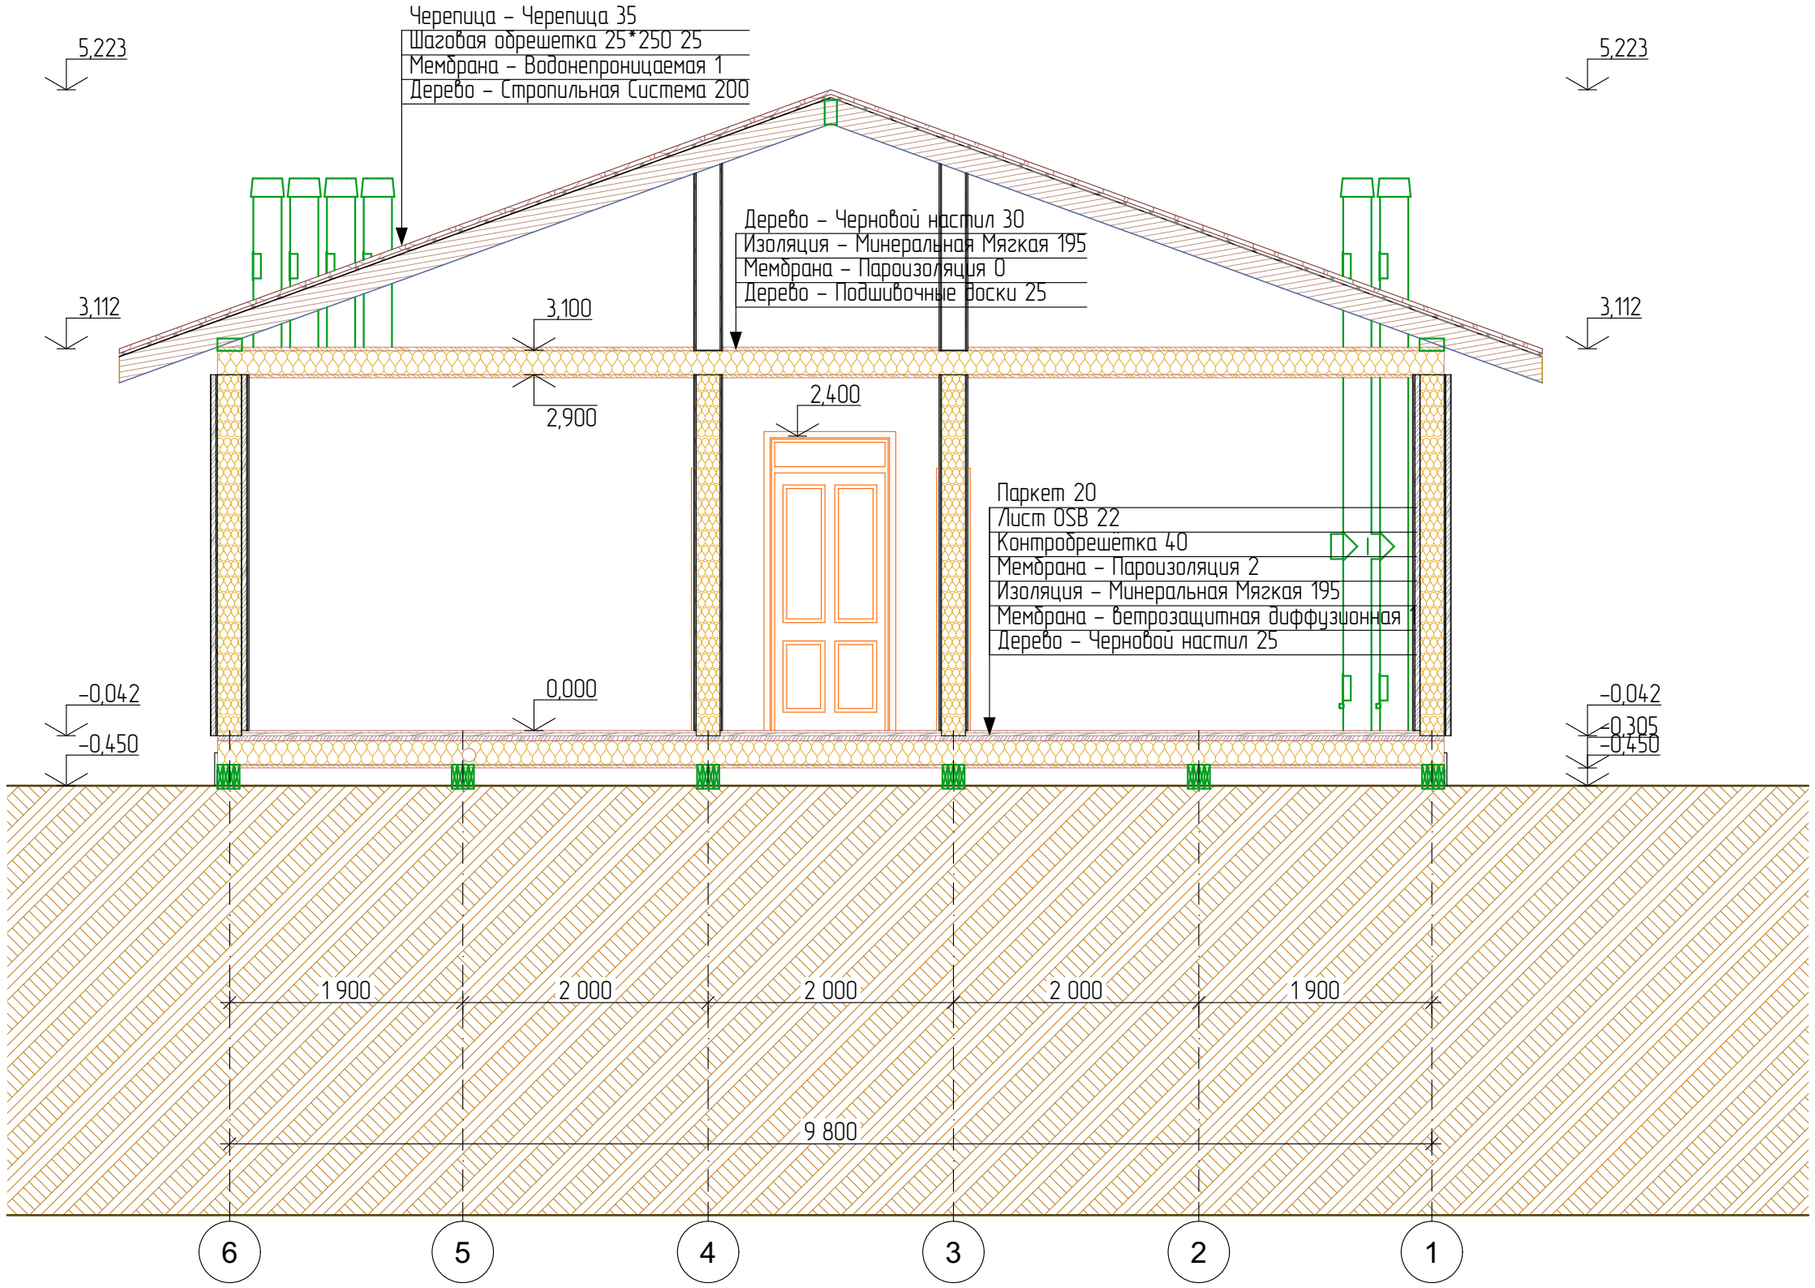

						#ID Проекта	
						кадастровый номер Россия	
Изм.	Кол.уч.	Лист	№Док.	Подп.	Дата		
Разраб.						Индивидуальный жилой дом	Стадия: #Стадия Проекта; Лист: 28; Листов:
ГАП							
						Разрез 1 - 1	

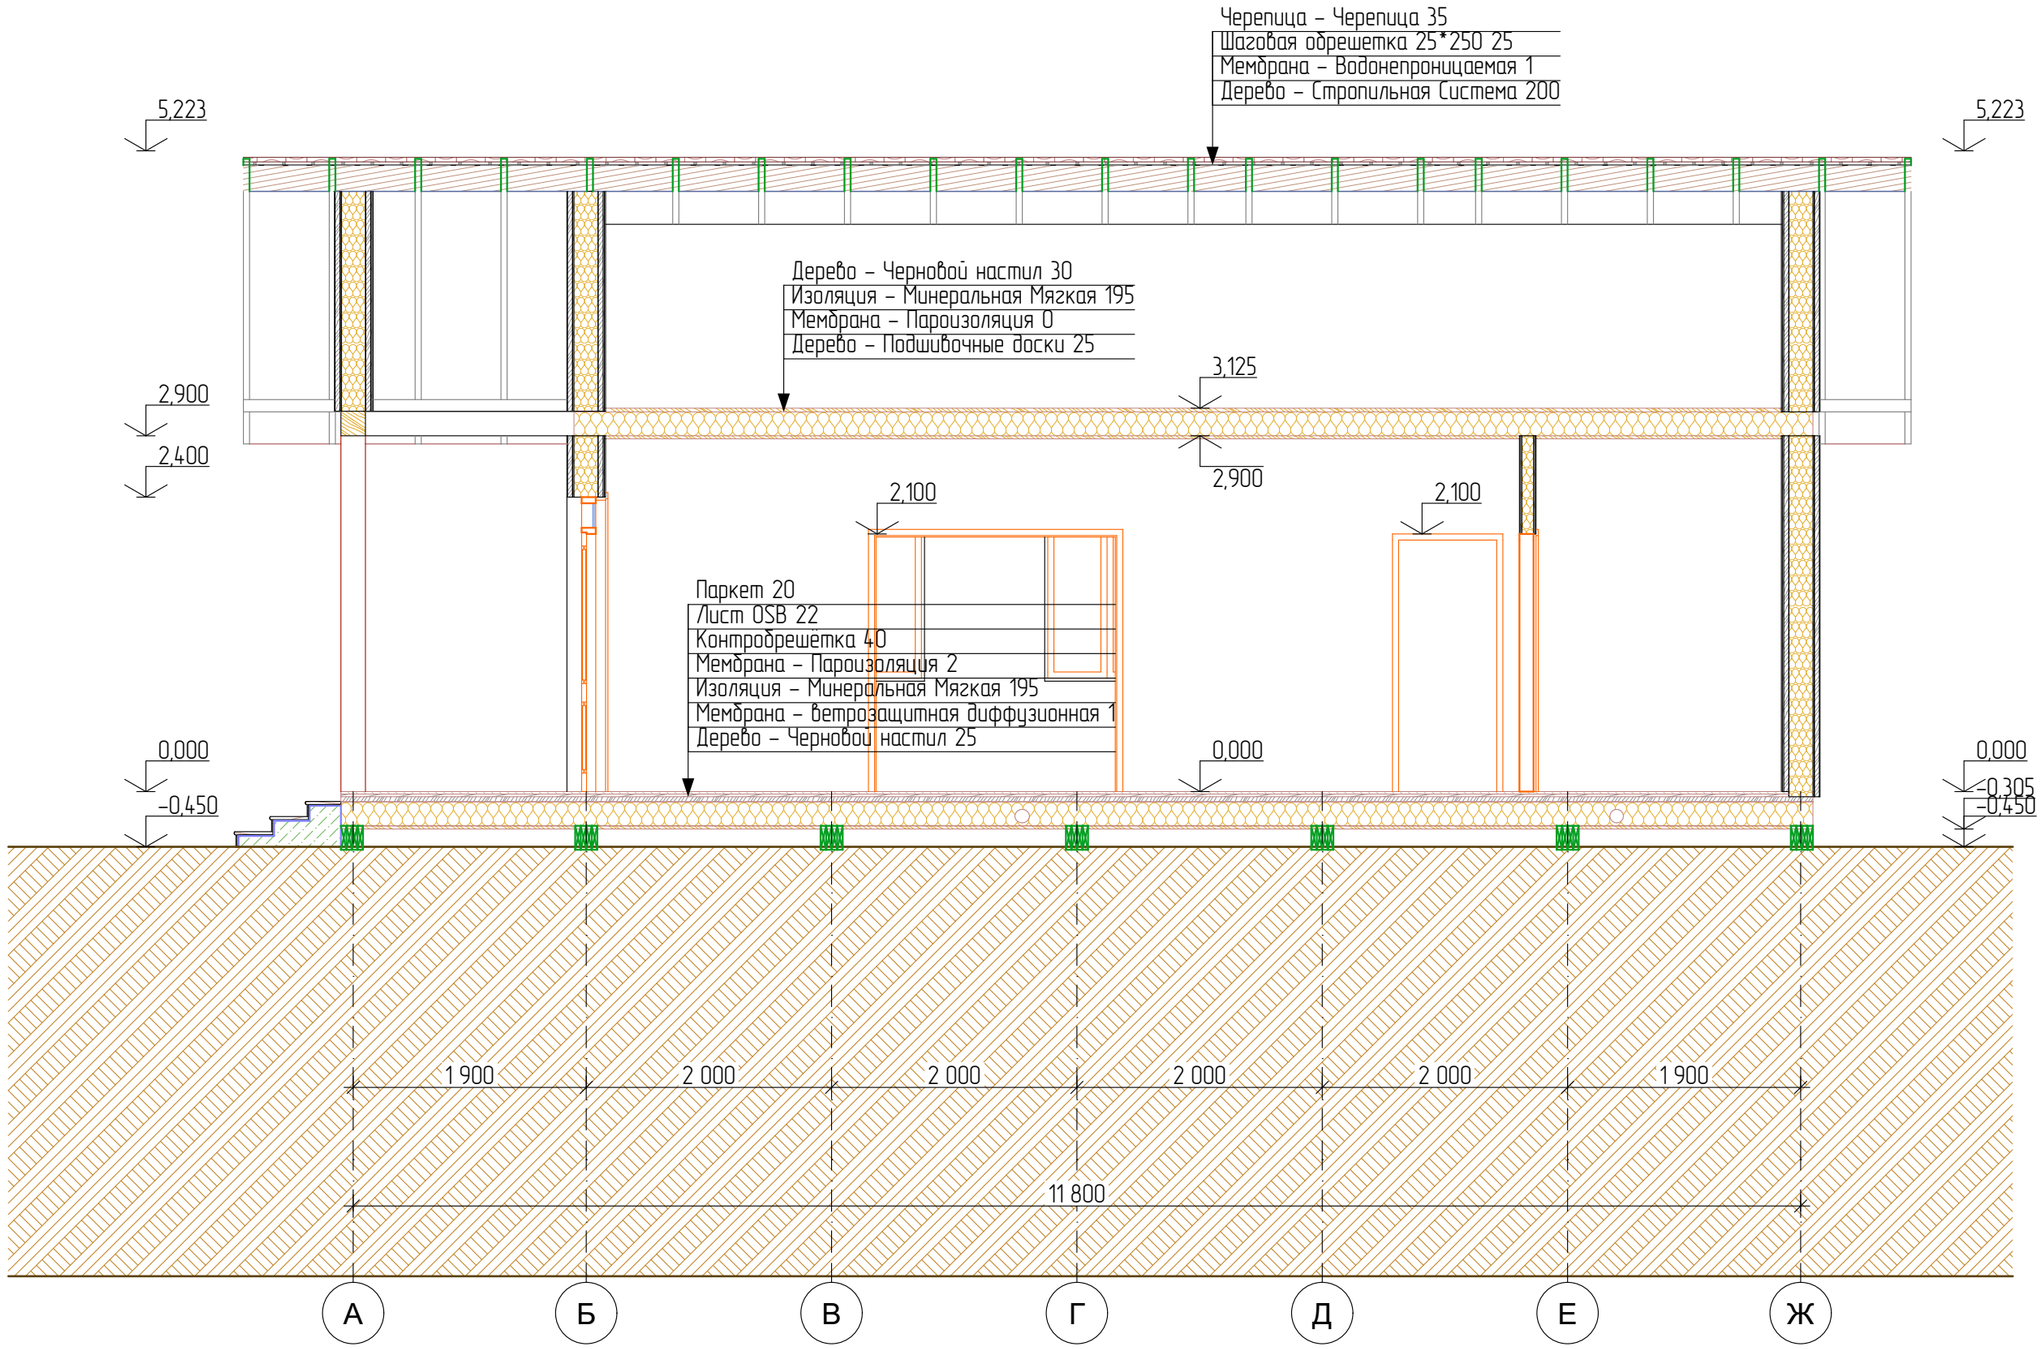

						#ID Проекта	
						кадастровый номер Россия	
Изм.	Кол.уч.	Лист	№Док.	Подп.	Дата		
Разраб.						Индивидуальный жилой дом	Стадия: #Стадия Проекта; Лист: 29; Листов:
ГАП							
Разрез 2 - 2							

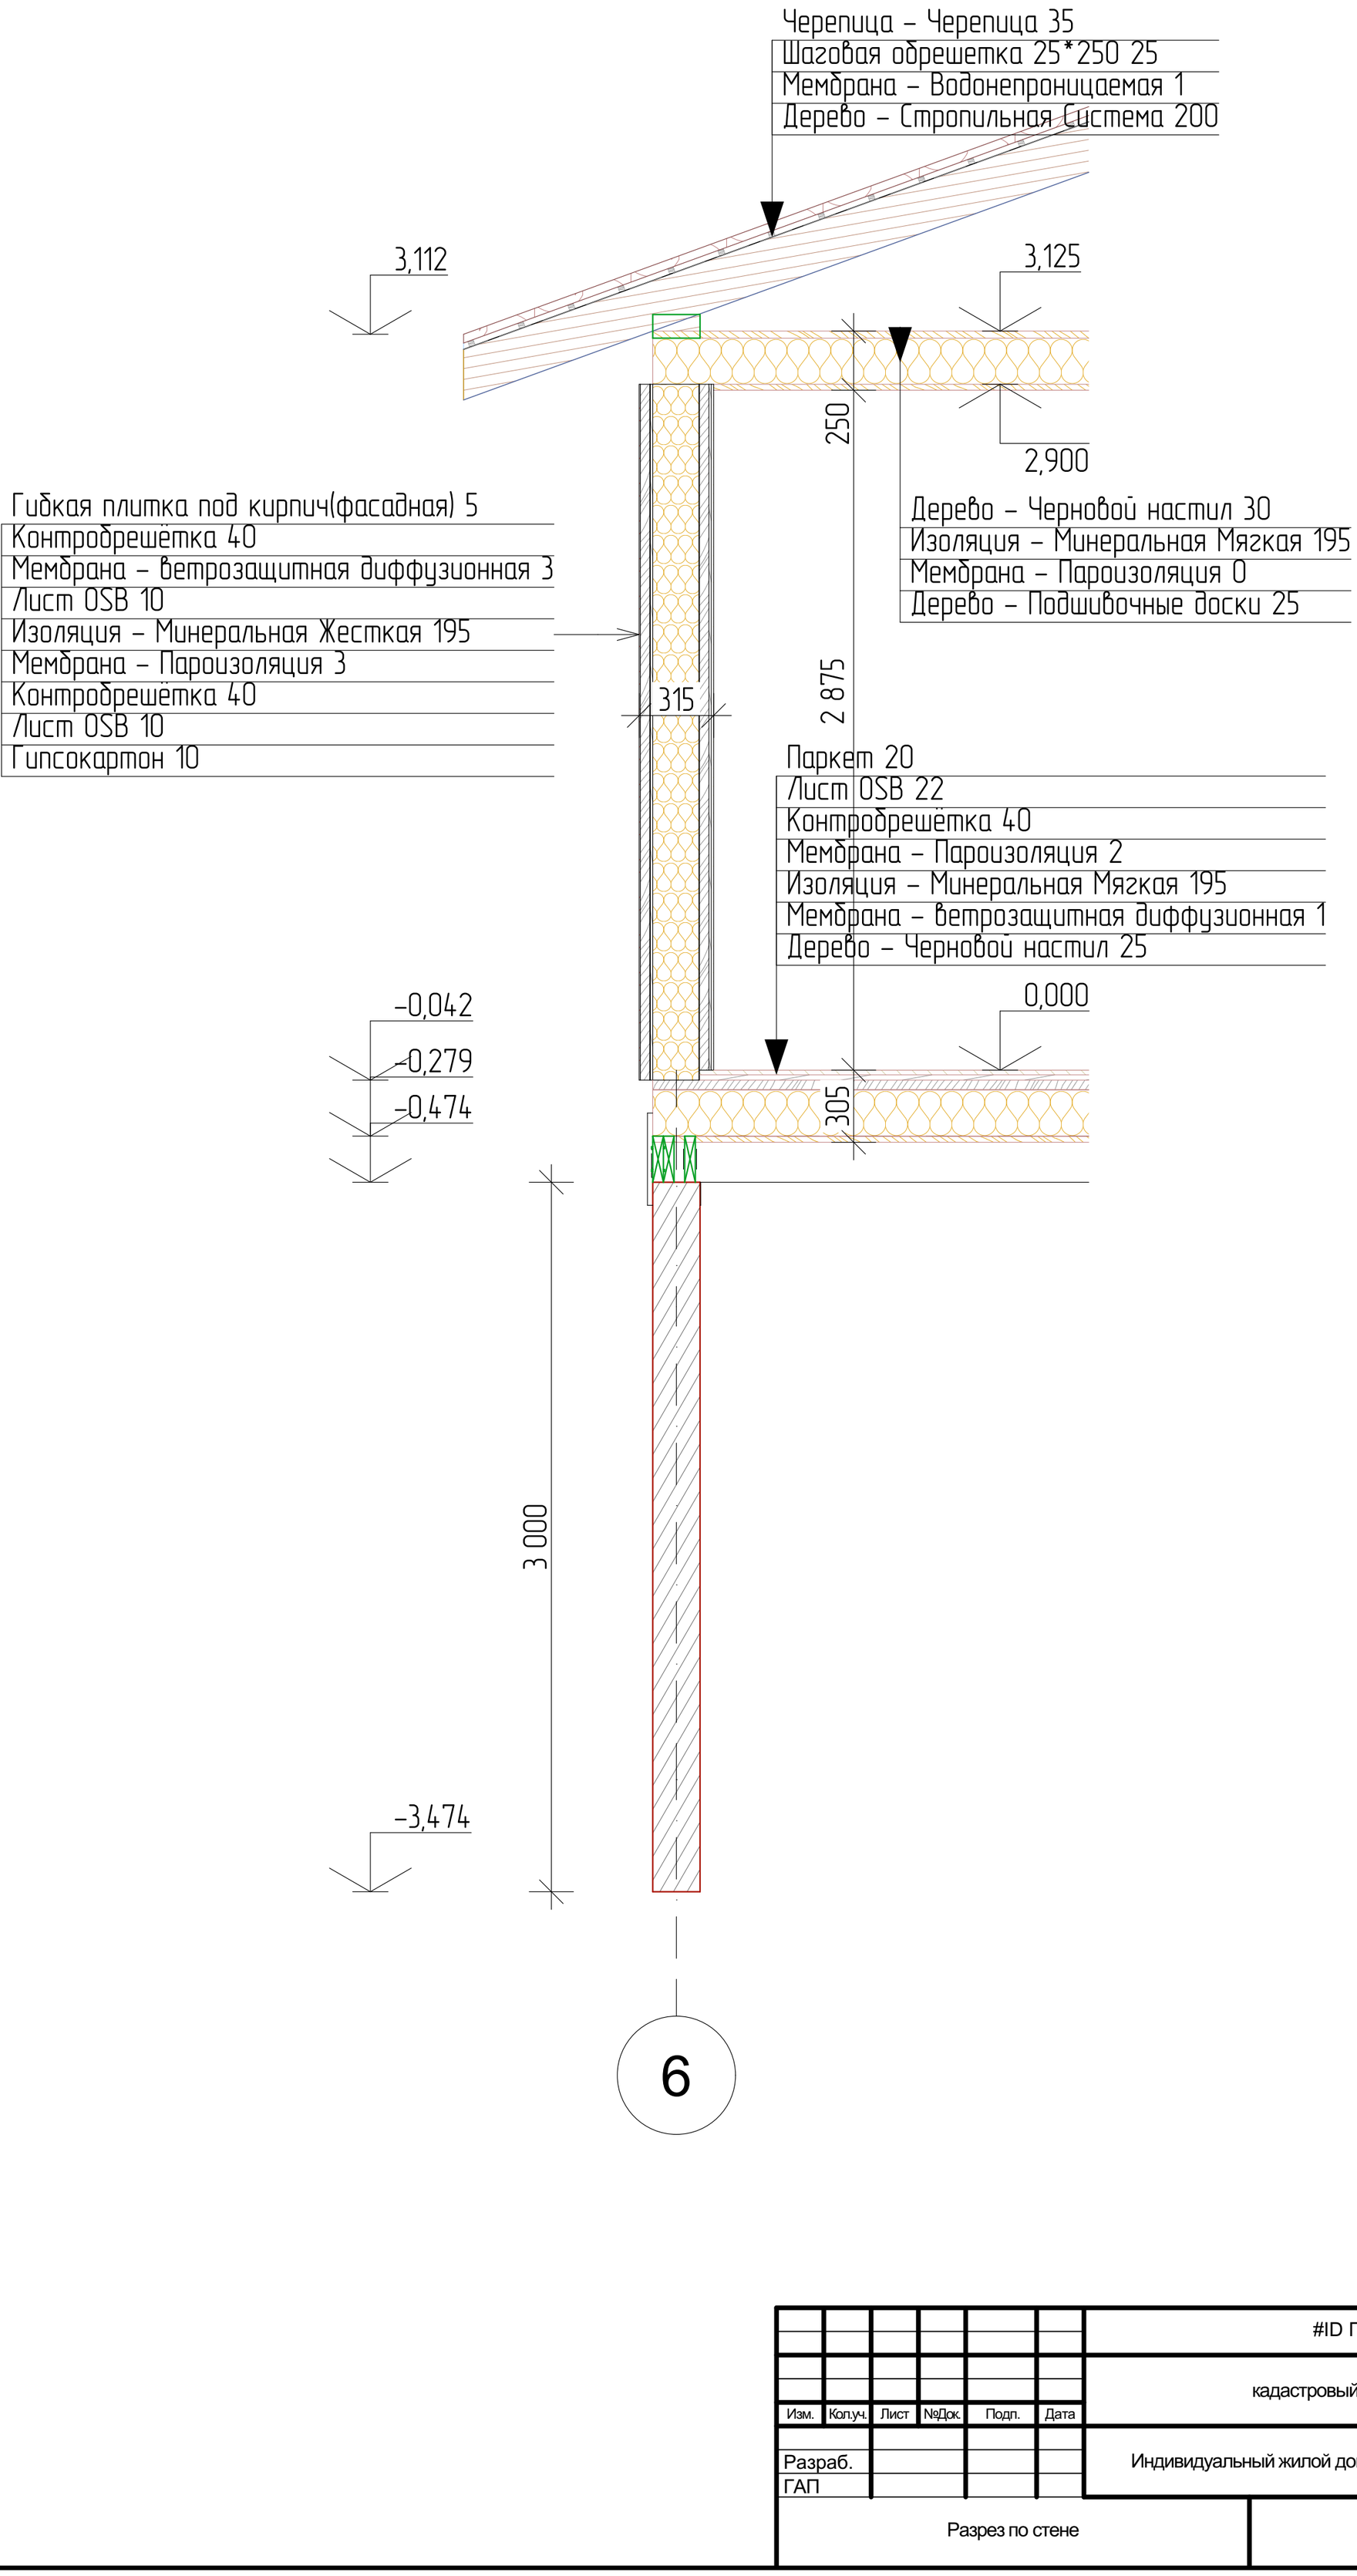

						#ID Проекта	
						кадастровый номер Россия	
Изм.	Кол.уч.	Лист	№Док.	Подп.	Дата		
Разраб.						Индивидуальный жилой дом	Стадия: #Стадия Проекта; Лист: 30; Листов:
ГАП							
Разрез по стене							

Пояснительная записка к устройству деревянного межэтажного перекрытия

Деревянное перекрытие выполняется в соответствии с проектной документацией и требованиями нормативных документов (СП 64.13330.2017 «Деревянные конструкции», СП 70.13330.2012 «Несущие и ограждающие конструкции»).

1. Подготовительные работы

- Проверить соответствие размеров и отметок несущих стен и опор проекту;
- Подготовить места опирания балок, при необходимости уложить гидроизоляционные прокладки (рубероид, битумная мастика);
- Заготовить балки сечением 200×50 мм, черновой и чистовой настил, утеплитель и крепёжные элементы;
- Все деревянные элементы обработать антисептическими и огнезащитными составами.

2. Устройство несущих балок

- Балки перекрытия устанавливаются с шагом согласно чертежам, что позволяет плотно укладывать утеплитель или звукоизоляцию;
- Опирание балок на стены или ригели должно быть не менее 150 мм;
- Концы балок, опираемые на стены, изолируются рулонными материалами от влаги;
- Балки выставляются в одной плоскости, горизонтальность проверяется лазерным уровнем (допуск ±5 мм на 2 м).

3. Черновой настил и пароизоляция

- С нижней стороны балок монтируется сплошной черновой настил из обрезной доски толщиной 25 мм;
- Настил укладывается плотно, без щелей, крепится к балкам гвоздями или саморезами;
- Поверх чернового настила укладывается сплошной слой пароизоляционной плёнки с нахлёстом 150–200 мм и проклейкой стыков.

4. Утепление и звукоизоляция

- Пространство между балками заполняется плитным утеплителем или звукоизоляцией в зависимости от назначения перекрытия;
- Ширина плит должна соответствовать шагу балок (600 мм) и обеспечивать плотную укладку;
- Толщина утеплителя определяется проектом, работы выполняются строго в соответствии с проектной документацией.

5. Чистовой настил (верхний слой перекрытия)

- По верхней плоскости балок укладывается настил из доски толщиной 30 мм;
- Доски прибиваются гвоздями или фиксируются саморезами к каждой балке;
- Настил выполняется сплошным, с плотным примыканием досок;
- Допустимое отклонение по горизонту — ±10 мм на всё перекрытие.

6. Работы в зимнее время


- Деревянные элементы должны быть сухими (влажность не более 20%);
- Запрещается применять отсыревшие или обледеневшие материалы;
- Утеплитель укладывается в сухом состоянии, с последующим контролем после прогрева помещений.

7. Контроль качества

- Проверяется правильность установки балок (сечение 200×50 мм, шаг 600 мм), надёжность креплений и горизонтальность;
- Контролируется плотность укладки утеплителя и герметичность пароизоляции;
- Проверяется качество чернового и чистового настила (отсутствие щелей, ровность поверхности);
- Все деревянные элементы должны быть обработаны антисептическими и огнезащитными составами;
- Работы выполняются в соответствии с требованиями СП 64.13330.2017 и СП 70.13330.2012.




						#ID Проекта		
						кадастровый номер Россия		
Изм.	Кол.уч.	Лист	№Док.	Подп.	Дата			
Разраб.						Индивидуальный жилой дом	Стадия: #Стадия Проекта	Лист: 31 / Листов:
ГАП								
ПЗ - Деревянное перекрытие								

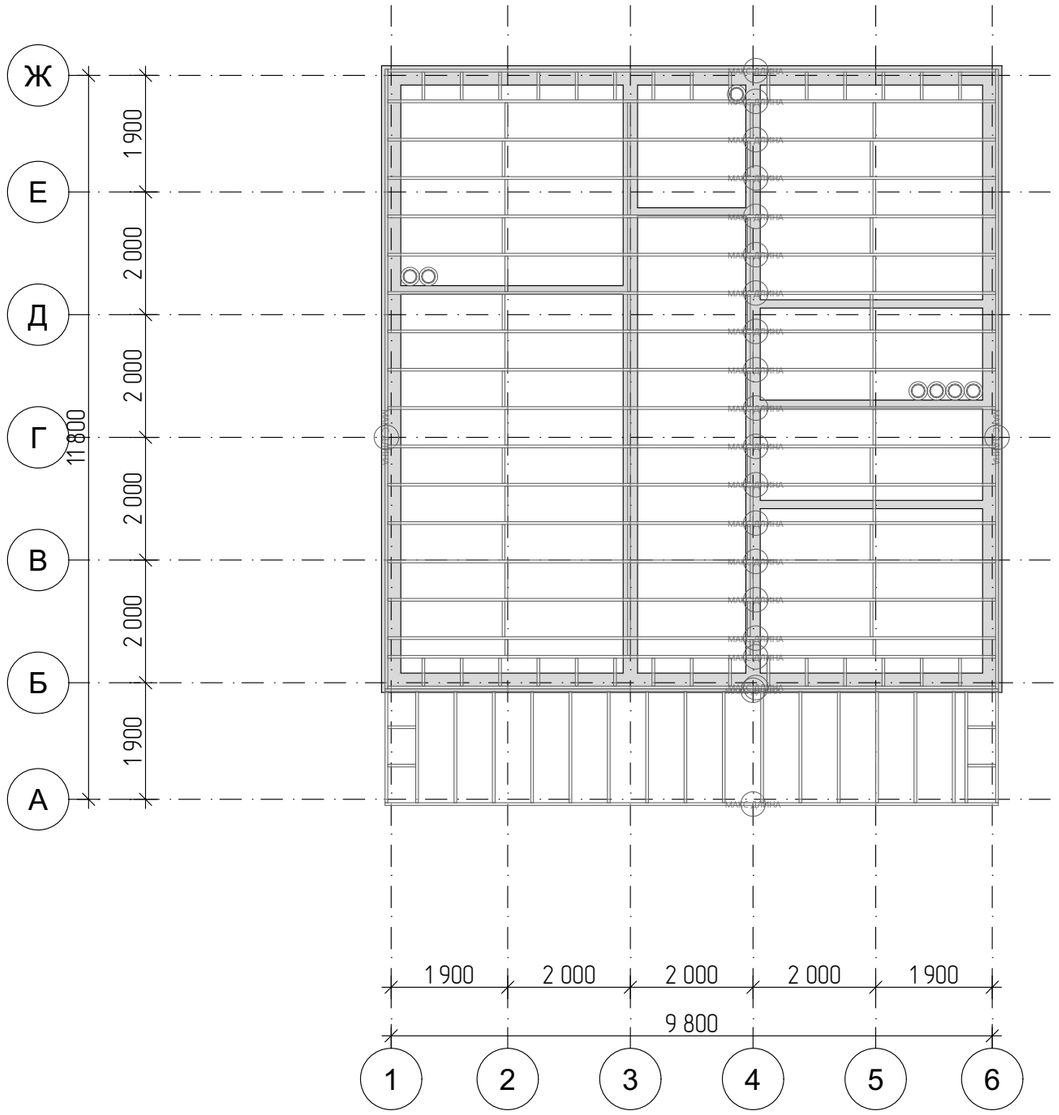

						#ID Проекта		
						кадастровый номер Россия		
Изм.	Кол.уч.	Лист	№Док.	Подп.	Дата			
Разраб.						Индивидуальный жилой дом	Стадия: #Стадия Проекта	Лист: 32 / Листов:
ГАП								
План перекрытия +0,000								


Вид каркаса снаружи

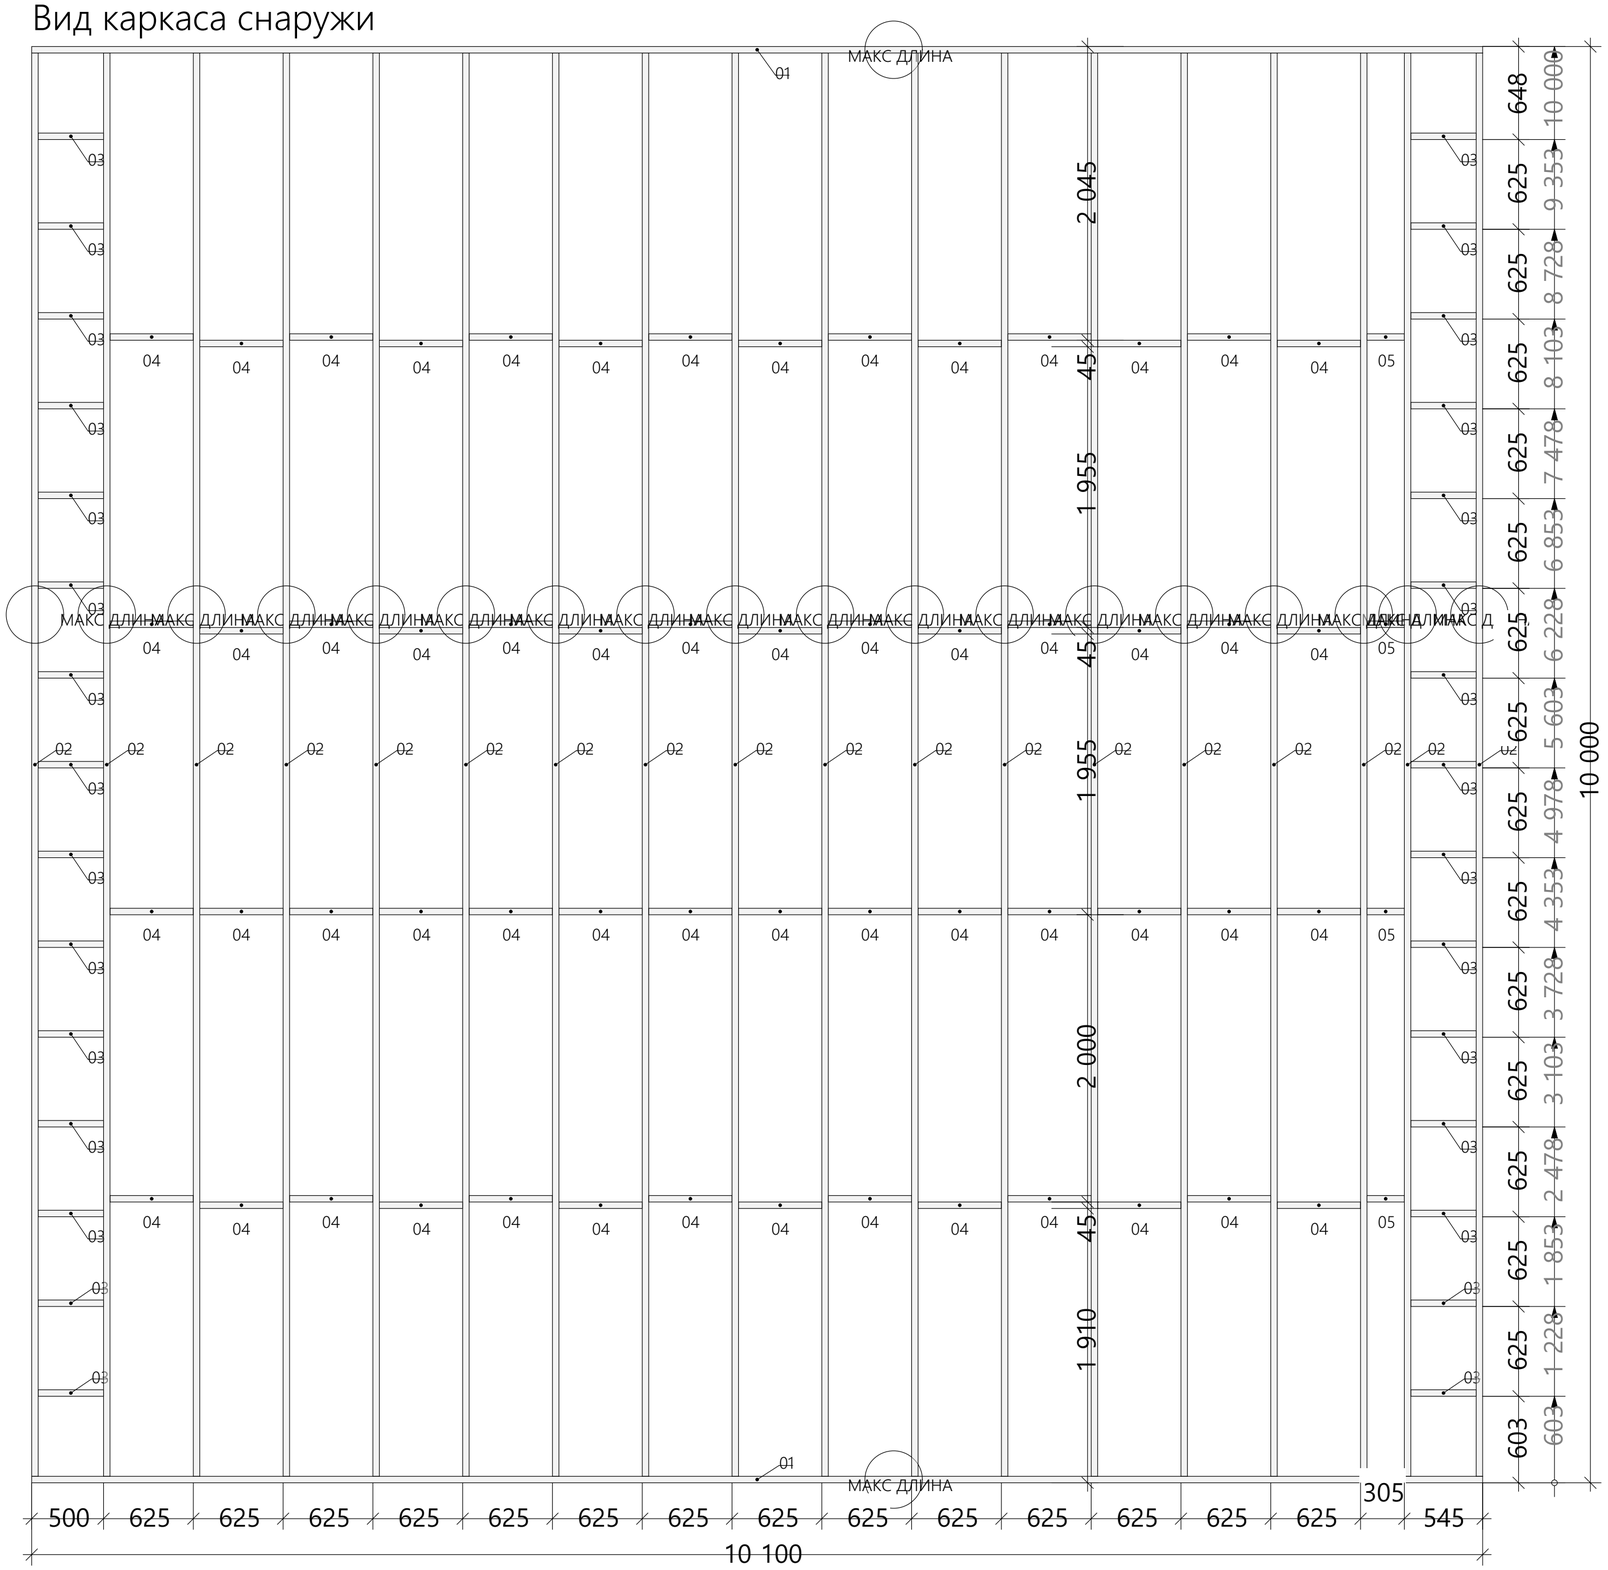

Основной каркас №Пол (дом)


Номер	Название	Сечение, мм	Длина, мм	Кол-во, шт	Объем, м3
Пол (дом)-01	Балка	45x195	10100	2	0.177
Пол (дом)-02	Балка	45x195	9910	18	1.565
Пол (дом)-03	Распорка перекрытия	45x195	455	30	0.120
Пол (дом)-04	Балка	45x195	580	56	0.285
Пол (дом)-05	Балка	45x195	260	4	0.009
			Общая сумма:	110	2.156

Вид каркаса сверху

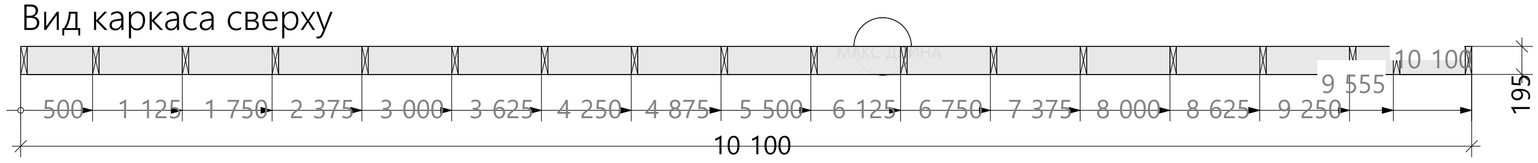

						#ID Проекта	
						кадастровый номер Россия	
Изм.	Колуч.	Лист	№Док.	Подп.	Дата		
Разраб.						Индивидуальный жилой дом	Стадия: #Стадия Проекта; Лист: 33; Листов:
ГАП							
Чертеж каркаса перекрытия № Пол (дом) #1							


Вид каркаса снаружи

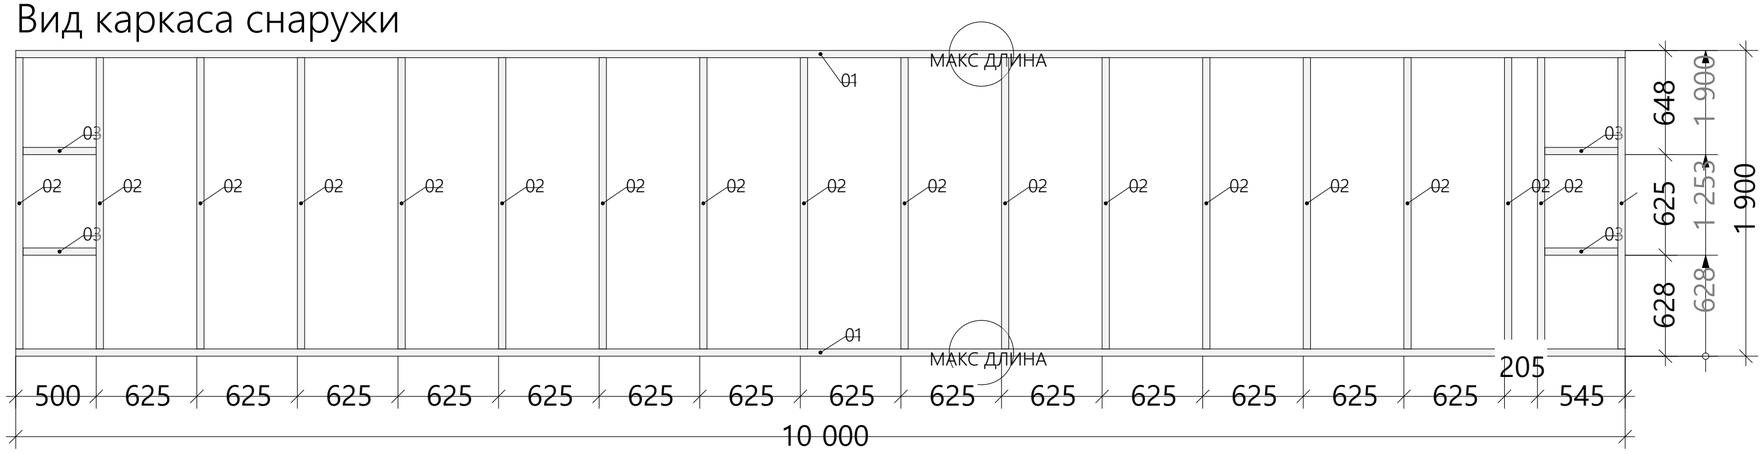


Основной каркас №Пол (Терраса)


Номер	Название	Сечение, мм	Длина, мм	Кол-во, шт	Объем, м3
Пол (Терраса)-01	Балка	45x195	10000	2	0.176
Пол (Терраса)-02	Балка	45x195	1810	18	0.286
Пол (Терраса)-03	Распорка перекрытия	45x195	455	4	0.016
			Общая сумма:	24	0.477


Вид каркаса сверху

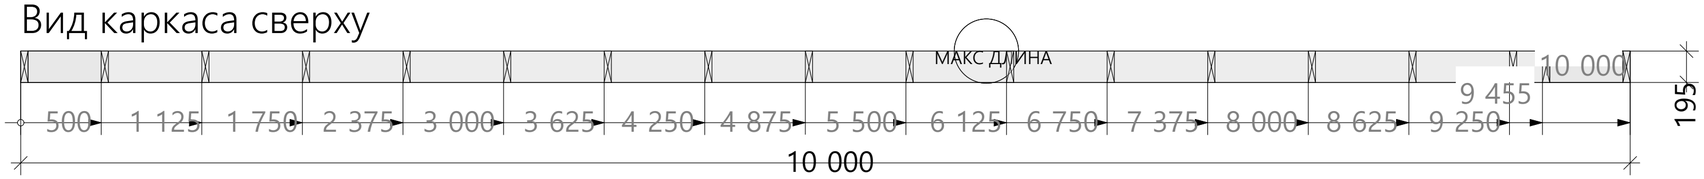

						#ID Проекта	
						кадастровый номер Россия	
Изм.	Колуч.	Лист	№Док.	Подп.	Дата		
Разраб.						Индивидуальный жилой дом	Стадия: #Стадия Проекта; Лист: 34; Листов:
ГАП							
Чертеж каркаса перекрытия № Пол (Терраса) #1							

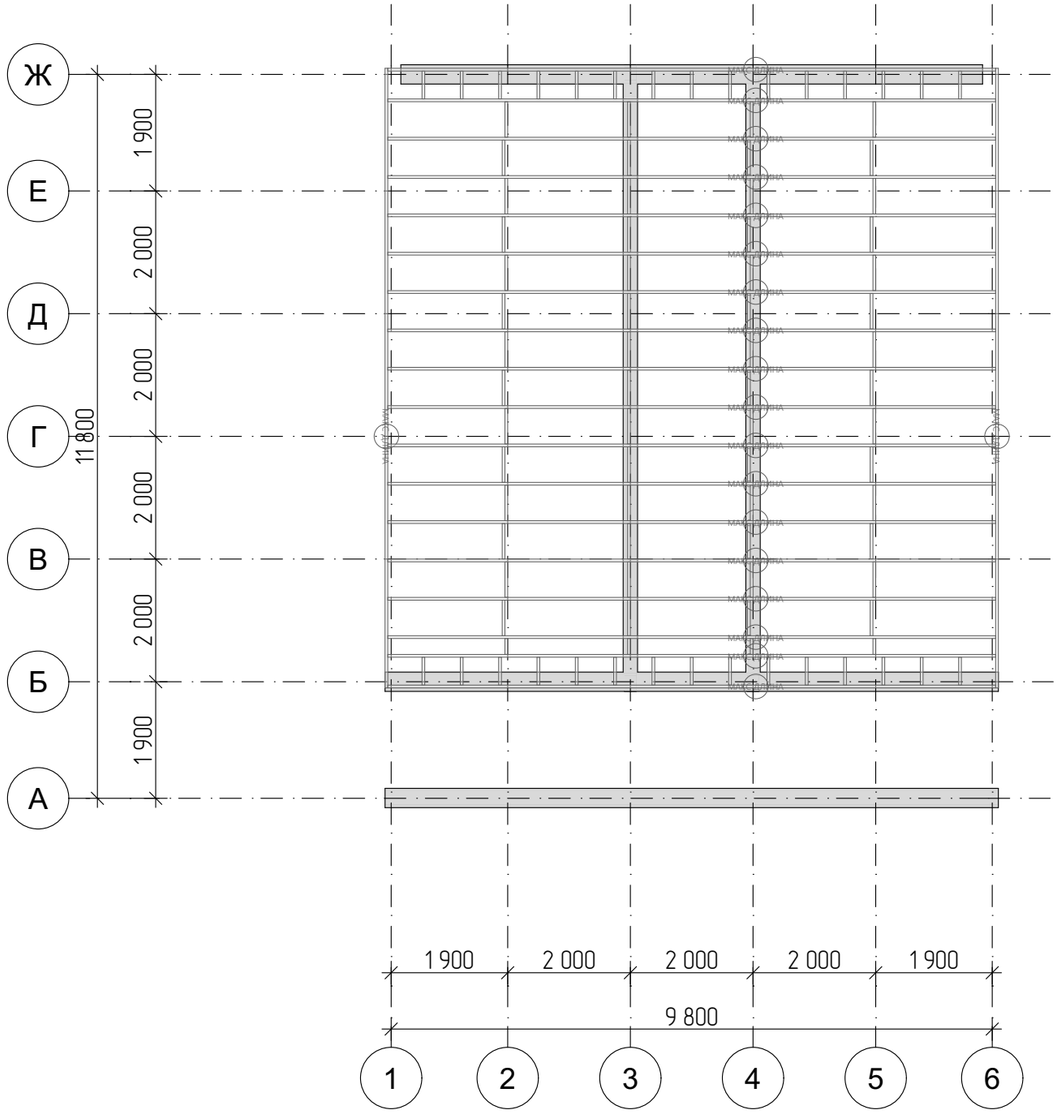


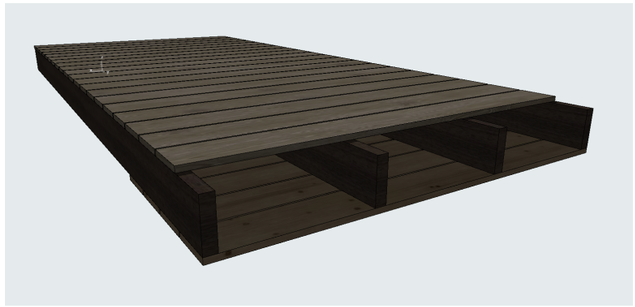

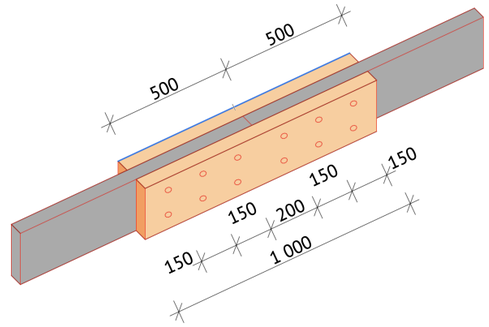

						#ID Проекта	
						кадастровый номер Россия	
Изм.	Кол.уч.	Лист	№Док.	Подп.	Дата		
Разраб.						Индивидуальный жилой дом	Стадия: #Стадия Проекта; Лист: 35; Листов:
ГАП							
План перекрытий на отм 3,100							


Вид каркаса снаружи

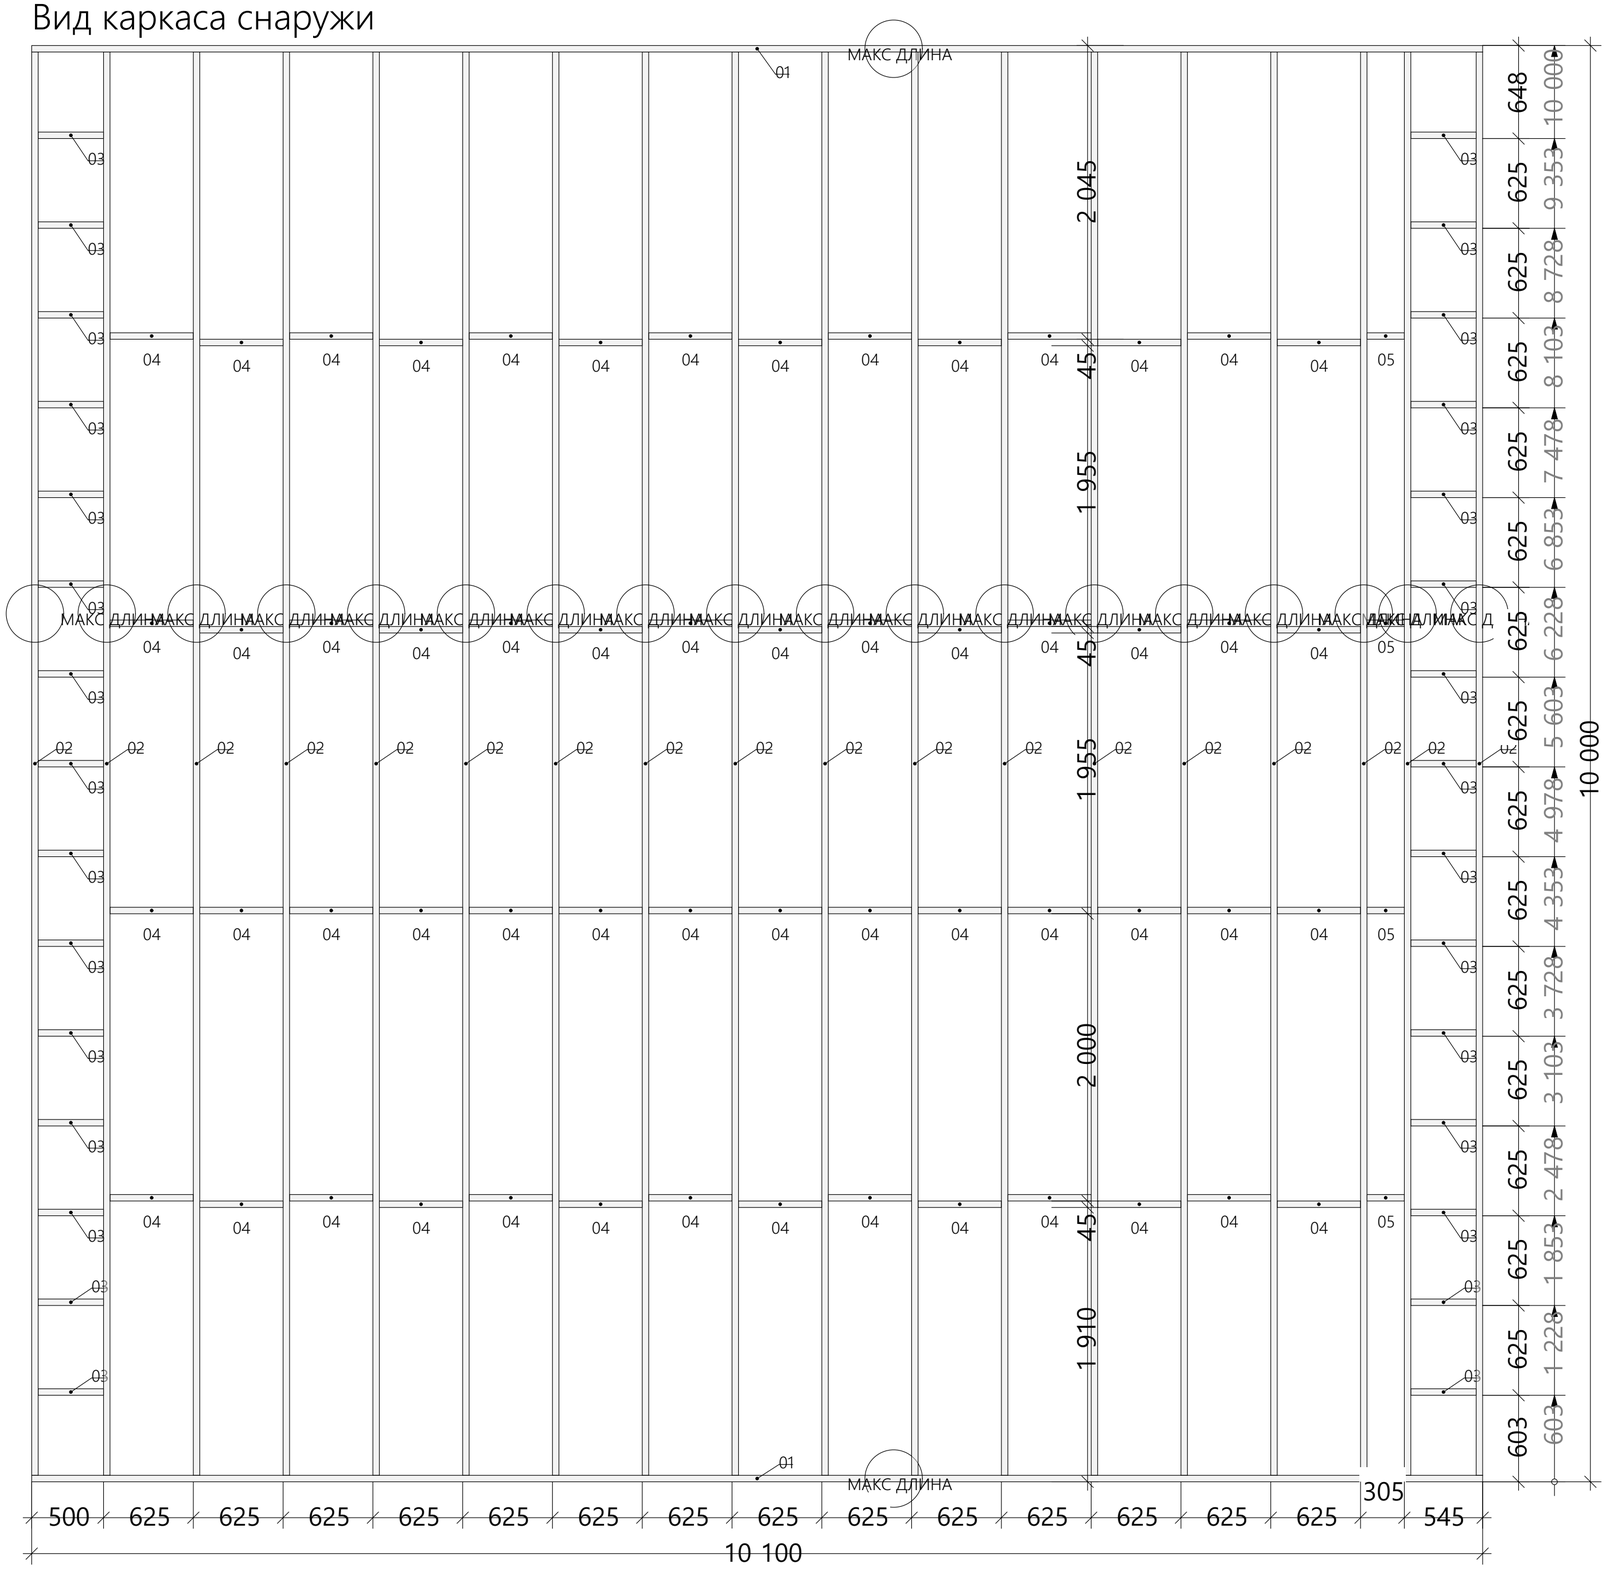

Основной каркас №Чердачное перекрытие

Номер	Название	Сечение, мм	Длина, мм	Кол-во, шт	Объем, м3
Чердачное перекрытие-01	Балка	45x195	10100	2	0.177
Чердачное перекрытие-02	Балка	45x195	9910	18	1.565
Чердачное перекрытие-03	Распорка перекрытия	45x195	455	30	0.120
Чердачное перекрытие-04	Распорка перекрытия	45x195	580	56	0.285
Чердачное перекрытие-05	Распорка перекрытия	45x195	260	4	0.009
			Общая сумма:	110	2.156

Вид каркаса сверху

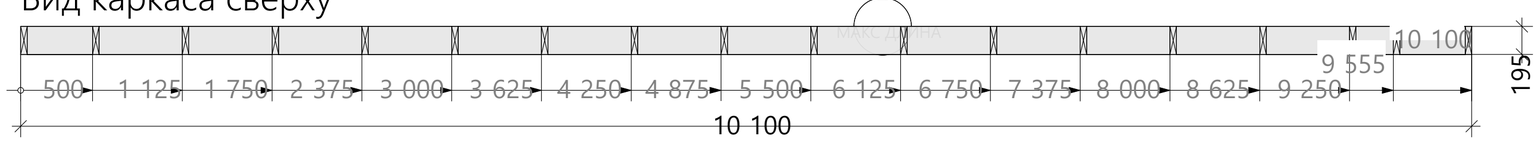

						#ID Проекта	
						кадастровый номер Россия	
Изм.	Кол.уч.	Лист	№Док.	Подп.	Дата		
Разраб.						Индивидуальный жилой дом	Стадия: #Стадия Проекта; Лист: 36; Листов:
ГАП							
Чертеж каркаса перекрытия № Чердачное перекр #1							

н Ведомость перекрытий (Каркасный Дом)	
Этаж	Объем, м3
1-й этаж, Пол (дом)-01	
	0,18
1-й этаж, Пол (дом)-02	
	1,62
1-й этаж, Пол (дом)-03	
	0,00
1-й этаж, Пол (дом)-04	
	0,56
1-й этаж, Пол (дом)-05	
	0,00
1-й этаж, Пол (Терраса)-01	
	0,18
1-й этаж, Пол (Терраса)-02	
	0,36
1-й этаж, Пол (Терраса)-03	
	0,00
Чердак, Чердачное перекрытие-01	
	0,18
Чердак, Чердачное перекрытие-02	
	1,62
Чердак, Чердачное перекрытие-03	
	0,00
Чердак, Чердачное перекрытие-04	
	0,56
Чердак, Чердачное перекрытие-05	
	0,00
	5,26 м³

Пояснительная записка к устройству скатной кровли

Скатная кровля выполняется в соответствии с проектной документацией и требованиями нормативных документов (СП 17.13330.2017 «Кровли», СП 64.13330.2017 «Деревянные конструкции», СП 70.13330.2012 «Несущие и ограждающие конструкции»).

1. Общие положения

- На представленном проекте отражён план расположения стропил, однако конструктивная часть кровли не проработана в полном объёме: отсутствуют узлы сопряжений, крепёжные решения, элементы жёсткости (ригелей, стоек, подкосов, прогонов и др.).
- Для обеспечения надёжности и пространственной жёсткости стропильной системы требуется дополнительная проработка в разделе КР.
- До разработки конструктивного решения допускается вести только подготовительные работы и укрупнённый монтаж с временными креплениями.

2. Стропильная система

- Основными несущими элементами скатной кровли являются стропила, в нашем случае балки сечением 200×50 мм;
- Шаг установки стропил принимается в соответствии с проектом, исходя из расчётной нагрузки на кровлю и применяемого покрытия;
- Нижние концы стропил опираются на мауэрлат, верхние соединяются в коньковом узле. В проекте данный узел не разработан, требуется уточнение способа сопряжения (врубка, металлические накладки, болтовые соединения);
- Для восприятия распорных усилий и предотвращения деформации стропильной системы необходимо предусмотреть дополнительные элементы — ригели, затяжки, стойки, подкосы, которые должны быть отражены в разделе КР;
- При необходимости устройства больших пролётов должны применяться прогоны с опиранием на стойки.

3. Мауэрлат

- В качестве мауэрлата применяется брус сечением 200×100 мм;
- Мауэрлат укладывается по верхнему ряду стен на гидроизоляционный слой (рулонные материалы в два слоя);
- Крепление мауэрлата выполняется анкерными болтами или шпильками, заранее выпущенными из монолитного армопояса;
- Проверяется правильность укладки и горизонтальность мауэрлата, так как он является базовым опорным элементом всей стропильной системы.

4. Крепление стропил

- Стропила к мауэрлату крепятся гвоздевыми соединениями, болтами, металлическими уголками или перфорированными пластинами в зависимости от выбранного узла;
- Узел крепления должен исключать скольжение и смещение стропил под нагрузкой;
- Дополнительно должны предусматриваться связи для предотвращения «разъезда» стропил.

5. Особенности конструкции

- В проекте отражено только расположение стропил, без конструктивного обеспечения жёсткости. Для нормальной работы системы необходимо разработать рабочие чертежи с указанием:


– узла конька;
– соединения стропил с мауэрлатом;
– устройства ригелей, затяжек и прогона;
– крепления стропил между собой и к вспомогательным элементам.

- Отсутствие этих решений влечёт риск недостаточной устойчивости кровли при ветровых и снеговых нагрузках.

6. Контроль качества

- Проверяется правильность установки стропил (сечение 200×50 мм, шаг по проекту);
- Контролируется горизонтальность мауэрлата и симметрия скатов;
- Оценивается качество креплений и прочность узлов;
- Все деревянные элементы должны быть обработаны антисептическими и огнезащитными составами;
- Работы выполняются в соответствии с требованиями СП 17.13330.2017, СП 64.13330.2017 и СП 70.13330.2012.

						#ID Проекта		
						кадастровый номер Россия		
Изм.	Кол.уч.	Лист	№Док.	Подп.	Дата			
Разраб.						Индивидуальный жилой дом	Стадия: #Стадия Проекта	Лист: 38 / Листов:
ГАП								
ПЗ - Скатная кровля								

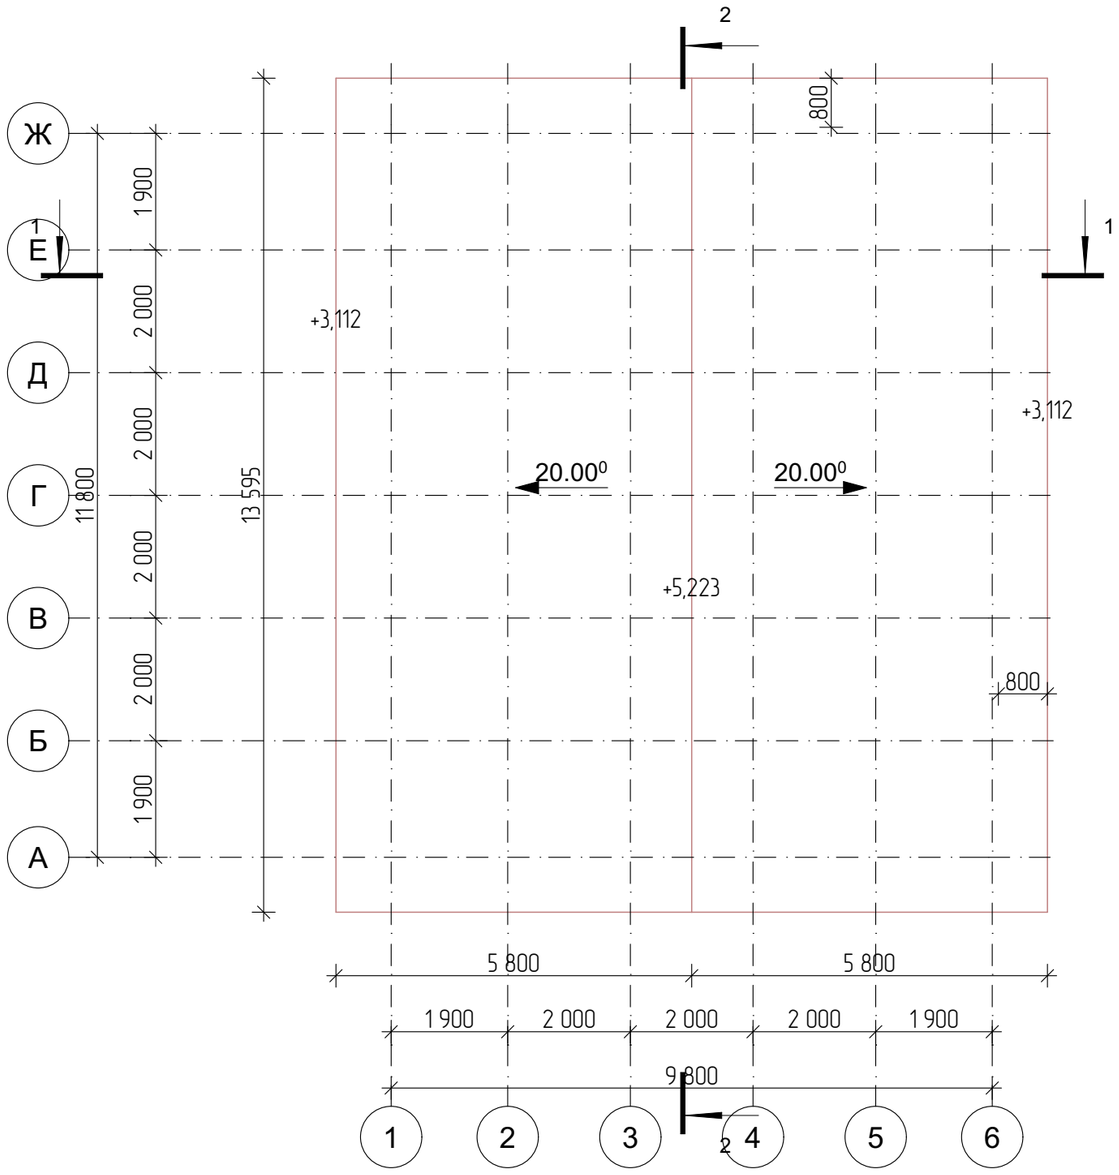

						#ID Проекта	
						кадастровый номер Россия	
Изм.	Кол.уч.	Лист	№Док.	Подп.	Дата		
Разраб.						Индивидуальный жилой дом	Стадия: #Стадия Проекта; Лист: 39; Листов:
ГАП							
План кровли							


ВЕДОМОСТЬ СТРОПИЛЬНОЙ СИСИТЕМЫ		
Уровень	**Наименование**	Объем, м3
Чердак	Контробрешетка 50х50	0,84
Чердак	Коньковый брус 200х100	0,27
Чердак	Мауэрлат 100х200	0,54
Чердак	Стропильная нога 200х50	2,52
		4,17 м³


Состав кровли		
Элемент	Наименование	Площадь, м2
Кровля дома		
	Мембрана - Водонепроницаемая	167,84
	Черепица - Черепица	168,16
	Шаговая обрешетка 25*250	168,08

Ведомость кровельного материала	
Наименование	Площадь, м2
Кровля дома	167,82
	167,82 м²


ВЕДОМОСТЬ НА УТЕПЛИТЕЛЬ (кровля)				
	Наименование	Компоненты		
		Толщина, мм	Объем, м3	Площадь, м2
Чердак				
	Изоляция - Минеральная Жесткая	195	5,24	26,90
	Изоляция - Минеральная Мягкая	195	19,70	101,00


						#ID Проекта	
						кадастровый номер Россия	
Изм.	Кол.уч.	Лист	№Док.	Подп.	Дата		
Разраб.						Индивидуальный жилой дом	Стадия: #Стадия Проекта; Лист: 40; Листов:
ГАП							
Ведомость кровельного пирога							

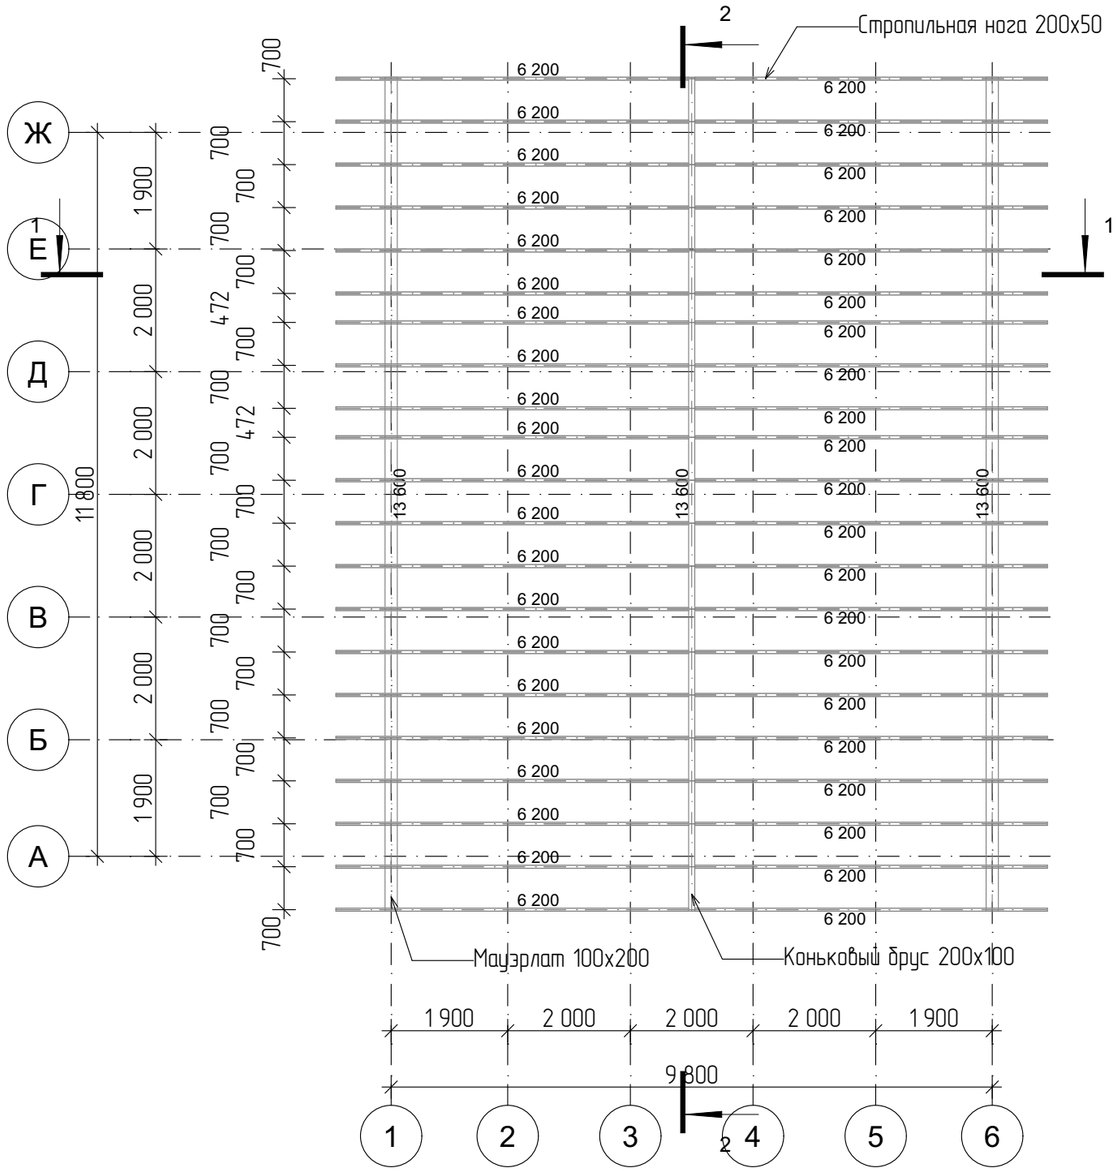

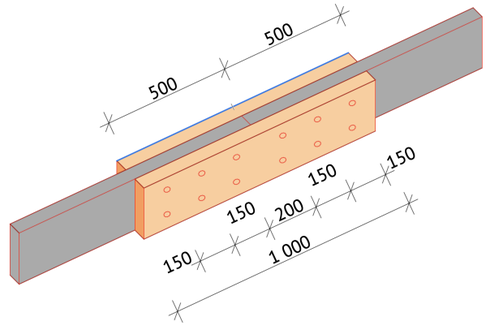

						#ID Проекта		
						кадастровый номер Россия		
Изм.	Кол.уч.	Лист	№Док.	Подп.	Дата			
Разраб.						Индивидуальный жилой дом	Стадия: #Стадия Проекта	Лист: 41 / Листов:
ГАП								
Схема расположения стропил								

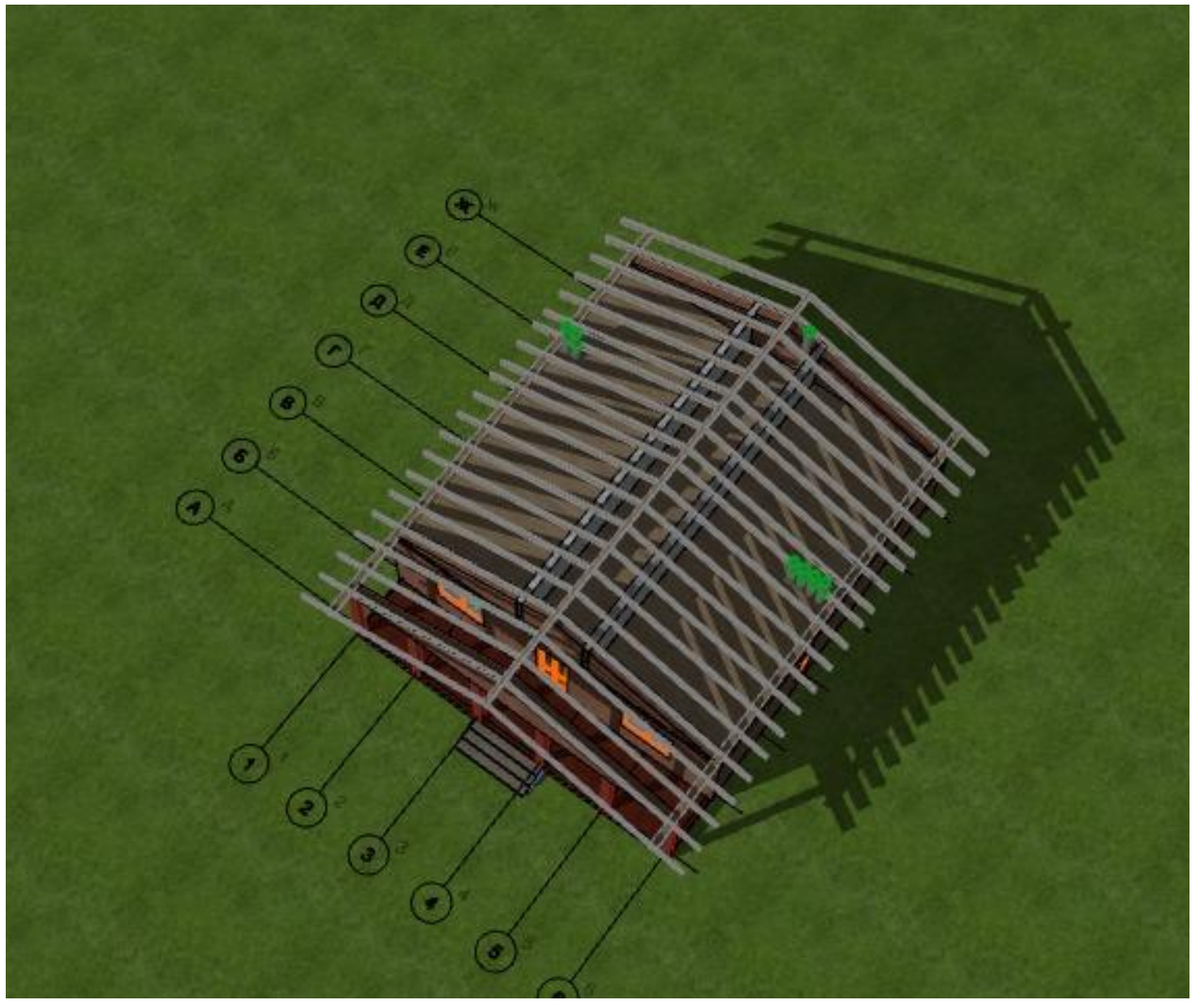


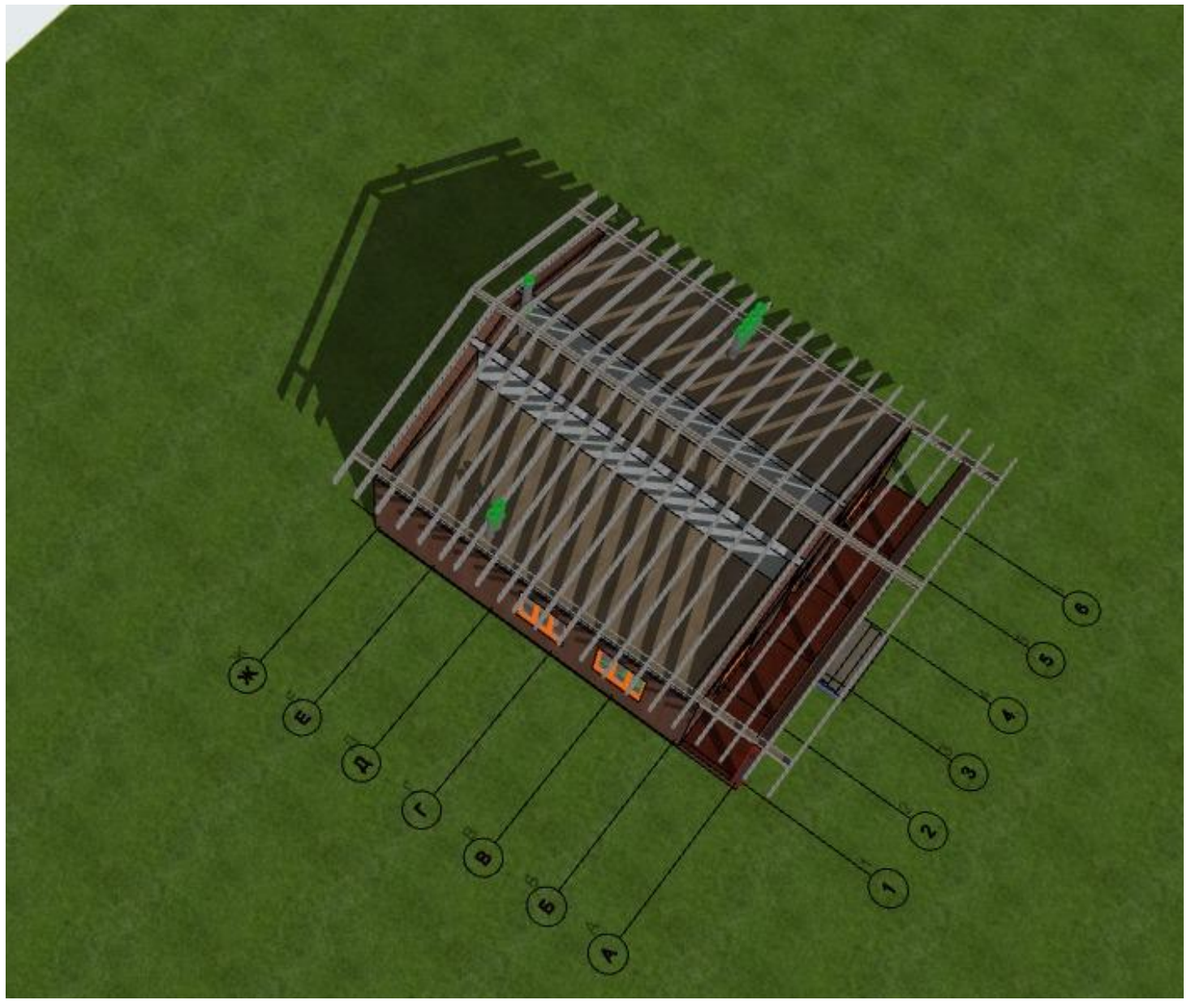


						#ID Проекта		
						кадастровый номер Россия		
Изм.	Кол.уч.	Лист	№Док.	Подп.	Дата			
Разраб.						Индивидуальный жилой дом	Стадия	Лист	Листов
ГАП							#Стадия Проекта	42	
3Д Вид стропильной системы									

ИКК-03 Стропильная система				
Наименование	Округленный Размер Пиломатериала	Длина, мм	Кол-во	Объем, м3
Контробрешетка 50х50				
	6 150	5 750	42	0,84
Коньковый брус 200х100				
	13 600	13 595	1	0,27
Мауэрлат 100х200				
	13 600	13 595	2	0,54
Стропильная нога 200х50				
	6 200	5 750	42	2,52
				4,17 м³

						#ID Проекта	
						кадастровый номер Россия	
Изм.	Кол.уч.	Лист	№Док.	Подп.	Дата		
Разраб.						Индивидуальный жилой дом	Стадия: #Стадия Проекта; Лист: 43; Листов:
ГАП							
Ведомость материалов (стропильная система)							

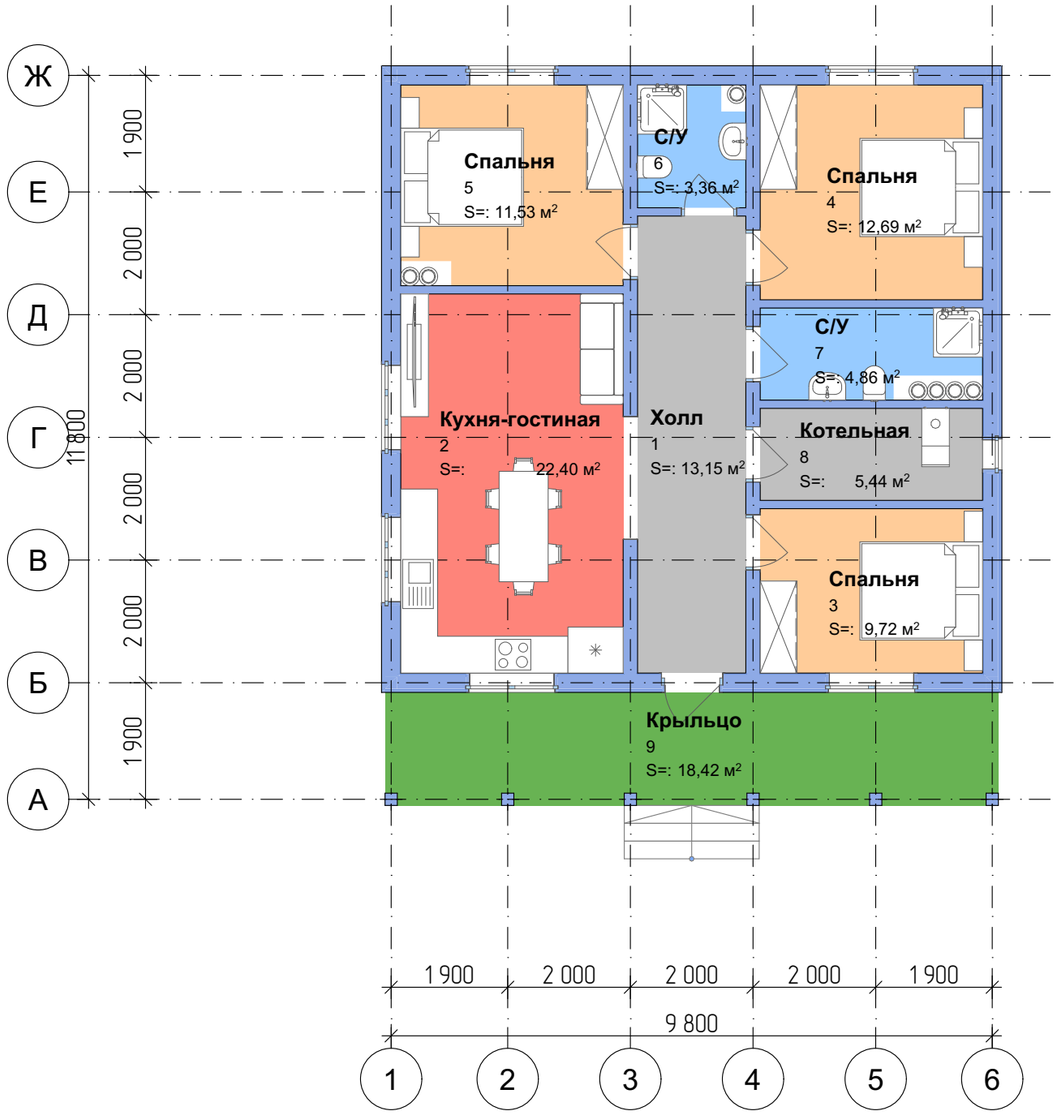


						#ID Проекта	
						кадастровый номер Россия	
Изм.	Кол.уч.	Лист	№Док.	Подп.	Дата		
Разраб.						Индивидуальный жилой дом	Стадия: #Стадия Проекта; Лист: 44; Листов:
ГАП							
План расстановки мебели 1 этаж							

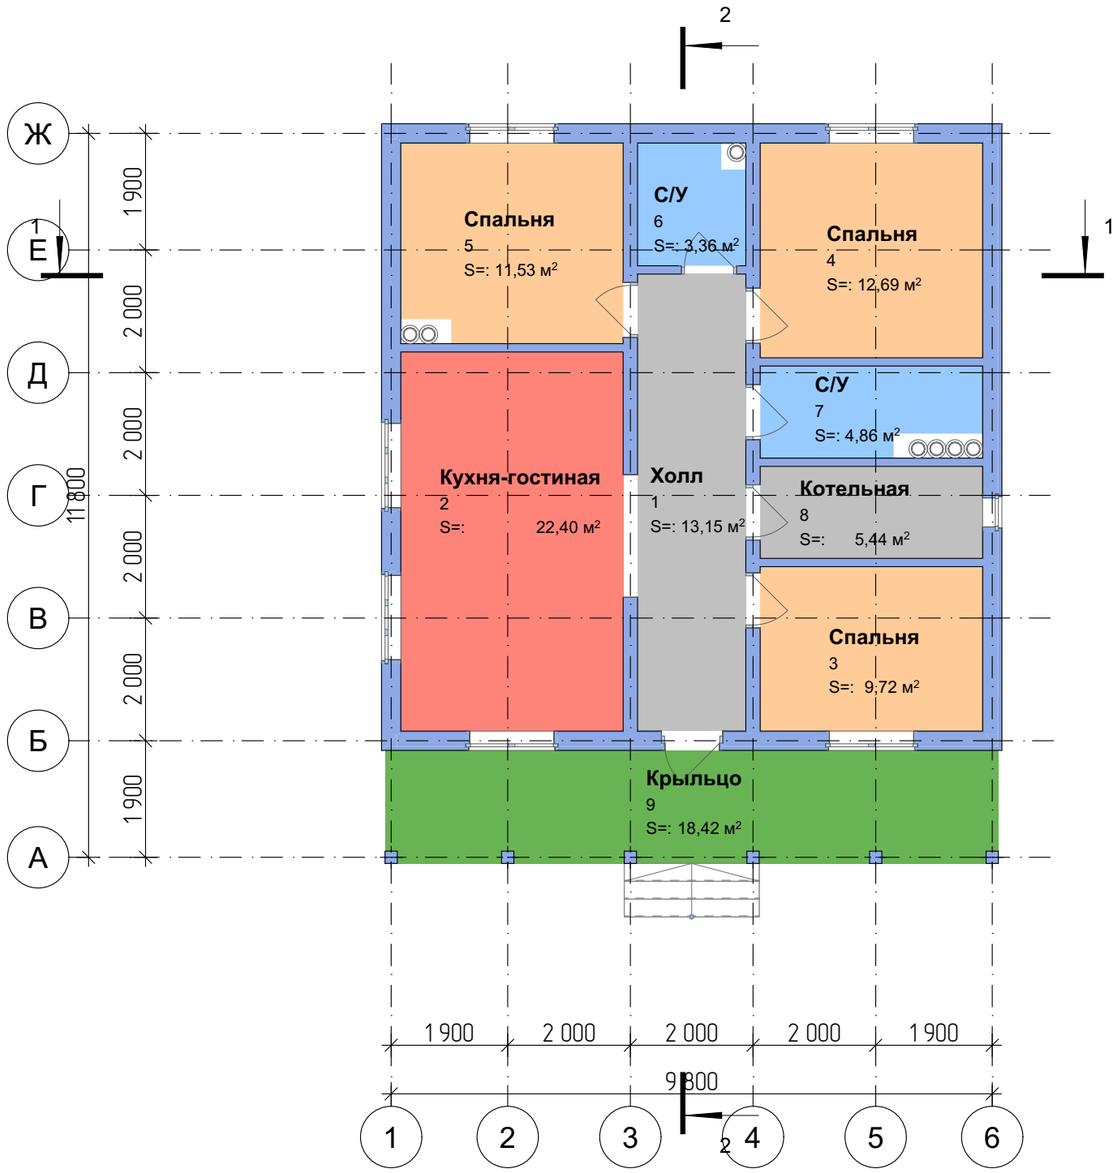


Категория	№	Наименование	Площадь, м2
ОБЩАЯ ПЛОЩАДЬ			
	1	Холл	13,15
	2	Кухня-гостиная	22,40
	3	Спальня	9,72
	4	Спальня	12,69
	5	Спальня	11,53
	6	С/У	3,36
	7	С/У	4,86
	8	Котельная	5,44
			83,15 м²
Транзитные Помещения			
	9	Крыльцо	18,42
			18,42 м²
			101,57 м²


						#ID Проекта	
						кадастровый номер Россия	
Изм.	Кол.уч.	Лист	№Док.	Подп.	Дата		
Разраб.						Индивидуальный жилой дом	Стадия: #Стадия Проекта; Лист: 45; Листов:
ГАП							
Экспликация помещений 1- го этажа							

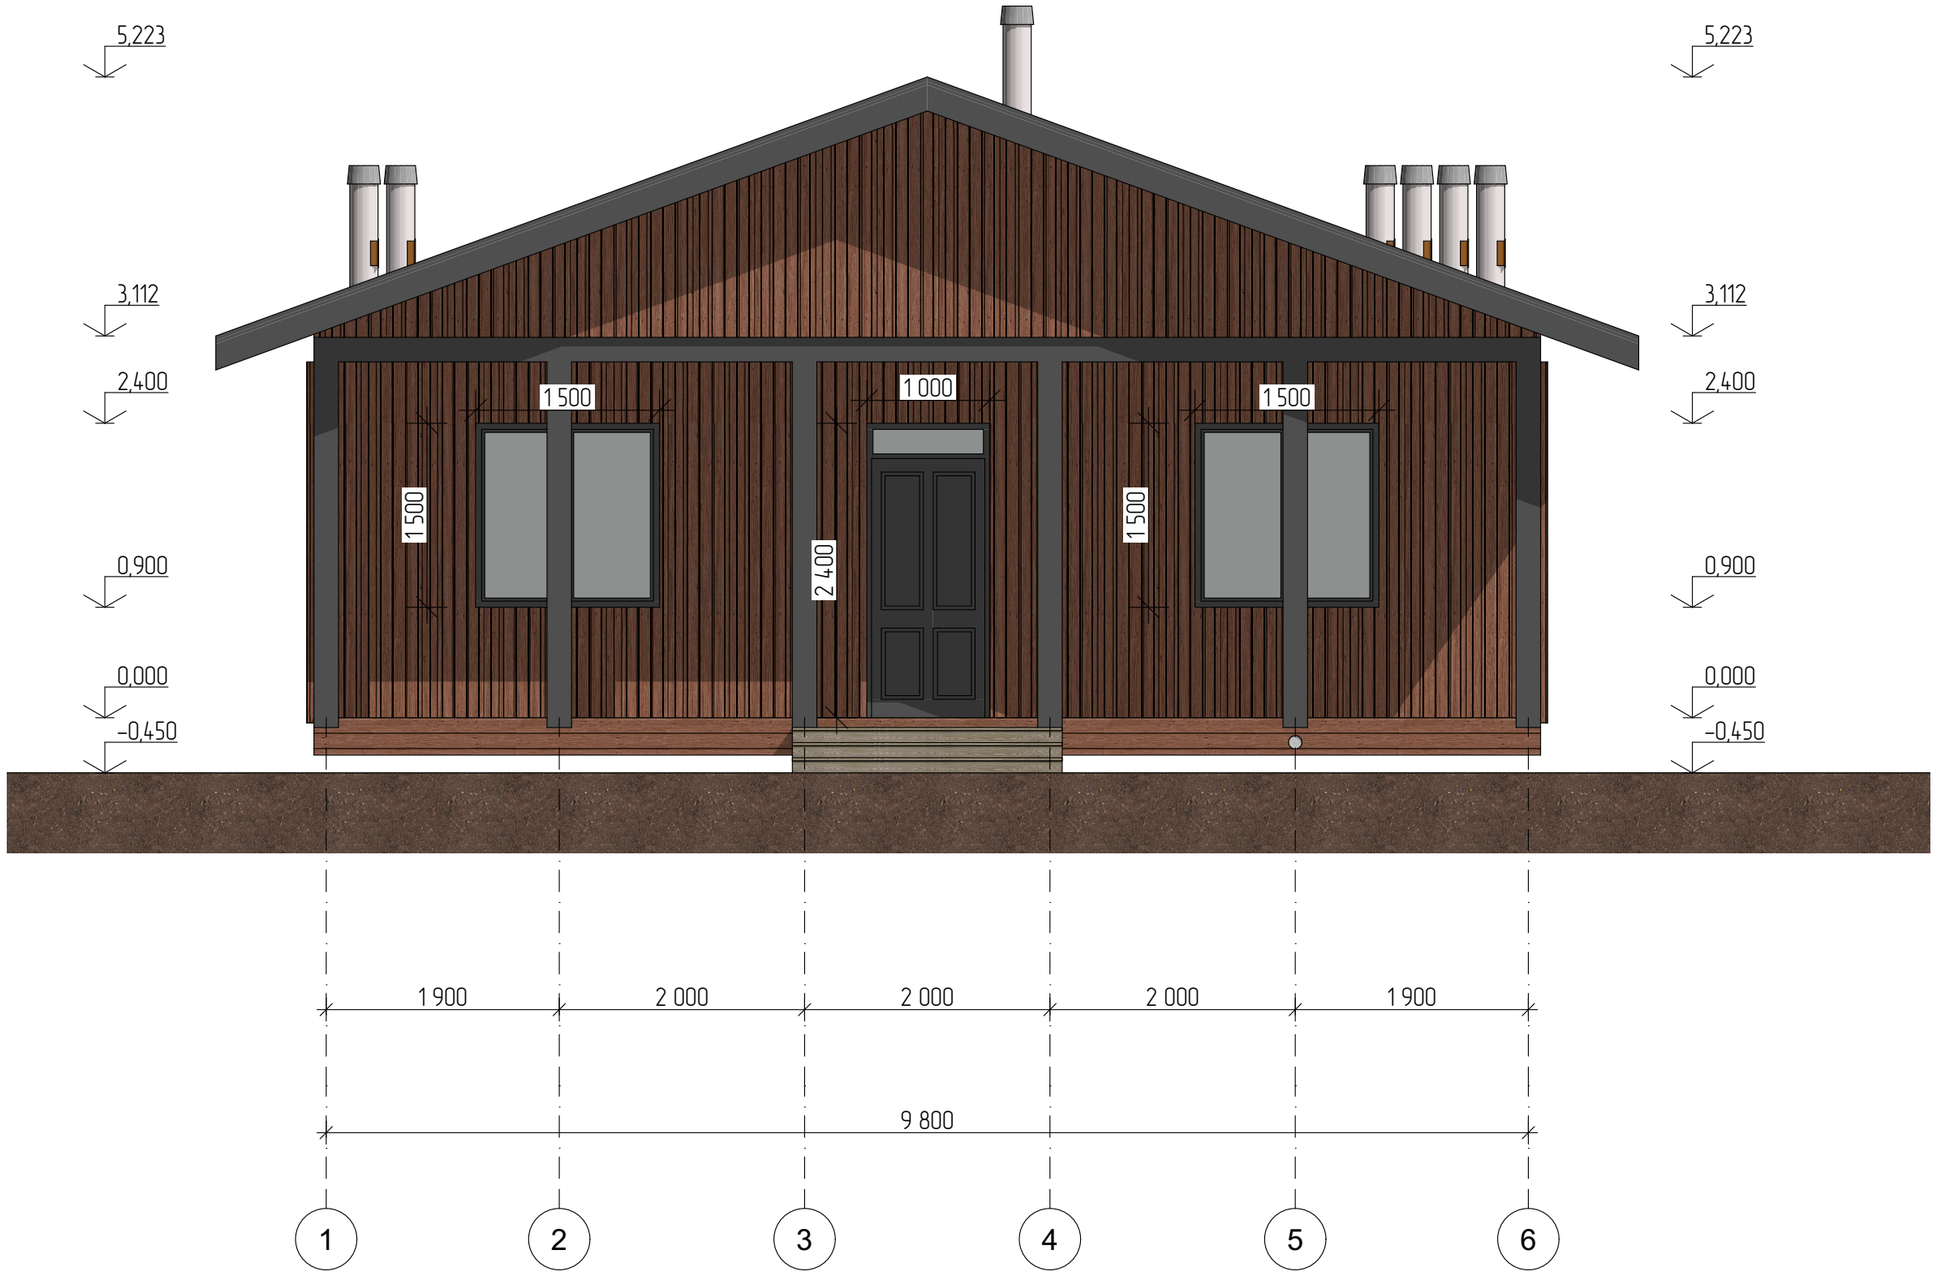


						#ID Проекта	
						кадастровый номер Россия	
Изм.	Кол.уч.	Лист	№Док.	Подп.	Дата		
Разраб.						Индивидуальный жилой дом	Стадия: #Стадия Проекта; Лист: 46; Листов:
ГАП							
Фасад в осях 1-6							

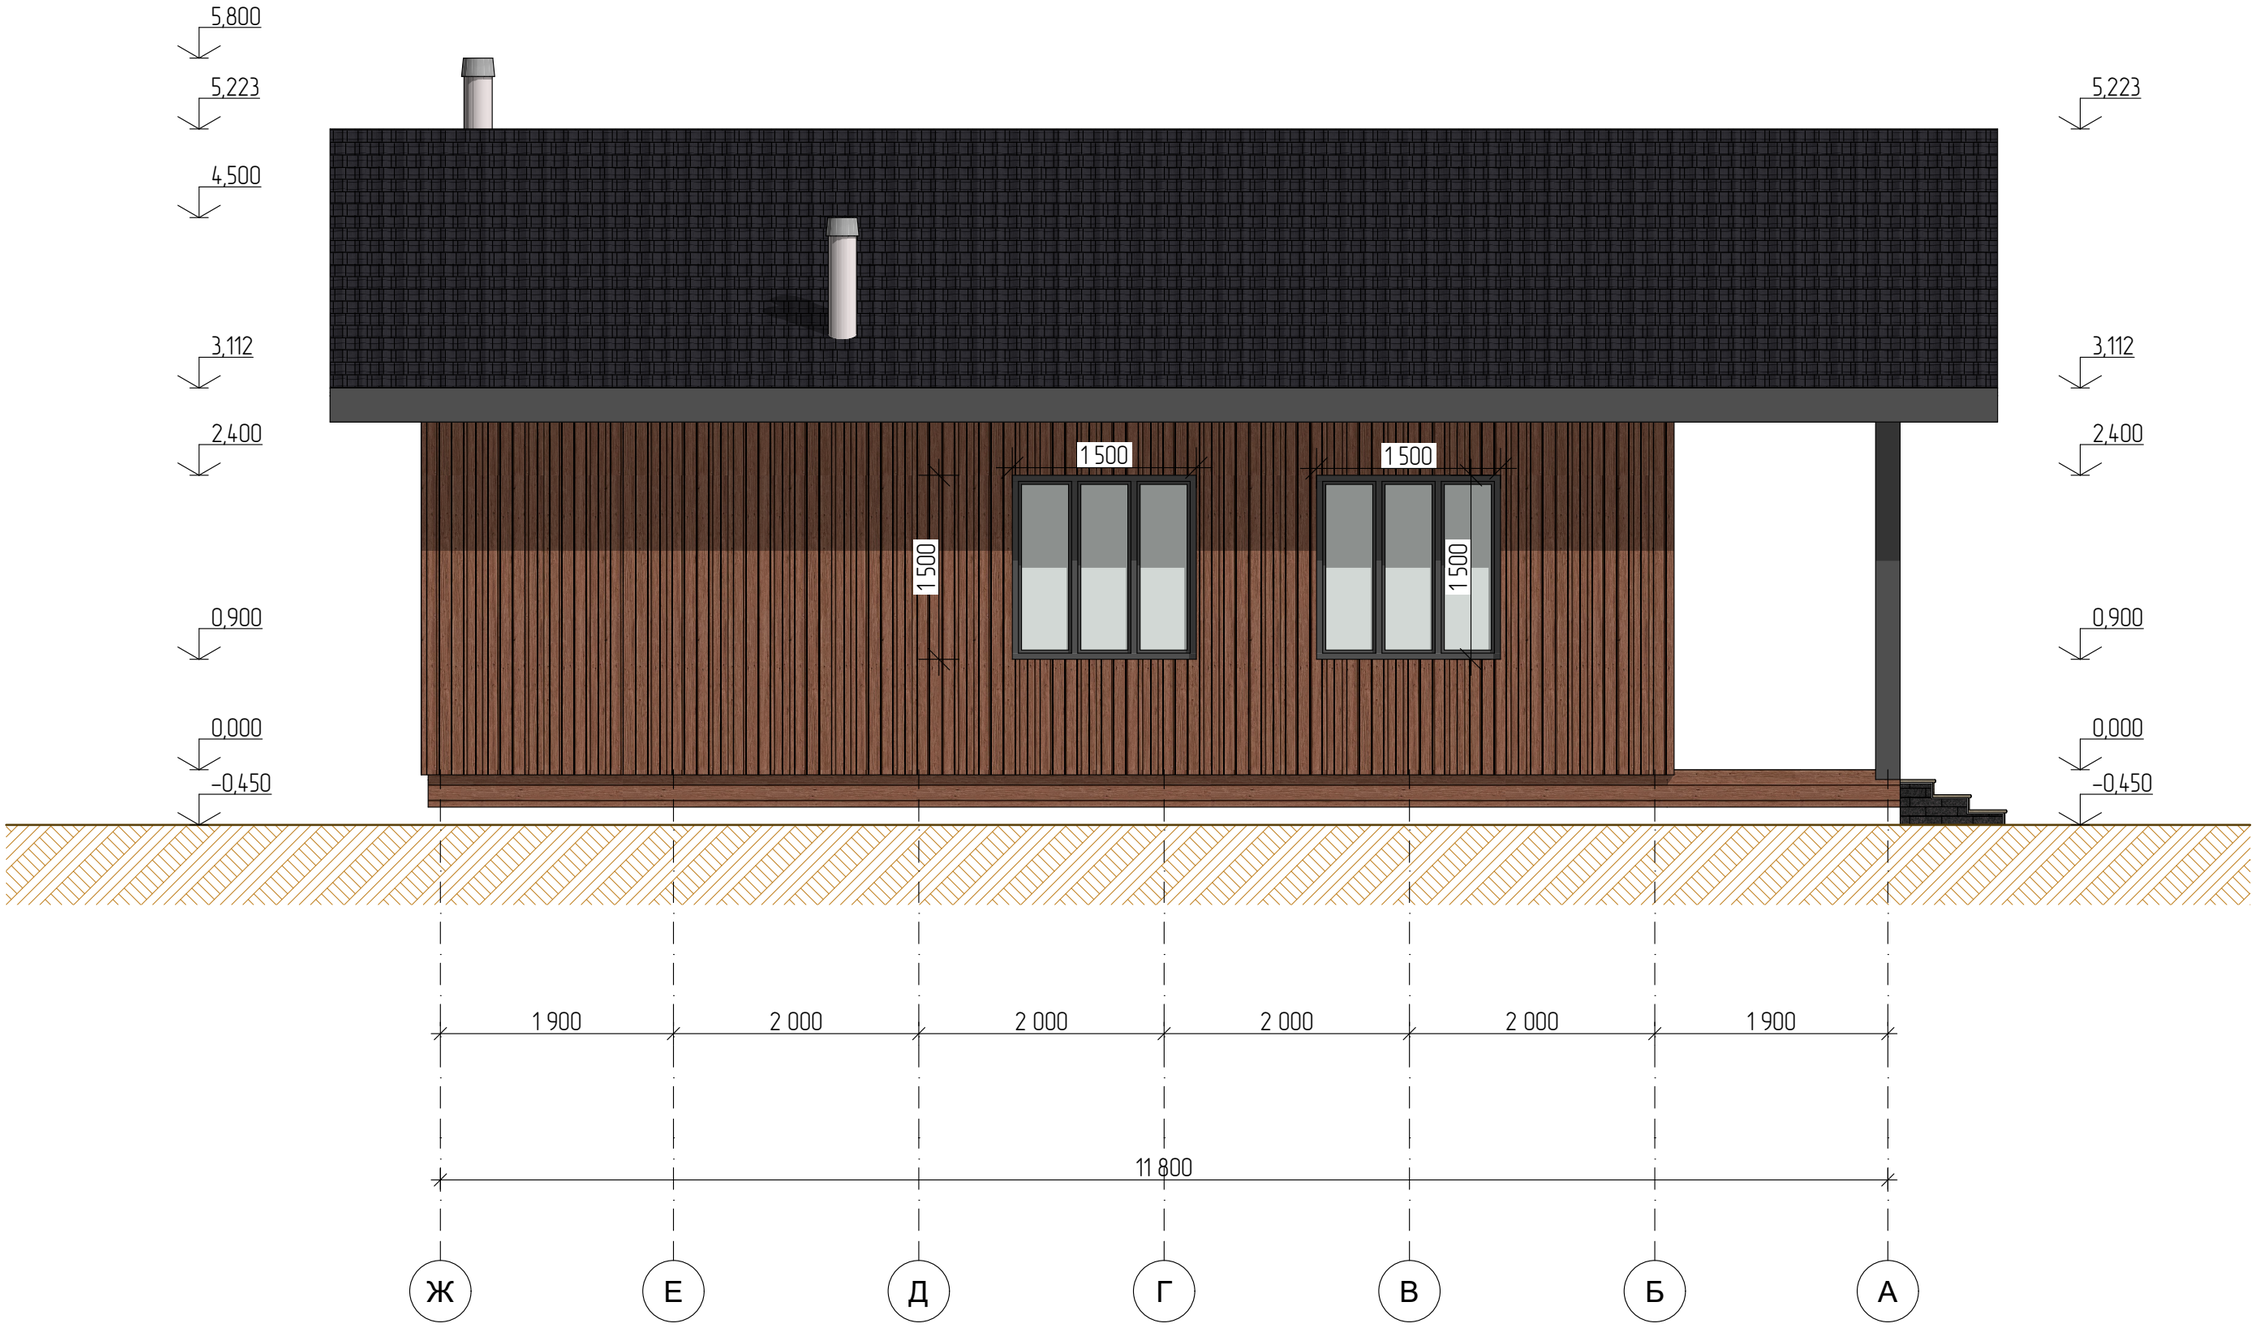

						#ID Проекта	
						кадастровый номер Россия	
Изм.	Кол.уч.	Лист	№Док.	Подп.	Дата		
Разраб.						Индивидуальный жилой дом	Стадия: #Стадия Проекта; Лист: 47; Листов:
ГАП							
Фасад в осях Ж-А							

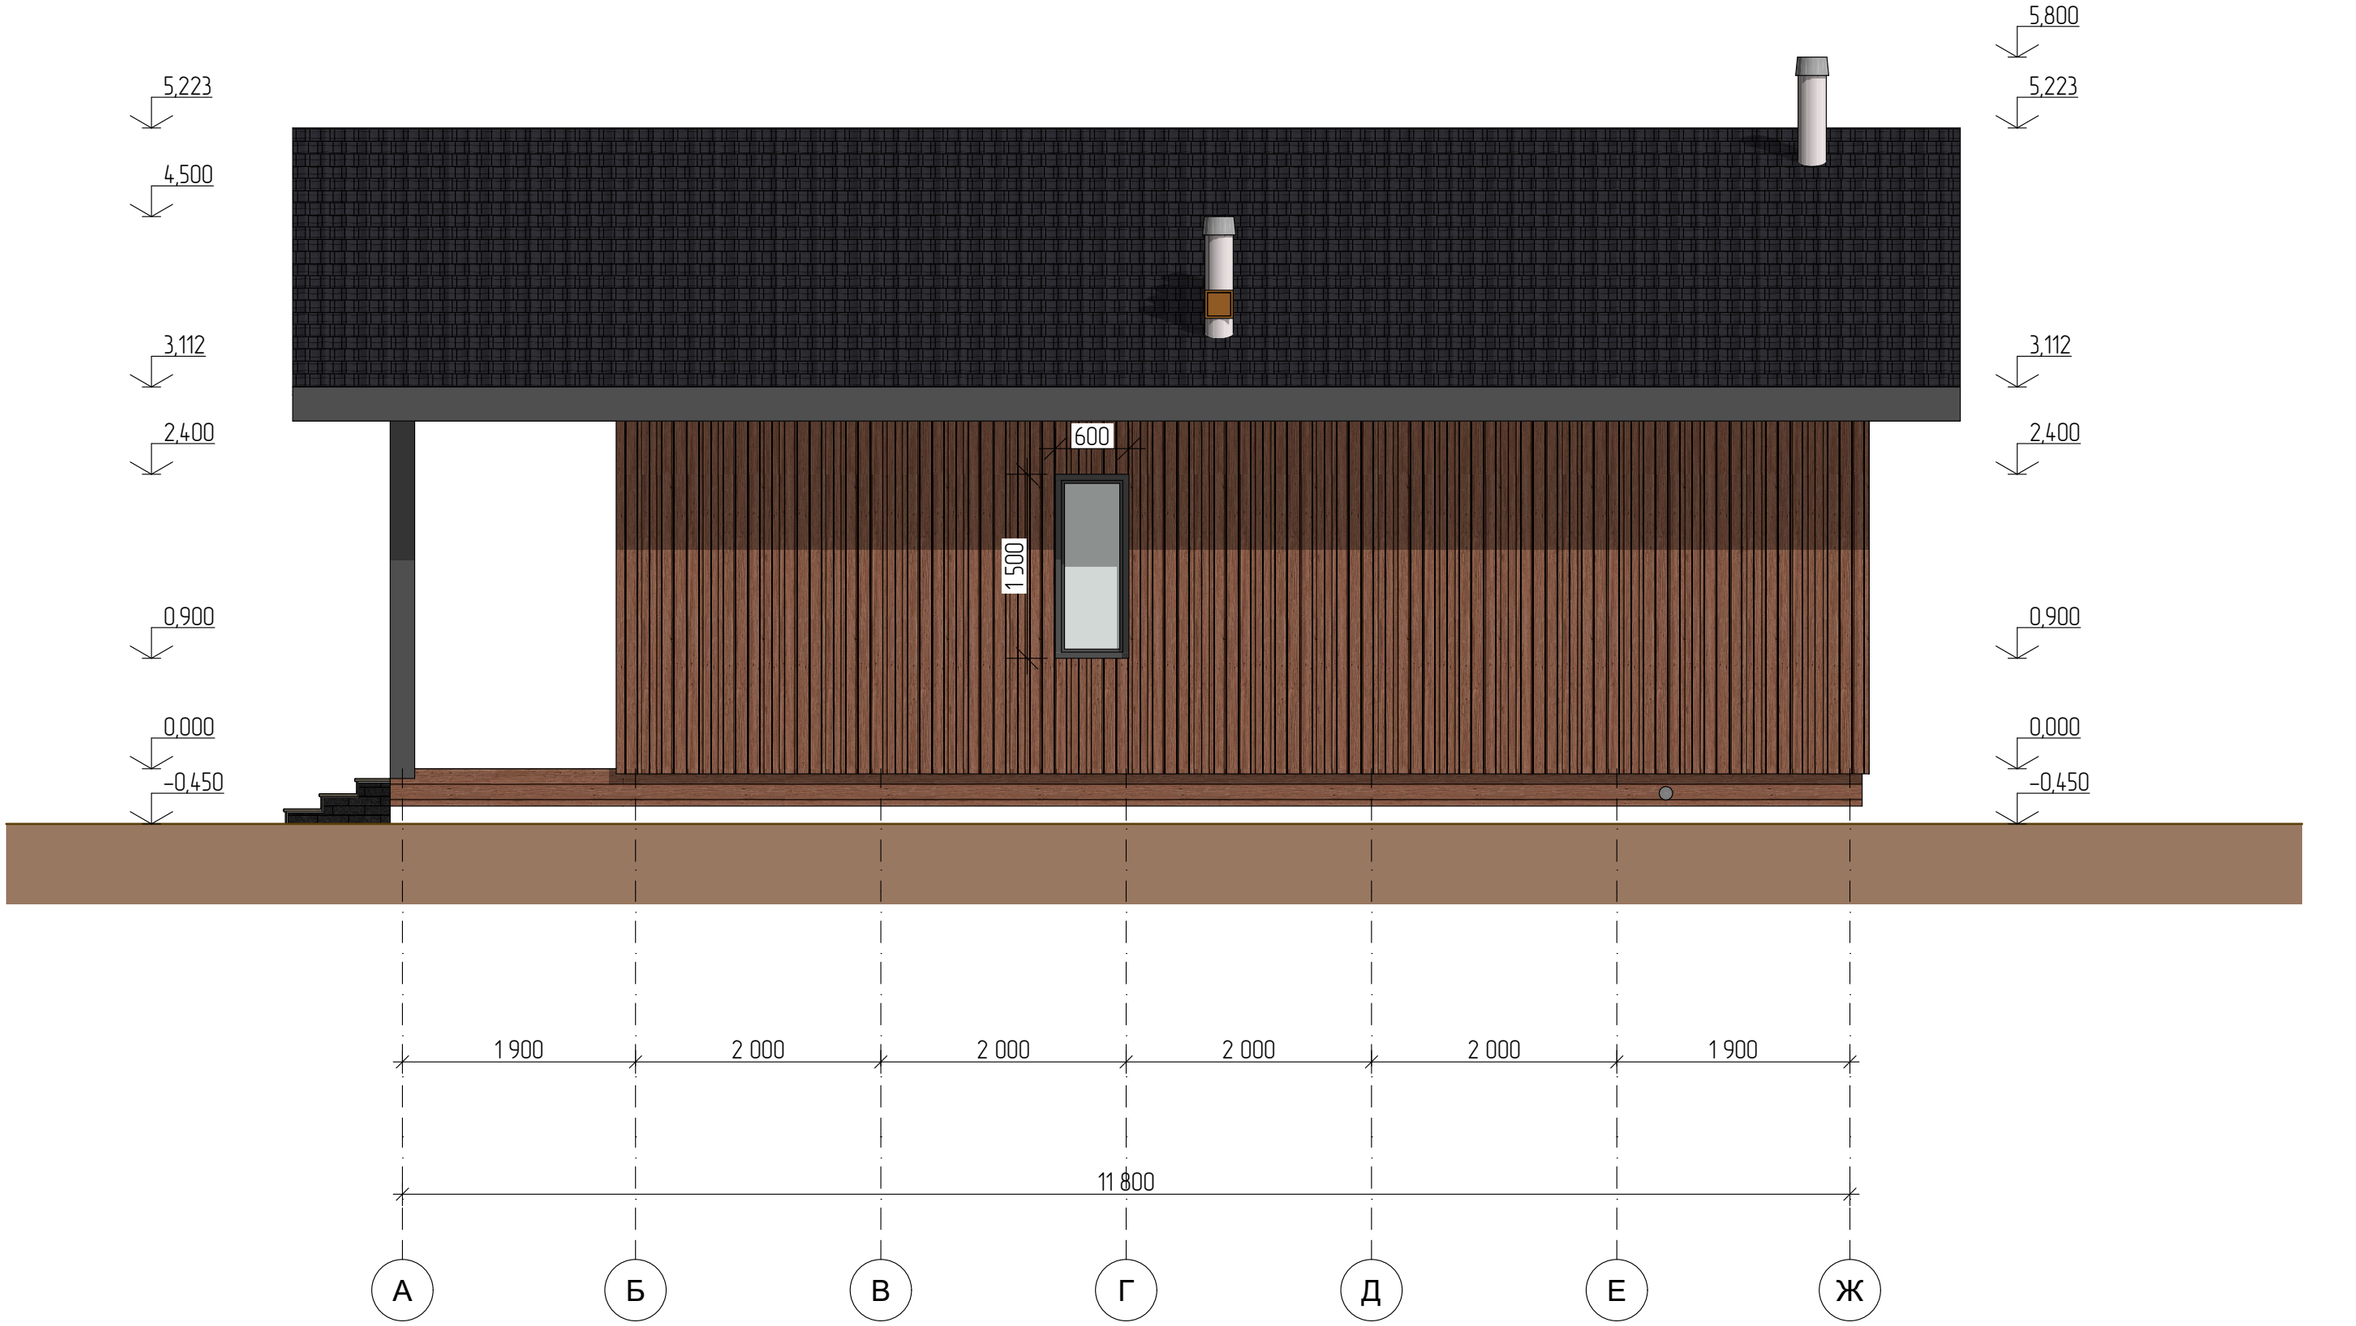


						#ID Проекта		
						кадастровый номер Россия		
Изм.	Кол.уч.	Лист	№Док.	Подп.	Дата			
Разраб.						Индивидуальный жилой дом	Стадия	Лист	Листов
ГАП							#Стадия Проекта	48	
Фасад в осях А-Ж									

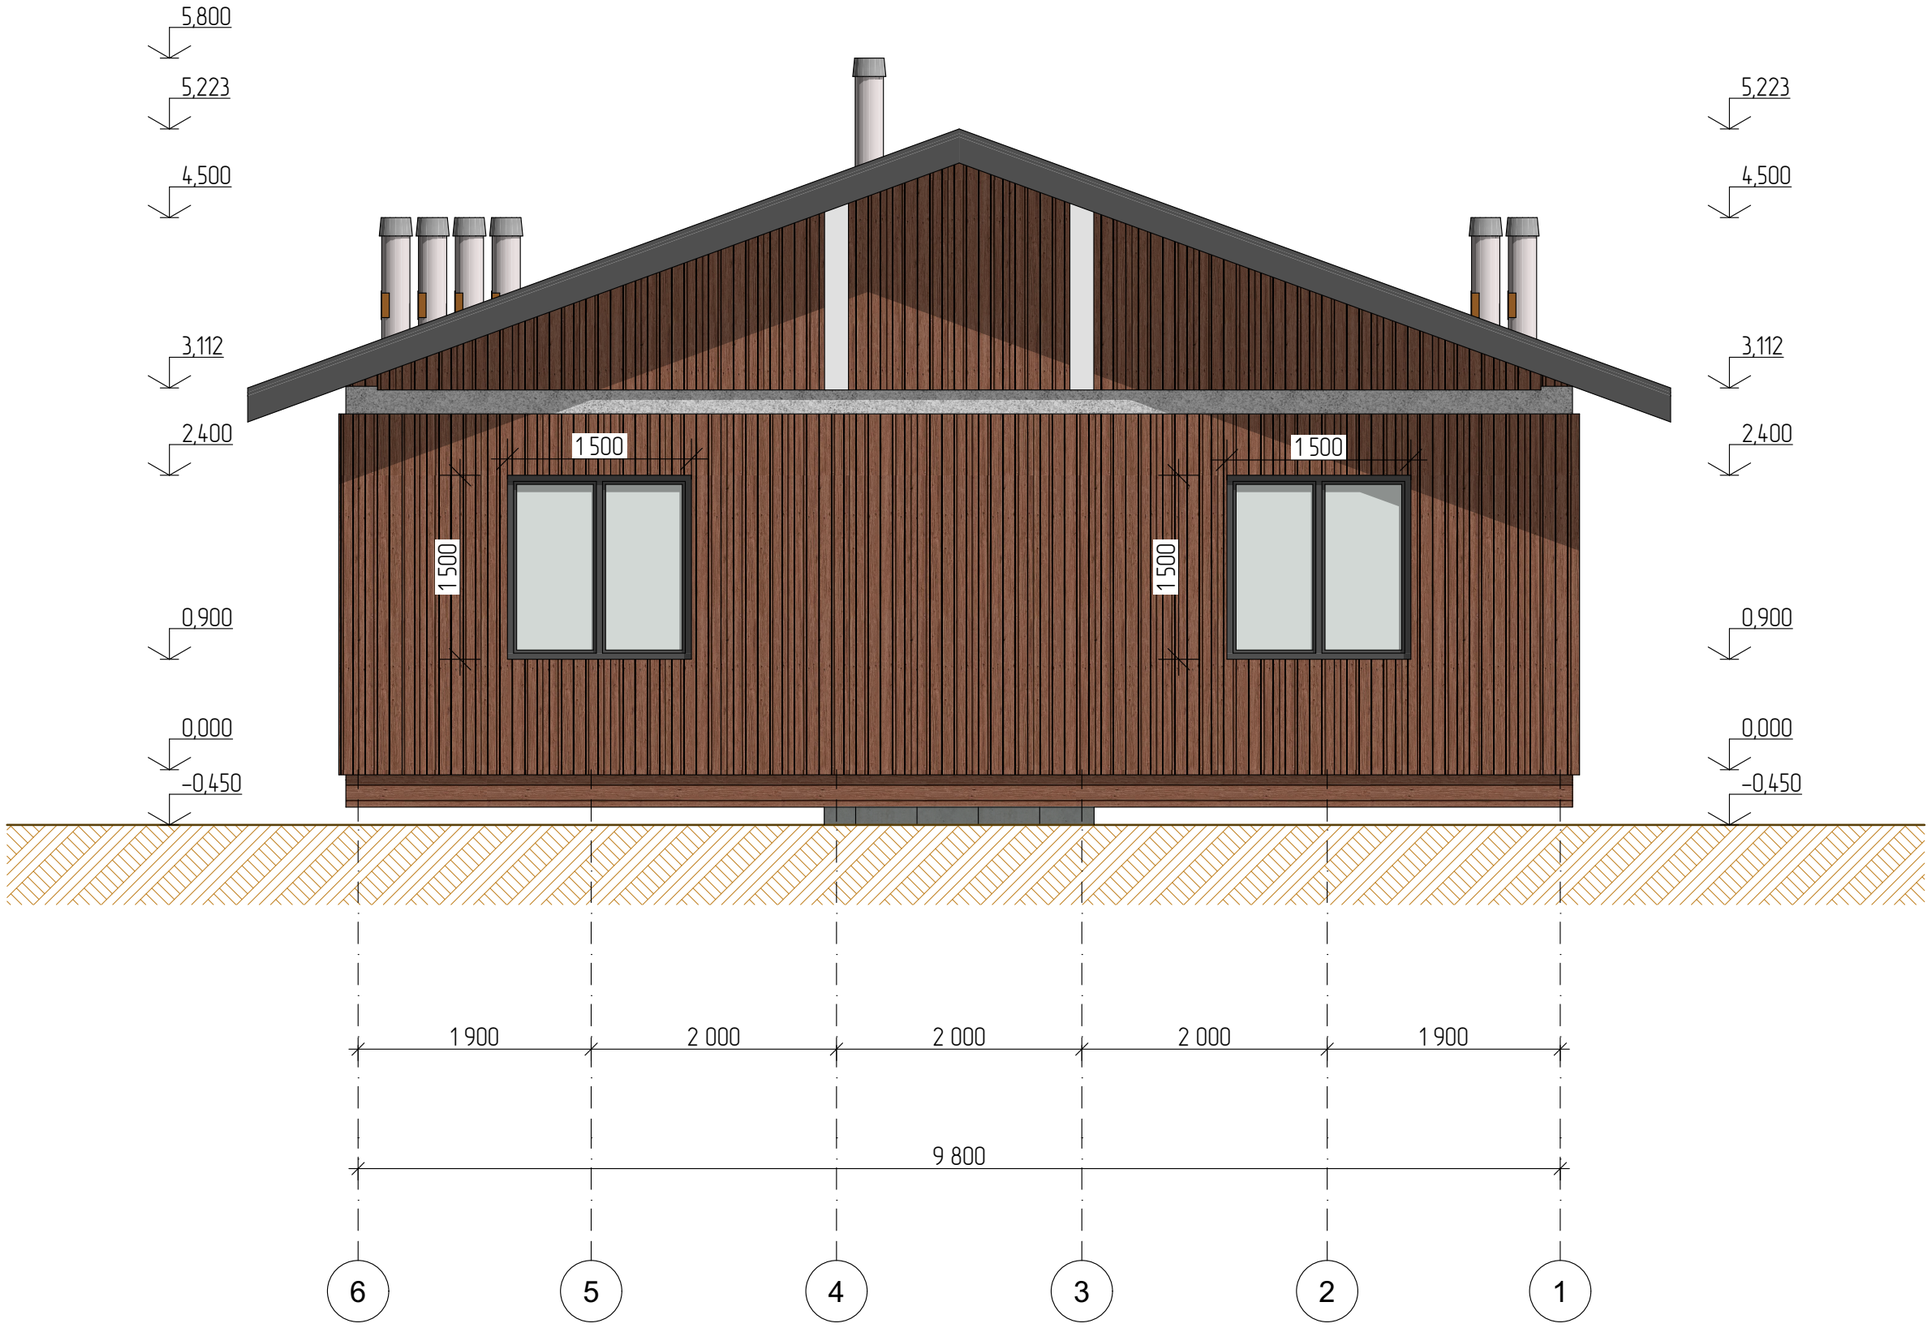


						#ID Проекта	
						кадастровый номер Россия	
Изм.	Кол.уч.	Лист	№Док.	Подп.	Дата		
Разраб.						Индивидуальный жилой дом	Стадия: #Стадия Проекта; Лист: 49; Листов:
ГАП							
Фасад в осях 6-1							


Ведомость материалов на фасад			
Наиме...	Компоненты		Объем, м3
	Толщина, мм	Площадь, м2	
Изоляция - Минеральная Жесткая			
	95	46,98	4,48
	195	169,21	32,99

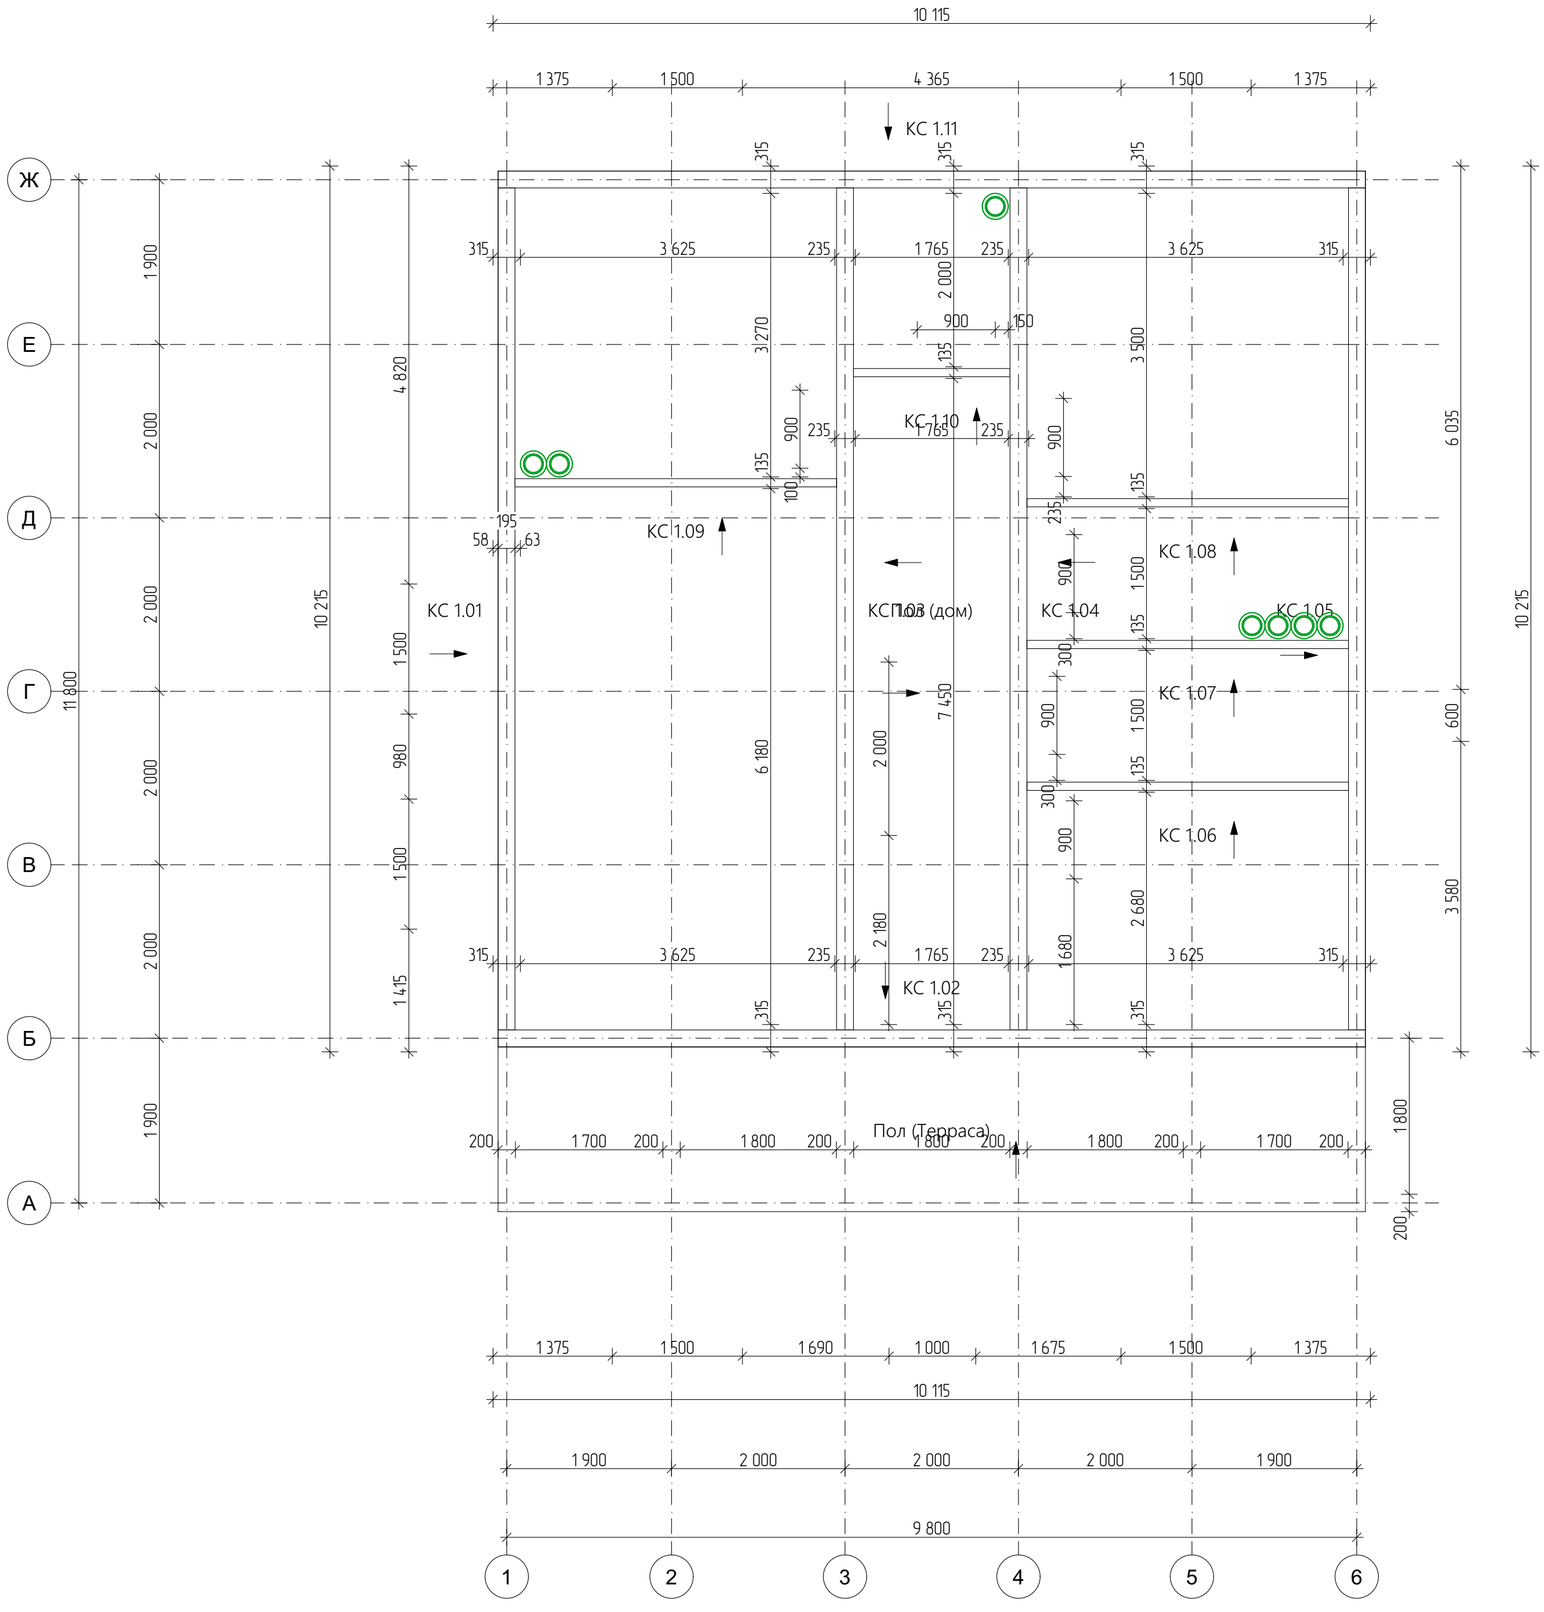


						#ID Проекта	
						кадастровый номер Россия	
Изм.	Колуч.	Лист	№Док.	Подп.	Дата		
Разраб.						Индивидуальный жилой дом	Стадия: #Стадия Проекта; Лист: 51; Листов:
ГАП							
Схема расположения стен 1-го этажа							

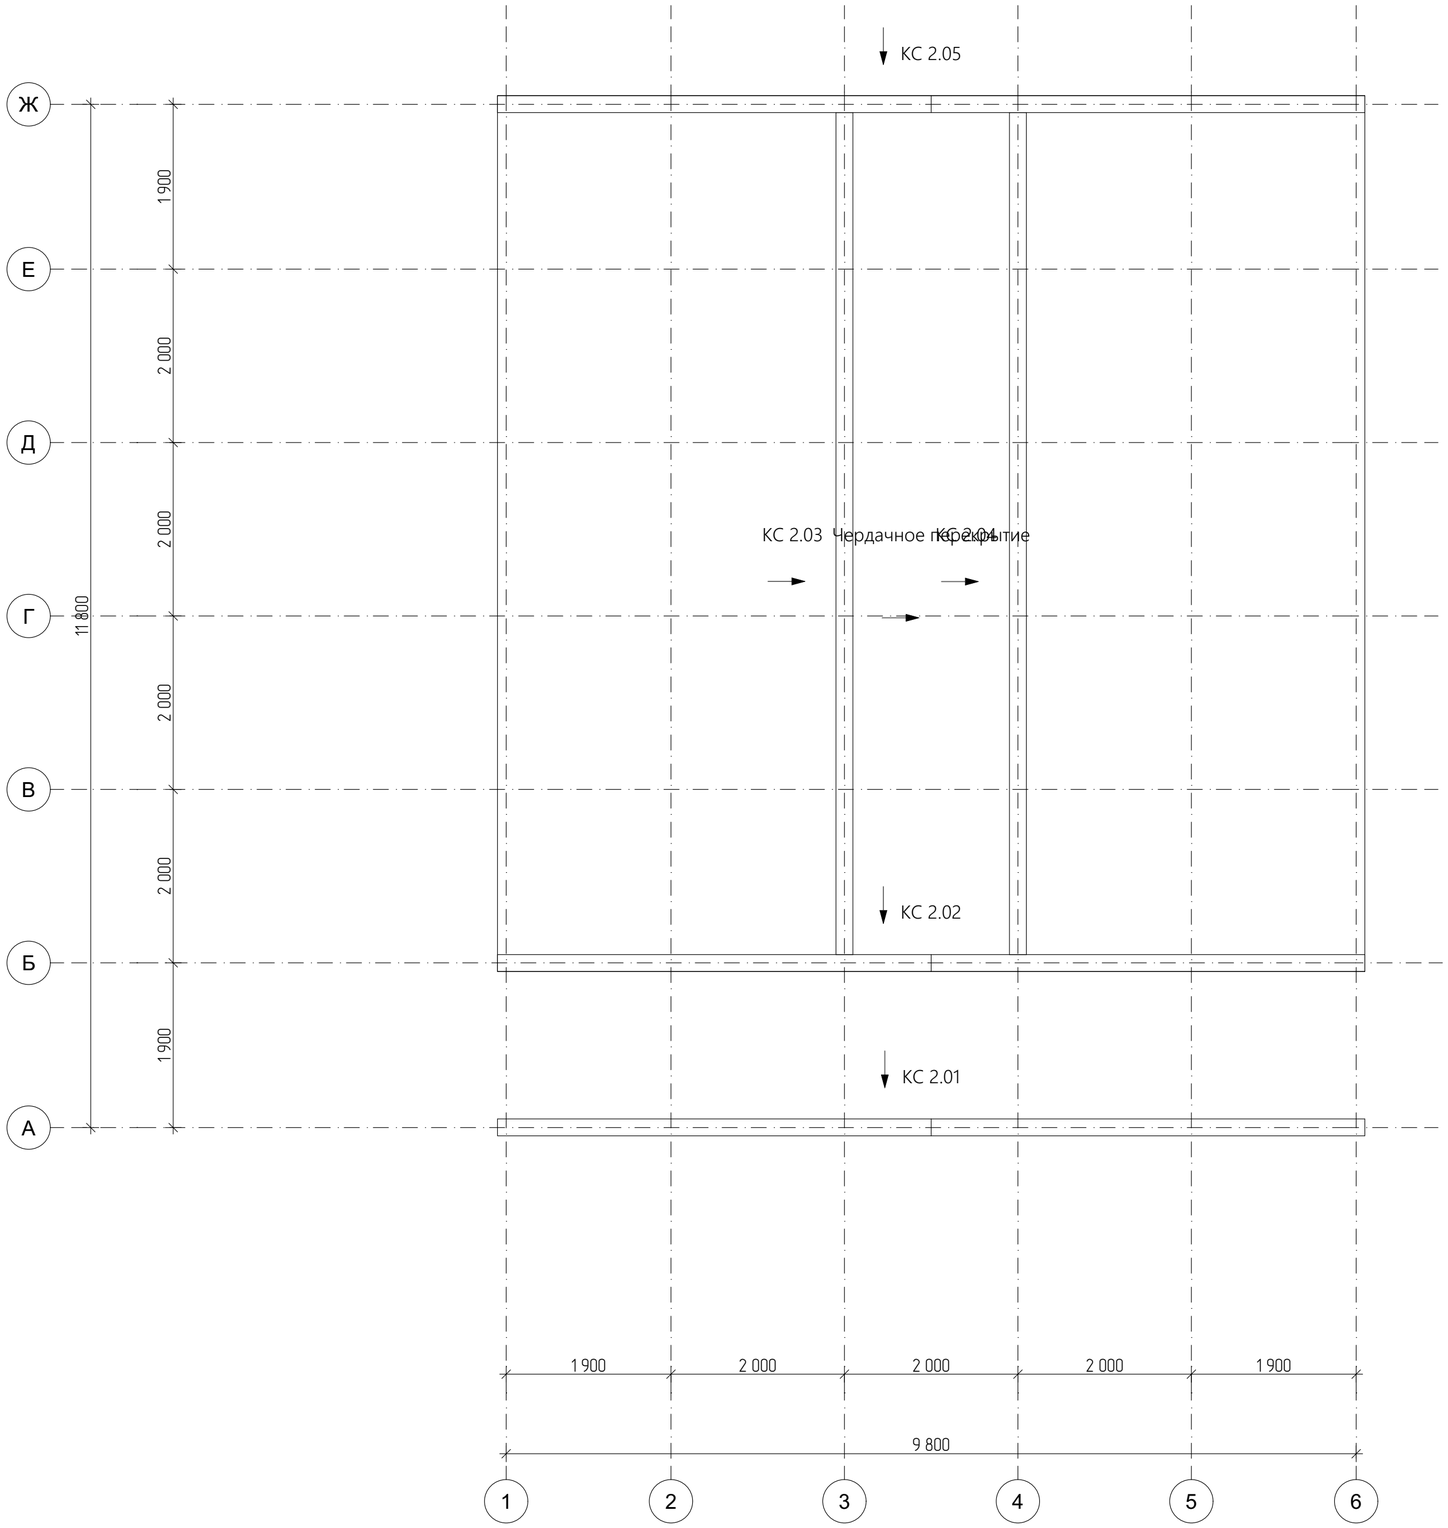

						#ID Проекта	
						кадастровый номер Россия	
Изм.	Колуч.	Лист	№Док.	Подп.	Дата		
Разраб.						Индивидуальный жилой дом	Стадия: #Стадия Проекта; Лист: 52; Листов:
ГАП							
Схема расположения каркасов чердака							

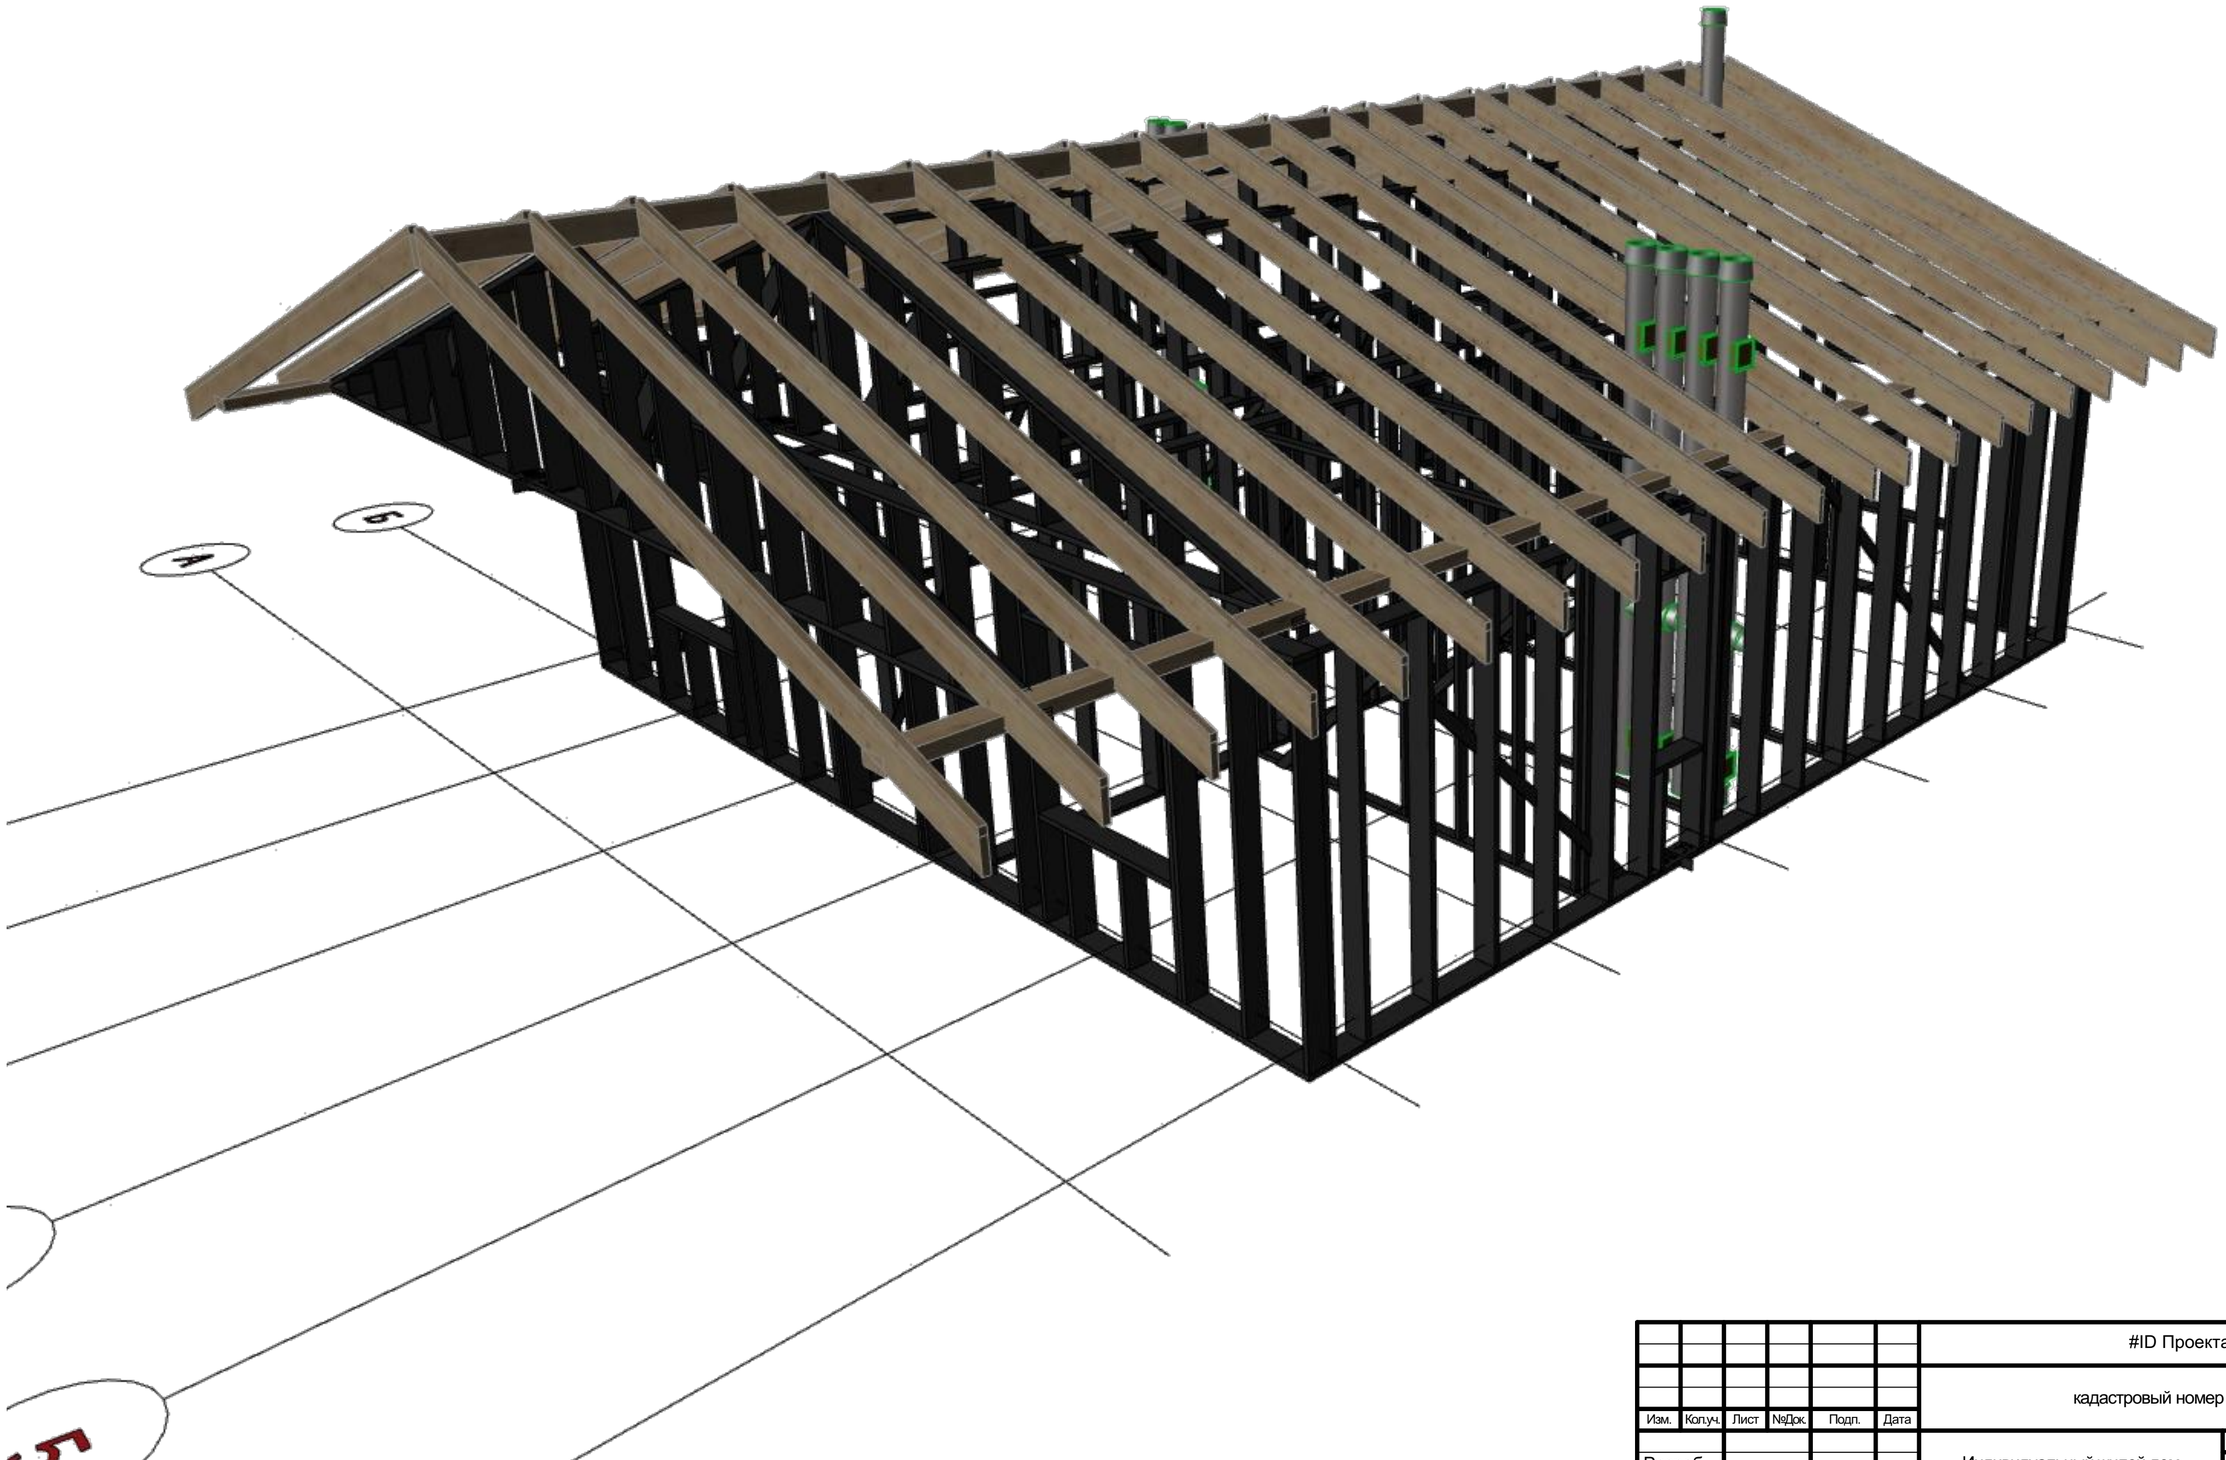


						#ID Проекта	
						кадастровый номер Россия	
Изм.	Кол.уч.	Лист	№Док.	Подп.	Дата		
Разраб.						Индивидуальный жилой дом	Стадия: #Стадия Проекта; Лист: 53; Листов:
ГАП							
3Д Вид каркаса							

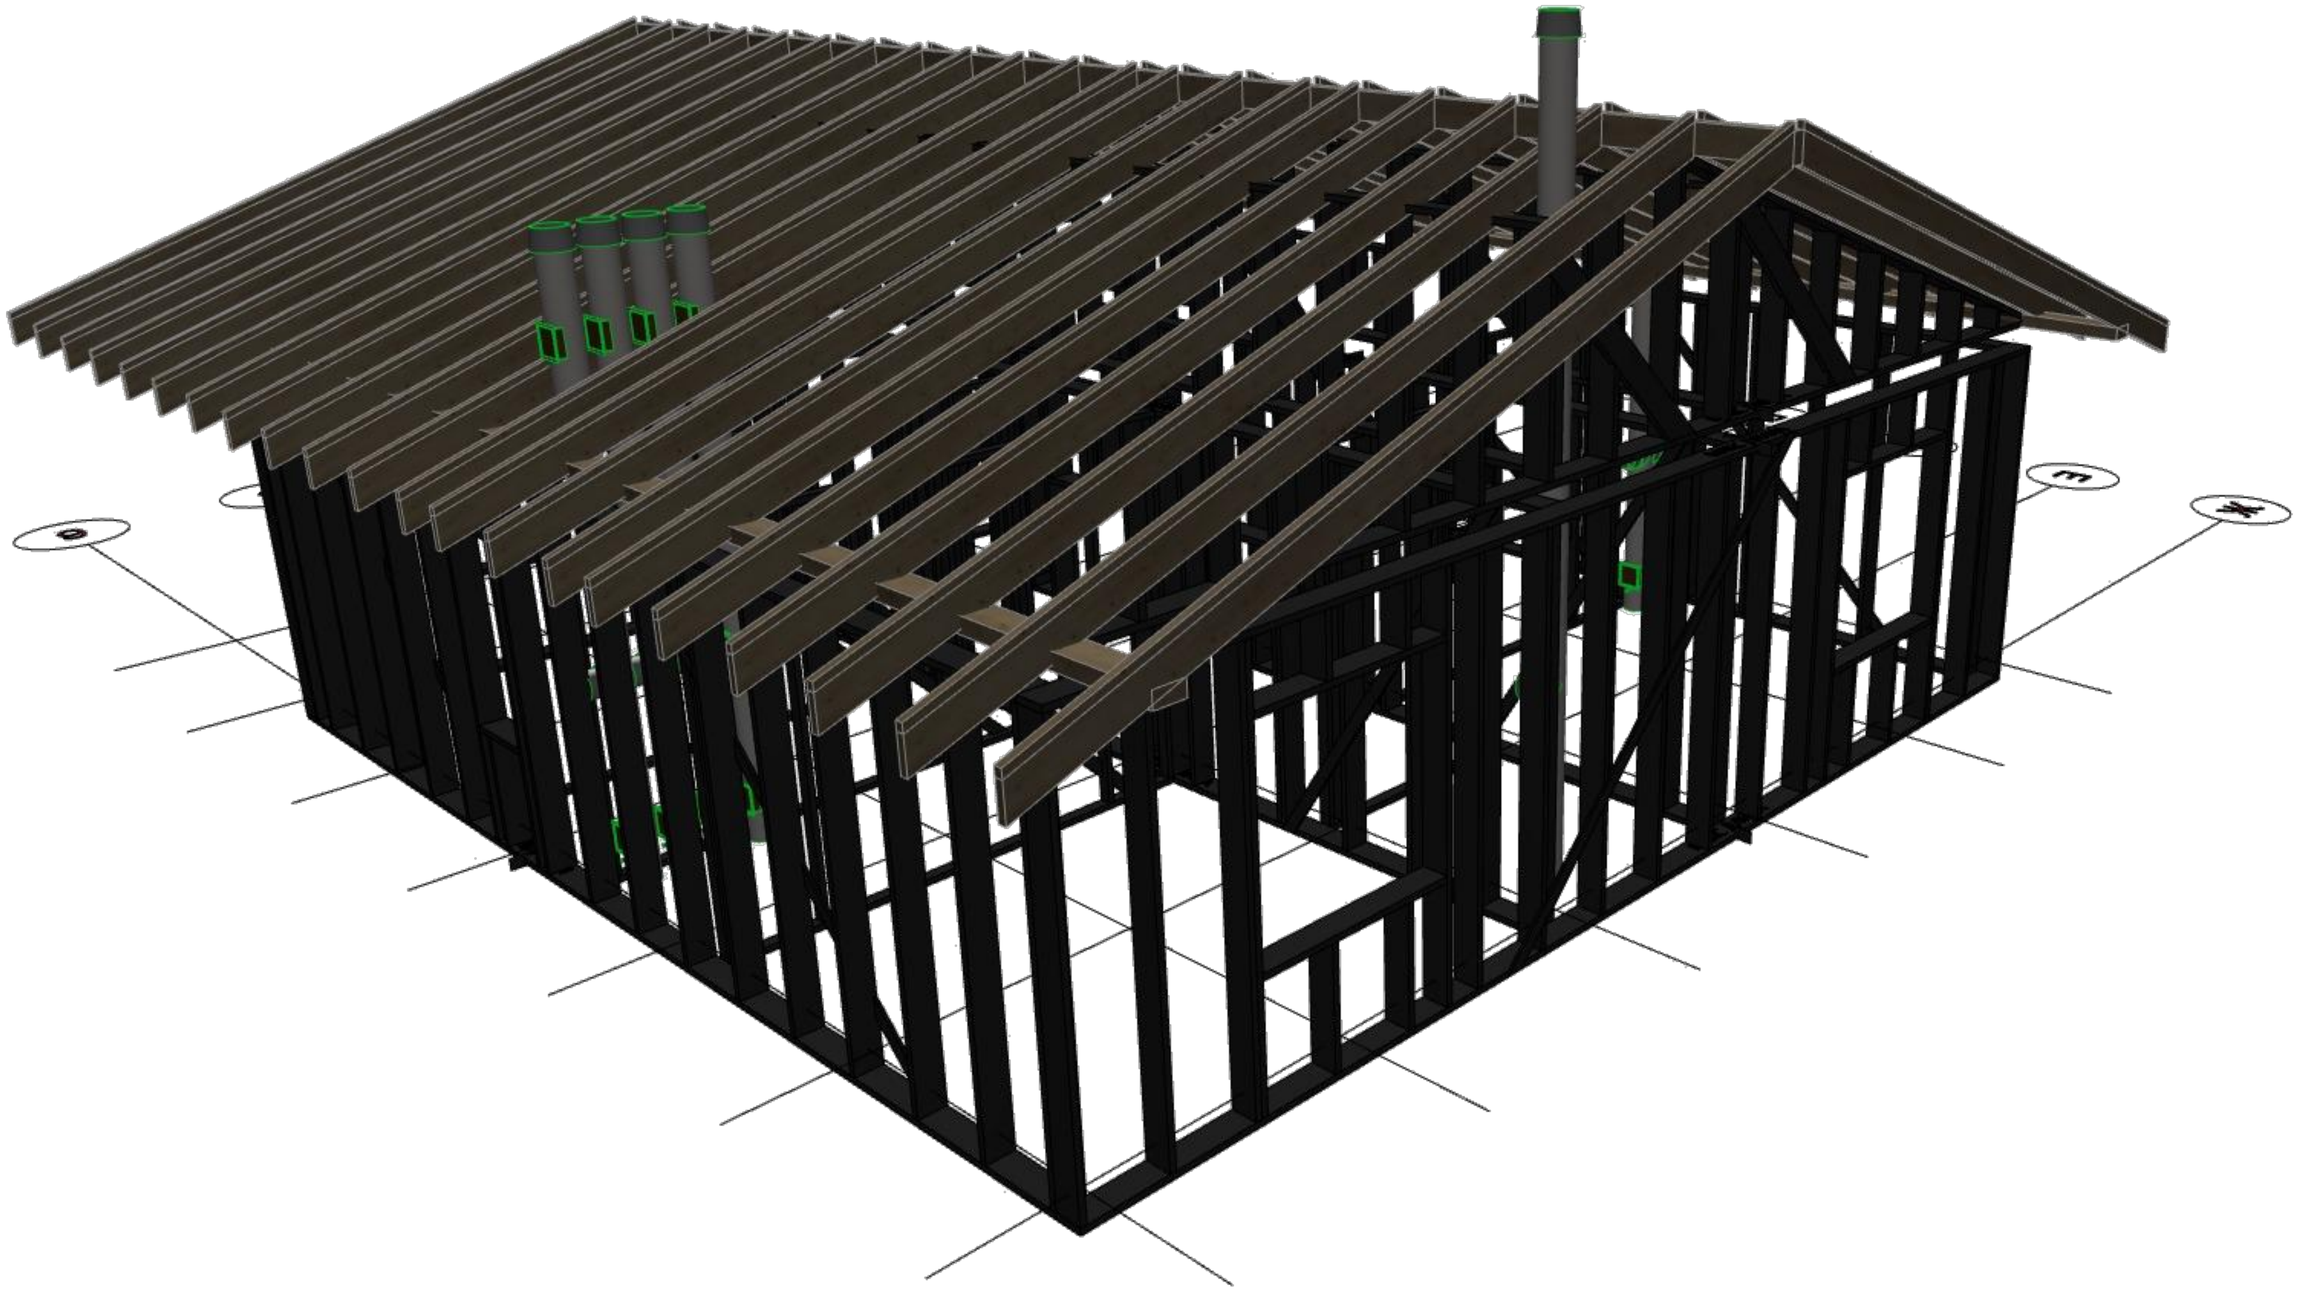

						#ID Проекта	
						кадастровый номер Россия	
Изм.	Кол.уч.	Лист	№Док.	Подп.	Дата		
Разраб.						Индивидуальный жилой дом	Стадия: #Стадия Проекта; Лист: 54; Листов:
ГАП							
3Д вид Каркаса							

Вид каркаса снаружи КС 1.01

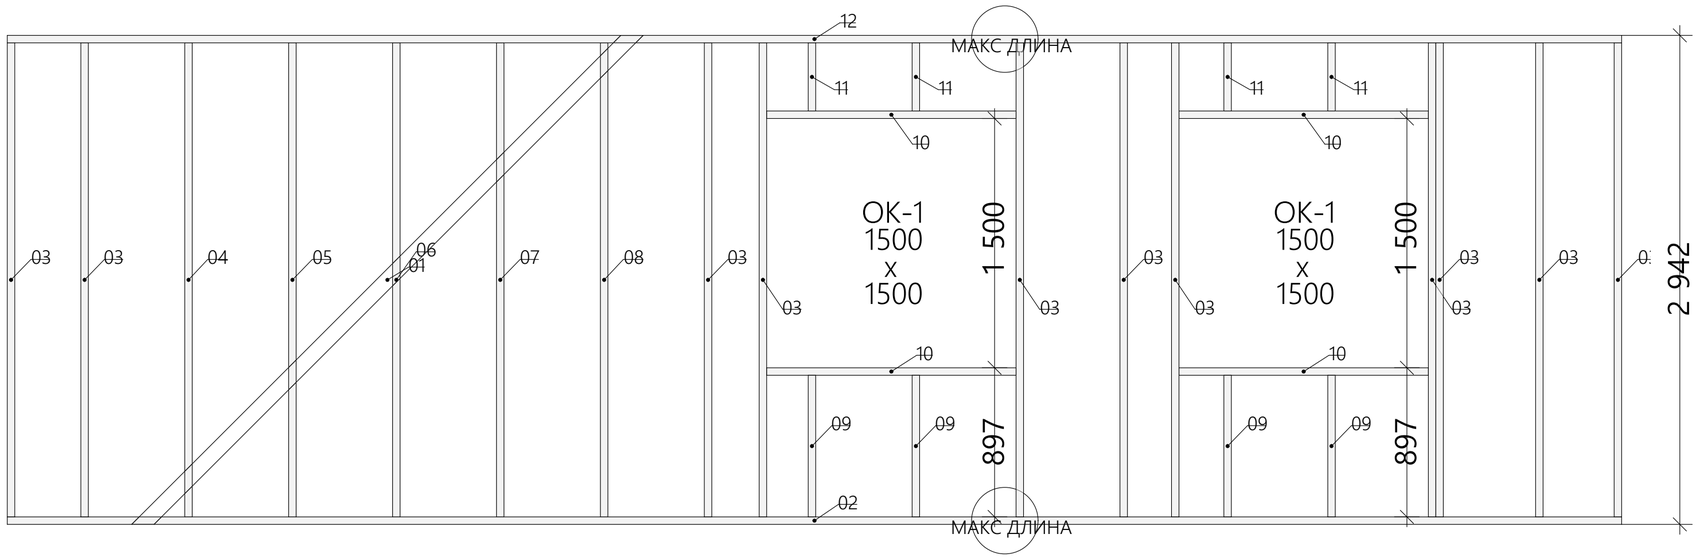

Основной каркас стены №КС 1.01


Номер	Название	Сечение, мм	Длина, мм	Кол-во, шт	Объем, м3
КС 1.01-01	Укосина	20x95	4256	1	0.008
КС 1.01-02	Обвязка	45x195	9710	1	0.085
КС 1.01-03	Стойка	45x195	2852	11	0.275
КС 1.01-04	Стойка	45x195	2852	1	0.025
КС 1.01-05	Стойка	45x195	2852	1	0.025
КС 1.01-06	Стойка	45x195	2852	1	0.025
КС 1.01-07	Стойка	45x195	2852	1	0.025
КС 1.01-08	Стойка	45x195	2852	1	0.025
КС 1.01-09	Стойка	45x195	852	4	0.030
КС 1.01-10	Доски под окна/двери	45x195	1500	4	0.053
КС 1.01-11	Стойка	45x195	410	4	0.014
КС 1.01-12	Обвязка	45x195	9710	1	0.085
			Общая сумма:	31	0.676

Вид каркаса сверху КС 1.01



						#ID Проекта	
						кадастровый номер Россия	
Изм.	Кол.уч.	Лист	№Док.	Подп.	Дата		
Разраб.						Индивидуальный жилой дом	Стадия: #Стадия Проекта; Лист: 55; Листов:
ГАП							
Чертеж каркаса стен № КС 1.01 #1							

Вид каркаса снаружи КС 1.02

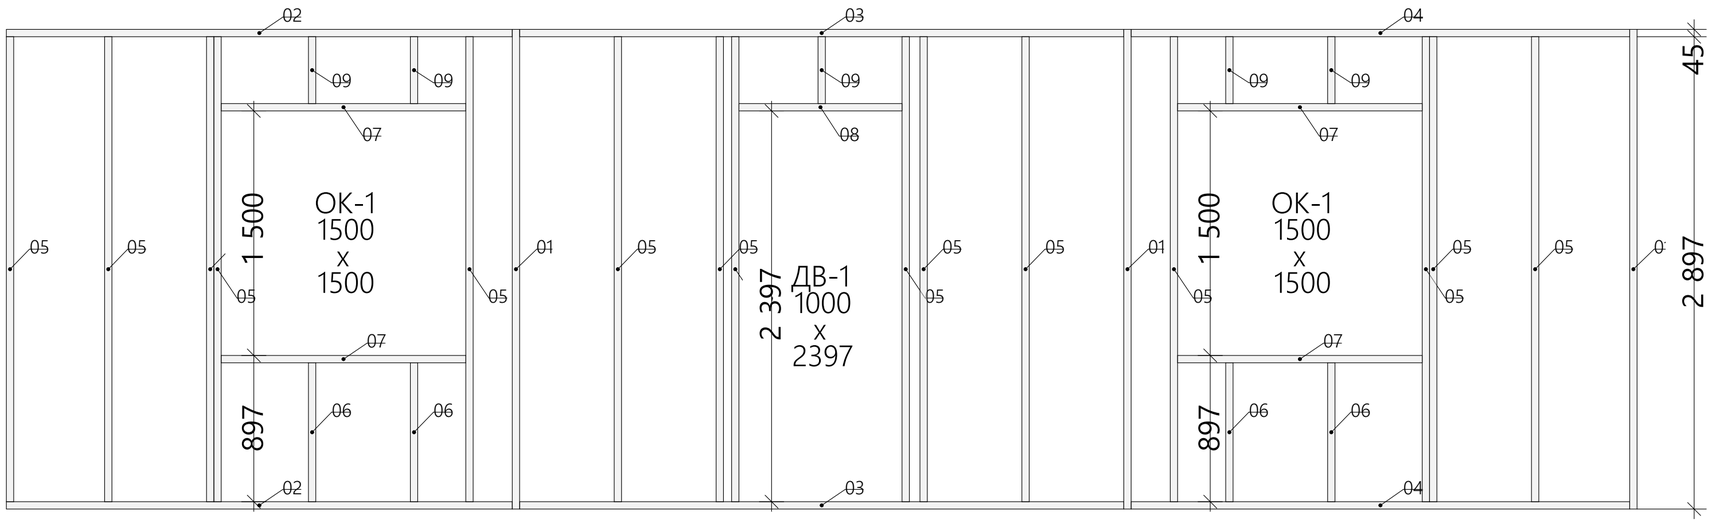

Основной каркас стены №КС 1.02


Номер	Название	Сечение, мм	Длина, мм	Кол-во, шт	Объем, м3
КС 1.02-01	Стойка	45x195	2942	3	0.077
КС 1.02-02	Обвязка	45x195	3102	2	0.054
КС 1.02-03	Обвязка	45x195	3705	2	0.065
КС 1.02-04	Обвязка	45x195	3057	2	0.054
КС 1.02-05	Стойка	45x195	2852	15	0.375
КС 1.02-06	Стойка	45x195	852	4	0.030
КС 1.02-07	Доски под окна/двери	45x195	1500	4	0.053
КС 1.02-08	Доски под окна/двери	45x195	1000	1	0.009
КС 1.02-09	Стойка	45x195	410	5	0.018
			Общая сумма:	38	0.735

Вид каркаса сверху КС 1.02



Изм.	Колуч.	Лист	№Док.	Подп.	Дата	#ID Проекта			
						кадастровый номер Россия			
Разраб.						Индивидуальный жилой дом	Стадия	Лист	Листов
ГАП							#Стадия Проекта	56	
Чертеж каркаса стен № КС 1.02 #1									

Вид каркаса снаружи КС 1.03

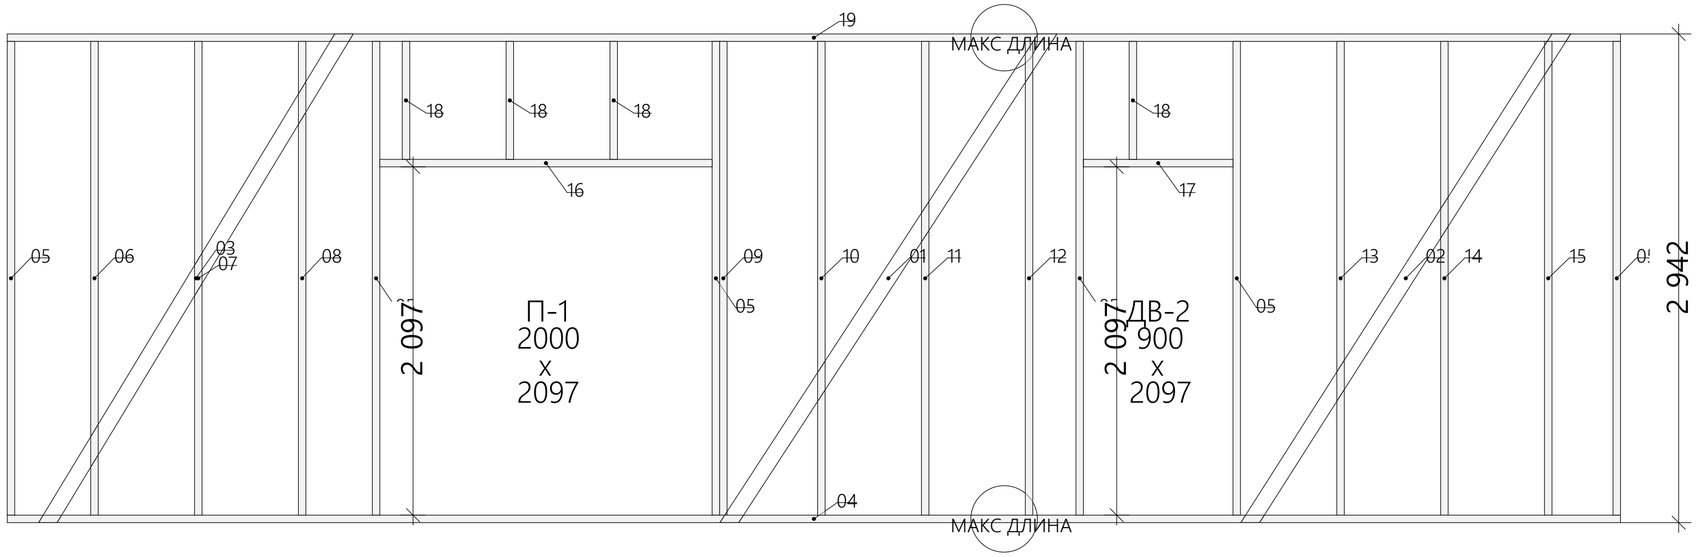


Вид каркаса сверху КС 1.03

Основной каркас стены №КС 1.03

Номер	Название	Сечение, мм	Длина, мм	Кол-во, шт	Объем, м3
КС 1.03-01	Укосина	20x95	3572	1	0.007
КС 1.03-02	Укосина	20x95	3548	1	0.007
КС 1.03-03	Укосина	20x95	3497	1	0.007
КС 1.03-04	Обвязка	45x195	9710	1	0.085
КС 1.03-05	Стойка	45x195	2852	6	0.150
КС 1.03-06	Стойка	45x195	2852	1	0.025
КС 1.03-07	Стойка	45x195	2852	1	0.025
КС 1.03-08	Стойка	45x195	2852	1	0.025
КС 1.03-09	Стойка	45x195	2852	1	0.025
КС 1.03-10	Стойка	45x195	2852	1	0.025
КС 1.03-11	Стойка	45x195	2852	1	0.025
КС 1.03-12	Стойка	45x195	2852	1	0.025
КС 1.03-13	Стойка	45x195	2852	1	0.025
КС 1.03-14	Стойка	45x195	2852	1	0.025
КС 1.03-15	Стойка	45x195	2852	1	0.025
КС 1.03-16	Доски под окна/двери	45x195	2000	1	0.018
КС 1.03-17	Доски под окна/двери	45x195	900	1	0.008
КС 1.03-18	Стойка	45x195	710	4	0.025
КС 1.03-19	Обвязка	45x195	9710	1	0.085
Общая сумма:				27	0.641

						#ID Проекта	
						кадастровый номер Россия	
Изм.	Колуч.	Лист	№Док.	Подп.	Дата		
Разраб.						Индивидуальный жилой дом	Стадия: #Стадия Проекта; Лист: 57; Листов:
ГАП							
Чертеж каркаса стен № КС 1.03 #1							

Вид каркаса снаружи КС 1.04

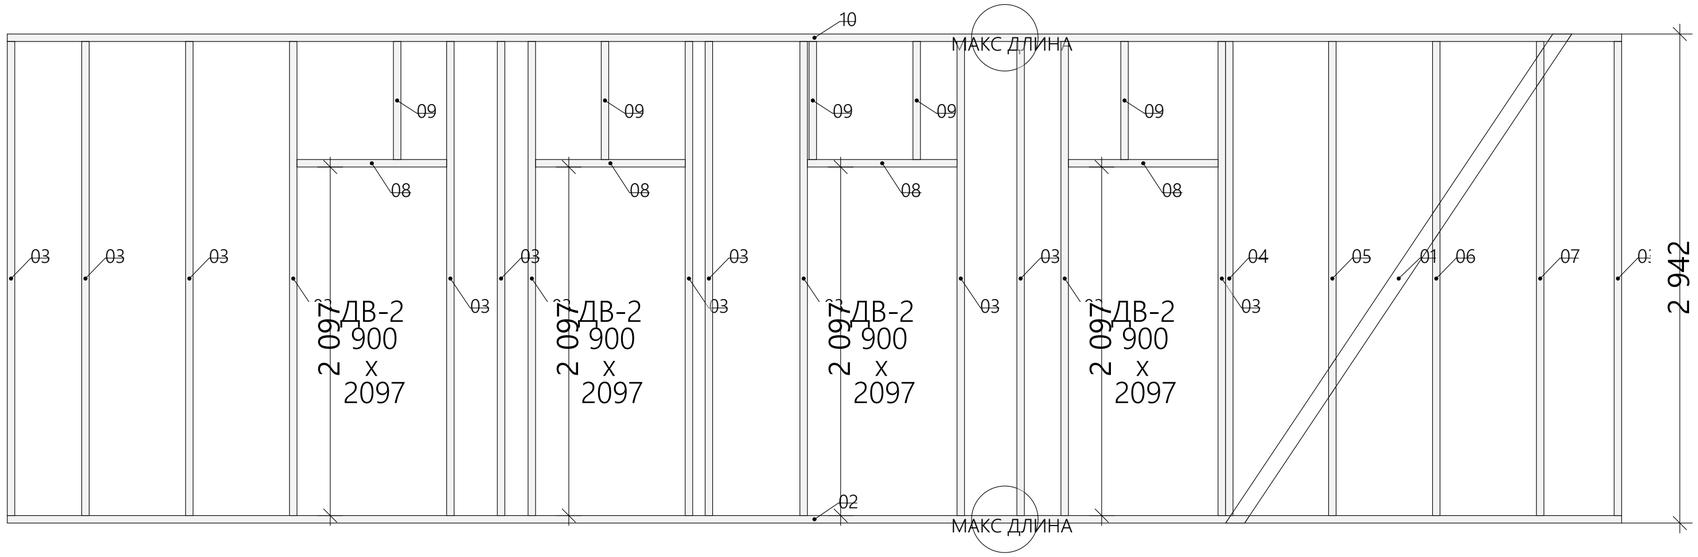

Основной каркас стены №КС 1.04


Номер	Название	Сечение, мм	Длина, мм	Кол-во, шт	Объем, м3
КС 1.04-01	Укосина	20x95	3603	1	0.007
КС 1.04-02	Обвязка	45x195	9710	1	0.085
КС 1.04-03	Стойка	45x195	2852	15	0.375
КС 1.04-04	Стойка	45x195	2852	1	0.025
КС 1.04-05	Стойка	45x195	2852	1	0.025
КС 1.04-06	Стойка	45x195	2852	1	0.025
КС 1.04-07	Стойка	45x195	2852	1	0.025
КС 1.04-08	Доски под окна/двери	45x195	900	4	0.032
КС 1.04-09	Стойка	45x195	710	5	0.031
КС 1.04-10	Обвязка	45x195	9710	1	0.085
			Общая сумма:	31	0.715

Вид каркаса сверху КС 1.04



						#ID Проекта	
						кадастровый номер Россия	
Изм.	Кол.уч.	Лист	№Док.	Подп.	Дата		
Разраб.						Индивидуальный жилой дом	Стадия: #Стадия Проекта; Лист: 58; Листов:
ГАП							
Чертеж каркаса стен № КС 1.04 #1							

Вид каркаса снаружи КС 1.05

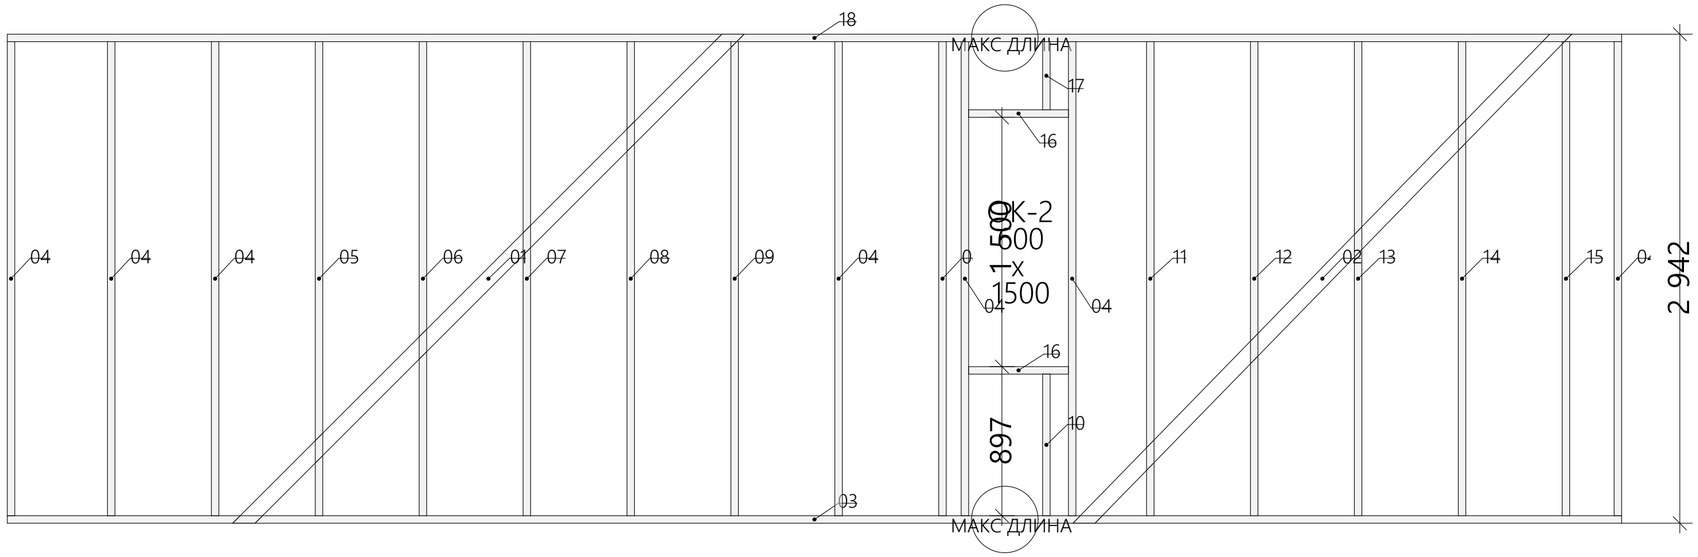

Вид каркаса сверху КС 1.05




Основной каркас стены №КС 1.05

Номер	Название	Сечение, мм	Длина, мм	Кол-во, шт	Объем, м3
КС 1.05-01	Укосина	20x95	4256	1	0.008
КС 1.05-02	Укосина	20x95	4201	1	0.008
КС 1.05-03	Обвязка	45x195	9710	1	0.085
КС 1.05-04	Стойка	45x195	2852	8	0.200
КС 1.05-05	Стойка	45x195	2852	1	0.025
КС 1.05-06	Стойка	45x195	2852	1	0.025
КС 1.05-07	Стойка	45x195	2852	1	0.025
КС 1.05-08	Стойка	45x195	2852	1	0.025
КС 1.05-09	Стойка	45x195	2852	1	0.025
КС 1.05-10	Стойка	45x195	852	1	0.007
КС 1.05-11	Стойка	45x195	2852	1	0.025
КС 1.05-12	Стойка	45x195	2852	1	0.025
КС 1.05-13	Стойка	45x195	2852	1	0.025
КС 1.05-14	Стойка	45x195	2852	1	0.025
КС 1.05-15	Стойка	45x195	2852	1	0.025
КС 1.05-16	Доски под окна/двери	45x195	600	2	0.011
КС 1.05-17	Стойка	45x195	410	1	0.004
КС 1.05-18	Обвязка	45x195	9710	1	0.085
			Общая сумма:	26	0.659

							#ID Проекта
							кадастровый номер Россия
Изм.	Колуч.	Лист	№Док.	Подп.	Дата		
Разраб.						Индивидуальный жилой дом	Стадия: #Стадия Проекта; Лист: 59; Листов:
ГАП							
Чертеж каркаса стен № КС 1.05 #1							

Вид каркаса снаружи КС 1.06

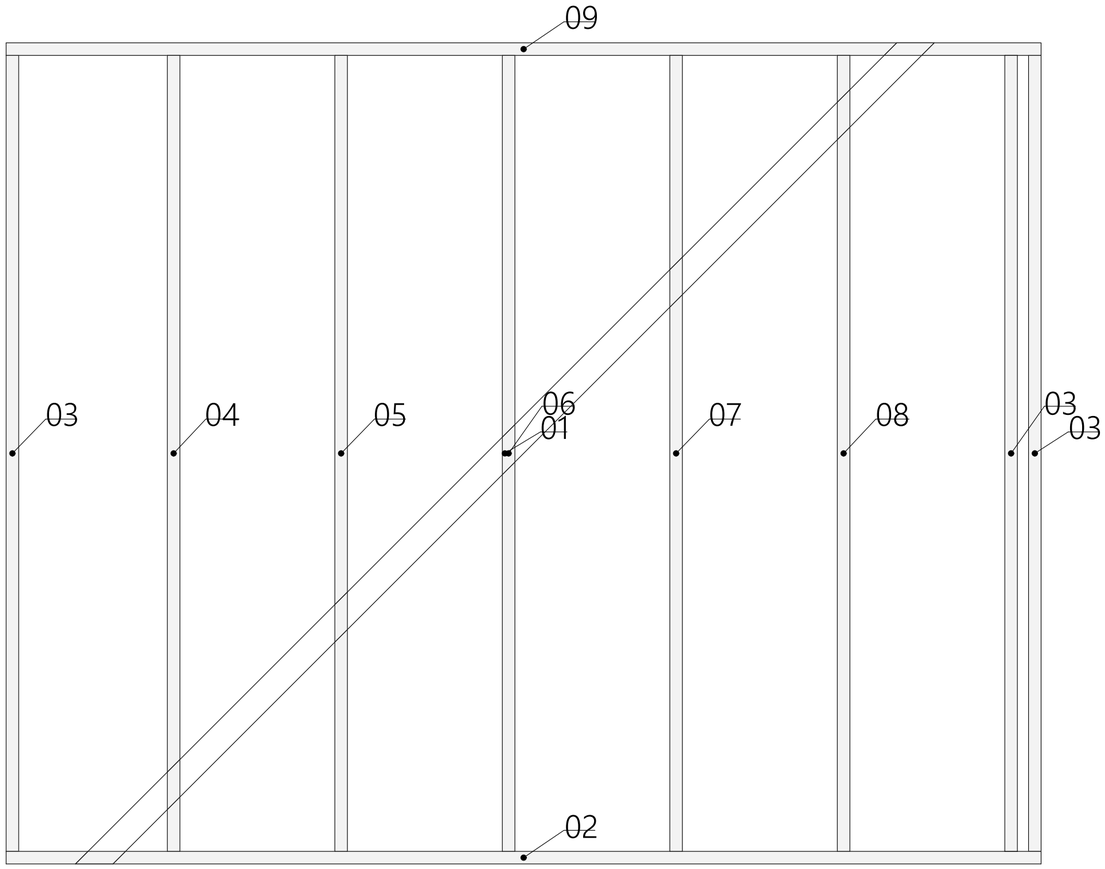

Основной каркас стены №КС 1.06


Номер	Название	Сечение, мм	Длина, мм	Кол-во, шт	Объем, м3
КС 1.06-01	Укосина	45x95	4256	1	0.018
КС 1.06-02	Обвязка	45x95	3708	1	0.016
КС 1.06-03	Стойка	45x95	2852	3	0.037
КС 1.06-04	Стойка	45x95	2852	1	0.012
КС 1.06-05	Стойка	45x95	2852	1	0.012
КС 1.06-06	Стойка	45x95	2852	1	0.012
КС 1.06-07	Стойка	45x95	2852	1	0.012
КС 1.06-08	Стойка	45x95	2852	1	0.012
КС 1.06-09	Обвязка	45x95	3708	1	0.016
			Общая сумма:	11	0.147

Вид каркаса сверху КС 1.06



						#ID Проекта		
						кадастровый номер Россия		
Изм.	Кол.уч.	Лист	№Док.	Подп.	Дата			
Разраб.						Индивидуальный жилой дом	Стадия: #Стадия Проекта	Лист: 60 / Листов:
ГАП								
Чертеж каркаса стен № КС 1.06 #1								

Вид каркаса снаружи КС 1.07

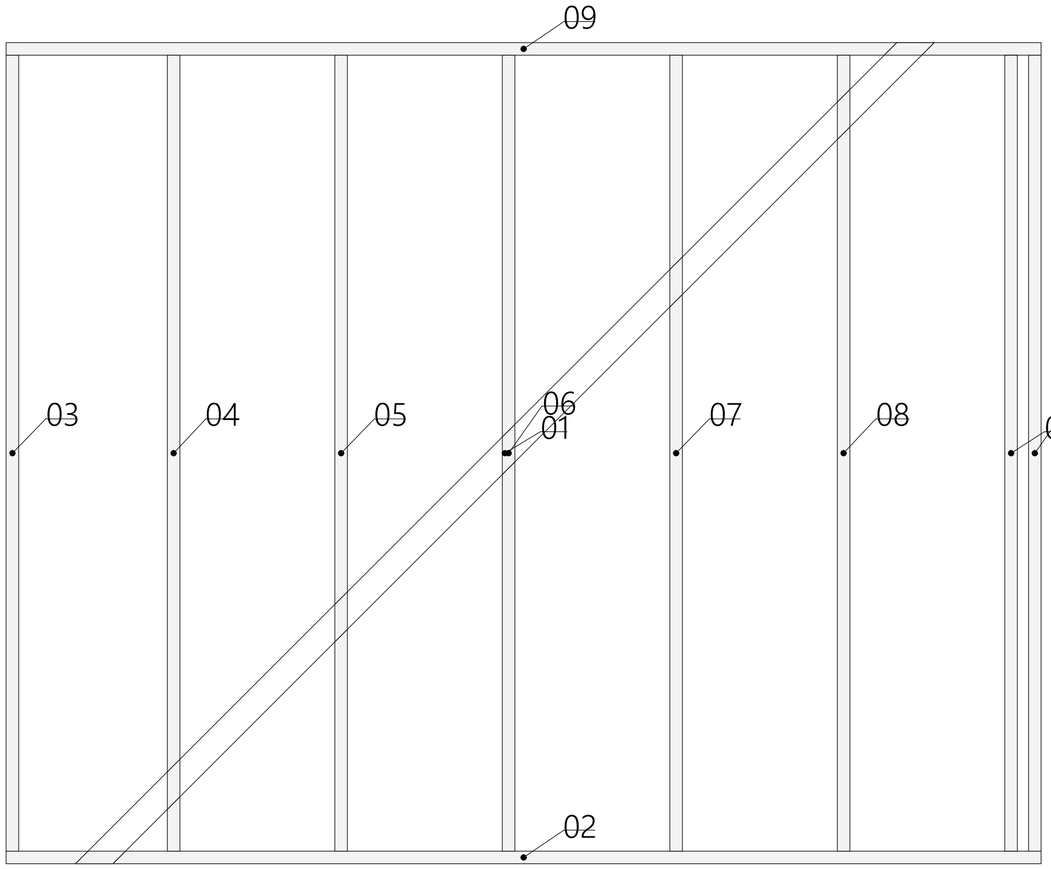

Основной каркас стены №КС 1.07


Номер	Название	Сечение, мм	Длина, мм	Кол-во, шт	Объем, м3
КС 1.07-01	Укосина	45x95	4256	1	0.018
КС 1.07-02	Обвязка	45x95	3708	1	0.016
КС 1.07-03	Стойка	45x95	2852	3	0.037
КС 1.07-04	Стойка	45x95	2852	1	0.012
КС 1.07-05	Стойка	45x95	2852	1	0.012
КС 1.07-06	Стойка	45x95	2852	1	0.012
КС 1.07-07	Стойка	45x95	2852	1	0.012
КС 1.07-08	Стойка	45x95	2852	1	0.012
КС 1.07-09	Обвязка	45x95	3708	1	0.016
			Общая сумма:	11	0.147

Вид каркаса сверху КС 1.07



						#ID Проекта	
						кадастровый номер Россия	
Изм.	Колуч.	Лист	№Док.	Подп.	Дата		
Разраб.						Индивидуальный жилой дом	Стадия: #Стадия Проекта; Лист: 61; Листов:
ГАП							
Чертеж каркаса стен № КС 1.07 #1							

Вид каркаса снаружи КС 1.08

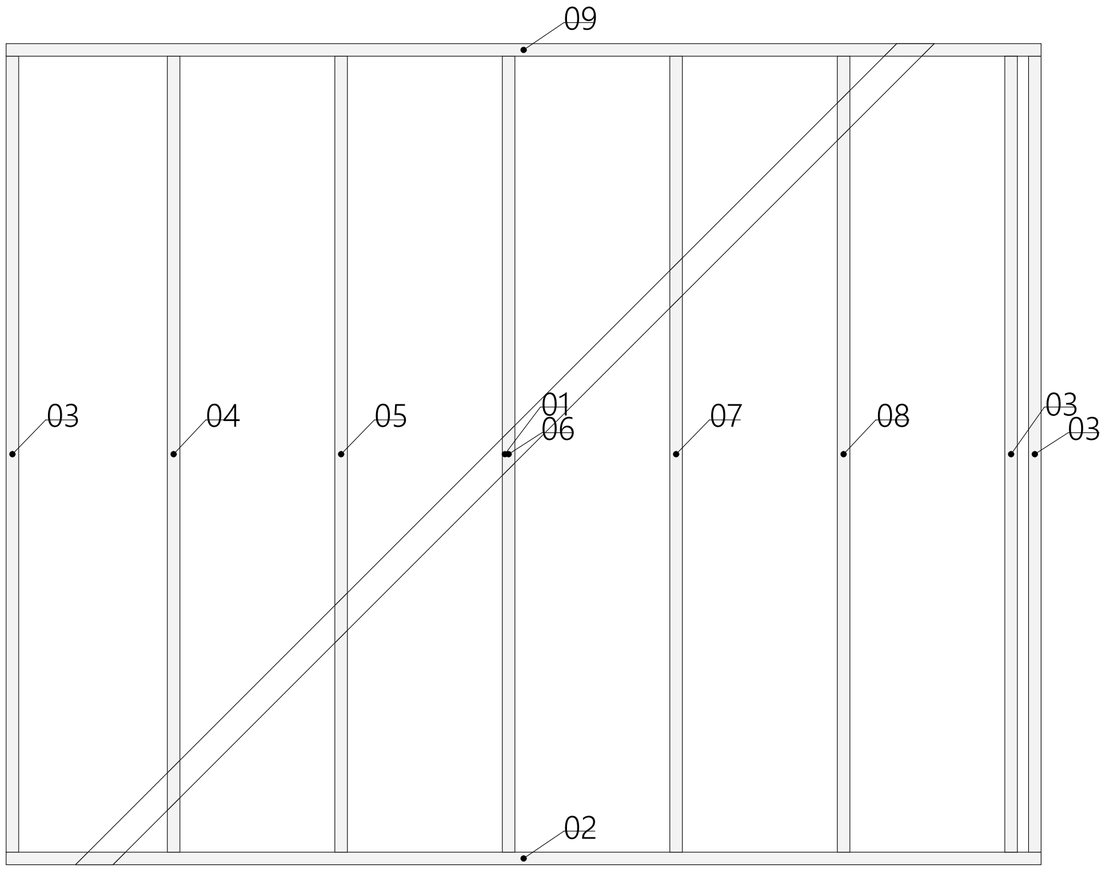

Основной каркас стены №КС 1.08


Номер	Название	Сечение, мм	Длина, мм	Кол-во, шт	Объем, м3
КС 1.08-01	Укосина	45x95	4256	1	0.018
КС 1.08-02	Обвязка	45x95	3708	1	0.016
КС 1.08-03	Стойка	45x95	2852	3	0.037
КС 1.08-04	Стойка	45x95	2852	1	0.012
КС 1.08-05	Стойка	45x95	2852	1	0.012
КС 1.08-06	Стойка	45x95	2852	1	0.012
КС 1.08-07	Стойка	45x95	2852	1	0.012
КС 1.08-08	Стойка	45x95	2852	1	0.012
КС 1.08-09	Обвязка	45x95	3708	1	0.016
			Общая сумма:	11	0.147

Вид каркаса сверху КС 1.08



						#ID Проекта	
						кадастровый номер Россия	
Изм.	Колуч.	Лист	№Док.	Подп.	Дата		
Разраб.						Индивидуальный жилой дом	Стадия: #Стадия Проекта; Лист: 62; Листов:
ГАП							
Чертеж каркаса стен № КС 1.08 #1							

Вид каркаса снаружи КС 1.09

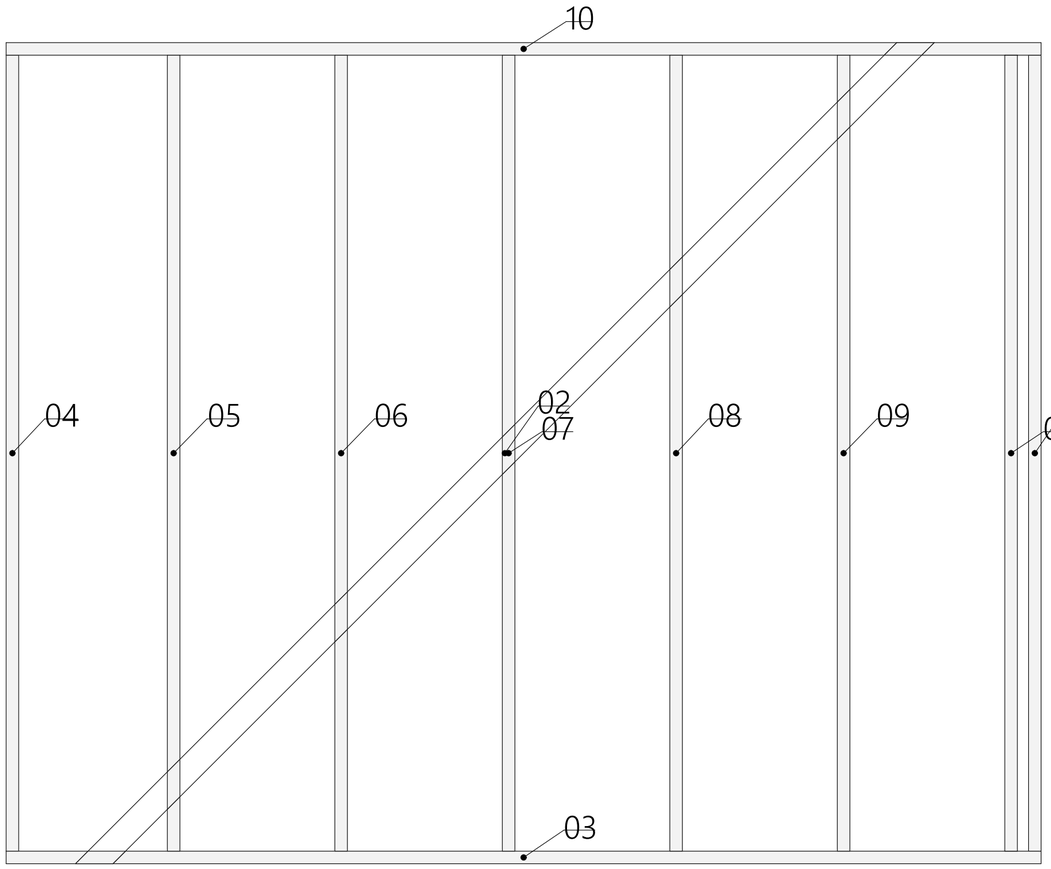

Основной каркас стены №КС 1.09


Номер	Название	Сечение, мм	Длина, мм	Кол-во, шт	Объем, м3
КС 1.09-01		45x95	3708	1	0.016
КС 1.09-02	Укосина	45x95	4256	1	0.018
КС 1.09-03	Обвязка	45x95	3708	1	0.016
КС 1.09-04	Стойка	45x95	2852	3	0.037
КС 1.09-05	Стойка	45x95	2852	1	0.012
КС 1.09-06	Стойка	45x95	2852	1	0.012
КС 1.09-07	Стойка	45x95	2852	1	0.012
КС 1.09-08	Стойка	45x95	2852	1	0.012
КС 1.09-09	Стойка	45x95	2852	1	0.012
КС 1.09-10	Обвязка	45x95	3708	1	0.016
				Общая сумма: 12	0.163

Вид каркаса сверху КС 1.09



						#ID Проекта	
						кадастровый номер Россия	
Изм.	Колуч.	Лист	№Док.	Подп.	Дата		
Разраб.						Индивидуальный жилой дом	Стадия: #Стадия Проекта; Лист: 63; Листов:
ГАП							
Чертеж каркаса стен № КС 1.09 #1							

Вид каркаса снаружи КС 1.10

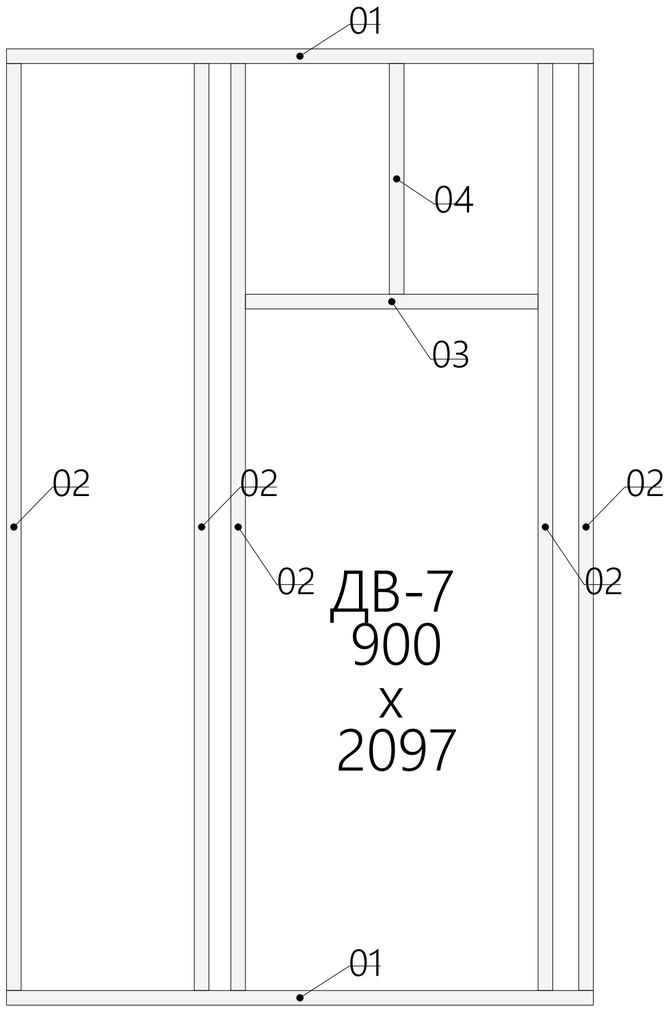

Основной каркас стены №КС 1.10


Номер	Название	Сечение, мм	Длина, мм	Кол-во, шт	Объем, м3
КС 1.10-01		45x95	1805	1	0.008
КС 1.10-01	Обвязка	45x95	1805	2	0.015
КС 1.10-02	Стойка	45x95	2852	5	0.061
КС 1.10-03	Доски под окна/двери	45x95	900	1	0.004
КС 1.10-04	Стойка	45x95	710	1	0.003
			Общая сумма:	10	0.091

Вид каркаса сверху КС 1.10




						#ID Проекта		
						кадастровый номер Россия		
Изм.	Кол.уч.	Лист	№Док.	Подп.	Дата			
Разраб.						Индивидуальный жилой дом	Стадия	Лист	Листов
ГАП							#Стадия Проекта	64	
Чертеж каркаса стен № КС 1.10 #1									

Вид каркаса снаружи КС 1.11

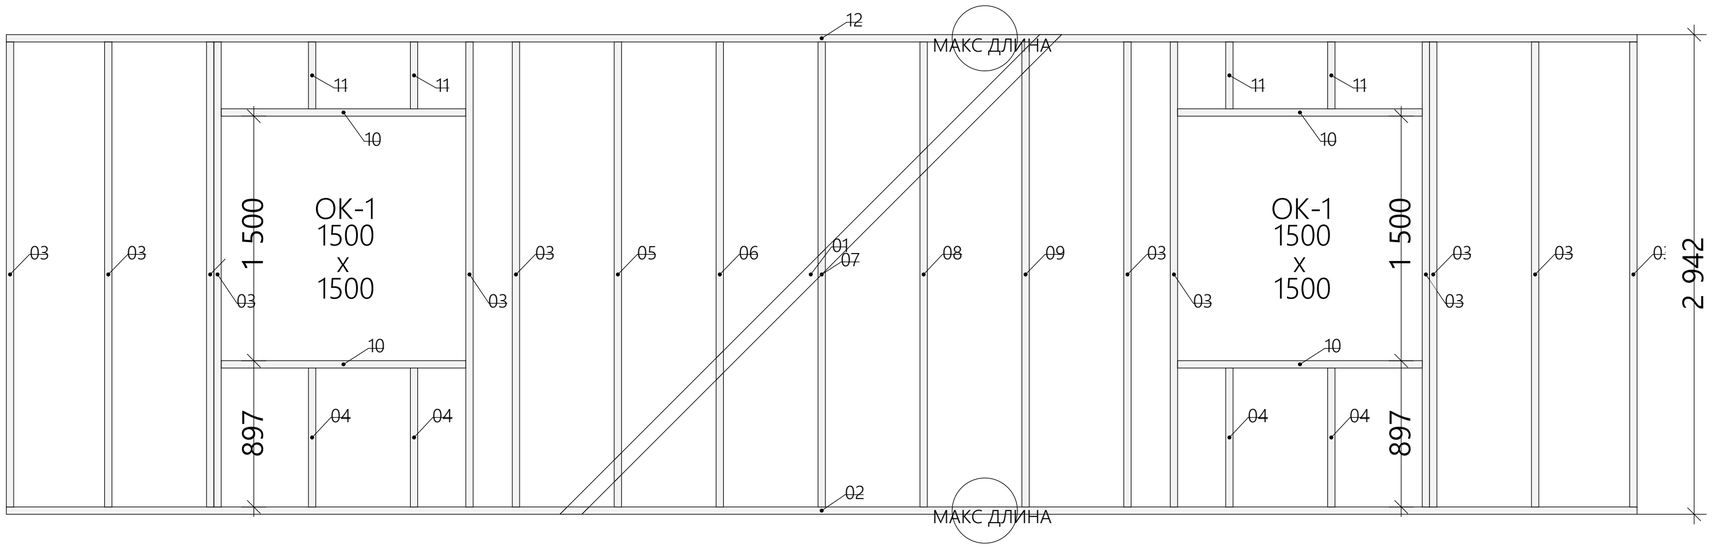

Вид каркаса сверху КС 1.11

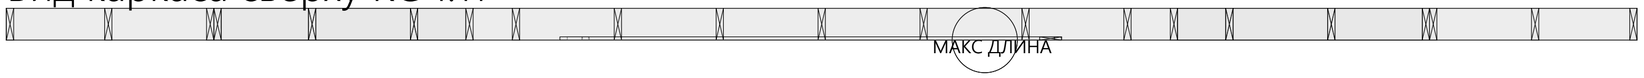


Основной каркас стены №КС 1.11

Номер	Название	Сечение, мм	Длина, мм	Кол-во, шт	Объем, м3
КС 1.11-01	Укосина	20x95	4256	1	0.008
КС 1.11-02	Обвязка	45x195	10000	1	0.088
КС 1.11-03	Стойка	45x195	2852	12	0.300
КС 1.11-04	Стойка	45x195	852	4	0.030
КС 1.11-05	Стойка	45x195	2852	1	0.025
КС 1.11-06	Стойка	45x195	2852	1	0.025
КС 1.11-07	Стойка	45x195	2852	1	0.025
КС 1.11-08	Стойка	45x195	2852	1	0.025
КС 1.11-09	Стойка	45x195	2852	1	0.025
КС 1.11-10	Доски под окна/двери	45x195	1500	4	0.053
КС 1.11-11	Стойка	45x195	410	4	0.014
КС 1.11-12	Обвязка	45x195	10000	1	0.088
			Общая сумма:	32	0.706

						#ID Проекта	
						кадастровый номер Россия	
Изм.	Кол.уч.	Лист	№Док.	Подп.	Дата		
Разраб.						Индивидуальный жилой дом	Стадия: #Стадия Проекта; Лист: 65; Листов:
ГАП							
Чертеж каркаса стен № КС 1.11 #1							

Вид каркаса снаружи КС 2.01

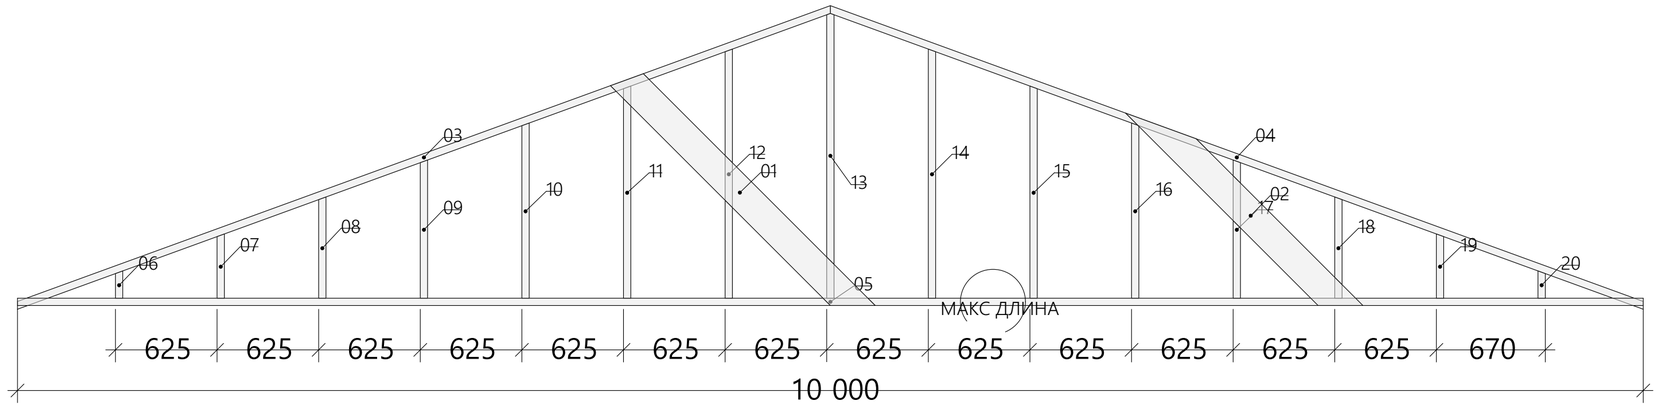

Вид каркаса сверху КС 2.01




Основной каркас стены №КС 2.01

Номер	Название	Сечение, мм	Длина, мм	Кол-во, шт	Объем, м3
КС 2.01-01	Укосина	45x195	2108	1	0.018
КС 2.01-02	Укосина	45x195	1869	1	0.016
КС 2.01-03	Обвязка	45x195	5337	1	0.047
КС 2.01-04	Обвязка	45x195	5337	1	0.047
КС 2.01-05	Обвязка	45x195	10000	1	0.088
КС 2.01-06	Стойка	45x195	168	1	0.001
КС 2.01-07	Стойка	45x195	395	1	0.003
КС 2.01-08	Стойка	45x195	623	1	0.005
КС 2.01-09	Стойка	45x195	850	1	0.007
КС 2.01-10	Стойка	45x195	1078	1	0.009
КС 2.01-11	Стойка	45x195	1305	1	0.011
КС 2.01-12	Стойка	45x195	1533	1	0.013
КС 2.01-13	Стойка	45x195	1752	1	0.015
КС 2.01-14	Стойка	45x195	1533	1	0.013
КС 2.01-15	Стойка	45x195	1305	1	0.011
КС 2.01-16	Стойка	45x195	1078	1	0.009
КС 2.01-17	Стойка	45x195	850	1	0.007
КС 2.01-18	Стойка	45x195	623	1	0.005
КС 2.01-19	Стойка	45x195	395	1	0.003
КС 2.01-20	Стойка	45x195	168	1	0.001
			Общая сумма:	20	0.336

						#ID Проекта	
						кадастровый номер Россия	
Изм.	Кол.уч.	Лист	№Док.	Подп.	Дата		
Разраб.						Индивидуальный жилой дом	Стадия: #Стадия Проекта; Лист: 66; Листов:
ГАП							
Чертеж каркаса стен № КС 2.01 #1							

Вид каркаса снаружи КС 2.02

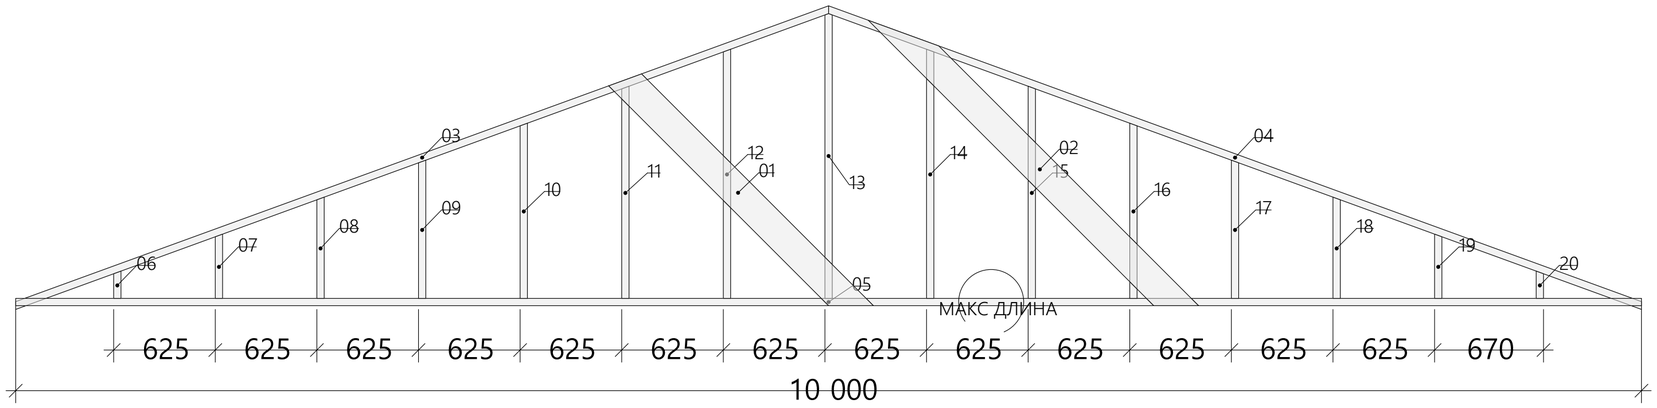

Вид каркаса сверху КС 2.02




Основной каркас стены №КС 2.02


Номер	Название	Сечение, мм	Длина, мм	Кол-во, шт	Объем, м3
КС 2.02-01	Укосина	45x195	2108	1	0.018
КС 2.02-02	Укосина	45x195	2678	1	0.024
КС 2.02-03	Обвязка	45x195	5337	1	0.047
КС 2.02-04	Обвязка	45x195	5337	1	0.047
КС 2.02-05	Обвязка	45x195	10000	1	0.088
КС 2.02-06	Стойка	45x195	168	1	0.001
КС 2.02-07	Стойка	45x195	395	1	0.003
КС 2.02-08	Стойка	45x195	623	1	0.005
КС 2.02-09	Стойка	45x195	850	1	0.007
КС 2.02-10	Стойка	45x195	1078	1	0.009
КС 2.02-11	Стойка	45x195	1305	1	0.011
КС 2.02-12	Стойка	45x195	1533	1	0.013
КС 2.02-13	Стойка	45x195	1752	1	0.015
КС 2.02-14	Стойка	45x195	1533	1	0.013
КС 2.02-15	Стойка	45x195	1305	1	0.011
КС 2.02-16	Стойка	45x195	1078	1	0.009
КС 2.02-17	Стойка	45x195	850	1	0.007
КС 2.02-18	Стойка	45x195	623	1	0.005
КС 2.02-19	Стойка	45x195	395	1	0.003
КС 2.02-20	Стойка	45x195	168	1	0.001
			Общая сумма:	20	0.343

Изм.	Колуч.	Лист	№Док.	Подп.	Дата	#ID Проекта			
						кадастровый номер Россия			
Разраб.						Индивидуальный жилой дом	Стадия	Лист	Листов
ГАП							#Стадия Проекта	67	
Чертеж каркаса стен № КС 2.02 #1									

Вид каркаса снаружи КС 2.03

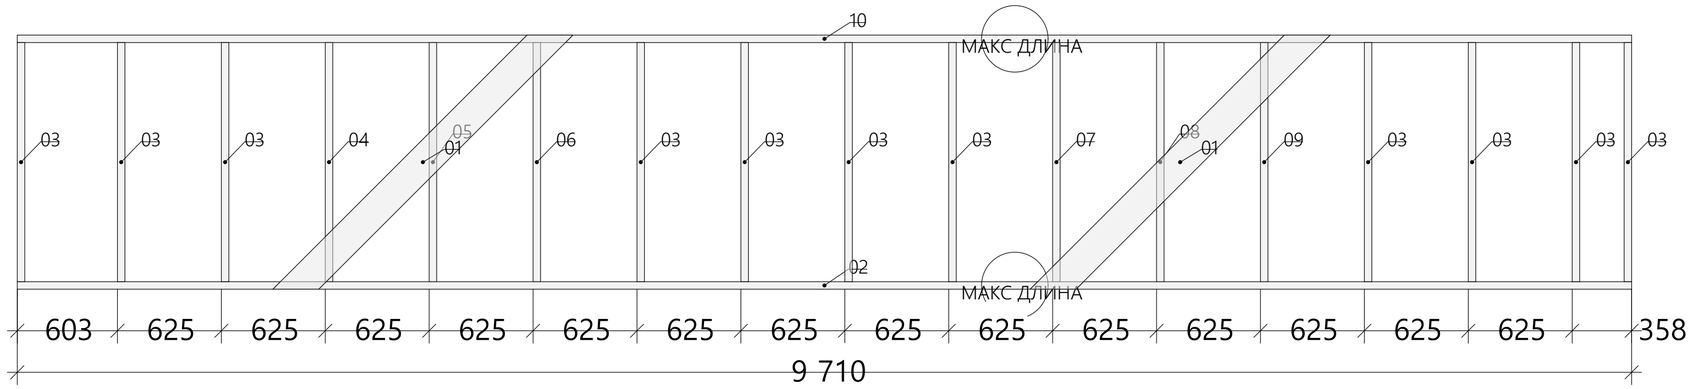

Вид каркаса сверху КС 2.03

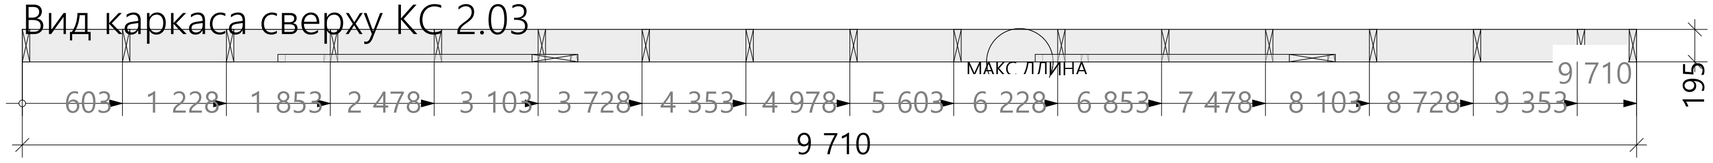


Основной каркас стены №КС 2.03


Номер	Название	Сечение, мм	Длина, мм	Кол-во, шт	Объем, м3
КС 2.03-01	Укосина	45x195	2357	2	0.041
КС 2.03-02	Обвязка	45x195	9710	1	0.085
КС 2.03-03	Стойка	45x195	1439	11	0.139
КС 2.03-04	Стойка	45x195	1439	1	0.013
КС 2.03-05	Стойка	45x195	1439	1	0.013
КС 2.03-06	Стойка	45x195	1439	1	0.013
КС 2.03-07	Стойка	45x195	1439	1	0.013
КС 2.03-08	Стойка	45x195	1439	1	0.013
КС 2.03-09	Стойка	45x195	1439	1	0.013
КС 2.03-10	Обвязка	45x195	9710	1	0.085
			Общая сумма:	21	0.426

						#ID Проекта	
						кадастровый номер Россия	
Изм.	Колуч.	Лист	№Док.	Подп.	Дата		
Разраб.						Индивидуальный жилой дом	Стадия: #Стадия Проекта; Лист: 68; Листов:
ГАП							
Чертеж каркаса стен № КС 2.03 #1							

Вид каркаса снаружи КС 2.04

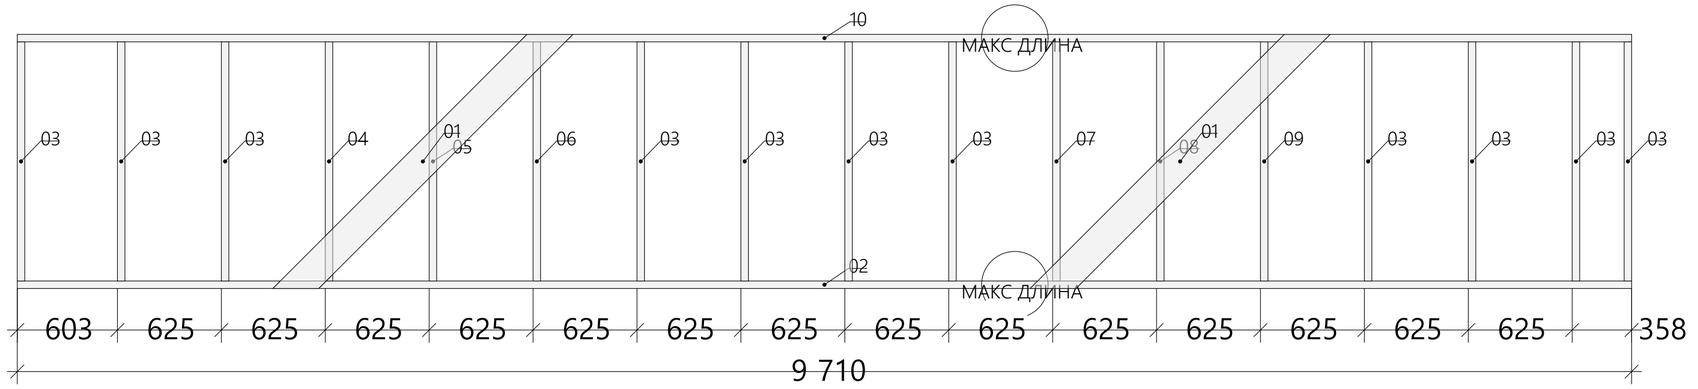

Вид каркаса сверху КС 2.04

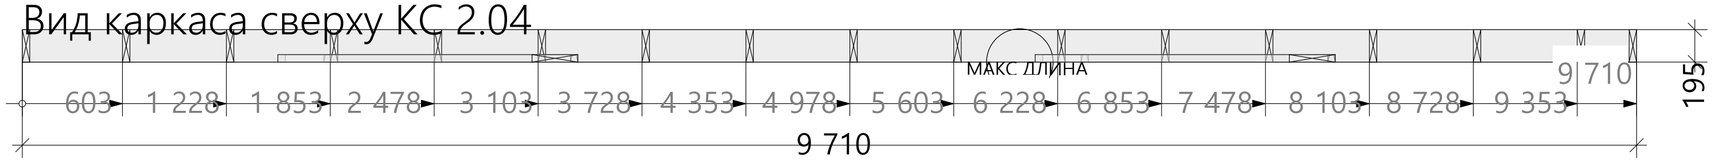


Основной каркас стены №КС 2.04

Номер	Название	Сечение, мм	Длина, мм	Кол-во, шт	Объем, м3
КС 2.04-01	Укосина	45x195	2357	2	0.041
КС 2.04-02	Обвязка	45x195	9710	1	0.085
КС 2.04-03	Стойка	45x195	1439	11	0.139
КС 2.04-04	Стойка	45x195	1439	1	0.013
КС 2.04-05	Стойка	45x195	1439	1	0.013
КС 2.04-06	Стойка	45x195	1439	1	0.013
КС 2.04-07	Стойка	45x195	1439	1	0.013
КС 2.04-08	Стойка	45x195	1439	1	0.013
КС 2.04-09	Стойка	45x195	1439	1	0.013
КС 2.04-10	Обвязка	45x195	9710	1	0.085
			Общая сумма:	21	0.426

						#ID Проекта	
						кадастровый номер Россия	
Изм.	Колуч.	Лист	№Док.	Подп.	Дата		
Разраб.						Индивидуальный жилой дом	Стадия: #Стадия Проекта; Лист: 69; Листов:
ГАП							
Чертеж каркаса стен № КС 2.04 #1							

Вид каркаса снаружи КС 2.05

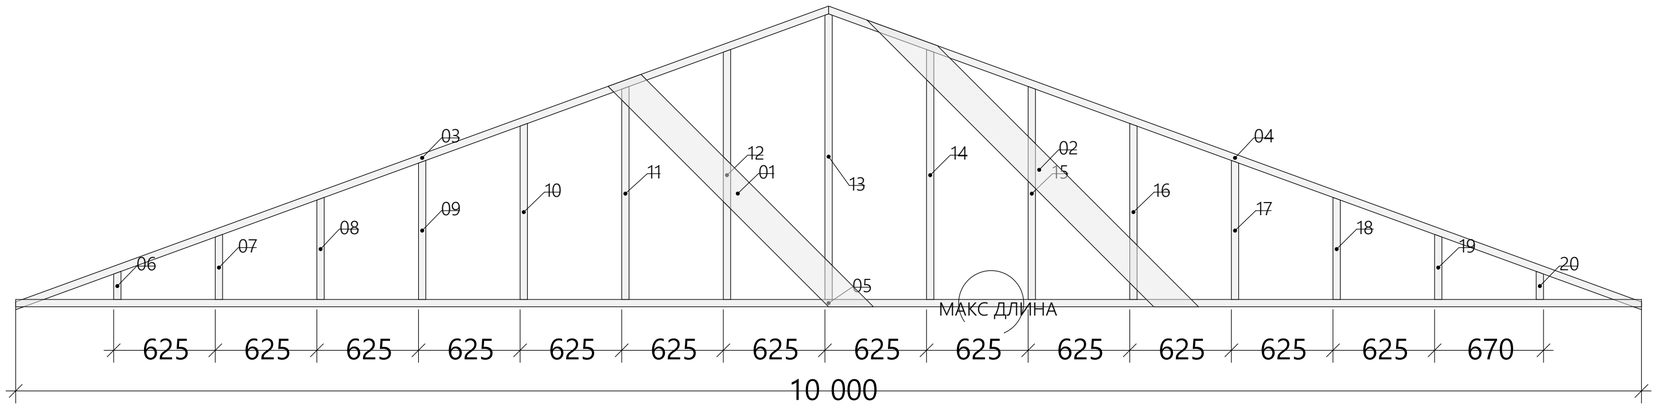

Вид каркаса сверху КС 2.05



Основной каркас стены №КС 2.05

Номер	Название	Сечение, мм	Длина, мм	Кол-во, шт	Объем, м3
КС 2.05-01	Укосина	45x195	2113	1	0.019
КС 2.05-02	Укосина	45x195	2690	1	0.024
КС 2.05-03	Обвязка	45x195	5337	1	0.047
КС 2.05-04	Обвязка	45x195	5337	1	0.047
КС 2.05-05	Обвязка	45x195	10000	1	0.088
КС 2.05-06	Стойка	45x195	173	1	0.002
КС 2.05-07	Стойка	45x195	400	1	0.004
КС 2.05-08	Стойка	45x195	628	1	0.006
КС 2.05-09	Стойка	45x195	855	1	0.008
КС 2.05-10	Стойка	45x195	1083	1	0.010
КС 2.05-11	Стойка	45x195	1310	1	0.011
КС 2.05-12	Стойка	45x195	1538	1	0.013
КС 2.05-13	Стойка	45x195	1757	1	0.015
КС 2.05-14	Стойка	45x195	1538	1	0.013
КС 2.05-15	Стойка	45x195	1310	1	0.011
КС 2.05-16	Стойка	45x195	1083	1	0.010
КС 2.05-17	Стойка	45x195	855	1	0.008
КС 2.05-18	Стойка	45x195	628	1	0.006
КС 2.05-19	Стойка	45x195	400	1	0.004
КС 2.05-20	Стойка	45x195	173	1	0.002
			Общая сумма:	20	0.344

						#ID Проекта	
						кадастровый номер Россия	
Изм.	Кол.уч.	Лист	№Док.	Подп.	Дата		
Разраб.						Индивидуальный жилой дом	Стадия: #Стадия Проекта; Лист: 70; Листов:
ГАП							
Чертеж каркаса стен № КС 2.05 #1							