


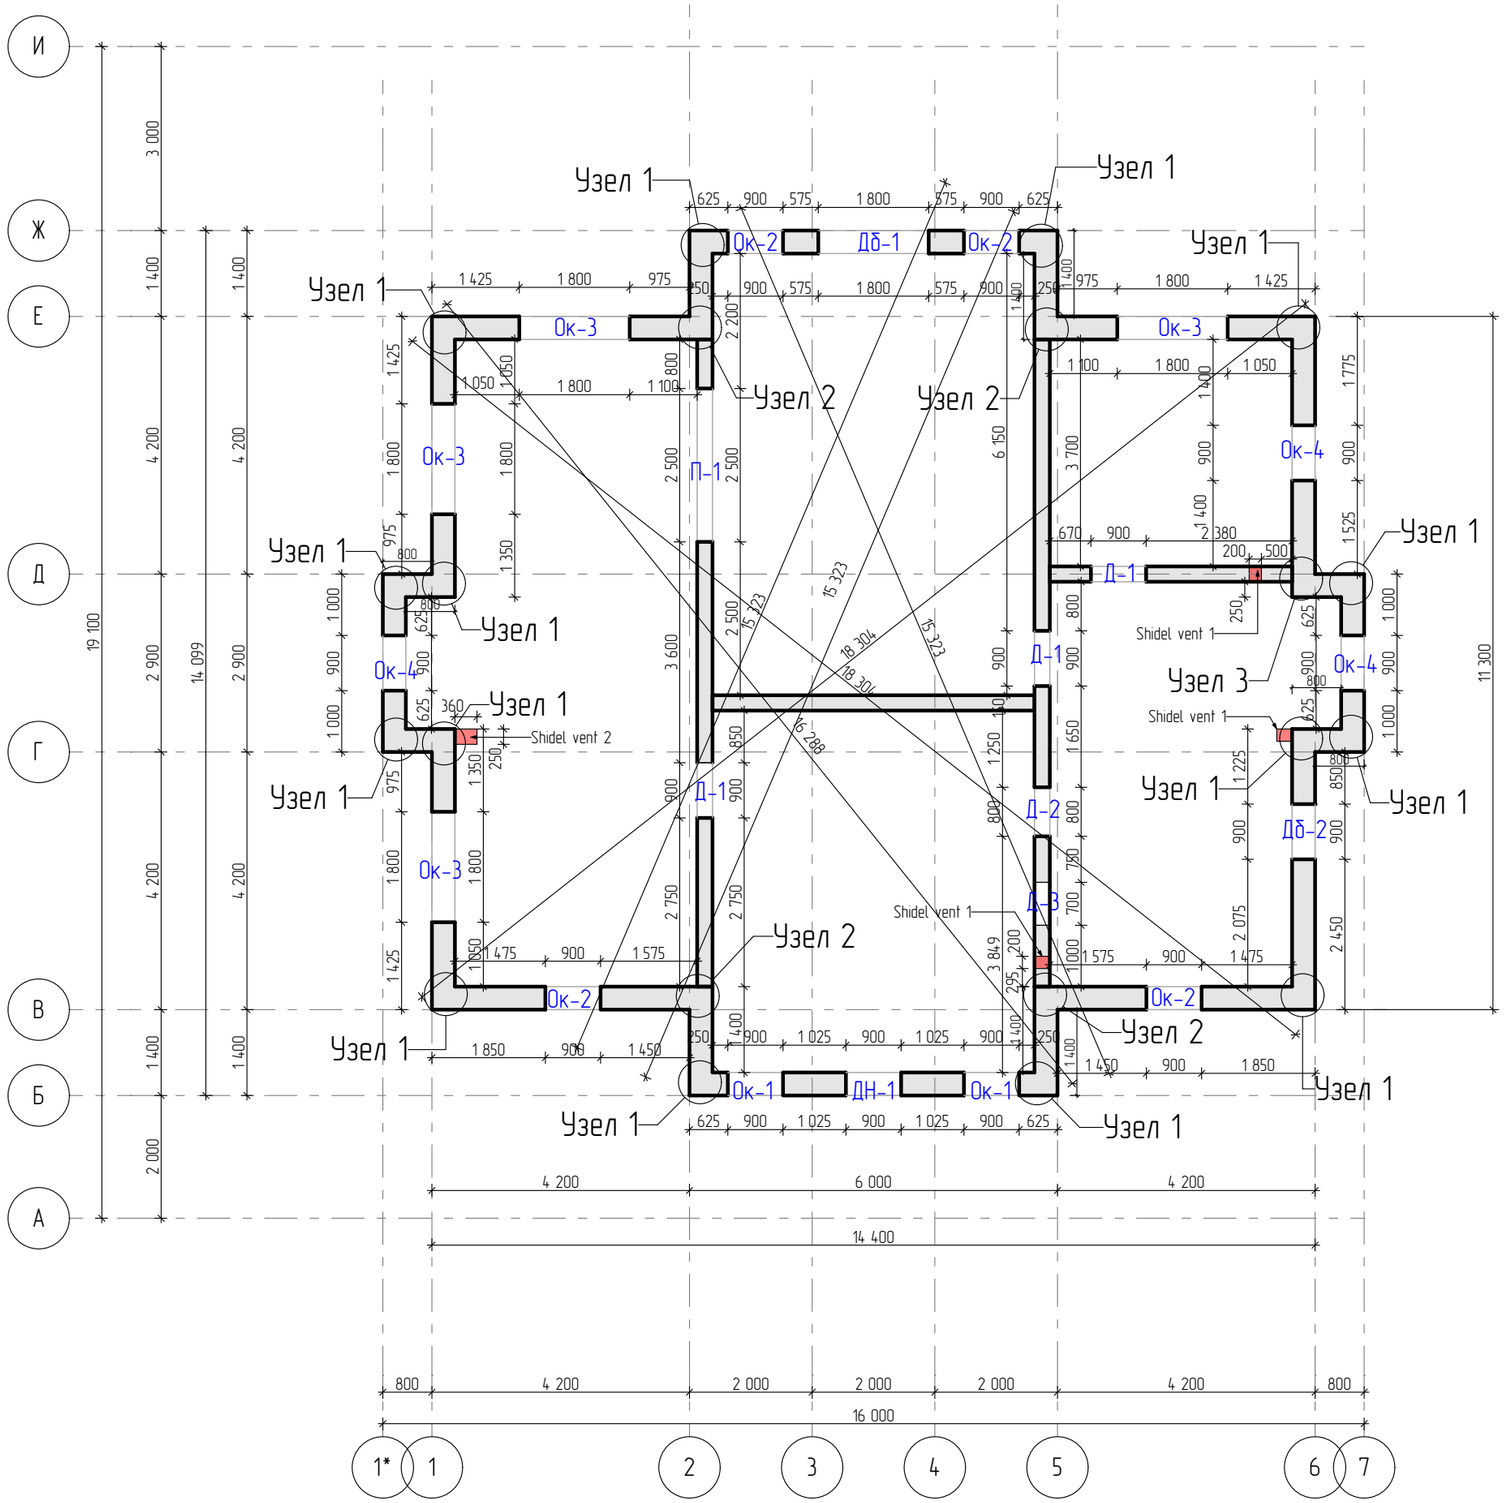



Узел 1

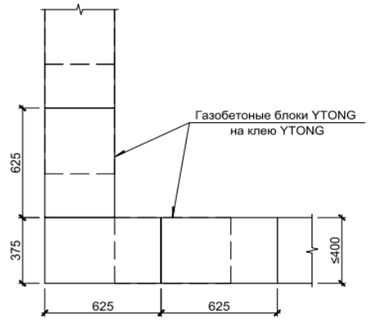

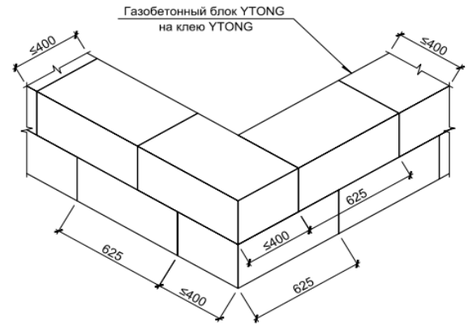

Узел 2

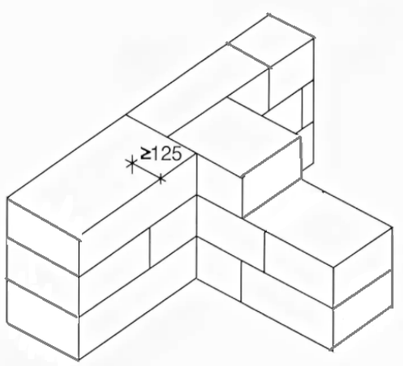

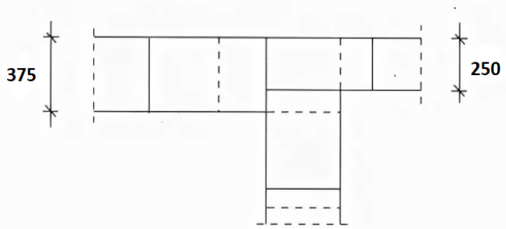

Согласовано


Взам. инв. №

Подпись и дата

Инв. № подл.

Кладочный план 1 этаж

Лист

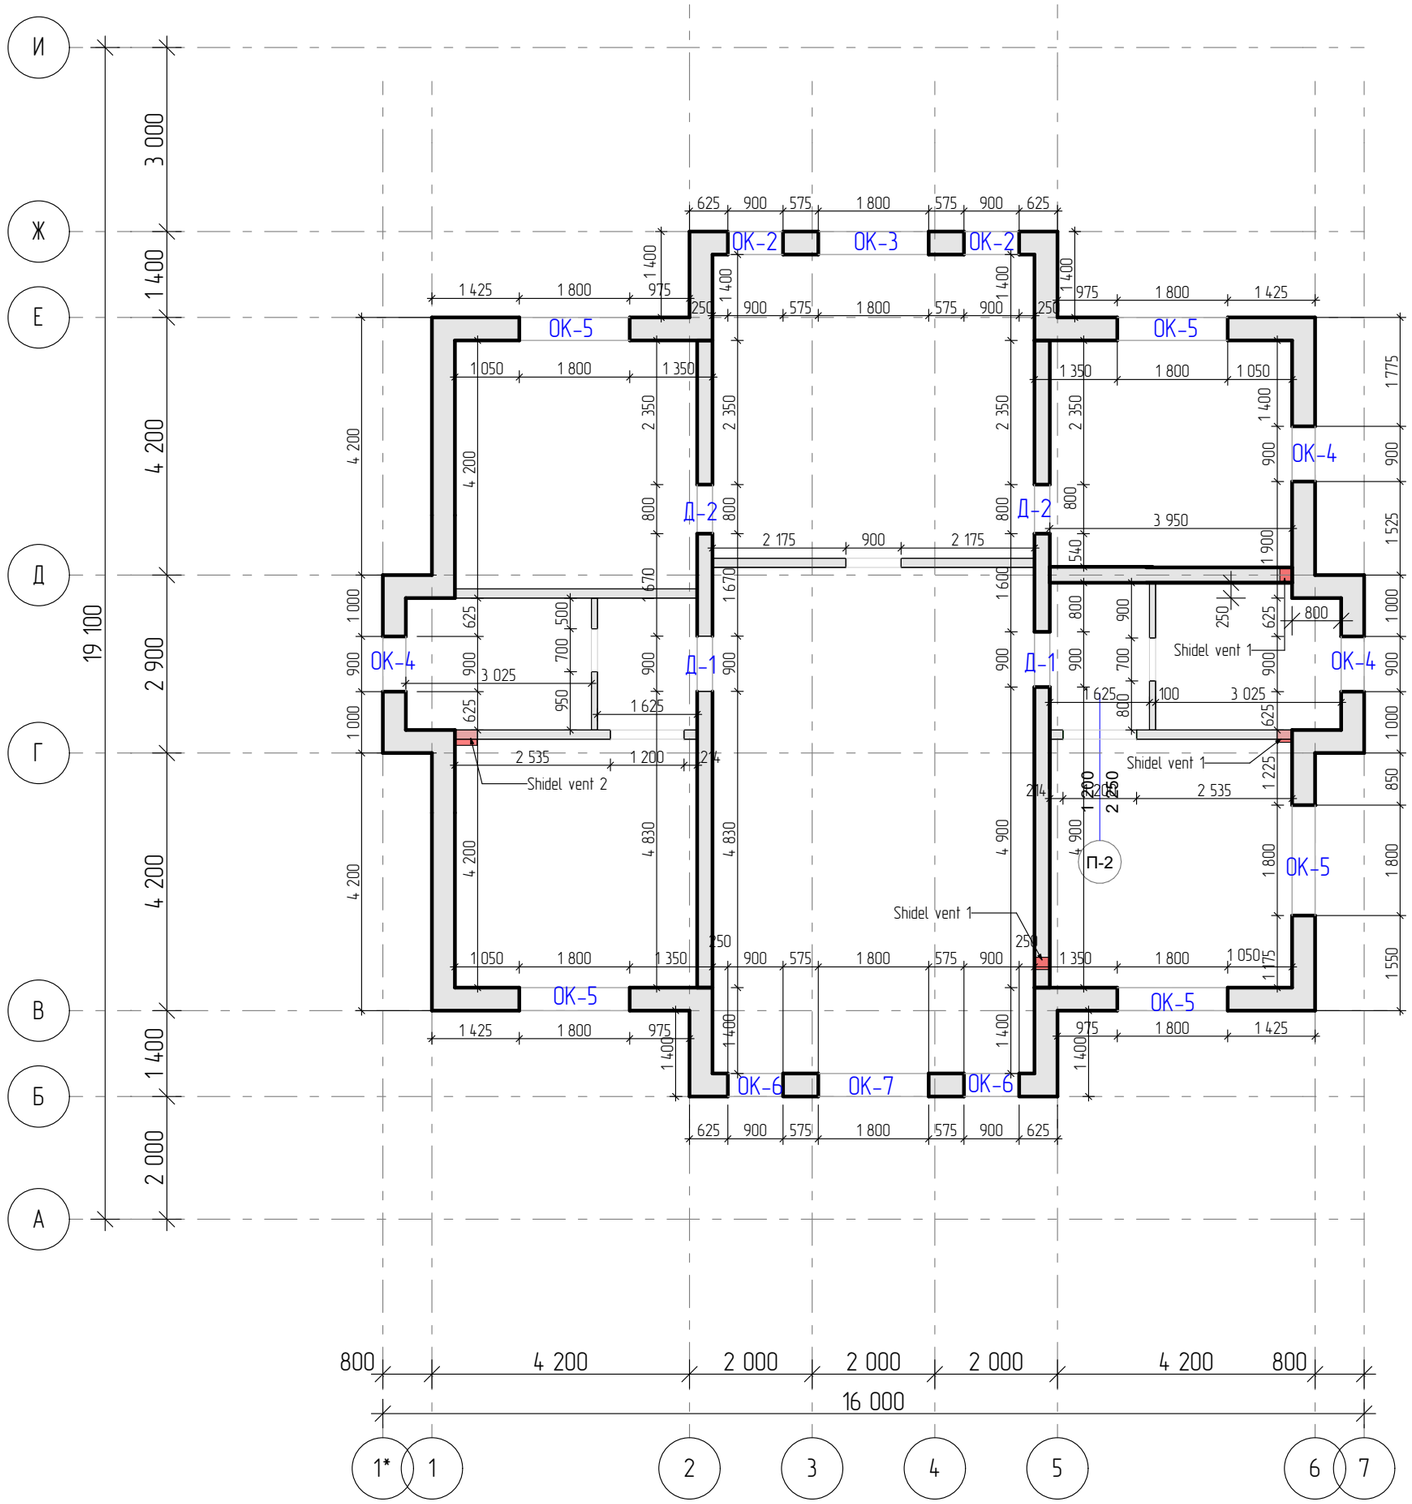

Согласовано

Взам. инв. №


Подпись и дата

Инв. № подл.


Кладочный план 2 этаж

Лист


План лестницы

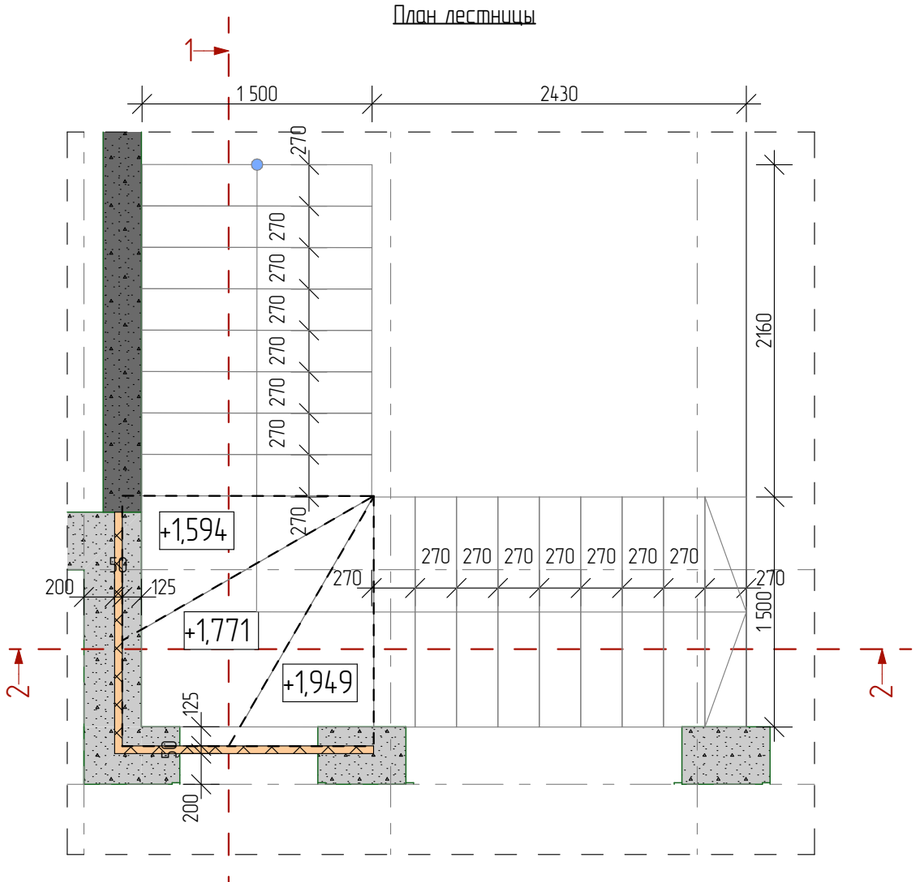

Сечение 1-1

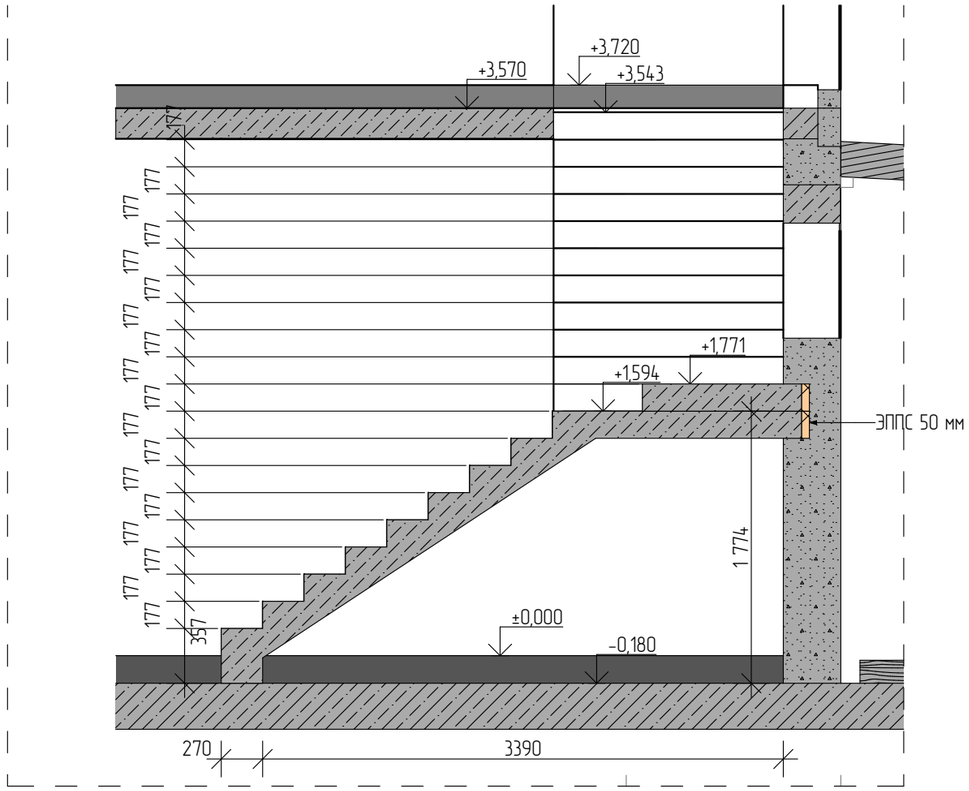

Сечение 2-2

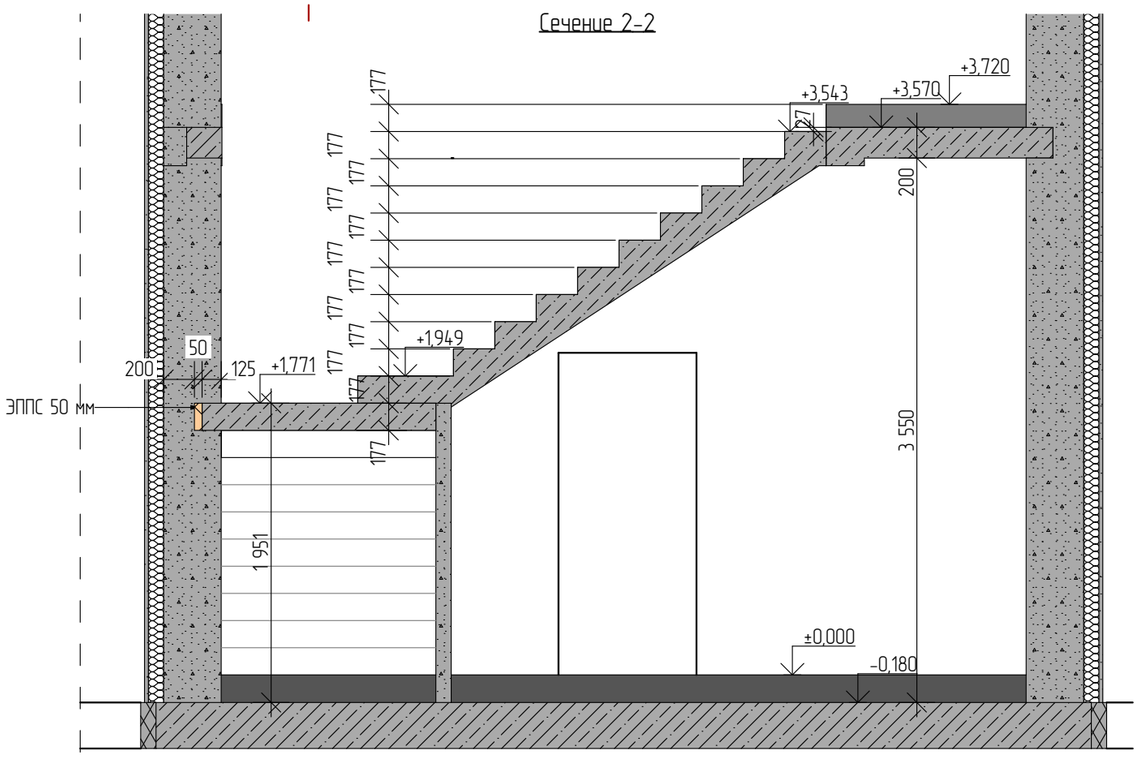

Примечание:

1) Проектное решение опирания лестницы может быть изменено инженером в процессе строительства без потери прочностных характеристик, если таковое потребуется.

					2020			
Изм.	Кол.уч	Лист	№док.	Подпись	Дата			
Разработал		–				Индивидуальный жилой дом	стадия	лист	листов
Архитектор		Салыкова В.Г.					РД	1	
Заказчик						План лестницы			


Согласовано:

Взам. инв. №


Подпись и дата

Инв. № подл.


Развертка по стене 1*

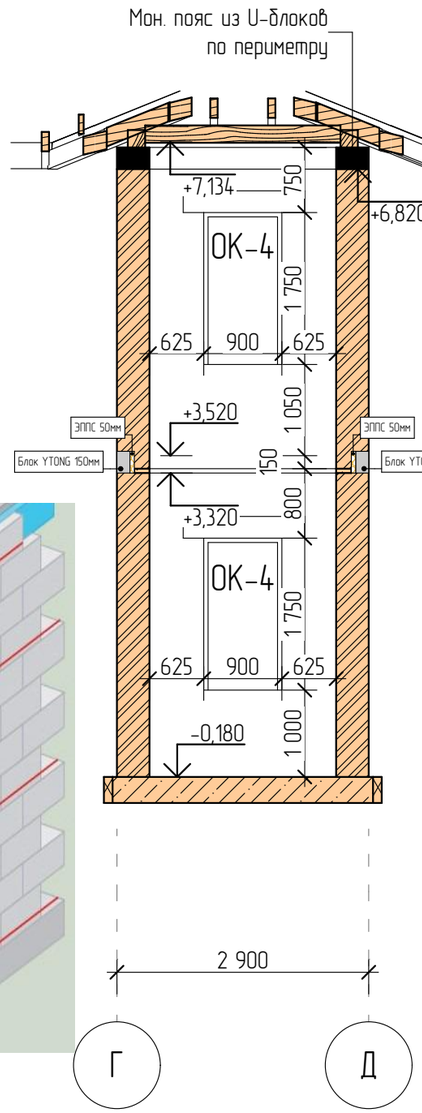

Развертка по стене 1

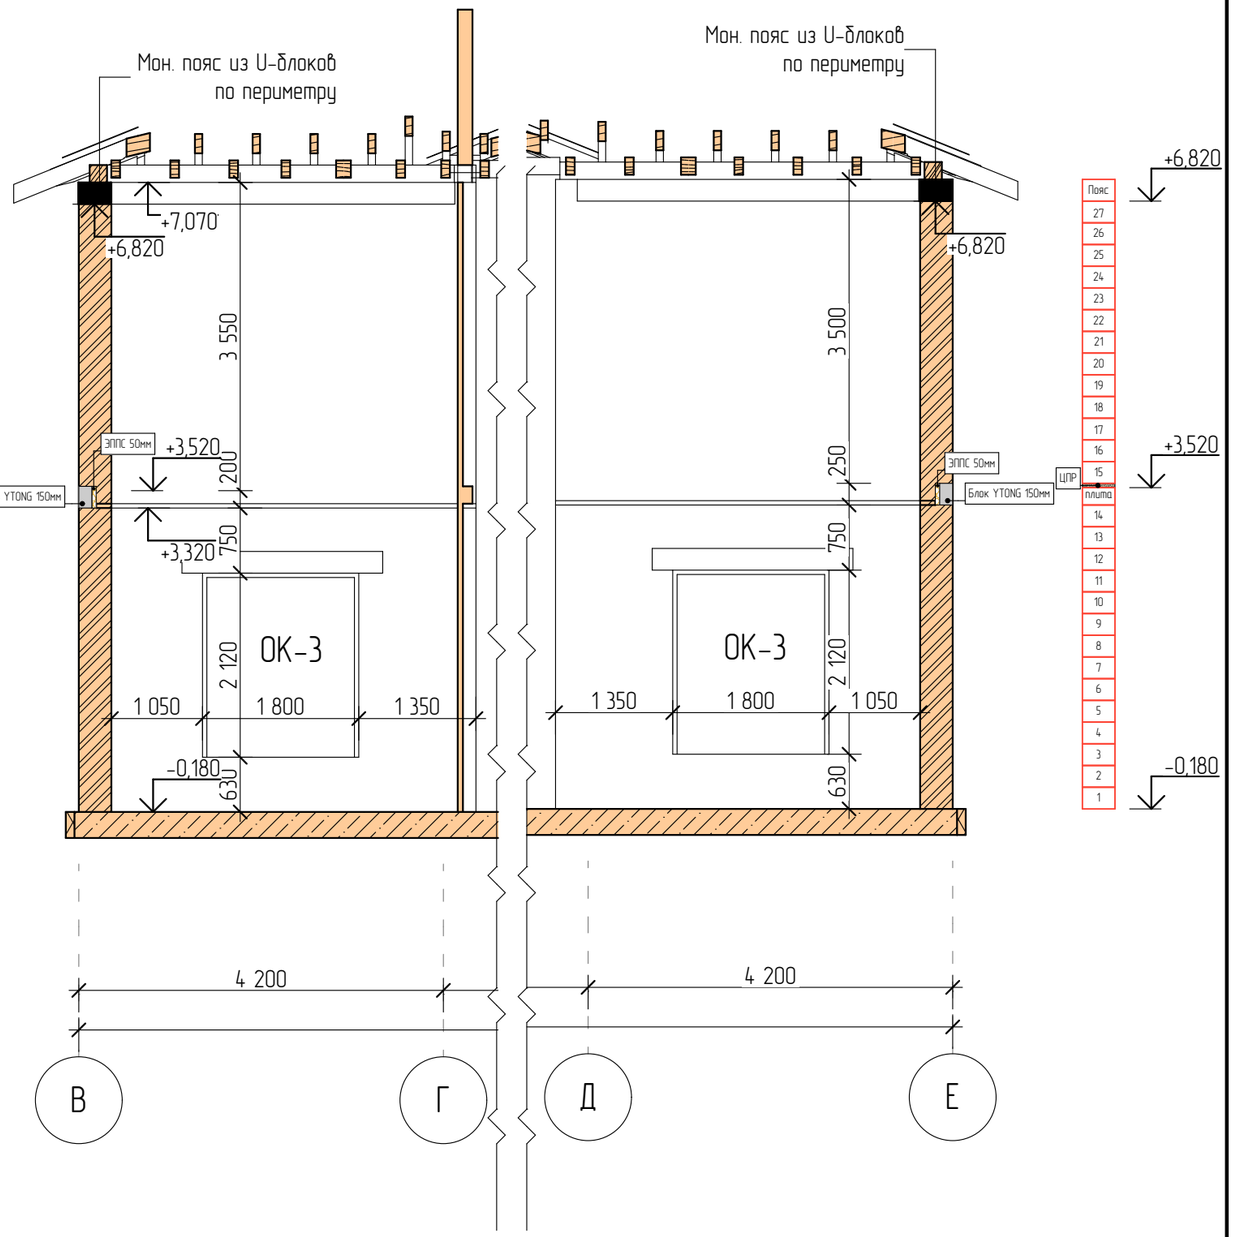

Армирование газосиликатных блоков

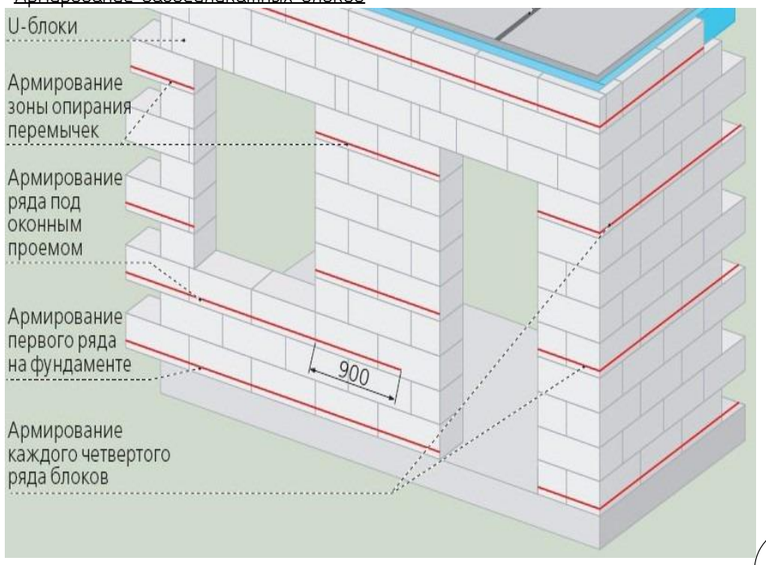

Примечание:

1) Модуль высоты кладки Ytong принят без учета шва и составляет 250 мм.
2) Первый ряд блоков укладывается на выравнивающий слой ЦПР
3) Кладка должна вестись на растворе для тонкошовной кладки столщиной шва 1-3 мм. Кладку вести от торцов/углов к центру стены. Блоки укладывать с перевязкой, со смещением камней по отношению к нижнему ряду на 125 мм
4) Несущие наружные и внутренние стены связывать между собой кладкой при помощи перевязки на всю высоту стены.
5) Перегородки крепить к несущим стенам с помощью гибких связей.
6) Перемычки над проемами из U-блоков, если не указано иное. Опирание перемычки на стену не менее 250 мм

					2020	
Изм.	Кол.уч	Лист	№док.	Подпись	Дата	
Разработал		–				Индивидуальный жилой дом
Архитектор		Салыкова В.Г.				
Заказчик						Развертки

стадия	лист	листов
РД	2	

Согласовано

Взам. инв. №

Подпись и дата

Инв. № подл.


Согласовано:

Взам. инв. №

Подпись и дата

Инв. № подл.

Развертка по стене 2

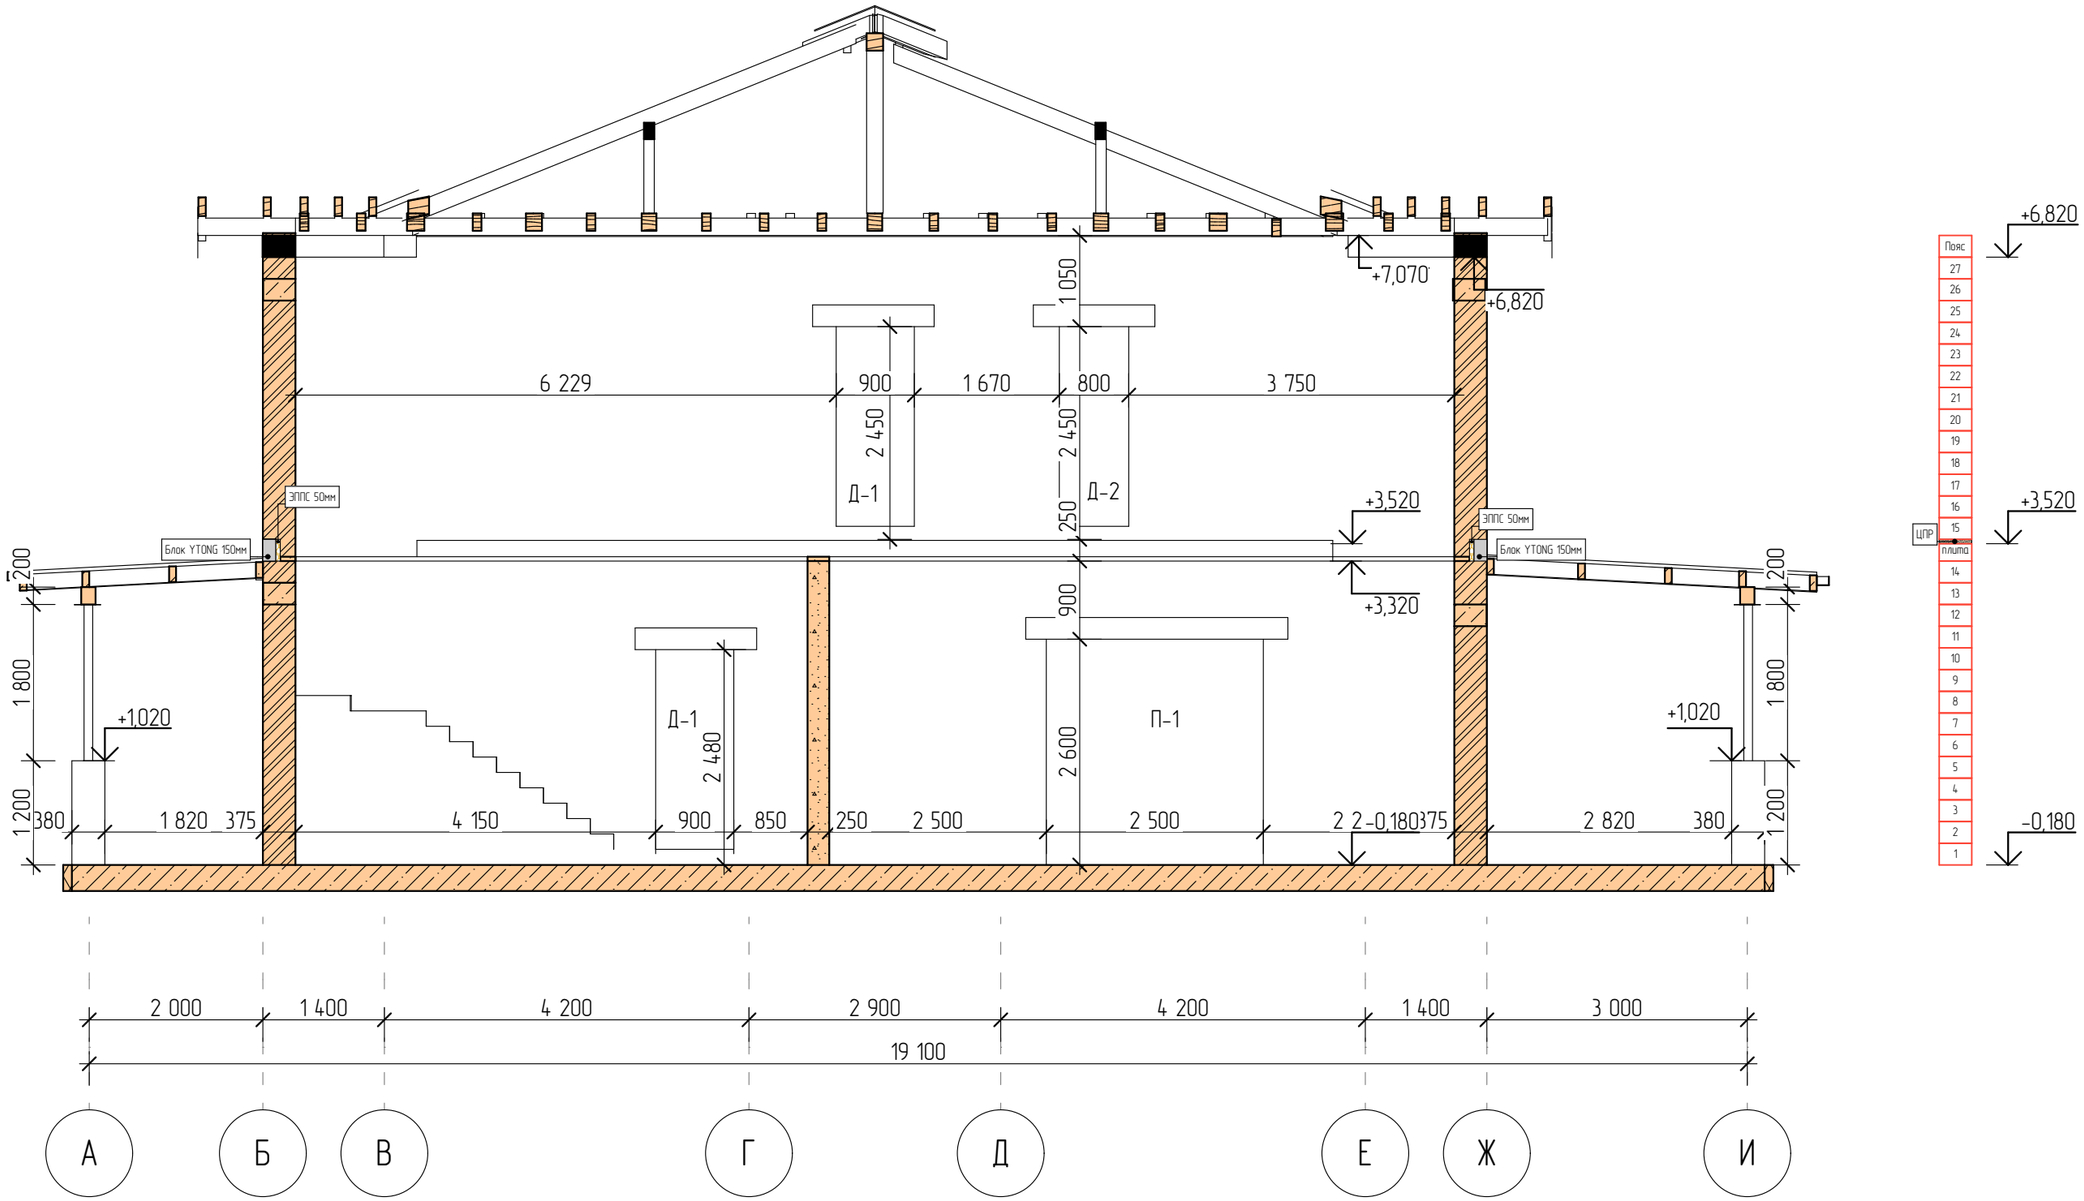



Примечание:

1) Модуль высоты кладки Ytong принят без учета шва и составляет 250 мм.
2) Первый ряд блоков укладывается на выравнивающий слой ЦПР
3) Кладка должна вестись на растворе для тонкошовной кладки столщиной шва 1-3 мм. Кладку вести от торцов/углов к центру стены. Блоки укладывать с перевязкой, со смещением камней по отношению к нижнему ряду на 125 мм
4) Несущие наружные и внутренние стены связывать между собой кладкой при помощи перевязки на всю высоту стены.
5) Перегородки крепить к несущим стенам с помощью гибких связей.
6) Перемычки над проемами из U-блоков, если не указано иное. Опирание перемычки на стену не менее 250 мм

					2020			
Изм.	Кол.уч	Лист	№док.	Подпись	Дата			
Разработал		–				Индивидуальный жилой дом	стадия	лист	листов
Архитектор		Салыкова В.Г.					РД	3	
Заказчик						Развертки			

Развертка по стене 5

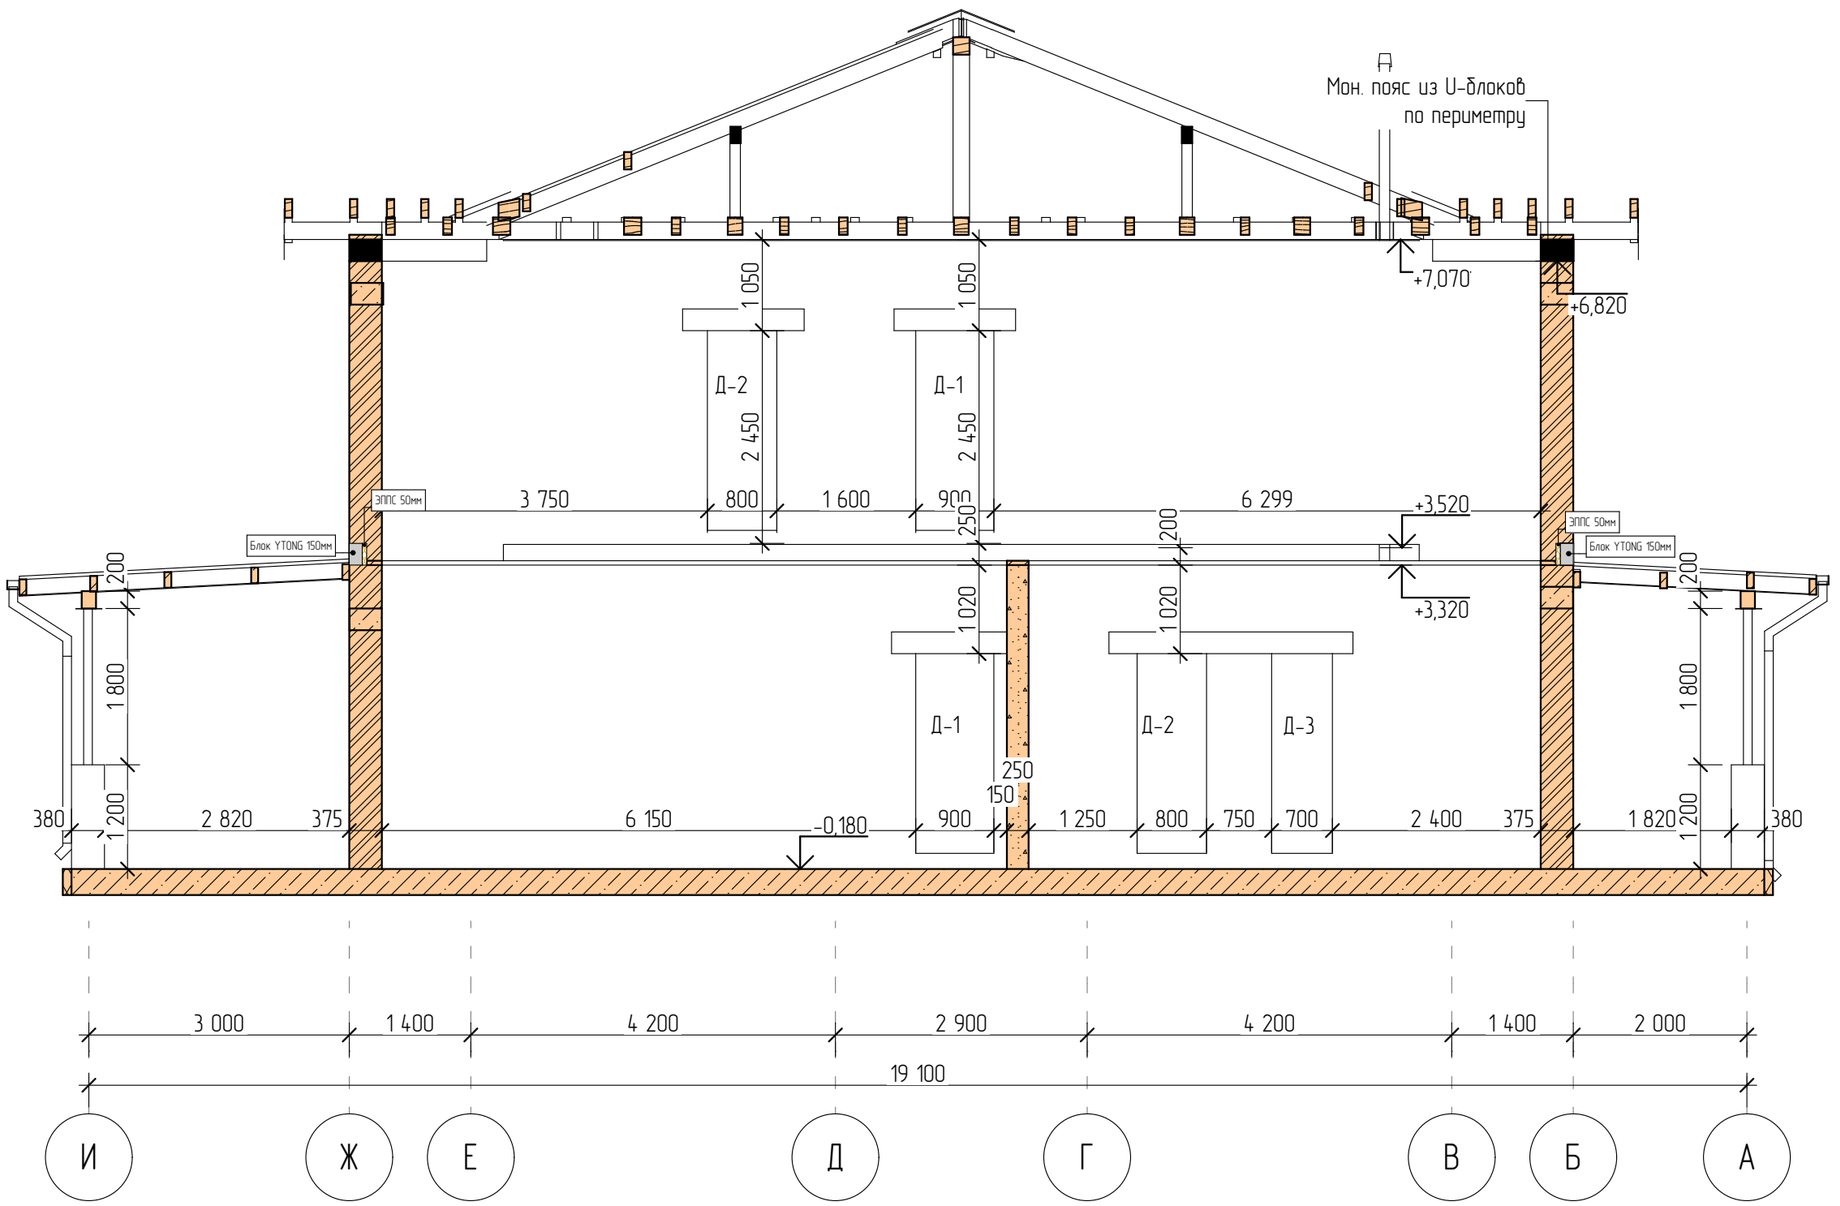

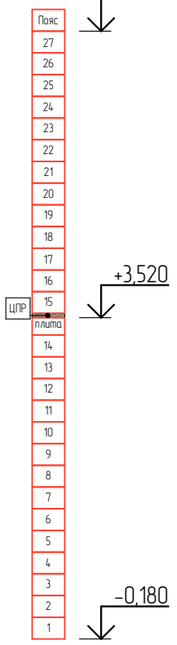

Примечание:
1) Модуль высоты кладки Ytong принят без учета шва и составляет 250 мм.
2) Первый ряд блоков укладывается на выравнивающий слой ЦПР
3) Кладка должна вестись на растворе для тонкошовной кладки столщиной шва 1-3 мм. Кладку вести от торцов/углов к центру стены. Блоки укладывать с перевязкой, со смещением камней по отношению к нижнему ряду на 125 мм
4) Несущие наружные и внутренние стены связывать между собой кладкой при помощи перевязки на всю высоту стены.
5) Перегородки крепить к несущим стенам с помощью гибких связей.
6) Перемычки над проемами из U-блоков, если не указано иное. Опирание перемычки на стену не менее 250 мм

					2020			
Изм.	Кол.уч	Лист	№док.	Подпись	Дата			
Разработал		–				Индивидуальный жилой дом	стадия	лист	листов
Архитектор		Салыкова В.Г.					РД	4	
Заказчик						Развертки			


Согласовано

Взам. инв. №


Подпись и дата

Инв. № подл.

Развертка по стене 6

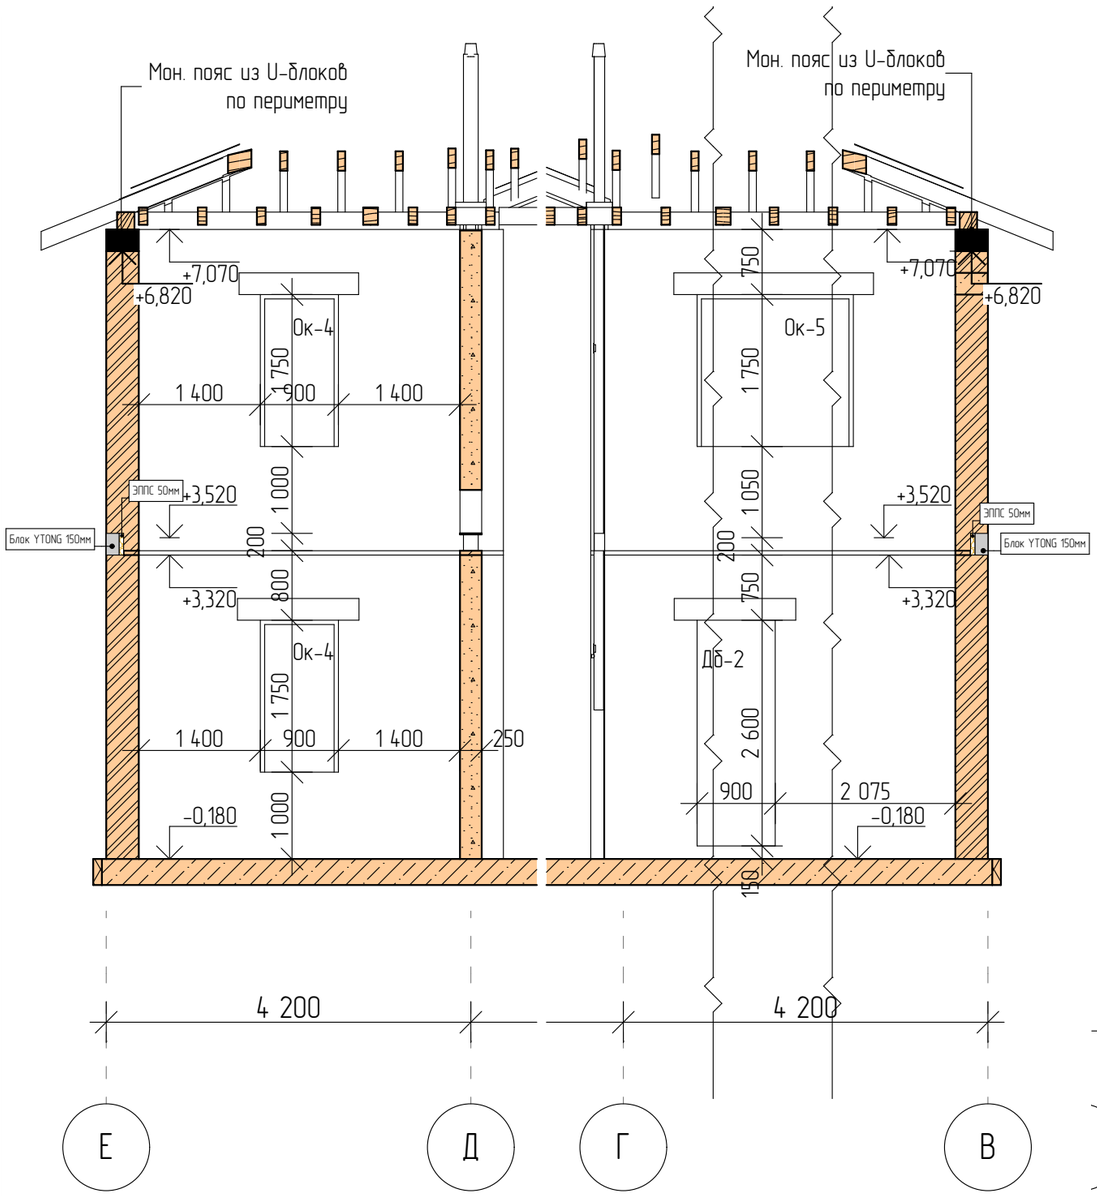

Развертка по стене 7

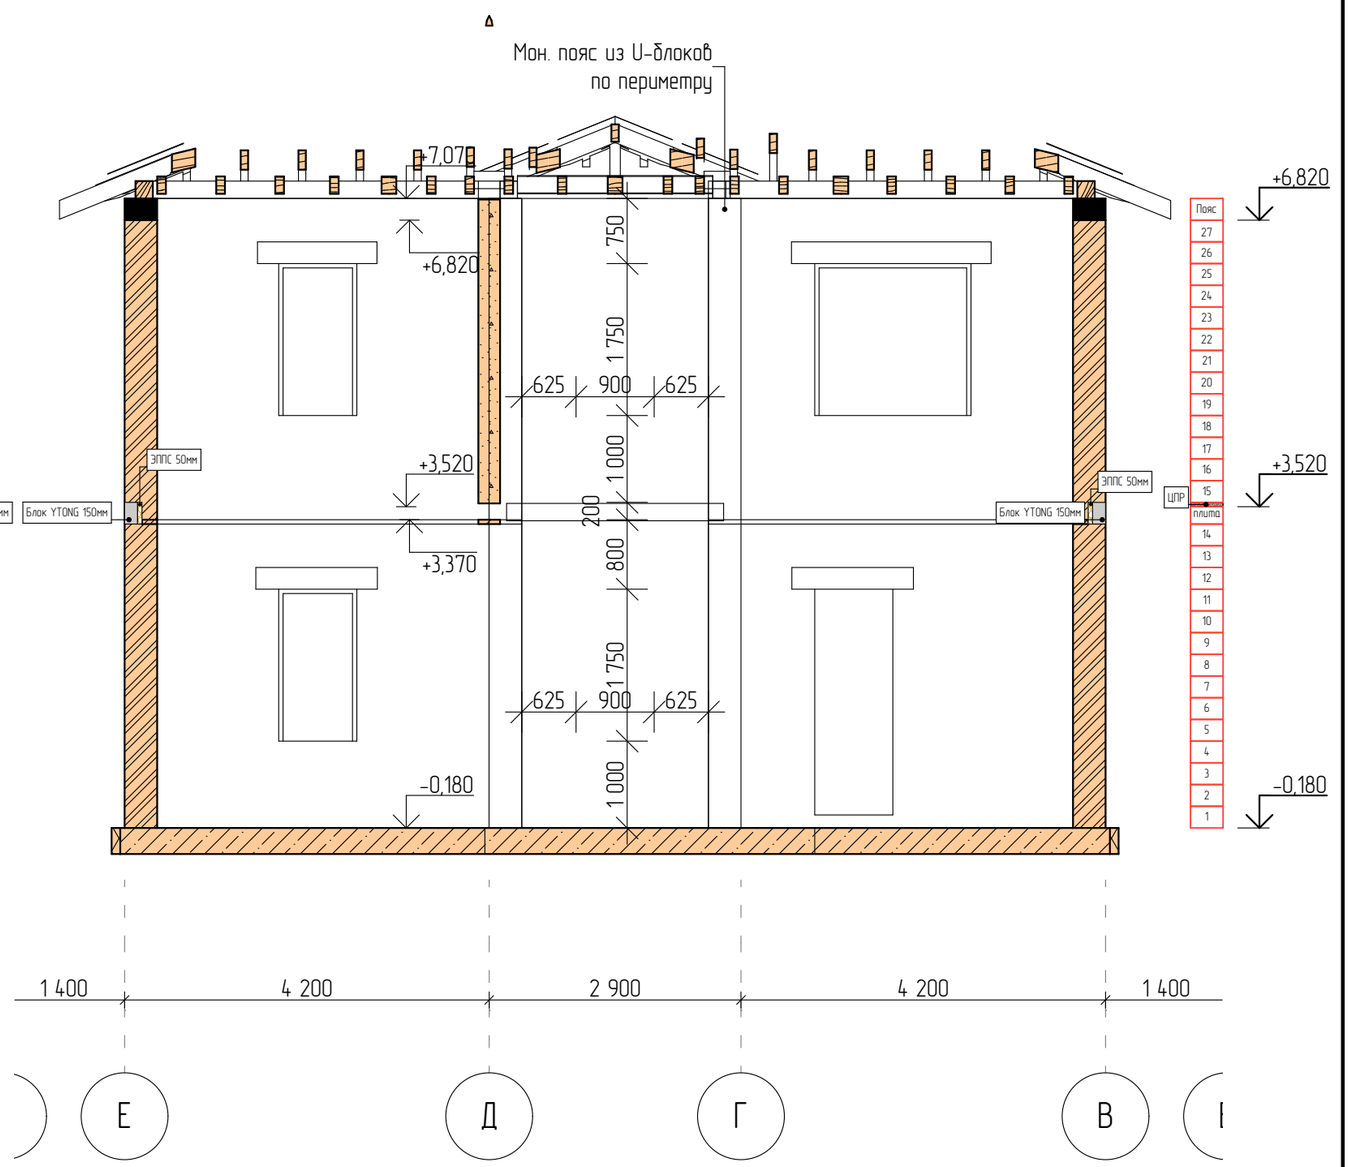

Примечание:
1) Модуль высоты кладки Ytong принят без учета шва и составляет 250 мм.
2) Первый ряд блоков укладывается на выравнивающий слой ЦПР
3) Кладка должна вестись на рстворе для тонкошовной кладки столщиной шва 1-3 мм. Кладку вести от торцов/углов к центру стены. Блоки укладывать с перевязкой, со смещением камней по отношению к нижнему ряду на 125 мм
4) Несущие наружные и внутренние стены связывать между собой кладкой при помощи перевязки на всю высоту стены.
5) Перегородки крепить к несущим стенам с помощью гибких связей.
6) Перемычки над проемами из U-блоков, если не указано иное. Опирание перемычки на стену не менее 250 мм

					2020			
Изм.	Кол.уч	Лист	№док.	Подпись	Дата			
Разработал		-				Индивидуальный жилой дом	стадия	лист	листов
Архитектор		Салыкова В.Г.					РД	5	
Заказчик						Развертки			

Согласовано

Взам. инв. №

Подпись и дата

Инв. № подл.


Согласовано


Взам. инв. №

Подпись и дата


Инв. № подл.

Развертка по стене А

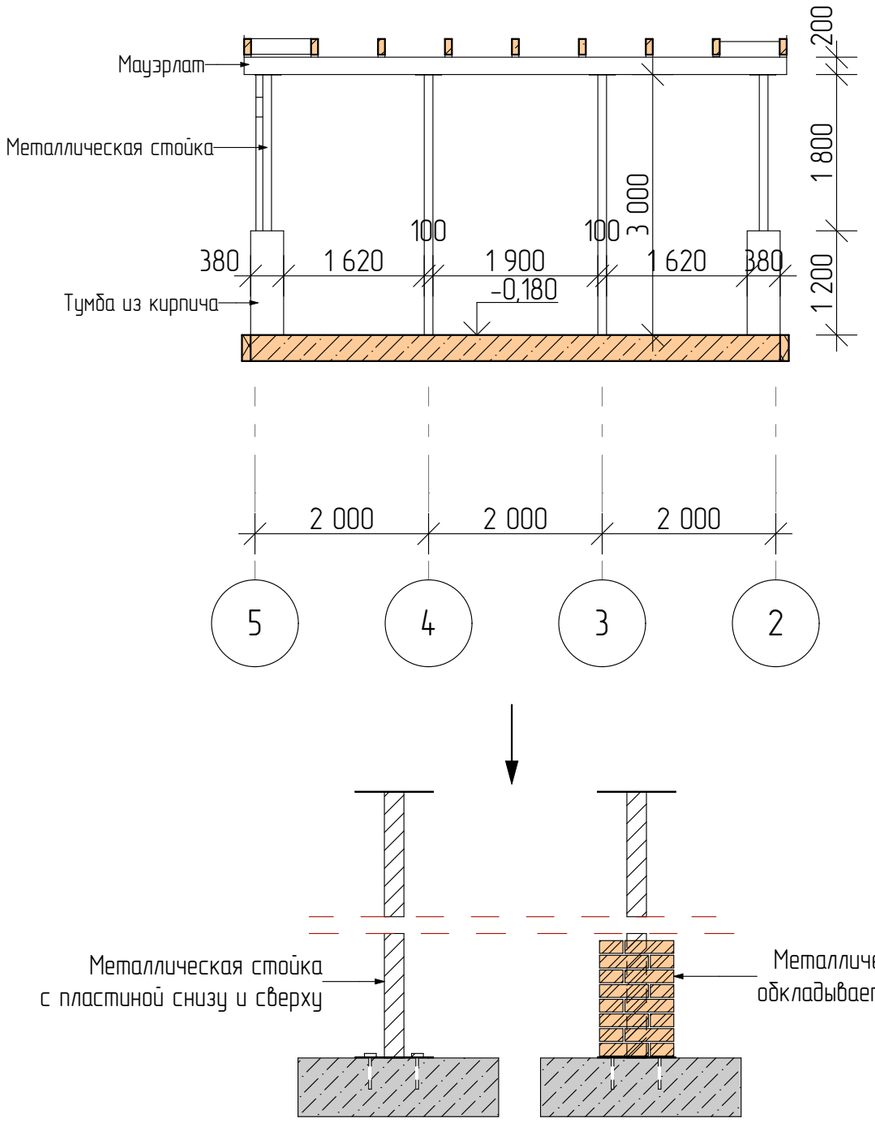

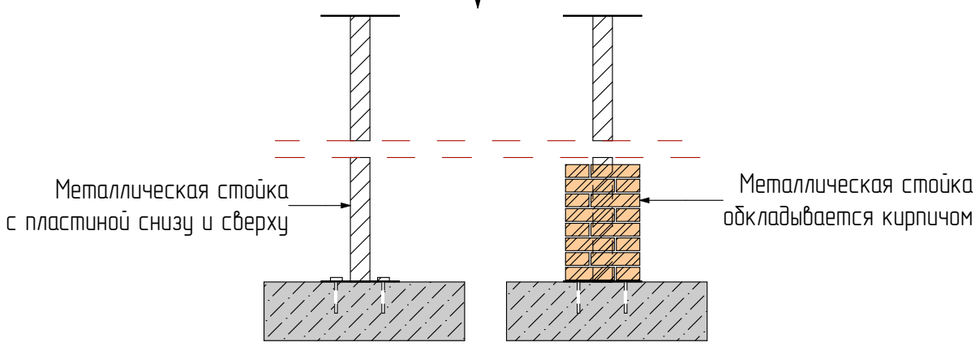

Развертка по стене Б

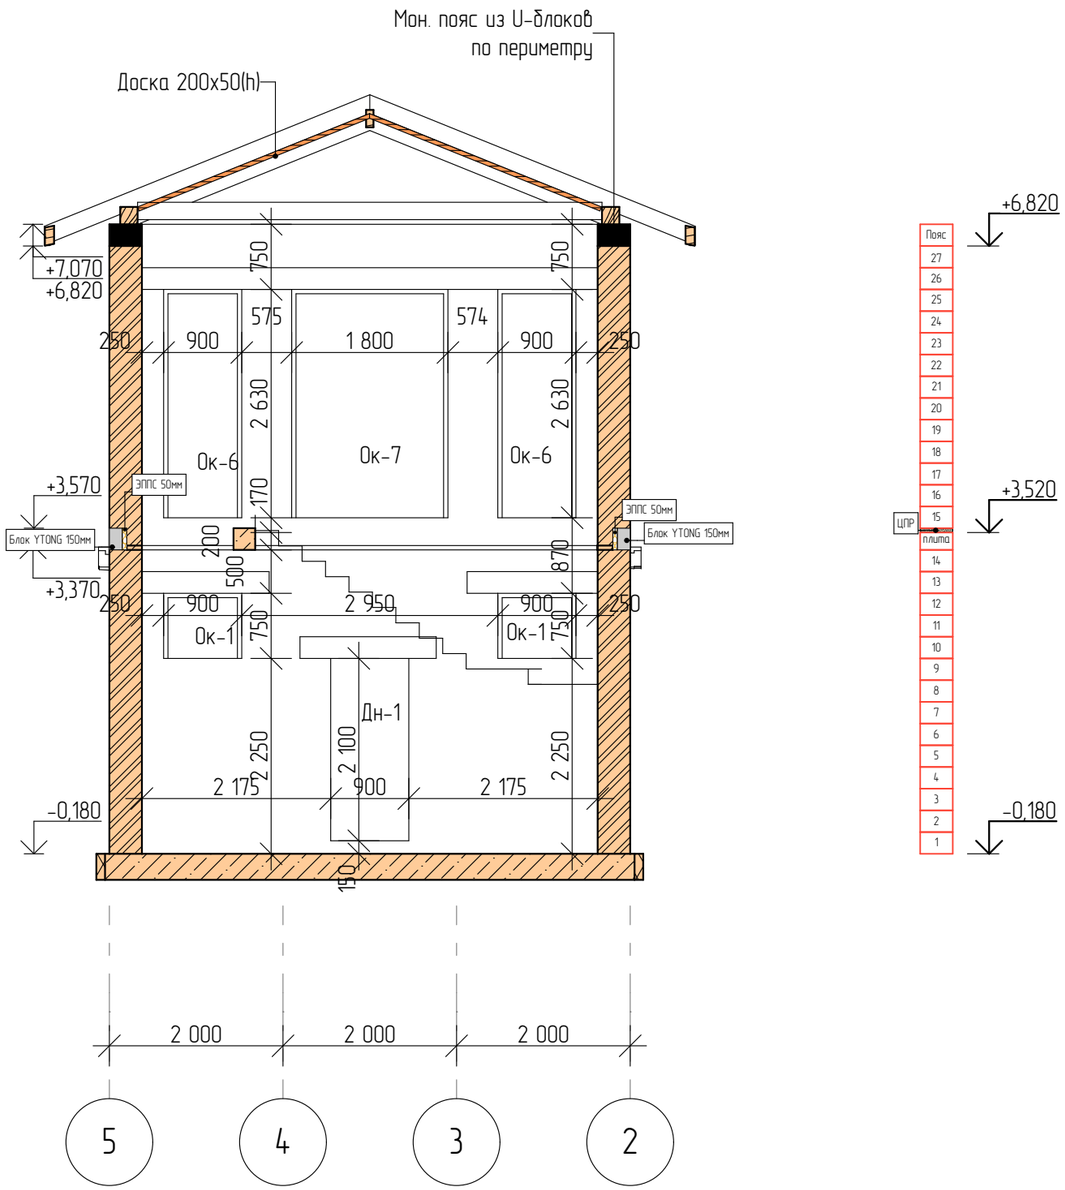

Примечание:


1) Модуль высоты кладки Ytong принят без учета шва и составляет 250 мм.
2) Первый ряд блоков укладывается на выравнивающий слой ЦПР
3) Кладка должна вестись на растворе для тонкошовной кладки столщиной шва 1-3 мм. Кладку вести от торцов/углов к центру стены. Блоки укладывать с перевязкой, со смещением камней по отношению к нижнему ряду на 125 мм
4) Несущие наружные и внутренние стены связывать между собой кладкой при помощи перевязки на всю высоту стены.
5) Перегородки крепить к несущим стенам с помощью гибких связей.
6) Перемычки над проемами из U-блоков, если не указано иное. Опирание перемычки на стену не менее 250 мм

					2020			
Изм.	Кол.уч	Лист	№док.	Подпись	Дата			
Разработал		–				Индивидуальный жилой дом	стадия	лист	листов
							РД	6	
Архитектор		Салыкова В.Г.							
Заказчик						Развертки			


Согласовано:

Инв. № подл. | Подпись и дата | Взам. инв. №

Развертка по стене В

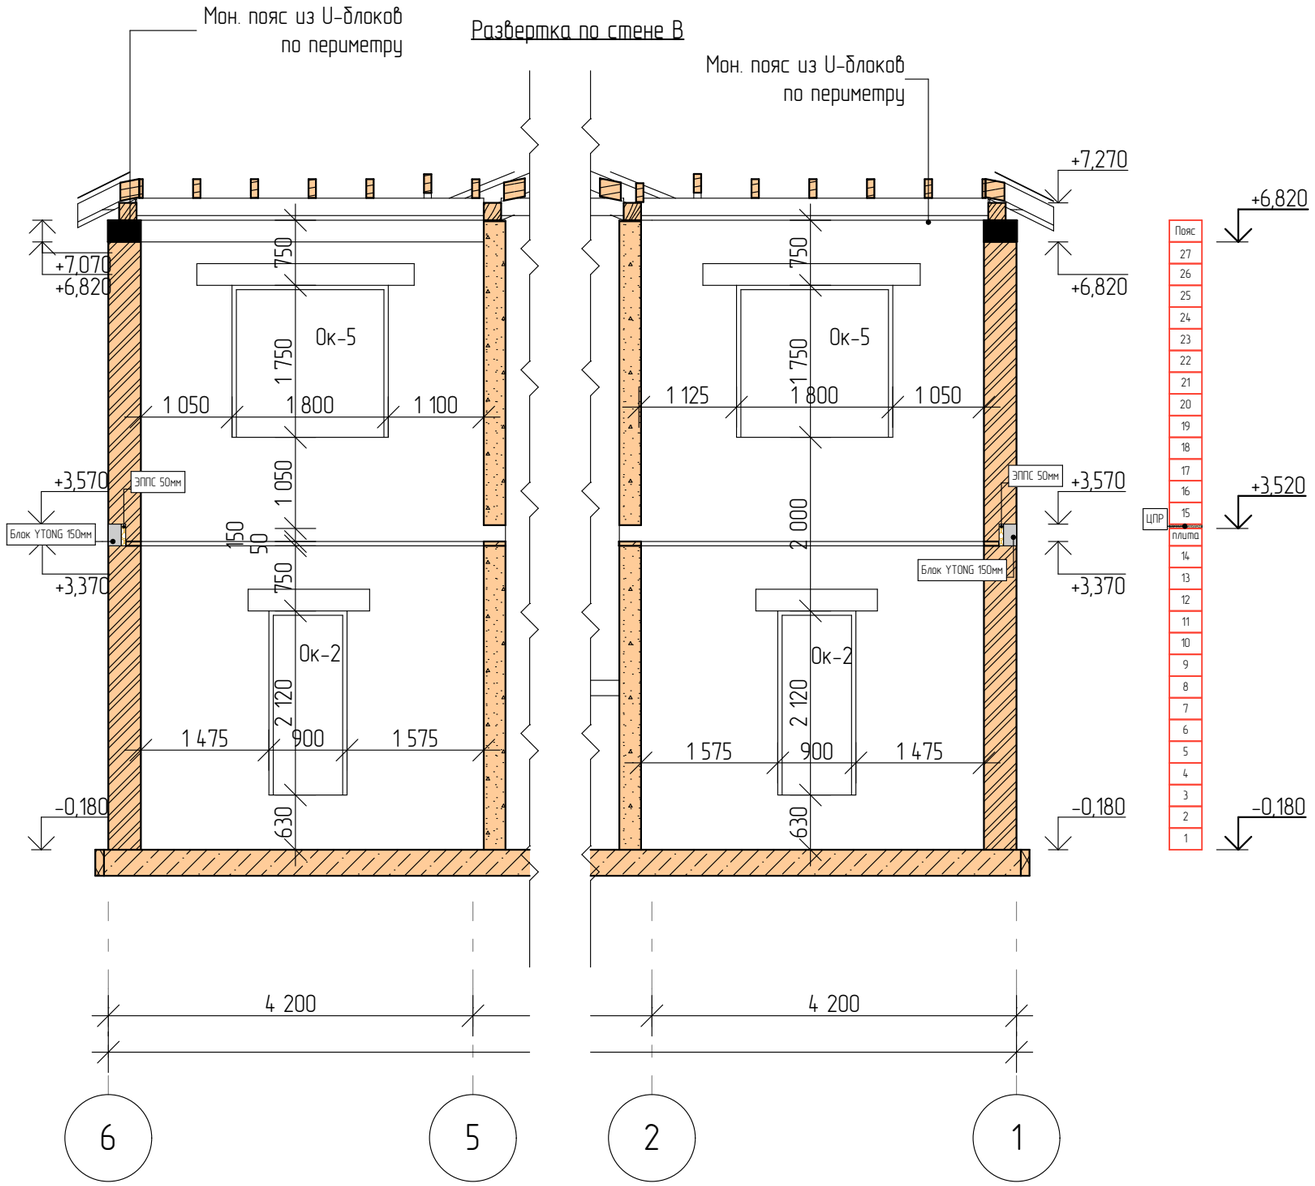


Развертка по стене Г

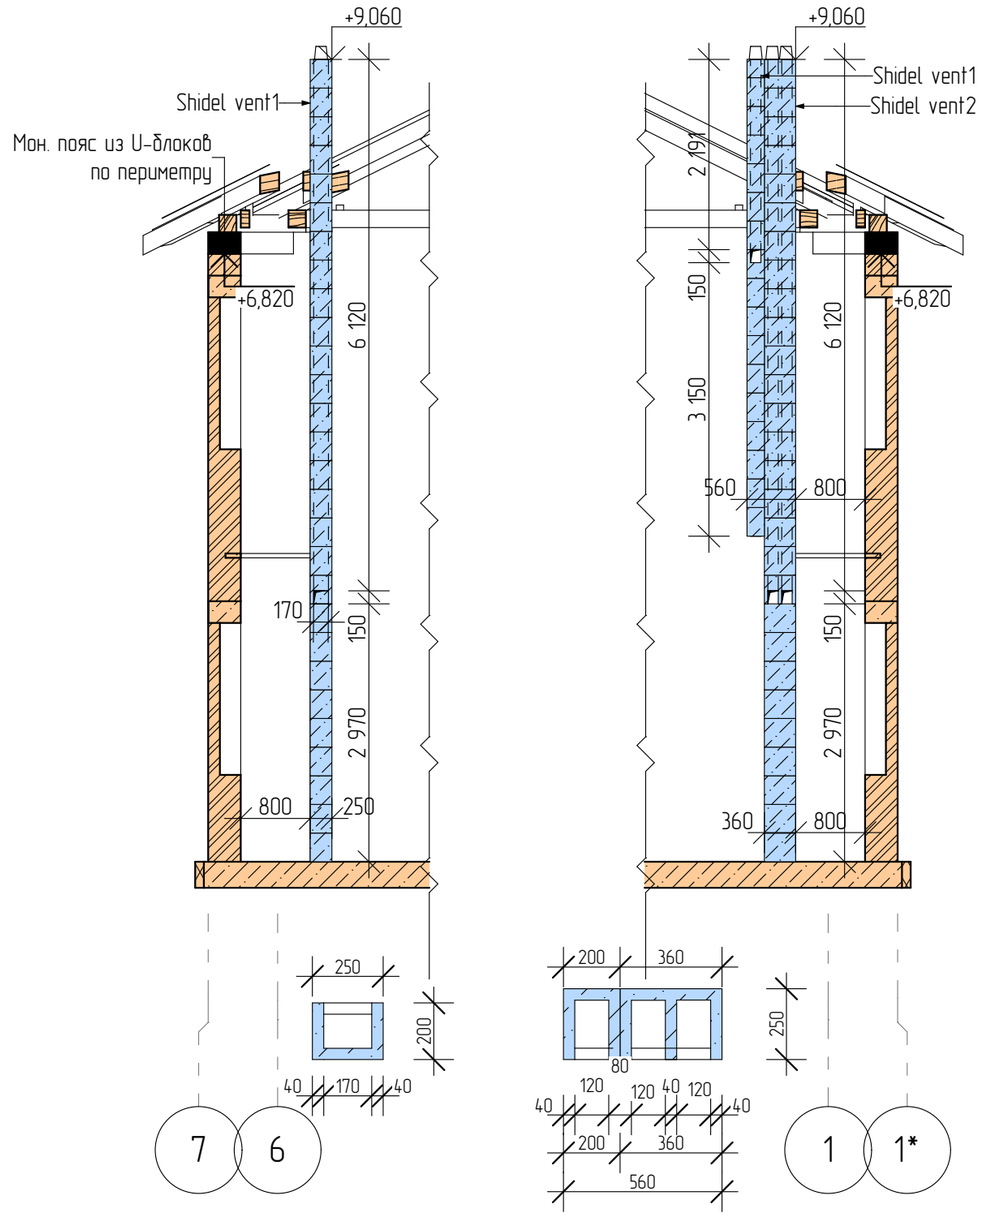


					2020	
Изм.	Кол.уч	Лист	№док.	Подпись	Дата	
Разработал		–				Индивидуальный жилой дом
Архитектор		Салыкова В.Г.				
Заказчик						Развертки


стадия	лист	листов
РД	7	

Развертка по стене Д

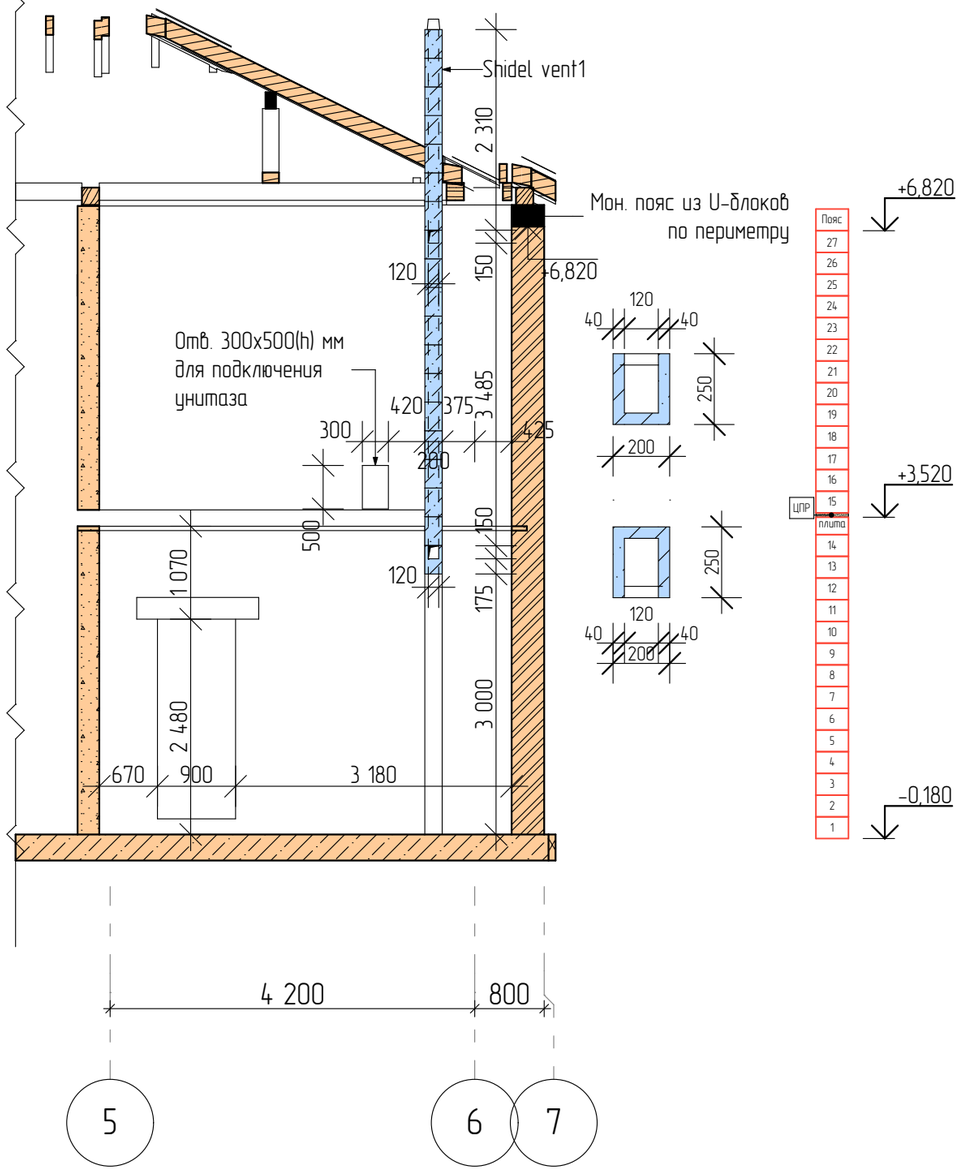

Развертка по стене Е

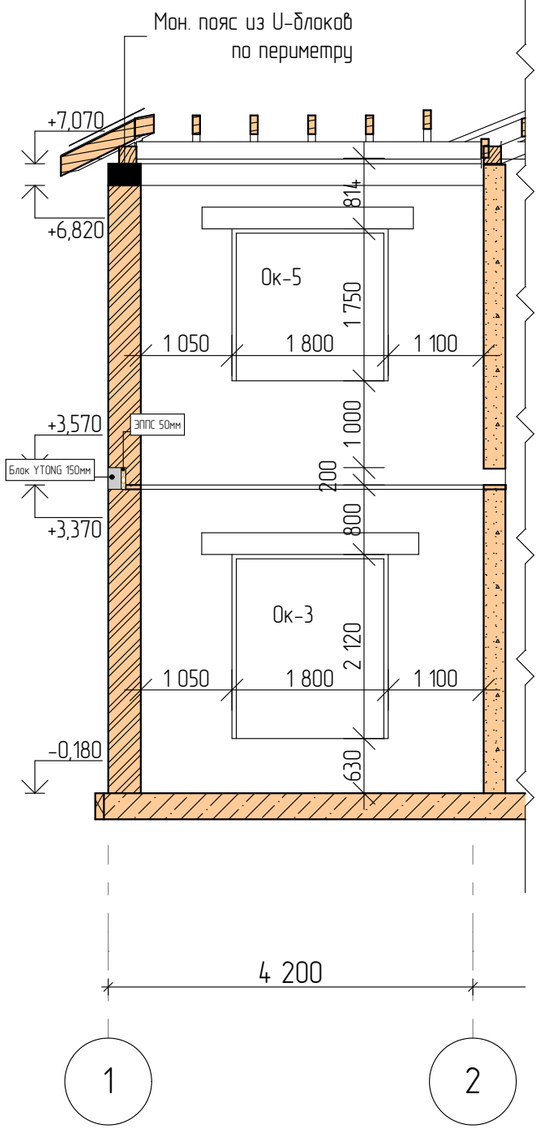

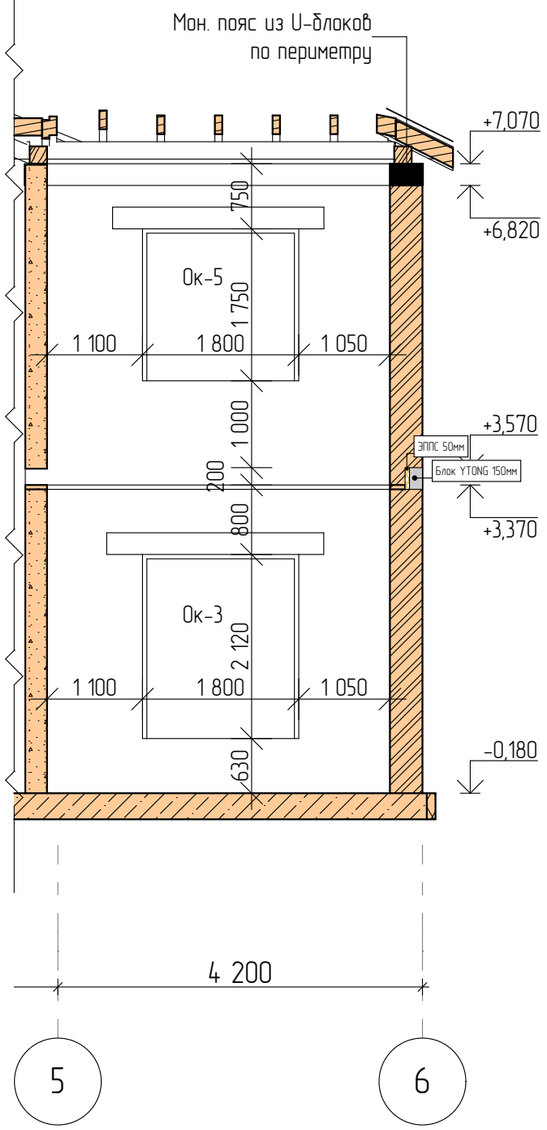


Примечание:
1) Модуль высоты кладки Ytong принят без учета шва и составляет 250 мм.
2) Первый ряд блоков укладывается на выравнивающий слой ЦПР
3) Кладка должна вестись на ртворе для тонкошовной кладки столщиной шва 1-3 мм. Кладку вести от торцов/углов к центру стены. Блоки укладывать с перевязкой, со смещением камней по отношению к нижнему ряду на 125 мм
4) Несущие наружные и внутренние стены связывать между собой кладкой при помощи перевязки на всю высоту стены.
5) Перегородки крепить к несущим стенам с помощью гибких связей.
6) Перемычки над проемами из U-блоков, если не указано иное. Опирание перемычки на стену не менее 250 мм


					2020			
Изм.	Кол.уч	Лист	№док.	Подпись	Дата			
Разработал		–				Индивидуальный жилой дом	стадия	лист	листов
Архитектор		Салыкова В.Г.					РД	8	
Заказчик						Развертки			

Согласовано:
Взам. инв. №
Подпись и дата
Инв. № подл.

Развертка по стене Ж

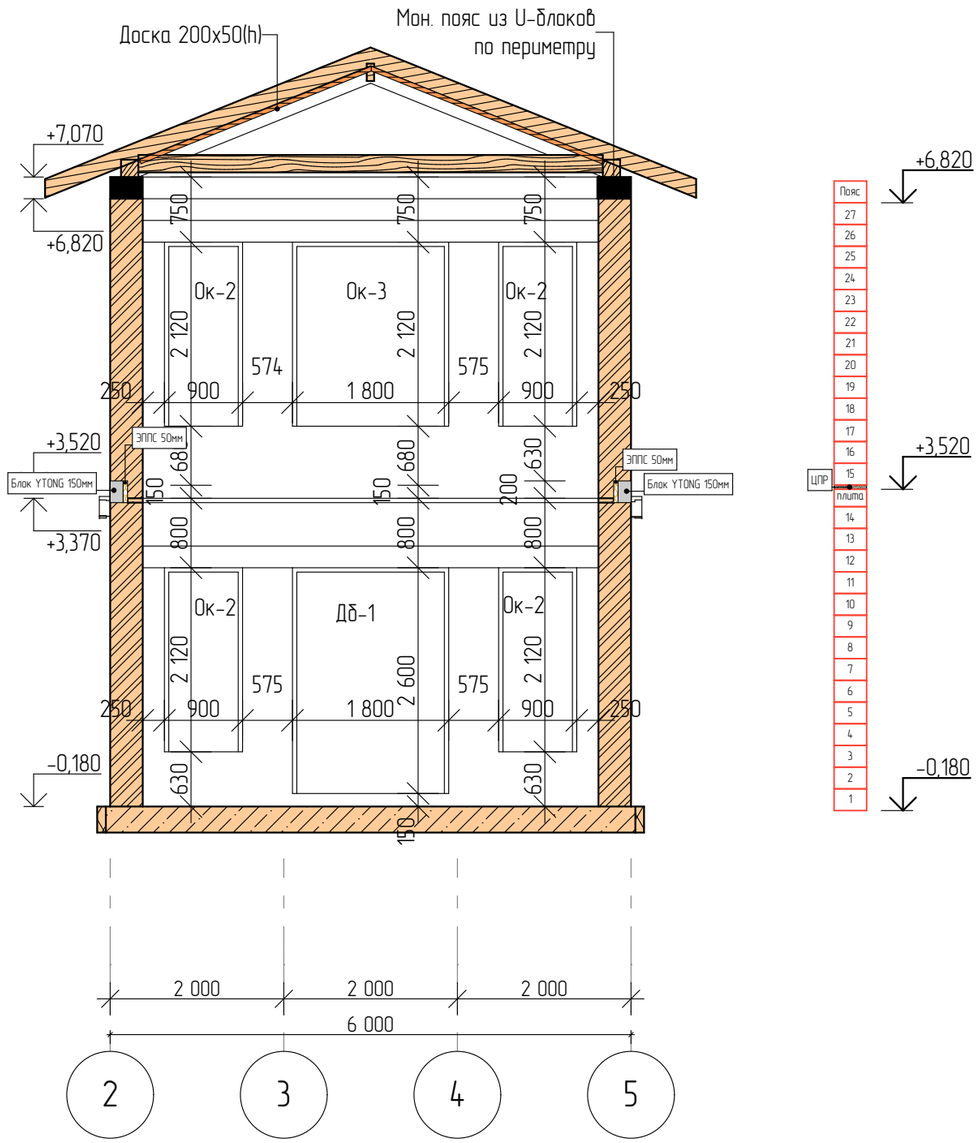

Развертка по стене И

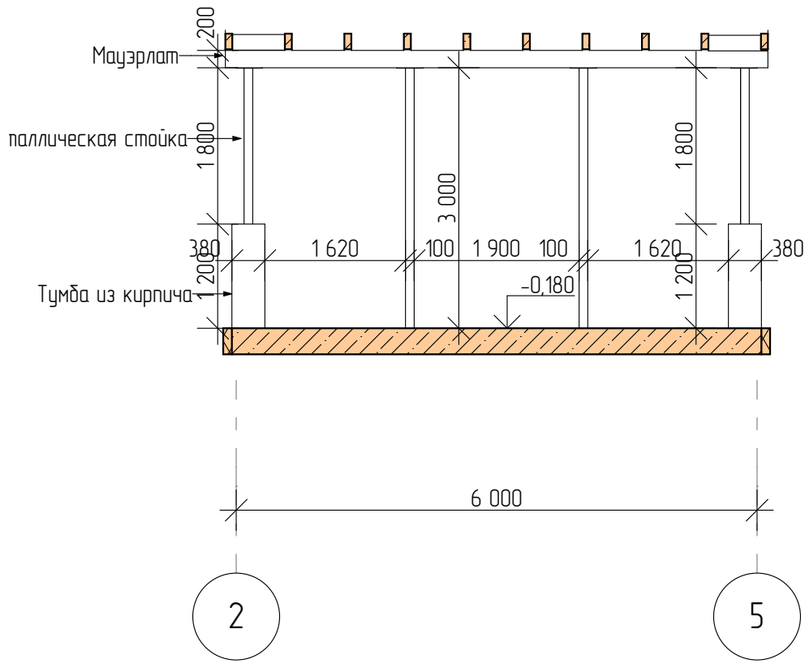

Примечание:

1) Модуль высоты кладки Ytong принят без учета шва и составляет 250 мм.
2) Первый ряд блоков укладывается на выравнивающий слой ЦПР
3) Кладка должна вестись на ртворе для тонкошовной кладки столщиной шва 1-3 мм. Кладку вести от торцов/углов к центру стены. Блоки укладывать с перевязкой, со смещением камней по отношению к нижнему ряду на 125 мм
4) Несущие наружные и внутренние стены связывать между собой кладкой при помощи перевязки на всю высоту стены.
5) Перегородки крепить к несущим стенам с помощью гибких связей.
6) Перемычки над проемами из U-блоков, если не указано иное. Опирание перемычки на стену не менее 250 мм


					2020			
Изм.	Кол.уч	Лист	№док.	Подпись	Дата			
Разработал		–				Индивидуальный жилой дом	стадия	лист	листов
							РД	9	
Архитектор		Салыкова В.Г.							
Заказчик						Развертки			


Согласовано:

Взам. инв. №

Подпись и дата

Инв. № подл.

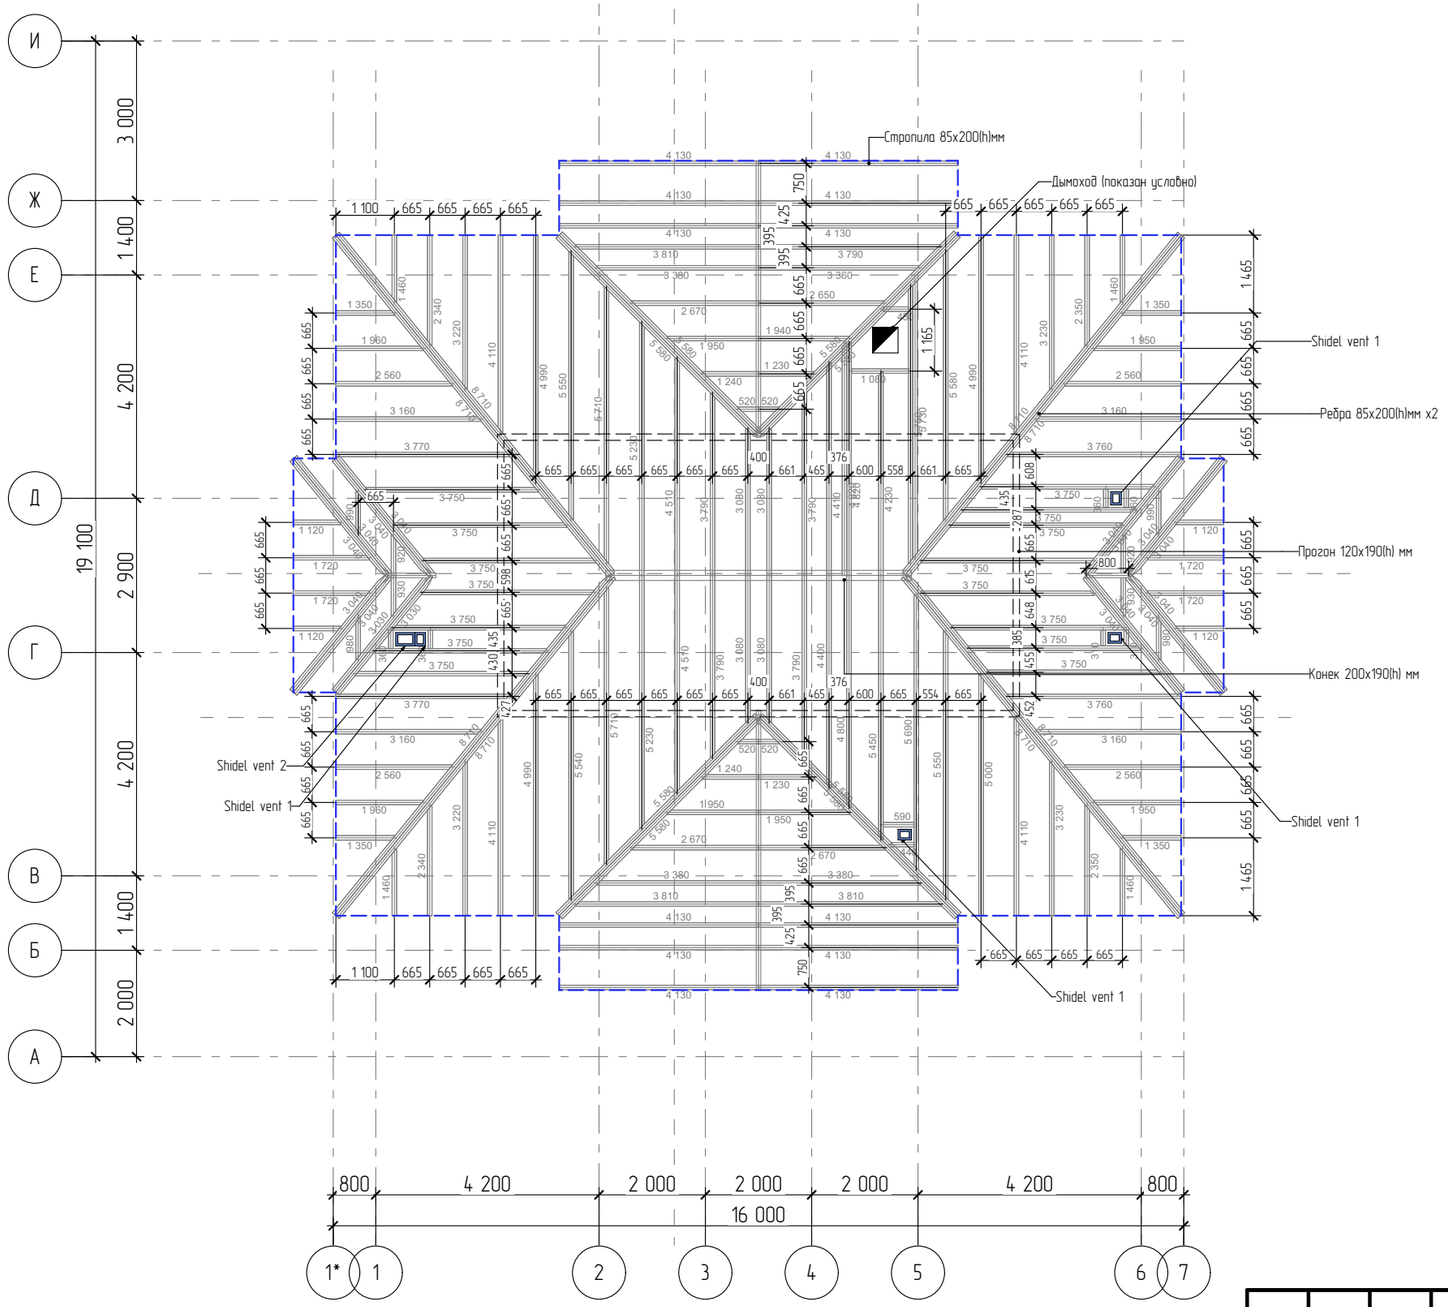

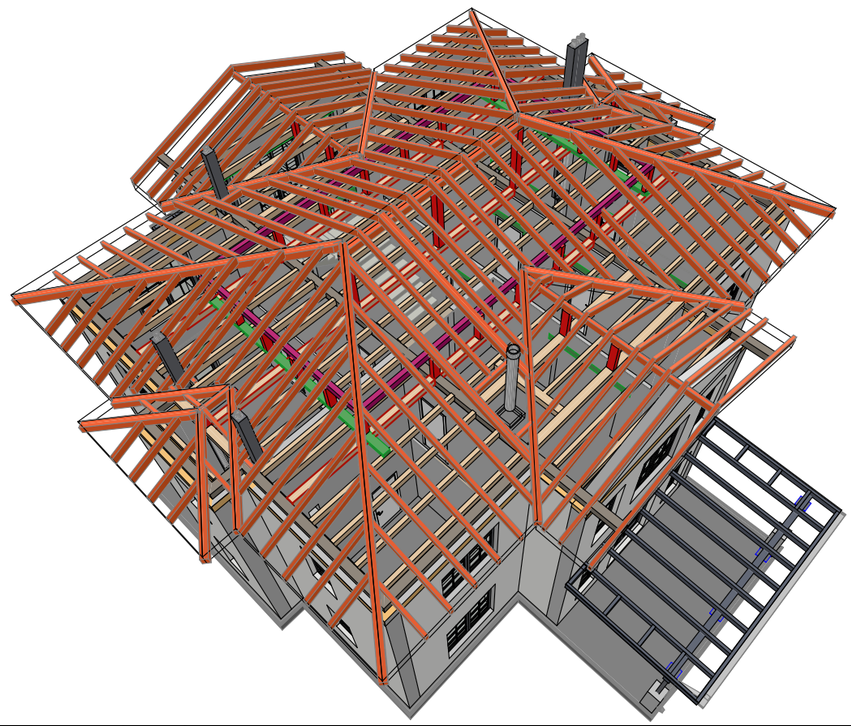

Примечание:
1) Шаг стропил 700 мм, если не указано иное

					2020		
Изм.	Кол.уч	Лист	№док.	Подпись	Дата		
Разработал		–				Индивидуальный жилой дом	стадия: РД; лист: 15; листов:
Архитектор		Салыкова В.Г.					
Заказчик						План стропил	

Согласовано:

Взам. инв. №

Подпись и дата

Инв. № подл.