Согласовано:

Взам. инв. №

Подпись и дата

Инв. № подл.

Ведомость чертежей

Лист	Наименование	Примечание
1	Общие данные	
2	Схема организации земельного участка М 1:400	
3	План 1 этажа с расстановкой мебели М 1:100	
4	План 2 этажа с расстановкой мебели М 1:100	
5	План 1 этажа с размерами М 1:100	
6	План 2 этажа с размерами М 1:100	
7	Спецификация заполнения оконных проёмов	
8	Разрезы М 1:100	
9	Фасады М 1:100	
10	Фасады М 1:100	
11	План фундамента М 1:100	
12	План ЖБ плиты с коммуникациями М 1:100	
13	План плиты межэтажного перекрытия М 1:100	
14	План чердачного перекрытия М 1:100	
15	План стропил	
16	План кровли М 1:100	

Проект разработан на основании техзадания, предоставленного заказчиком, соответствует установленным общегосударственным нормам и требованиям малоэтажному строительству в соответствии со СП 55.13330.2011 "Дома жилые одноквартирные". Актуализированная редакция СНиП 31-02-2001; СП 131.13330.2012 "Строительная климатология", ГОСТ 21.501-2011 "Система проектной документации для строительства. Правила выполнения рабочей документации архитектурных и конструктивных решений". СП 63.13330.2012 «Бетонные и железобетонные конструкции», ГОСТ 31360-2007 "Изделия стеновые неармированные из ячеистого бетона автоклавного твердения", ГОСТ 31359-2007 "Бетоны ячеистые автоклавного твердения"

Характеристика проектируемого объекта:

Этажность - 2 этажа

Строительно-климатический район и характеристики условий смотреть в соответствии со СНИП 23-01-99.

Данные о фактических размерах участка, габаритов его границ, наличие заборов, крупных растений, близость соседских построек, различных ограничений, схемы с точной привязкой их расположения на территории участка предоставляет заказчик. Точность вышеописанных сведений лежит на Заказчике. Подрядчиком не проводятся работы по межеванию и он основывается на данных, предоставленных Заказчиком.

Архитектурно-планировочные решения:

Объект строительсва-жилой дом

За отм. 0,000 принята отм. чистого пола

Покрытие кровли - согласно смете.

Водосточная система - согласно смете.

Окна и двери-индивидуального изготовления.

Конструктивные решения:

Фундамент-плитный.

Наружние несущие стены - из газобетонных блоков Ytong, толщ. 375 мм D500

Внутренние несущие стены -из газобетонных блоков Ytong, толщ. 250 мм D500

Перегородки-из газобетонных блоков Ytong, толщ. 150 мм/100 мм

Проемы- перемычки из U-образных блоков/монолитные ж/б

Обязательно выполнение работ по водоотведению - дренажных работ с монтажом смотровых колодцев, отмостки и других работ, направленных на отведение воды от пятна застройки. Выполняется в объеме, определенном сметой. Гарантия на фундаментные работы осуществляется только при условии надлежащей системы водоотведения и ее эксплуатации.

Указания по устройству стен:

Модуль высоты кладки Ytong составляет 250 мм без учета толщины шва.

Первый ряд блоков укладывается на выравнивающий слой .

Кладка должна вестись на рстворе с толщиной шва 1-3 мм

Кладку вести от торцов/углов к центру стены.

Блоки укладывать с перевязкой, со смещением камней по отношению к нижнему ряду на 125 мм

Несущие наружные и внутренние стены связывать между собой кладкой при помощи перевязки на всю высоту стены.

Материалы, технология работ и способы исполнения, гарантийные обязательства, способы эксплуатации и другое, связанное с использованием строения, а также его монтажом регулируется ТУ 16.23.19-001-17010764-2018

Подписанием настоящего проектного решения Заказчик подтверждает, что Подрядчик без согласований и уведомлений может изменять, дополнять конструктивные решения строения по своему усмотрению в целях конструктивной надежности здания.

ТЕХНИКО-ЭКОНОМИЧЕСКИЕ ПОКАЗАТЕЛИ:

Наименование	Ед.изм.	Количество
Площадь застройки	$м^2$	222
Площадь общая	$м^2$	333
Площадь жилая	$м^2$	128

*Площадь помещений указана без учета отделочных материалов и понижающего коэффициента

					2020			
Изм.	Кол.уч	Лист	№док.	Подпись	Дата			
Разработал		–				Индивидуальный жилой дом	стадия	лист	листов
							РД	1	
Архитектор		Салыкова В.Г.							
Заказчик						Общие данные			

Инсоляция по временам года


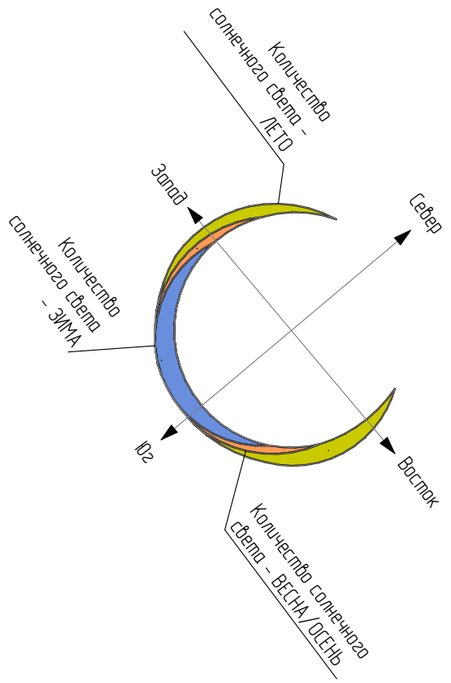


Схема участка
М=1:400

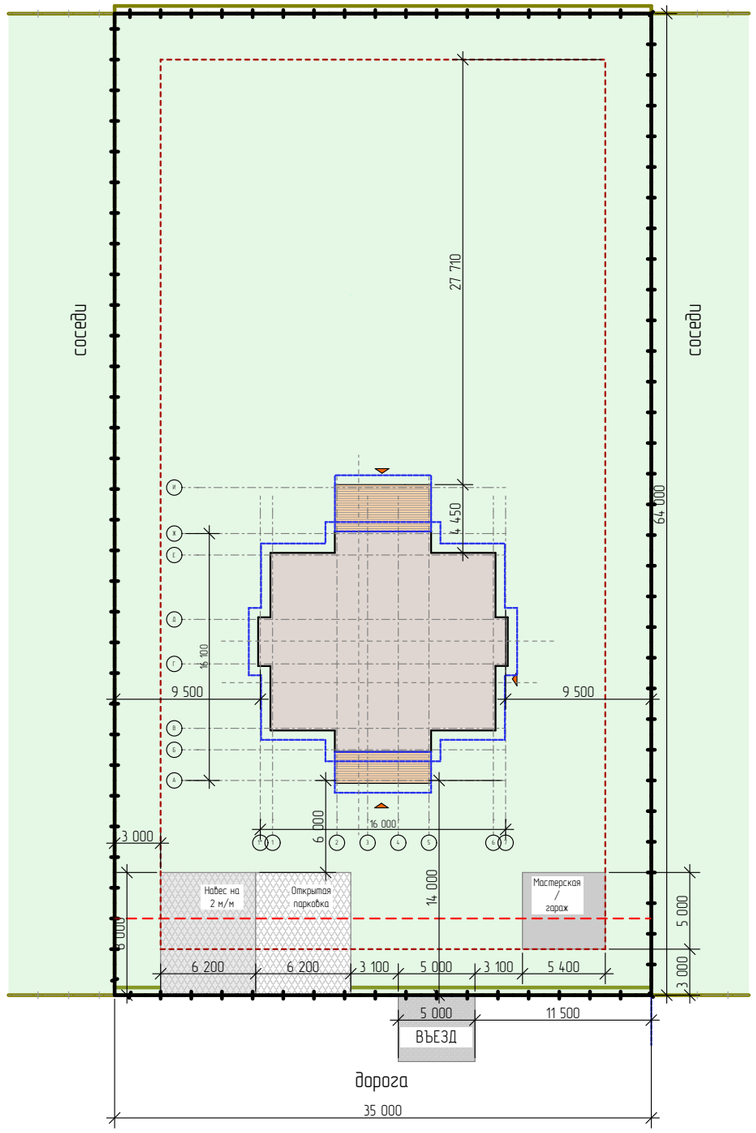

Условные обозначения:

- Проектируемое здание
- Терраса/крыльцо
- Вход
- Контур кровли
- Зона отступа от края участка (красной линии улицы) = 5,0 м
- Зона отступа от края участка = 3,0 м
- Граница участка

Ситуационный план



Примечание:
1) Расположение дома показано от забора до конструктивных осей.
2) Привязка показана условно. Скорректировать по месту.
3) При расположении дома учитывать требования по противопожарным расстояниям между строениями на соседних участках в соответствии с СП 53.13330.2011
4) Монтаж и расположение наружных сетей согласовывается с инженером по месту.


					2020			
Изм.	Кол.уч	Лист	№док.	Подпись	Дата			
Разработал		-				Индивидуальный жилой дом	стадия	лист	листов
Архитектор		Салыкова В.Г.					РД	2	
Заказчик						Схема организации земельного участка М 1:400			

Согласовано

Взам. инв. №

Подпись и дата

Инв. № подл.

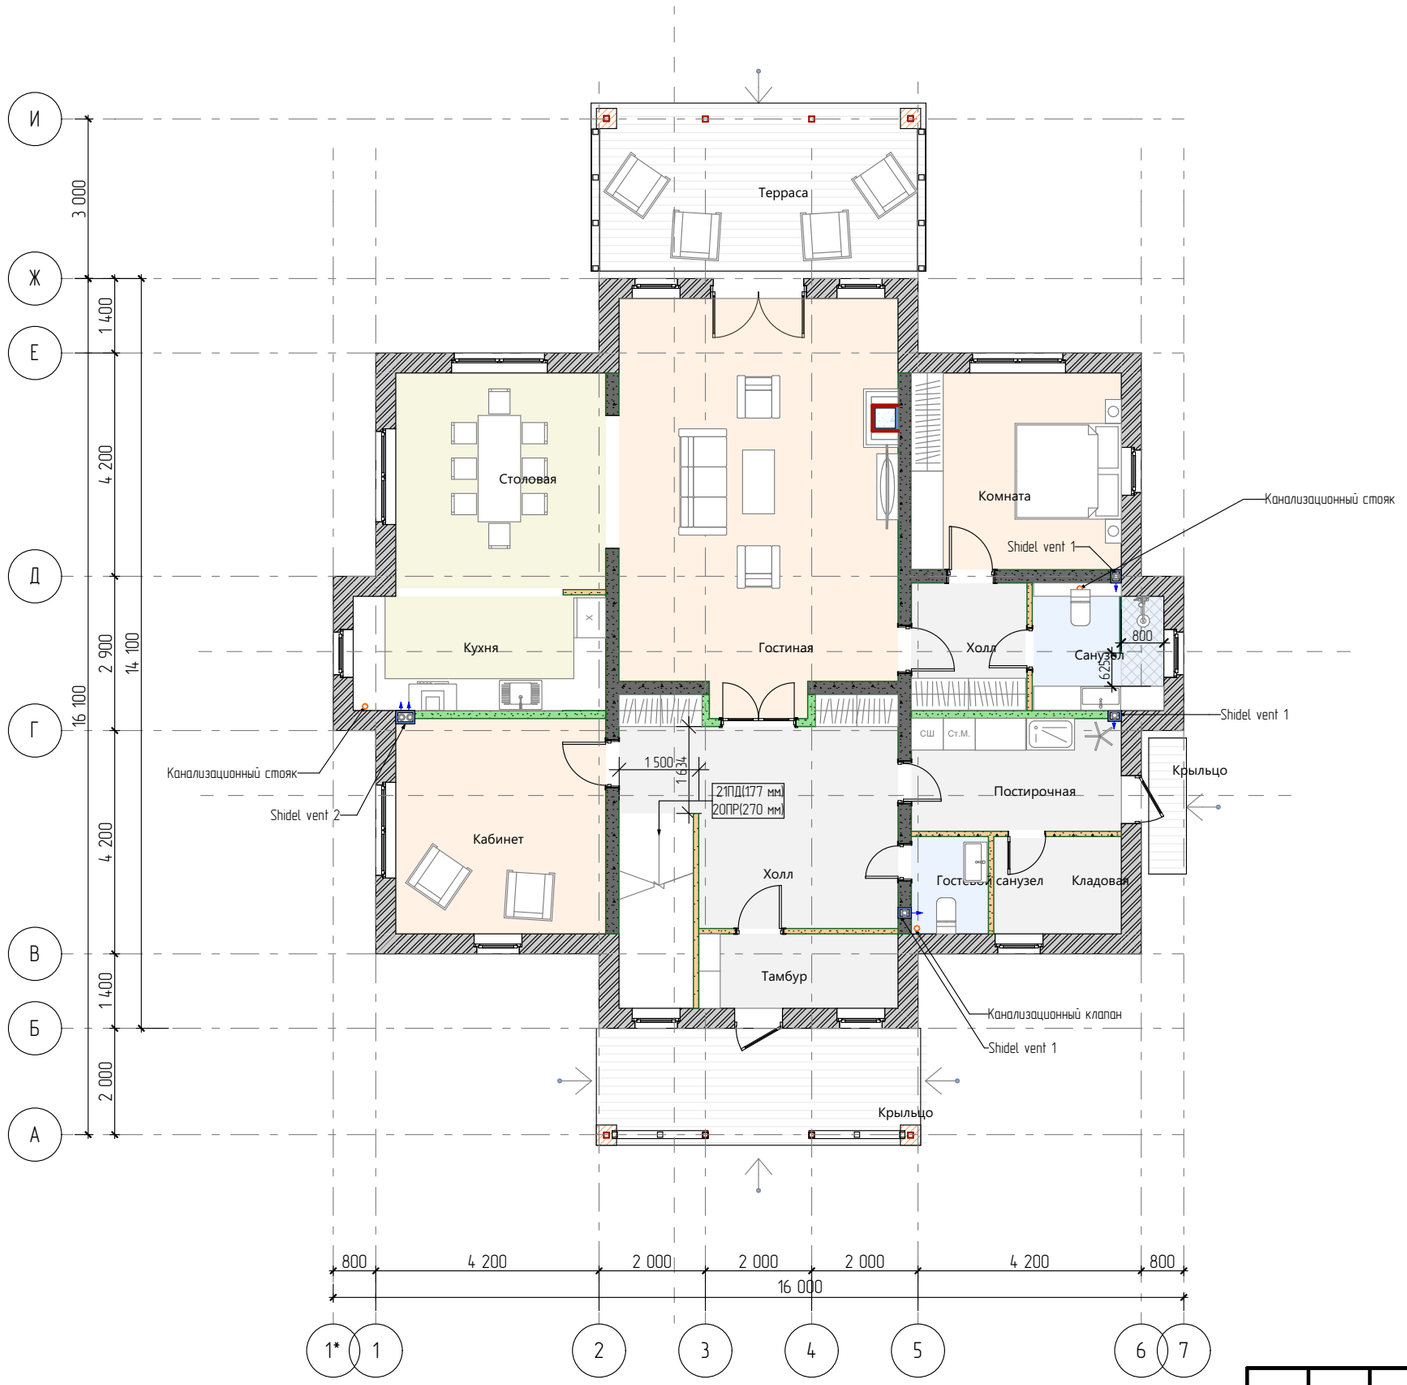

Примечание:
1) Вся показанная мебель, а также назначение комнат носят условный характер
2) Расположение сантехнических приборов не подлежит перемещению.
Закладные в железобетонной плите перекрытия устанавливаются в соответствии с расположением сантехнических приборов во время заливки жб плиты.
3) Площадь помещений показана без учета отделочных материалов и понижающего коэффициента по периметру пола.
4) Нагрузка от камина и дымохода вместе с отделкой не должна превышать 1500 кг/м2.
5) Вентиляция помещений приточно-вытяжная естественная. Поступление наружного воздуха осуществляется через открывающиеся створки окон. Вытяжка-через вентиляционные каналы.

Экспликация помещений 1 этажа

Тип помещения	№ п/п	Наименование	Площадь, м
Внутренние помещения			
	2	Тамбур	5,24
	3	Холл	18,57
	4	Гостевой санузел	2,62
	5	Кабинет	16,00
	6	Кухня	10,21
	7	Столовая	16,00
	8	Гостиная	39,09
	9	Комната	14,62
	10	Холл	5,14
	11	Санузел	5,66
	12	Постирочная	8,31
	13	Кладовая	4,33
			145,79 м²
Крыльцо, терраса			
	1	Крыльцо	12,88
	14	Крыльцо	1,85
	16	Терраса	19,91
			34,64 м²
			180,43 м²

Согласовано:

Взам. инв. №

Подпись и дата

Инв. № подл.


Изм.	Кол.уч	Лист	№док.	Подпись	Дата
					2020

Разработал	–	
Архитектор	Салыкова В.Г.	
Заказчик		

Индивидуальный жилой дом

стадия	лист	листов
РД	3	

План 1 этажа с расстановкой мебели М 1:100

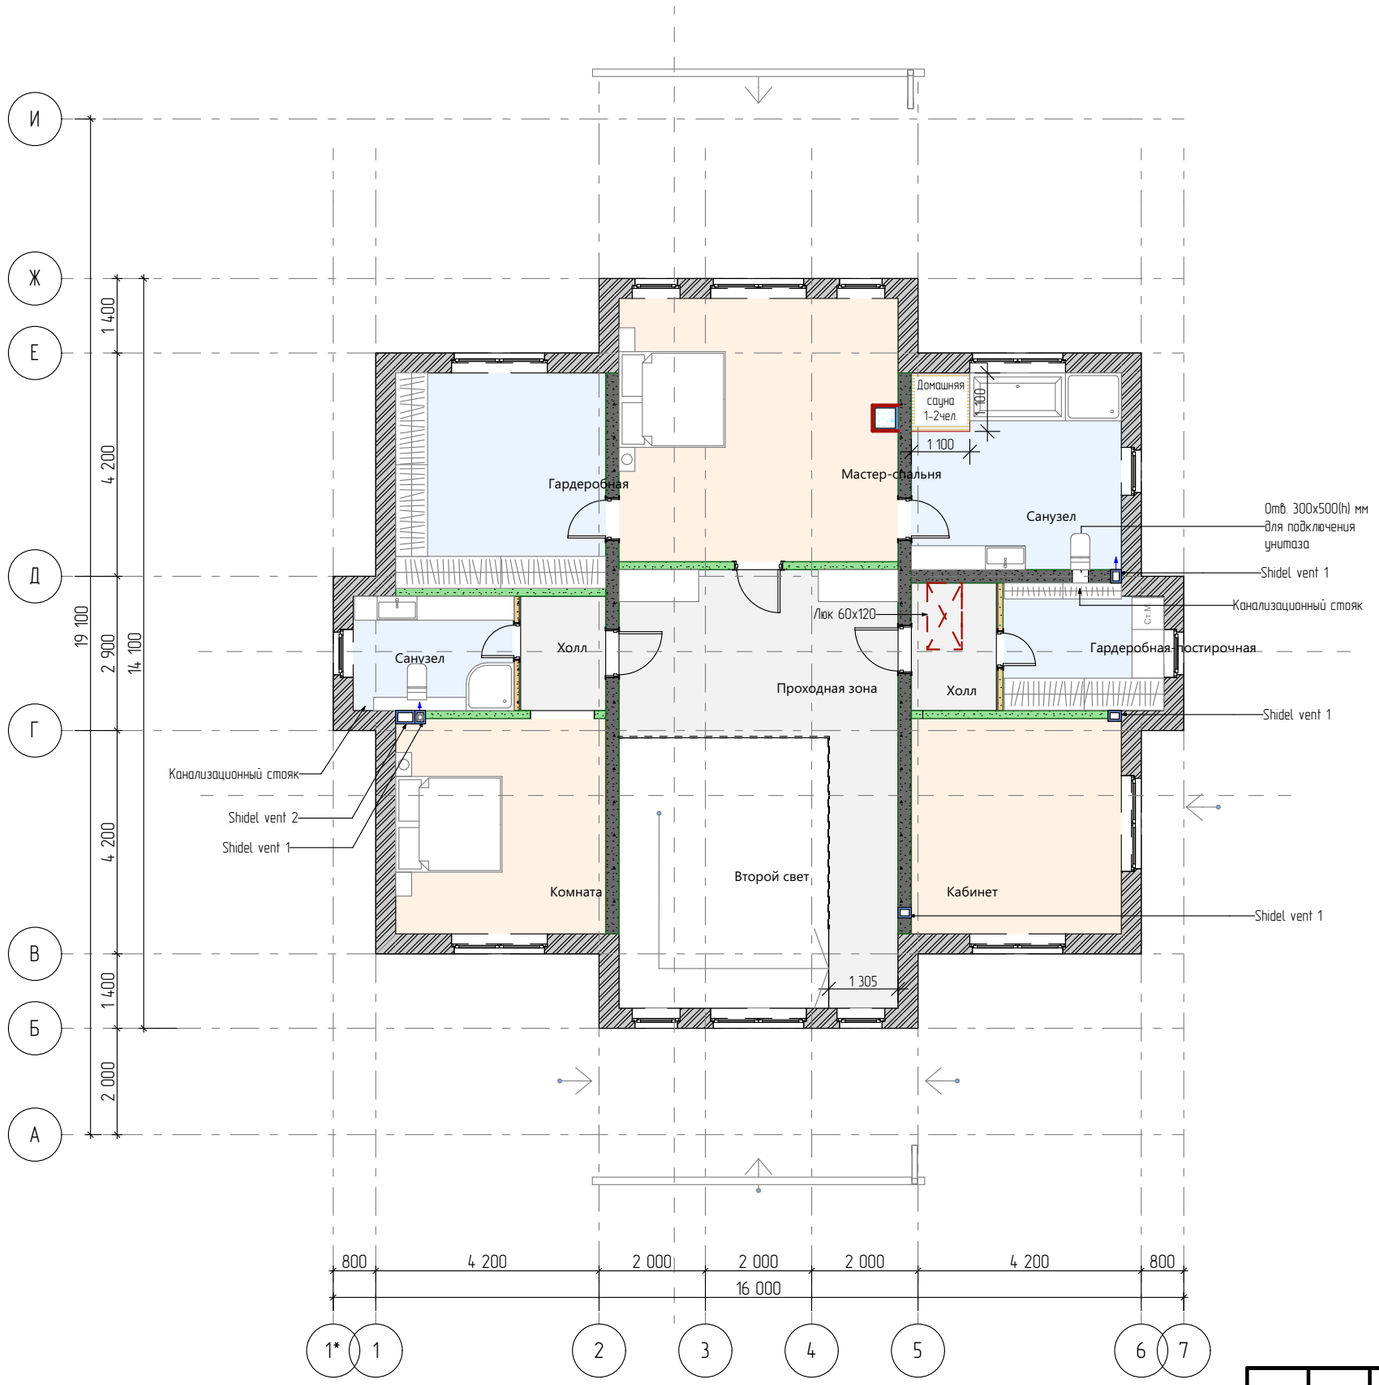

Экспликация помещений 2 этажа

Тип помещения	№ п/п	Наименование	Площадь, м
Внутренние помещения			
	1	Проходная зона	23,19
	1*	Второй свет	20,09
	2	Комната	16,00
	3	Холл	3,44
	4	Санузел	6,45
	5	Гардеробная	16,00
	6	Мастер-спальня	25,99
	7	Санузел	14,62
	8	Гардеробная-постирочная	7,00
	9	Холл	3,84
	10	Кабинет	16,00
			152,62 м²

Примечание:
1) Вся показанная мебель, а также назначение комнат носят условный характер
2) Расположение сантехнических приборов не подлежит перемещению.
Закладные в железобетонной плите перекрытия устанавливаются в соответствии с расположением сантехнических приборов во время заливки жб плиты.
3) Площадь помещений показана без учета отделочных материалов и понижающего коэффициента по периметру пола.
4) Нагрузка от камина и дымохода вместе с отделкой не должна превышать 1500 кг/м2.
5) Вентиляция помещений приточно-вытяжная естественная. Поступление наружного воздуха осуществляется через открывающиеся створки окон. Вытяжка-через вентиляционные каналы.

Изм.	Кол.уч	Лист	№док.	Подпись	Дата
					2020
Разработал		–			
Архитектор		Салыкова В.Г.			
Заказчик					

Индивидуальный жилой дом

стадия	лист	листов
РД	4	


План 2 этажа с расстановкой мебели М 1:100

Согласовано:

Взам. инв. №

Подпись и дата

Инв. № подл.

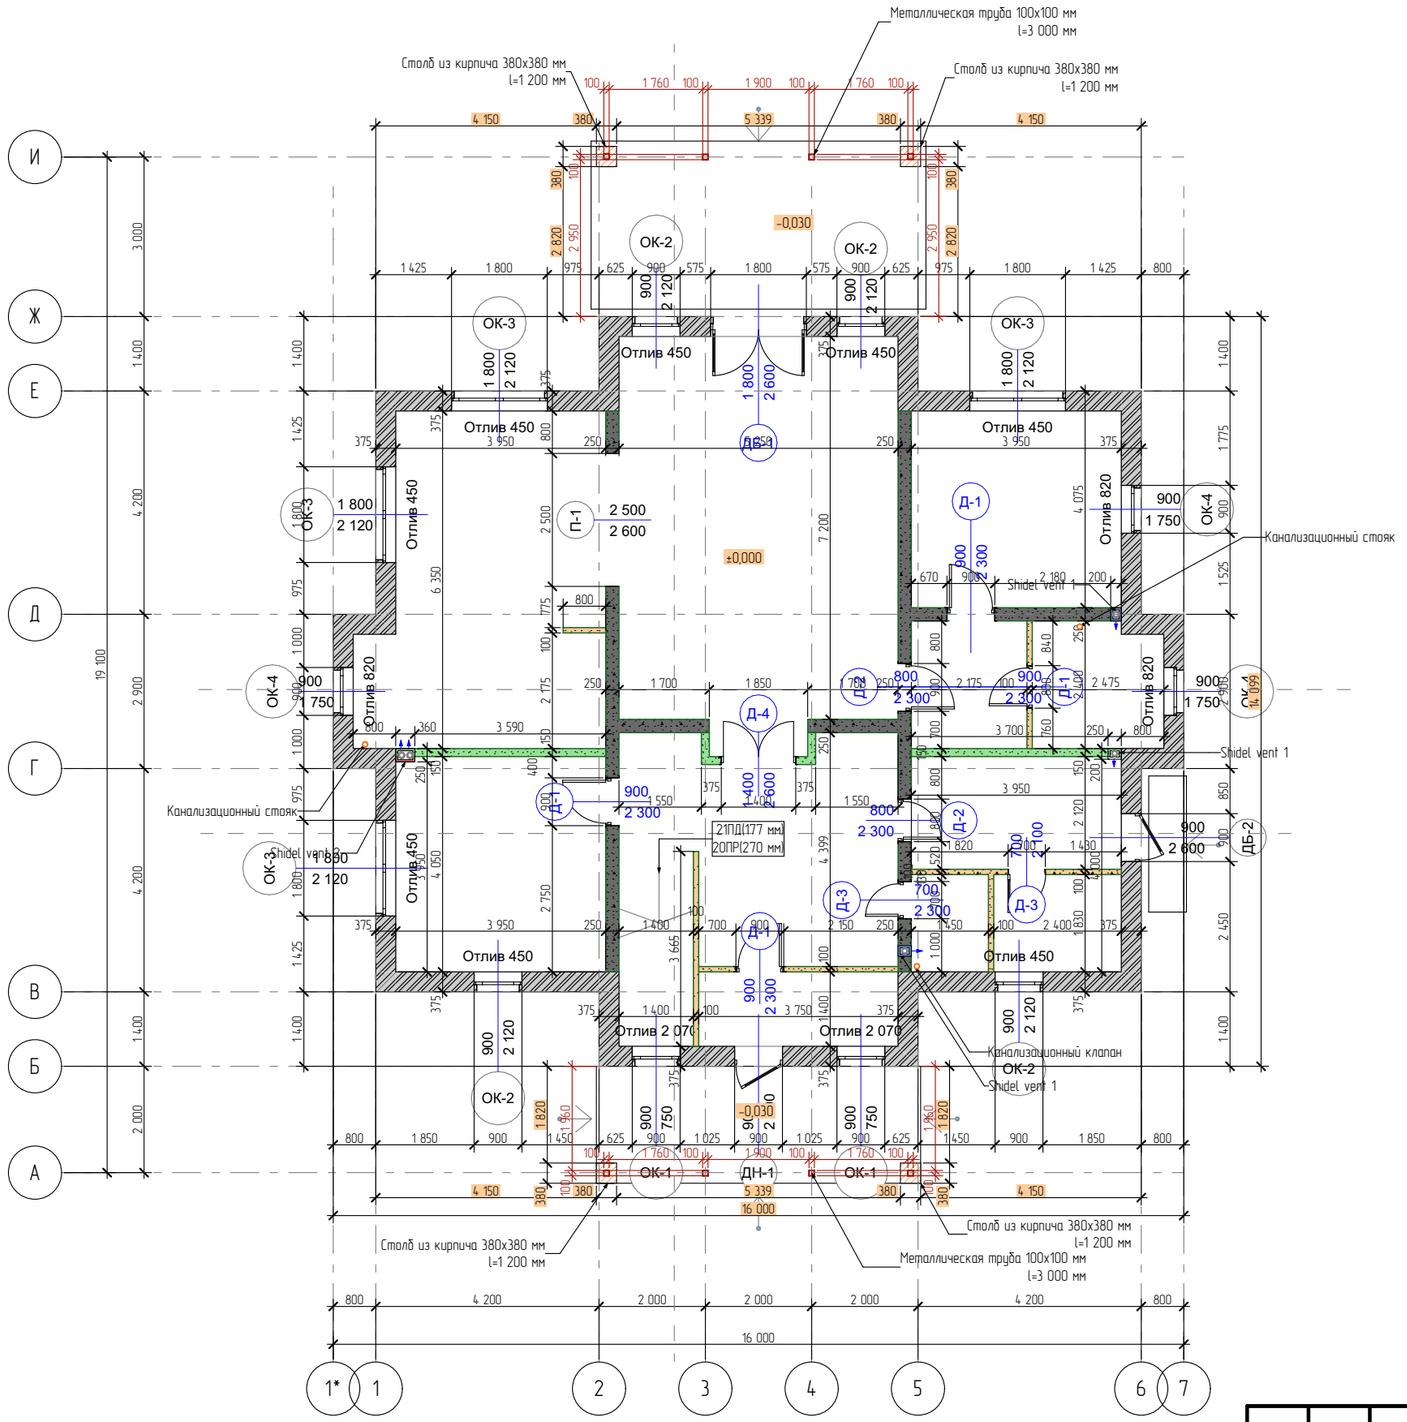

Условные обозначения

- Наружные несущие стены-блоки Ytong 375мм (указаны без отделки)
- Внутренние несущие стены-блоки Ytong 250 мм
- Перегородки-блоки Ytong 150 мм
- Перегородки-блоки Ytong 100 мм
- Столбы из кирпича 380х380 мм с металлической стойкой
- Металлическая стойка 100х100 мм
- ОК- Оконный проем
- Д- Дверной проем
- От.ч.п. Высота от чистого пола

Примечание:
1) За отметку +-0,000 принята отметка чистового пола первого этажа
2) Наружные размерные ципочки указаны по блокам без чистовой отделки
3) На планах этажей изображены маркеры, указывающие габариты проемов. Размеры изделий расчитываются индивидуально,в зависимости от способа установки и типа оконного или дверного блока.

					2020	
Изм.	Кол.уч	Лист	№док.	Подпись	Дата	
Разработал		–				Индивидуальный жилой дом
Архитектор		Салыкова В.Г.				
Заказчик						План 1 этажа с размерами М 1:100


стадия	лист	листов
РД	5	

Согласовано:

Взам. инв. №

Подпись и дата

Инв. № подл.

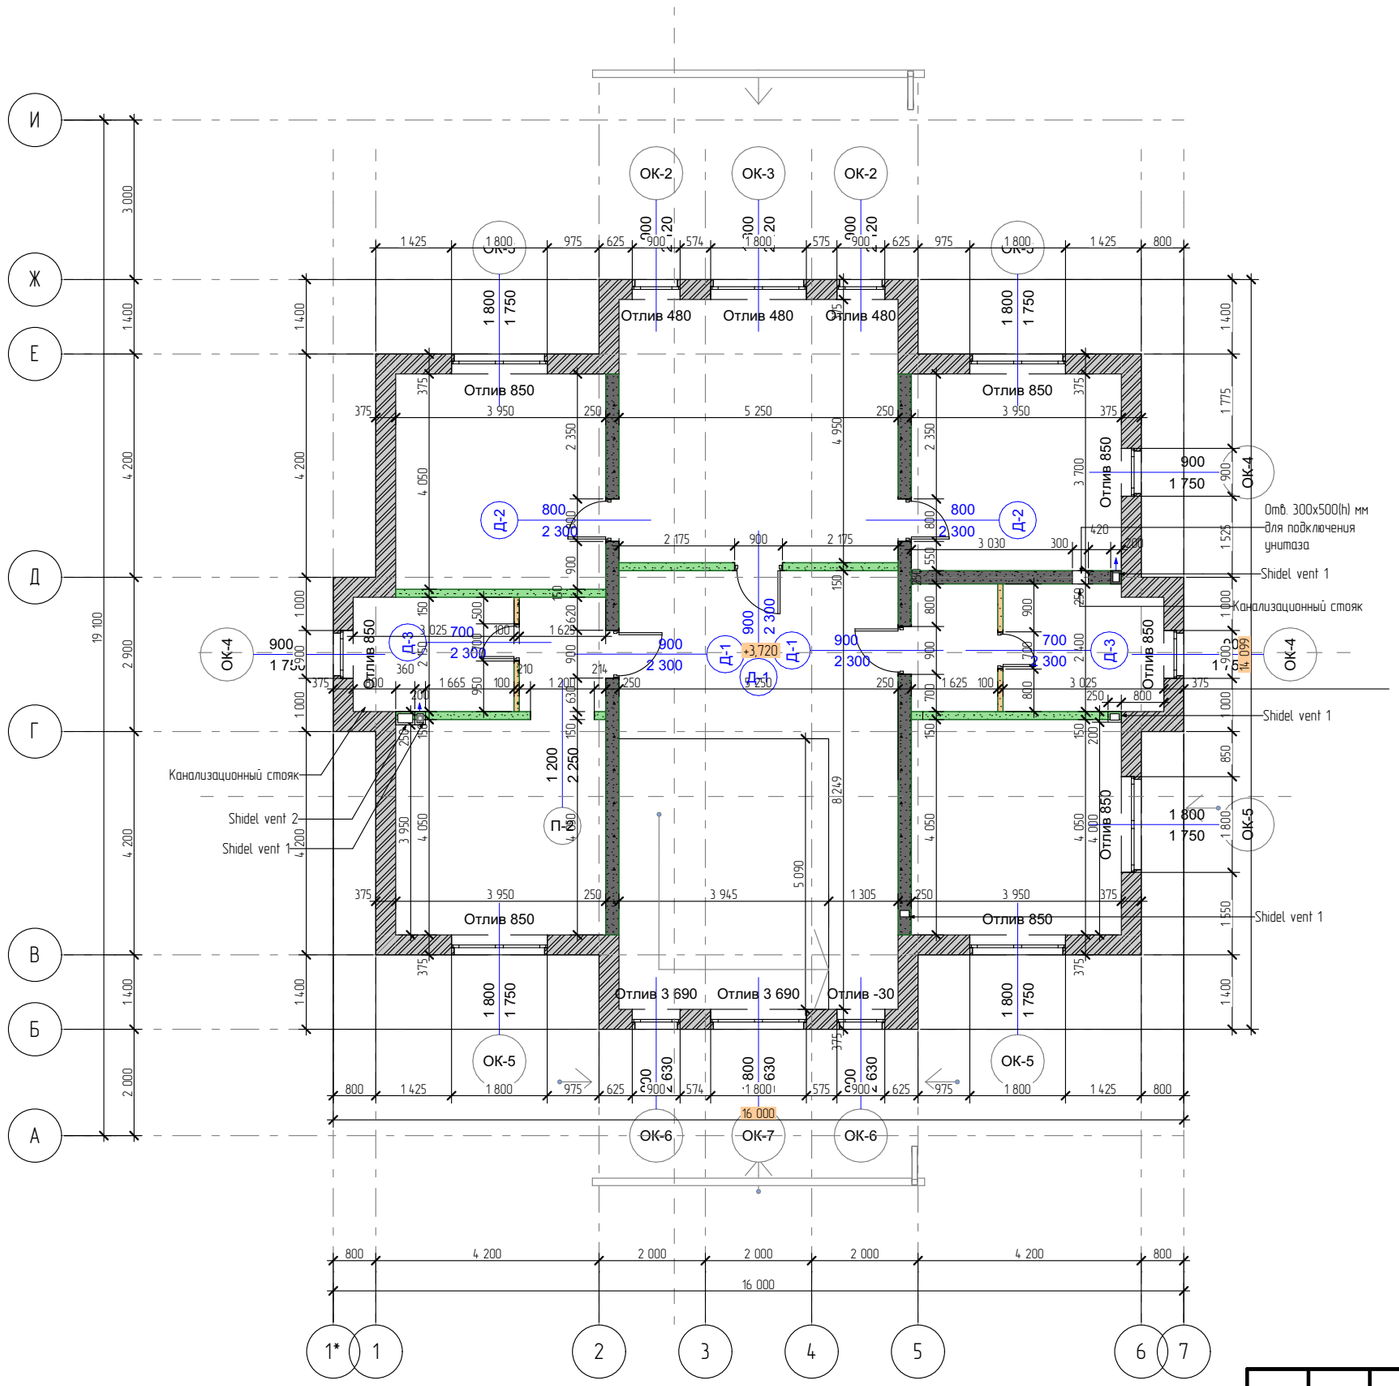




Условные обозначения



- Наружные несущие стены-блоки Ytong 375мм (указаны без отделки)
- Внутренние несущие стены-блоки Ytong 250 мм
- Перегородки-блоки Ytong 150 мм
- Перегородки-блоки Ytong 100 мм
- Столбы из кирпича 380х380 мм с металлической стойкой
- Металлическая стойка 100х100 мм
- ОК- Оконный проем
- Д- Дверной проем
- От.ч.п. Высота от чистого пола


Примечание:
1) За отметку +-0,000 принята отметка чистового пола первого этажа
2) Наружные размерные цепочки указаны по блокам без чистовой отделки
3) На планах этажей изображены маркеры, указывающие габариты проемов. Размеры изделий расчитываются индивидуально,в зависимости от способа установки и типа оконного или дверного блока.

					2020		
Изм.	Кол.уч	Лист	№док.	Подпись	Дата		
Разработал	–					Индивидуальный жилой дом	стадия: РД; лист: 6; листов:
Архитектор	Салыкова В.Г.						
Заказчик						План 2 этажа с размерами М 1:100	

Согласовано:
Взам. инв. №
Подпись и дата
Инв. № подл.

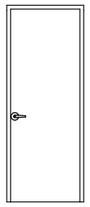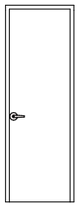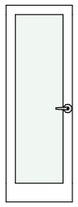Дверные проемы			
Поз.	Д-1	Д-2	Д-3
Общий вид			
Проем, мм	900×2 300	800×2 300	700×2 100
Количество	7	4	1
Примечание			

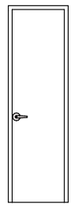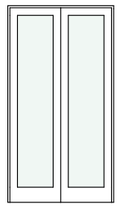Дверные проемы			
Поз.	Д-3	Д-4	ДБ-1
Общий вид			
Проем, мм	700×2 300	1 400×2 600	1 800×2 600
Количество	3	1	2
Примечание			Инд. изготовления


 
Дверные проемы			
Поз.	ДБ-2	ДН-1	П-1
Общий вид			
Проем, мм	900×2 600	900×2 100	2 500×2 600
Количество	2	2	1
Примечание	Инд. изготовления	Наруж.металлич.у тепл.	Проем (высота от плиты)


Дверные проемы


Примечание:

1)Открывание окон, итоговые размеры оконных/дверных проемов и блоков, и их конструкции, расположение, кол-во, наличие шпросов, а также доп. декоративных и конструктивных элементов согласовывается в отдельной спецификации с производителем.

2) Высота фрамуги согласовывается в отдельной спецификации дополнительно

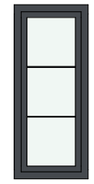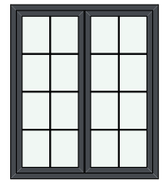Оконные проемы			
Поз.	ОК-1	ОК-2	ОК-3
Общий вид			
Проем, мм	900×750	900×2 120	1 800×2 120
Количество	4	10	9
Примечание			

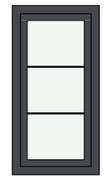Оконные проемы			
Поз.	ОК-4	ОК-5	ОК-6
Общий вид			
Проем, мм	900×1 750	1 800×1 750	900×2 630
Количество	9	5	2
Примечание			

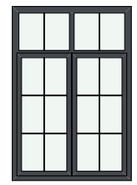Оконные проемы	
Поз.	ОК-7
Общий вид	
Проем, мм	1 800×2 630
Количество	1
Примечание	

					2020	
Изм.	Кол.уч	Лист	№док.	Подпись	Дата	
Разработал		–				Индивидуальный жилой дом
Архитектор		Салыкова В.Г.				
Заказчик						Спецификация заполнения оконных проёмов

стадия	лист	листов
РД	7	


Согласовано:

Взам. инв. №

Подпись и дата

Инв. № подл.

Разрез 1-1

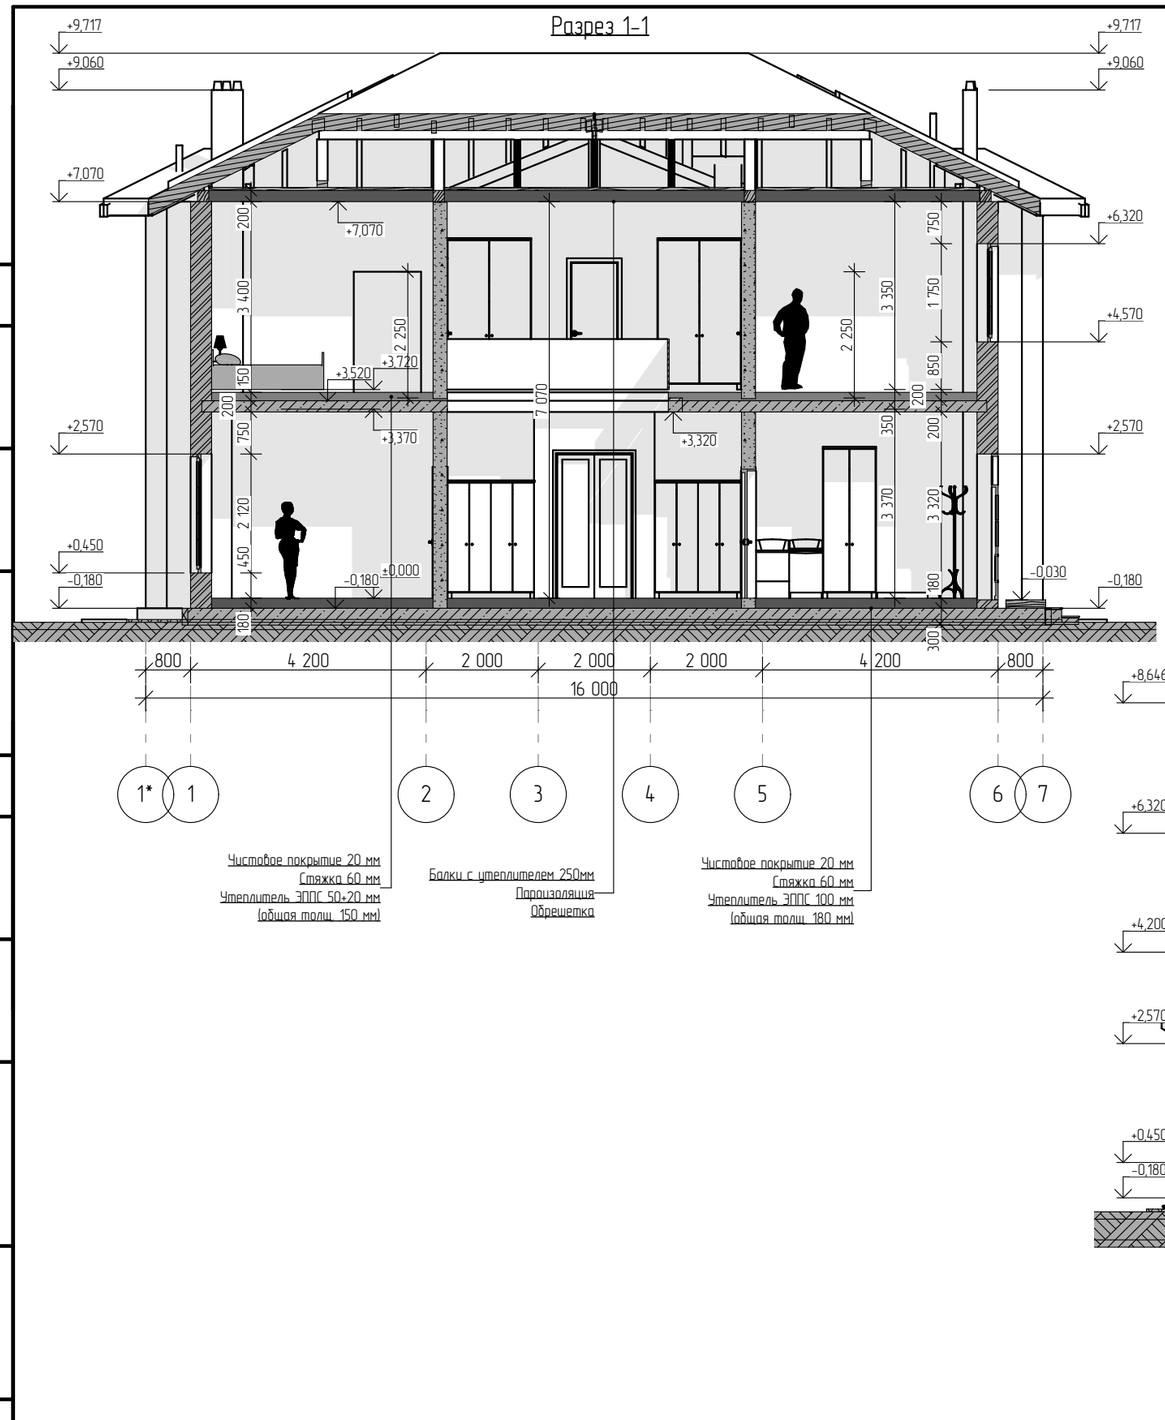


Чистовое покрытие 20 мм
Стяжка 60 мм
Утеплитель ЭППС 50+20 мм
(общая толщ. 150 мм)

Балки с утеплителем 250мм
Пароизоляция
Обрешетка

Чистовое покрытие 20 мм
Стяжка 60 мм
Утеплитель ЭППС 100 мм
(общая толщ. 180 мм)

Разрез 2-2

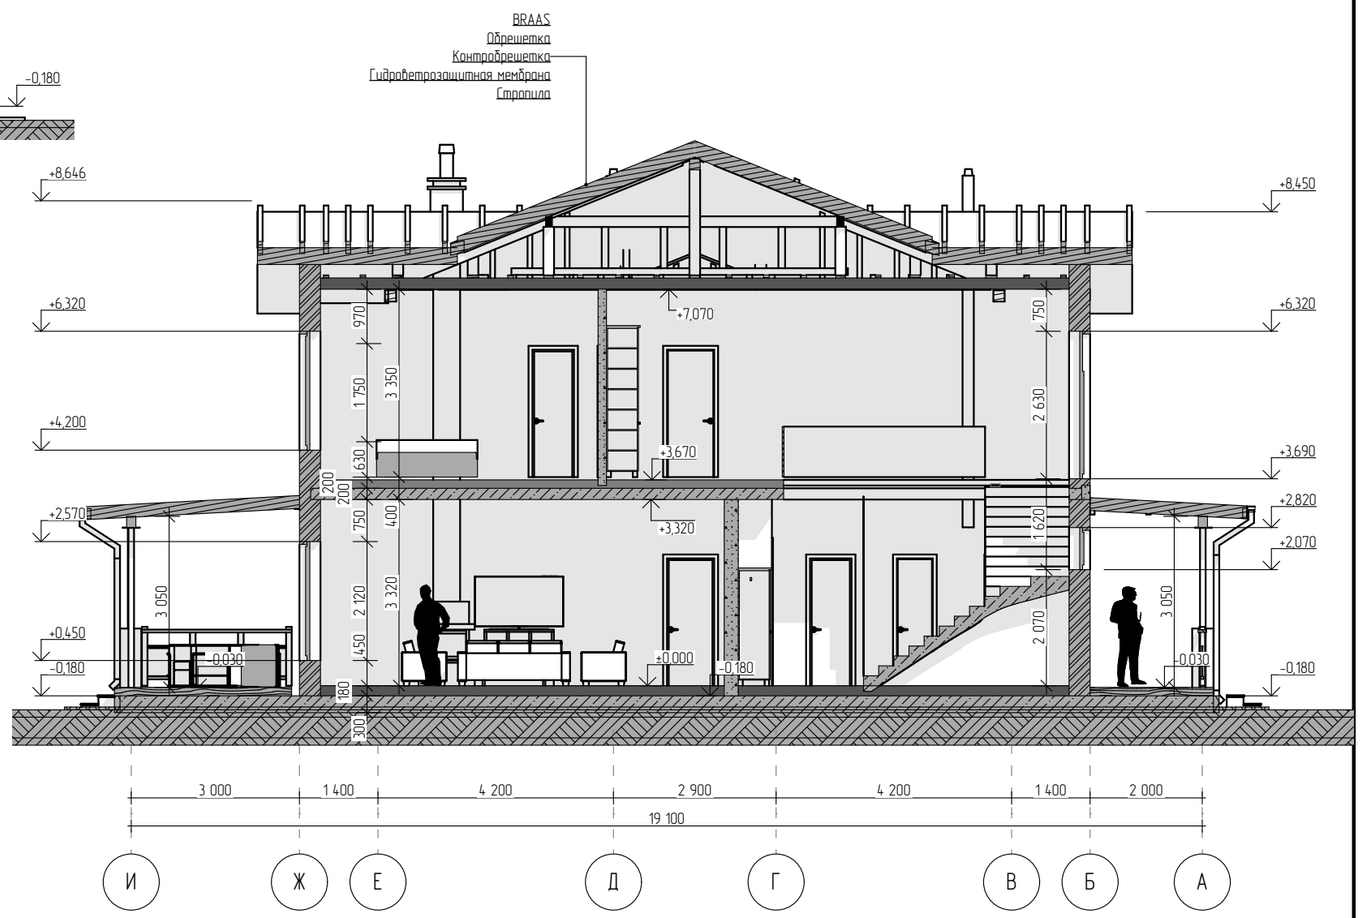

Примечание:
1) За отметку +-0,000 принята отметка чистового пола первого этажа.
2) Номинальные высотные размеры могут отличаться от фактических.
3)Несущие конструкции (конструкционные балки, прогоны кровли и т.д.) могут быть ниже основного уровня потолка.

					2020	
Изм.	Кол.уч	Лист	№док.	Подпись	Дата	
Разработал		–				Индивидуальный жилой дом
Архитектор		Салыкова В.Г.				
Заказчик						Разрезы М 1:100

стадия	лист	листов
РД	8	


Согласовано

Взам. инв. №

Подпись и дата

Инв. № подл.



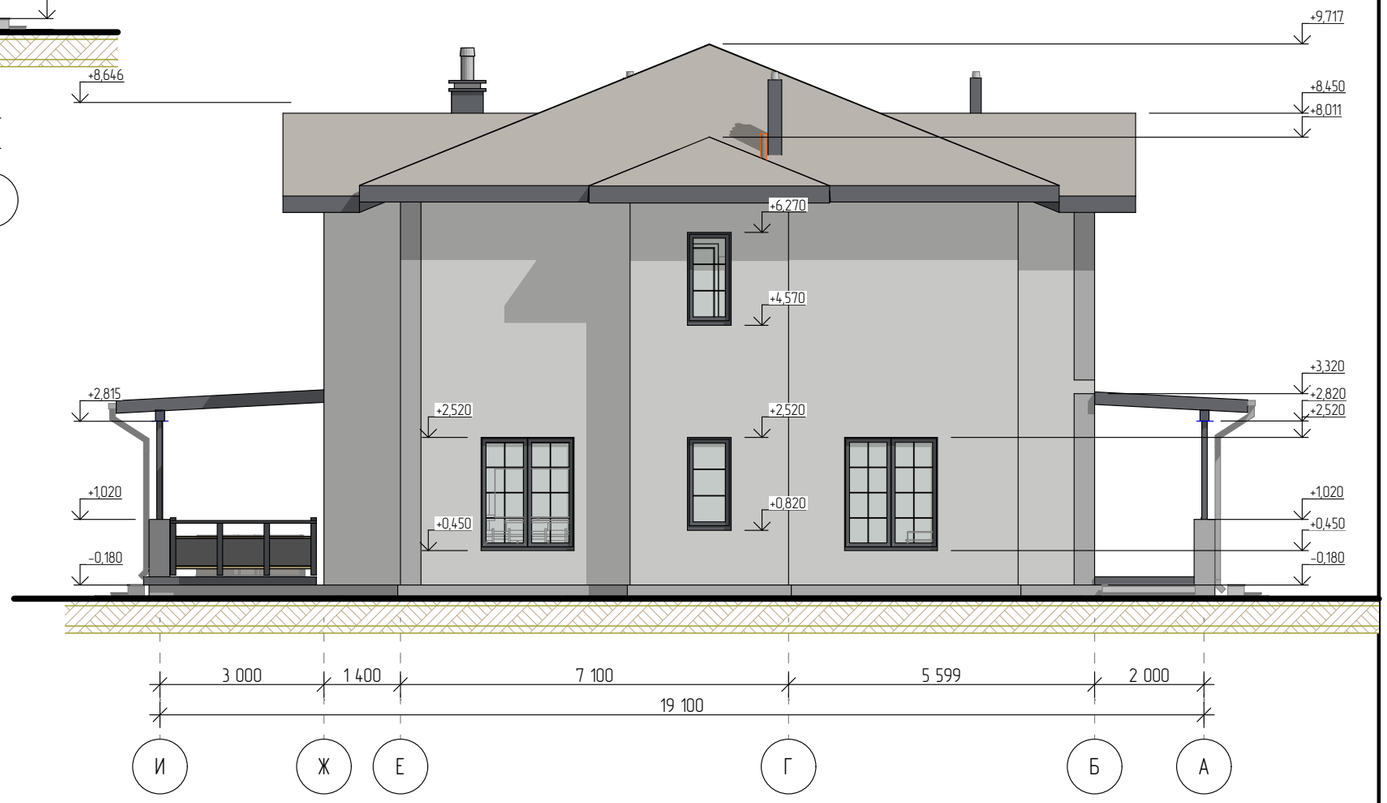

Примечание:
1) За отметку +-0,000 принята отметка чистового пола первого этажа.
2) Номинальные высотные размеры могут отличаться от фактических.
3)Несущие конструкции (конструкционные балки, прогоны кровли и т.д.) могут быть ниже основного уровня потолка.

Согласовано:

Взам. инв. №

Подпись и дата

Инв. № подл.

					2020			
Изм.	Кол.уч	Лист	№док.	Подпись	Дата			
Разработал		–				Индивидуальный жилой дом	стадия	лист	листов
Архитектор		Салыкова В.Г.					РД	9	
Заказчик						Фасады М 1:100			





Примечание:
1) За отметку +-0,000 принята отметка чистового пола первого этажа.
2) Номинальные высотные размеры могут отличаться от фактических.
3)Несущие конструкции (конструкционные балки, прогоны кровли и т.д.) могут быть ниже основного уровня потолка.

					2020	
Изм.	Кол.уч	Лист	№док.	Подпись	Дата	
Разработал	–					Индивидуальный жилой дом
Архитектор	Салыкова В.Г.					
Заказчик						Фасады М 1:100


стадия	лист	листов
РД	10	

Согласовано:


Взам. инв. №

Подпись и дата

Инв. № подл.

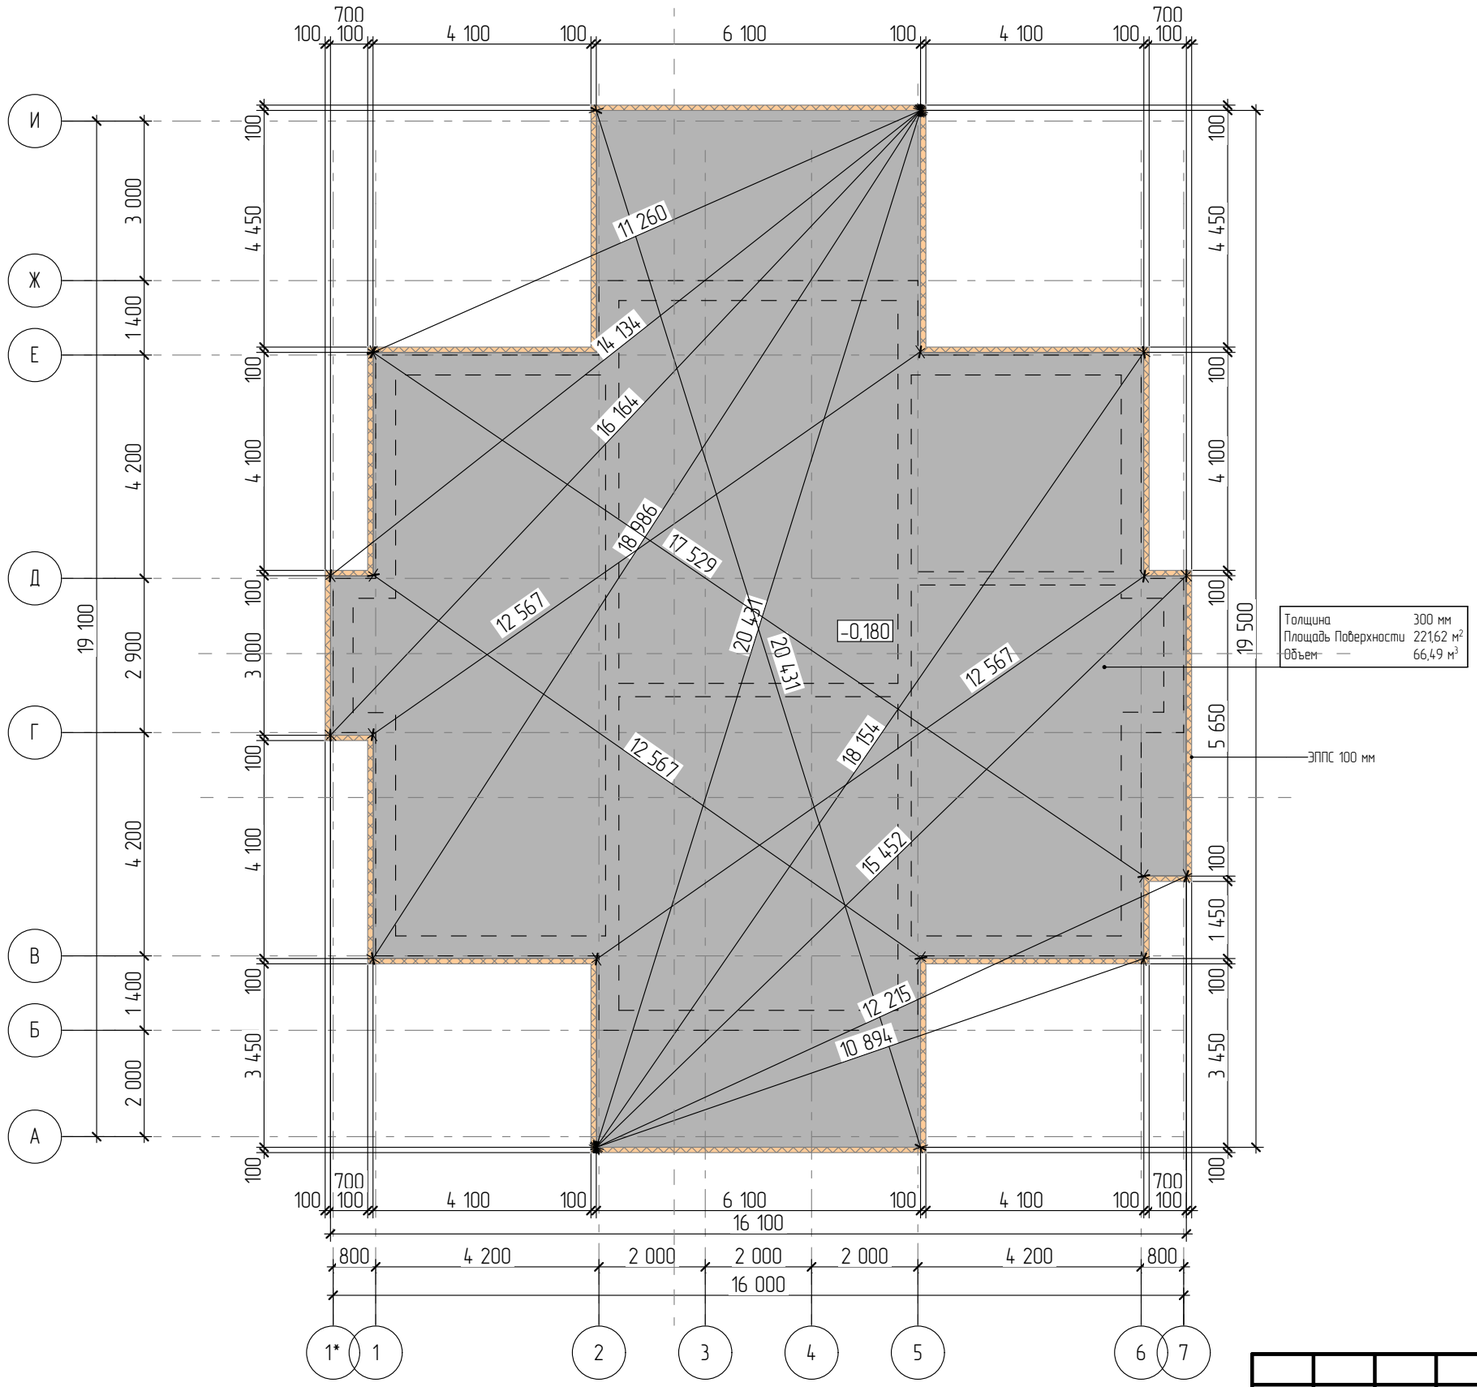

Сечение фундамета
Посадка стены на фундамент

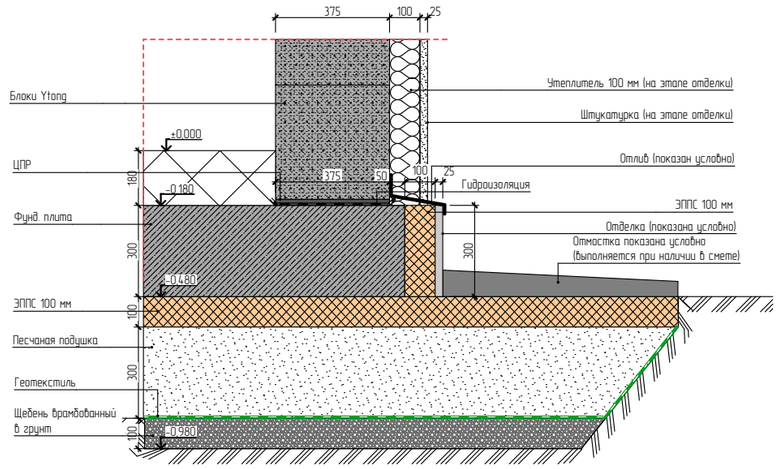


Примечание:
1) За отметку +-0,000 принята отметка чистого пола
2) Диагональные размеры фундамента указаны по наружной грани фундамента без учета ЭППС
3) Обязательно выполнение работ по водоотведению - дренажных работ с монтажом смотровых колодцев, отмостки и других работ, направленных на отведение воды от пятна застройки. Выполняется в объеме, определенном сметой. Гарантия на фундаментные работы осуществляется только при условии надлежащей системы водоотведения и ее эксплуатации.

					2020	
Изм.	Кол.уч	Лист	№док.	Подпись	Дата	
Разработал		–				Индивидуальный жилой дом
Архитектор		Салыкова В.Г.				План фундамента М 1:100
Заказчик						

стадия	лист	листов
РД	11	

Согласовано:
Взам. инв. №
Подпись и дата
Инв. № подл.

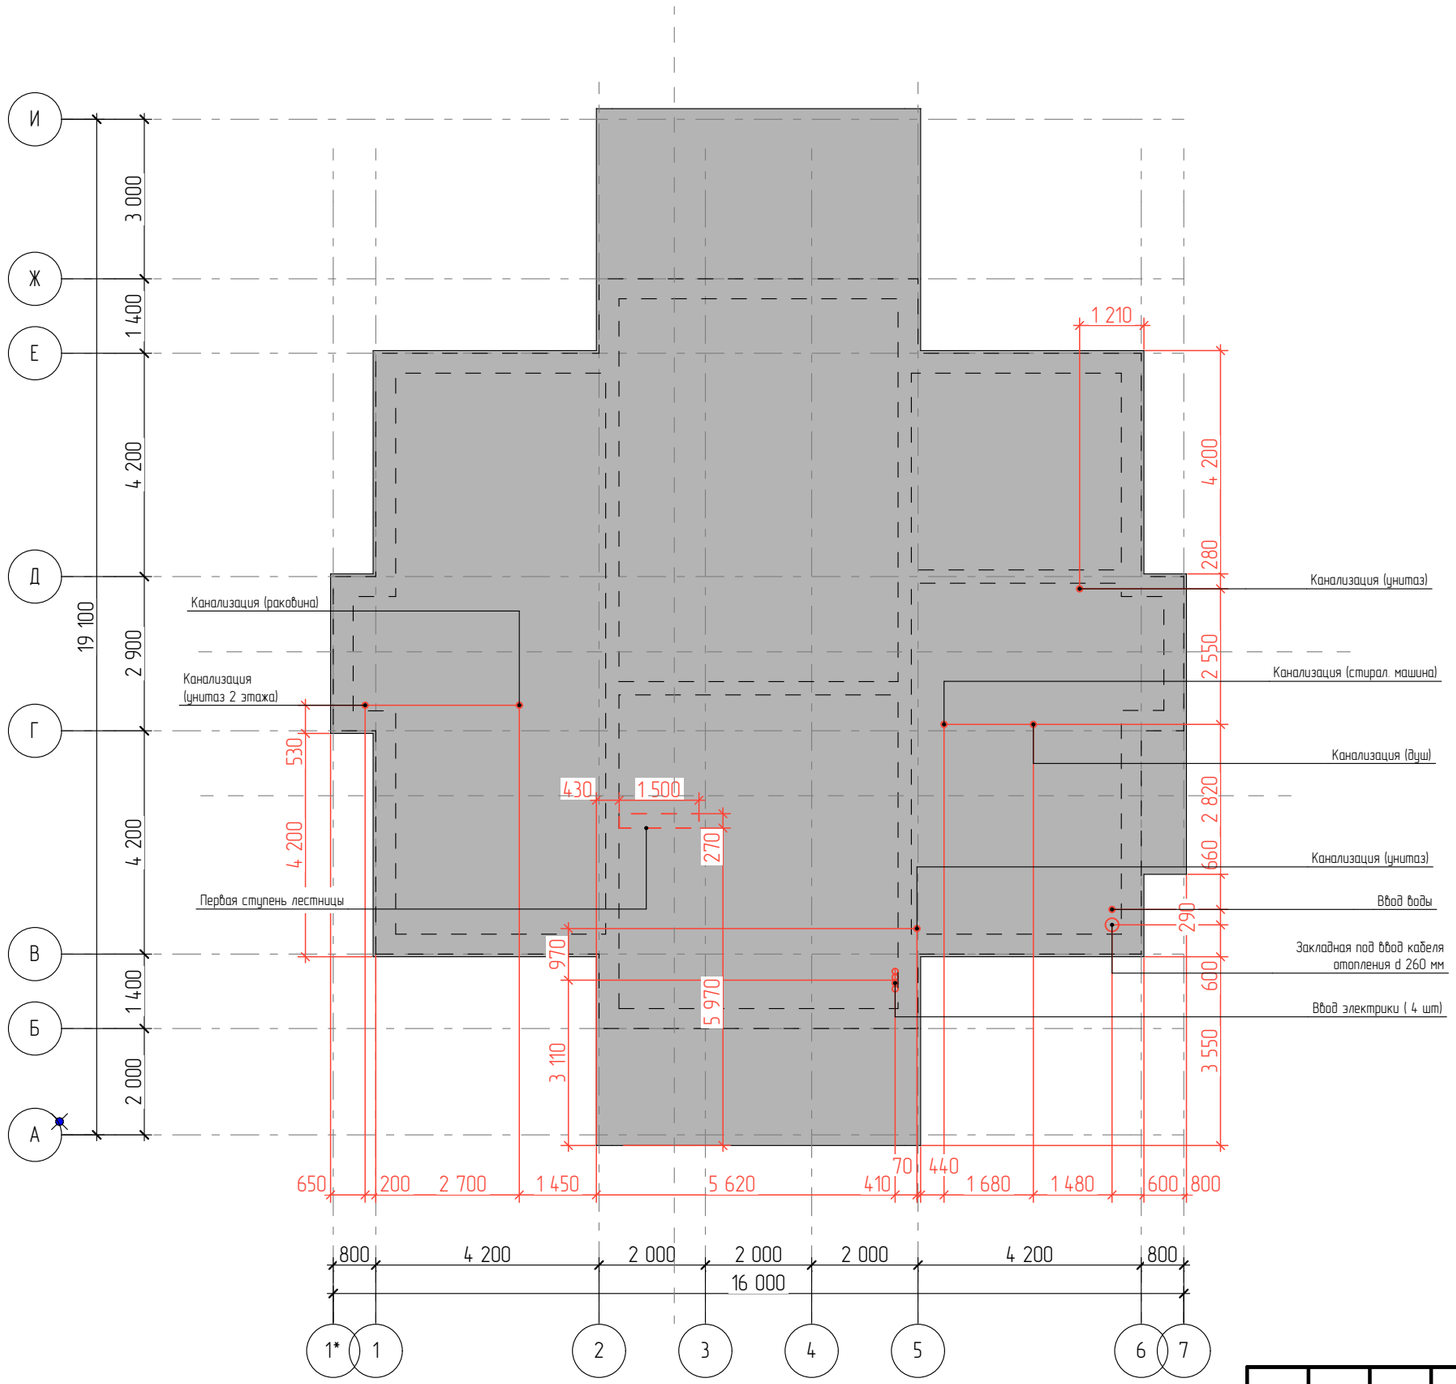

Примечание:
1) За отметку +-0,000 принята отметка чистого пола
2) Закладные в железобетонной плите перекрытия устанавливаются в соответствии с расположением сантехнических приборов во время заливки жб плиты с учетом допуска +-16 см.
3) Разводка сантехнических приборов производится в пироге чистого пола, которая составляет 180 мм

					2020
Изм.	Кол.уч	Лист	№док.	Подпись	Дата
Разработал		–			
Архитектор		Салыкова В.Г.			
Заказчик					

Индивидуальный жилой дом

стадия	лист	листов
РД	12	


План ЖБ плиты с коммуникациями М 1:100

Согласовано:

Взам. инв. №

Подпись и дата

Инв. № подл.

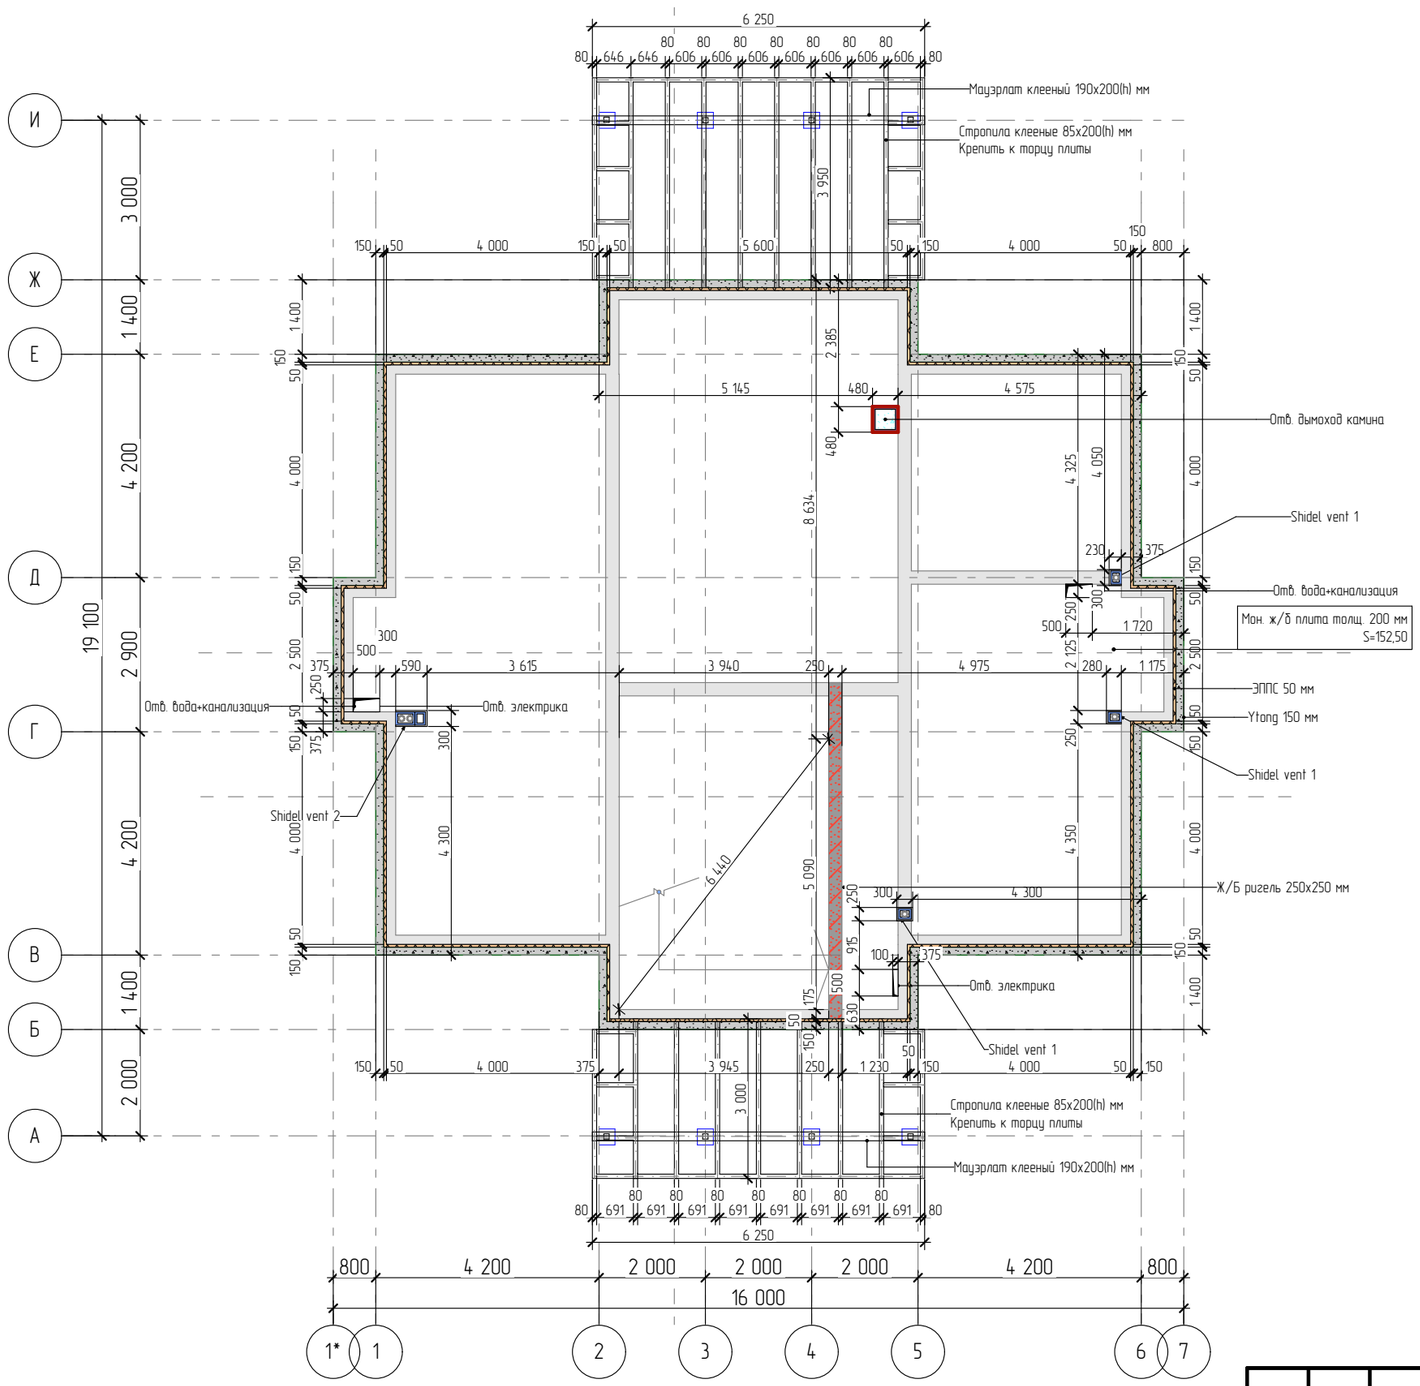

Примечание:

1) В местах прохождения инженерных коммуникаций предусмотрены отвестия в плите. Количество и наличие вентиляционных, фановых и дымовых труб определяется проектом инженерных коммуникаций, сметным расчетом и согласовывается дополнительно.

2) Отверстия под трубы отопления, а также остальные отверстия, которые будут определены инженерным проектом, выполняются по месту.

3) Трассировка труб для подключения раковины, душевой кабины и прочих сантехприборов осуществляется в пироге чистого пола


					2020			
Изм.	Кол.уч	Лист	№док.	Подпись	Дата			
Разработал		–				Индивидуальный жилой дом	стадия	лист	листов
Архитектор		Салыкова В.Г.					РД	13	
Заказчик						План плиты межэтажного перекрытия М 1:100			

Согласовано:

Взам. инв. №

Подпись и дата


Инв. № подл.

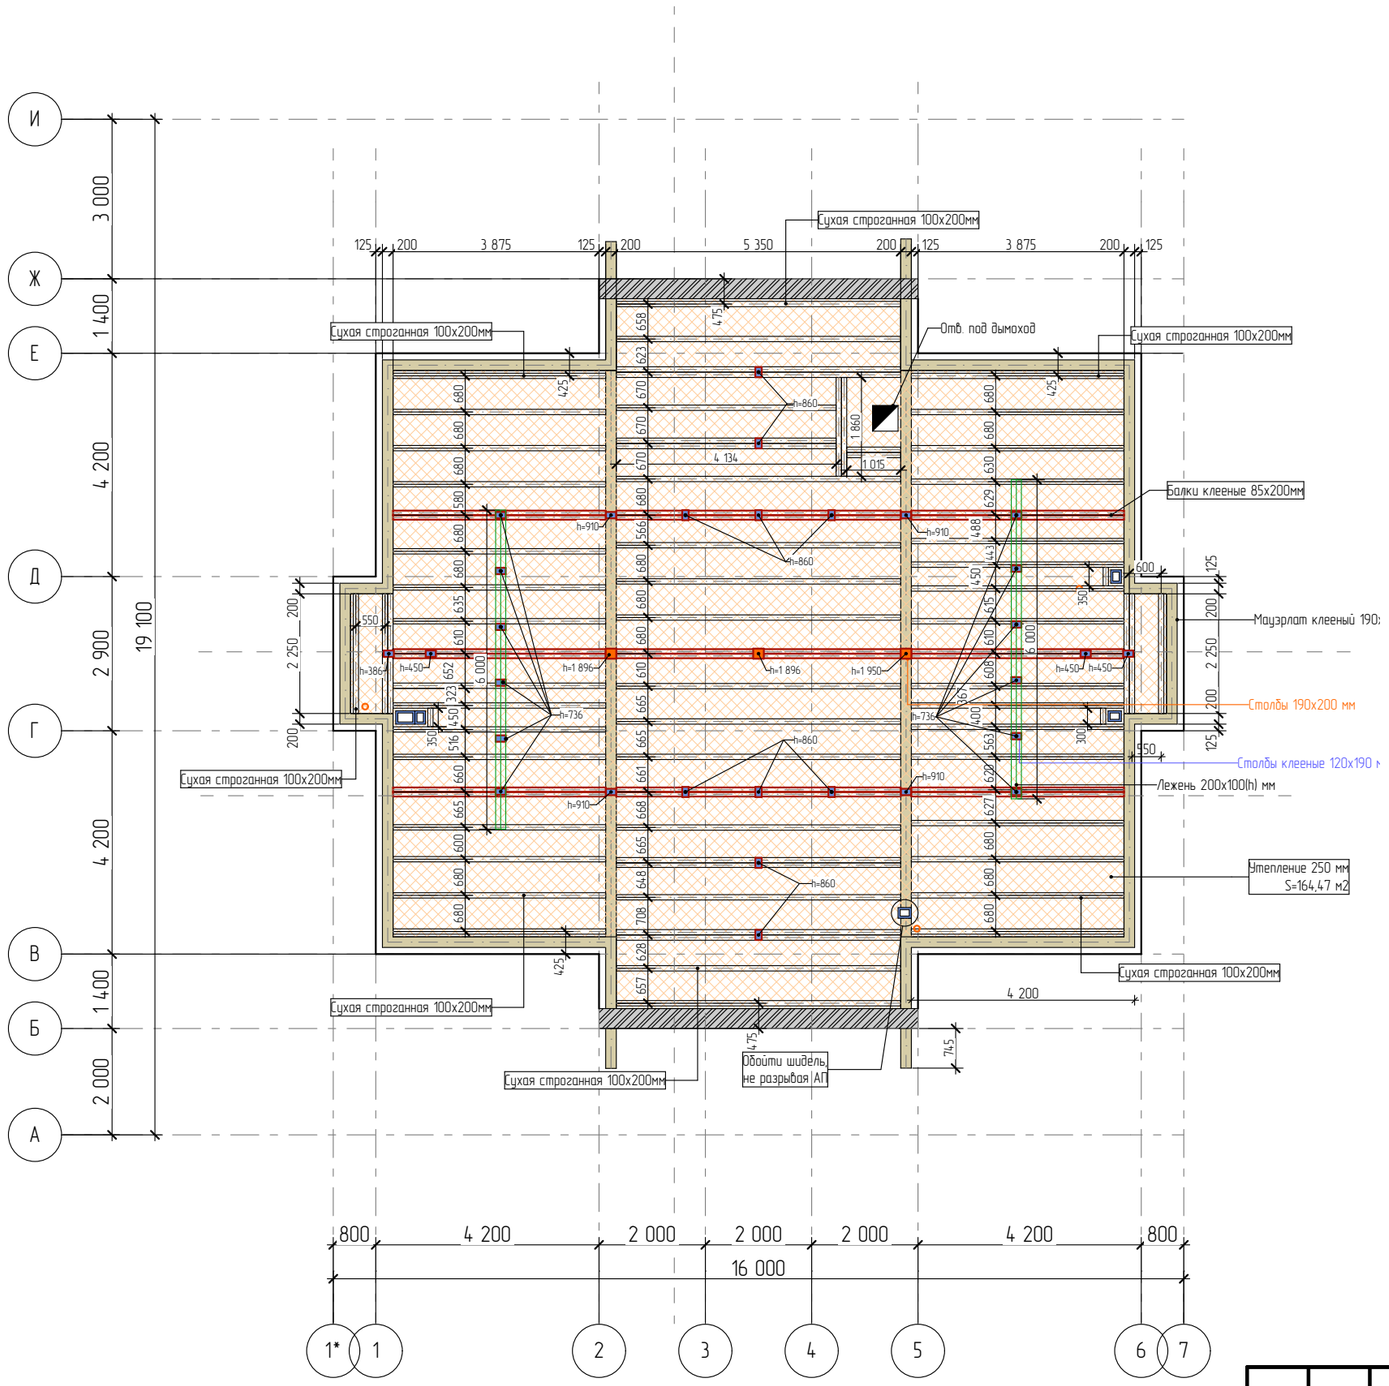


Примечание:
1) За отметку +-0,000 принята отметка чистого пола
2) Балки чердака запроектированы из сухой строганной доски 100х200(h) мм, мауэрлат 200х190 мм клееный, опорные столбы 120х190 и 190х200мм клееные

					2020		
Изм.	Кол.уч	Лист	№док.	Подпись	Дата		
Разработал		–				Индивидуальный жилой дом	стадия: РД; лист: 14; листов:
Архитектор		Салыкова В.Г.					
Заказчик						План чердачного перекрытия М 1:100	

Согласовано:
Взам. инв. №
Подпись и дата
Инв. № подл.

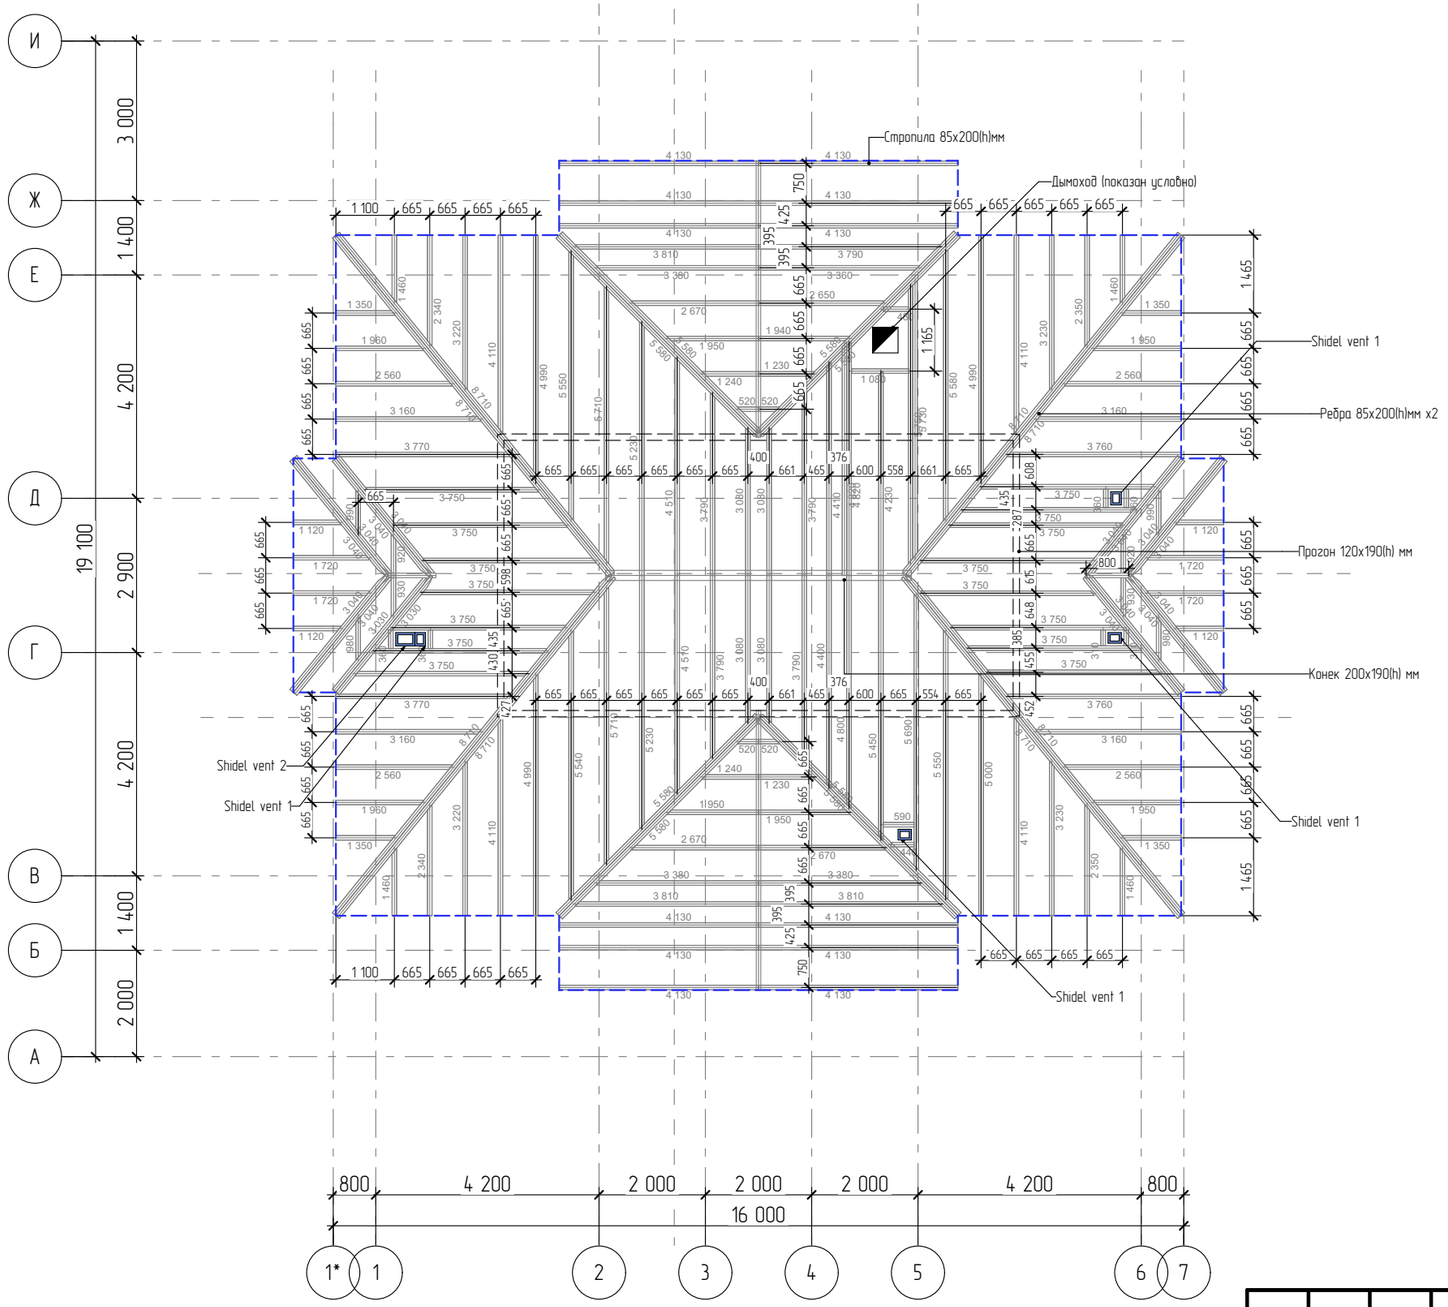

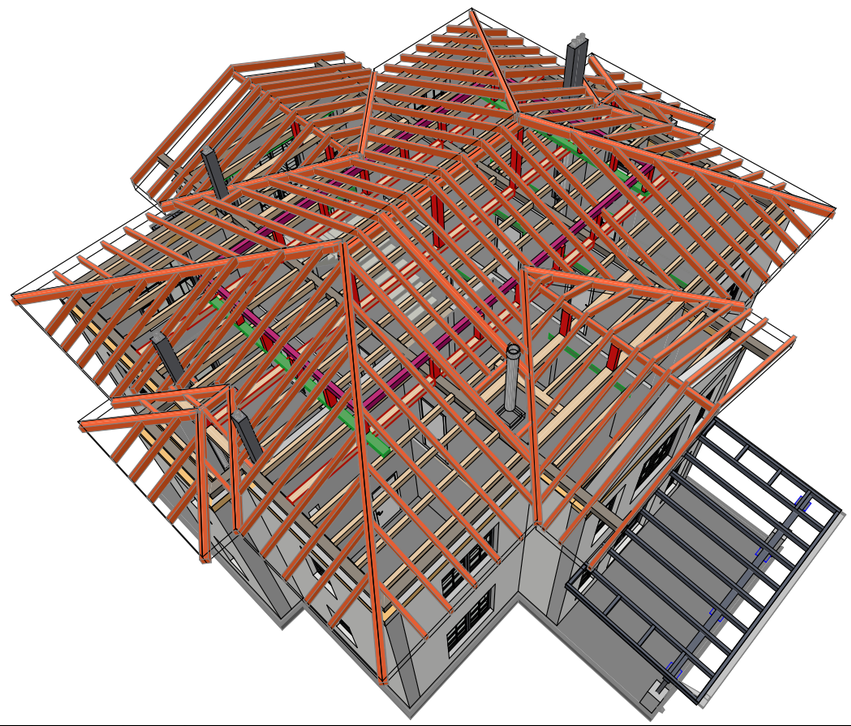

Примечание:
1) Шаг стропил 700 мм, если не указано иное


					2020		
Изм.	Кол.уч	Лист	№док.	Подпись	Дата		
Разработал		–				Индивидуальный жилой дом	стадия: РД; лист: 15; листов:
Архитектор		Салыкова В.Г.					
Заказчик						План стропил	

Согласовано:

Взам. инв. №

Подпись и дата

Инв. № подл.

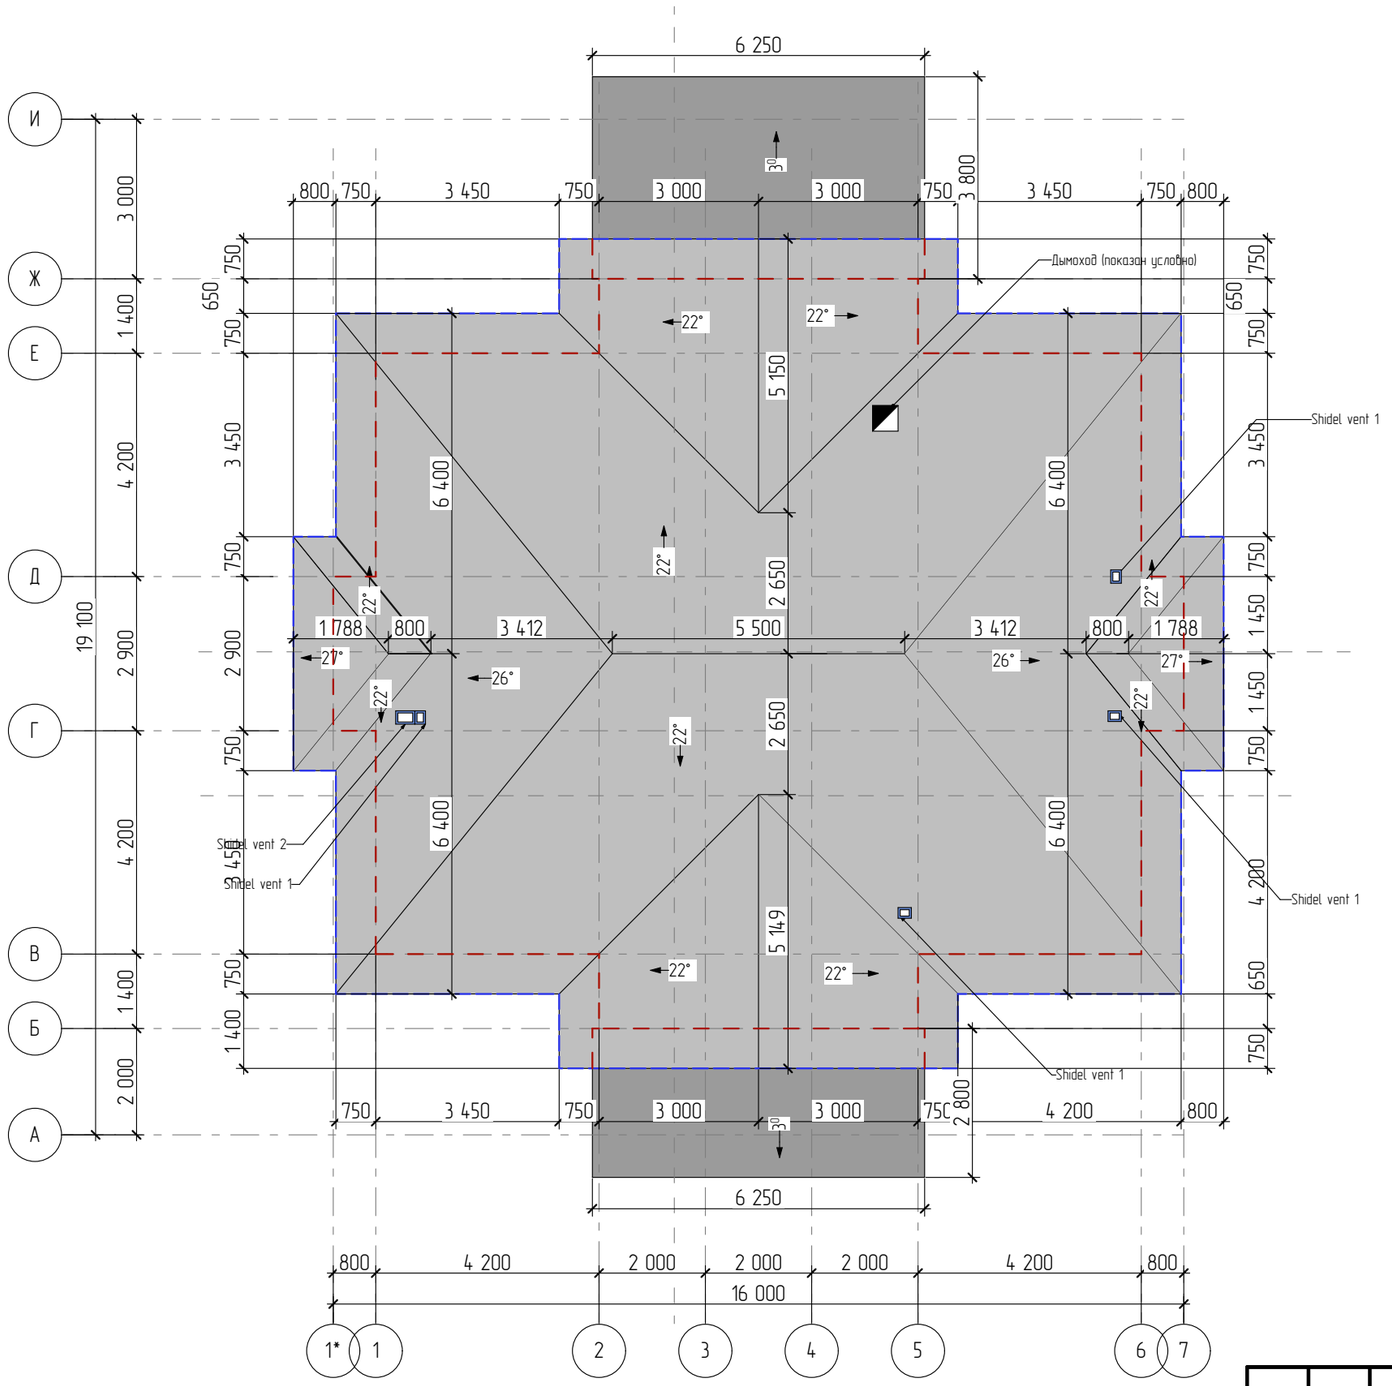

Кровля	
Поз.	Площадь, м
Кровля braas	252,28
Кровля плоская	41,30

Условные обозначения:

- - - - - - контур наружной стены

Примечание:

1) Все размеры даны в ортогональной проекции.
2) Наличие снегозадержателей и водосточной системы определяется сметным расчётом.
3) Погрешность монтажа вент выхода по горизонтали 16см а по длине волны 380 (при монтаже в металлочерепицу или Брас).
4) Монтаж кровельного покрытия выполнять в соответствии с инструкциями завода-изготовителя.
5) Расположение вентиляционных коммуникаций и прочих инженерных систем показано условно. Проект инженерных коммуникаций будет разрабатываться при заключении договора на инженерные работы. Количество и наличие вентиляционных, фановых и дымовых труб определяется дополнительным согласованием в сметном расчёте на этапе отделочных работ.
6)При устройстве вентиляционных шахт предусмотреть фартук для отвода воды со стороны конька

Изм.	Кол.уч	Лист	№док.	Подпись	Дата
					2020
Разработал	–				
Архитектор	Салыкова В.Г.				
Заказчик					

Индивидуальный жилой дом

стадия	лист	листов
РД	16	

План кровли М 1:100

Согласовано:

Взам. инв. №

Подпись и дата

Инв. № подл.