

Экспликация помещений 1 этажа

Тип помещения	№ п/п	Наименование	Площадь, м
Внутренние помещения			
	2	Тамбур	5,24
	3	Холл	18,57
	4	Гостевой санузел	2,62
	5	Кабинет	16,00
	6	Кухня	10,21
	7	Столовая	16,00
	8	Гостиная	39,09
	9	Комната	14,62
	10	Холл	5,14
	11	Санузел	5,66
	12	Постирочная	8,31
	13	Кладовая	4,33
			145,79 м²
Крыльцо, терраса			
	1	Крыльцо	12,88
	14	Крыльцо	1,85
	16	Терраса	19,91
			34,64 м²
			180,43 м²

Примечание:
1) Вся показанная мебель, а также назначение комнат носят условный характер
2) Расположение сантехнических приборов не подлежит перемещению.
Закладные в железобетонной плите перекрытия устанавливаются в соответствии с расположением сантехнических приборов во время заливки жб плиты.
3) Площадь помещений показана без учета отделочных материалов и понижающего коэффициента по периметру пола.
4) Нагрузка от камина и дымохода вместе с отделкой не должна превышать 1500 кг/м2.
5) Вентиляция помещений приточно-вытяжная естественная. Поступление наружного воздуха осуществляется через открывающиеся створки окон. Вытяжка-через вентиляционные каналы.

Изм.	Кол.уч	Лист	№док.	Подпись	Дата
					2020
Разработал		–			
Архитектор		Салыкова В.Г.			
Заказчик					

Индивидуальный жилой дом

стадия	лист	листов
ЭП	3	


План 1 этажа с расстановкой мебели М 1:100

Согласовано:

Взам. инв. №

Подпись и дата

Инв. № подл.

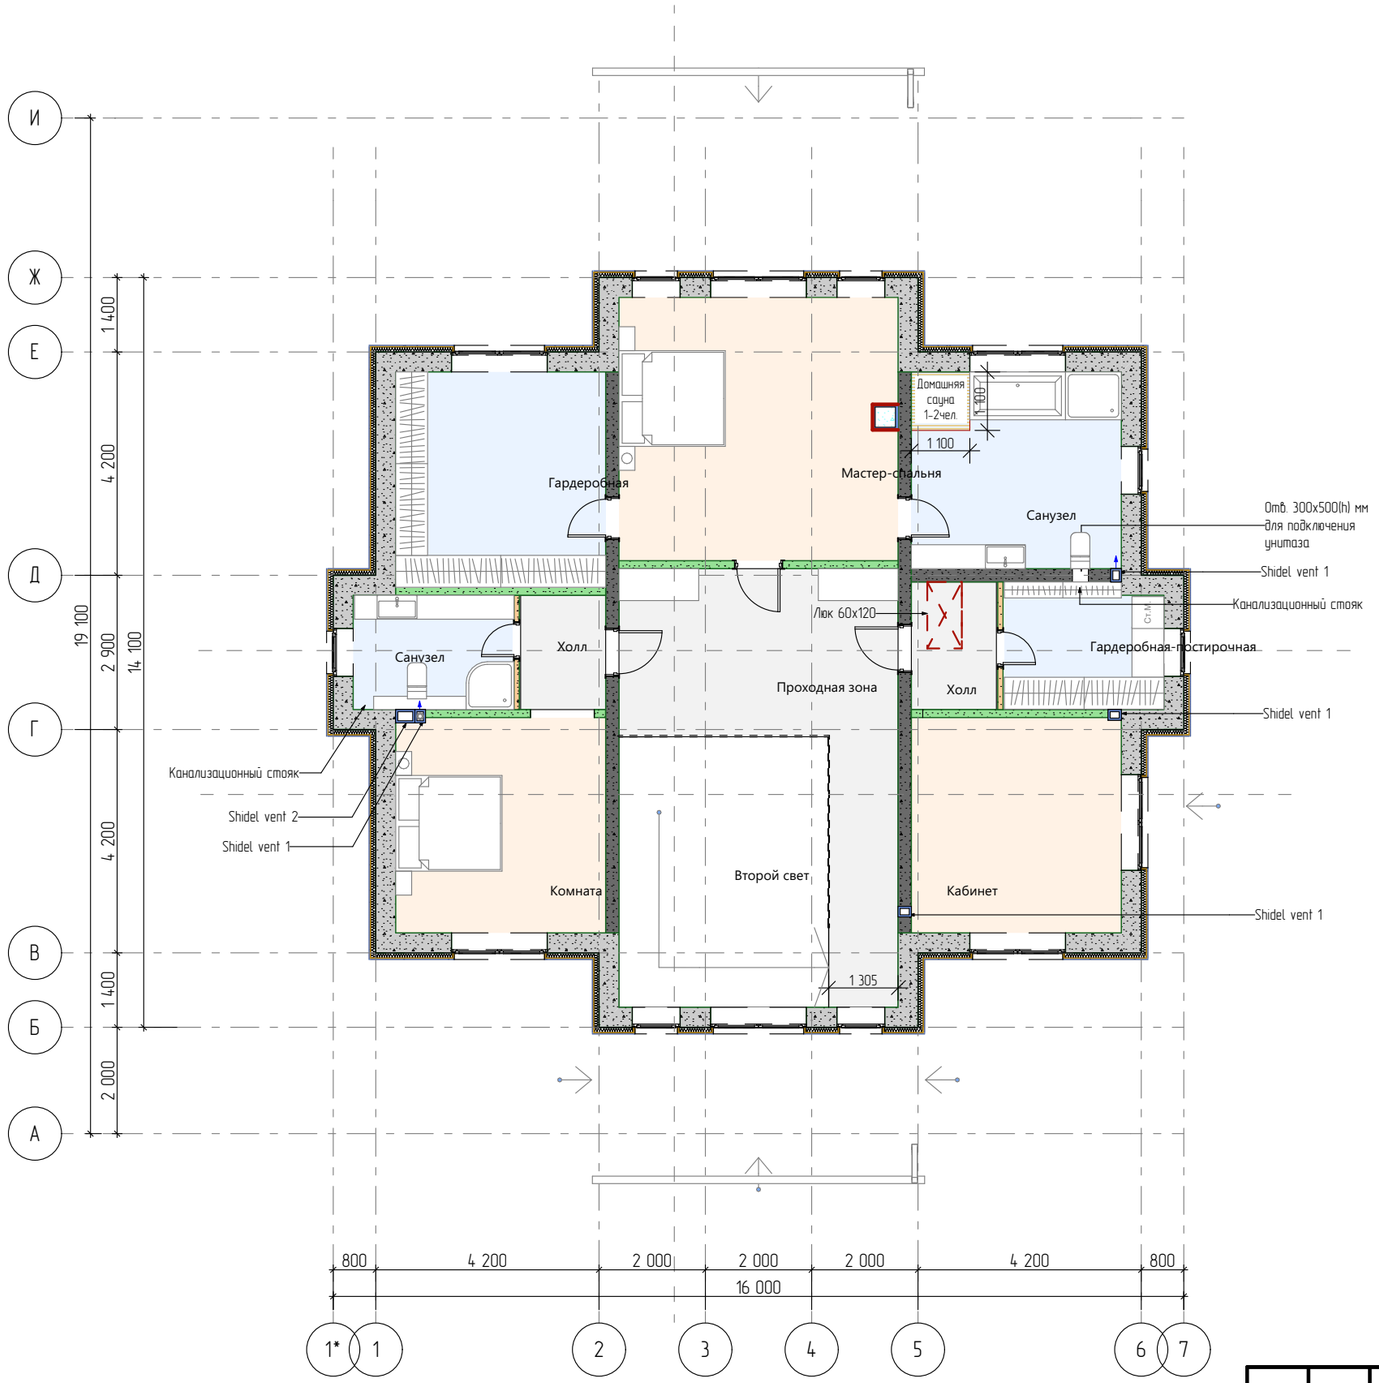

Примечание:
1) Вся показанная мебель, а также назначение комнат носят условный характер
2) Расположение сантехнических приборов не подлежит перемещению.
Закладные в железобетонной плите перекрытия устанавливаются в соответствии с расположением сантехнических приборов во время заливки жб плиты.
3) Площадь помещений показана без учета отделочных материалов и понижающего коэффициента по периметру пола.
4) Нагрузка от камина и дымохода вместе с отделкой не должна превышать 1500 кг/м2.
5) Вентиляция помещений приточно-вытяжная естественная. Поступление наружного воздуха осуществляется через открывающиеся створки окон. Вытяжка-через вентиляционные каналы.

Экспликация помещений 2 этажа

Тип помещения	№ п/п	Наименование	Площадь, м
Внутренние помещения			
	1	Проходная зона	23,19
	1*	Второй свет	20,09
	2	Комната	16,00
	3	Холл	3,44
	4	Санузел	6,45
	5	Гардеробная	16,00
	6	Мастер-спальня	25,99
	7	Санузел	14,62
	8	Гардеробная-постирочная	7,00
	9	Холл	3,84
	10	Кабинет	16,00
			152,62 м²

Изм.	Кол.уч	Лист	№док.	Подпись	Дата
					2020
Разработал		–			
Архитектор		Салыкова В.Г.			
Заказчик					


Индивидуальный жилой дом

стадия	лист	листов
ЭП	4	

План 2 этажа с расстановкой мебели М 1:100

Согласовано:
Взам. инв. №
Подпись и дата
Инв. № подл.

Разрез 1-1

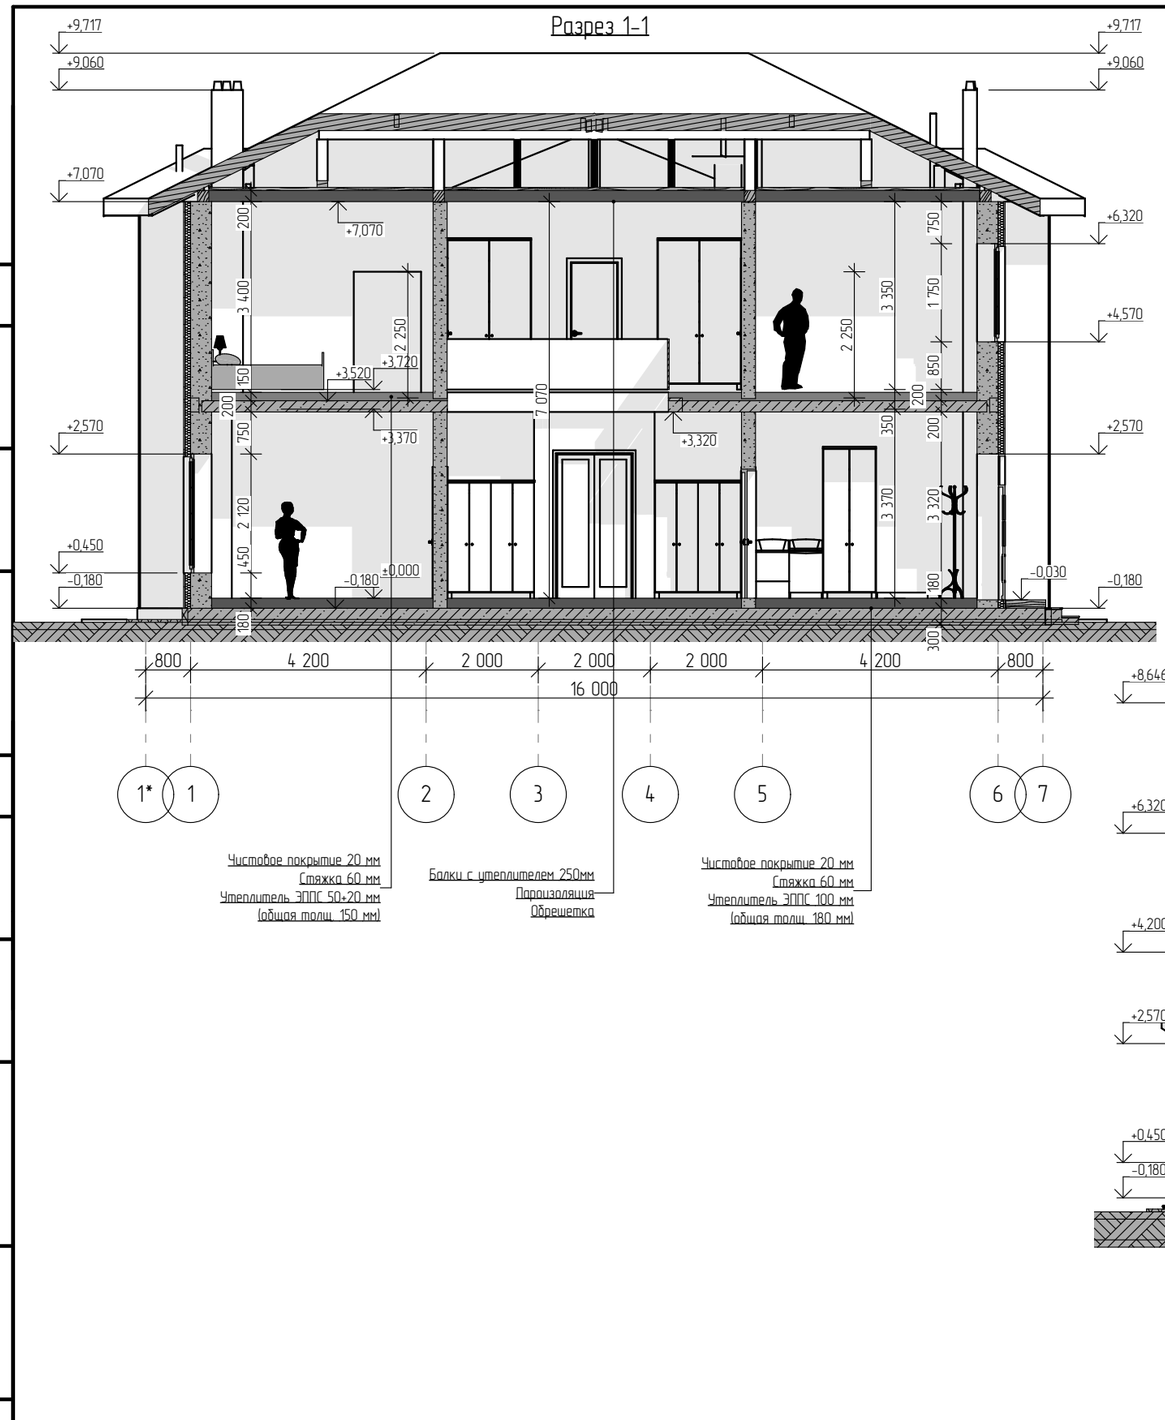


Чистовое покрытие 20 мм
Стяжка 60 мм
Утеплитель ЭППС 50+20 мм
(общая толщ. 150 мм)

Балки с утеплителем 250мм
Пароизоляция
Обрешетка

Чистовое покрытие 20 мм
Стяжка 60 мм
Утеплитель ЭППС 100 мм
(общая толщ. 180 мм)

Разрез 2-2

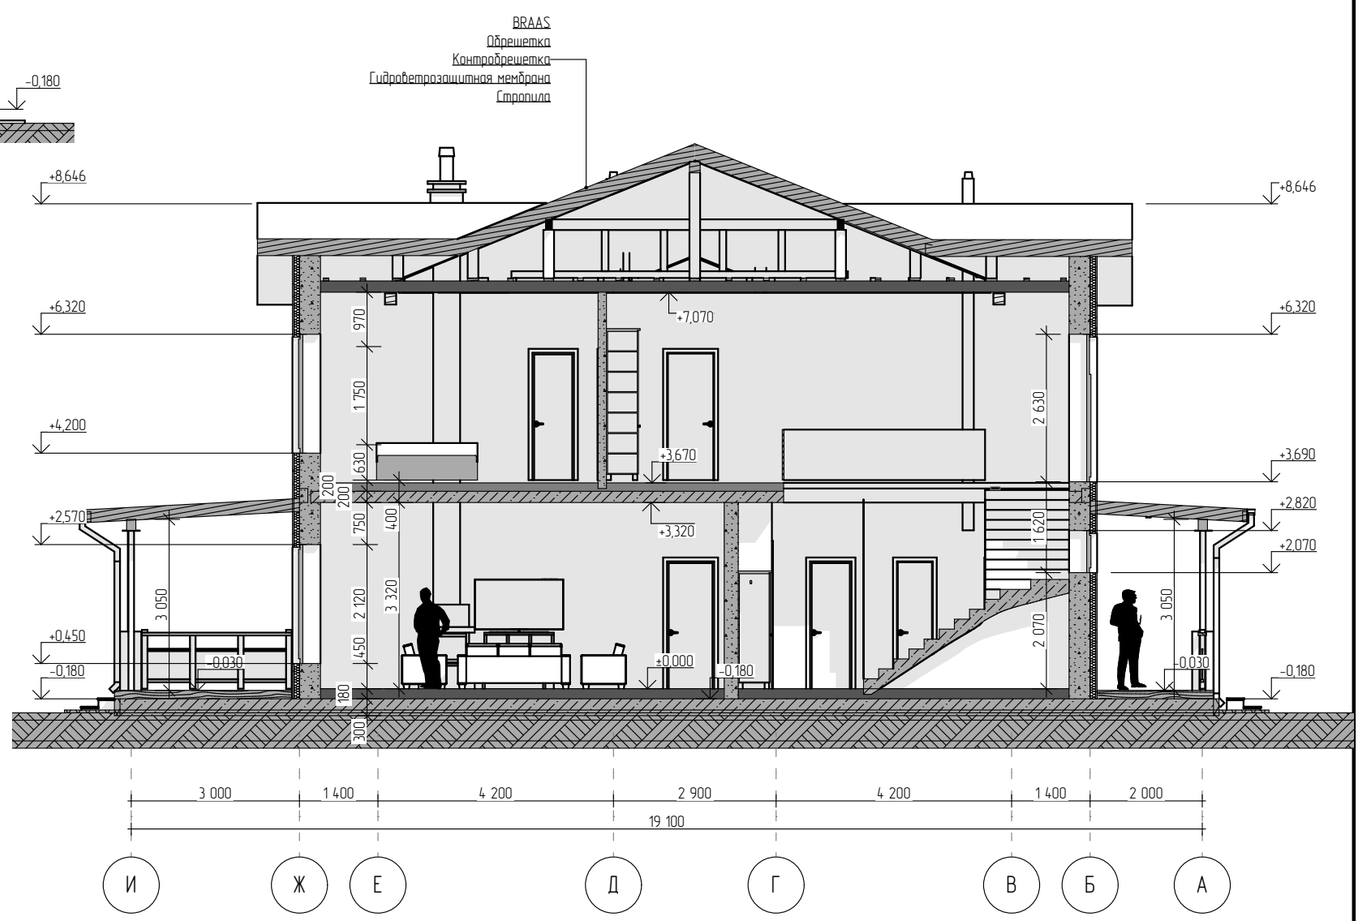

Примечание:
1) За отметку +-0,000 принята отметка чистового пола первого этажа.
2) Номинальные высотные размеры могут отличаться от фактических.
3)Несущие конструкции (конструкционные балки, прогоны кровли и т.д.) могут быть ниже основного уровня потолка.

					2020		
Изм.	Кол.уч	Лист	№док.	Подпись	Дата		
Разработал		–				Индивидуальный жилой дом	стадия: ЭП; лист: 8; листов:
Архитектор		Салыкова В.Г.					
Заказчик						Разрезы М 1:100	

Согласовано

Взам. инв. №

Подпись и дата

Инв. № подл.

Вид 1



Примечание:

1) Все декоративные элементы разрабатываются в отдельно проекте
Цветовое решение дано схематично, краска подбирается Заказчиком самостоятельно.

					2020			
Изм.	Кол.уч	Лист	№док.	Подпись	Дата			
Разработал	–					Индивидуальный жилой дом	стадия	лист	листов
Архитектор	Салыкова В.Г.						ЭП	11	
Заказчик						Общий вид			

Согласовано:

Взам. инв. №

Подпись и дата

Инв. № подл.

Вид 2



Примечание:

1) Все декоративные элементы разрабатываются в отдельно проекте
Цветовое решение дано схематично, краска подбирается Заказчиком самостоятельно.

					2020	
Изм.	Кол.уч	Лист	№док.	Подпись	Дата	
						Индивидуальный жилой дом
Разработал		–				
Архитектор		Салыкова В.Г.				
						Общий вид
Заказчик						

стадия	лист	листов
ЭП	12	

Согласовано:

Взам. инв. №

Подпись и дата

Инв. № подл.

Вид 3



Согласовано

Взам. инв. №

Подпись и дата

Инв. № подл.

Общий вид

Лист

21

Вид 4



Согласовано

Взам. инв. №

Подпись и дата

Инв. № подл.

Общий вид

Лист

25

Вид 5



Согласовано

Взам. инв. №

Подпись и дата

Инв. № подл.

Общий вид

Лист

26