М 1:100

## Маркировочный план 1 этажа

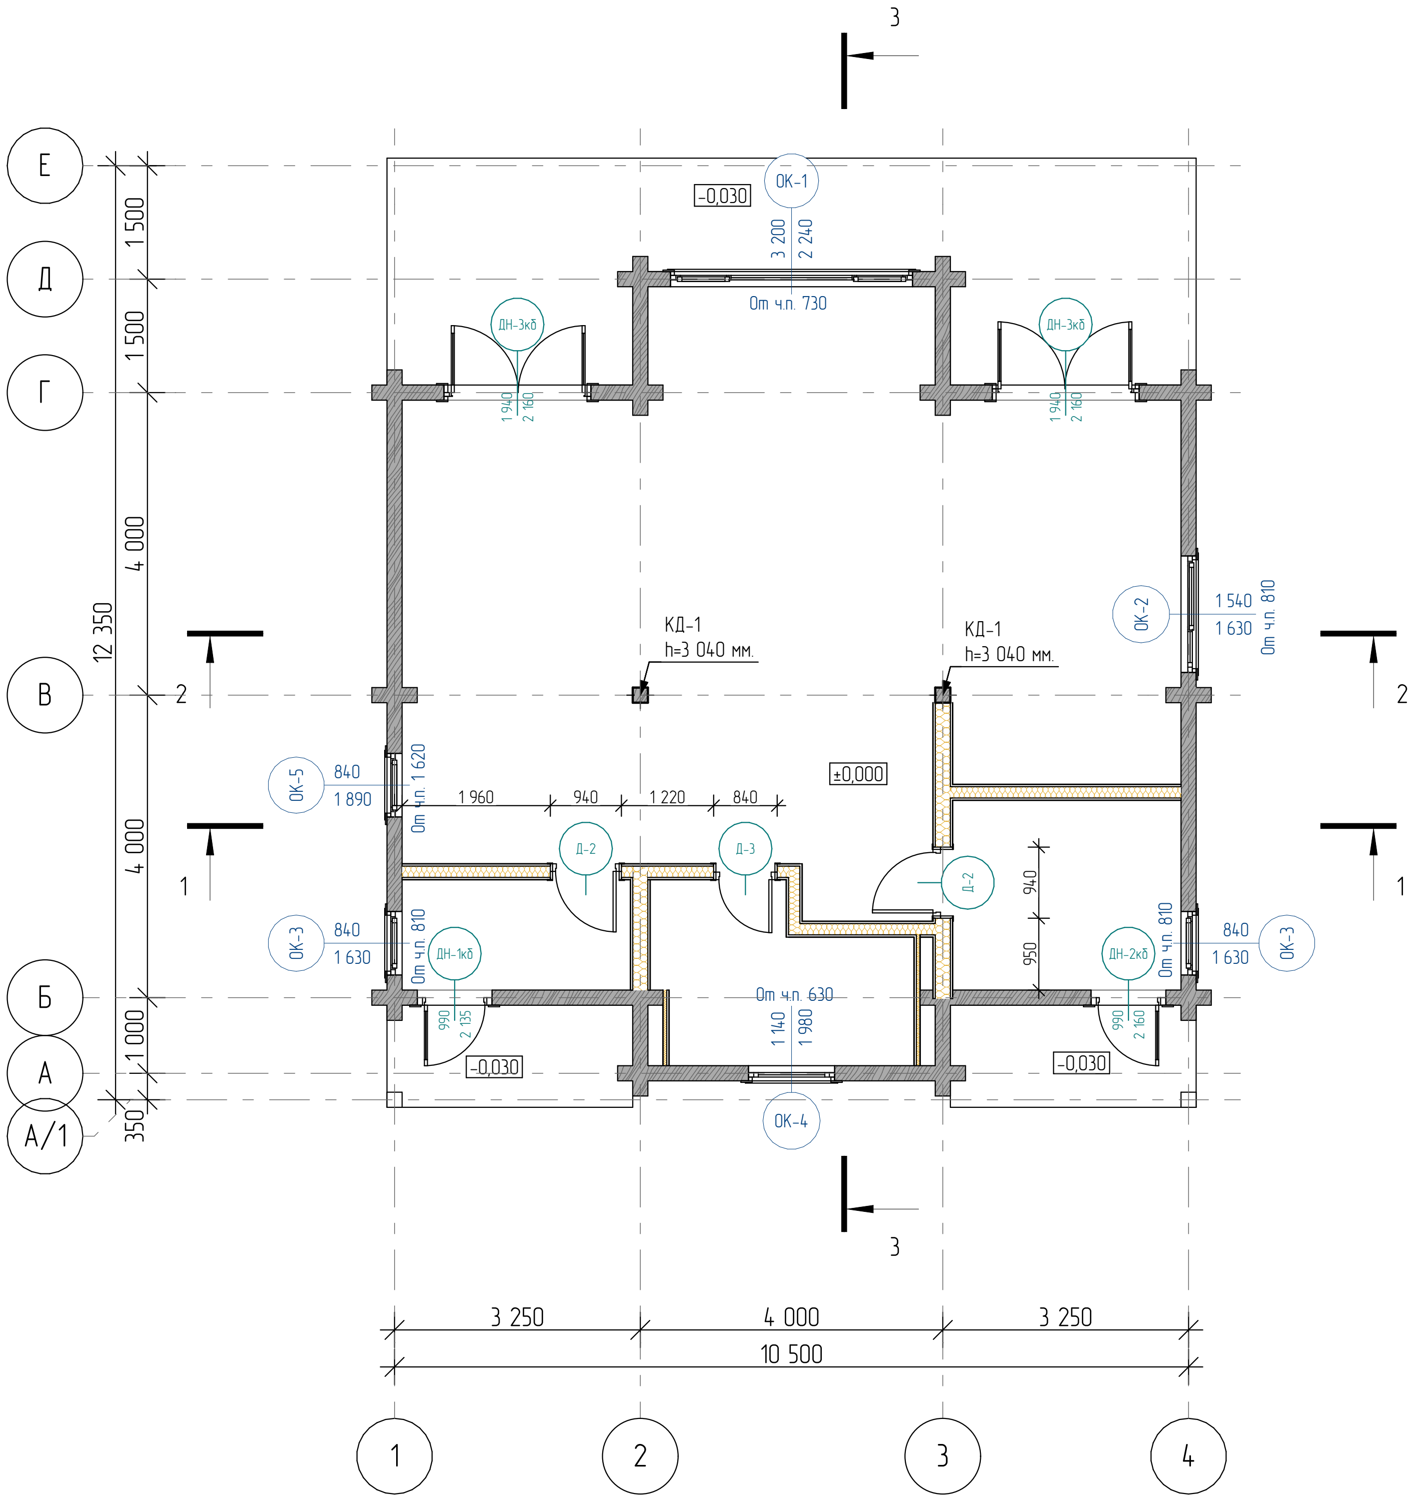

Примечание:

1) Привязка проёмов окон и дверей в клееном брусе указывается с учетом обсады

Согласовано:

Взам. инв. №

Подпись и дата

Инв. № подл.

| Изм. | Кол.уч | Лист | №док. | Подпись | Дата |
|---|---|---|---|---|---|
| | | | | | 2020 |

#ID Проекта

Адрес: #Полный Адрес Участка

| | | | |
|---|---|---|---|
| Архитектор | Салыкова В.Г. | | |
| Конструктор | | | |
| Заказчик | #Обращение к<br>Заказчику | | |

Индивидуальный жилой дом

| стадия | лист | листов |
|---|---|---|
| РП | 1 | |

Маркировочный план 1 этажа М 1:100

М 1:100

# Маркировочный план 2 этажа

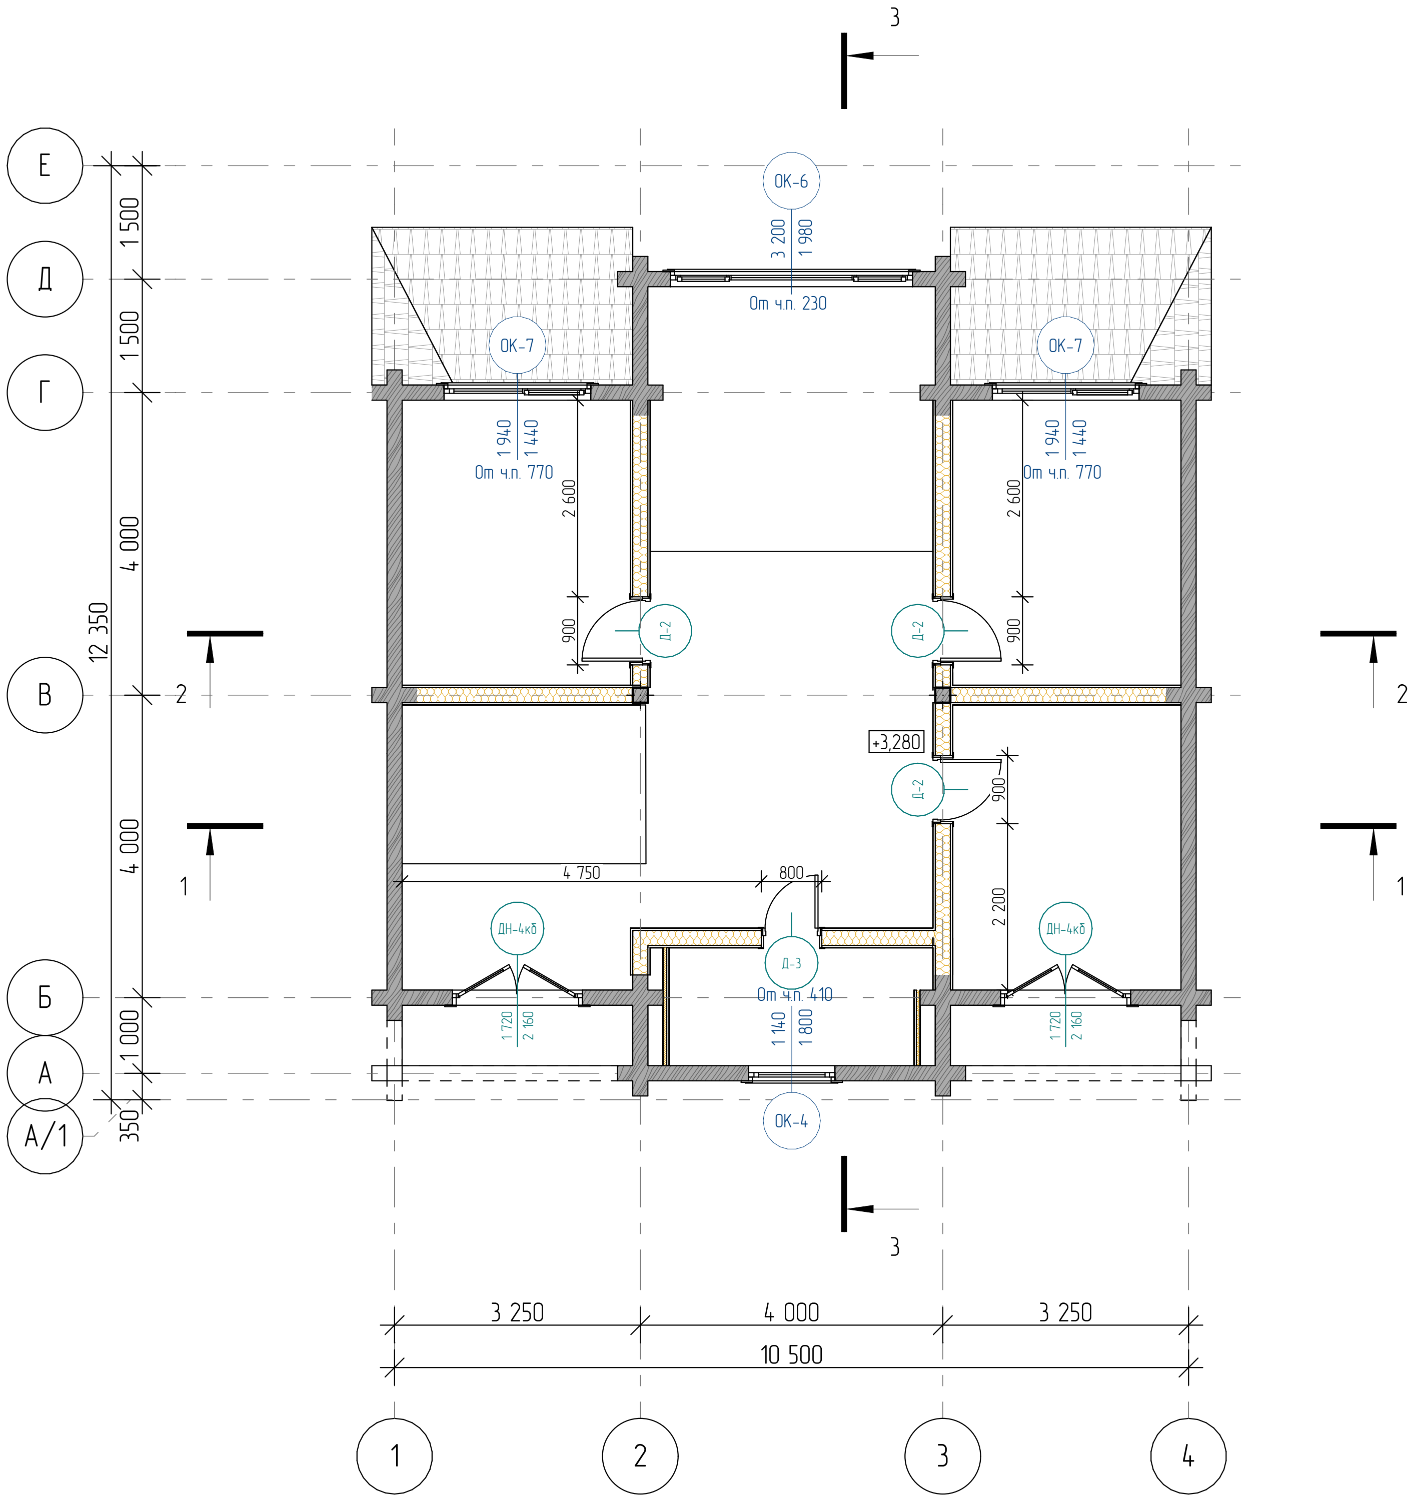

Примечание:

1) Привязка проёмов окон и дверей в клееном брусе указывается с учетом обсады

Согласовано:

Взам. инв. №

Подпись и дата

Инв. № подл.

| | | | | | | | | |
|---|---|---|---|---|---|---|---|---|
| | | | | | 2020 | #ID Проекта | | |
| | | | | | | Адрес: #Полный Адрес Участка | | |
| Изм. | Кол.уч | Лист | №док. | Подпись | Дата | | | |
| | | | | | | Индивидуальный жилой дом | стадия | лист | листов |
| | | | | | | | РП | 2 | |
| Архитектор | | Салыкова В.Г. | | | | Маркировочный план 2 этажа М 1:100 | | |
| Конструктор | | | | | | | | |
| Заказчик | | #Обращение к Заказчику | | | | | | |

## Стена 1

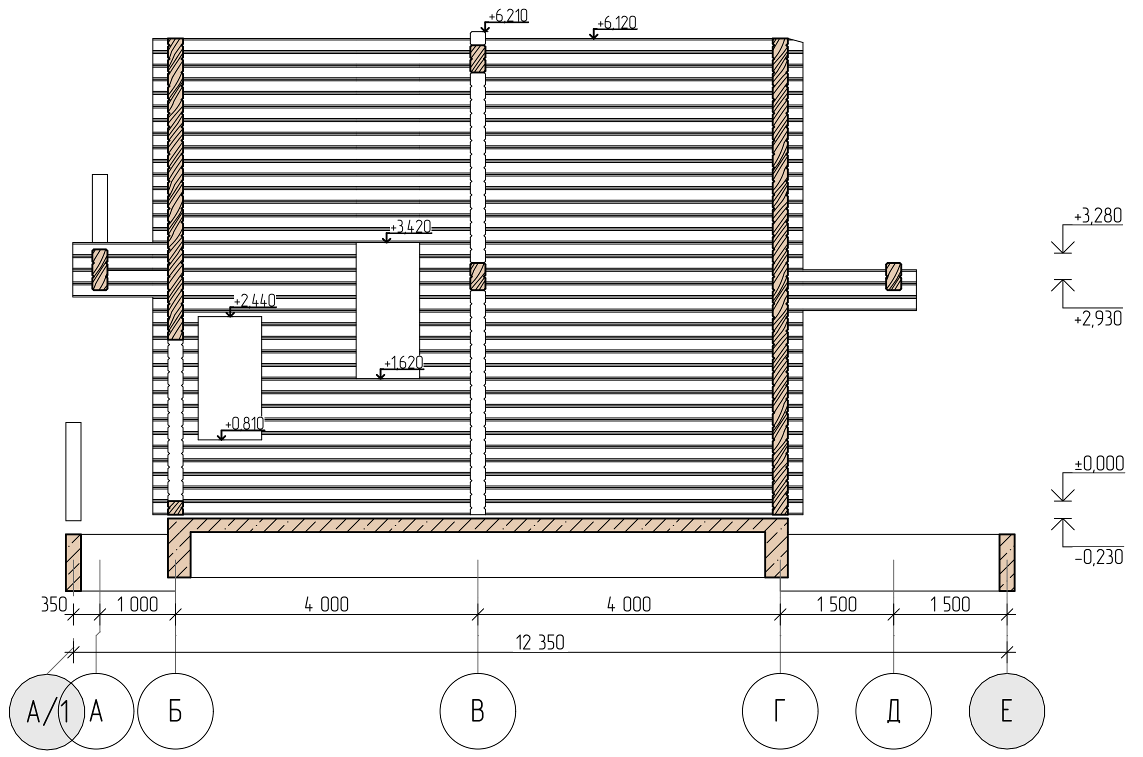

## Стена 2

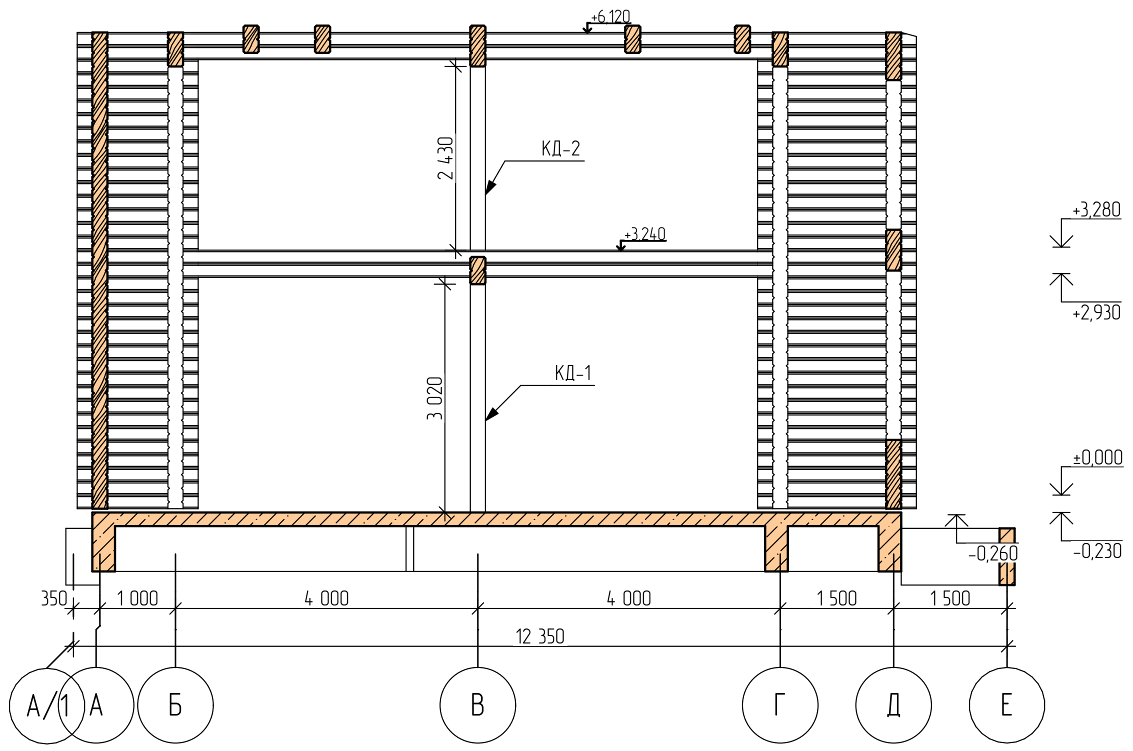

## Стена 3

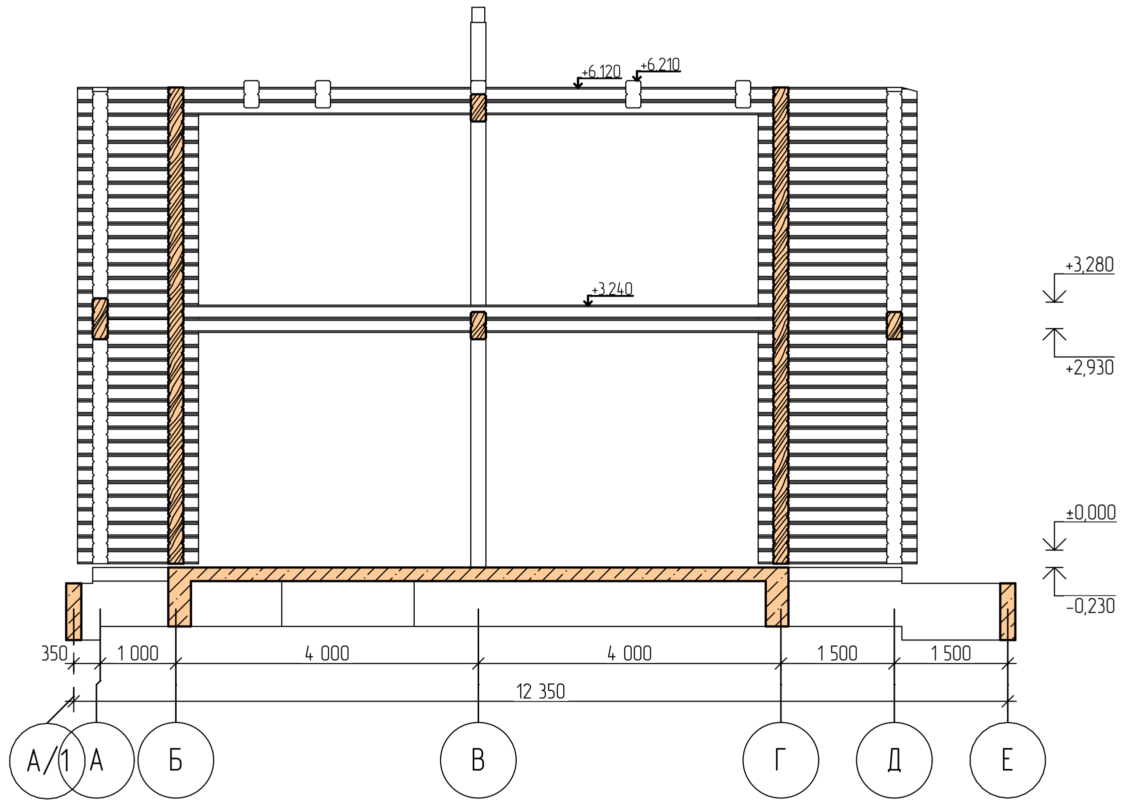

## Стена 4

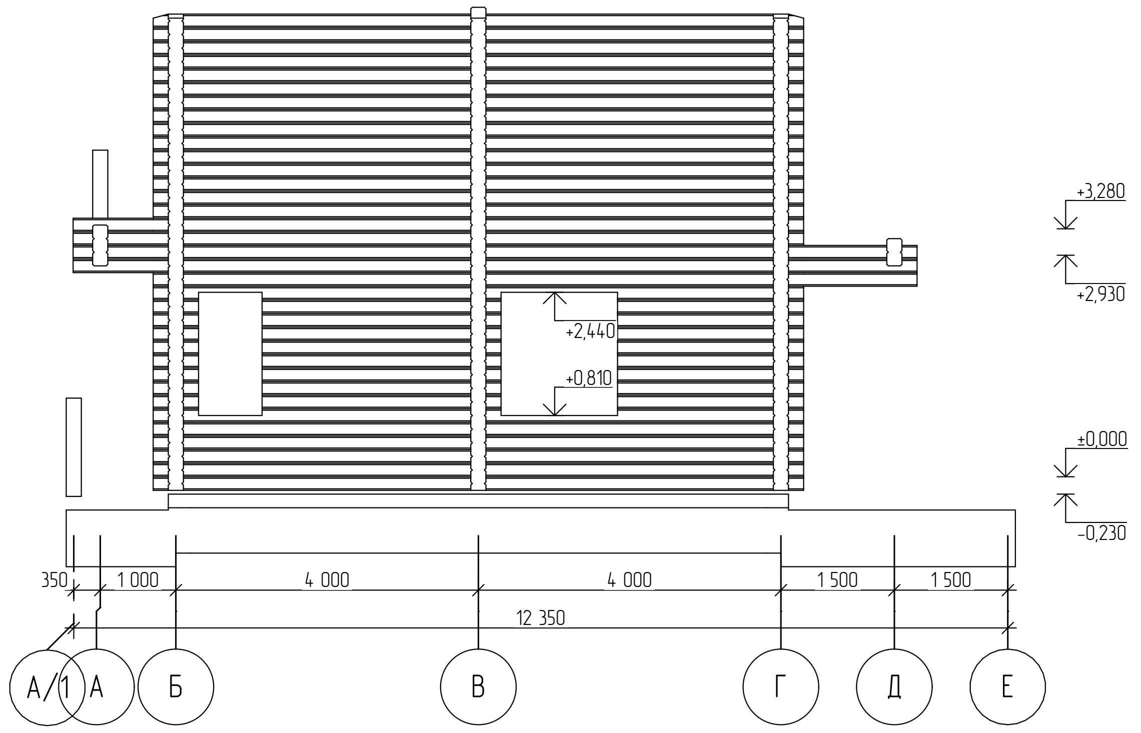

## Стена А

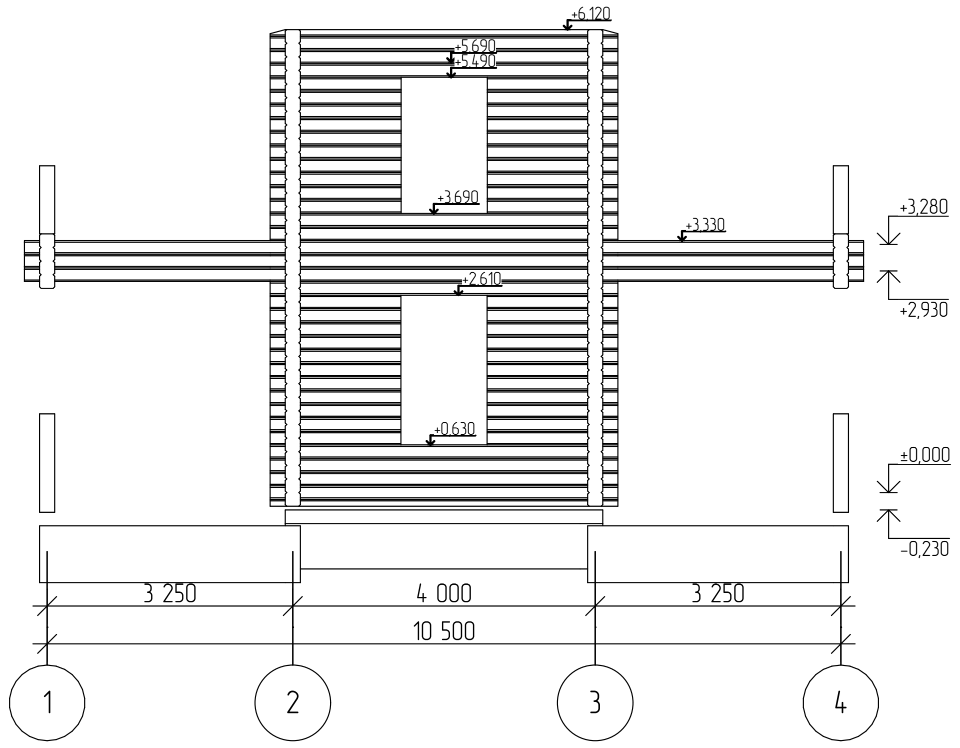

## Стена Б

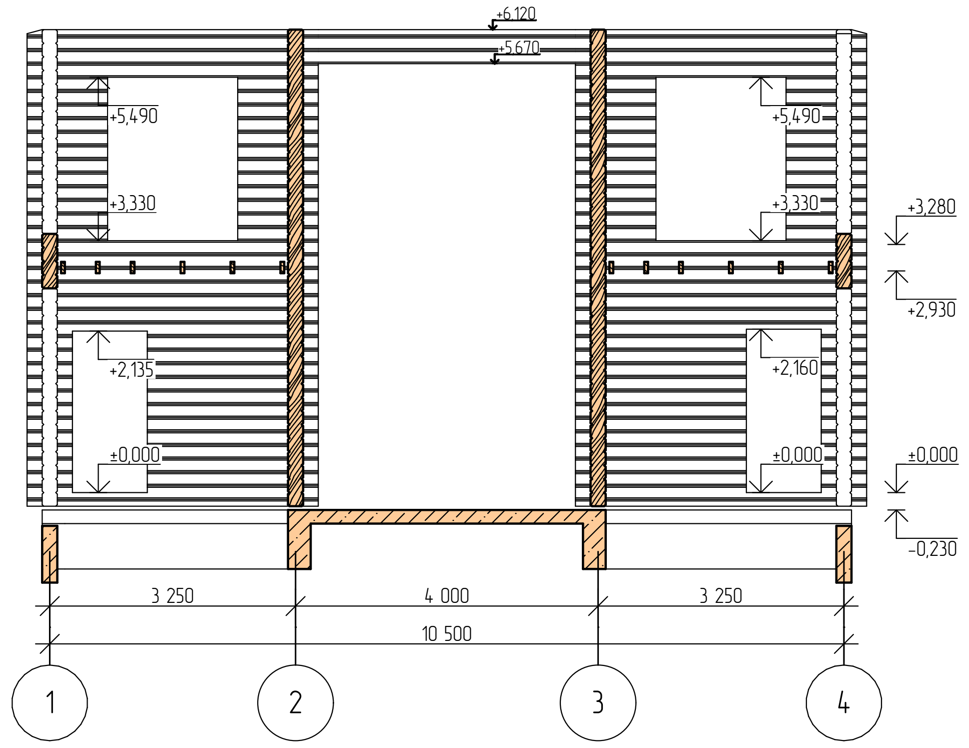

## Стена В

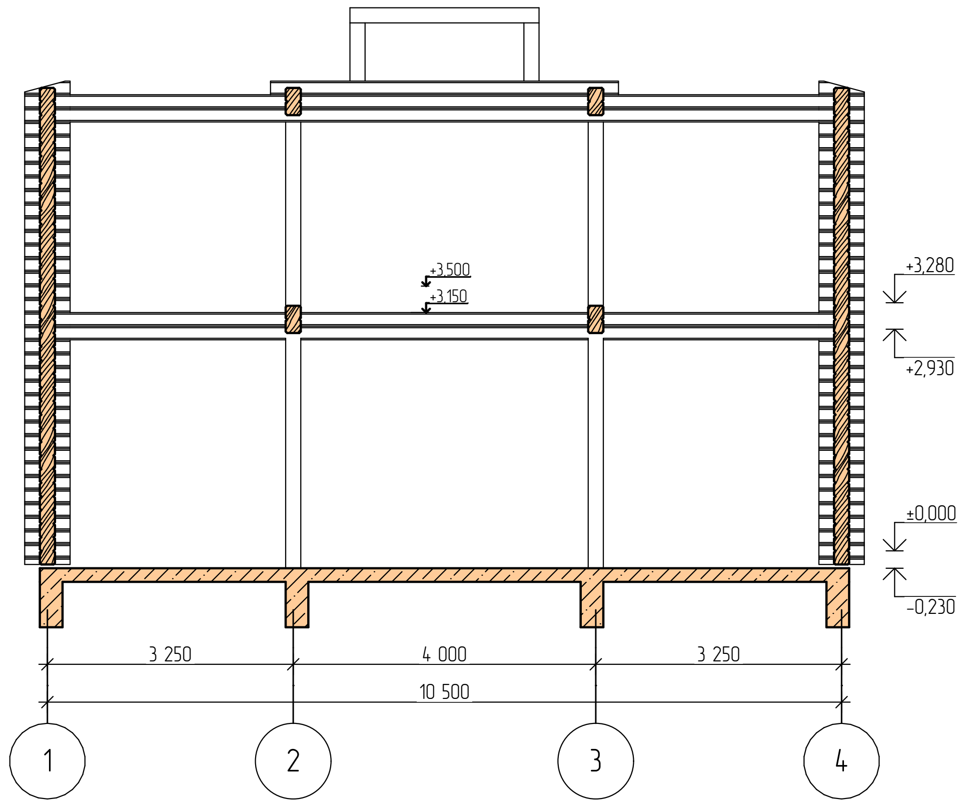

## Стена Г

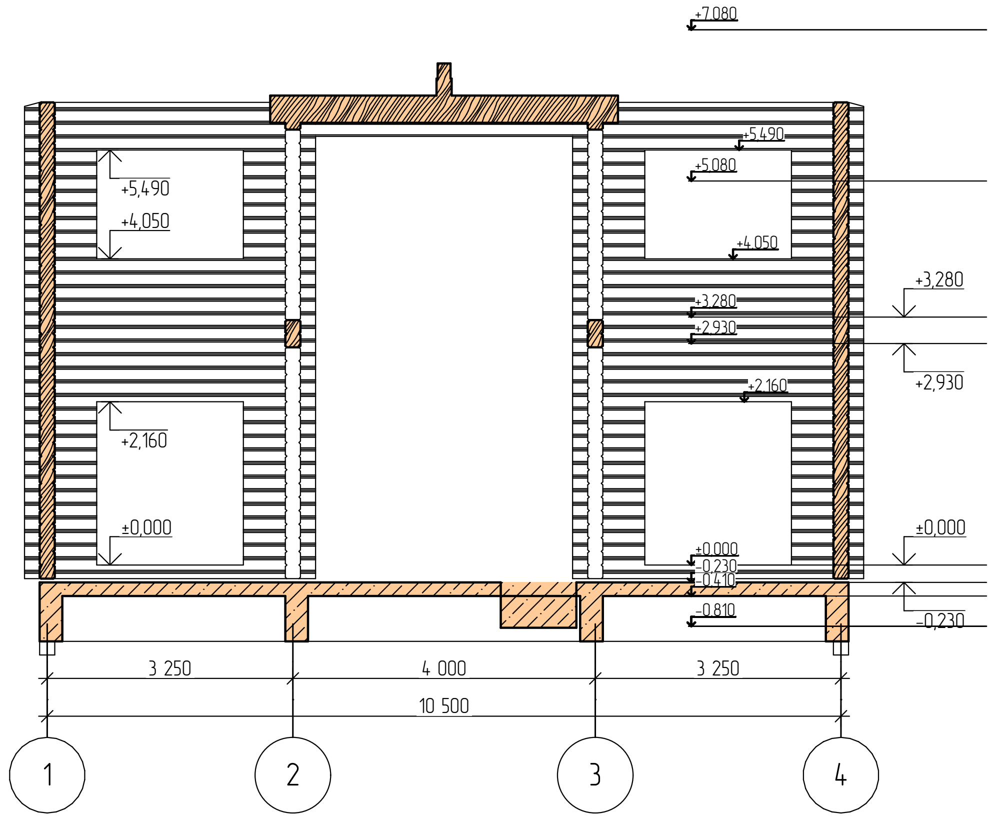

## Стена Д

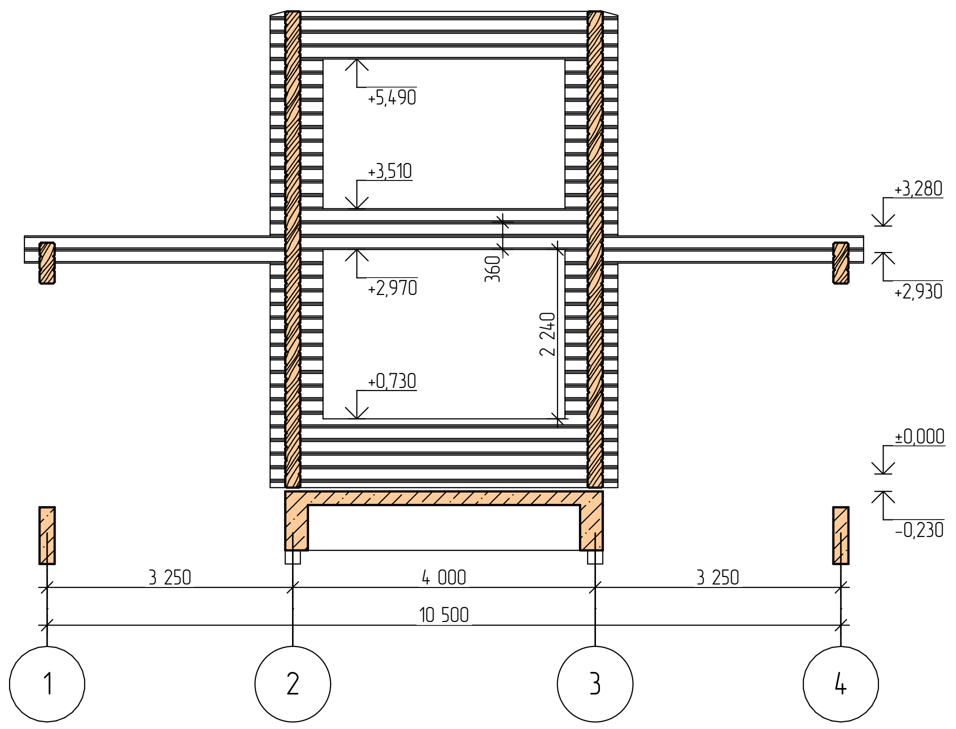

Согласовано

Взам. инв. №

Подпись и дата

Инв. № подл.

КД СТЕНЫ

Лист

КД_Кошелева_Людмила_3

Общий вид КД – 1

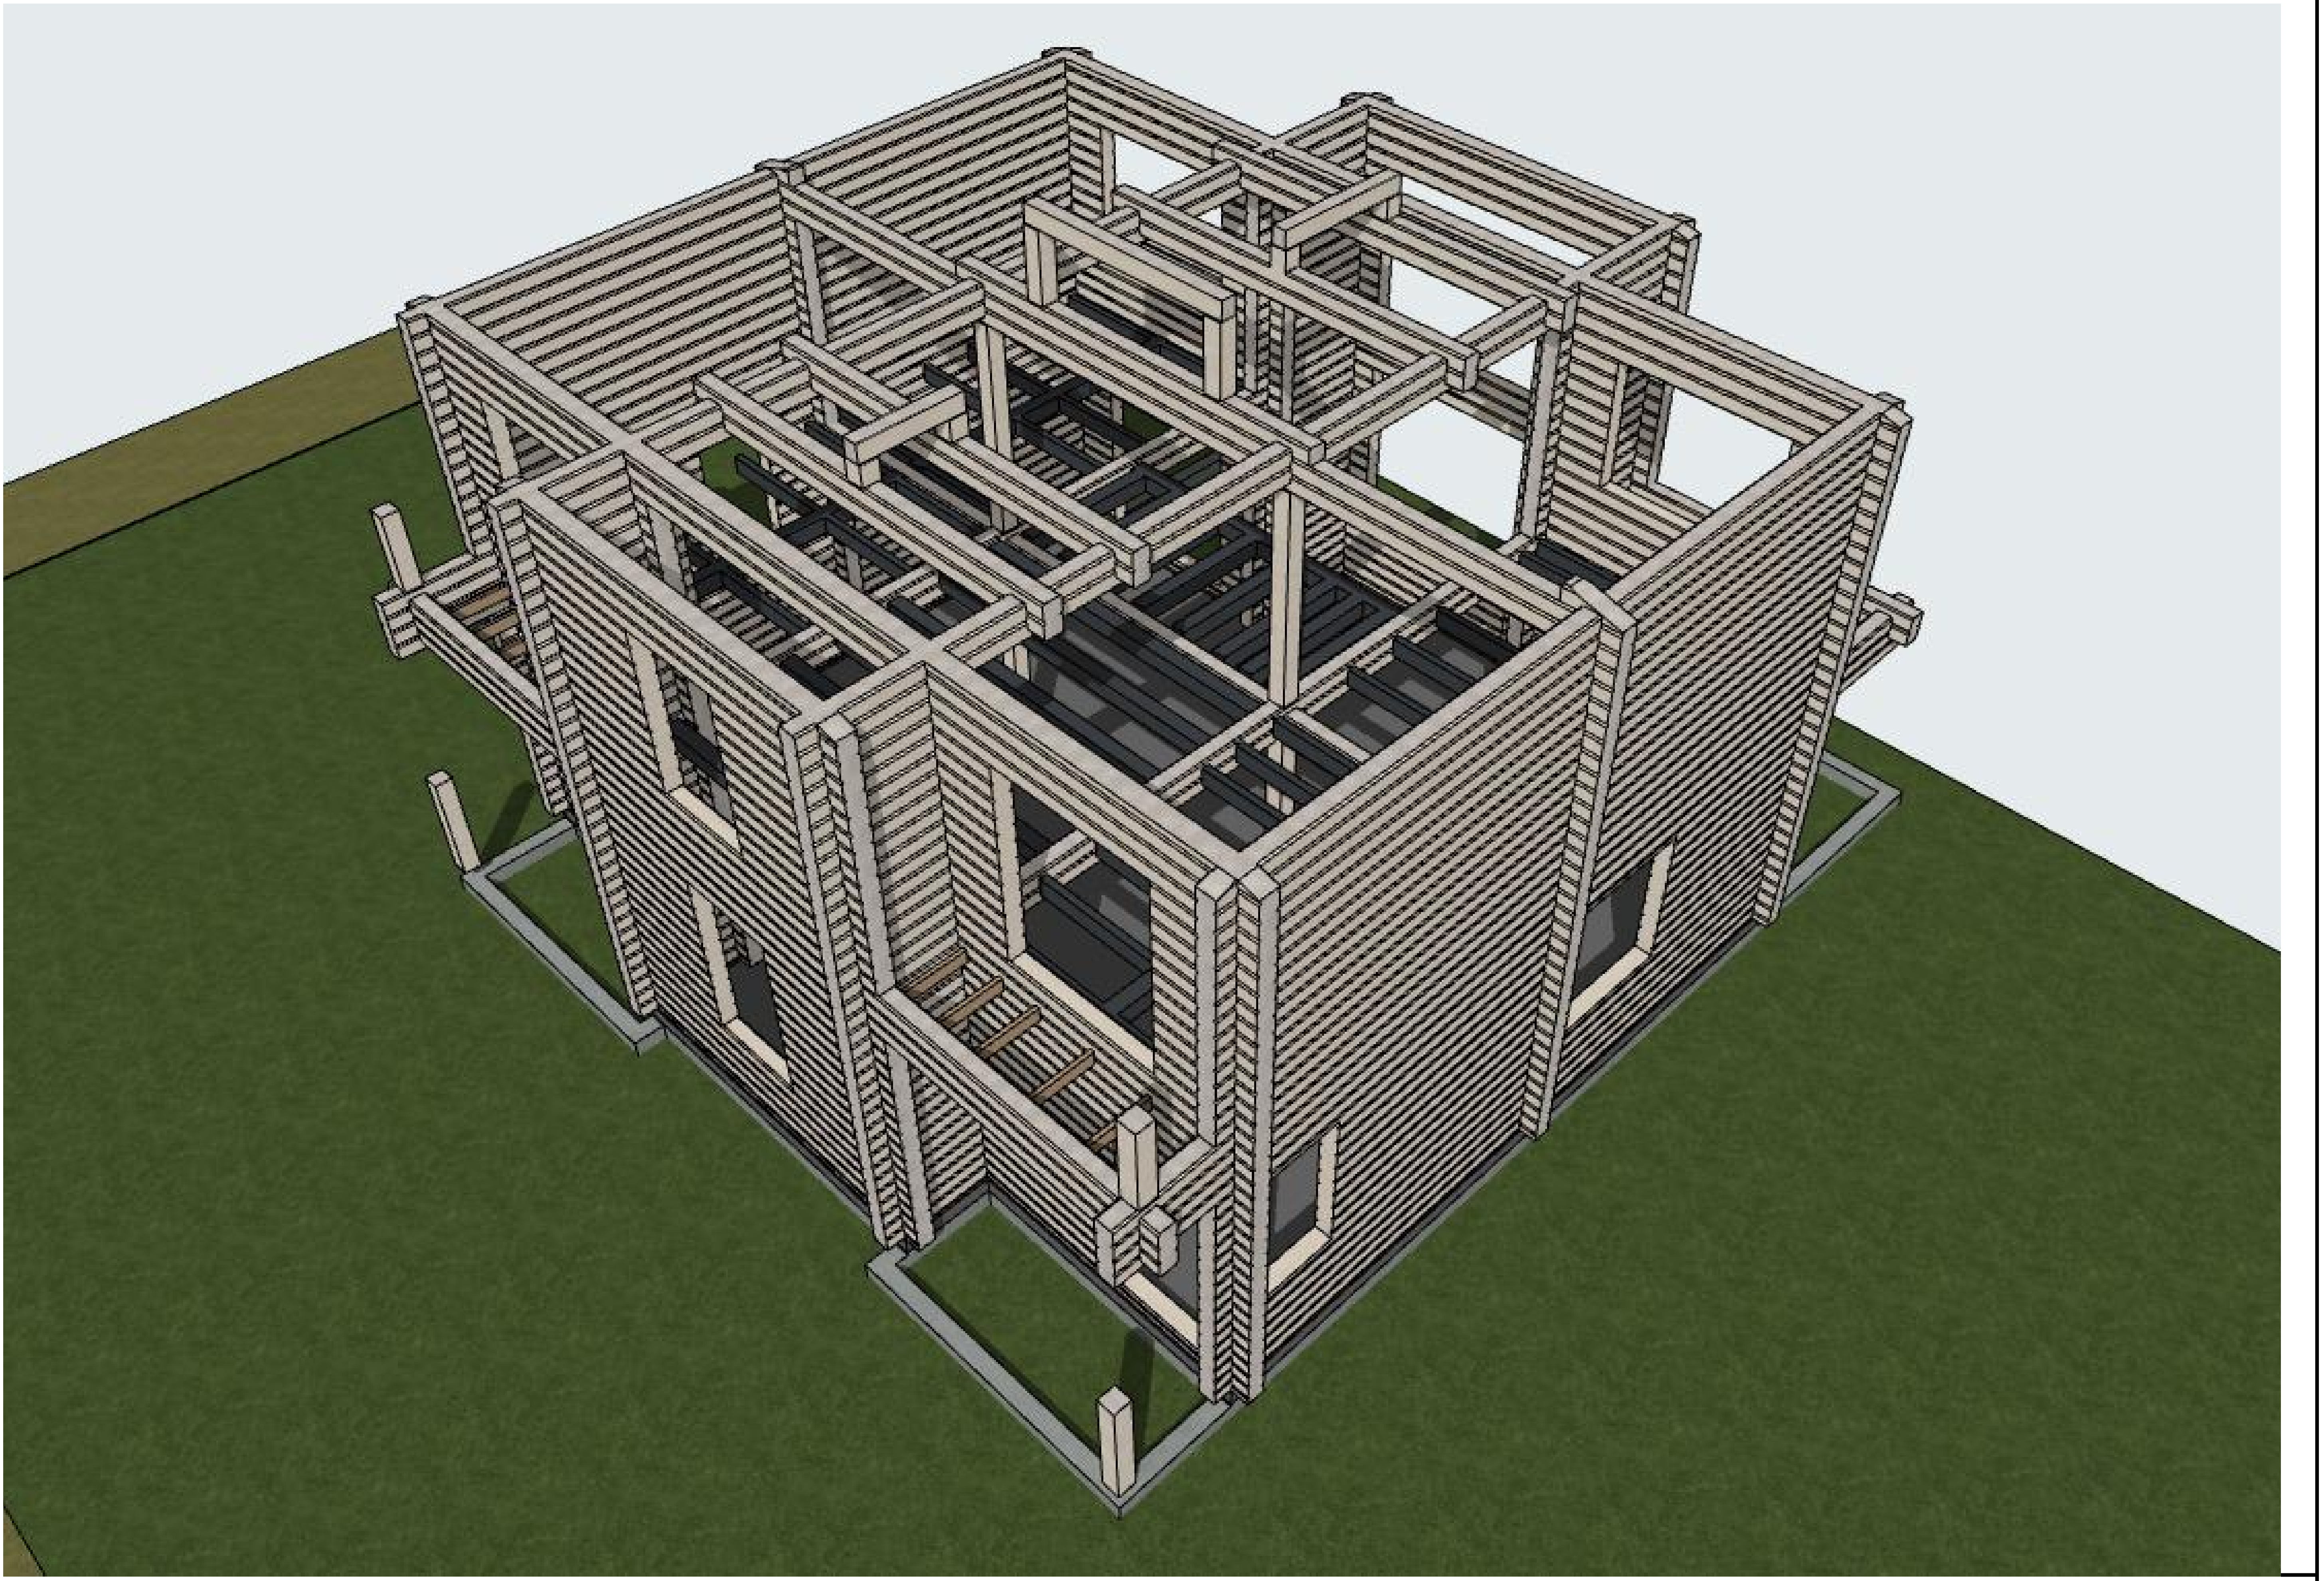

Согласовано

Взам. инв. №

Подпись и дата

Инв. № подл.

Общие виды

Вид 2

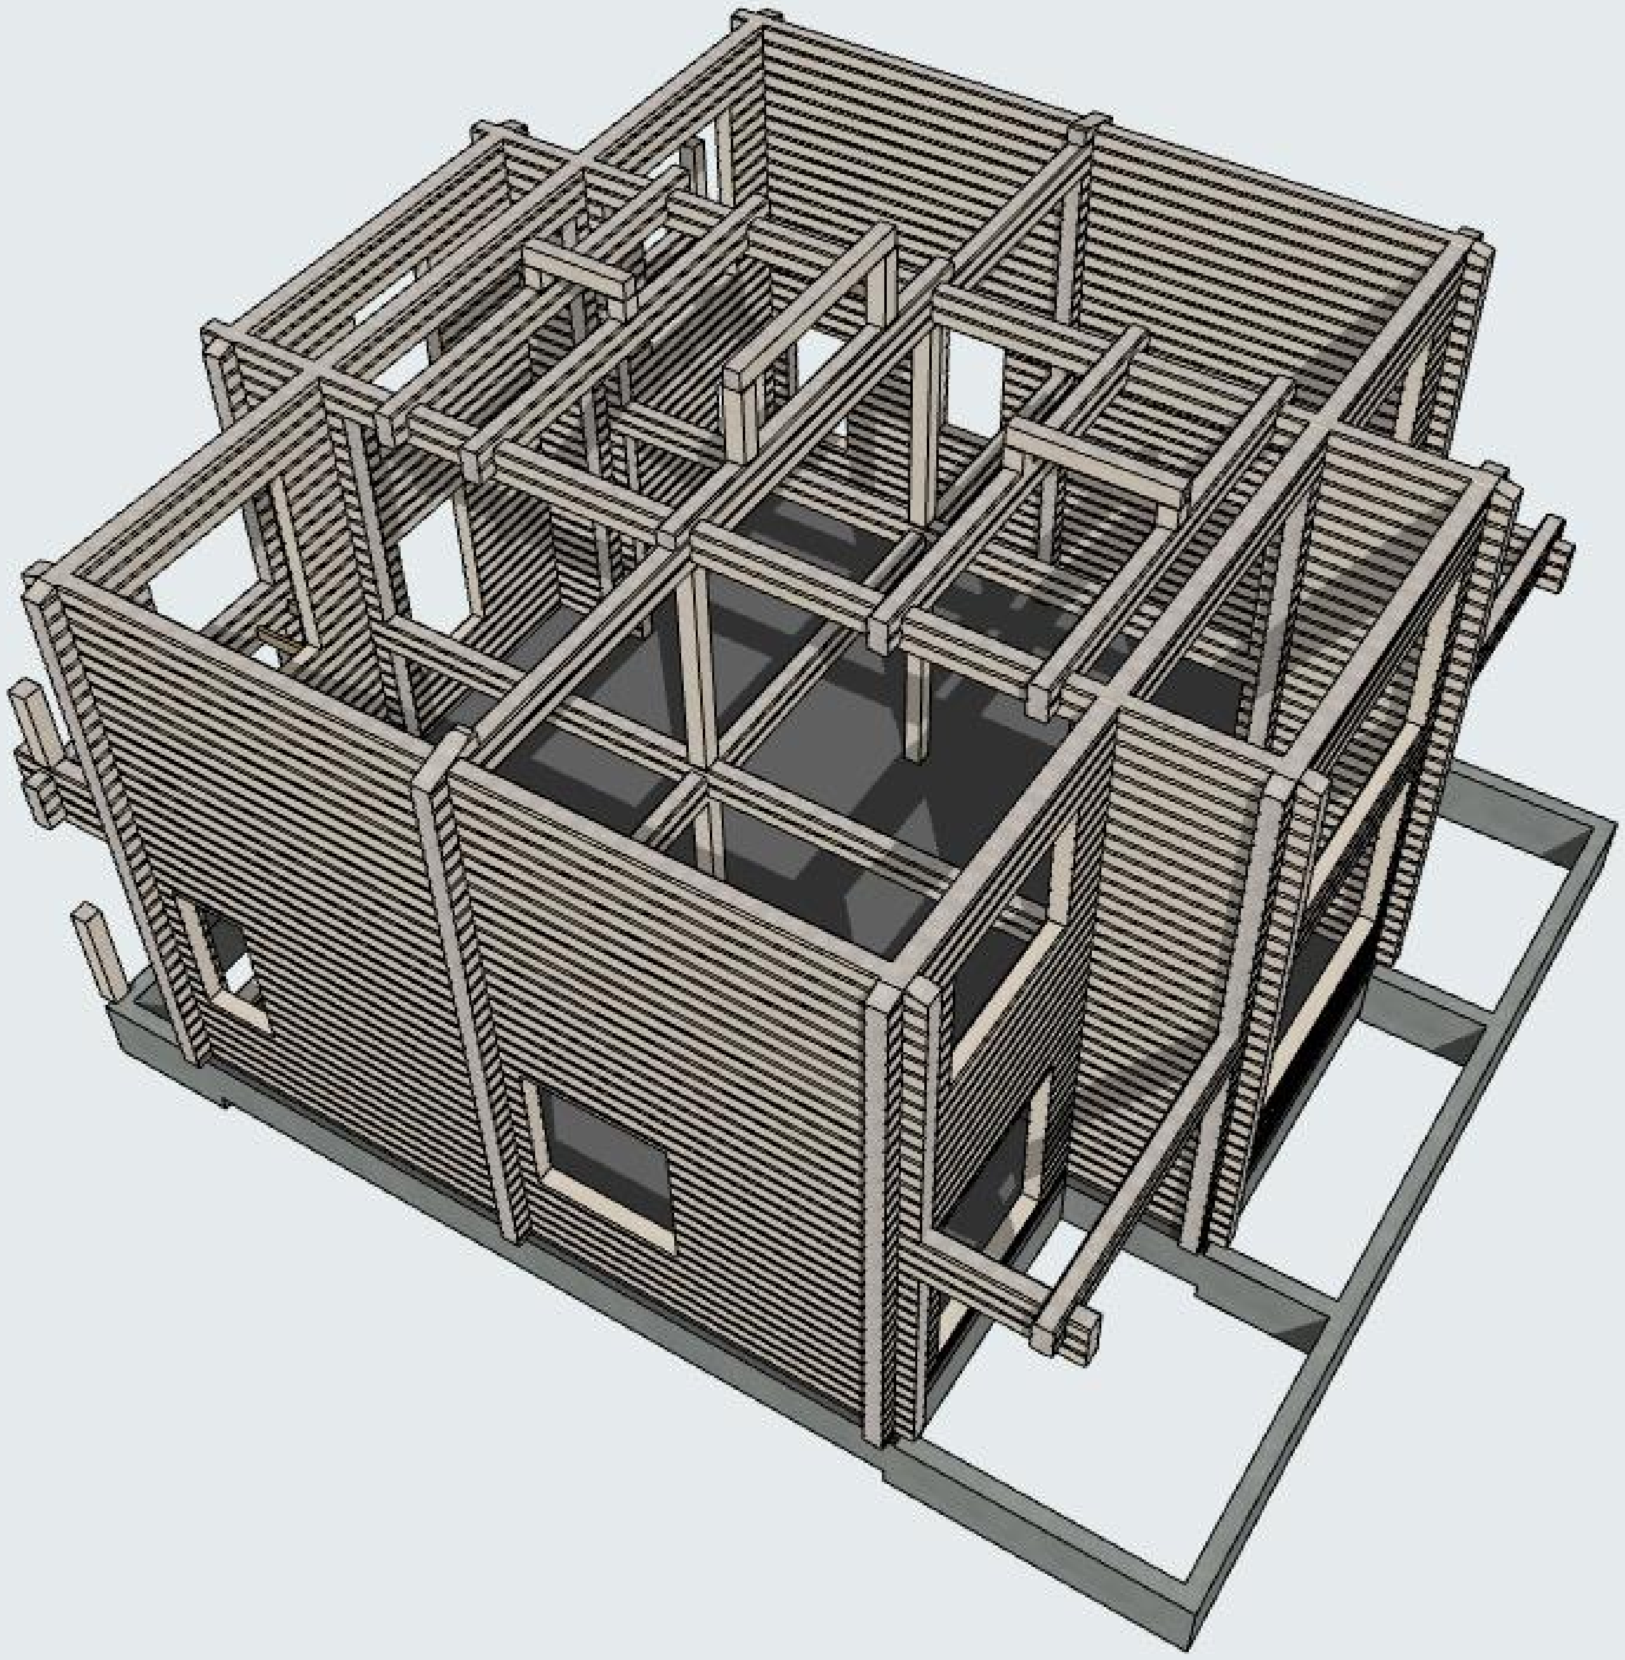

Согласовано

Взам. инв. №

Подпись и дата

Инв. № подл.

Общие виды

Лист
КД_Кошелева Людмила_5

Вид 3

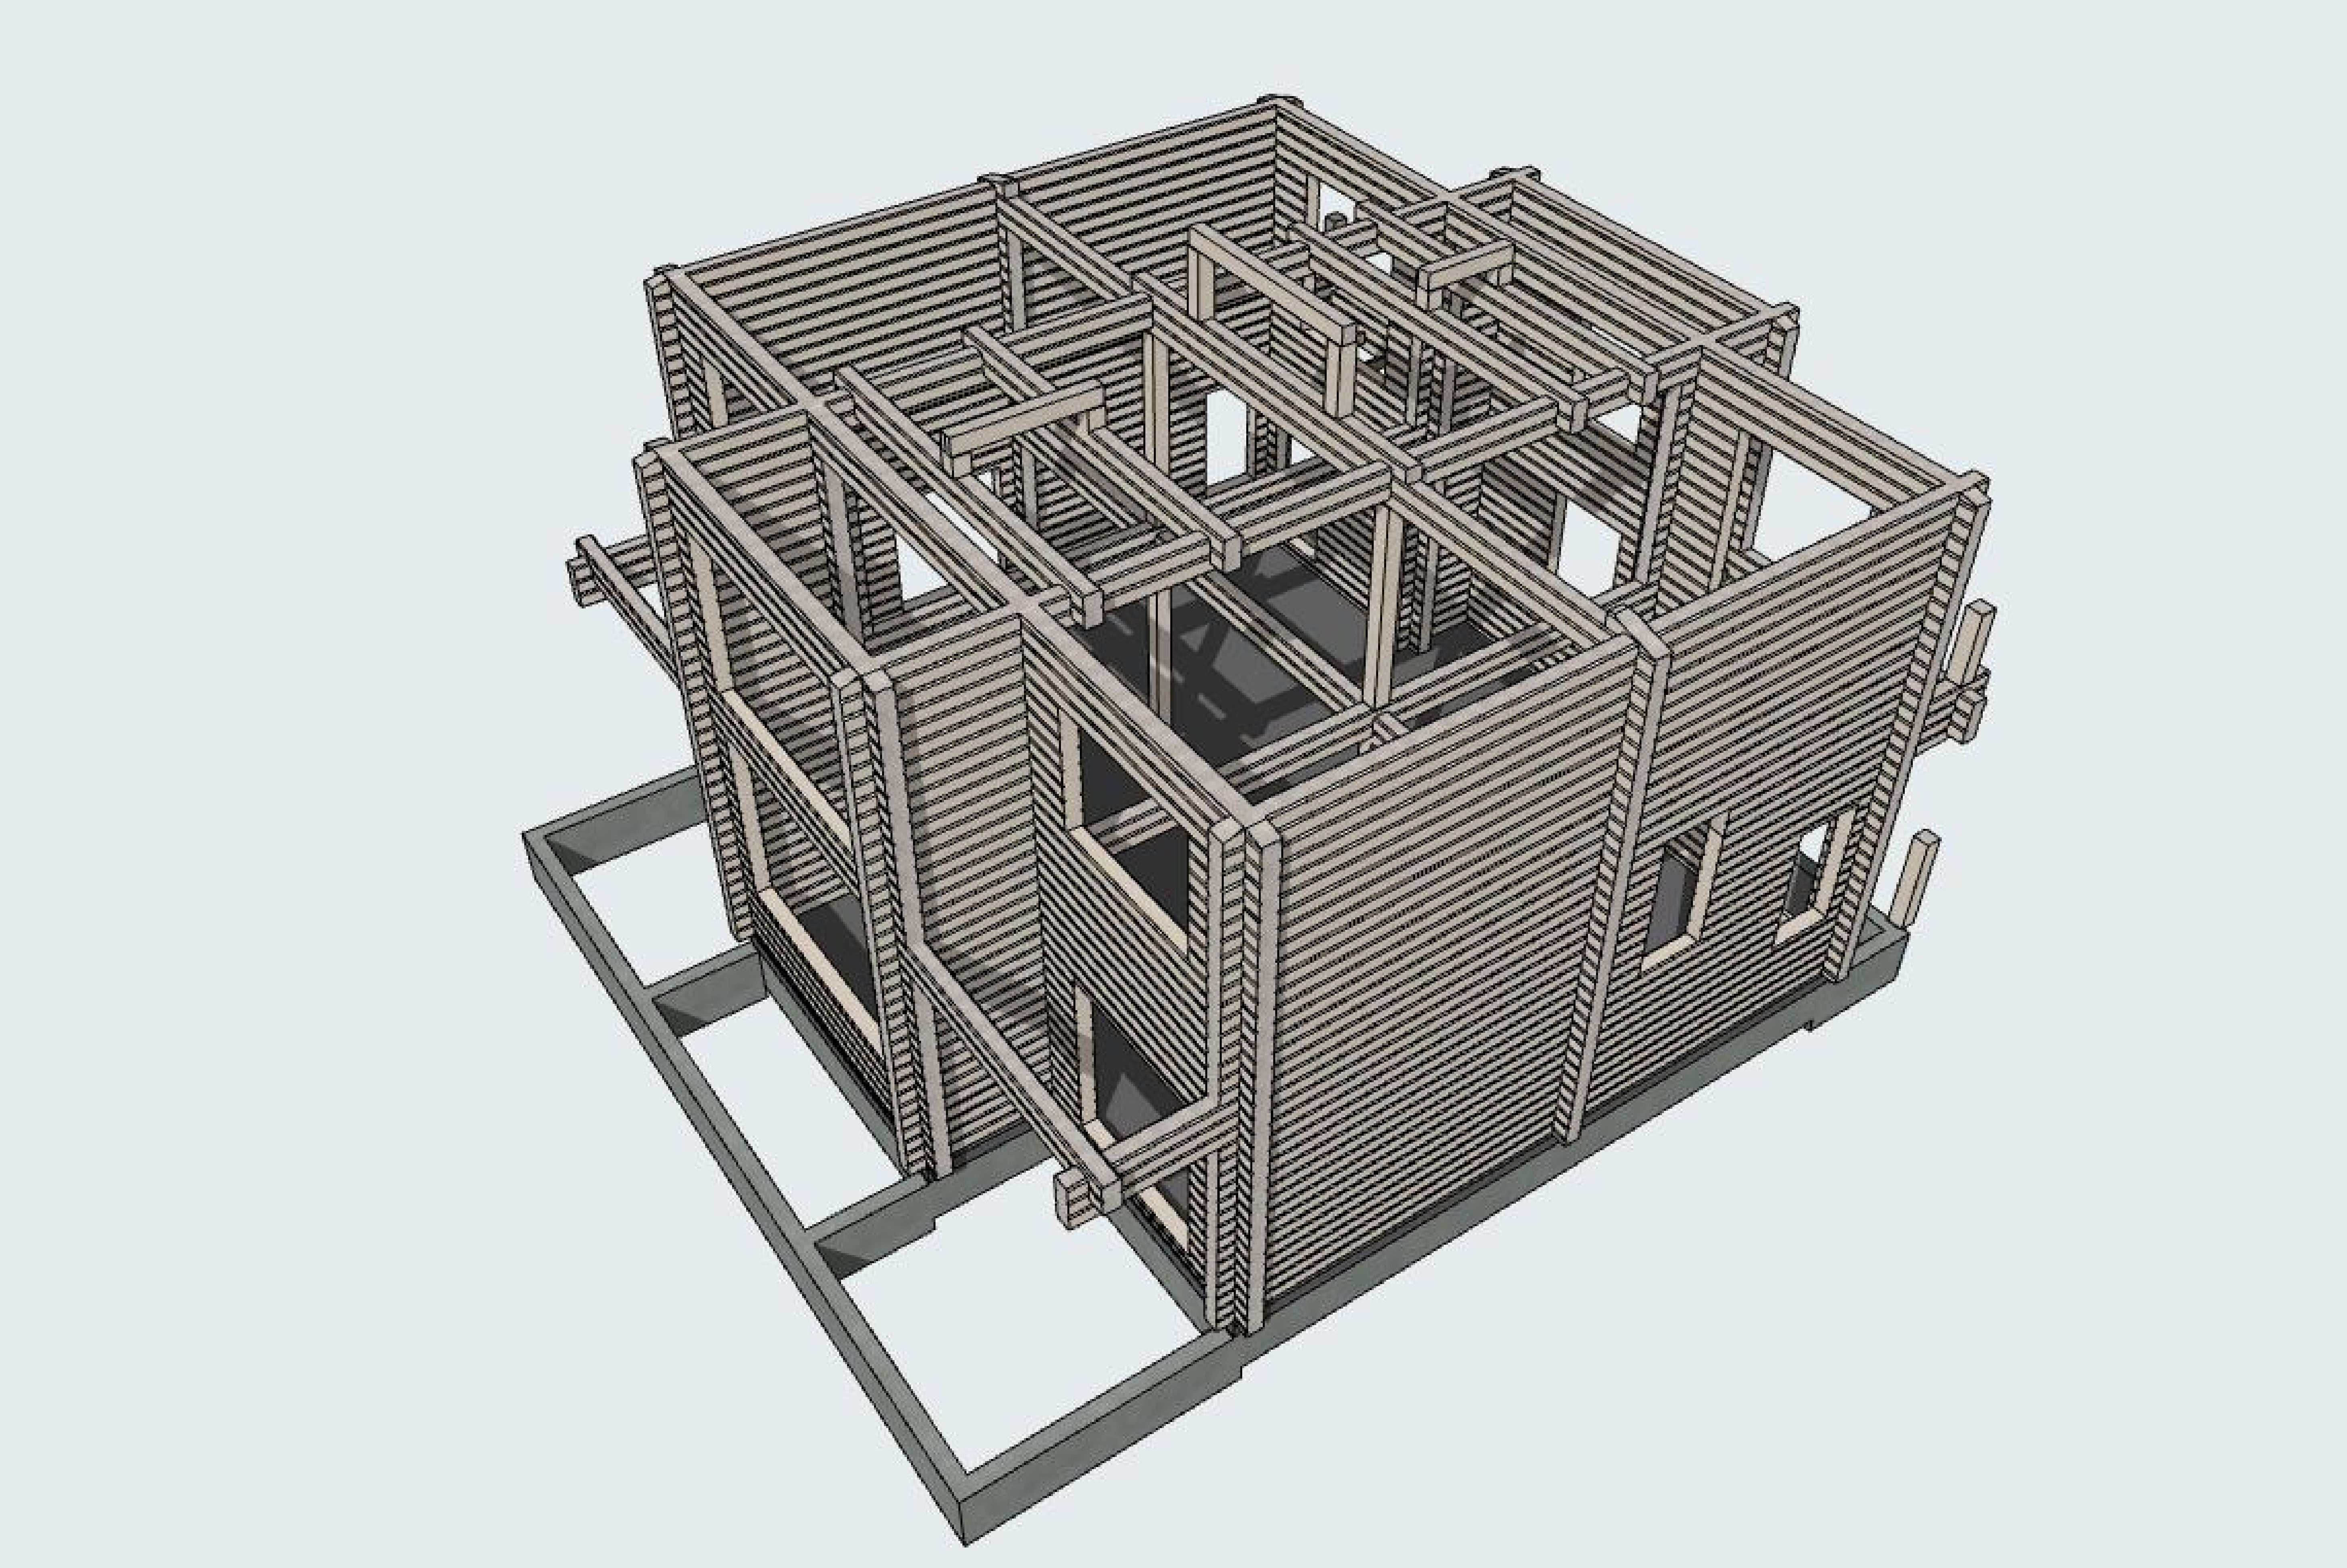

Согласовано

Взам. инв. №

Подпись и дата

Инв. № подл.

| | |
|---|---|
| Общие виды | Лист<br>КД_Кошелева Людмила_6 |

Вид 4

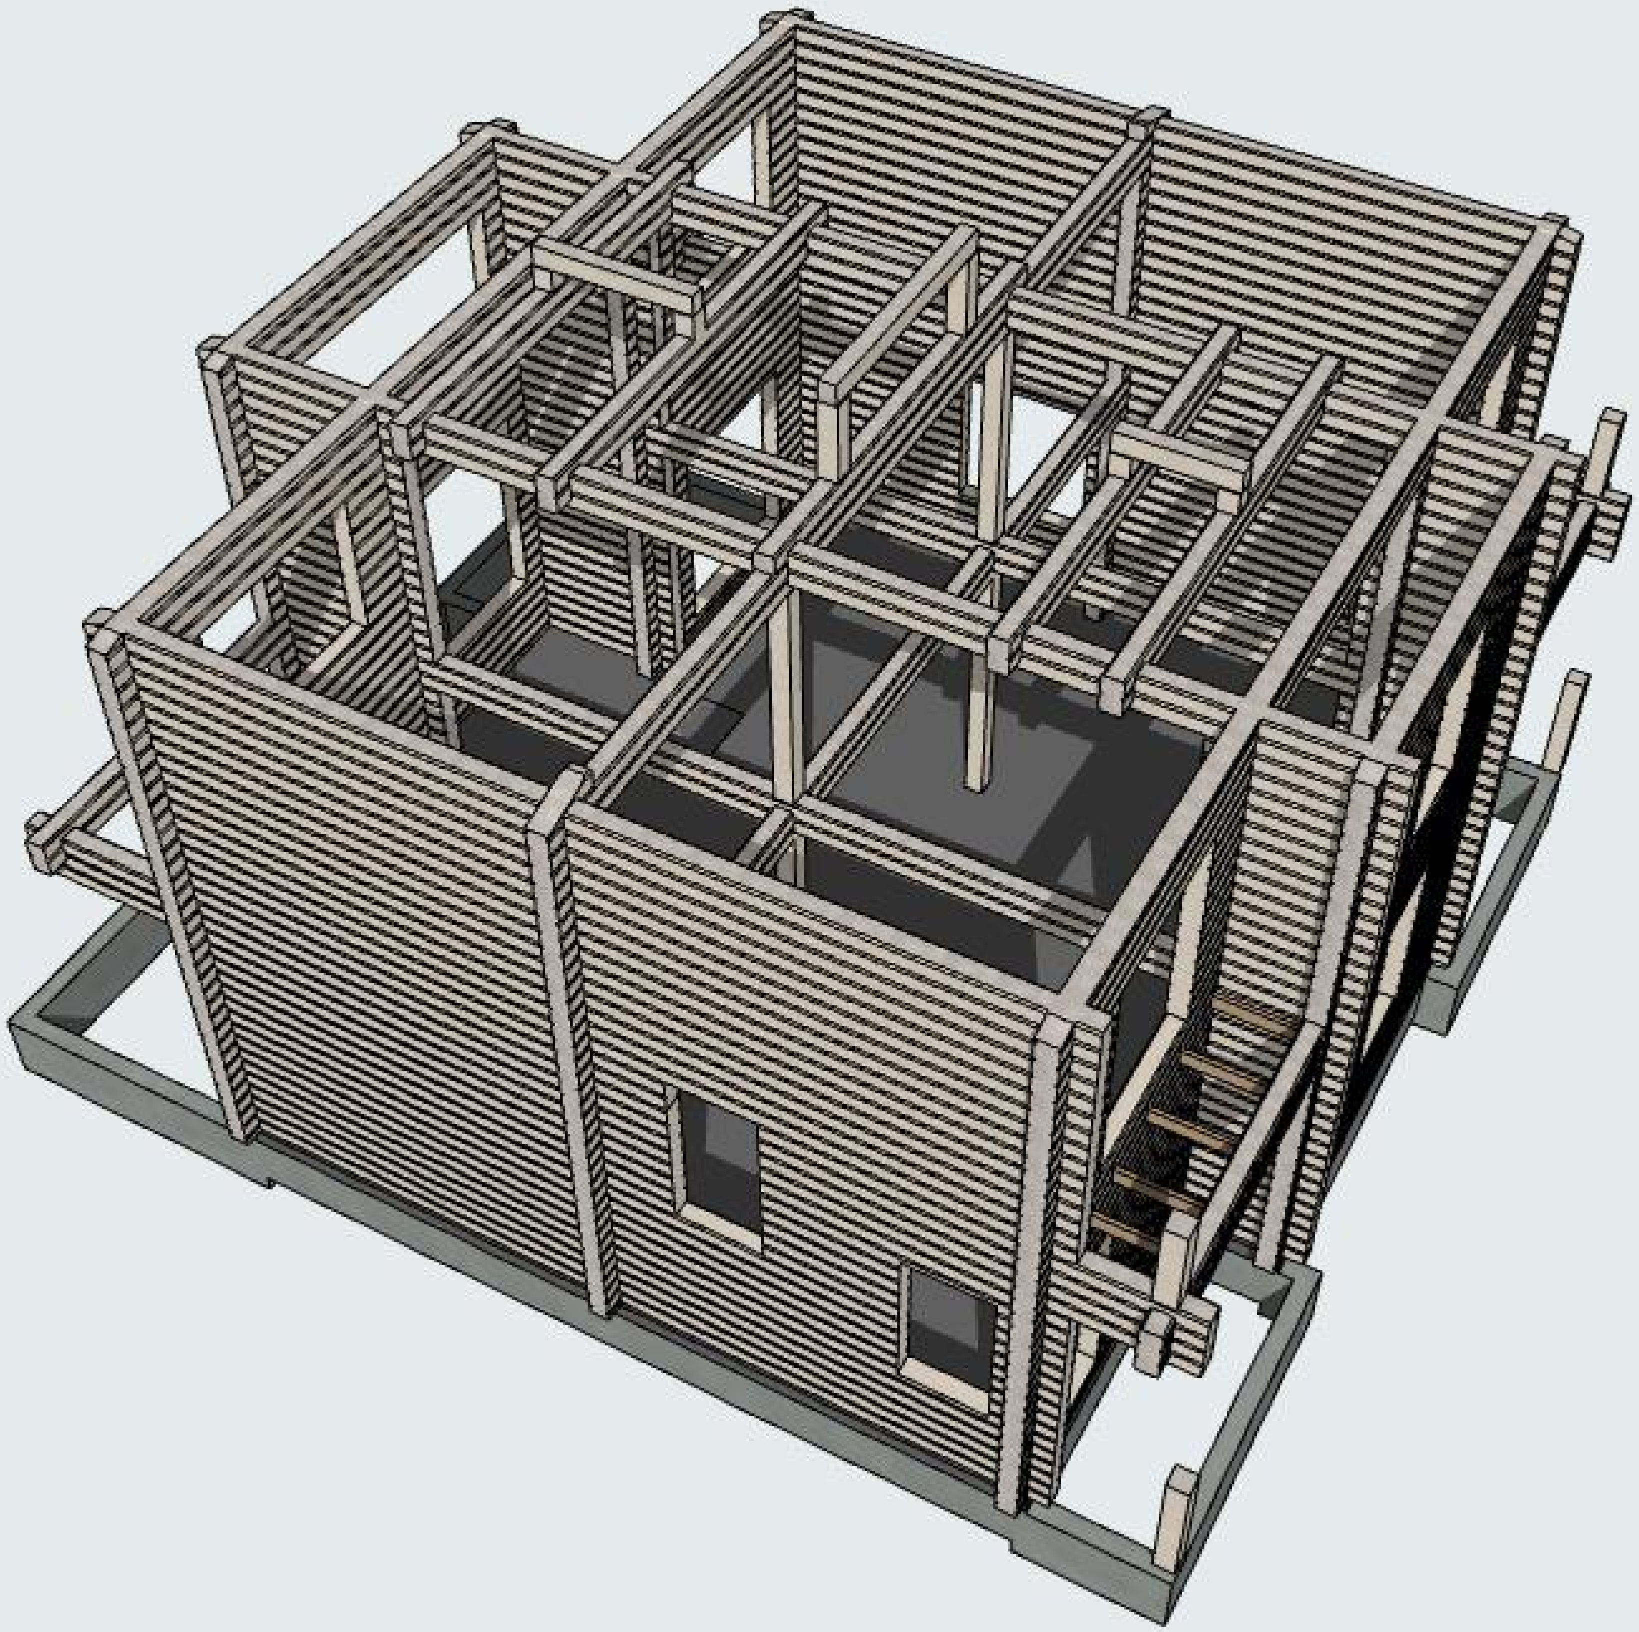

Согласовано

Взам. инв. №

Подпись и дата

Инв. № подл.

Общие виды

Лист
КД_Кошелева Людмила_
7