ОБЪЕКТ ИНДИВИДУАЛЬНОГО ЖИЛИЩНОГО СТРОИТЕЛЬСТВА



РАБОЧИЙ ПРОЕКТ

ШИФР: #ID ПРОЕКТА

АРХИТЕКТУРНЫЕ РЕШЕНИЯ

САНКТ-ПЕТЕРБУРГ 2020

ОБЪЕКТ: ОБЪЕКТ ИНДИВИДУАЛЬНОГО ЖИЛИЩНОГО СТРОИТЕЛЬСТВА

ПО АДРЕСУ: #ПОЛНЫЙ АДРЕС УЧАСТКА; К/Н: #ID УЧАСТКА

ЗАКАЗЧИК: _____#ОБРАЩЕНИЕ К ЗАКАЗЧИКУ

АРХИТЕКТОР _____САЛЫКОВА В.Г.

КОНСТРУКТОР _____

РАБОЧИЙ ПРОЕКТ

ШИФР: #ID ПРОЕКТА

АРХИТЕКТУРНЫЕ РЕШЕНИЯ

САНКТ-ПЕТЕРБУРГ 2020

Согласовано:

Взам. инв. №

Подпись и дата

Инв. № подл.

Ведомость чертежей

Лист	Наименование	Примечание
	Обложка	
	Титульный лист	
2	Общие данные (начало)	
3	Общие данные (окончание)	
4	Схема организации участка М 1:250	
5	План 1 этажа с расстановкой мебели М 1:100	
6	План 2 этажа с расстановкой мебели М 1:100	
7	Разрез 1-1 М 1:100	
8	Разрез 2-2 М 1:100	
9	Разрез 3-3 М 1:100	
10	Фасады М 1:100	
11	Фасады М 1:100	
12	План фундамента М 1:100	
13	План ЖБ плиты	
14	План ЖБ плиты с закладными	
15	Подкладочный ряд М 1:100	
16	План раскладки балок межэтажного перекрытия М 1:100	
17	План 1 этажа с размерами М 1:100	
18	План 2 этажа с размерами М 1:100	
19	Маркировочный план 1 этажа М 1:100	
20	Маркировочный план 2 этажа М 1:100	
21	План кровли М 1:100	
22	Общий вид крыши	
23	Спецификация заполнения оконных проёмов	
24	Спецификация заполнения дверных проёмов	
25	Общие виды	
26	Общие виды	
27	Общие виды	
28	Общие виды	
29	Общие виды 1 этаж	
30	Общие виды 2 этаж	

Пояснительная записка /начало/

Проект разработан на основании техзадания, предоставленного заказчиком, соответствует установленным общегосударственным нормам и требованиям помалоэтажному строительству в соответствии со СП 55.13330.2011 "Дома жилые одноквартирные". Актуализированная редакция СНиП 31-02-2001; СП 131.13330.2018 "Строительная климатология", ГОСТ 21.501-2011 "Система проектной документации для строительства. Правила выполнения рабочей документации архитектурных и конструктивных решений". СП 63.13330.2012 «Бетонные и железобетонные конструкции», СП 64.13330.2017 "Деревянные конструкции", ГОСТ 8486-86 "Пиломатериалы хвойных пород"

Нормативное значение равномено-распределенной временной нагрузки на перекрытие согласно СП 20.13330.2016 «Нагрузки и воздействия» равно 150,0кг/м2.

Производство работ должно выполняться в строгом соответствии с тербованиями Подрядчика.
Обязательно выполнение работ по водоотведению - дренажных работ с монтажом смотровых колодцев, отмостки и других работ, направленных на отведение воды от пятна застройки. Выполняется в объеме, определенном сметой.

Гарантия на фундаментные работы осуществляется только при условии надлежащей системы водоотведения и ее эксплуатации.

Данные о фактических размерах участка, габаритов его границ, наличие заборов, крупных растений, близость соседских построек, различных ограничений, схемы с точной привязкой их расположения на территории участка предоставляет заказчик. Точность вышеописанных сведений лежит на Заказчике. Подрядчиком не проводятся работы по межеванию и он основывается на данных, предоставленных Заказчиком.

Характеристика проектируемого объекта:

- этажность - 2 этажа
- класс функциональной пожарной опасности здания - Ф 1,4 (по СП 112.13330.2011)

Строительно-климатический район IIВ в соответствии с СП 131.13330.2018 со следующими характеристиками условий:
- температура наружного воздуха наиболее холодных суток - -32оС
- температура наружного воздуха наиболее холодной пятидневки - -28оС
- рассчетная снеговая нагрузка по району - 180кг/м2
- нормативное давление ветра - 23кгс/м2

					2020	#ID Проекта
						Адрес: #Полный Адрес Участка
Изм.	Кол.уч	Лист	№док.	Подпись	Дата	
						Индивидуальный жилой дом
Архитектор		Салыкова В.Г.				
Конструктор						Общие данные (начало)
Заказчик		#Обращение к Заказчику				

стадия	лист	листов
РП	2	

Пояснительная записка /окончание/

Архитектурно-планировочные решения:

Проектируемый коттедж одноквартирный, двухэтажный . Размеры в осях 12,35х10,5 м.

На первом этаже дома размещаются помещения: тамбур, холл, котельная(электричество), санузел, кухня, гостиная, лестничная площадка, 2 крыльца, терраса.

На втором этаже размещаются: 3 спальных комнаты, холл, 1 с/у, холл, 2 балкона.

Дом без чердака.

За отм. 0,000 принят уровень чистого пола первого этажа дома.

За отм. 3,280 принят уровень чистого пола второго этажа дома.

Покрытие кровли - согласно смете.

Водосточная система - водосточные трубы и желоба , цвет индивидуальный.

Окна - ПВХ или деревянные, 2- камерные стеклопакеты, индивидуального изготовления.

Двери наружные - металлические, сендвич, внутренняя сторона МДФ или индивидуального изготовления.

Двери внутренние - деревянные по индивидуальному проекту.

Отмостка -утепленная, бетонная толщ.100мм из бетона Кл.В7.5 по гравийно-песчаному основанию шириной 1000мм.

Конструктивные решения:

Фундамент представляет собой монолитную железобетонную ленту толщ. 300мм, высотой 600мм на песчанной подушке 250мм, заглубленный по проекту. На террасе/крыльце ЖБ лента 200х750(h)мм

Полы первого этажа перекрытия выполнены по деревянным балкам с шагом согласно проекту. Полы террасы/крыльца выполнены по деревянным балкам с шагом согласно проекту.

Несущие стены из клееного профилированного бруса 200х190(180)(h)мм. Материал строительства - клееный брус соответствует техническим условиям, опряделяемыми строительной компанией подрядчиком.

Номинальные, проектные линейные и высотные размеры строения могут отличаться от фактических в силу технических и технологических особенностей, выполняемых работ и применяемых материалов, технологической усадки стенового комплекта, нормативных допусков и отклонений от предельных размеров строения и материалов в частности, сезонности и влажности, погодных явлений и других обстоятельств.

Номинальные и проектные размеры отдельных применяемых материалов могут отличаться в силу характера их применения, естественной реакции на окружающую среду, способ применения, технических и технологических допусков и т.д.

Перегородки - деревянный каркас - стойки с шагом 600мм, между ними расположен утеплитель. Внешняя и внутренняя обшивка имитацией бруса, во влажных помещениях отделка влагостойким ГВЛ, либо иными материалами по согласованию сторон.

Крыша - двускатная из деревянных наслонных стропил с обрешеткой, покрытие согласно смете. Между стропилами укладывается утеплитель толщ.200мм.

Стропила- сухая строганая доска 40х180мм.

Материалы, технология работ и способы исполнения, гарантийные обязательства, способы эксплуатации и другое, связанное с использованием строения, а также его монтажом регулируется ТУ 16.23.19-001-17010764-2018

ТЕХНИКО-ЭКОНОМИЧЕСКИЕ ПОКАЗАТЕЛИ:

Наименование	Ед.изм.	Количество
Площадь застройки	$м^2$	156,75
Площадь общая, включая террасы, балконы	$м^2$	196,21
Площадь жилая	$м^2$	68,07
Строительный объем	$м^3$	627,23

*Площадь помещений указана без учета отделочных материалов и понижающего коэффициента

Проект строительства жилого дома разработан в соответствии с действующими строительными, технологическими и санитарными нормами и правилами, предусматривает мероприятия, обеспечивающие конструктивную надежность, врзрывопожарную и пожарную безопасность объекта, защиту окружающей природной среды при его эксплуатации и отвечает требованиям законодательства Российской Федерации в области капитального строительства.

Архитектор проекта _____ Салыкова В.Г.

Согласовано:


Взам. инв. №


Подпись и дата

Инв. № подл.

					2020	#ID Проекта
						Адрес: #Полный Адрес Участка
Изм.	Кол.уч	Лист	№док.	Подпись	Дата	
						Индивидуальный жилой дом
Архитектор		Салыкова В.Г.				
Конструктор						Общие данные (окончание)
Заказчик		#Обращение к Заказчику				

стадия	лист	листов
РП	3	

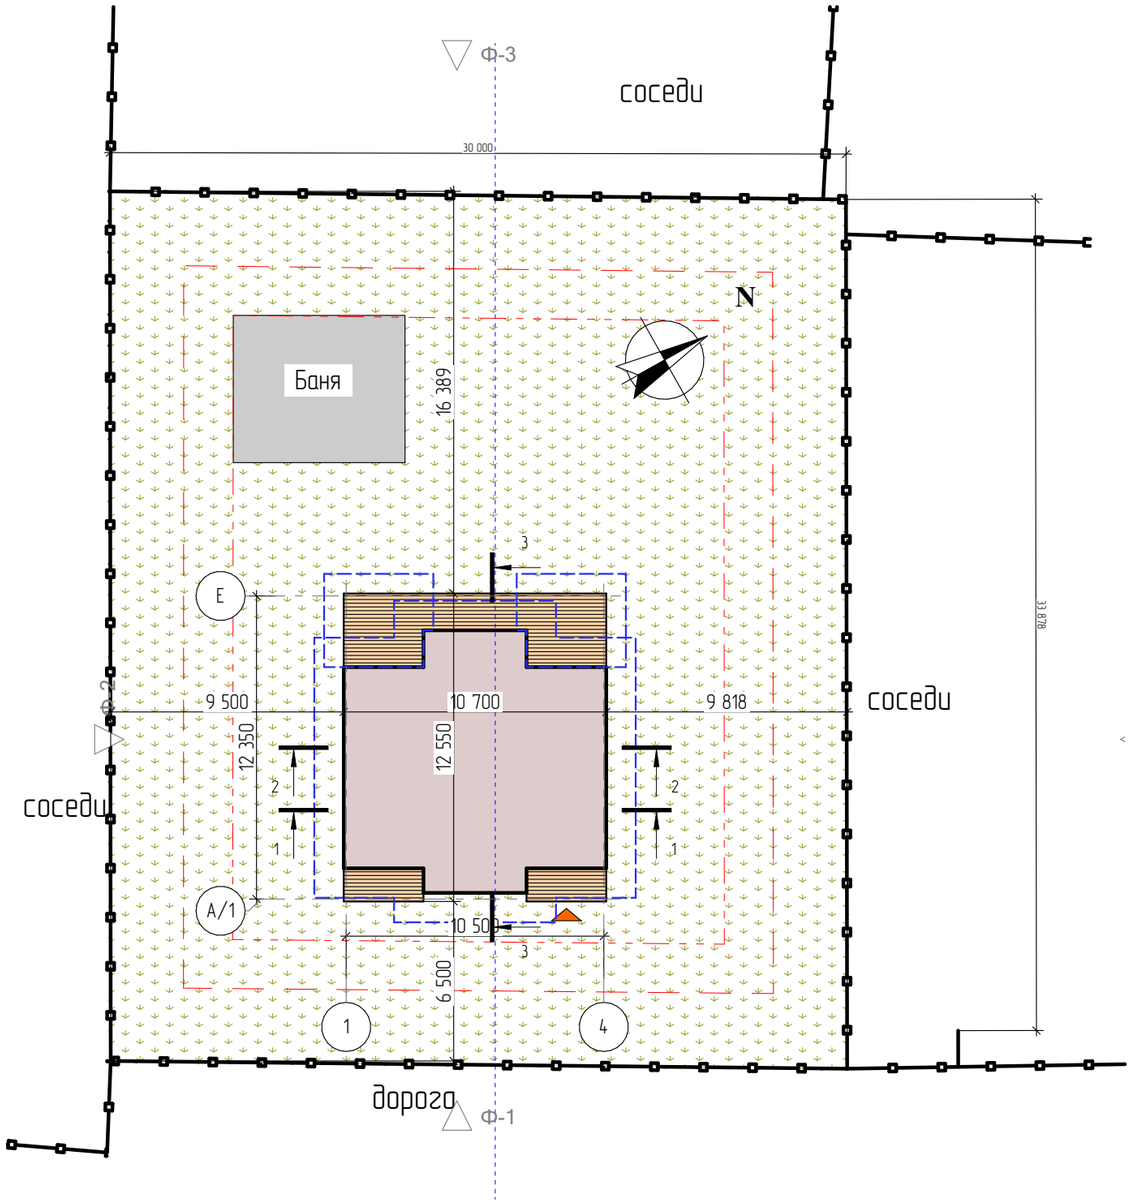

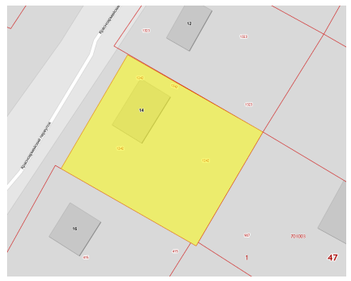


#ID Участка

Условные обозначения:

- Проектируемое здание
- Терраса/крыльцо/веранда
- Вход
- Контур кровли
- Зона отступа от края участка (красной линии улицы) = 5,0 м
- Зона отступа от края участка = 3,0 м
- Граница участка

Инсоляция по временам года

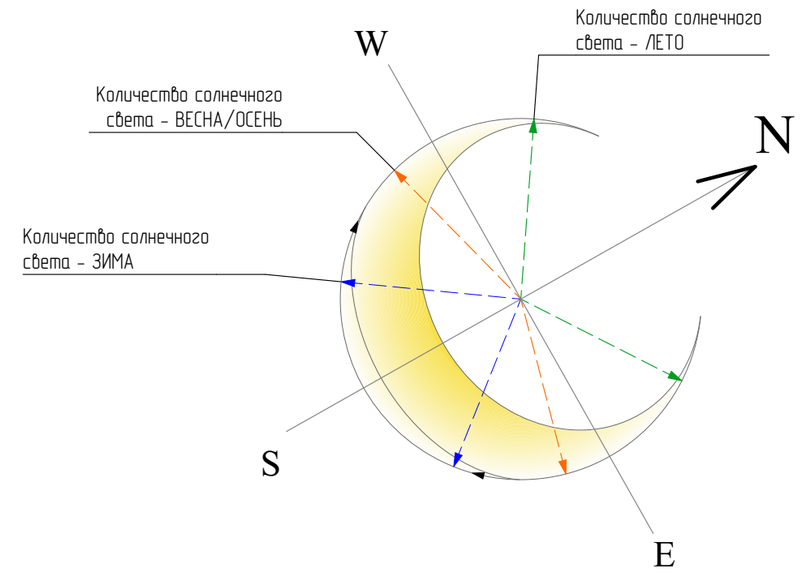

Примечание:
1) Расположение дома показано от забора до края фундамента.
2) Привязка показана условно. Скорректировать по месту.
3) При расположении дома учитывать требования по противопожарным расстояниям между строениями на соседних участках в соответствии с СП 53.13330.2011
4) Монтаж и расположение наружных сетей согласовывается с инженером по месту.

					2020	#ID Проекта			
						Адрес: #Полный Адрес Участка; к/н #ID Участка			
Изм.	Кол.уч	Лист	№док.	Подпись	Дата				
						Индивидуальный жилой дом	стадия	лист	листов
							ЭП	4	
Архитектор		Салыкова В.Г.							
Конструктор						Схема организации участка М 1:250			
Заказчик		#Обращение к Заказчику							

Согласовано:


Взам. инв. №

Подпись и дата

Инв. № подл.

М 1:100

План 1 этажа с расстановкой мебели

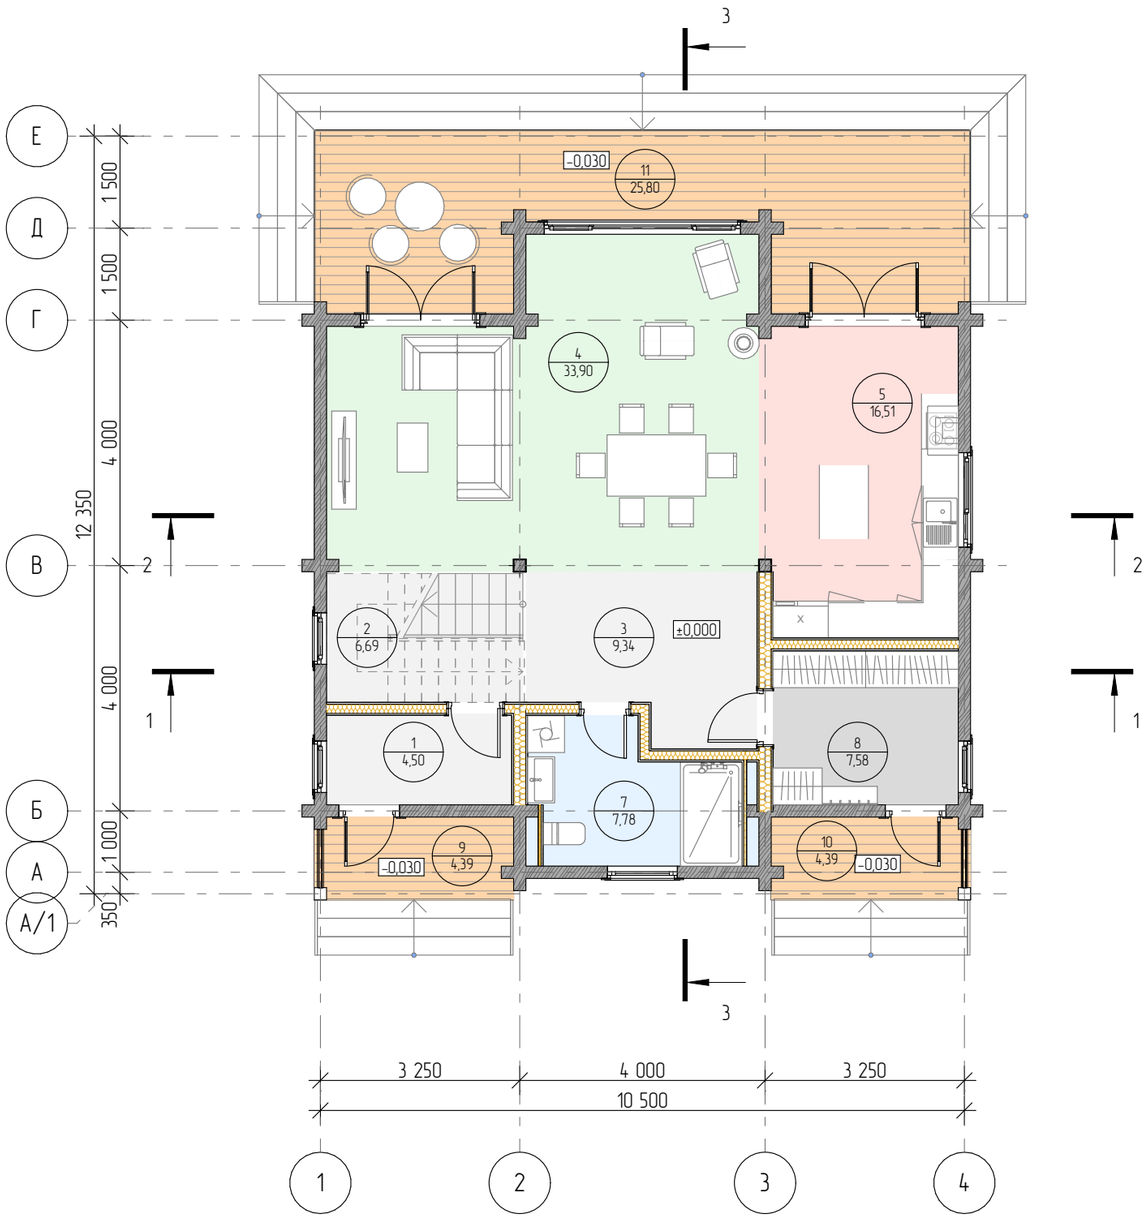

Экспликация 1 этажа

Расположение поиещений	№ п/п	Наименование	Площадь, м2
Внутр. пом.			
	1	Котельная (Электричество)	4,50
	2	Лестничный пролет	6,69
	3	Холл	9,34
	4	Гостиная	33,90
	5	Кухня	16,51
	7	Санузел	7,78
	8	Тамбур	7,58
			86,30 м²
Наружн. пом.			
	9	Крыльцо 1	4,39
	10	Крыльцо 2	4,39
	11	Терраса	25,80
			34,58 м²
			120,88 м²

Примечание:
1) Вся показанная мебель, а также назначение комнат носят условный характер
2) Расположение сан.технических приборов не подлежит перемещению.
3) Площадь помещений показана без учета отделочных материалов и понижающего коэффициента по периметру пола.
4) Все декоративные элементы подлежат дополнительному сметному согласованию.

					2020	#ID Проекта		
						Адрес: #Полный Адрес Участка		
Изм.	Кол.уч	Лист	№док.	Подпись	Дата			
						Индивидуальный жилой дом	стадия	лист	листов
							РП	5	
Архитектор		Салыкова В.Г.				План 1 этажа с расстановкой мебели М 1:100			
Конструктор									
Заказчик		#Обращение к Заказчику							

Согласовано:


Взам. инв. №

Подпись и дата

Инв. № подл.

М 1:100

План 2 этажа с расстановкой мебели

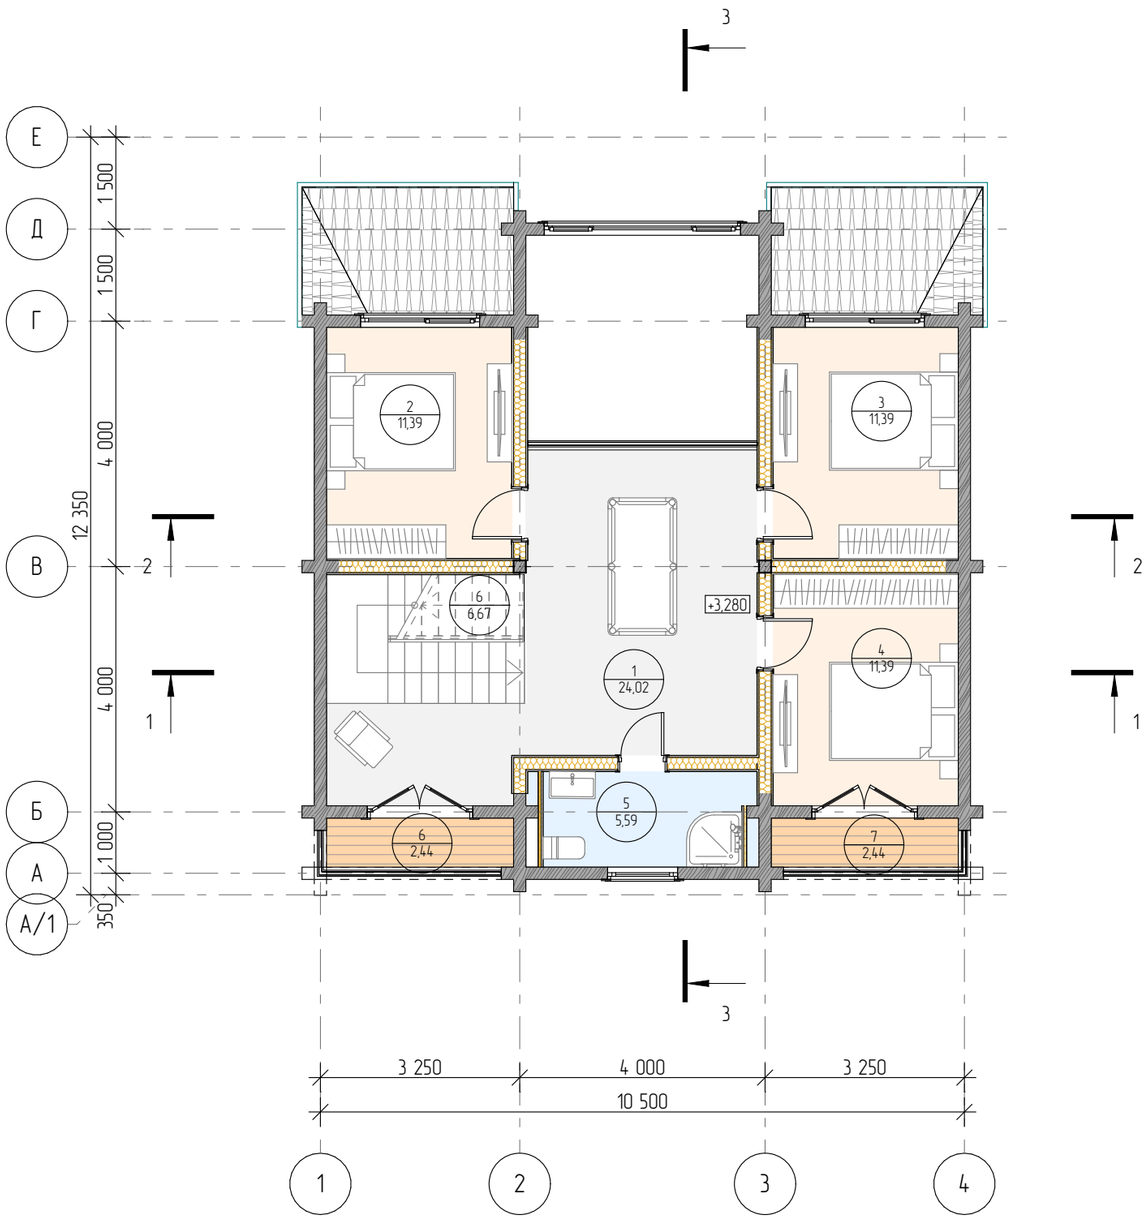

Экспликация 2 этажа

Расположение поиещений	№ п/п	Наименование	Площадь, м2
Внутр. пом.			
	1	Холл	24,02
	2	Спальня	11,39
	3	Спальня	11,39
	4	Спальня	11,39
	5	Санузел	5,59
	6	Лестничный пролет	6,67
			70,45 м²
Наружн. пом.			
	6	Балкон 1	2,44
	7	Балкон 2	2,44
			4,88 м²
			75,33 м²

Примечание:
1) Вся показанная мебель, а также назначение комнат носят условный характер
2) Расположение сан.технических приборов не подлежит перемещению.
3) Площадь помещений показана без учета отделочных материалов и понижающего коэффициента по периметру пола.
4) Все декоративные элементы подлежат дополнительному сметному согласованию.

					2020	#ID Проекта
						Адрес: #Полный Адрес Участка
Изм.	Кол.уч	Лист	№док.	Подпись	Дата	
Архитектор		Салыкова В.Г.				Индивидуальный жилой дом
Конструктор						План 2 этажа с расстановкой мебели М 1:100
Заказчик		#Обращение к Заказчику				

стадия	лист	листов
РП	6	

Согласовано:


Взам. инв. №

Подпись и дата

Инв. № подл.

1:75

Разрез 1-1

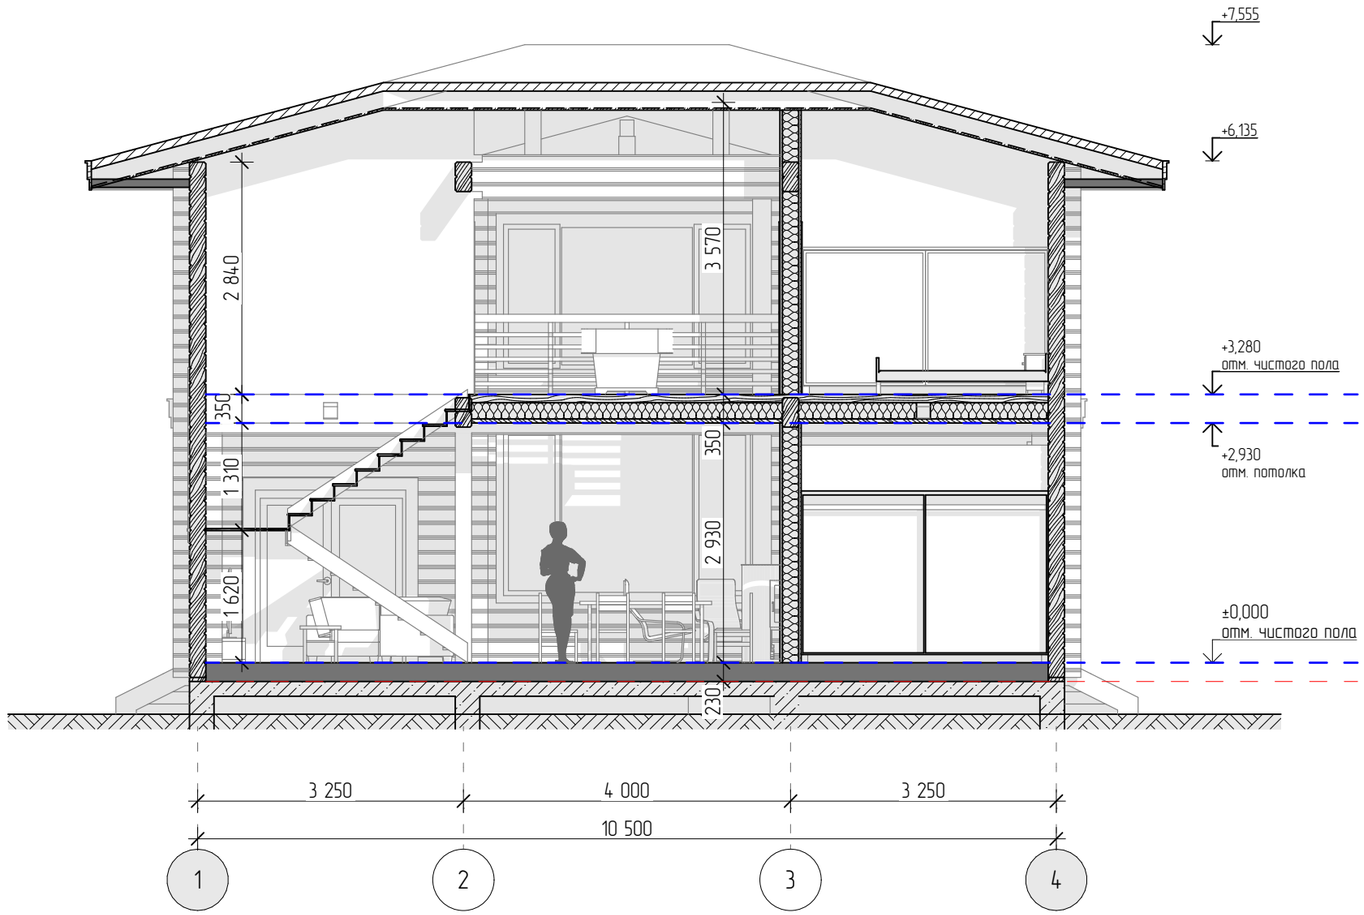

Примечание:

1) За отметку +0,000 принята отметка чистового пола первого этажа
2) За отметку +3,280 принята отметка чистового пола второго этажа
3) Номинальные высотные размеры могут отличаться от фактических в силу технологической усадки стенового комплекта и принимаемых отделочных материалов.
4) Несущие перевязки из бруса могут быть ниже основного уровня потолка
5) Высота фундамента дана без учета перепада. Замер перепада производится на участке при выезде инженера. Изменение габаритов и типа фундаментов согласовывается дополнительным согласованием по смете.
6) Все декоративные элементы показаны условно.

					2020	#ID Проекта			
						Адрес: #Полный Адрес Участка			
Изм.	Кол.уч	Лист	№док.	Подпись	Дата				
						Индивидуальный жилой дом	стадия	лист	листов
							РП	7	
Архитектор		Салыкова В.Г.							
Конструктор						Разрез 1-1 М 1:100			
Заказчик		#Обращение к Заказчику							

Согласовано:


Взам. инв. №

Подпись и дата

Инв. № подл.

1:75

Разрез 2-2

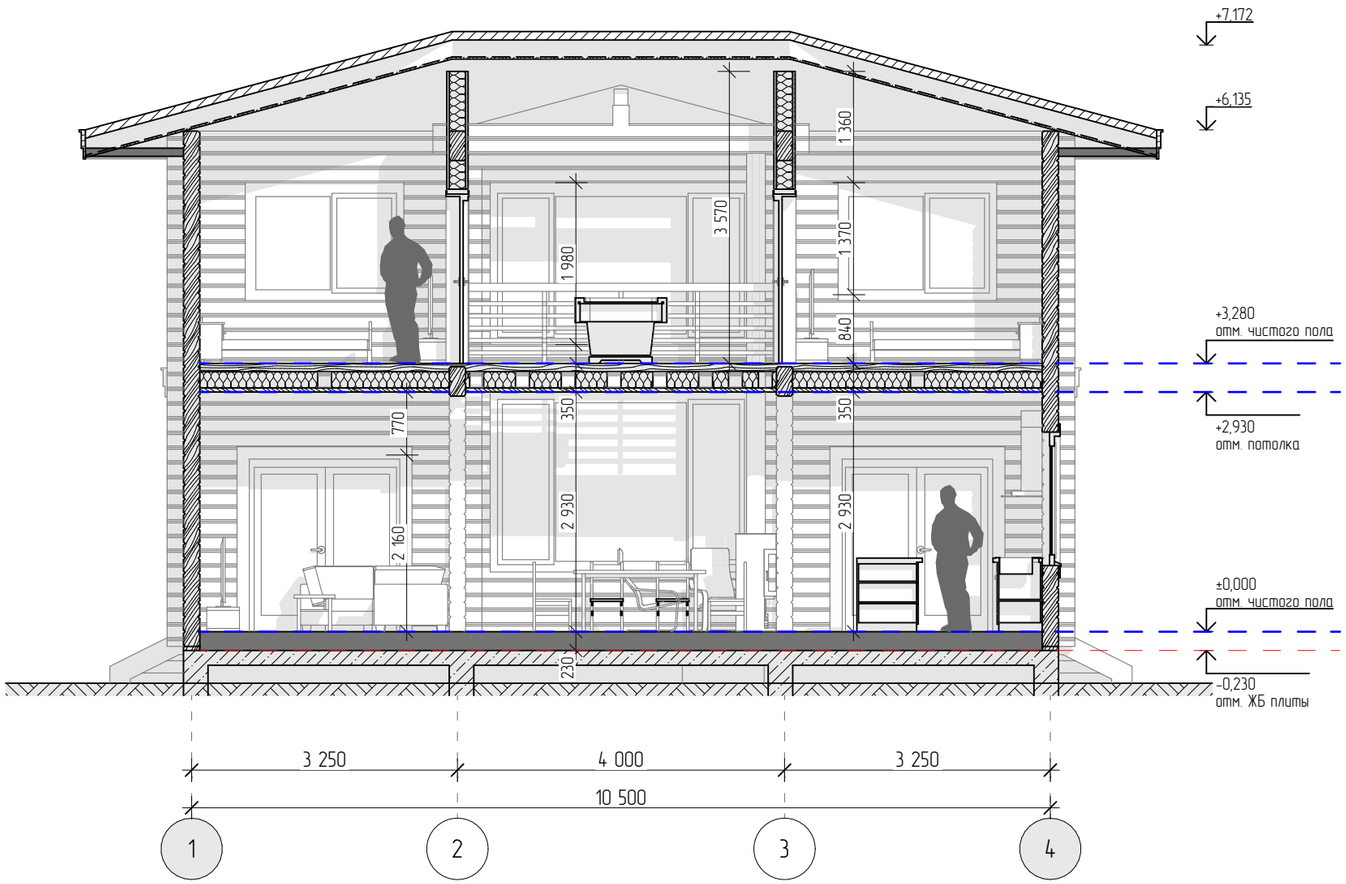

Примечание:

1) За отметку +0,000 принята отметка чистового пола первого этажа
2) За отметку +3,280 принята отметка чистового пола второго этажа
3) Номинальные высотные размеры могут отличаться от фактических в силу технологической усадки стенового комплекта и принимаемых отделочных материалов.
4) Несущие перевязки из бруса могут быть ниже основного уровня потолка
5) Высота фундамента дана без учета перепада. Замер перепада производится на участке при выезде инженера. Изменение габаритов и типа фундаментов согласовывается дополнительным согласованием по смете.
6) Все декоративные элементы показаны условно.

					2020	#ID Проекта			
						Адрес: #Полный Адрес Участка			
Изм.	Кол.уч	Лист	№док.	Подпись	Дата				
						Индивидуальный жилой дом	стадия	лист	листов
							РП	8	
Архитектор		Салыкова В.Г.							
Конструктор						Разрез 2-2 М 1:100			
Заказчик		#Обращение к Заказчику							

Согласовано


Взам. инв. №

Подпись и дата

Инв. № подл.

1:75

Разрез 3-3

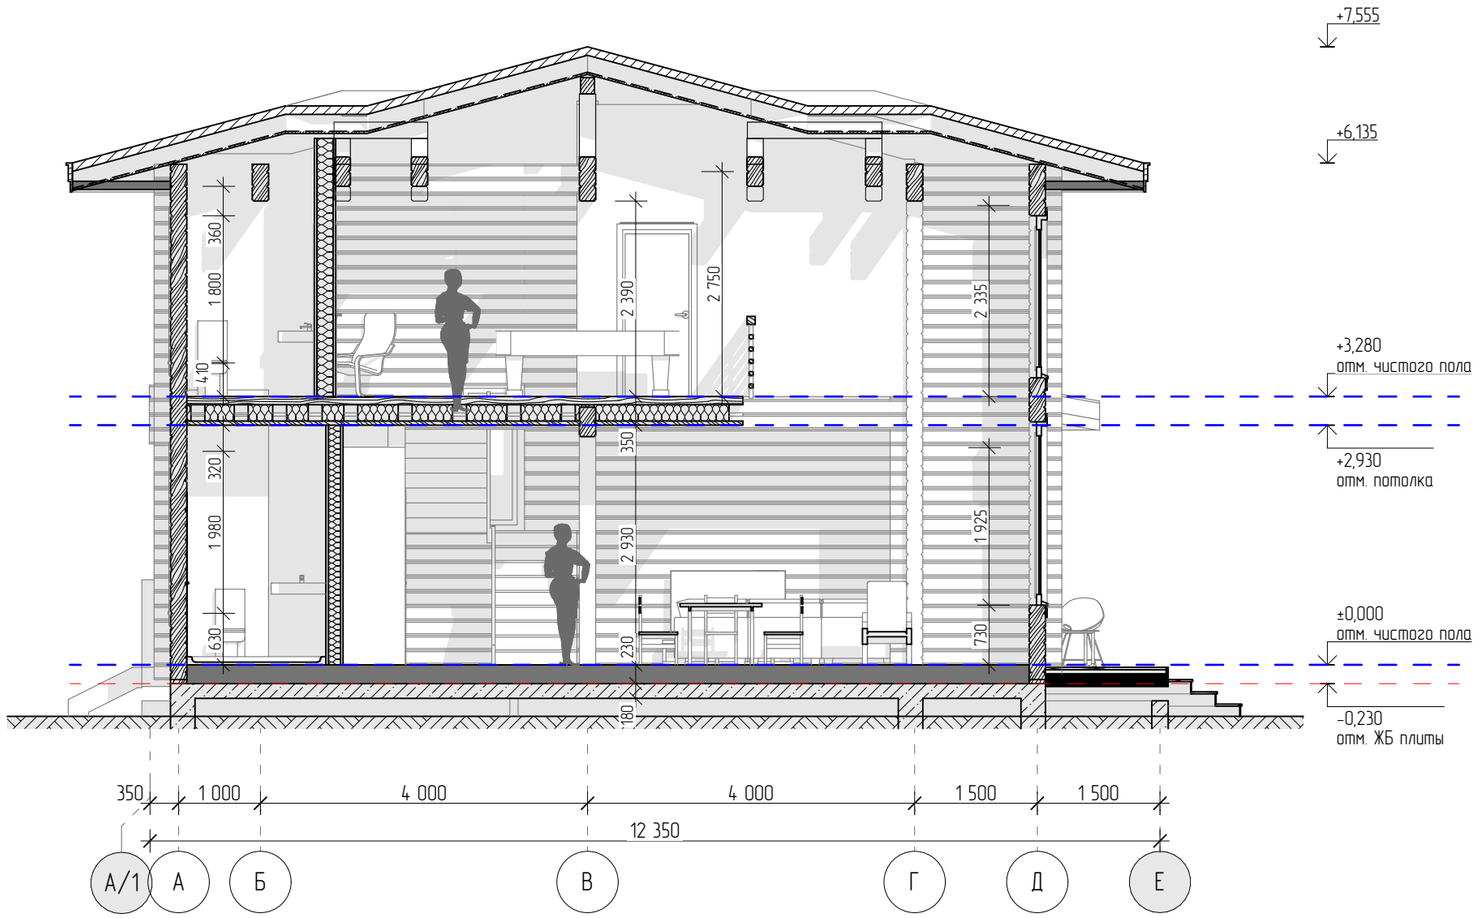

Примечание:

1) За отметку +0,000 принята отметка чистового пола первого этажа
2) За отметку +3,280 принята отметка чистового пола второго этажа
3) Номинальные высотные размеры могут отличаться от фактических в силу технологической усадки стенового комплекта и принимаемых отделочных материалов.
4) Несущие перевязки из бруса могут быть ниже основного уровня потолка
5) Высота фундамента дана без учета перепада. Замер перепада производится на участке при выезде инженера. Изменение габаритов и типа фундаментов согласовывается дополнительным согласованием по смете.
6) Все декоративные элементы показаны условно.

					2020	#ID Проекта	
						Адрес: #Полный Адрес Участка	
Изм.	Кол.уч	Лист	№док.	Подпись	Дата		
						Индивидуальный жилой дом	стадия: РП; лист: 9; листов:
Архитектор		Салыкова В.Г.					
Конструктор						Разрез 3-3 М 1:100	
Заказчик		#Обращение к Заказчику					

Согласовано:

Взам. инв. №


Подпись и дата

Инв. № подл.

Фасад 1-4



Фасад Е-А

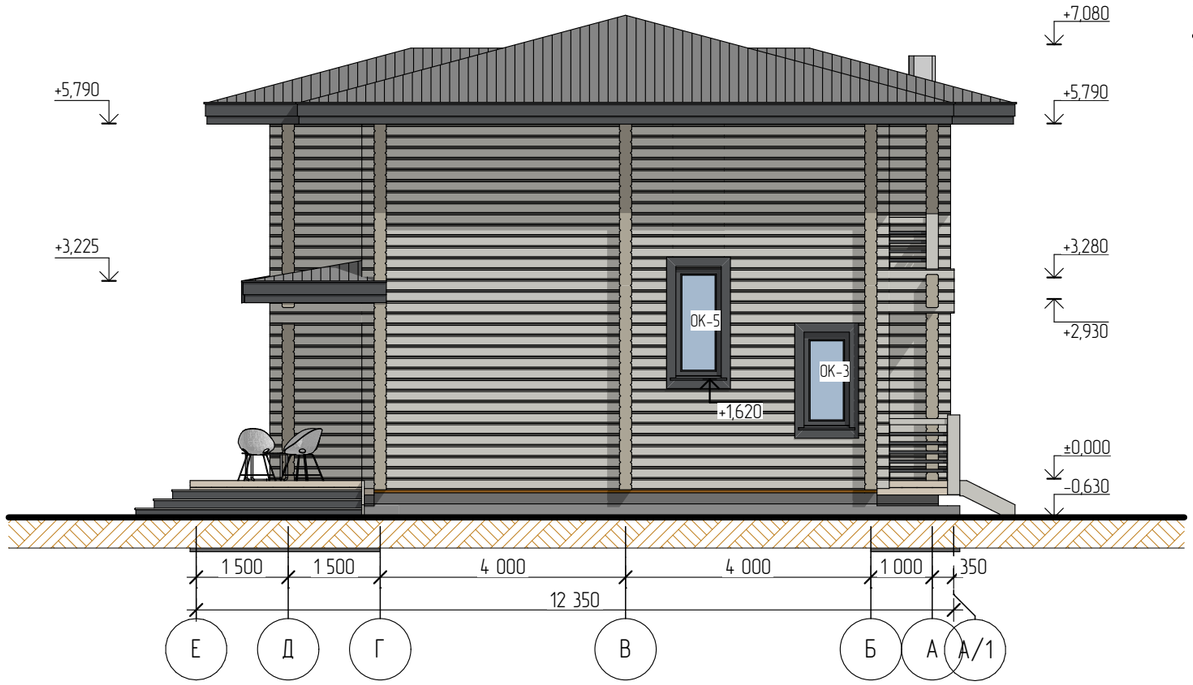

Примечание:
1) За отметку +0,000 принята отметка чистового пола первого этажа
2) Номинальные высотные размеры могут отличаться от фактических в силу технологической усадки стенового
комплекта и принимаемых отделочных материалов.
3) Несущие перевязки из бруса могут быть ниже основного уровня потолка
4) Высота фундамента дана без учета перепада. Замер перепада производится на участке при выезде инженера.
Изменение габаритов и типа фундаментов согласовывается дополнительным согласованием по смете.
5) Все декоративные элементы показаны условно.

					2020	#ID Проекта			
						Адрес: #Полный Адрес Участка			
Изм.	Кол.уч	Лист	№док.	Подпись	Дата				
						Индивидуальный жилой дом	стадия	лист	листов
							РП	10	
Архитектор		Салыкова В.Г.							
Конструктор						Фасады М 1:100			
Заказчик		#Обращение к Заказчику							


Согласовано

Взам. инв. №

Подпись и дата

Инв. № подл.

Фасад А-Е

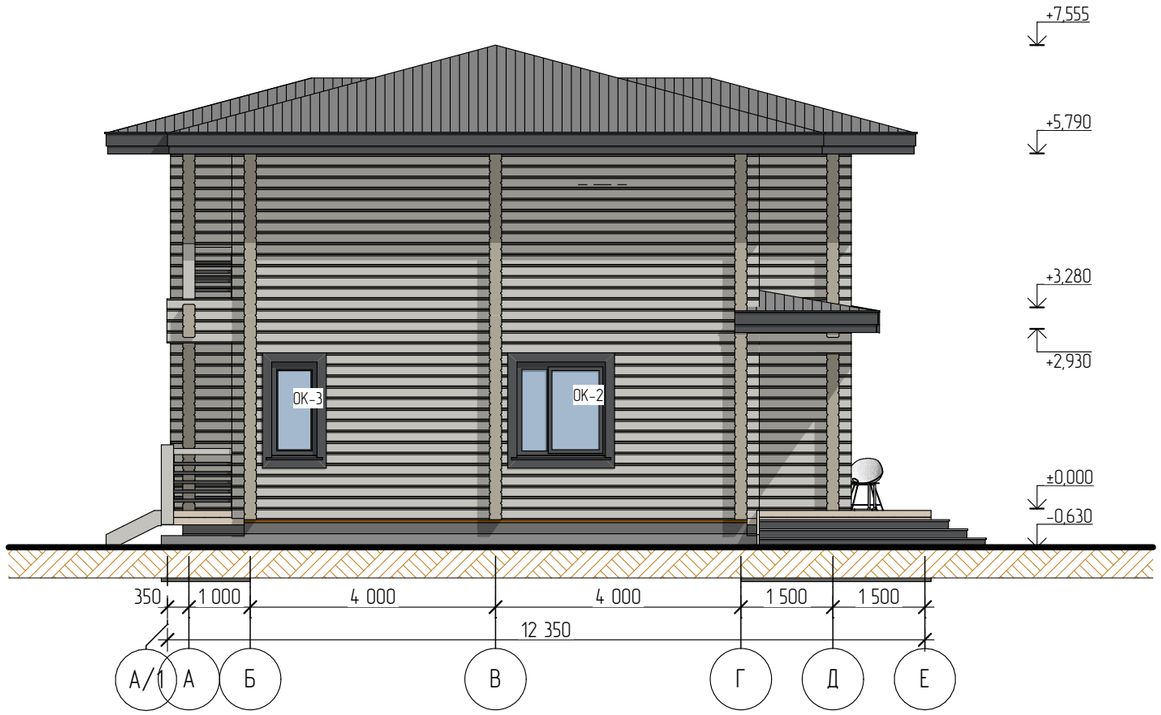

Фасад 4-1



Примечание:
1) За отметку +0,000 принята отметка чистового пола первого этажа
2) Номинальные высотные размеры могут отличаться от фактических в силу технологической усадки стенового комплекта и принимаемых отделочных материалов.
3) Несущие перевязки из бруса могут быть ниже основного уровня потолка
4) Высота фундамента дана без учета перепада. Замер перепада производится на участке при выезде инженера.
Изменение габаритов и типа фундаментов согласовывается дополнительным согласованием по смете.
5) Все декоративные элементы показаны условно.

Согласовано:

Взам. инв. №


Подпись и дата

Инв. № подл.

					2020	#ID Проекта			
						Адрес: #Полный Адрес Участка			
Изм.	Кол.уч	Лист	№док.	Подпись	Дата				
						Индивидуальный жилой дом	стадия	лист	листов
							РП	11	
Архитектор		Салыкова В.Г.							
Конструктор						Фасады М 1:100			
Заказчик		#Обращение к Заказчику							

М 1:100

Лента / Сваи

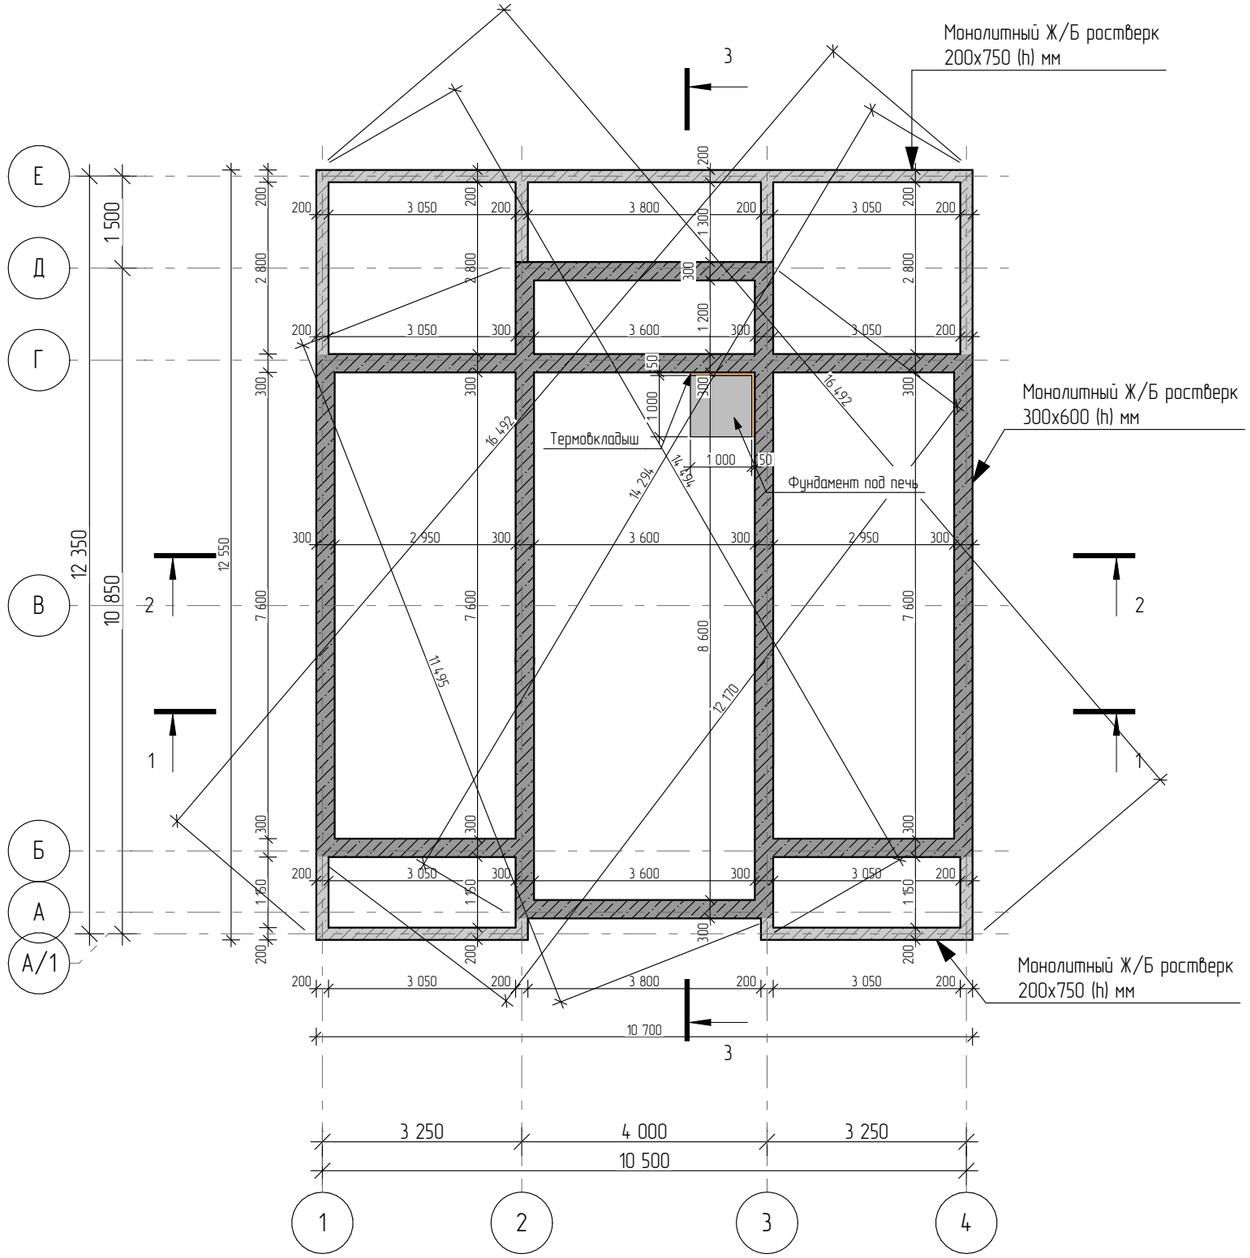

Примечание:

1) Отметка 0,000 задана по верху чистого пола первого этажа
2) Диагональная привязка фундамента осуществляется по наружной грани фундамента
3) Продухи Ø=110мм на террасе и крыльце устанавливаются по месту. Высота до низа продуха не менее 200мм от уровня земли.

					2020	#ID Проекта
						Адрес: #Полный Адрес Участка
Изм.	Кол.уч	Лист	№док.	Подпись	Дата	
						Индивидуальный жилой дом
Архитектор		Салыкова В.Г.				План фундамента М 1:100
Конструктор						
Заказчик		#Обращение к Заказчику				


стадия	лист	листов
РП	12	

Согласовано:

Взам. инв. №

Подпись и дата

Инв. № подл.

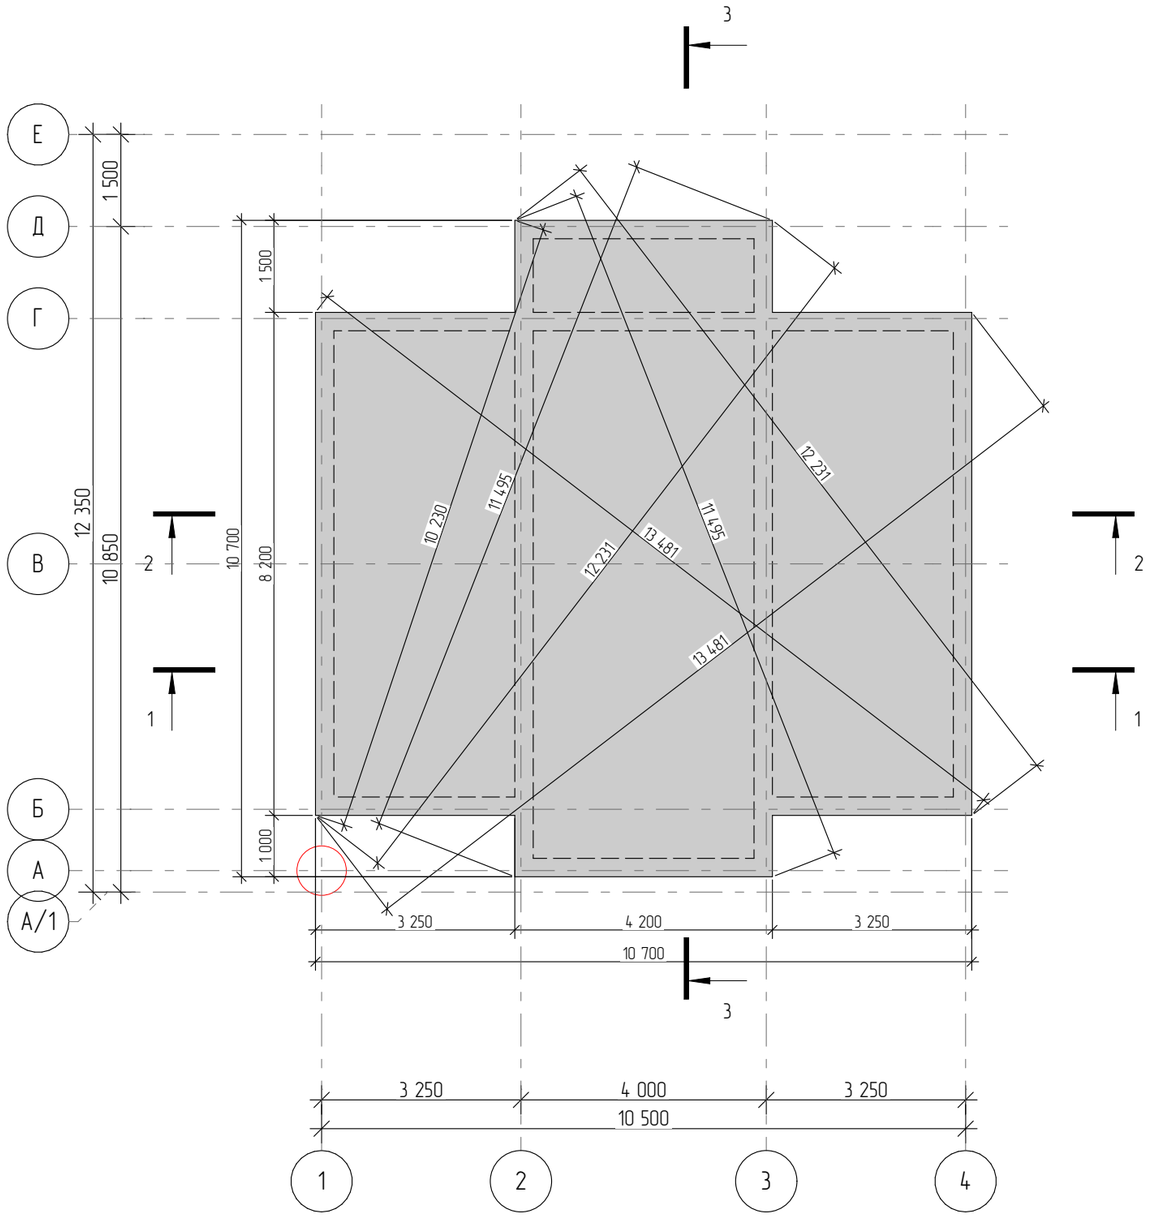

Согласовано


Взам. инв. №

Подпись и дата

Инв. № подл.

					2020	#ID Проекта
						Адрес: #Полный Адрес Участка; к/н #ID Участка
Изм.	Кол.уч	Лист	№док.	Подпись	Дата	
						Индивидуальный жилой дом
Архитектор		Салыкова В.Г.				
Конструктор						План ЖБ плиты
Заказчик		#Обращение к Заказчику				

стадия	лист	листов
ЭП	13	

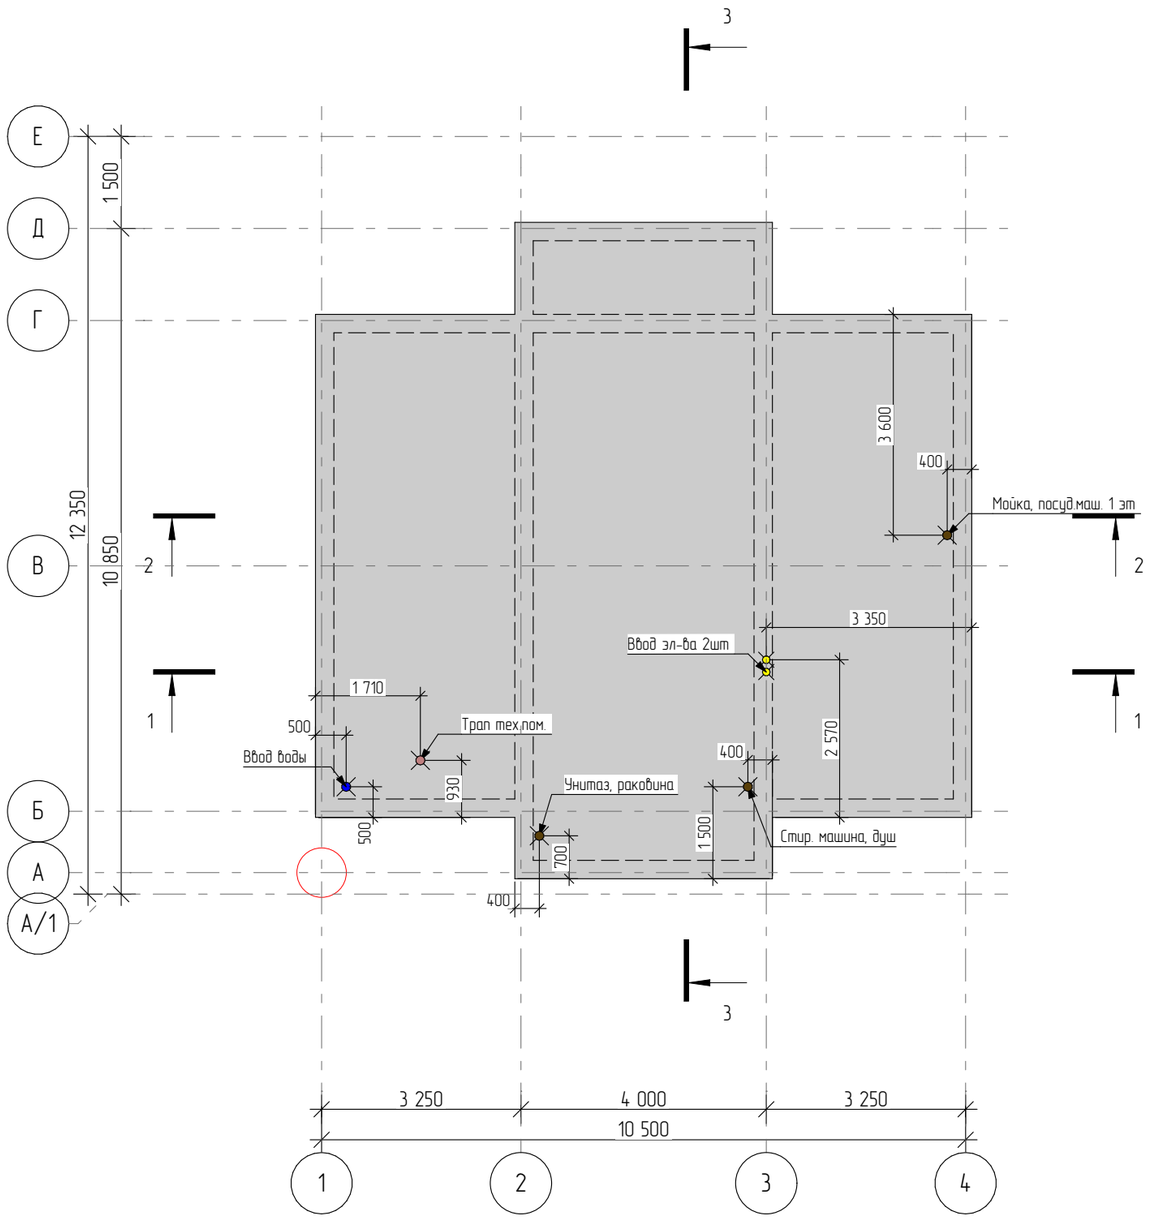

Согласовано

Взам. инв. №

Подпись и дата


Инв. № подл.

					2020	#ID Проекта
						Адрес: #Полный Адрес Участка; к/н #ID Участка
Изм.	Кол.уч	Лист	№док.	Подпись	Дата	
						Индивидуальный жилой дом
Архитектор		Салыкова В.Г.				План ЖБ плиты с закладными
Конструктор						
Заказчик		#Обращение к Заказчику				

стадия	лист	листов
ЭП	14	

М 1:100

Подкладочный ряд -0.180 / -0.305

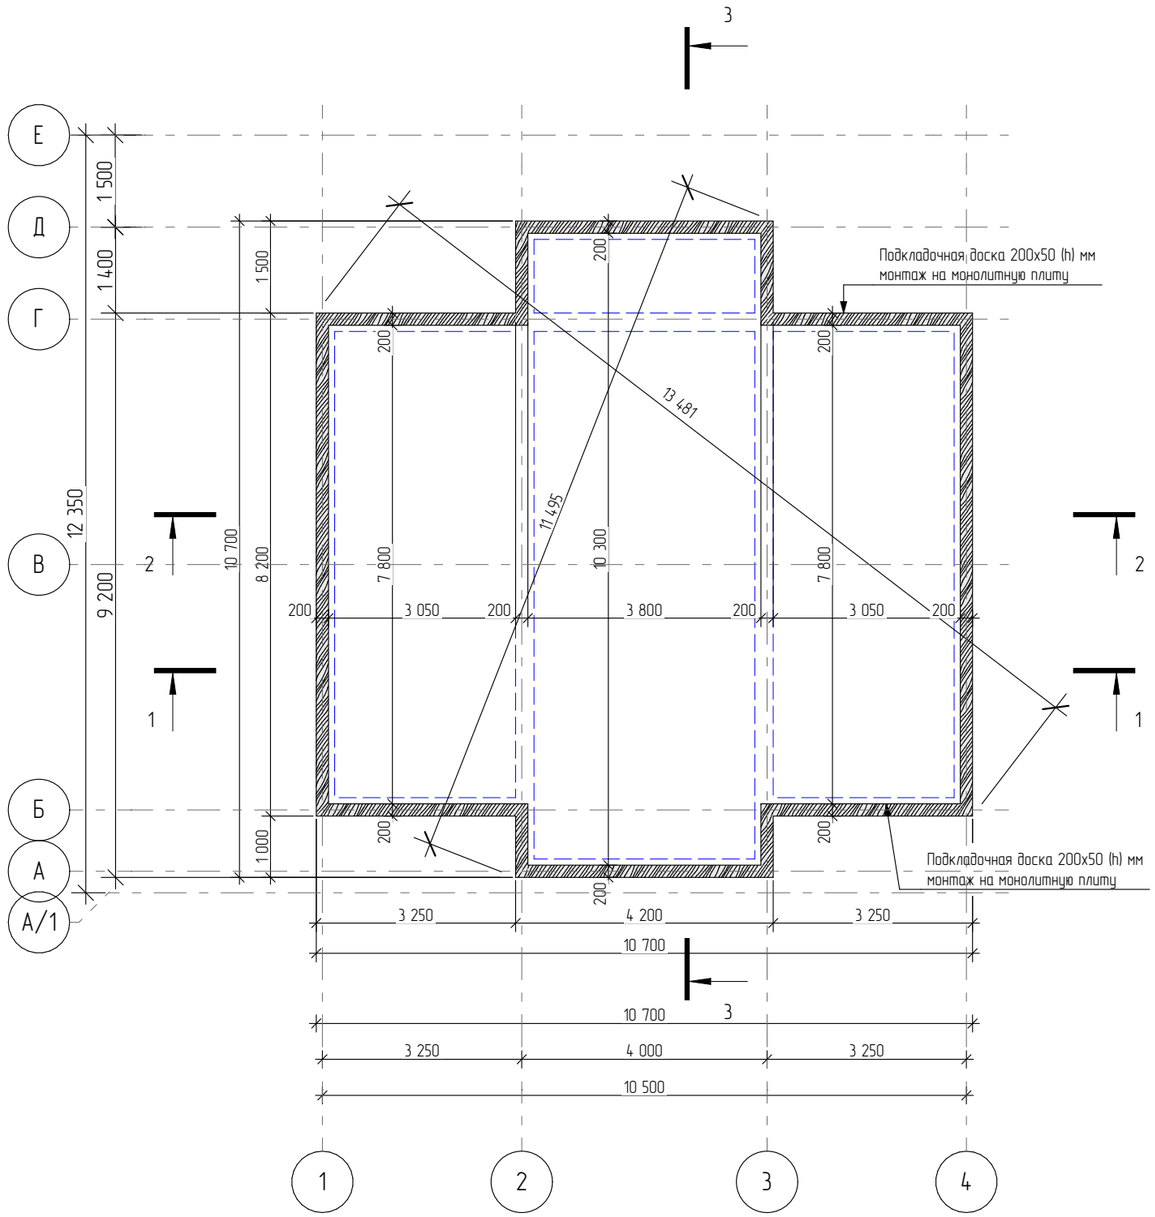

Примечание:

1) Обвязочный брус - обрезная доска 50х200(+/- 10мм), естеств. влажности, сосна или ель.
2) Сечение обвязочного ряда определяется сметным расчёто

					2020	#ID Проекта		
						Адрес: #Полный Адрес Участка		
Изм.	Кол.уч	Лист	№док.	Подпись	Дата			
						Индивидуальный жилой дом	стадия	лист	листов
							РП	15	
Архитектор		Салыкова В.Г.							
Конструктор						Подкладочный ряд М 1:100			
Заказчик		#Обращение к							
		Заказчику							

Согласовано


Взам. инв. №

Подпись и дата

Инв. № подл.

М 1:100

Ригели/плита межэтажная/балки перекрытия

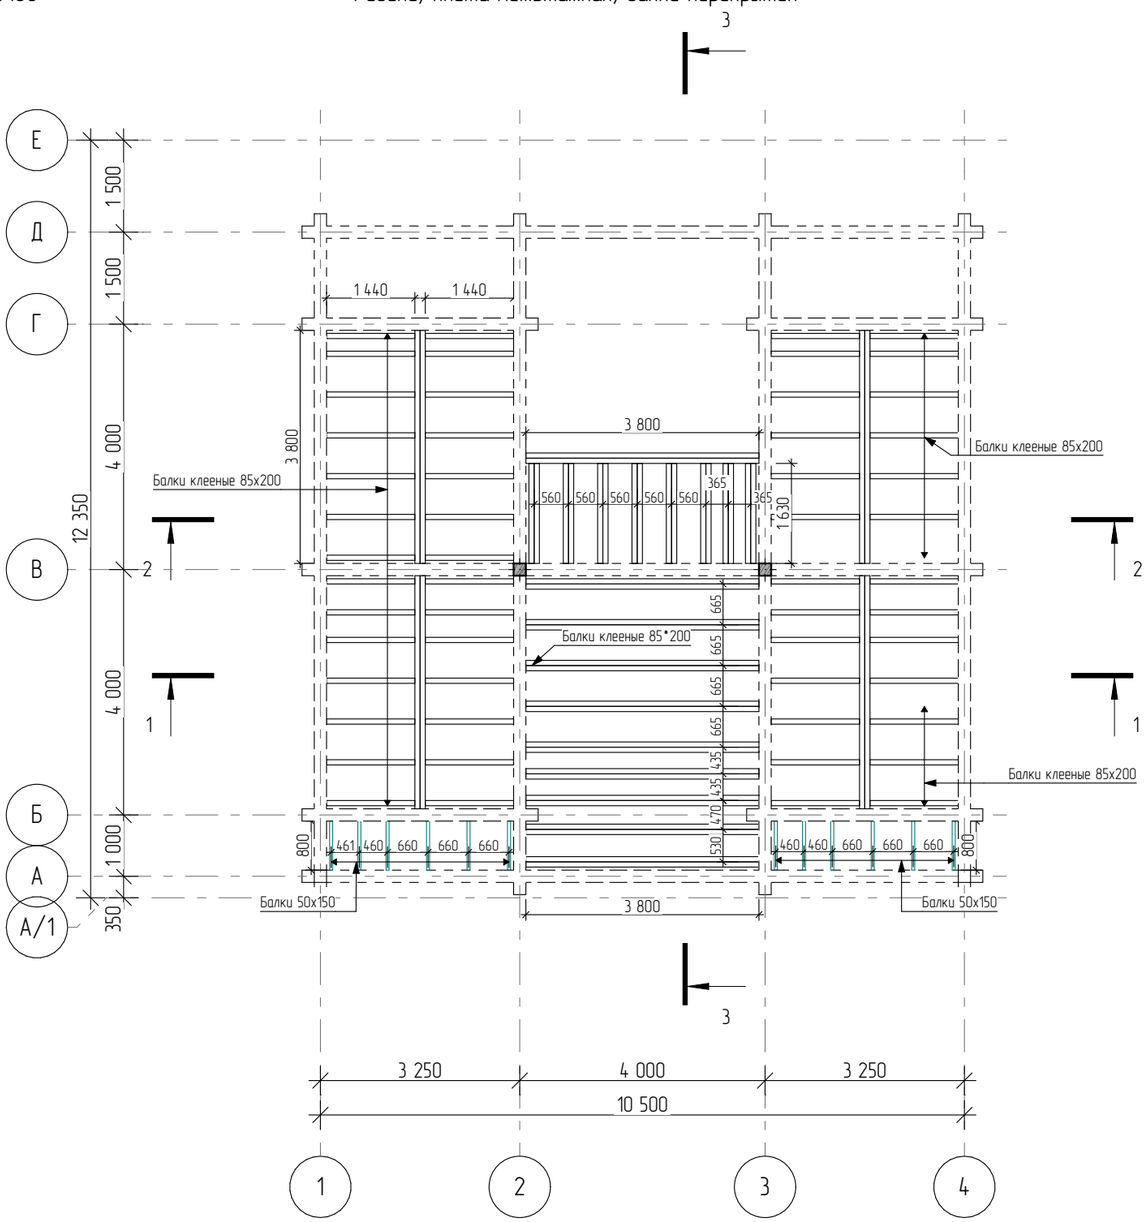

Примечание:

1) Балки перекрытия - 85х200 клееные
На балконах обрезная доска 50х150 (+/- 10мм), естеств. влажности, сосна/ель(или сухая строганая доска)
2) Сечение балок перекрытия определяется сметным расчётом

					2020	#ID Проекта	
						Адрес: #Полный Адрес Участка	
Изм.	Кол.уч	Лист	№док.	Подпись	Дата		
						Индивидуальный жилой дом	стадия: РП; лист: 16; листов:
Архитектор		Салыкова В.Г.					
Конструктор						План раскладки балок межэтажного перекрытия М 1:100	
Заказчик		#Обращение к Заказчику					

Согласовано:


Взам. инв. №

Подпись и дата

Инв. № подл.

М 1:100

Монтажный план 1 этажа

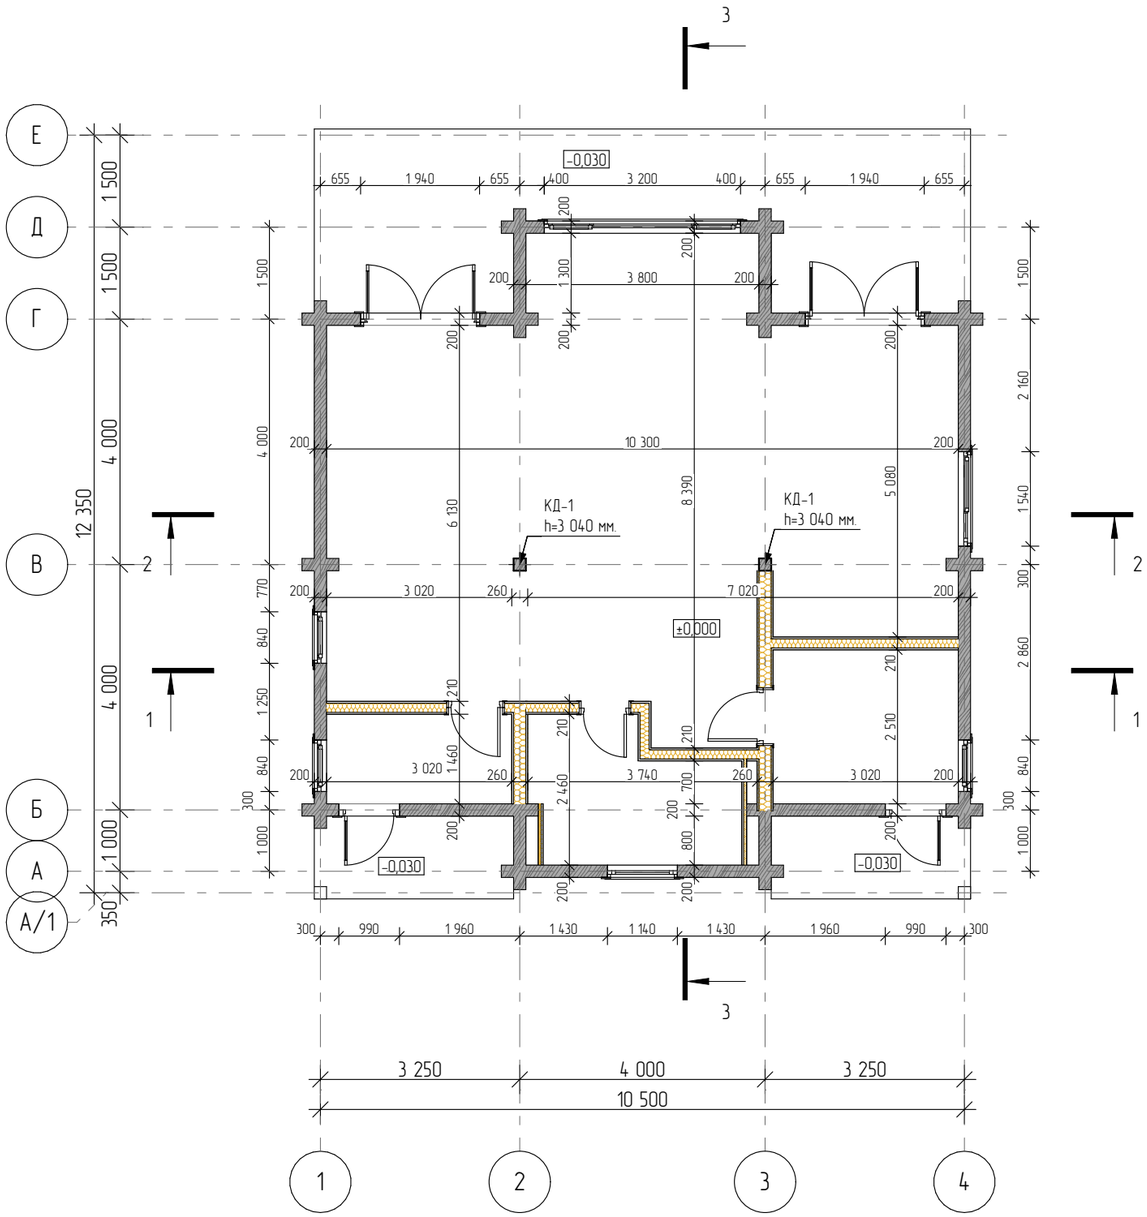

Согласовано:

Взам. инв. №

Подпись и дата

Инв. № подл.

Условные обозначения

- Наружняя стена – клеенный профилированный брус h=190(180), d=200мм
- Перегородки – стены по каркасной технологии, обшивка имитацией бруса и ГВЛ или иными материалами
- Столбы клееные 200х200
- Столб клееный 120х200


Примечание:

1) За отметку +-0,000 принята отметка чистового пола первого этажа
2) Толщина каркасных перегородок показана без учета отделочных материалов
3) Расположение вентиляционных коммуникаций и прочих инженерных систем показано условно. Проект инженерных коммуникаций будет разрабатываться при заключении договора на инженерные работы. Количество и наличие вентиляционных, фановых и дымовых труб определяется дополнительным согласованием в сметном расчёте на этапе отделочных работ.
4) Габаритные размеры и расположение печи/камина могут измениться в процессе строительства
5) Ответственность за конструктивное решение и расположение печи/камина относительно несущих деревянных конструкций, фундамента, а также соблюдение мер пожарной безопасности при сооружении и эксплуатации печи/камина, полностью лежат на Заказчике

					2020	#ID Проекта		
						Адрес: #Полный Адрес Участка		
Изм.	Кол.уч	Лист	№док.	Подпись	Дата			
						Индивидуальный жилой дом	стадия	лист	листов
							РП	17	
Архитектор		Салыкова В.Г.				План 1 этажа с размерами М 1:100			
Конструктор									
Заказчик		#Обращение к Заказчику							

М 1:100

Монтажный план 2 этажа

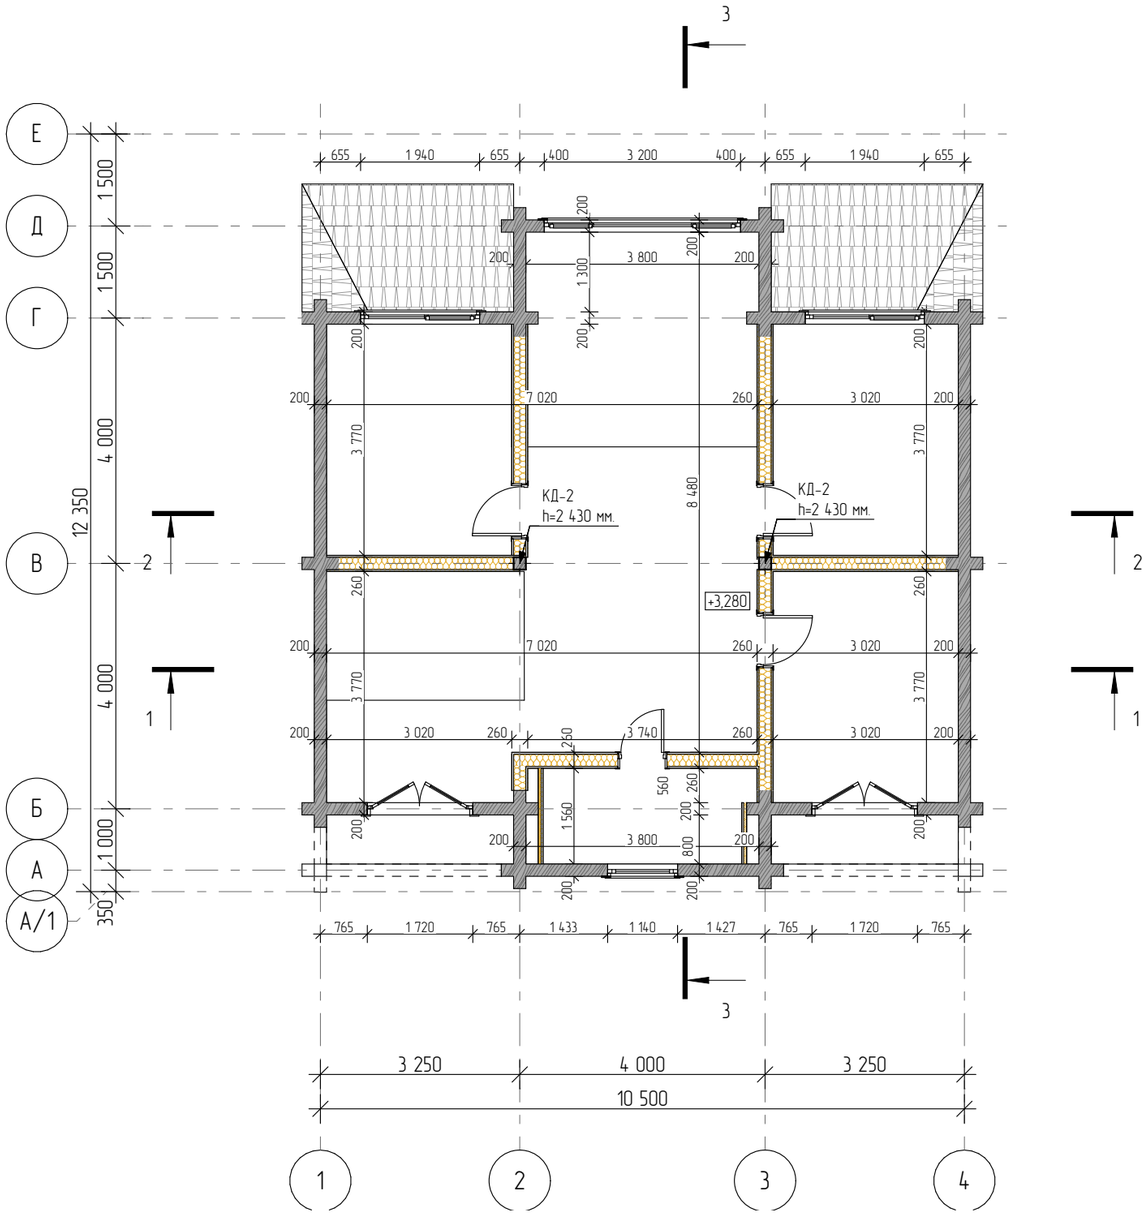

Условные обозначения

Наружняя стена - клеенный профилированный брус h=190(180), d=200мм

Перегородки - стены по каркасной технологии, обшивка имитацией бруса и ГВЛ или иными материалами

Столбы клееные 200х200

Примечание:

1) За отметку +3,280 принята отметка чистового пола второго этажа
2) Толщина каркасных перегородок показана без учета отделочных материалов
3) Расположение вентиляционных коммуникаций и прочих инженерных систем показано условно. Проект инженерных коммуникаций будет разрабатываться при заключении договора на инженерные работы. Количество и наличие вентиляционных, фановых и дымовых труб определяется дополнительным согласованием в сметном расчёте на этапе отделочных работ.
4) Габаритные размеры и расположение печи/камина могут измениться в процессе строительства
5) Ответственность за конструктивное решение и расположение печи/камина относительно несущих деревянных конструкций, фундамента, а также соблюдение мер пожарной безопасности при сооружении и эксплуатации печи/камина, полностью лежат на Заказчике

Согласовано

Взам. инв. №


Подпись и дата

Инв. № подл.

					2020	#ID Проекта		
						Адрес: #Полный Адрес Участка		
Изм.	Кол.уч	Лист	№док.	Подпись	Дата			
						Индивидуальный жилой дом	стадия	лист	листов
							РП	18	
Архитектор		Салыкова В.Г.				План 2 этажа с размерами М 1:100			
Конструктор									
Заказчик		#Обращение к Заказчику							

М 1:100

Маркировочный план 1 этажа

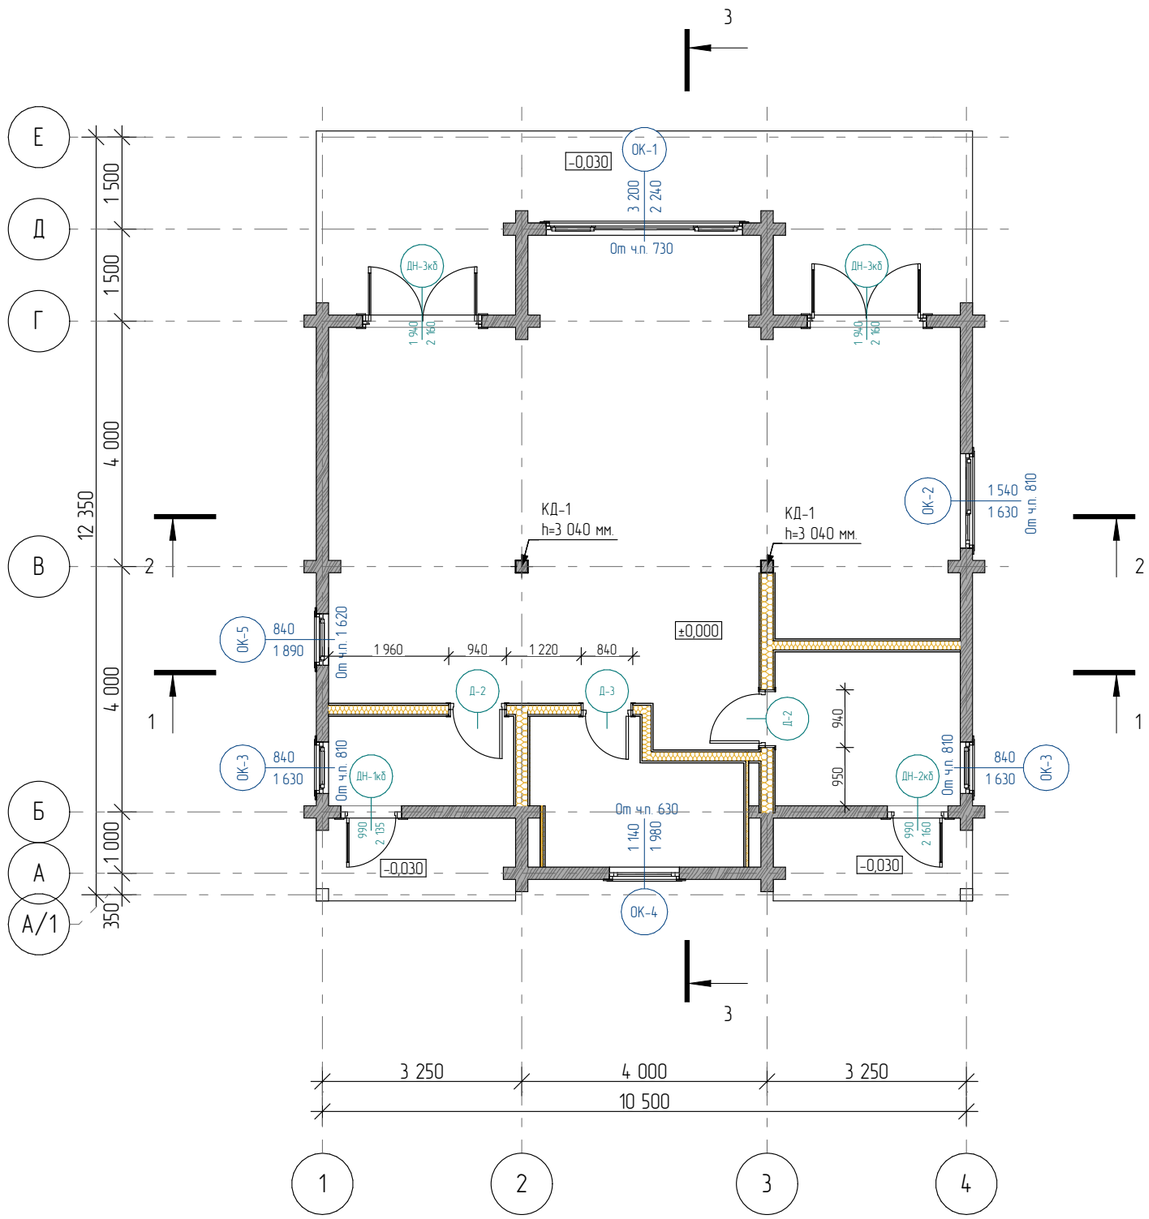

Условные обозначения

ОК-3	Окно маркировка 3. См. спецификацию заполнения оконных проемов
ДН-1КБ	Дверь наружняя в клееном брусе. См. спецификацию заполнения дверных проемов
ДН-1К	Дверь наружняя в каркасе
Д-1	Дверь межкомнатная
ДН-3п	Дверь противопожарная

Примечание:

1) Привязка проёмов окон и дверей в клееном брусе указывается с учетом обсады

Согласовано:

Взам. инв. №


Подпись и дата

Инв. № подл.


					2020	#ID Проекта	
						Адрес: #Полный Адрес Участка	
Изм.	Кол.уч	Лист	№док.	Подпись	Дата		
						Индивидуальный жилой дом	стадия: РП; лист: 19; листов:
Архитектор		Салыкова В.Г.					
Конструктор						Маркировочный план 1 этажа М 1:100	
Заказчик		#Обращение к Заказчику					

М 1:100

Маркировочный план 2 этажа

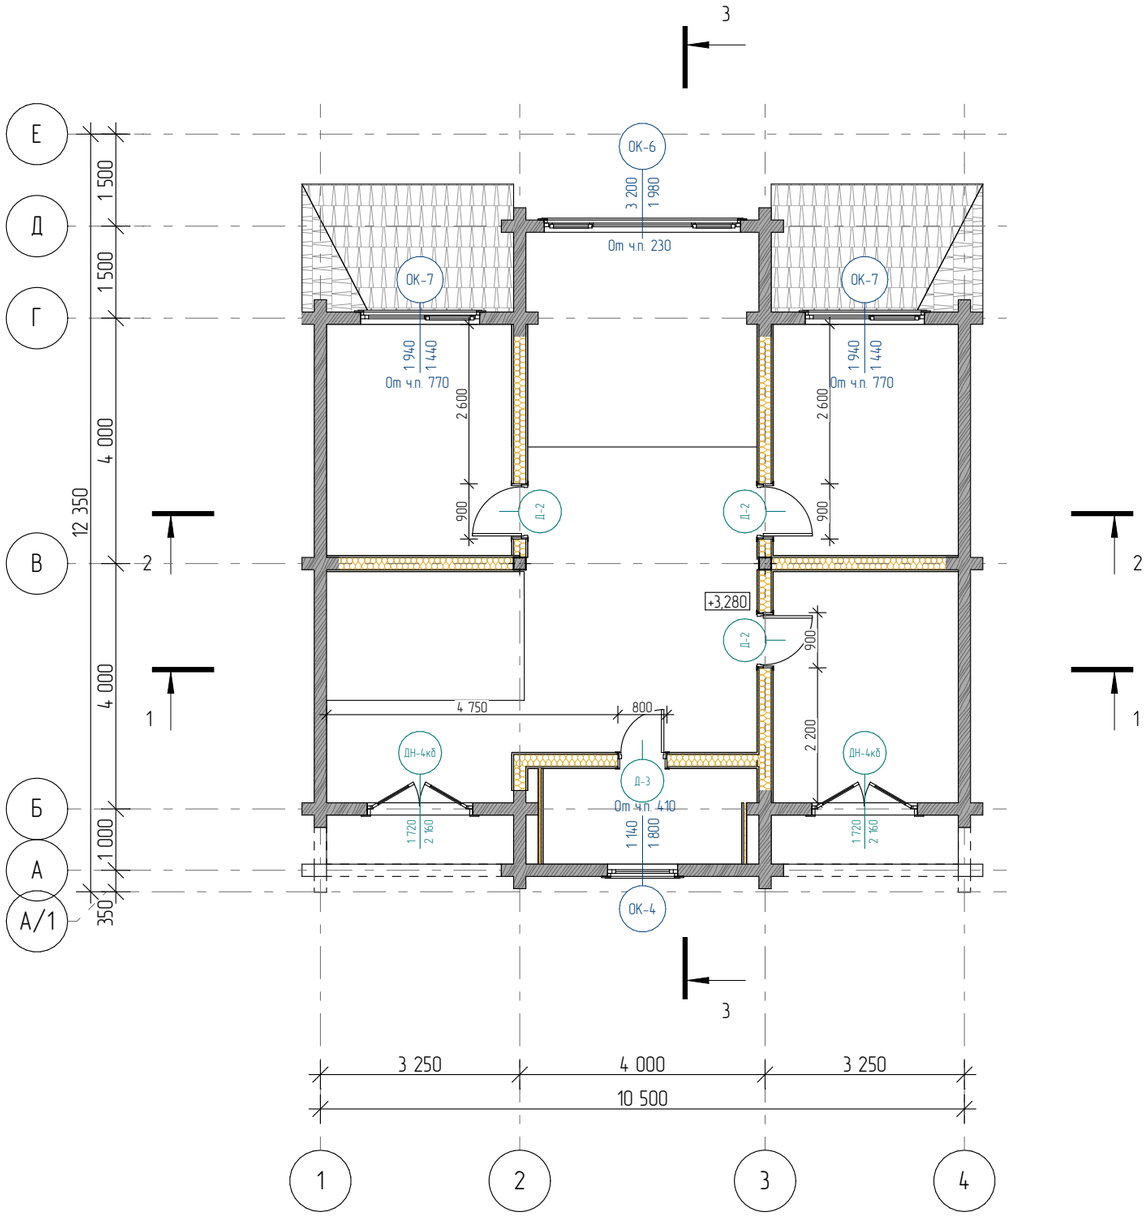

Условные обозначения

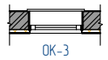 ОК-3	Окно маркировка 3. См. спецификацию заполнения оконных проемов
ДН-1	Дверь наружняя. См. спецификацию заполнения дверных проемов
Д-1	Дверь межкомнатная
ДН-3п	Дверь противопожарная

Примечание:

1) Привязка проёмов окон и дверей в клееном брусе указывается с учетом обсады

Согласовано:

Взам. инв. №


Подпись и дата

Инв. № подл.

					2020	#ID Проекта	
						Адрес: #Полный Адрес Участка	
Изм.	Кол.уч	Лист	№док.	Подпись	Дата		
						Индивидуальный жилой дом	стадия: РП; лист: 20; листов:
Архитектор		Салыкова В.Г.					
Конструктор						Маркировочный план 2 этажа М 1:100	
Заказчик		#Обращение к Заказчику					

М 1:100

План кровли

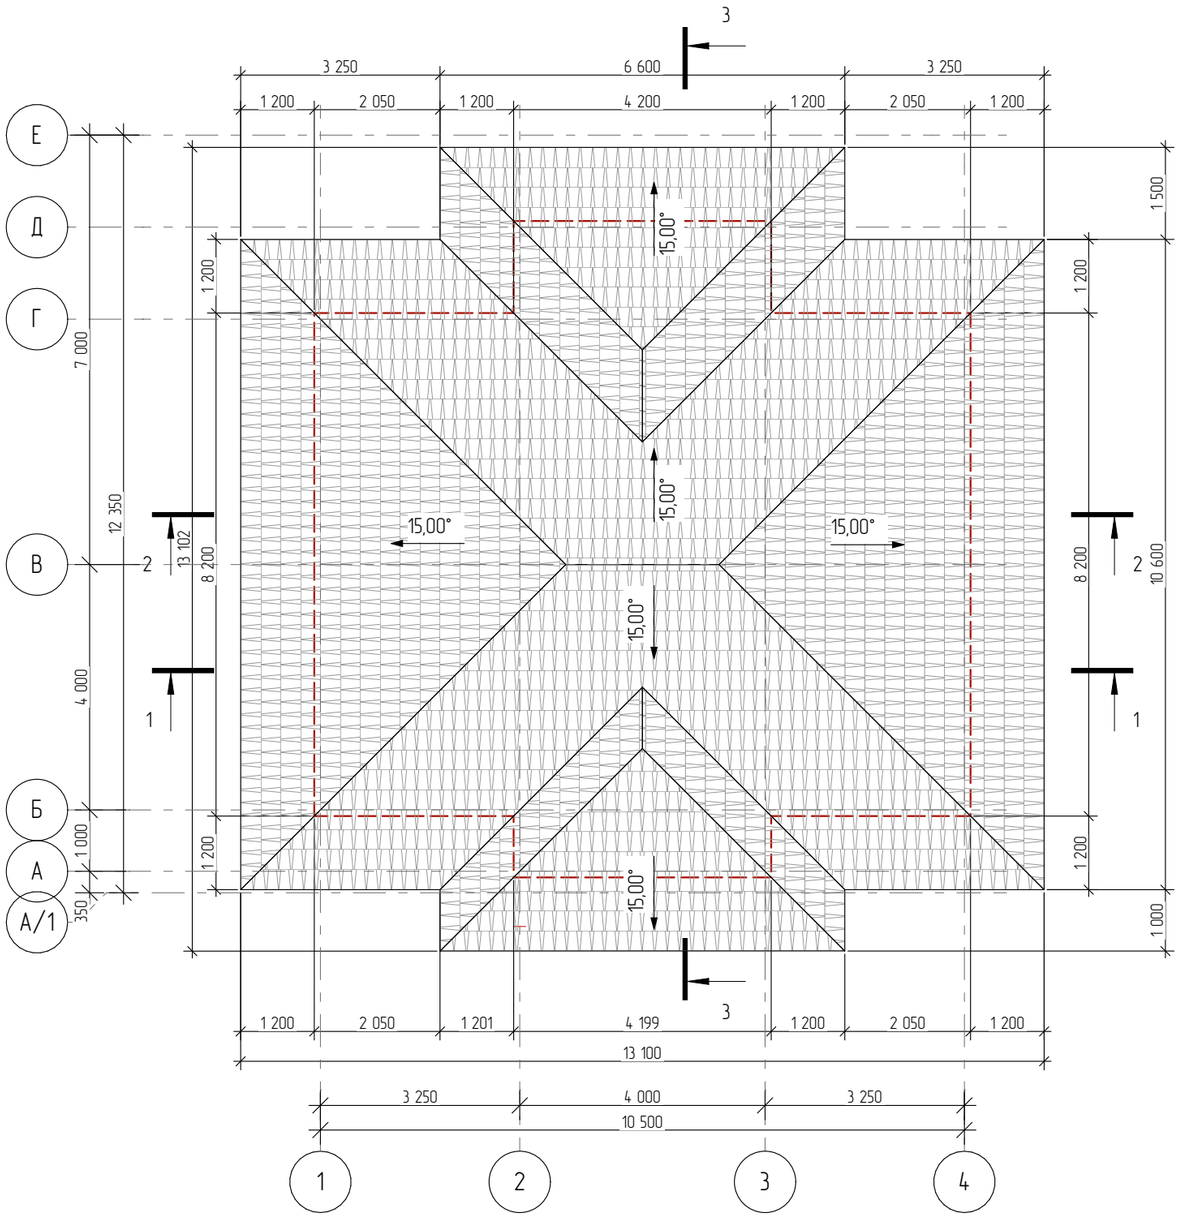

Примечание:

1) Все размеры даны в горизонтальной проекции
2) Наличие снегозадержателей и водосточной системы определяется сметным расчётом.
3) Погрешность монтажа вент выхода по горизонтали 16см а по длине волны 38 (при монтаже в металлочерепицу или Брас)
4) Монтаж кровельного покрытия выполнять в соответствии с инструкциями завода-изготовителя.
5) Расположение вентиляционных коммуникаций и прочих инженерных систем показано условно. Проект инженерных коммуникаций будет разрабатываться при заключении договора на инженерные работы. Количество и наличие вентиляционных, фановых и дымовых труб определяется дополнительным согласованием в сметном расчёте на этапе отделочных работ.

Условные обозначения:

- - — — - контур наружной стены


Согласовано


Взам. инв. №

Подпись и дата

Инв. № подл.

					2020	#ID Проекта			
						Адрес: #Полный Адрес Участка			
Изм.	Кол.уч	Лист	№док.	Подпись	Дата				
						Индивидуальный жилой дом	стадия	лист	листов
							РП	21	
Архитектор		Салыкова В.Г.				План кровли М 1:100			
Конструктор									
Заказчик		#Обращение к Заказчику							

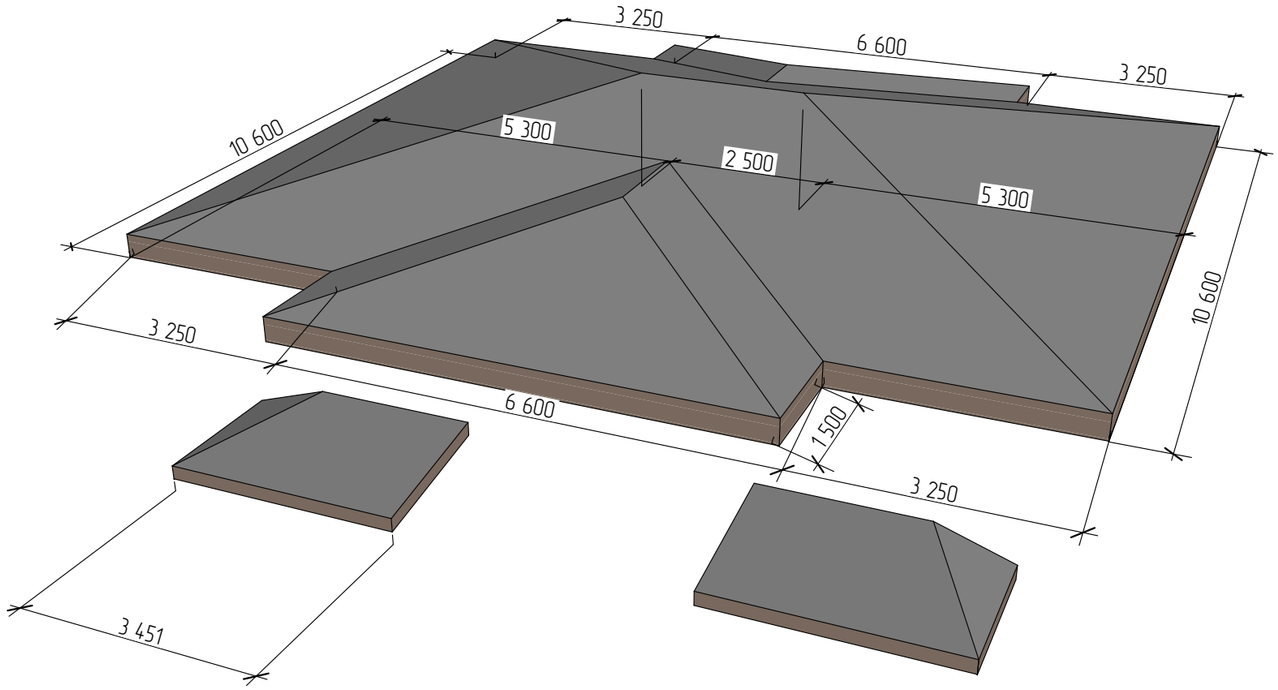

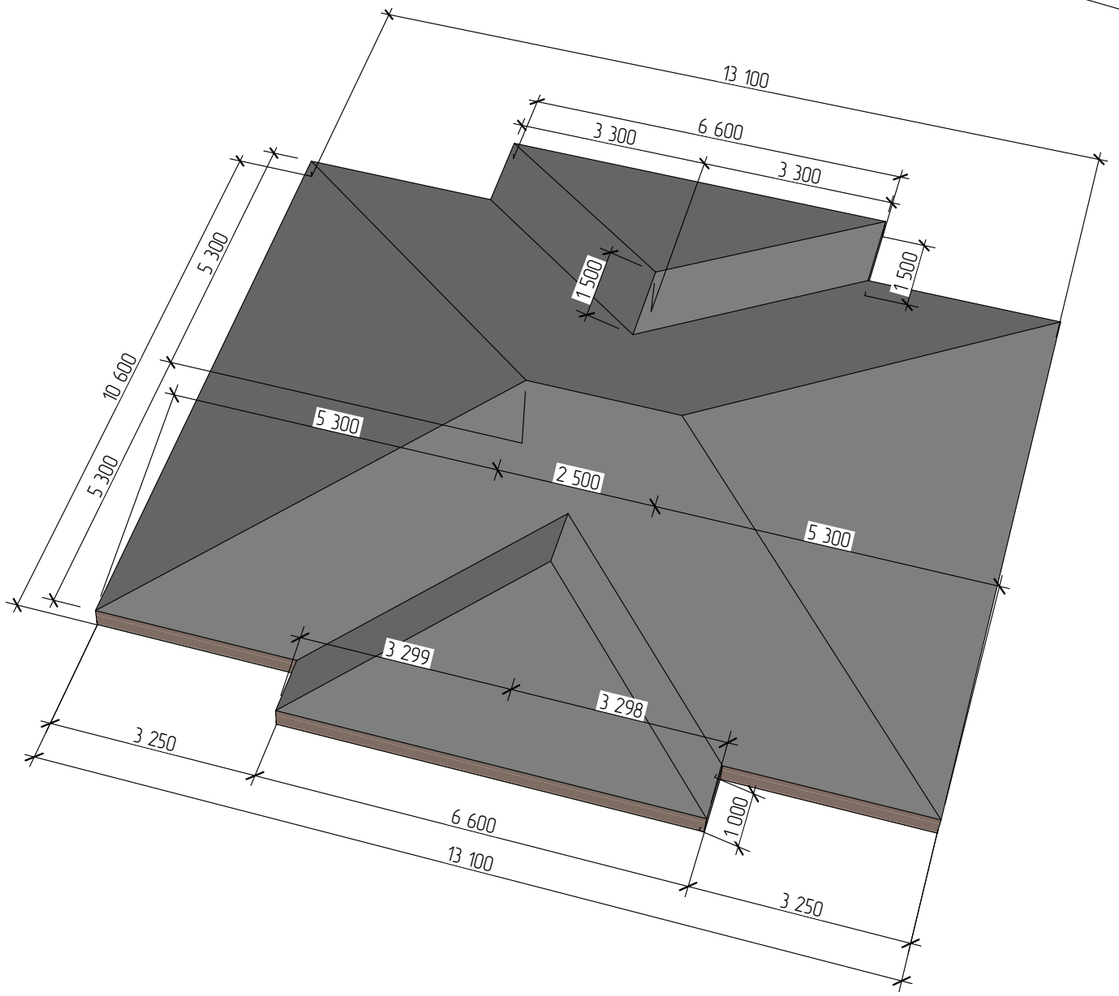

Примечение:
Привязка окна см. разрез 1-1 и план кровли лист 18

Общий вид крыши









Лист
ДСП № 30/10 - КБ22

Согласовано

Взам. инв. №

Подпись и дата

Инв. № подл.

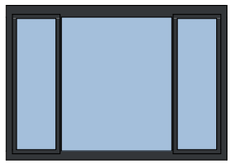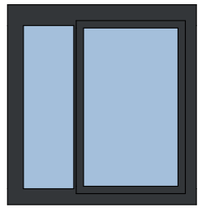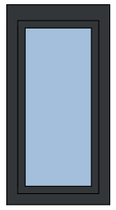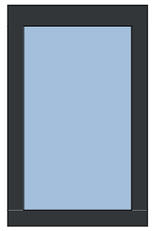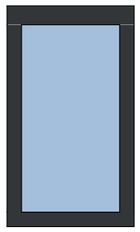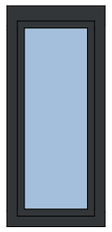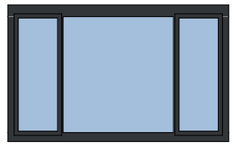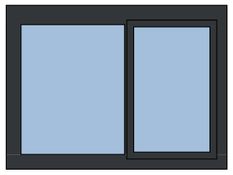Поз.	ОК-1	ОК-2	ОК-3	ОК-4
Общий вид				
Проем, мм	3 060×2 060	1 400×1 450	700×1 450	1 000×1 620
Поз.	ОК-4	ОК-5	ОК-6	ОК-7
Общий вид				
Проем, мм	1 000×1 800	700×1 710	3 060×1 800	1 800×1 260

Спецификация окон

Поз.	Обозначение	Проем, мм	Кол-во, шт	Этаж	Примечание
ОК-1		3 060×2 060	1	1 этаж	
ОК-2		1 400×1 450	1	1 этаж	
ОК-3		700×1 450	2	1 этаж	
ОК-4		1 000×1 620	1	2 этаж	
ОК-4		1 000×1 800	1	1 этаж	
ОК-5		700×1 710	1	1 этаж	
ОК-6		3 060×1 800	1	2 этаж	
ОК-7		1 800×1 260	2	2 этаж	

Примечание:

1) Открывание окон, итоговые размеры оконных/дверных проемов и блоков, и их конструкции, расположение, кол-во, наличие шпросов, а также доп. декоративных и конструктивных элементов согласовывается с фирмой производителем/Подрядчиком.

2) Окна показаны снаружи.

3) Итоговый материал изготовления окон определяется сметным расчётом

4) В габариты оконных проемов включен размер обсадной коробки.

5) Оконный проем (фактический размер окна отличается на размер обсадной коробки и технологического зазора на установку. Ориентировочно размер изделия будет меньше на 15 см на всю ширину и высоту окна)

Согласовано:





Взам. инв. №



Подпись и дата

Инв. № подл.

					2020	#ID Проекта
						Адрес: #Полный Адрес Участка
Изм.	Кол.уч	Лист	№док.	Подпись	Дата	
						Индивидуальный жилой дом
Архитектор		Салыкова В.Г.				
Конструктор						Спецификация заполнения оконных проёмов
Заказчик		#Обращение к Заказчику				

стадия	лист	листов
РП	23	

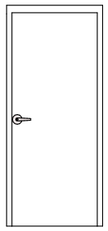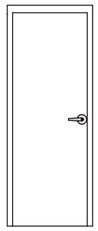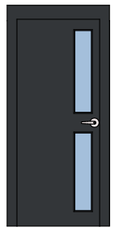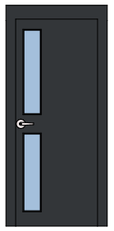Поз.	Д-2	Д-3	ДН-1кб	ДН-2кб
Общий вид				
Проем, мм	800×2 000	700×2 000	850×2 025	850×2 050

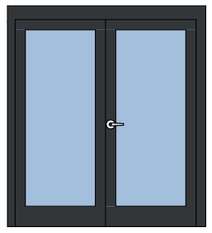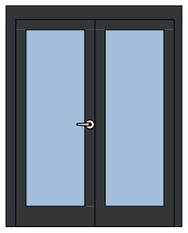Поз.	ДН-3кб	ДН-4кб
Общий вид		
Проем, мм	1 820×2 050	1 600×2 050

Спецификация дверей

Поз.	Ориентация	Обозначение	Проем, мм	Кол-во, шт	Этаж	Площадь Проема	Примечание
Д-2	П		800×2 000	2	1 этаж	1,97	
Д-2	П		800×2 000	2	2 этаж	1,92	
Д-2	Л		800×2 000	1	2 этаж	1,92	
Д-3	П		700×2 000	1	1 этаж	1,76	
Д-3	Л		700×2 000	1	2 этаж	1,70	
ДН-1кб	Л		850×2 025	1	1 этаж	2,31	
ДН-2кб	П		850×2 050	1	1 этаж	2,34	
ДН-3кб	П		1 820×2 050	1	1 этаж	4,58	
ДН-3кб	Л		1 820×2 050	1	1 этаж	4,58	
ДН-4кб	Л		1 600×2 050	2	2 этаж	4,06	
						35,09 м²	

Примечание:

1) Открывание дверных проемов; расположение, количество и наличие шпросов согласовывается с фирмой производителем в отдельной спецификации.

2) Двери показаны снаружи.

3) Итоговый материал изготовления дверей определяется сметным расчётом

4) Двери с маркировкой кб. Пример Д-1кб даны на плане с размерами с учетом обсады в стенах из клееного бруса. Проемы по высоте выпиливаются по месту. В спецификации указан размер с деревянной коробкой.

5) Дверной проем (фактический размер двери в стене из клееного бруса отличается на размер обсадной коробки и технологического зазора на установку по ширине. Ориентировочно размер изделия будет меньше на 10 см на всю ширину двери, по высоте проем выбирается по месту)

Согласовано:

Взам. инв. №

Подпись и дата

Инв. № подл.

					2020	#ID Проекта
						Адрес: #Полный Адрес Участка
Изм.	Кол.уч	Лист	№док.	Подпись	Дата	
						Индивидуальный жилой дом
Архитектор		Салыкова В.Г.				
Конструктор						Спецификация заполнения дверных проёмов
Заказчик		#Обращение к Заказчику				

стадия	лист	листов
РП	24	

Вид 1



Согласовано

Взам. инв. №

Подпись и дата

Инв. № подл.

Общие виды

Лист

ДСП № 30/10 - КБ25

Вид 2



Согласовано

Взам. инв. №

Подпись и дата

Инв. № подл.

Общие виды

Лист

ДСП № 30/10 - КБ26

Вид 3



Общие виды

Лист

ДСП № 30/10 - К627

Согласовано

Взам. инв. №

Подпись и дата

Инв. № подл

Вид 4



Согласовано

Взам. инв. №

Подпись и дата

Инв. № подл.

Общие виды

Лист

ДСП № 30/10 - КБ28

Согласовано

Инв № подл | Подпись и дата | Взам инв №

Общие виды 1 этаж

Лист
Дсп №
30/10 -
К629






Общие виды 2 этаж

Лист

Лист №
30/10 -
КБ30



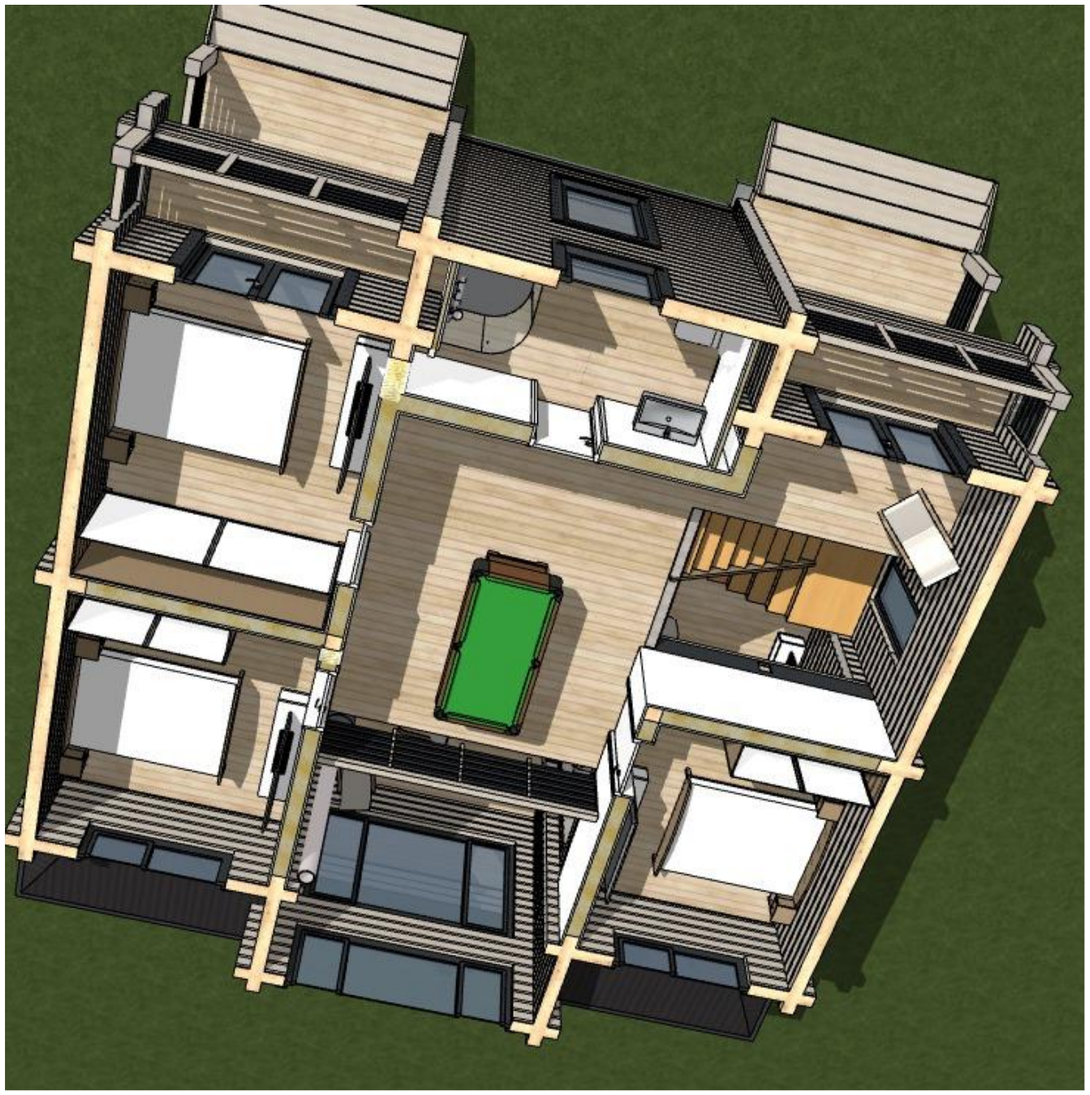

Согласовано

Инв № подл

Подпись и дата

Взам инв №