ПРОЕКТНАЯ ДОКУМЕНТАЦИЯ

Индивидуальный жилой дом

кадастровый номер Россия

#ID Проекта



РОССИЯ
2024

Ведомость листов

Наименование	Лист
Обложка	
Общие данные	02
Сводная ведомость материалов	03
Генеральный план	04
3D Виды	05
План фундамента	06
3Д вид фундамента	07
Схема нижнего армирования фундмаента	08
Схема верхнего армирования фундмаента	09
Узлы фундамента	10
Схема арматурного каркаса фундаментной плиты	11
План на отм. ±0.000	12
План коммуникаций	13
Наружные сети	14
Каталог дверных проемов	15
Каталог оконных проемов	16
Маркировка оконных проемов первого этажа	17
Маркировка дверных проемов первого этажа	18
Разрез 1 - 1	19
Разрез 2 - 2	20
Разрез по стене	21
План перекрытия +3,100	22
План кровли	23
План расстановки мебели 1 этаж	24
Экспликация помещений 1- го этажа	25
Фасад в осях 1-5	26
Фасад в осях Д-А	27
Фасад в осях А-Д	28
Фасад в осях 2-1	29

Изм.	Кол.уч.	Лист	№Док.	Подп.	Дата	#ID Проекта		
						кадастровый номер Россия		
Разраб.						Индивидуальный жилой дом	Стадия: #Стадия Проекта	Лист: 02 / Листов:
						Общие данные		

ВЕДОМОСТЬ ПЕРЕКРЫТИЙ	
Наименование	Объем, м3
Монолитная плита	25,08

ИКК-03 Кровля	
Наименование	Площадь Ве...
Кровля	108,49

ВЕДОМОСТЬ БЛОКА ДЛЯ СТЕН		
Имя	Тип конструкций	Объем, м3
Газобетон D400	Несущие 400мм	55,25
Газобетон перегородки	Перегородки 100мм	6,44

ВЕДОМОСТЬ БЕТОНА	
Наименование	Объем, м3
Плита фундамента	44,60

Отделочные материалы		
Наименование	**Компоненты**	
	Толщина [м]	**Площадь [м2]**
Алюминий-Фиброцементная плита		
	10	138,95


ВЕДОМОСТЬ НА УТЕПЛИТЕЛЬ ДЛЯ СТЕН, ПОЛА ПЕРВОГО ЭТАЖА, РОСТВЕРКА			
Наименование	**Компоненты**		
	Толщина [м]	**Объем [м3]**	**Площадь [м2]**
Изоляция - Минеральная Жесткая			
	50	6,83	136,28
Изоляция - ЭППС			
	50	0,58	11,52
	100	8,06	80,58
Экструзионный пенополистирол ТЕХНОНИКОЛЬ CARBON PROF (СТО 72746455-3.3.1-2012) (1)			
	100	10,77	107,73
Экструзионный пенополистирол ТЕХНОНИКОЛЬ CARBON PROF SLOPE (СТО 72746455-3.3.1-2012) (1)			
	50	5,39	107,73


Конструкция пола			
Наименование	**Толщина [м]**	**Объем [м3]**	**Площадь [м2]**
Бетон В 7,5			
	100	12,74	127,44
Мембрана - Гидроизоляция			
	0	0,00	96,00
Стяжка ЦПР			
	80	6,19	96,00
	100	2,99	31,44

Изм.	Кол.уч.	Лист	№Док.	Подп.	Дата	#ID Проекта		
						кадастровый номер Россия		
Разраб.						Индивидуальный жилой дом	Стадия: #Стадия Проекта	Лист: 03
							Листов:	
						Сводная ведомость материалов		

Отступ от границ участка принят
по требованию заказчика

Проектируемый
участок

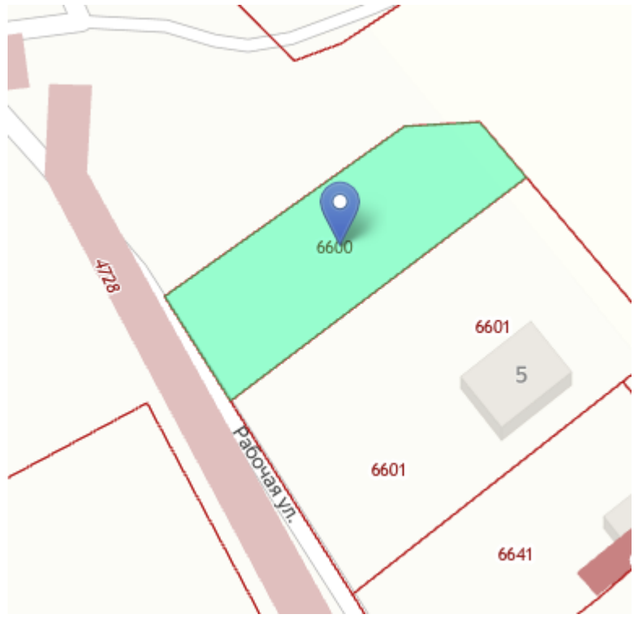

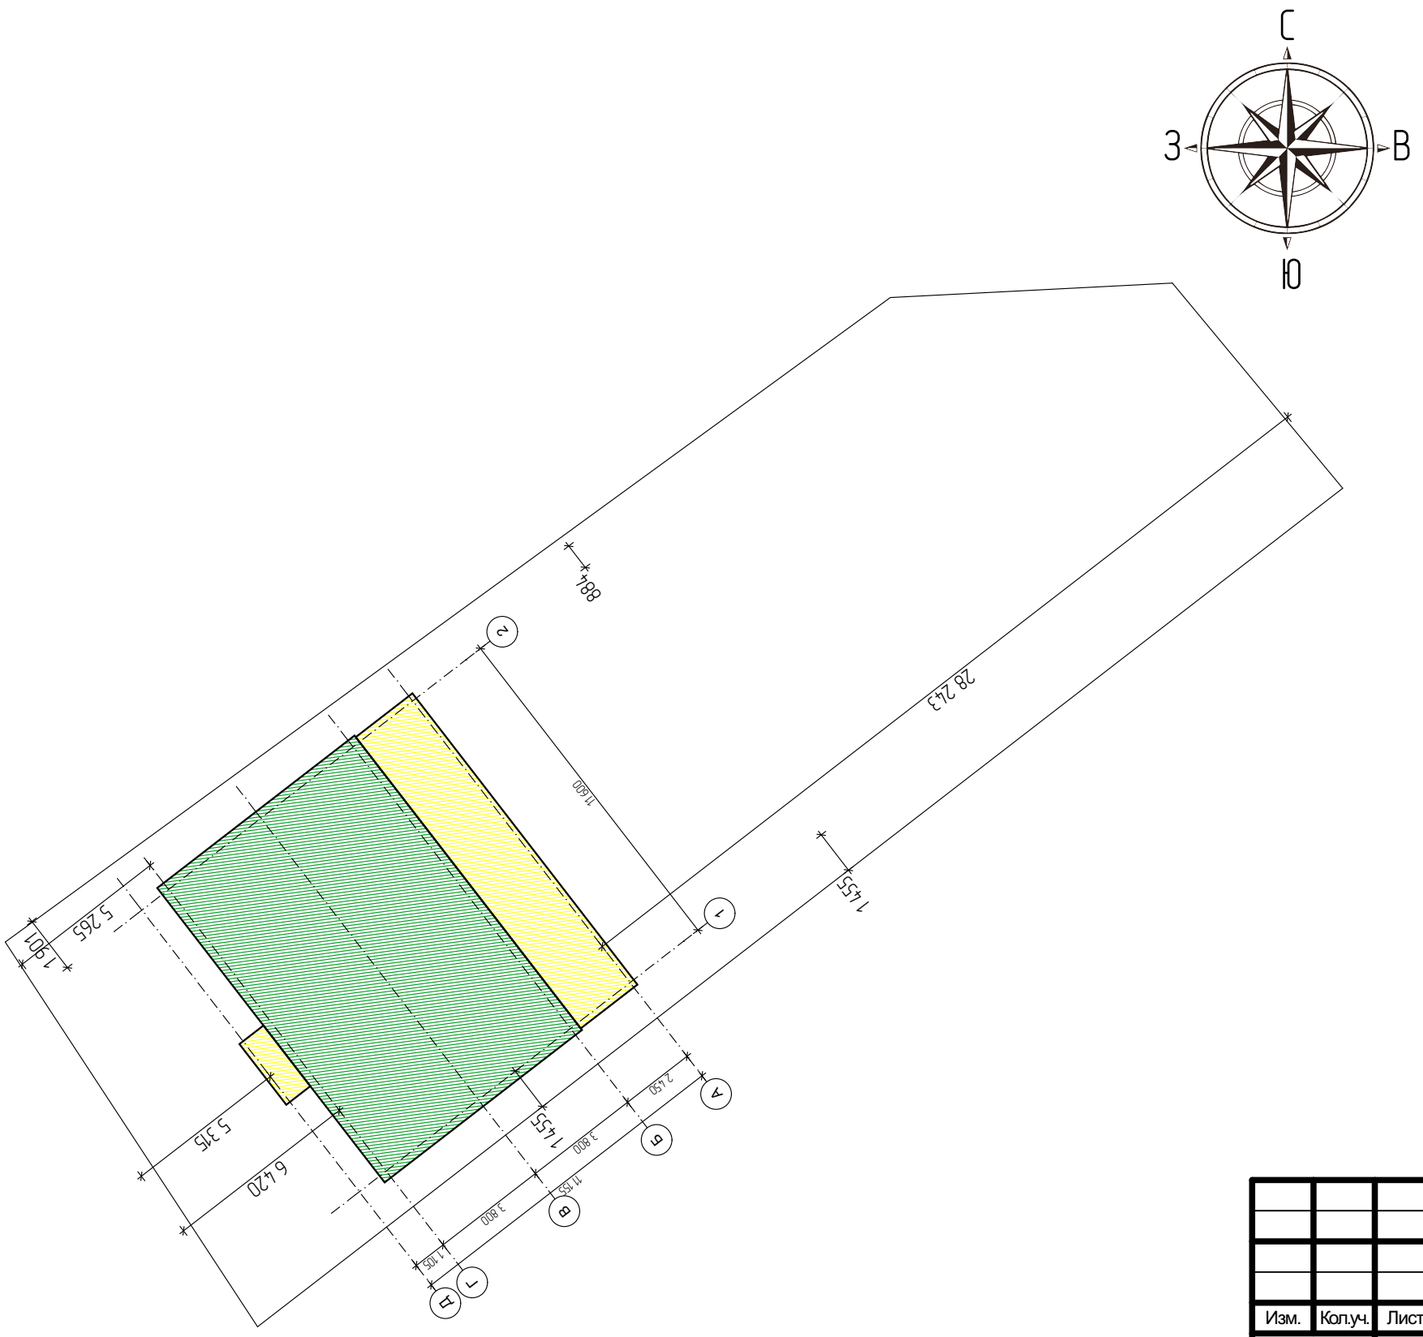

Проектируемый дом

Терраса, крыльцо

						#ID Проекта		
						кадастровый номер Россия		
Изм.	Кол.уч.	Лист	№Док.	Подп.	Дата			
Разраб.						Индивидуальный жилой дом	Стадия: #Стадия Проекта	Лист: 04 / Листов:
						Генеральный план		








						#ID Проекта
						кадастровый номер Россия
Изм.	Кол.уч.	Лист	№Док.	Подп.	Дата	
Разраб.						Индивидуальный жилой дом
						3D Виды

Стадия	Лист	Листов
#Стадия Проекта	05	

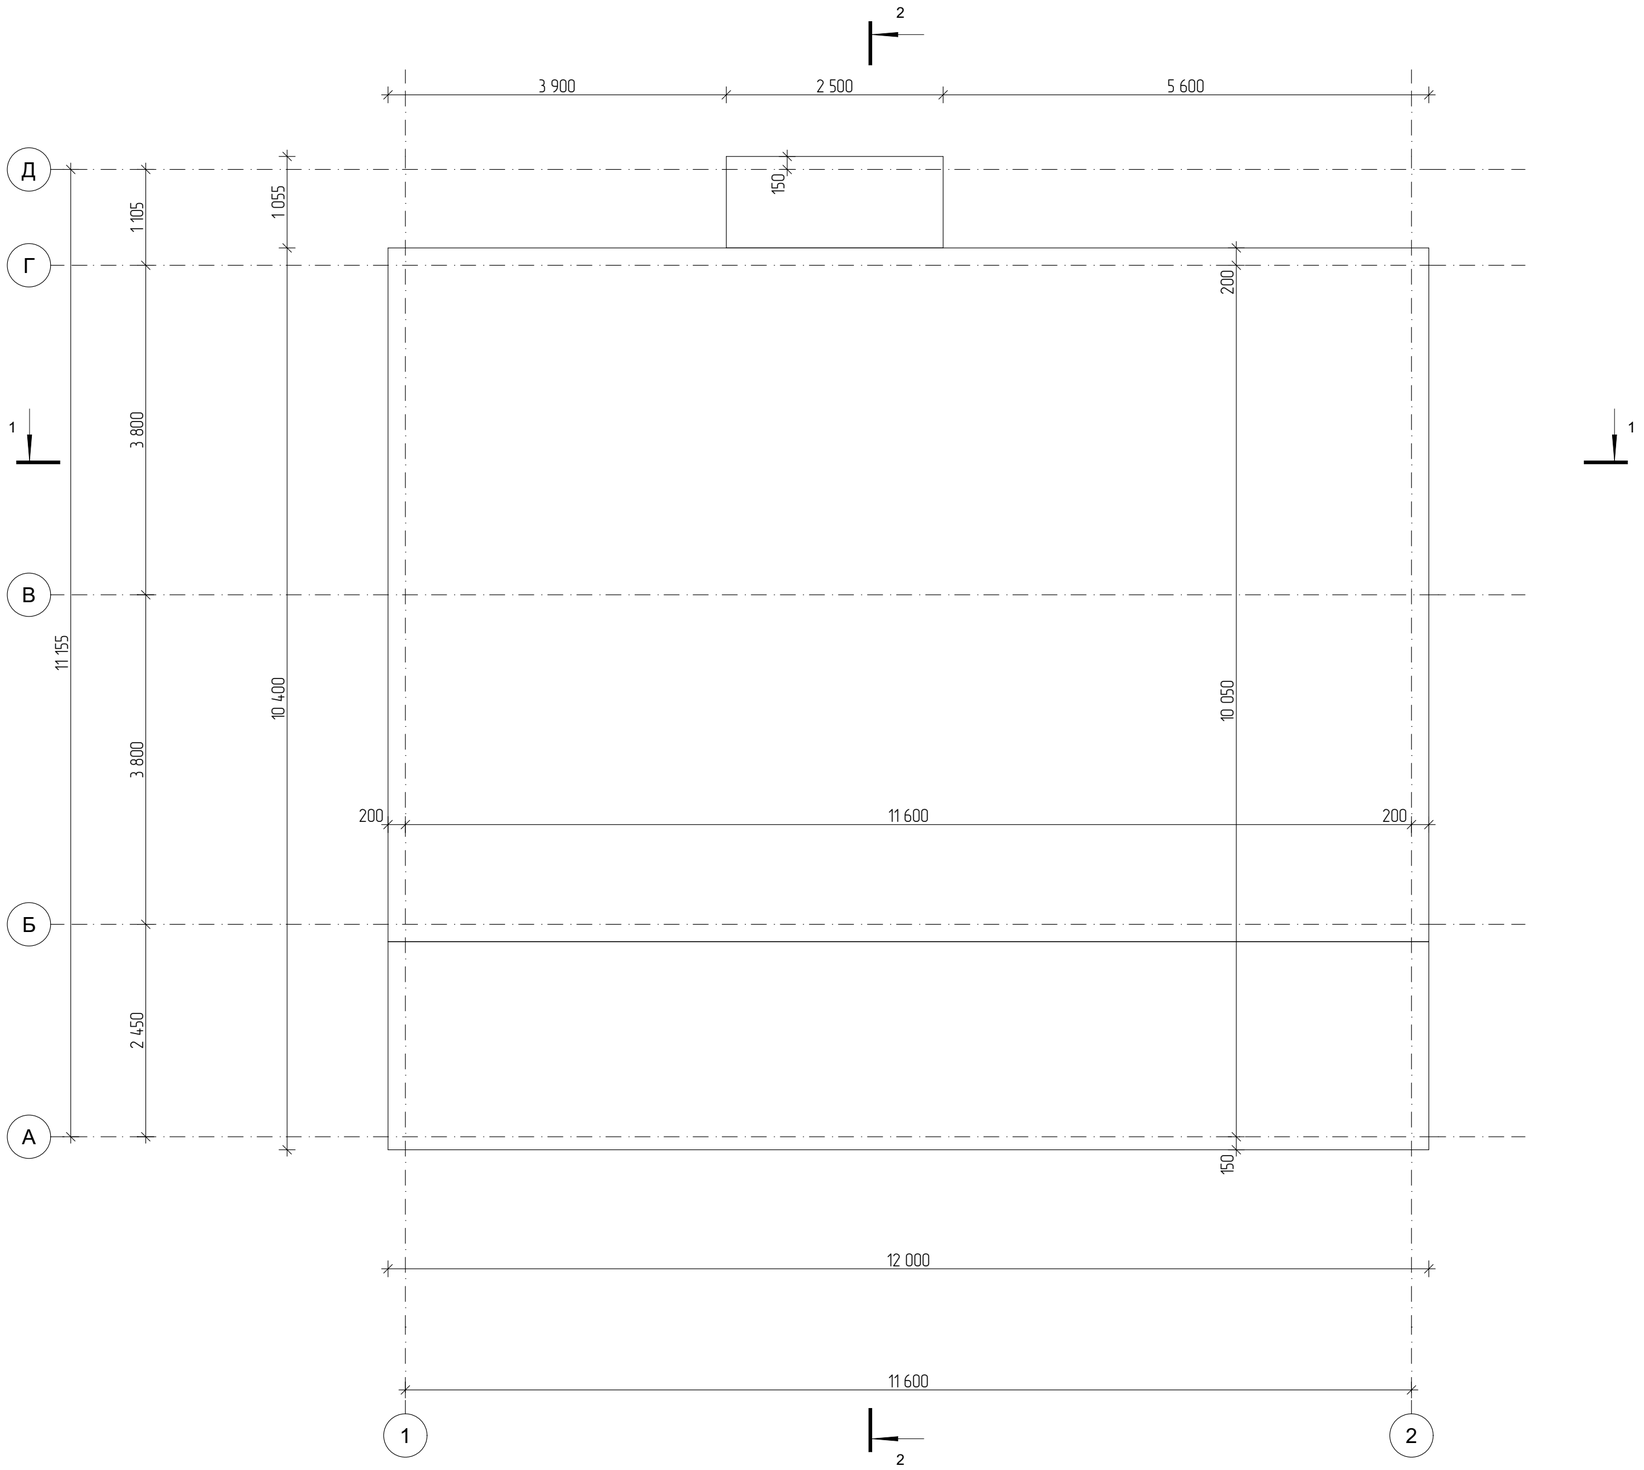


Фундамент выполнить из бетона класса В25


ВЕДОМОСТЬ БЕТОНА

Наименование	Объем, м3
Плита фундамента	44,60


						#ID Проекта		
						кадастровый номер Россия		
Изм.	Кол.уч.	Лист	№Док.	Подп.	Дата			
Разраб.						Индивидуальный жилой дом	Стадия: #Стадия Проекта	Лист: 06 / Листов:
						План фундамента		

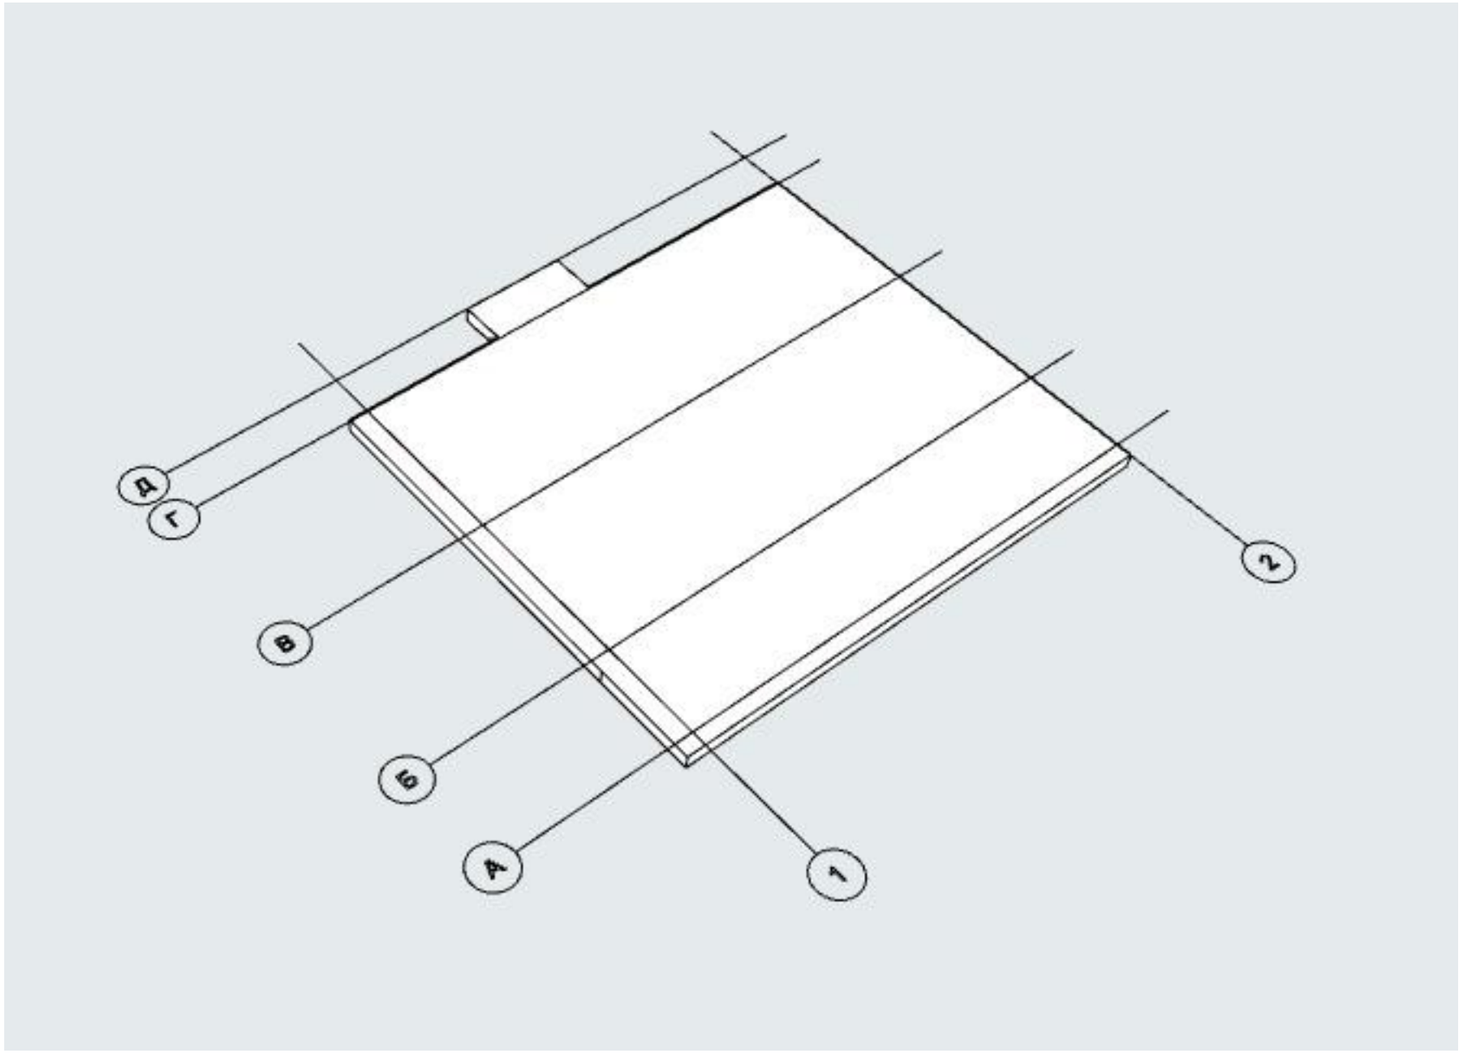


						#ID Проекта		
						кадастровый номер Россия		
Изм.	Кол.уч.	Лист	№Док.	Подп.	Дата			
Разраб.						Индивидуальный жилой дом	Стадия	Лист	Листов
							#Стадия Проекта	07	
						3Д вид фундамента			

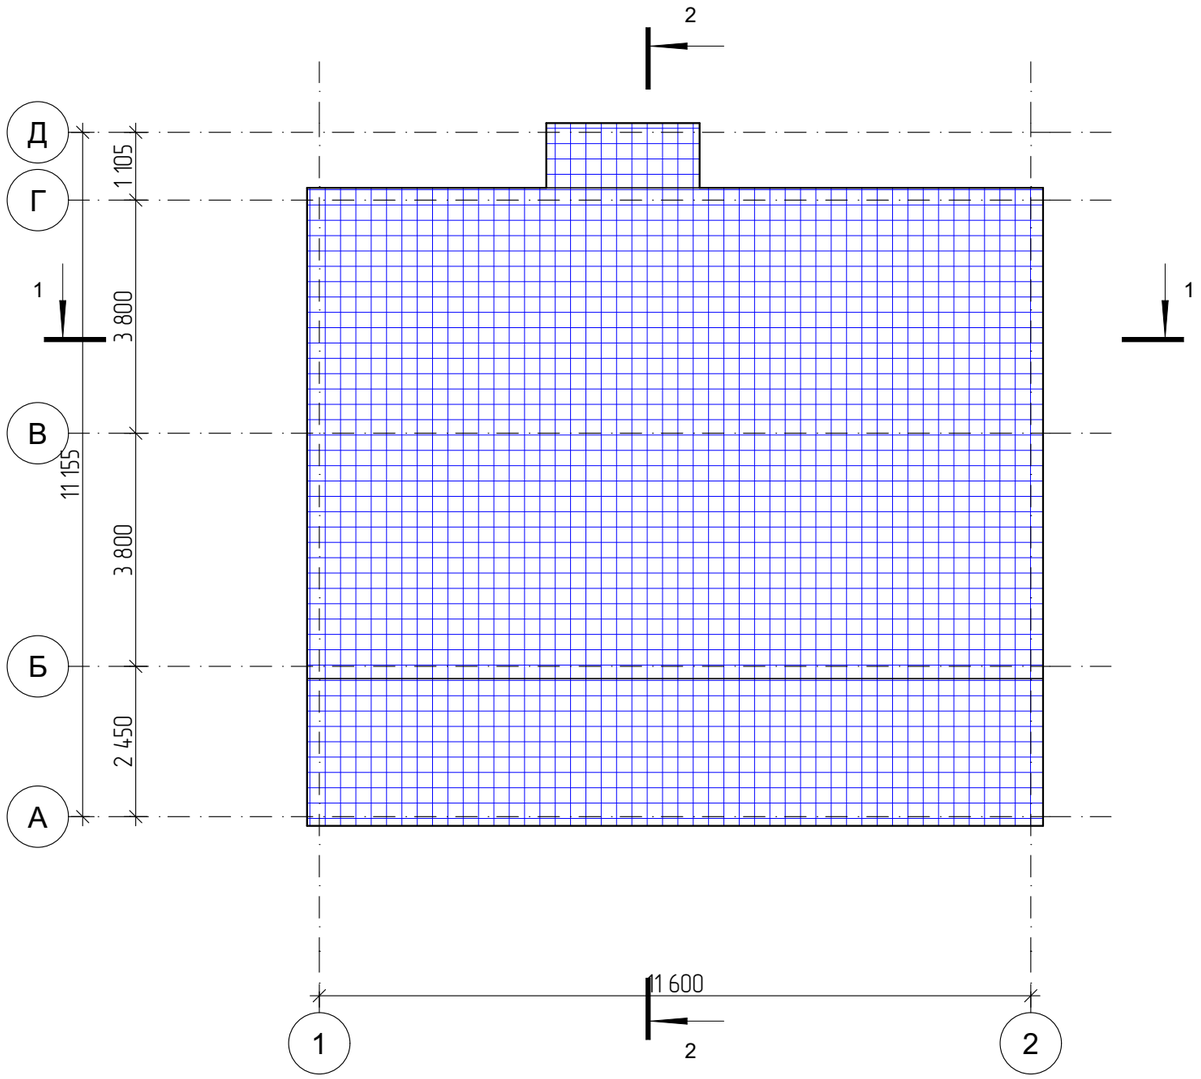


						#ID Проекта		
						кадастровый номер Россия		
Изм.	Кол.уч.	Лист	№Док.	Подп.	Дата			
Разраб.						Индивидуальный жилой дом	Стадия / #Стадия Проекта	Лист / 08	Листов
						Схема нижнего армирования фундмаента		

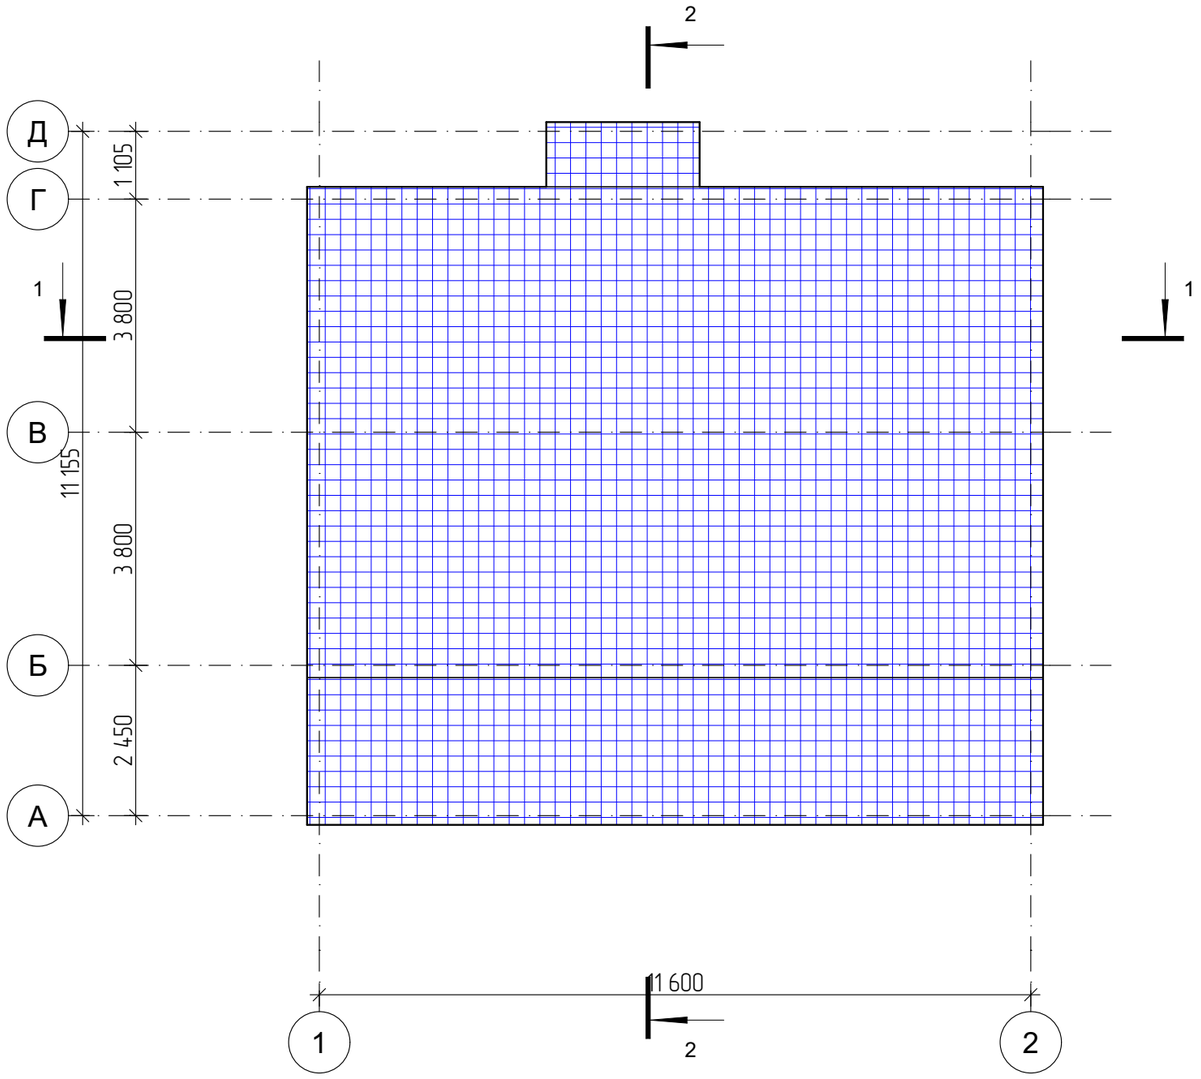


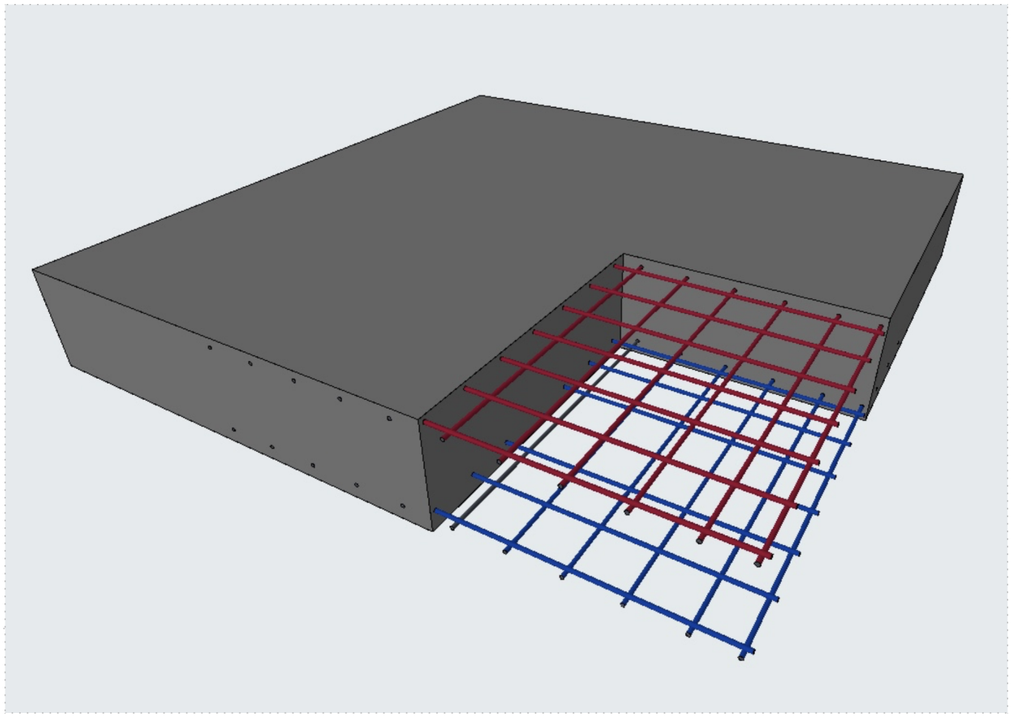



						#ID Проекта		
						кадастровый номер Россия		
Изм.	Кол.уч.	Лист	№Док.	Подп.	Дата			
Разраб.						Индивидуальный жилой дом	Стадия: #Стадия Проекта	Лист: 09 / Листов:
						Схема верхнего армирования фундмаента		

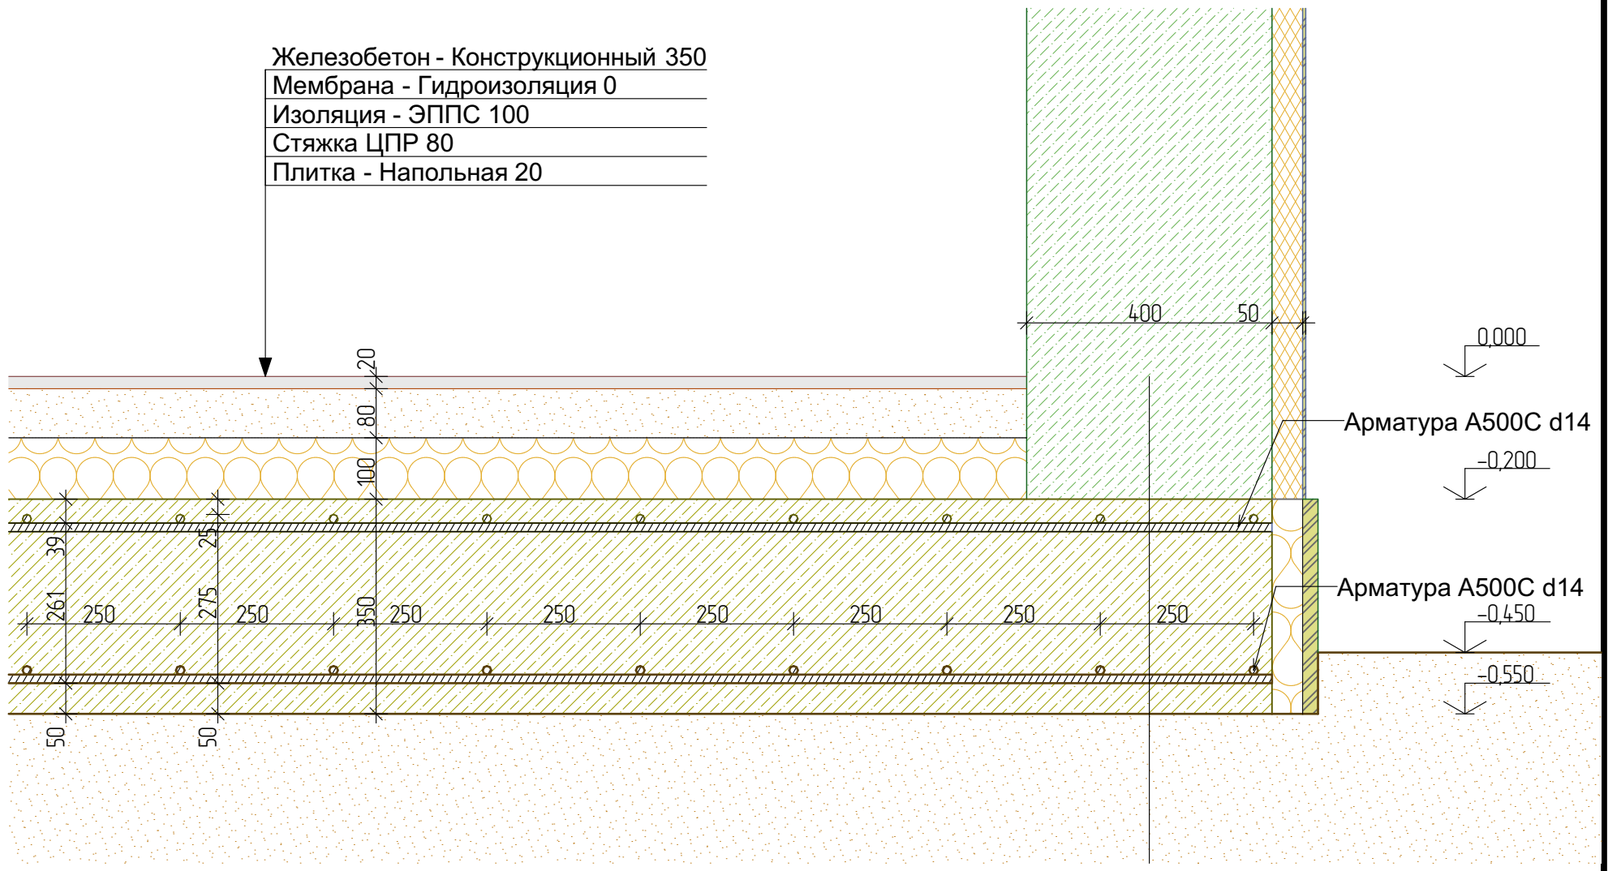

						#ID Проекта		
						кадастровый номер Россия		
Изм.	Кол.уч.	Лист	№Док.	Подп.	Дата			
Разраб.						Индивидуальный жилой дом	Стадия: #Стадия Проекта	Лист: 10 / Листов:
						Узлы фундамента		

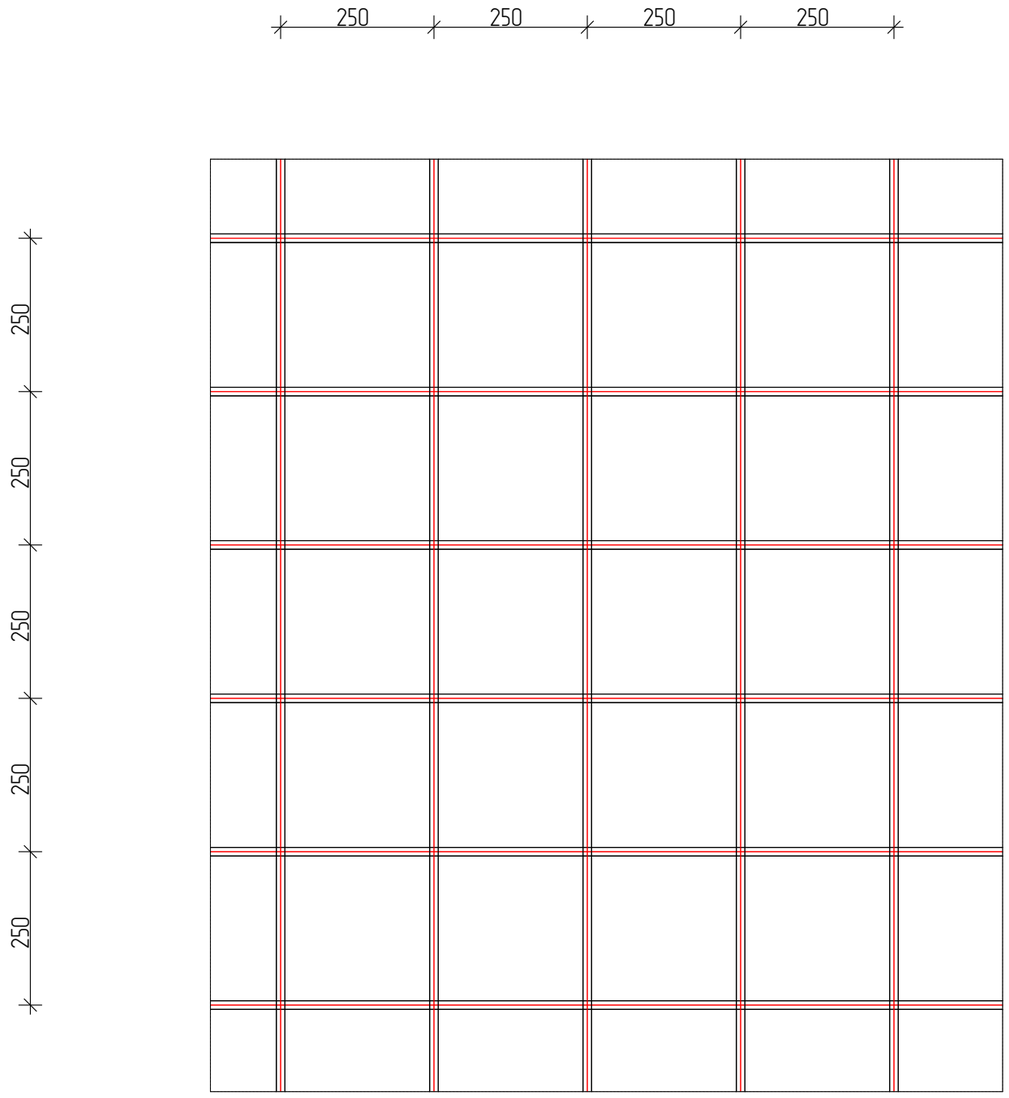

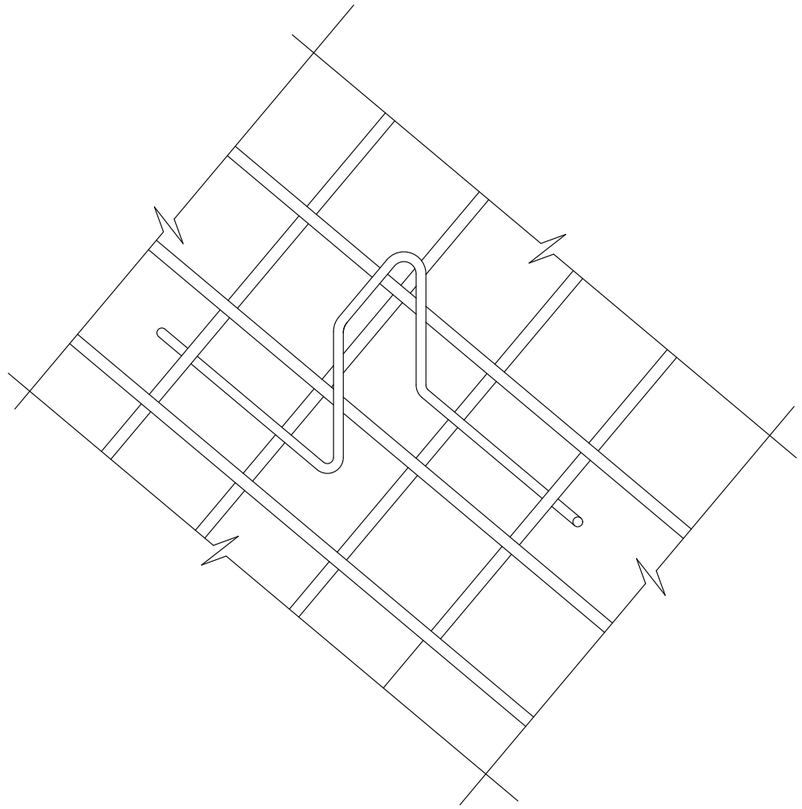


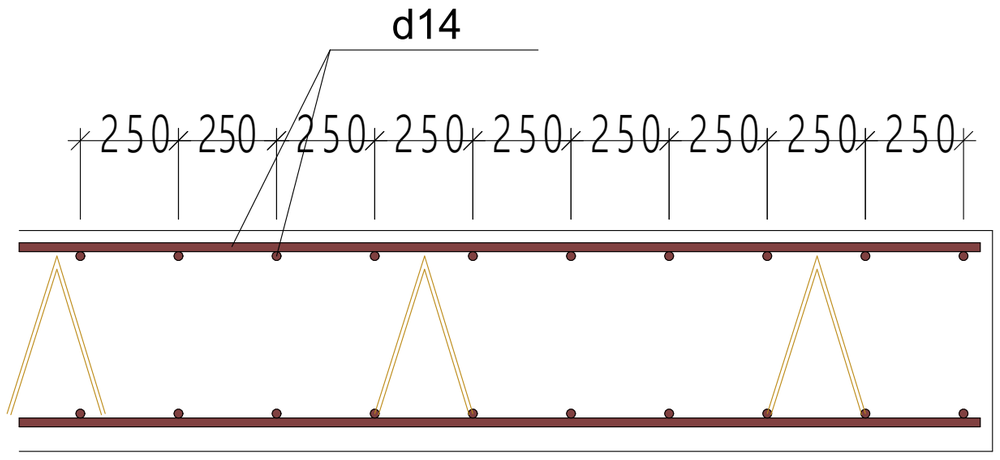

Спецификация элементов к фундаментной плите Фпм-1

МАРКА ПОЗ.	ОБОЗНАЧЕНИЕ	НАИМЕНОВАНИЕ	Кол.	МАССА, КГ	ПРИМЕ-ЧАНИЕ
		Детали			
1		Ø14AIII ГОСТ5781-82* п.м.	2182		


Изм.	Кол.уч.	Лист	№Док.	Подп.	Дата	#ID Проекта		
						кадастровый номер Россия		
Разраб.						Индивидуальный жилой дом	Стадия: #Стадия Проекта	Лист: 11 / Листов:
						Схема арматурного каркаса фундаментной плиты		

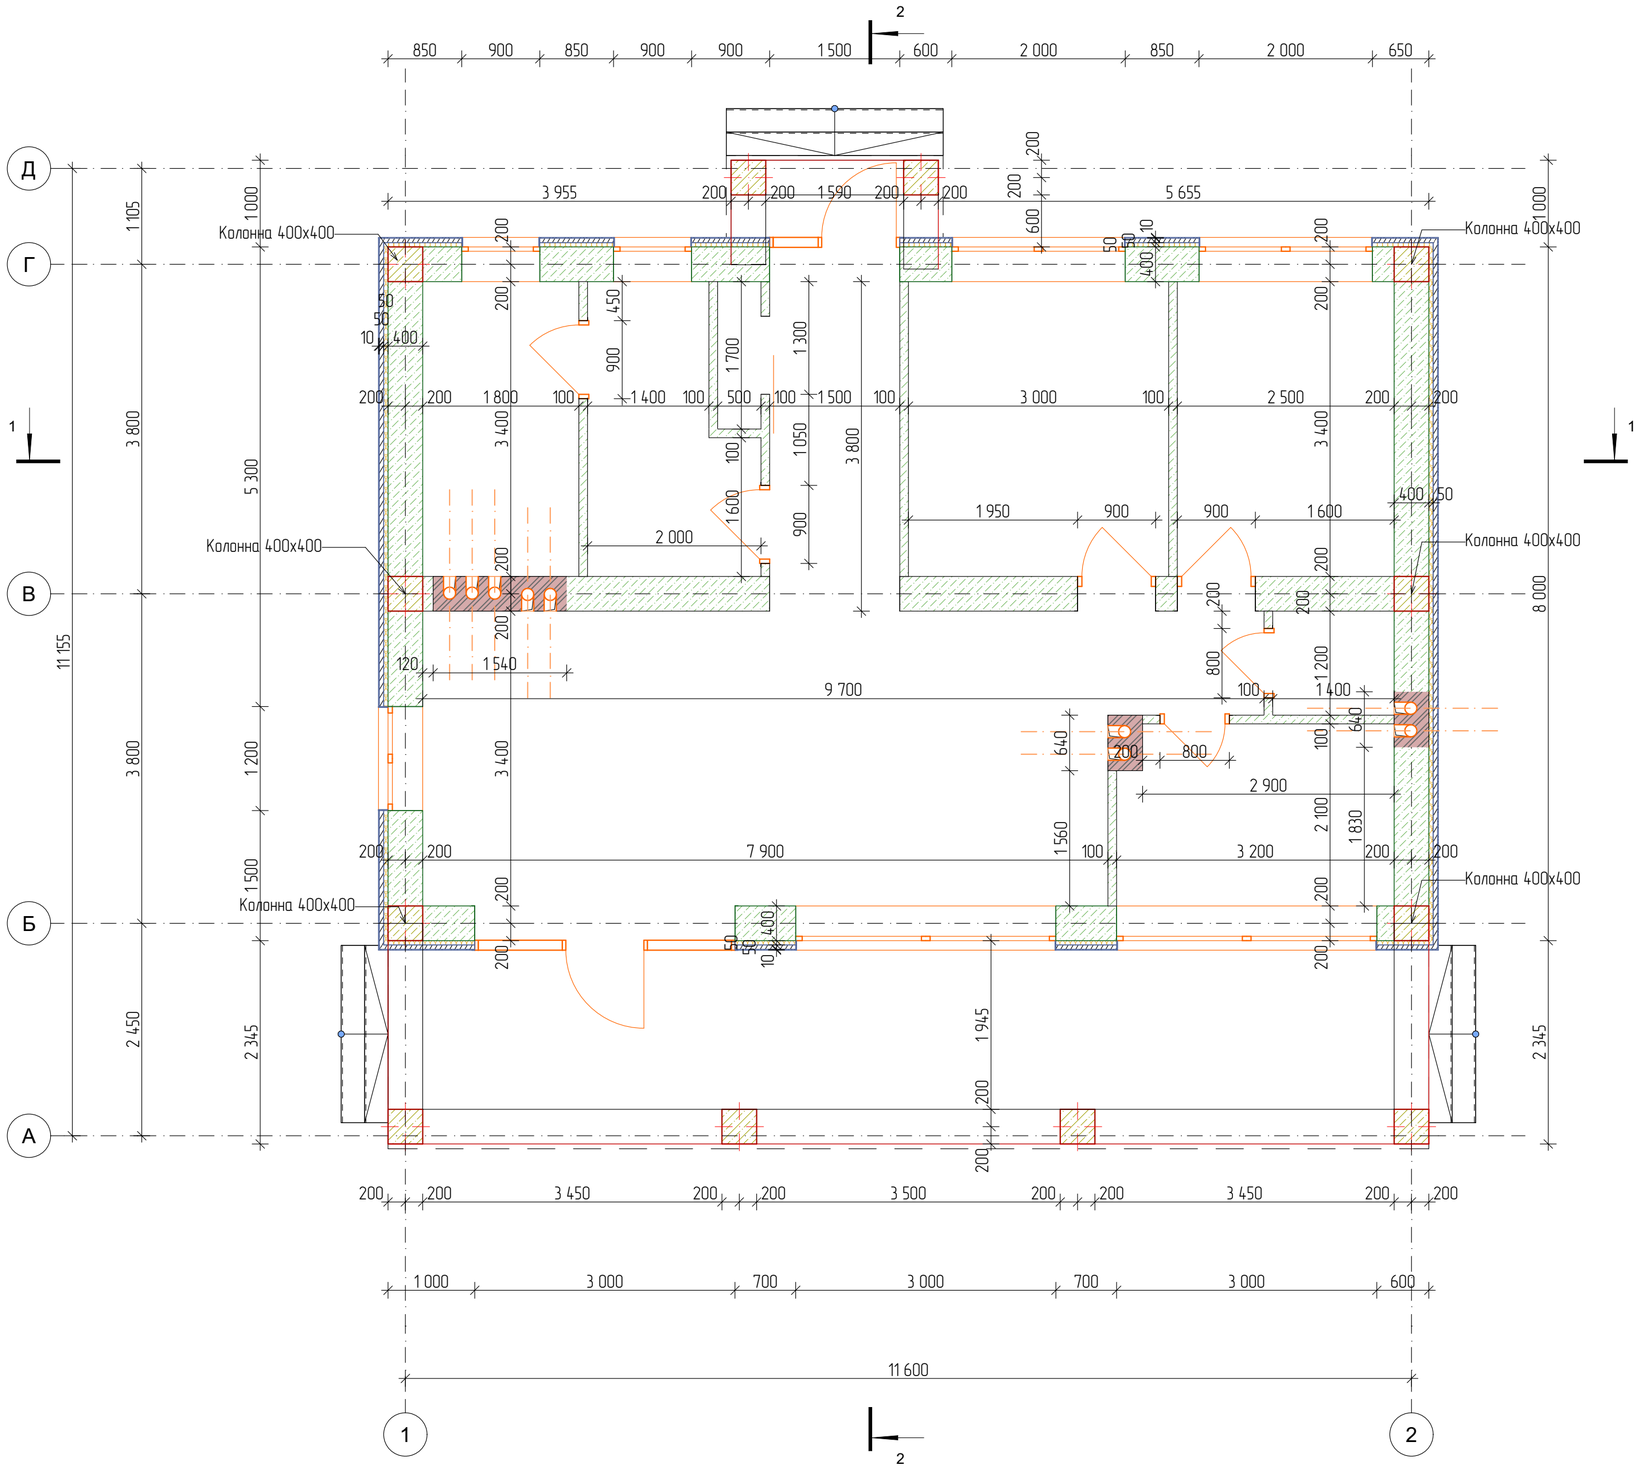


ВЕДОМОСТЬ БЛОКА ДЛЯ СТЕН

Имя	Тип конструкций	Объем, м3
Газобетон D400	Несущие 400мм	55,25
Газобетон перегородки	Перегородки 100мм	6,44





							#ID Проекта	
							кадастровый номер Россия	
Изм.	Колуч.	Лист	№Док.	Подп.	Дата			
Разраб.						Индивидуальный жилой дом	Стадия	Лист	Листов
							#Стадия Проекта	12	
						План на отм. ±0.000			

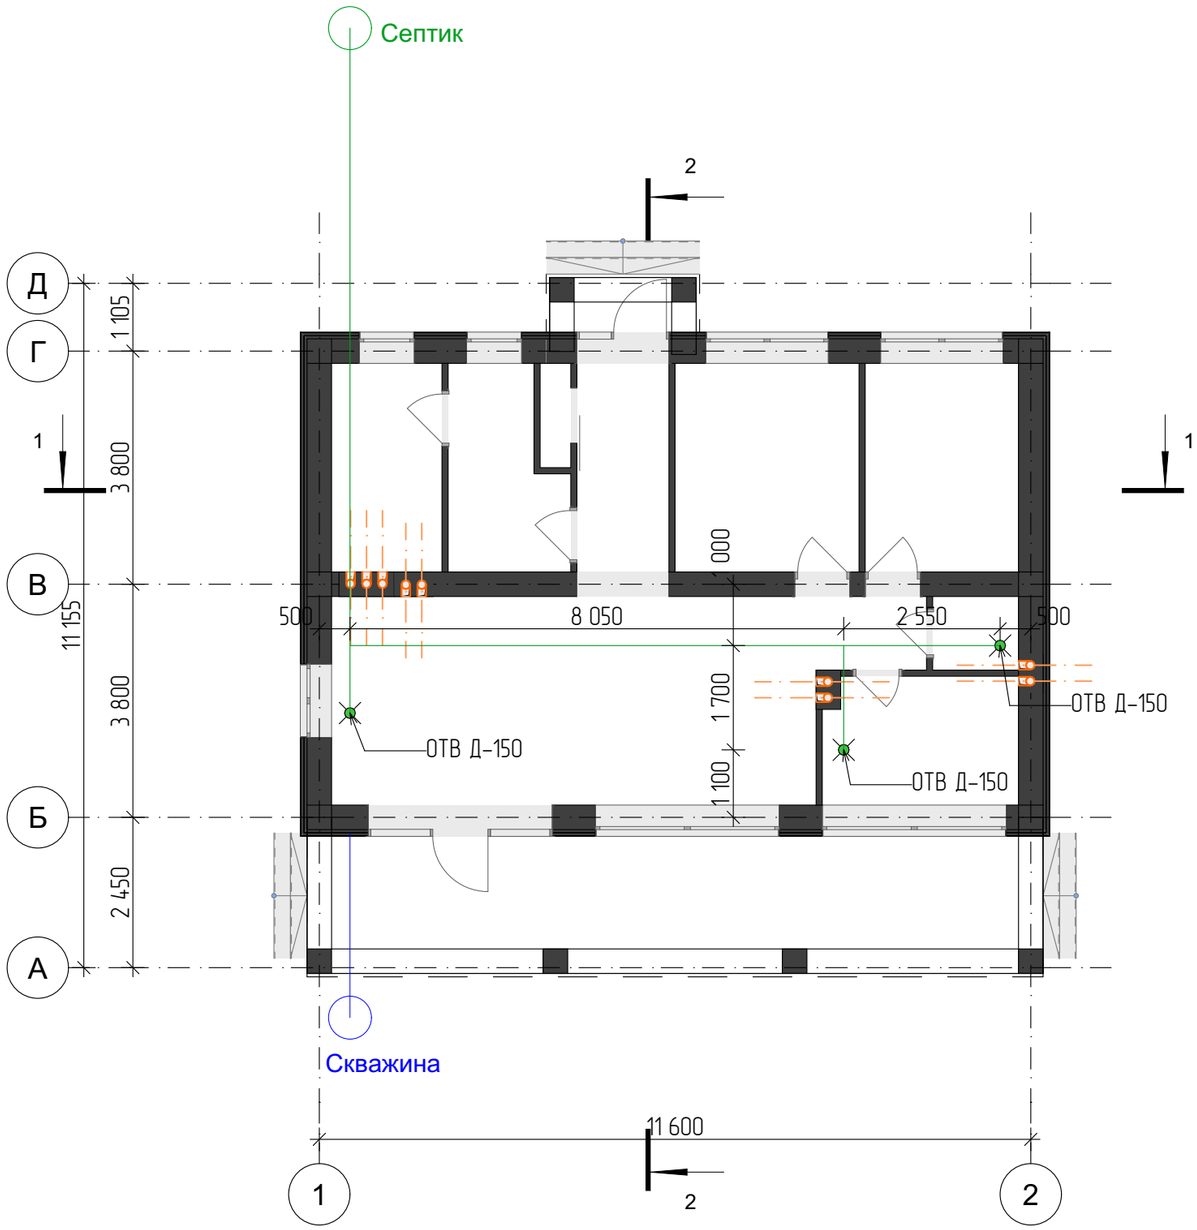

						#ID Проекта	
						кадастровый номер Россия	
Изм.	Кол.уч.	Лист	№Док.	Подп.	Дата		
Разраб.						Индивидуальный жилой дом	Стадия: #Стадия Проекта; Лист: 13; Листов:
						План коммуникаций	




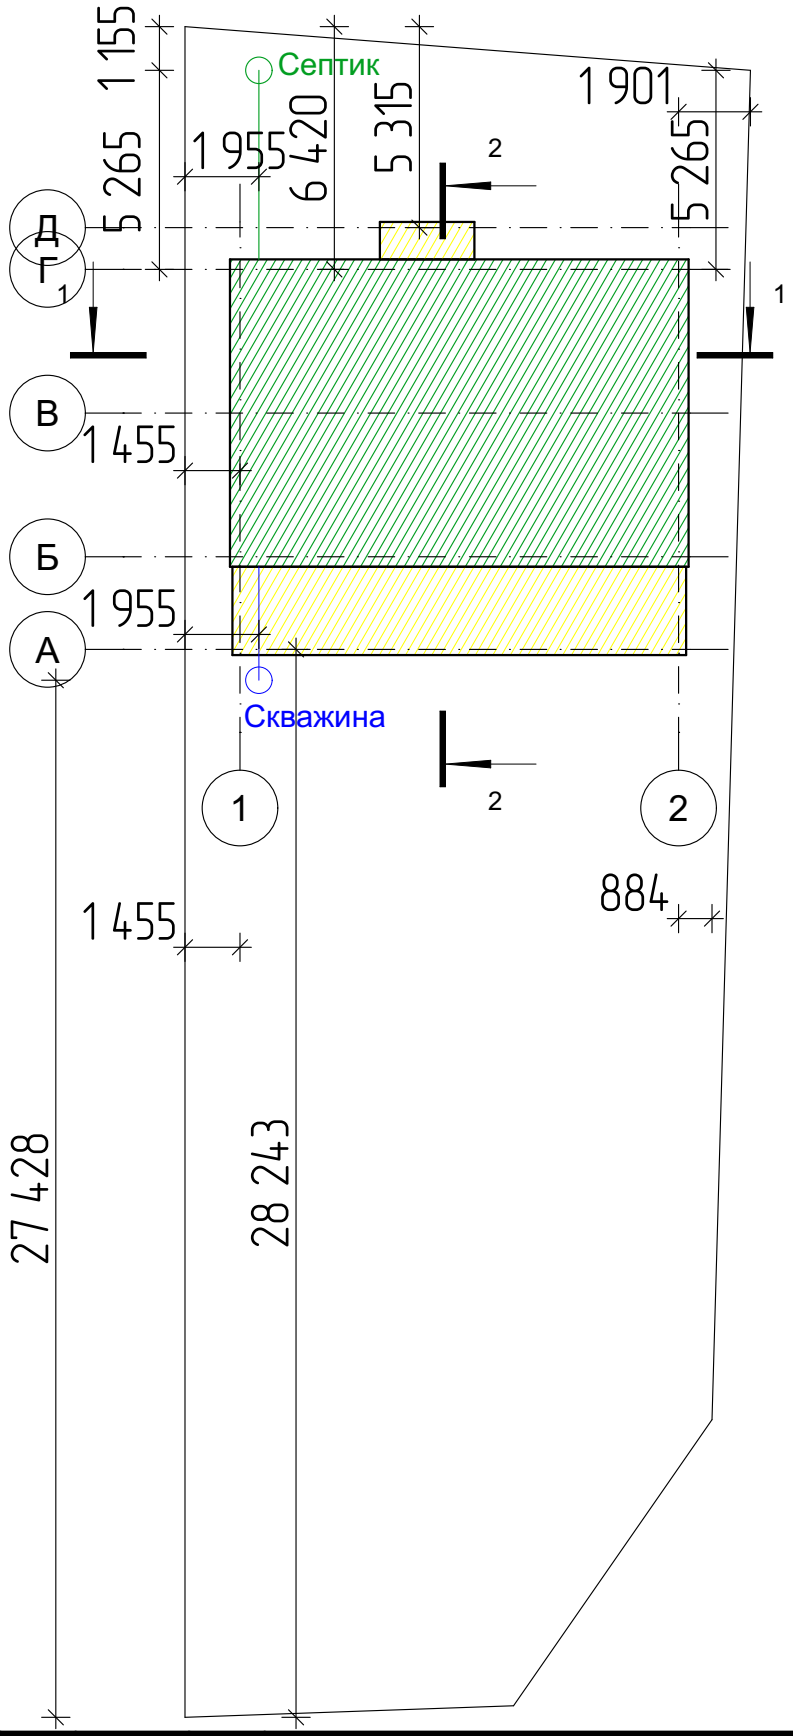


						#ID Проекта	
						кадастровый номер Россия	
Изм.	Кол.уч.	Лист	№Док.	Подп.	Дата		
Разраб.						Индивидуальный жилой дом	Стадия: #Стадия Проекта; Лист: 14; Листов:
						Наружные сети	

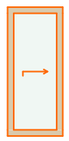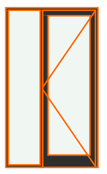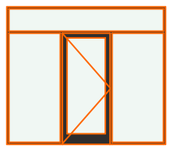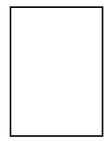
Каталог Дверей								
Полный ID Элемента	Д-1	Д-1	Д-1	Д-2	Д-2	ДВ-1	ДВ-2	П/П
D по Классификации	Дверь -1	Дверь -1	Дверь -1	Дверь -2	Дверь -2	Дверь -1	Дверь -2	Дверь -П/П
Наименование Двери	Наружная Раздвижная Дверь 27	Однопольная Дверь 27	Однопольная Дверь 27	Однопольная Дверь 27	Однопольная Дверь 27	Дверь с Боковой Панелью со Стороны 2 27	Дверь с Боковыми Панелями и Фрамугой 27	Простой Проем Двери
Количество	1	1	3	1	1	1	1	1
Размер Ш x В	900×2 100	900×2 100	900×2 100	800×2 100	800×2 100	1 500×2 600	3 000×2 600	1 500×2 100
Ориентация	Л	Л	П	Л	П	Л	П	
Высота Порога Двери	0	0	0	0	0	0	0	0
Высота Перемычки Двери	2 100	2 100	2 100	2 100	2 100	2 600	2 600	2 100
2D-символ								
Вид со Стороны, Противоположной Стороне Открывания								

						#ID Проекта		
						кадастровый номер Россия		
Изм.	Кол.уч.	Лист	№Док.	Подп.	Дата			
Разраб.						Индивидуальный жилой дом	Стадия: #Стадия Проекта	Лист: 15 / Листов:
						Каталог дверных проемов		


Каталог Окон

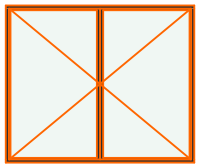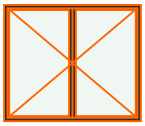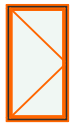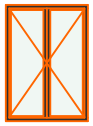Полный ID Элемента	ОК-1	ОК-2	ОК-3	ОК-3	ОК-4
Наименование Окна	Раздвижное Двустворчатое Окно 27	Раздвижное Двустворчатое Окно 27	Окно 27	Окно 27	Раздвижное Двустворчатое Окно 27
Количество	2	2	1	1	1
Размер Ш x В	3 000×2 500	2 000×1 700	900×1 700	900×1 700	1 200×1 700
Ориентация	П	П	Л	П	П
Высота Подоконника Окна	100	900	900	900	900
Высота Перемычки Окна	2 600	2 600	2 600	2 600	2 600
2D-символ					
Вид со Стороны, Противоположной Стороне Открывания					


Изм.	Кол.уч.	Лист	№Док.	Подп.	Дата	#ID Проекта		
						кадастровый номер Россия		
Разраб.						Индивидуальный жилой дом	Стадия: #Стадия Проекта	Лист: 16 / Листов:
						Каталог оконных проемов		

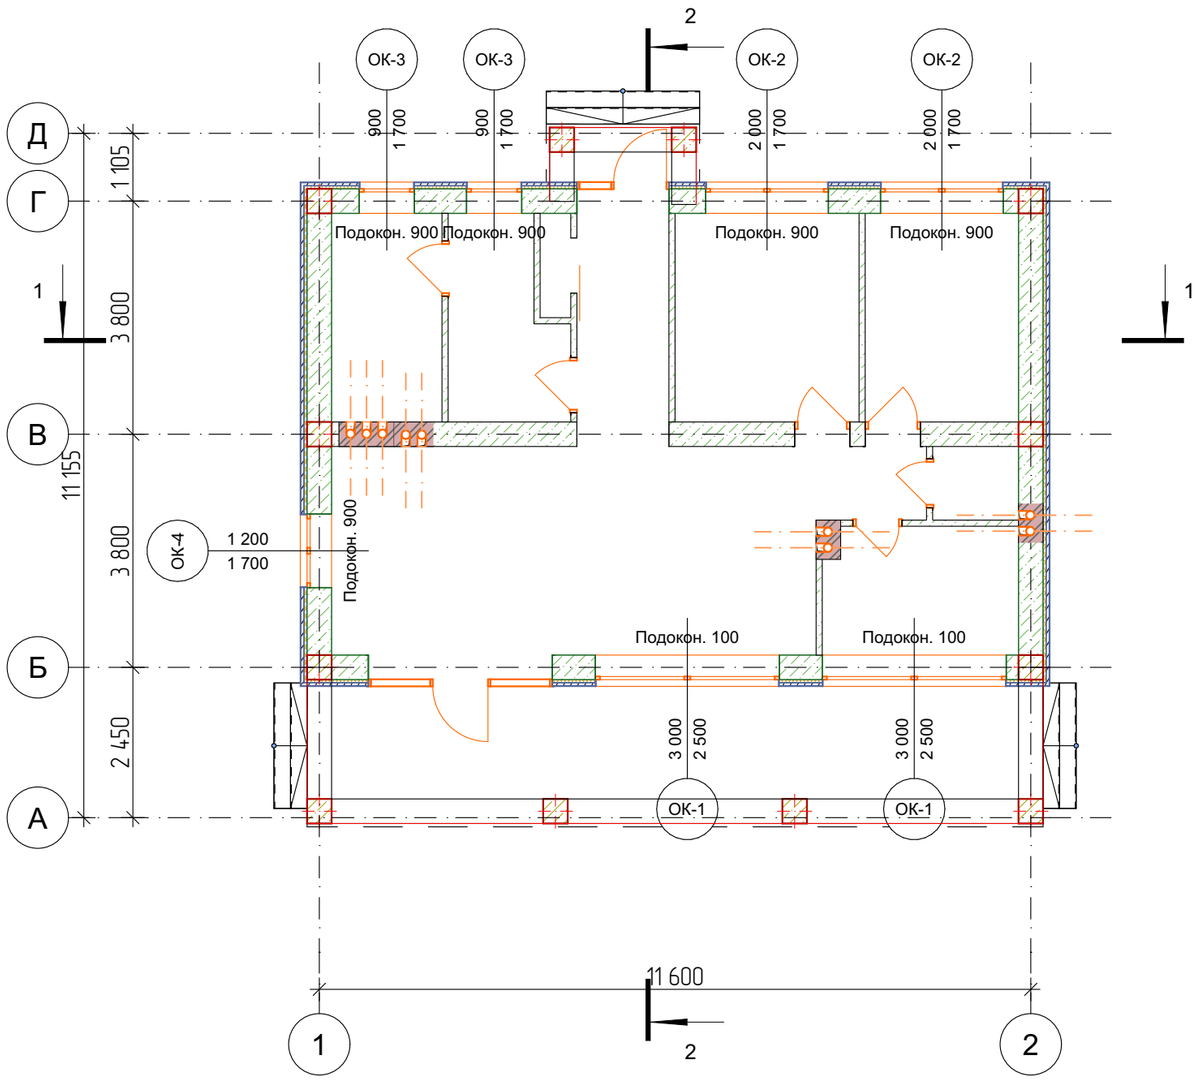


						#ID Проекта	
						кадастровый номер Россия	
Изм.	Кол.уч.	Лист	№Док.	Подп.	Дата		
Разраб.						Индивидуальный жилой дом	Стадия: #Стадия Проекта; Лист: 17; Листов:
						Маркировка оконных проемов первого этажа	

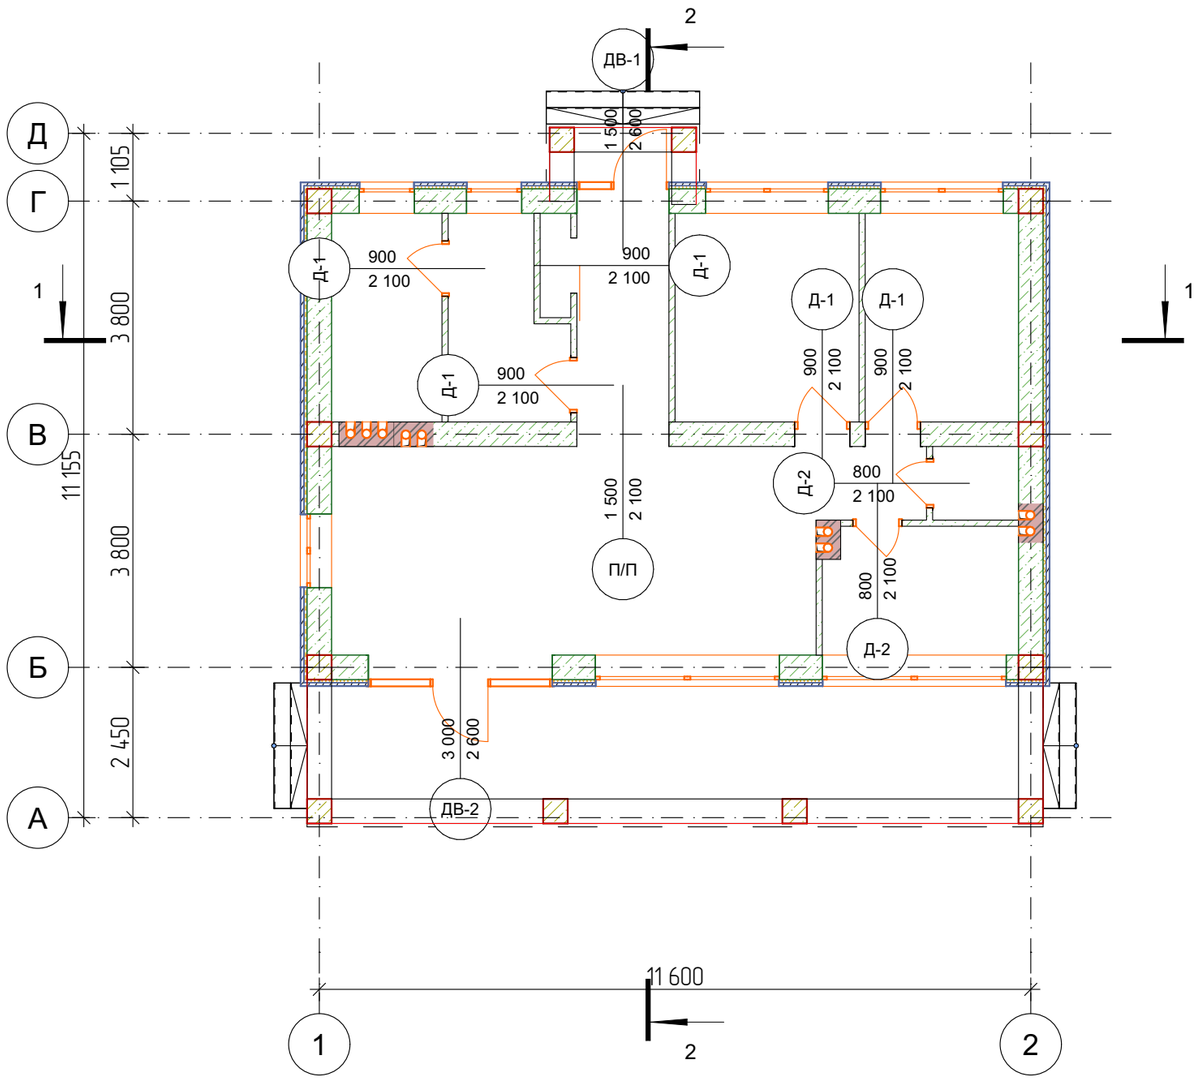

						#ID Проекта	
						кадастровый номер Россия	
Изм.	Кол.уч.	Лист	№Док.	Подп.	Дата		
Разраб.						Индивидуальный жилой дом	Стадия: #Стадия Проекта; Лист: 18; Листов:
						Маркировка дверных проемов первого этажа	

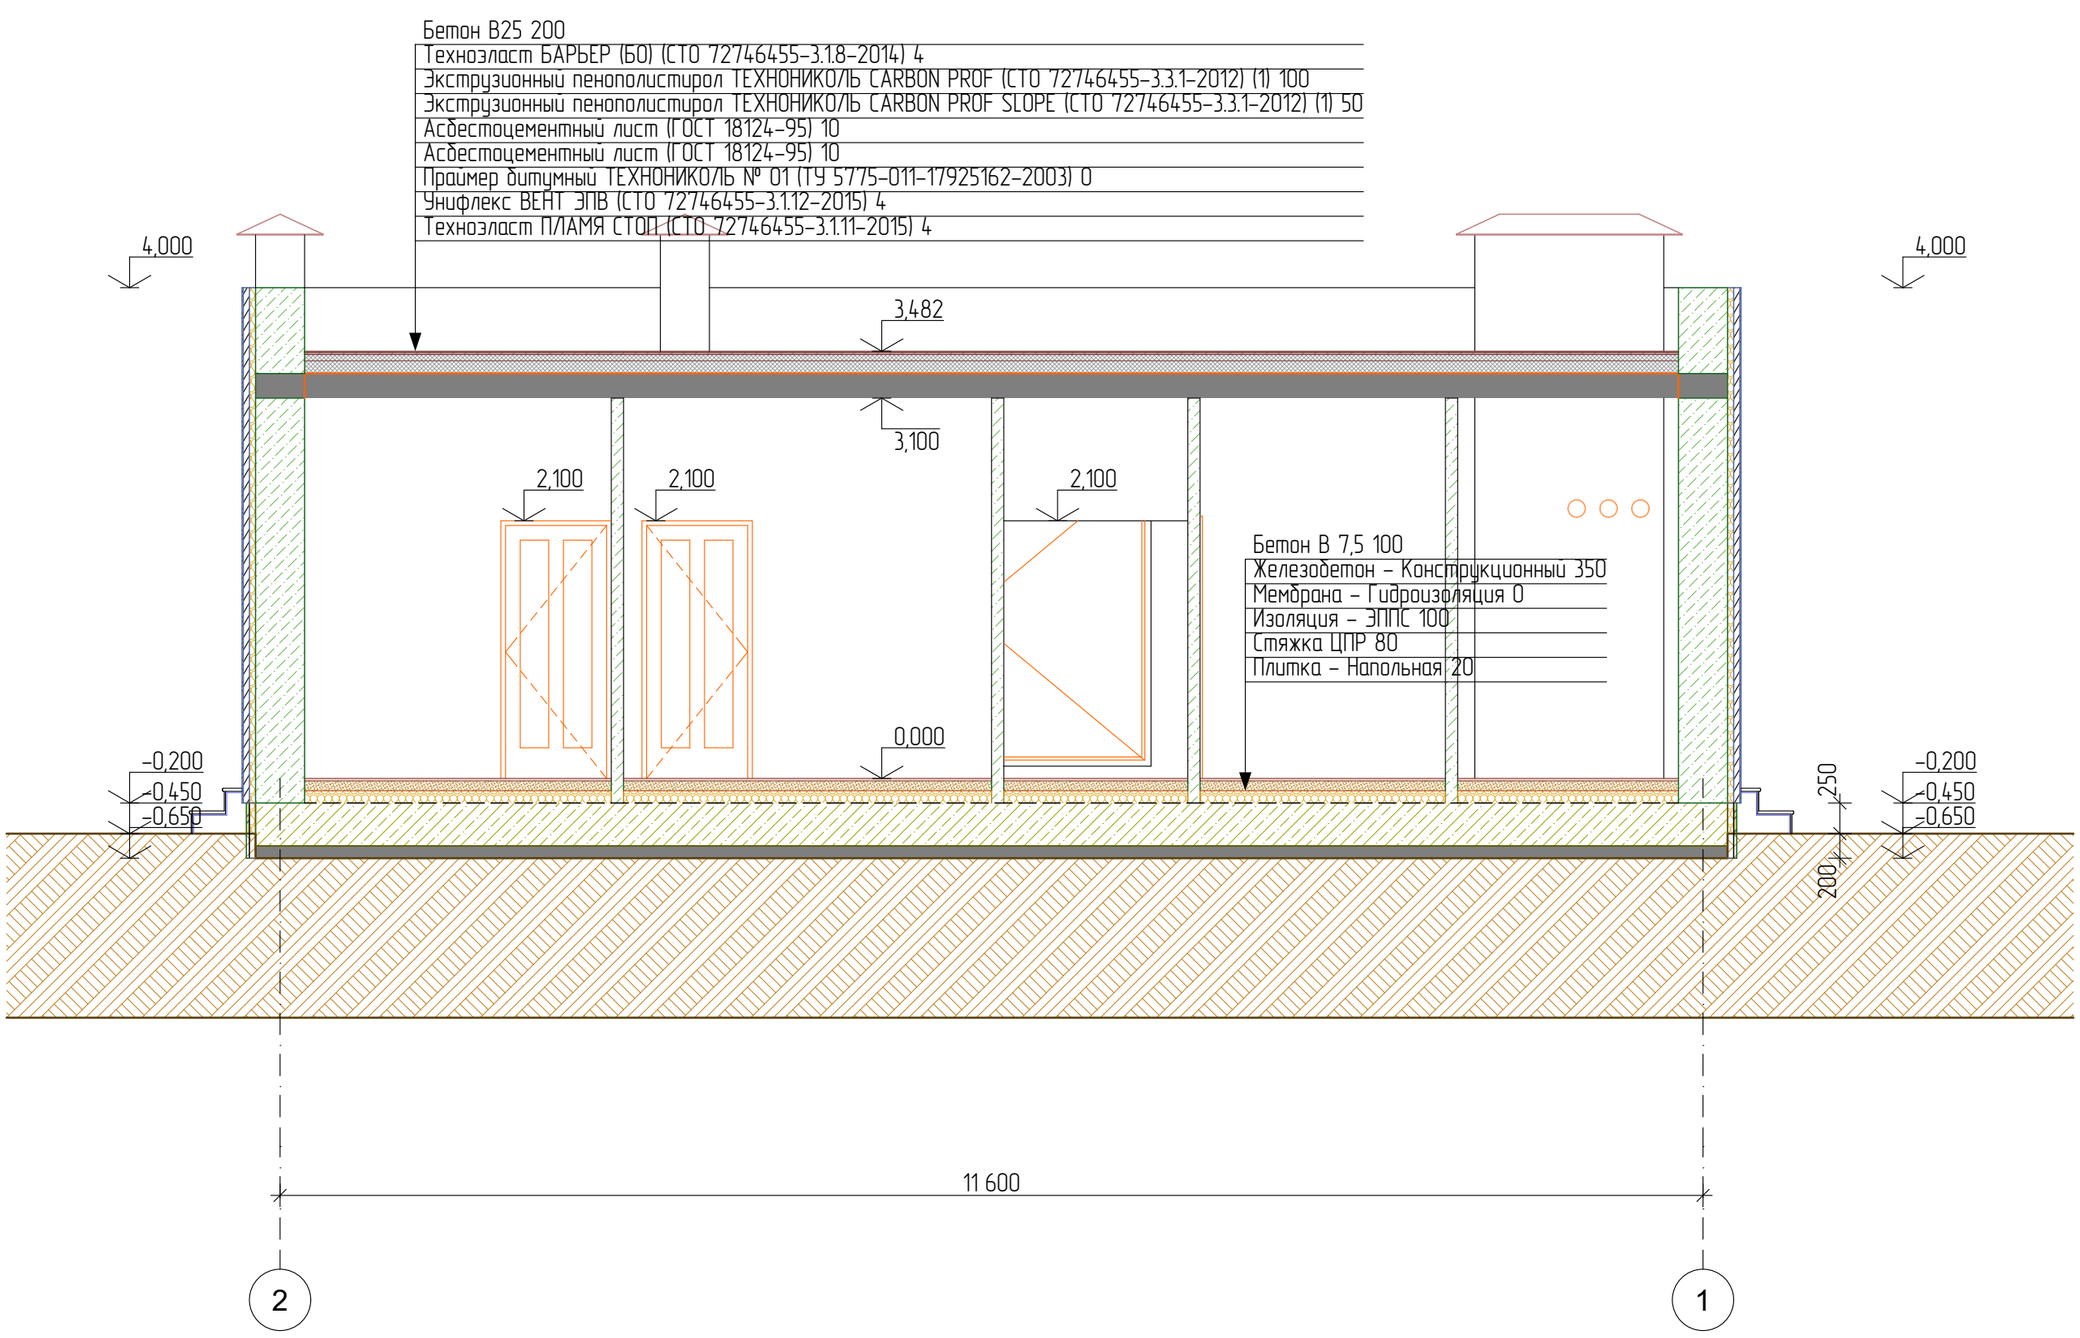


						#ID Проекта	
						кадастровый номер Россия	
Изм.	Кол.уч.	Лист	№Док.	Подп.	Дата		
Разраб.						Индивидуальный жилой дом	Стадия: #Стадия Проекта; Лист: 19; Листов:
						Разрез 1 - 1	

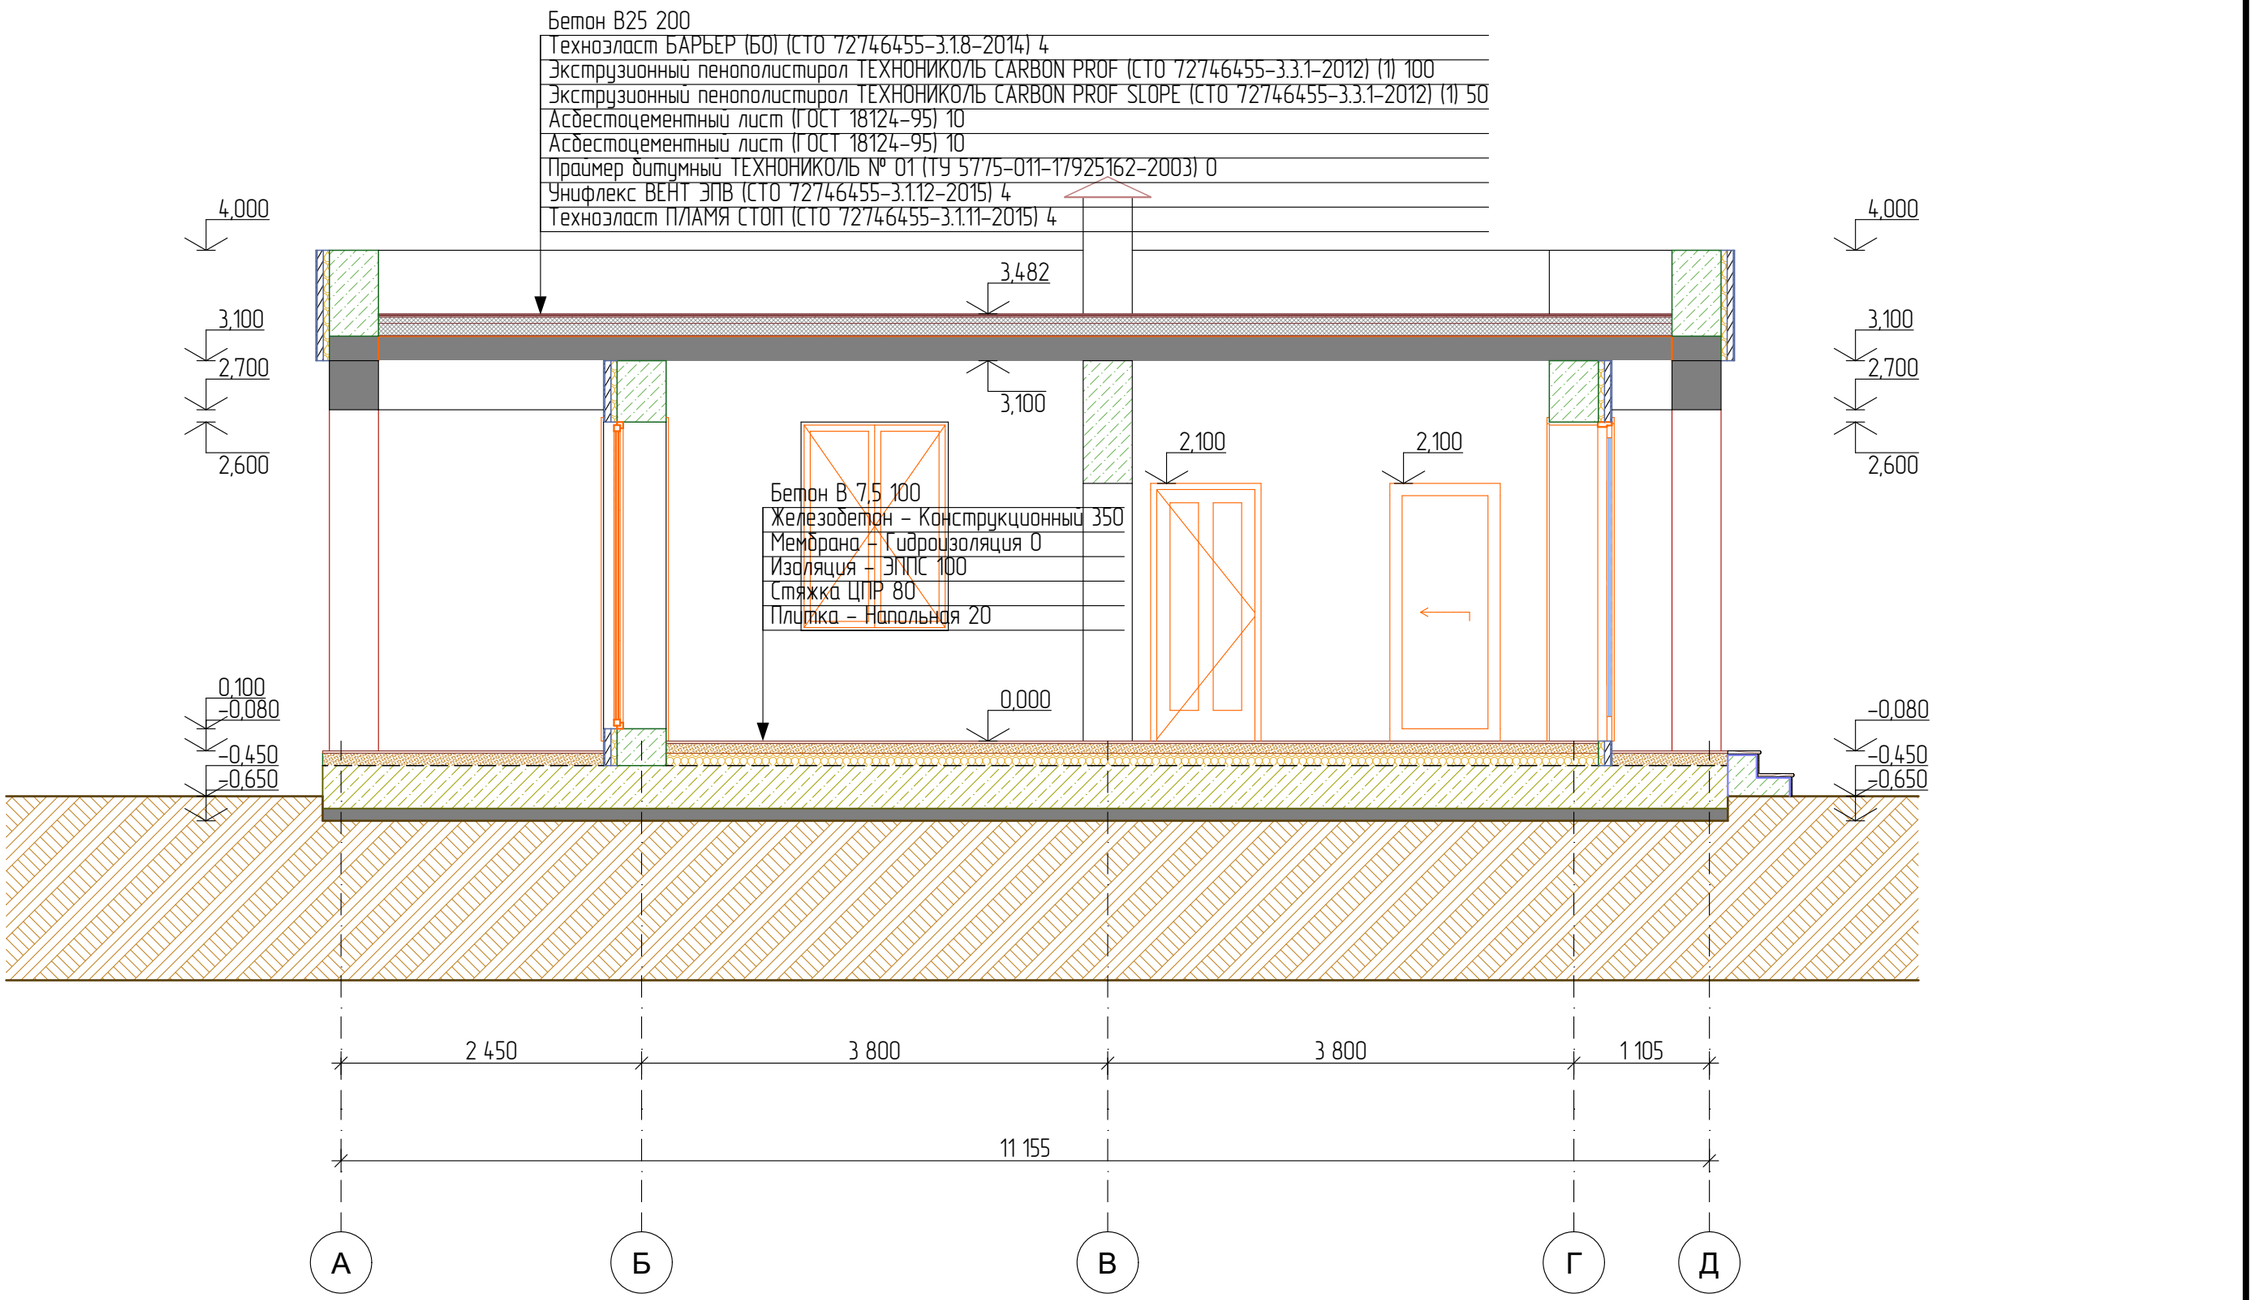


						#ID Проекта	
						кадастровый номер Россия	
Изм.	Кол.уч.	Лист	№Док.	Подп.	Дата		
Разраб.						Индивидуальный жилой дом	Стадия: #Стадия Проекта; Лист: 20; Листов:
						Разрез 2 - 2	

Бетон В25 200
Техноэласт БАРЬЕР (БО) (СТО 72746455-3.1.8-2014) 4
Экструзионный пенополистирол ТЕХНОНИКОЛЬ CARBON PROF (СТО 72746455-3.3.1-2012) (1) 100
Экструзионный пенополистирол ТЕХНОНИКОЛЬ CARBON PROF SLOPE (СТО 72746455-3.3.1-2012) (1) 50
Асбестоцементный лист (ГОСТ 18124-95) 10
Асбестоцементный лист (ГОСТ 18124-95) 10
Праймер битумный ТЕХНОНИКОЛЬ № 01 (ТУ 5775-011-17925162-2003) 0
Унифлекс ВЕНТ ЭПВ (СТО 72746455-3.1.12-2015) 4
Техноэласт ПЛАМЯ СТОП (СТО 72746455-3.1.11-2015) 4

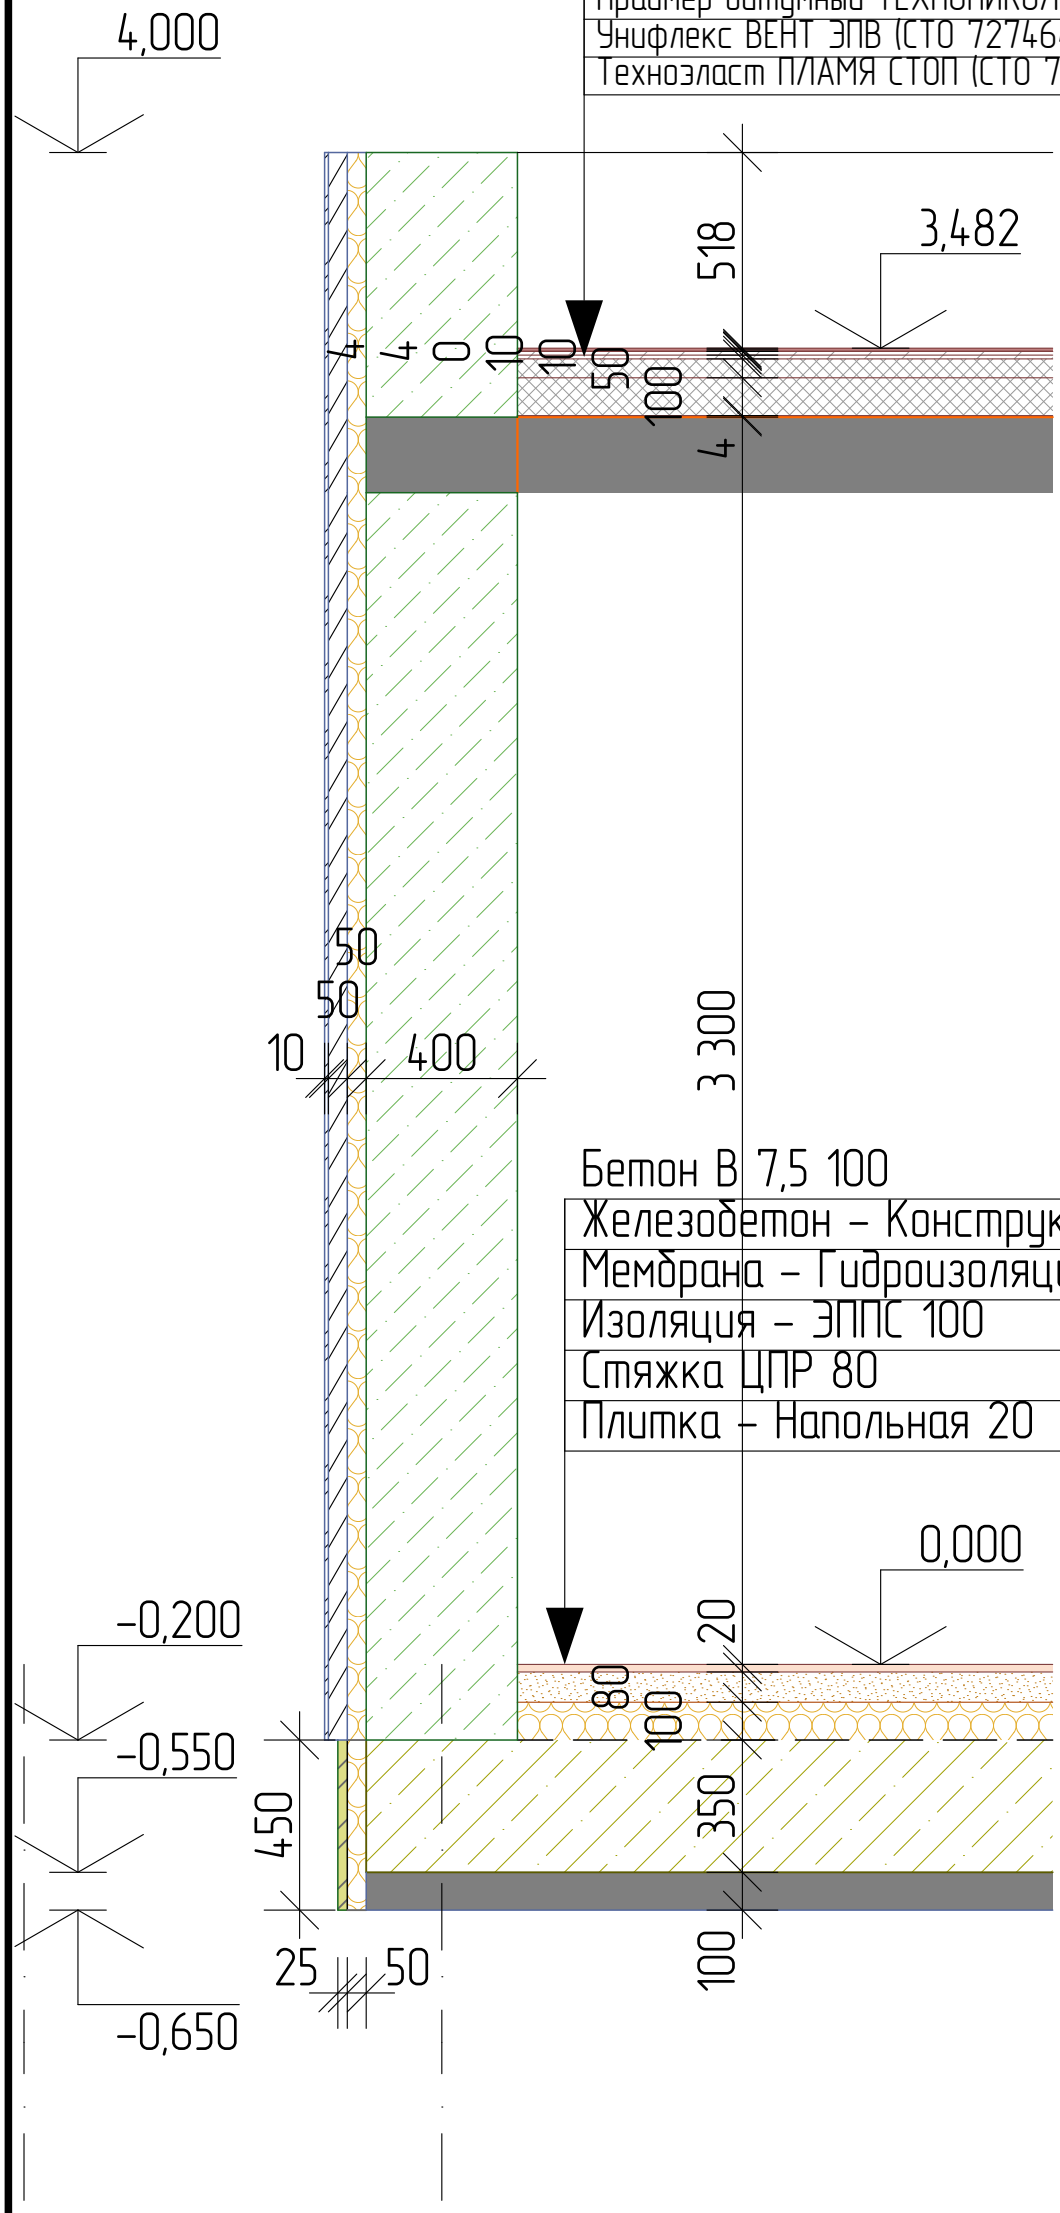


Изм.	Кол.уч.	Лист	№Док.	Подп.	Дата	#ID Проекта			
						кадастровый номер Россия			
Разраб.						Индивидуальный жилой дом	Стадия	Лист	Листов
							#Стадия Проекта	21	
						Разрез по стене			

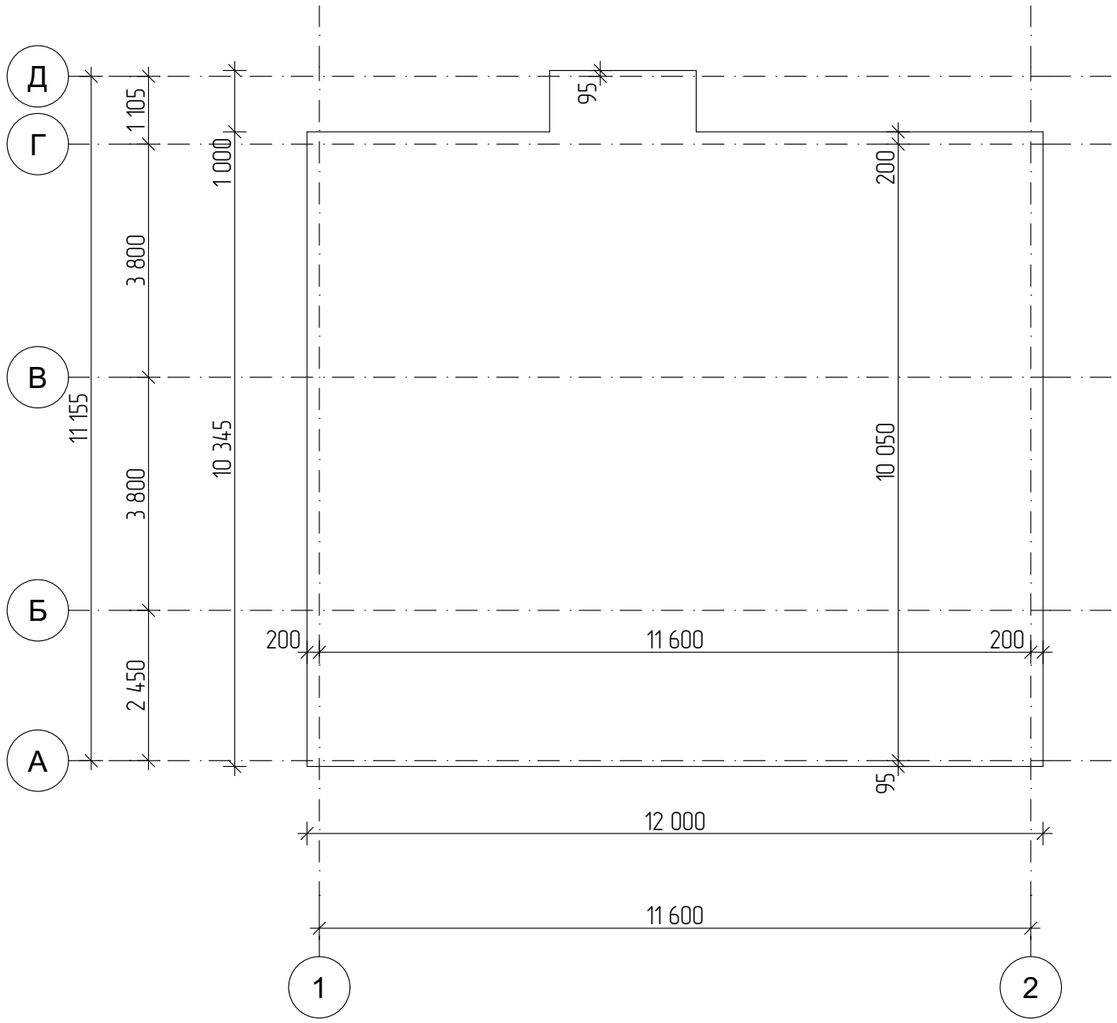


ВЕДОМОСТЬ ПЕРЕКРЫТИЙ

Наименование	Объем, м3
Монолитная плита	25,08


Изм.	Кол.уч.	Лист	№Док.	Подп.	Дата	#ID Проекта			
						кадастровый номер Россия			
Разраб.						Индивидуальный жилой дом	Стадия	Лист	Листов
							#Стадия Проекта	22	
						План перекрытия +3,100			

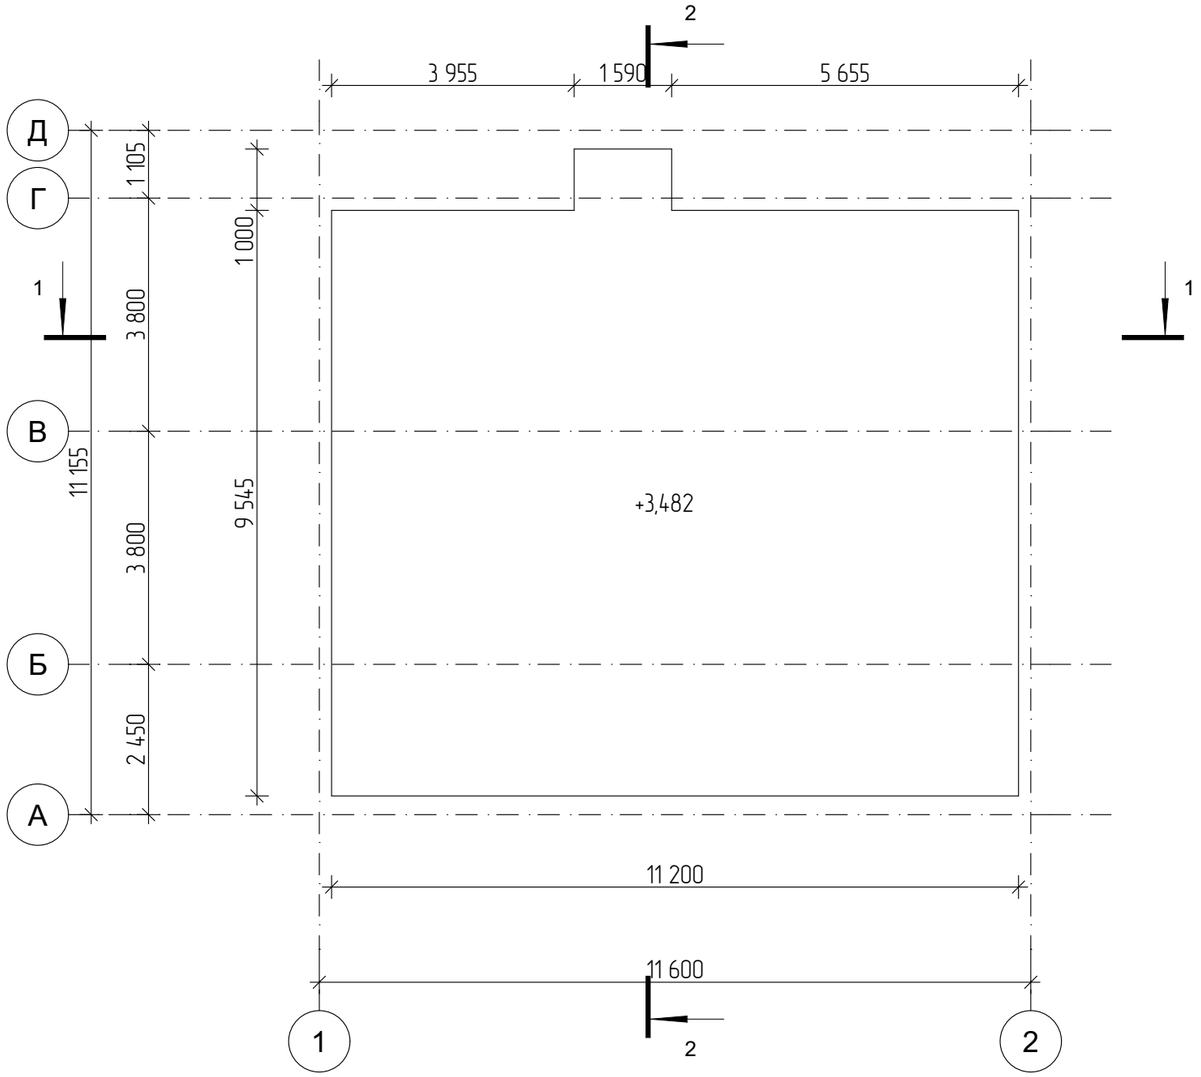

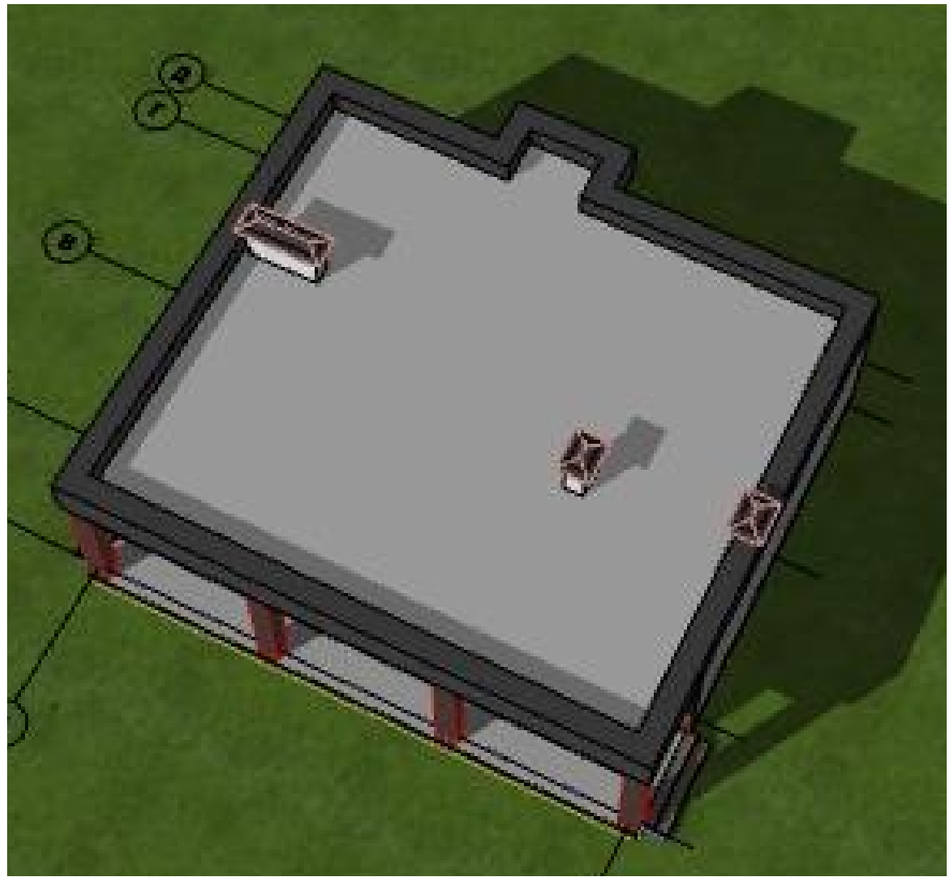


ИКК-03 Кровля	
Наименование	Площадь Ве...
Кровля	108,49

						#ID Проекта		
						кадастровый номер Россия		
Изм.	Кол.уч.	Лист	№Док.	Подп.	Дата			
Разраб.						Индивидуальный жилой дом	Стадия	Лист	Листов
							#Стадия Проекта	23	
						План кровли			

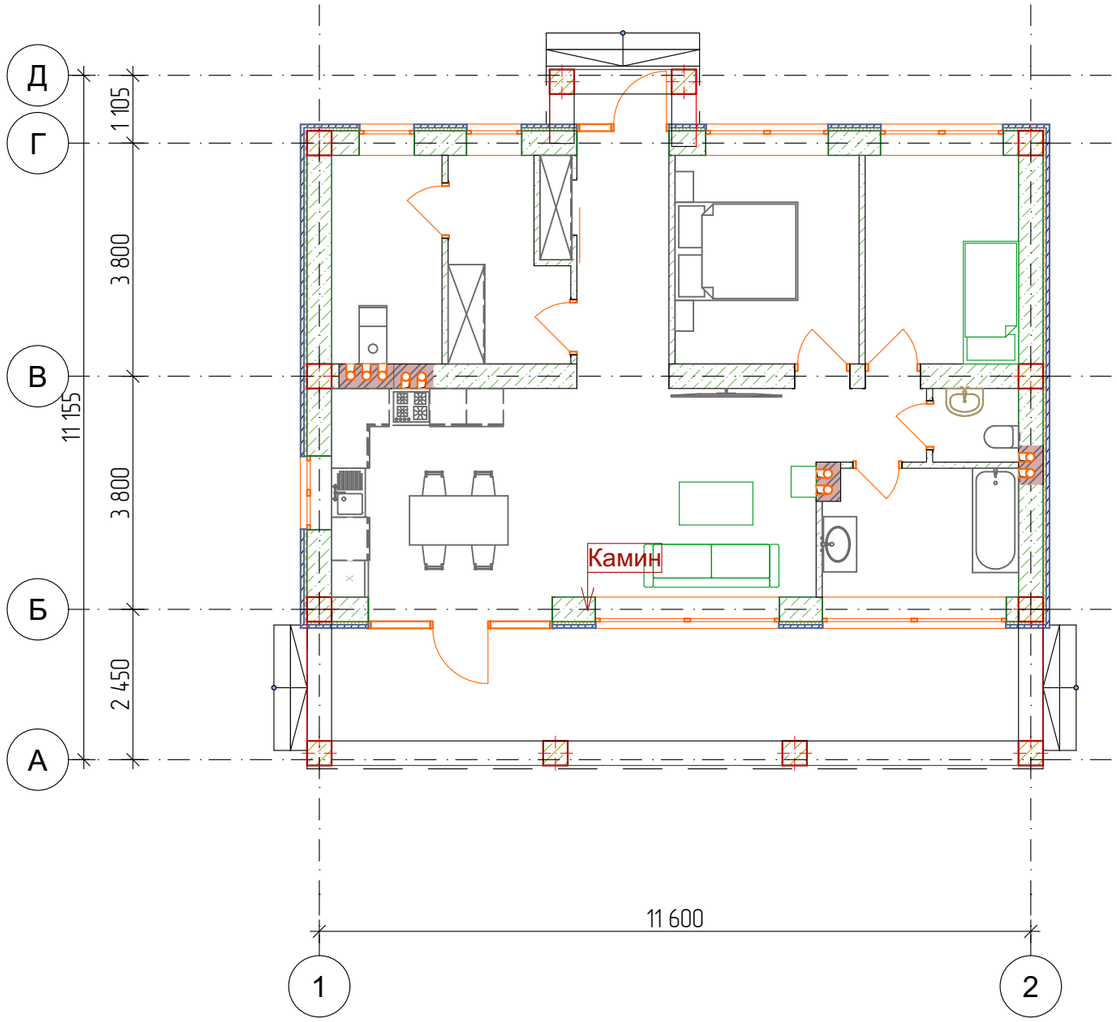


						#ID Проекта	
						кадастровый номер Россия	
Изм.	Кол.уч.	Лист	№Док.	Подп.	Дата		
Разраб.						Индивидуальный жилой дом	Стадия: #Стадия Проекта; Лист: 24; Листов:
						План расстановки мебели 1 этаж	

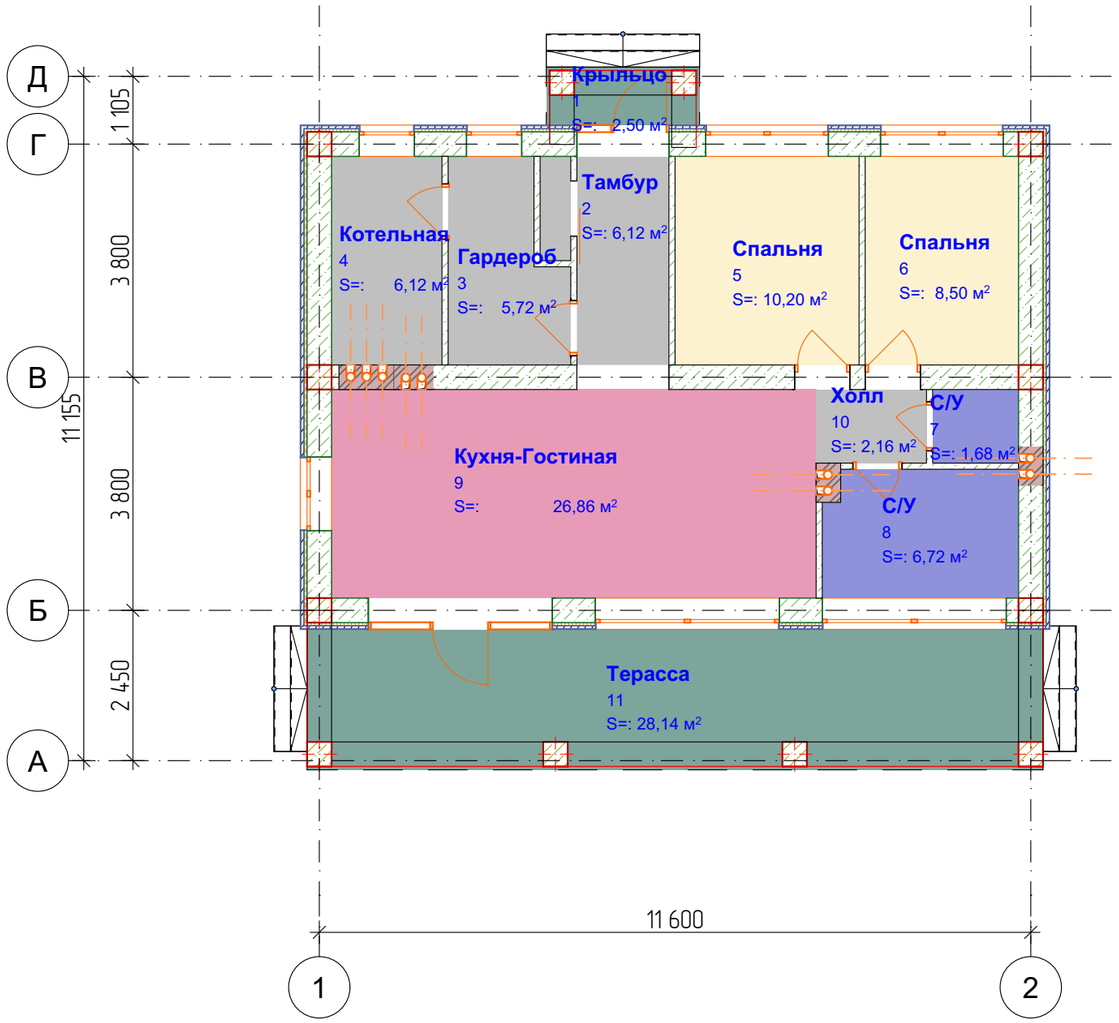


№	Наименование	Площадь
1	Крыльцо	2,50
2	Тамбур	6,63
3	Гардероб	5,72
4	Котельная	6,12
5	Спальня	10,20
6	Спальня	8,50
7	С/У	1,68
8	С/У	6,72
9	Кухня-Гостиная	28,02
10	Холл	2,16
11	Терасса	28,14
		106,39 м²

Изм.	Кол.уч.	Лист	№Док.	Подп.	Дата	#ID Проекта		
						кадастровый номер Россия		
Разраб.						Индивидуальный жилой дом	Стадия: #Стадия Проекта	Лист: 25 / Листов:
						Экспликация помещений 1- го этажа		

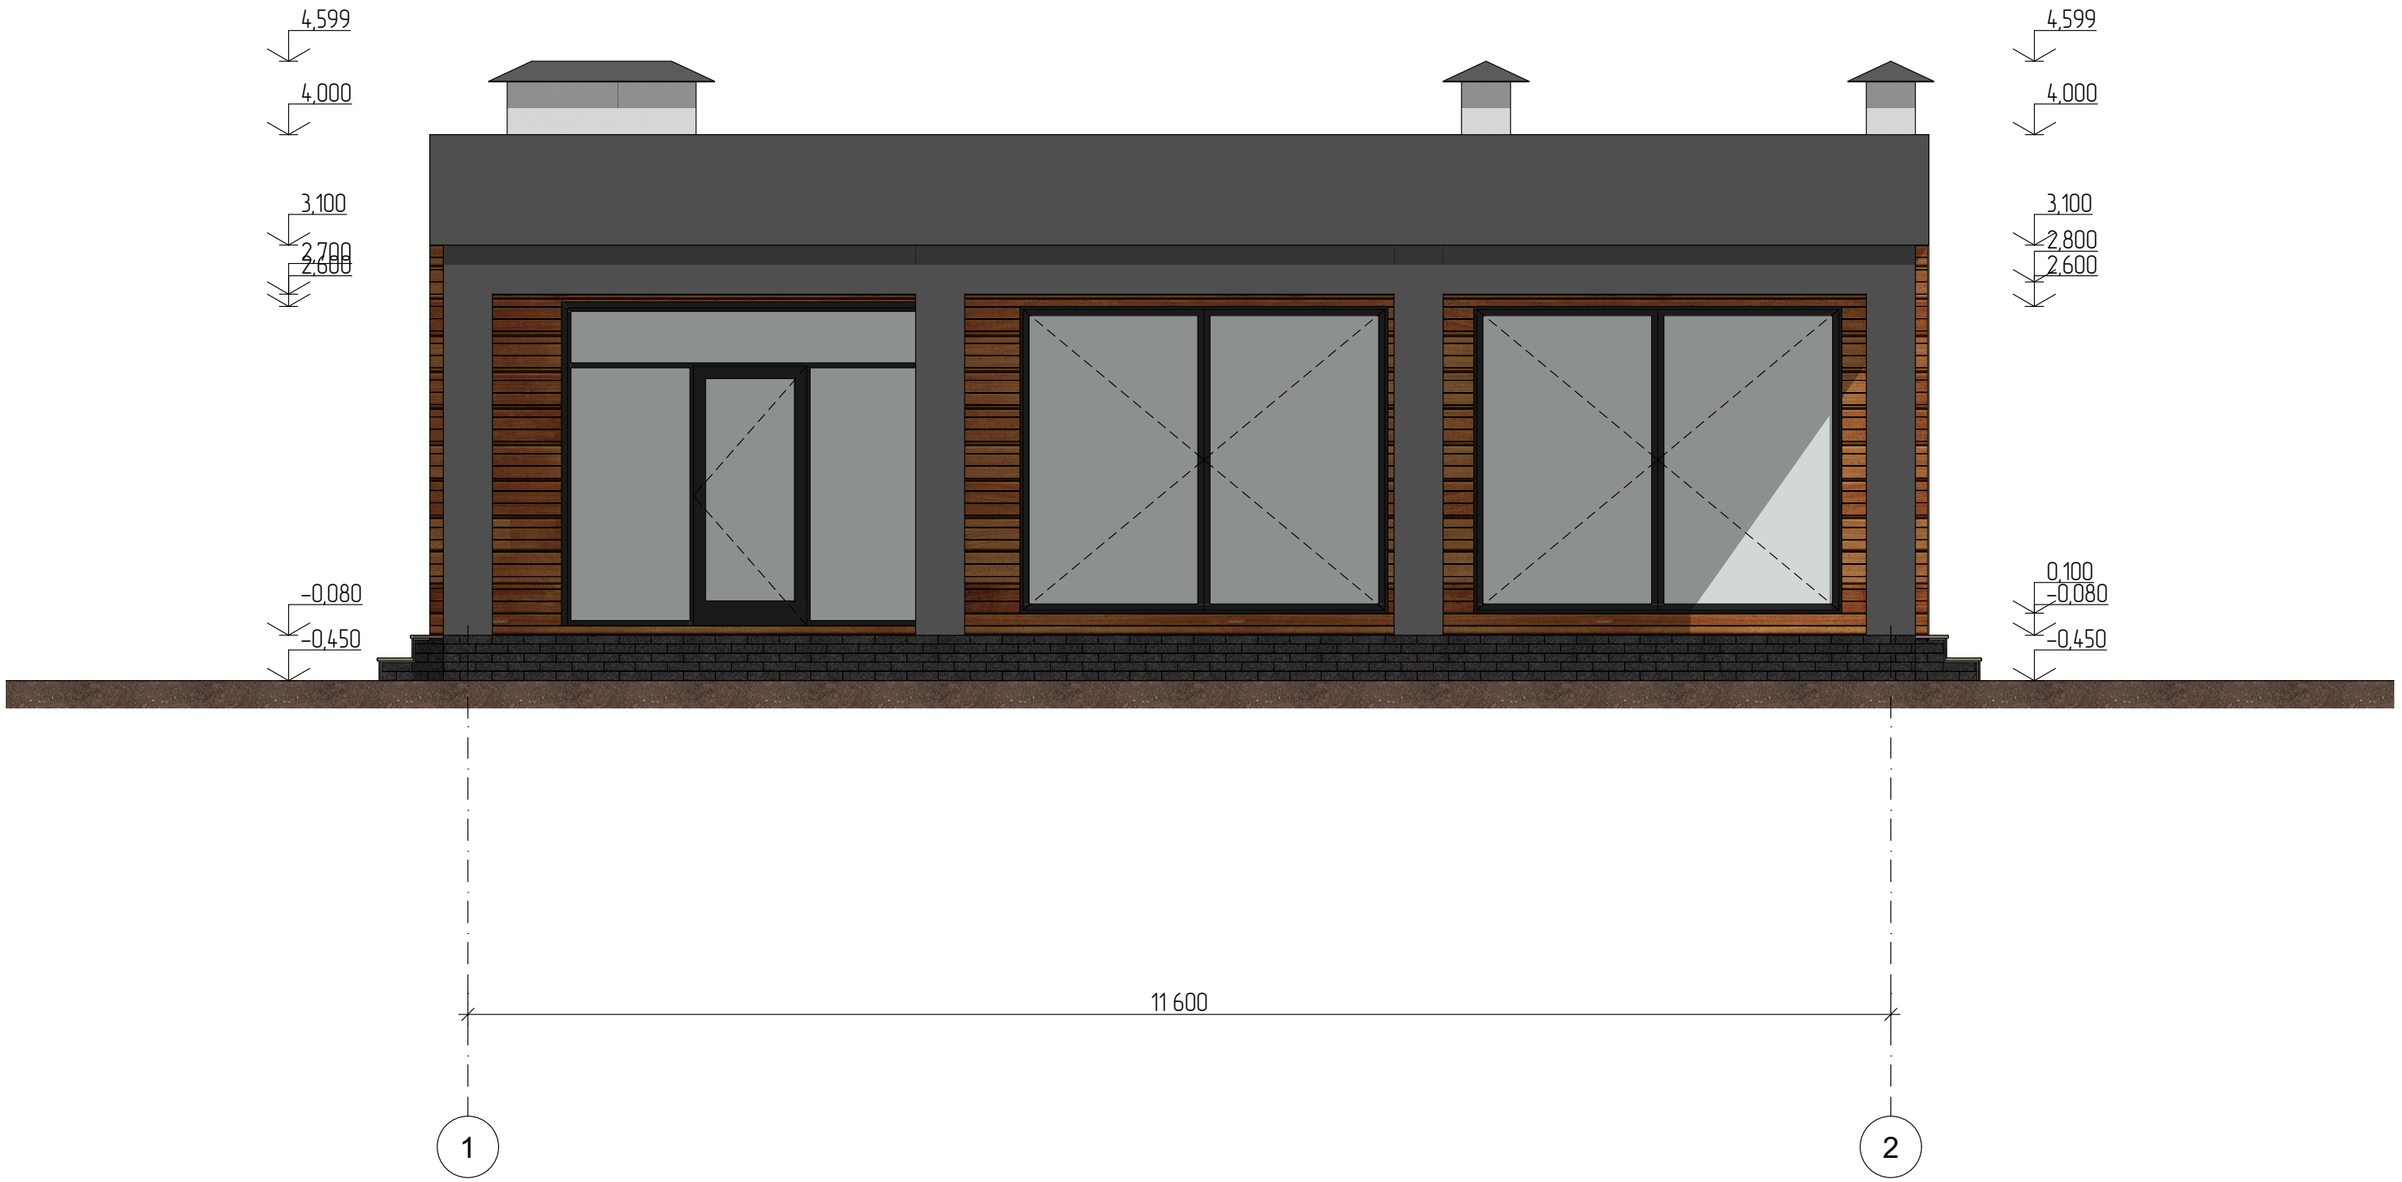


						#ID Проекта	
						кадастровый номер Россия	
Изм.	Кол.уч.	Лист	№Док.	Подп.	Дата		
Разраб.						Индивидуальный жилой дом	Стадия: #Стадия Проекта; Лист: 26; Листов:
						Фасад в осях 1-5	

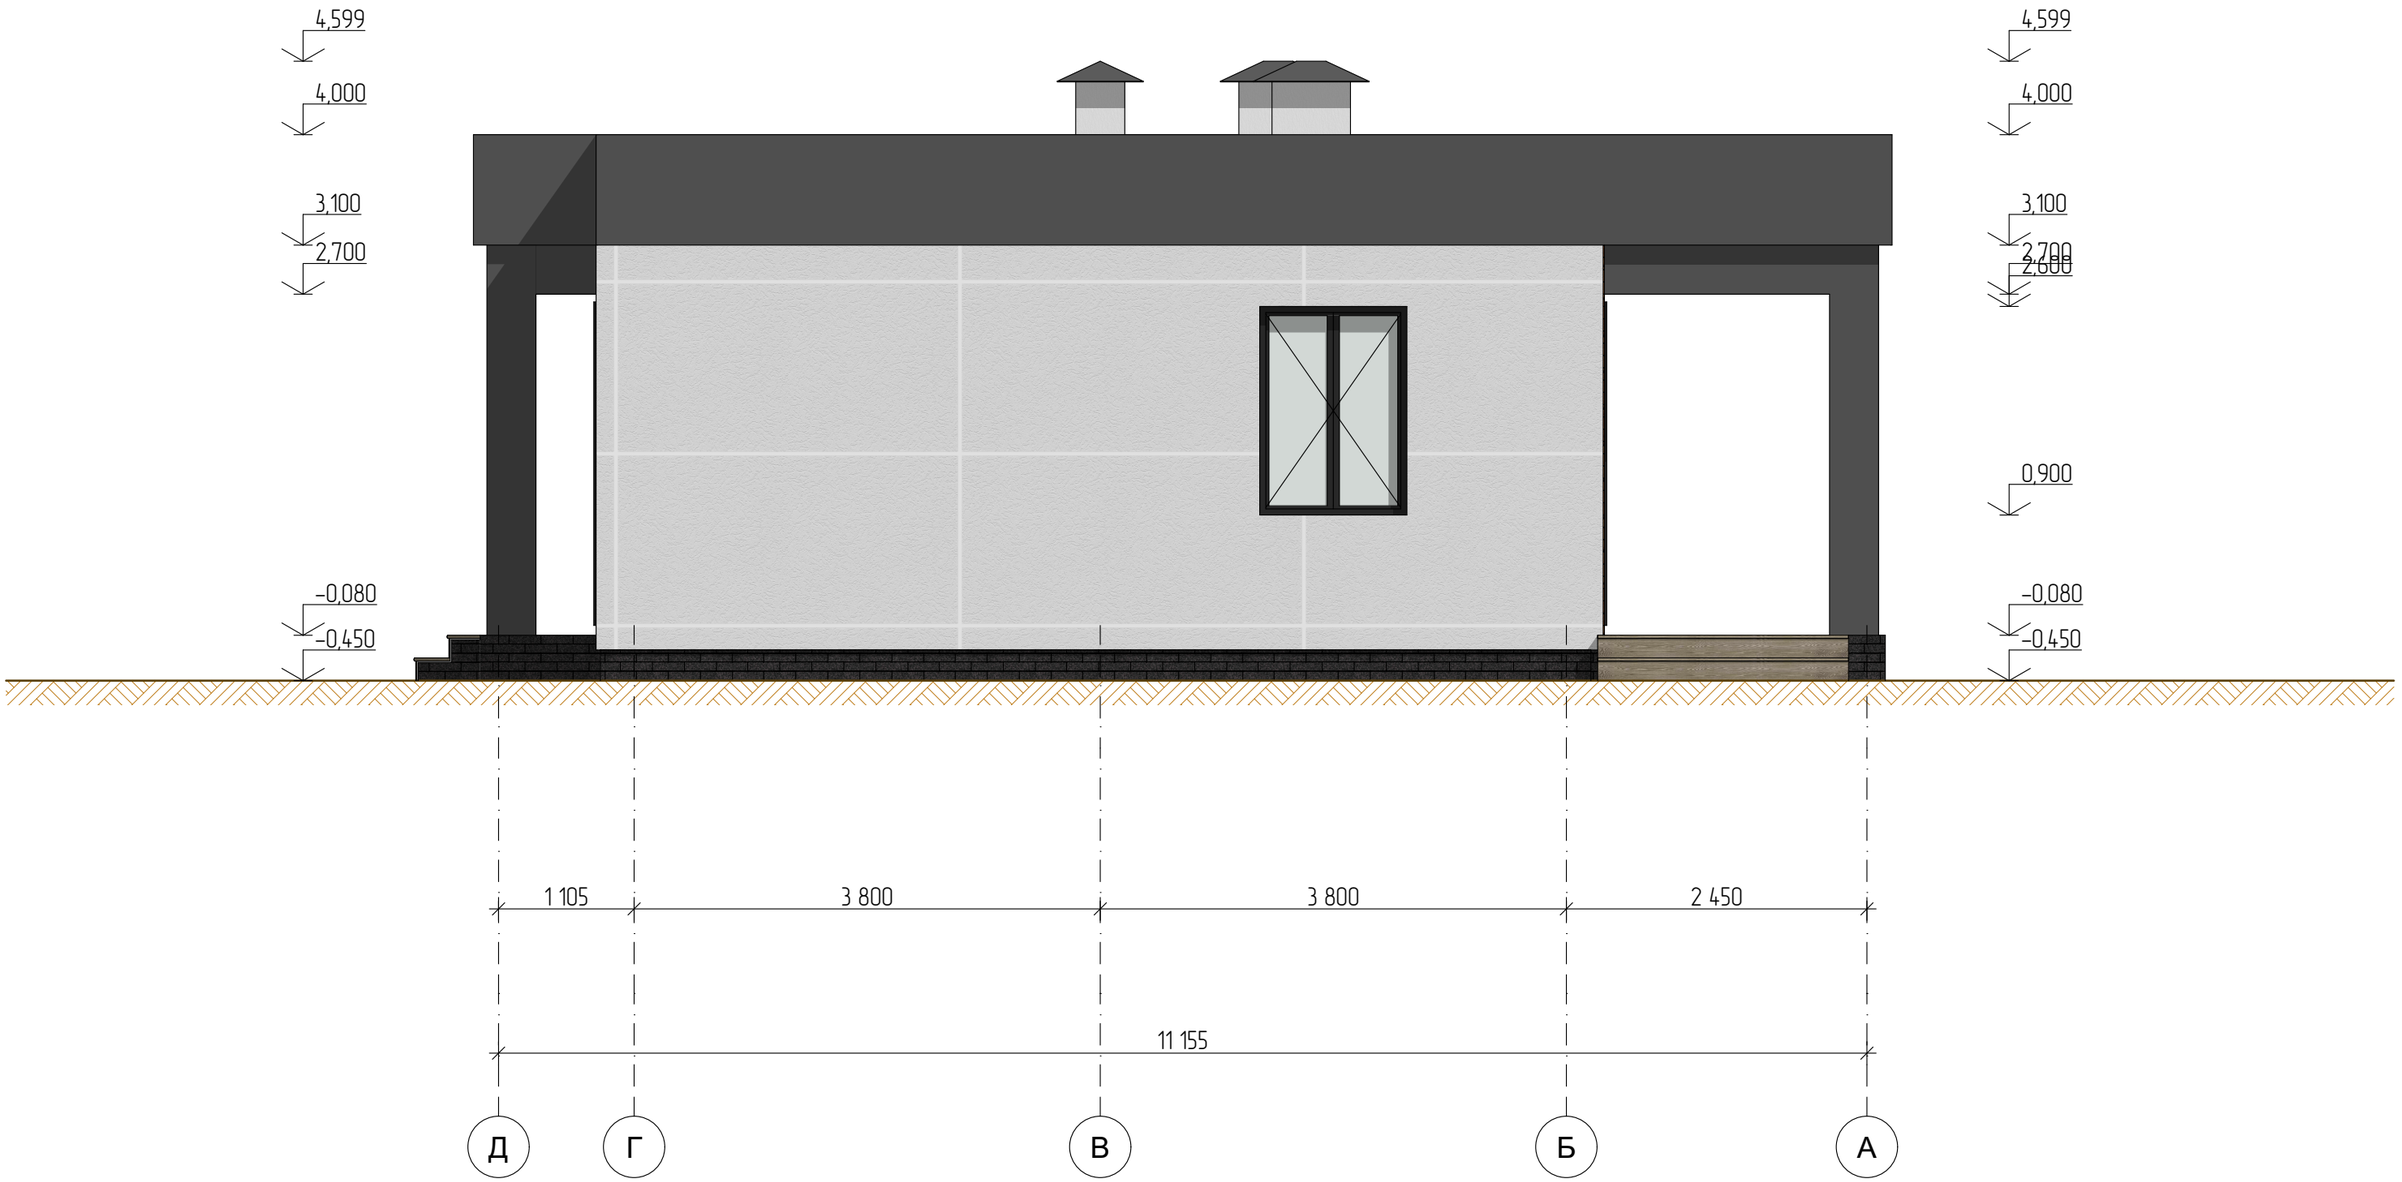

						#ID Проекта
						кадастровый номер Россия
Изм.	Кол.уч.	Лист	№Док.	Подп.	Дата	
Разраб.						Индивидуальный жилой дом
						Фасад в осях Д-А

Стадия	Лист	Листов
#Стадия Проекта	27	

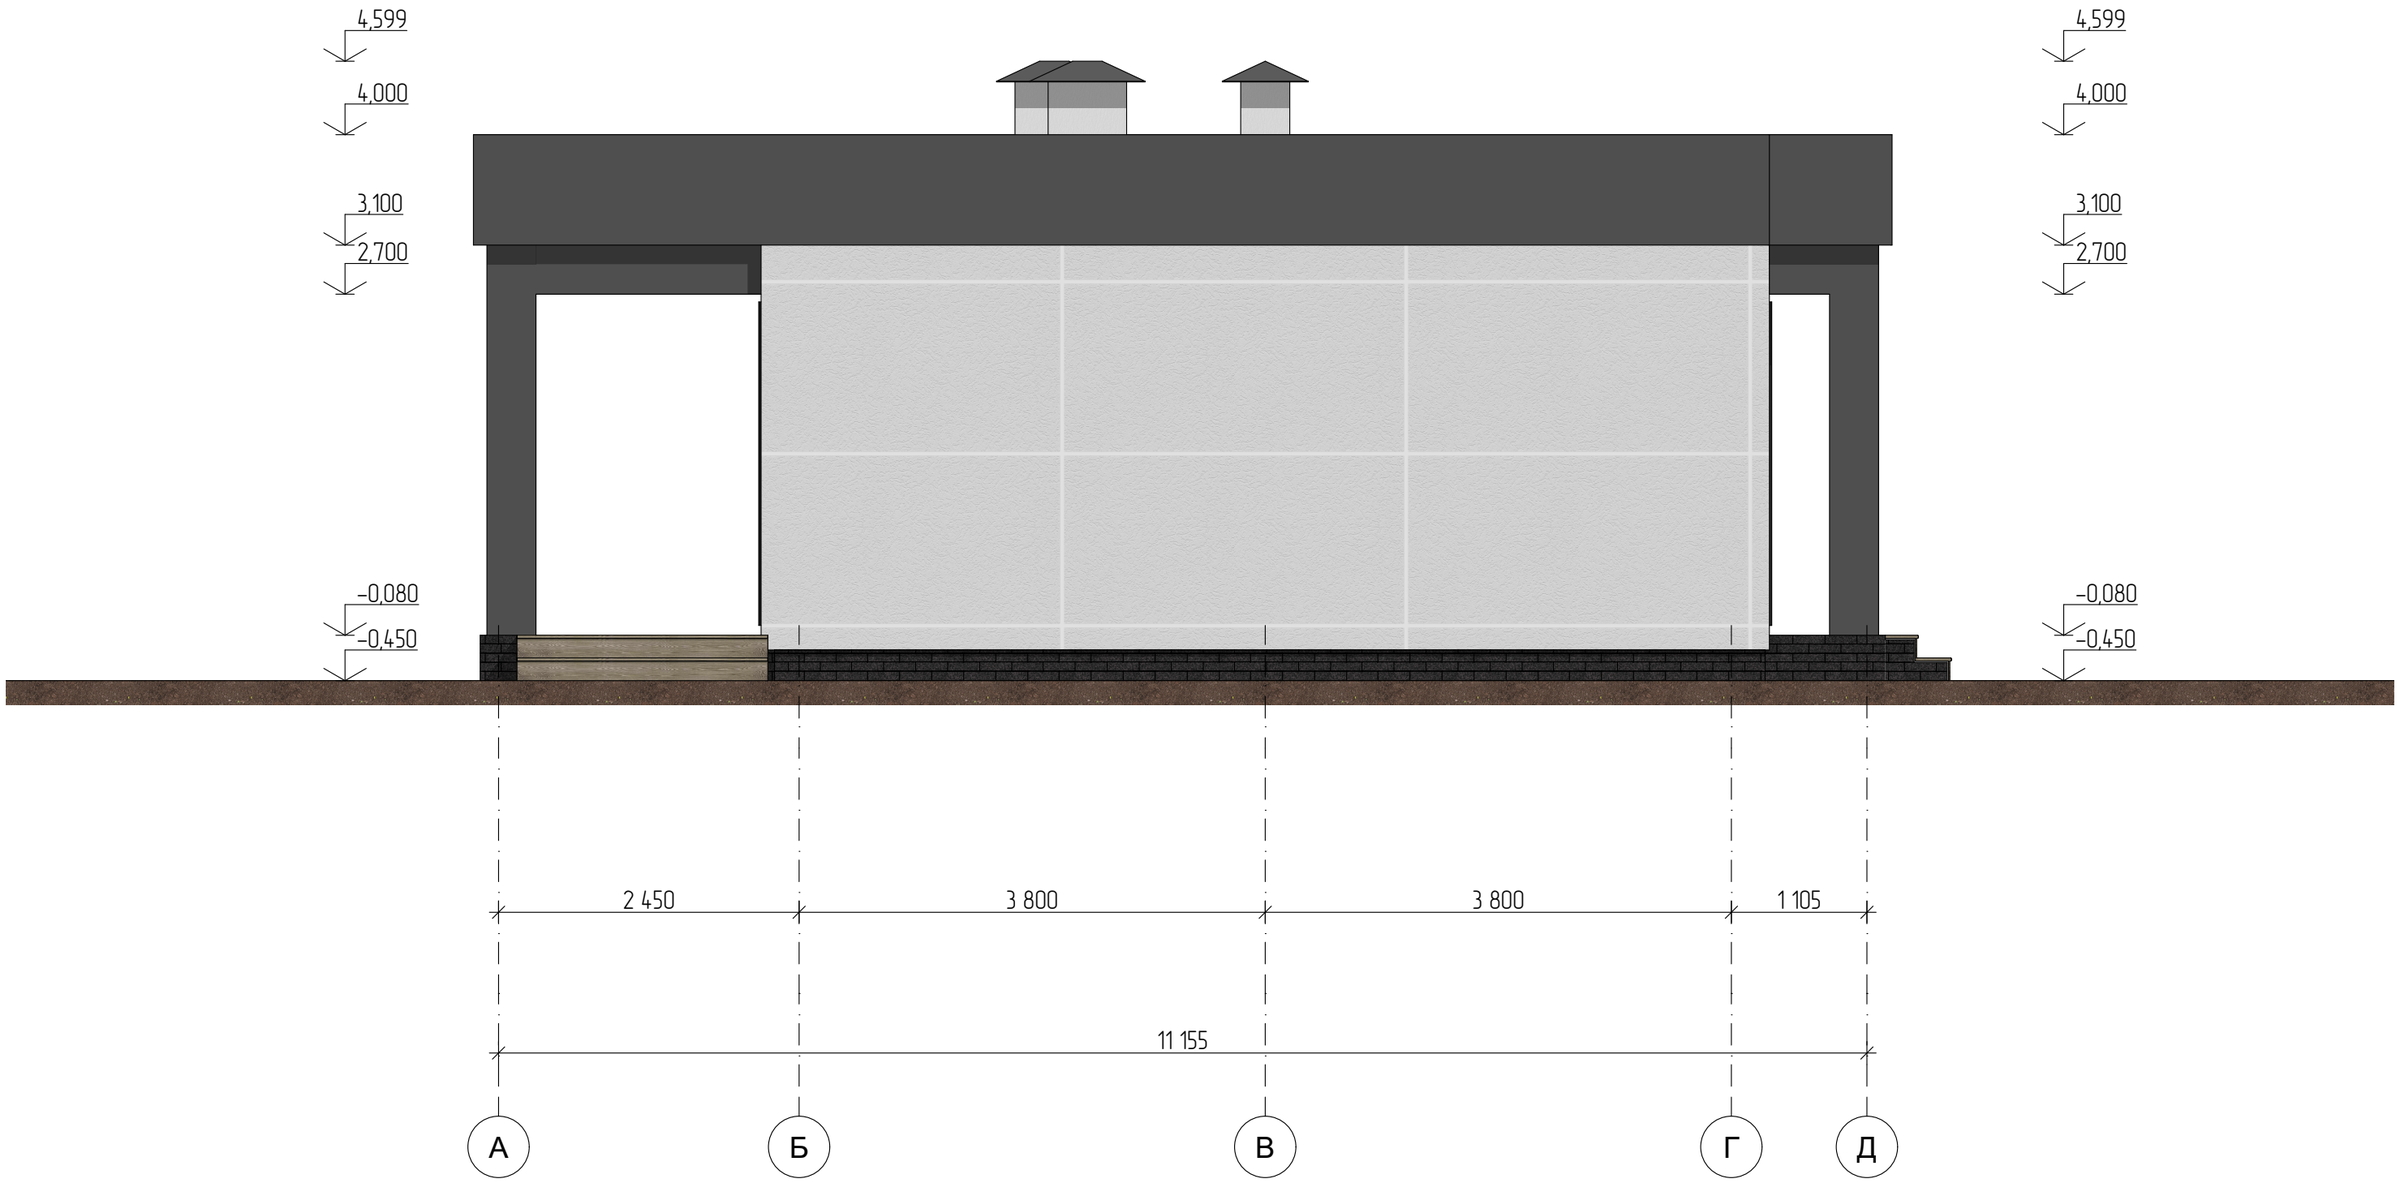

						#ID Проекта
						кадастровый номер Россия
Изм.	Кол.уч.	Лист	№Док.	Подп.	Дата	
Разраб.						Индивидуальный жилой дом
						Фасад в осях А-Д

Стадия	Лист	Листов
#Стадия Проекта	28	



						#ID Проекта	
						кадастровый номер Россия	
Изм.	Кол.уч.	Лист	№Док.	Подп.	Дата		
Разраб.						Индивидуальный жилой дом	Стадия: #Стадия Проекта; Лист: 29; Листов:
						Фасад в осях 2-1	