ПРОЕКТНАЯ ДОКУМЕНТАЦИЯ

Индивидуальный жилой дом

кадастровый номер 63:03:0211031:617, Самарская область, г. Кинель, ул. Уральская, 72а Россия



Разработал Салыкова В.

2024

Ведомость листов

Наименование	Лист
Обложка	
Общие данные	02
Сводная ведомость материалов	03
Схема организации участка	04
3D Виды	05
План фундамента	06
План 1 этажа	07
План 2 этаж	08
Маркировочный план 1 этаж	09
Маркировочный план 2 этаж	10
Каталог дверных проемов	11
Каталог оконных проемов	12
Разрез 1 - 1	13
Разрез 2 - 2	14
Разрез по стене	15
План перекрытия +2,970	16
План армопояса	17
План кровли на отм. +2,300	18
План кровли на отм. +4,975	19
Схема расположения стропил на отм. +2,300	20
Схема расположения стропил на отм. +4,975	21
3Д вид стропильной системы	22
План расстановки мебели 1 этаж	23
План расстановки мебели 2 этаж	24
Экспликация помещений 1- го этажа	25
Экспликация помещений 2- го этажа	26
3Д разрезы	27
Фасад в осях 1-5	28
Фасад в осях Г-А	29
Фасад в осях А-Г	30
Фасад в осях 5-1	31

Изм.	Кол.уч.	Лист	№Док.	Подп.	Дата

кадастровый номер 63:03:0211031:617, Самарская область, г. Кинель, ул. Уральская, 72а Россия

Разраб.	Салыкова В.	Индивидуальный жилой дом	Стадия: ЭП	Лист: 02 / Листов:
		Общие данные		

ВЕДОМОСТЬ ПЕРЕКРЫТИЯ	
Наименование	Объем ,м3
Монолитное перекрытие	11,79

ВЕДОМОСТЬ НА МОНОЛИТНЫЙ ПОЯС 2-ГО ЭТАЖА	
Наименование	Объем, м3
	7,16
Армопояс	7,16

ВЕДОМОСТЬ КРОВЕЛЬНОГО МАТЕРИАЛА	
Наименование	Площадь, м2
Кровля дома	89,69

ИКК-03 Кровля	
Наименование	Площадь Ве...
Кровля дома	129,76

ИКК-03 Стропильная система	
Наименование	Объем, м3
	0,05
Коньковый брус 200х100	0,05
Мауэрлат 100х200	0,57
Стропильная нога 200х50	0,05
Стропильная нога 200х100	5,14

ВЕДОМОСТЬ СТРОПИЛЬНОЙ СИСИТЕМЫ	
Наименование	Объем, м3
	0,06
Мауэрлат 100х200	0,26
Стропильная нога 200х100	4,06


ВЕДОМОСТЬ НА УТЕПЛИТЕЛЬ ДЛЯ СТЕН, ПОЛА ПЕРВОГО ЭТАЖА, РОСТВЕРКА			
Наименование	**Компоненты**		
	Толщина [м]	**Объем [м3]**	**Площадь [м2]**
Изоляция - Минеральная Жесткая			
	200	43,23	218,17
Изоляция - ЭППС			
	50	6,02	120,94
	150	19,06	127,03

Отделочные материалы		
Наименование	**Компоненты**	
	Толщина [м]	**Площадь [м2]**
Штукатурка - фасадная		
	10	244,93


ВЕДОМОСТЬ БЕТОНА	
Наименование	Объем, м3
Лента Фундамента	69,81

ВЕДОМОСТЬ БЛОКА ДЛЯ СТЕН	
ID Элемента	Объем, м3
Несущие 300мм	22,52
Несущие 400мм	68,48
Перегородки 100мм	10,22

Изм.	Кол.уч.	Лист	№Док.	Подп.	Дата	кадастровый номер 63:03:0211031:617, Самарская область, г. Кинель, ул. Уральская, 72а Россия			
Разраб.		Салыкова Е.				Индивидуальный жилой дом	Стадия	Лист	Листов
							ЭП	03	
						Сводная ведомость материалов			

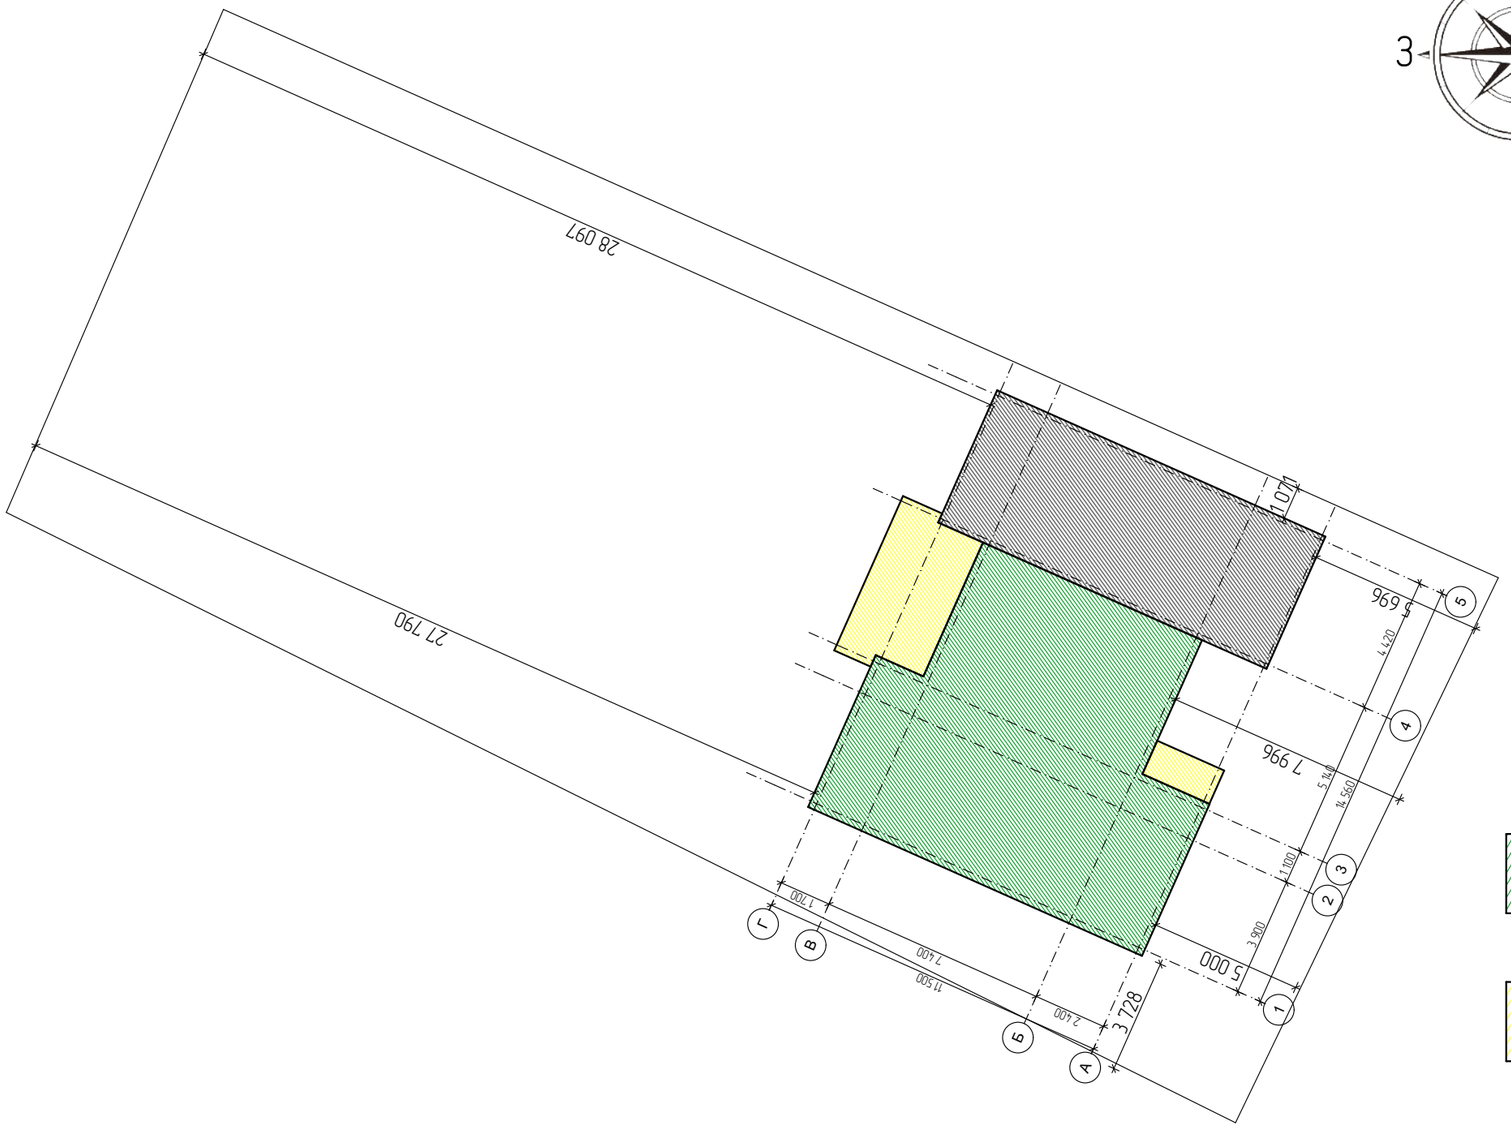



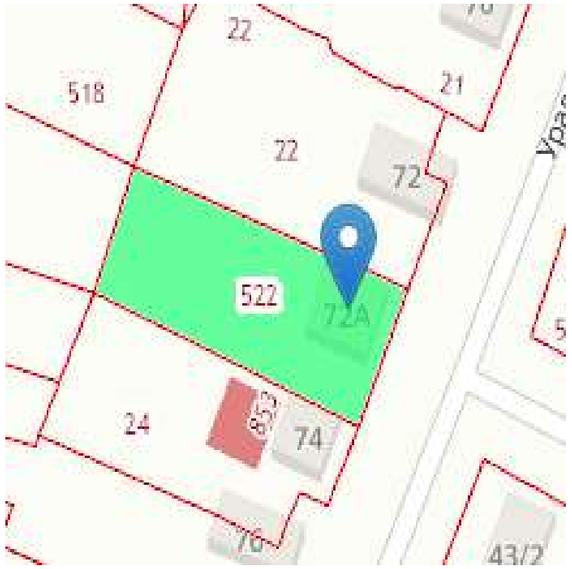

Проектируемый дом

Крыльцо, терраса

Гараж

						кадастровый номер 63:03:0211031:617, Самарская область, г. Кинель, ул. Уральская, 72а Россия
Изм.	Кол.уч.	Лист	№Док.	Подп.	Дата	
Разраб.		Салыкова Е.				Индивидуальный жилой дом

Стадия	Лист	Листов
ЭП	04	


Схема организации участка







						кадастровый номер 63:03:0211031:617, Самарская область, г. Кинель, ул. Уральская, 72а Россия	
Изм.	Кол.уч.	Лист	№Док.	Подп.	Дата		
Разраб.		Салыкова Е.				Индивидуальный жилой дом	Стадия: ЭП; Лист: 05; Листов:
						3D Виды	

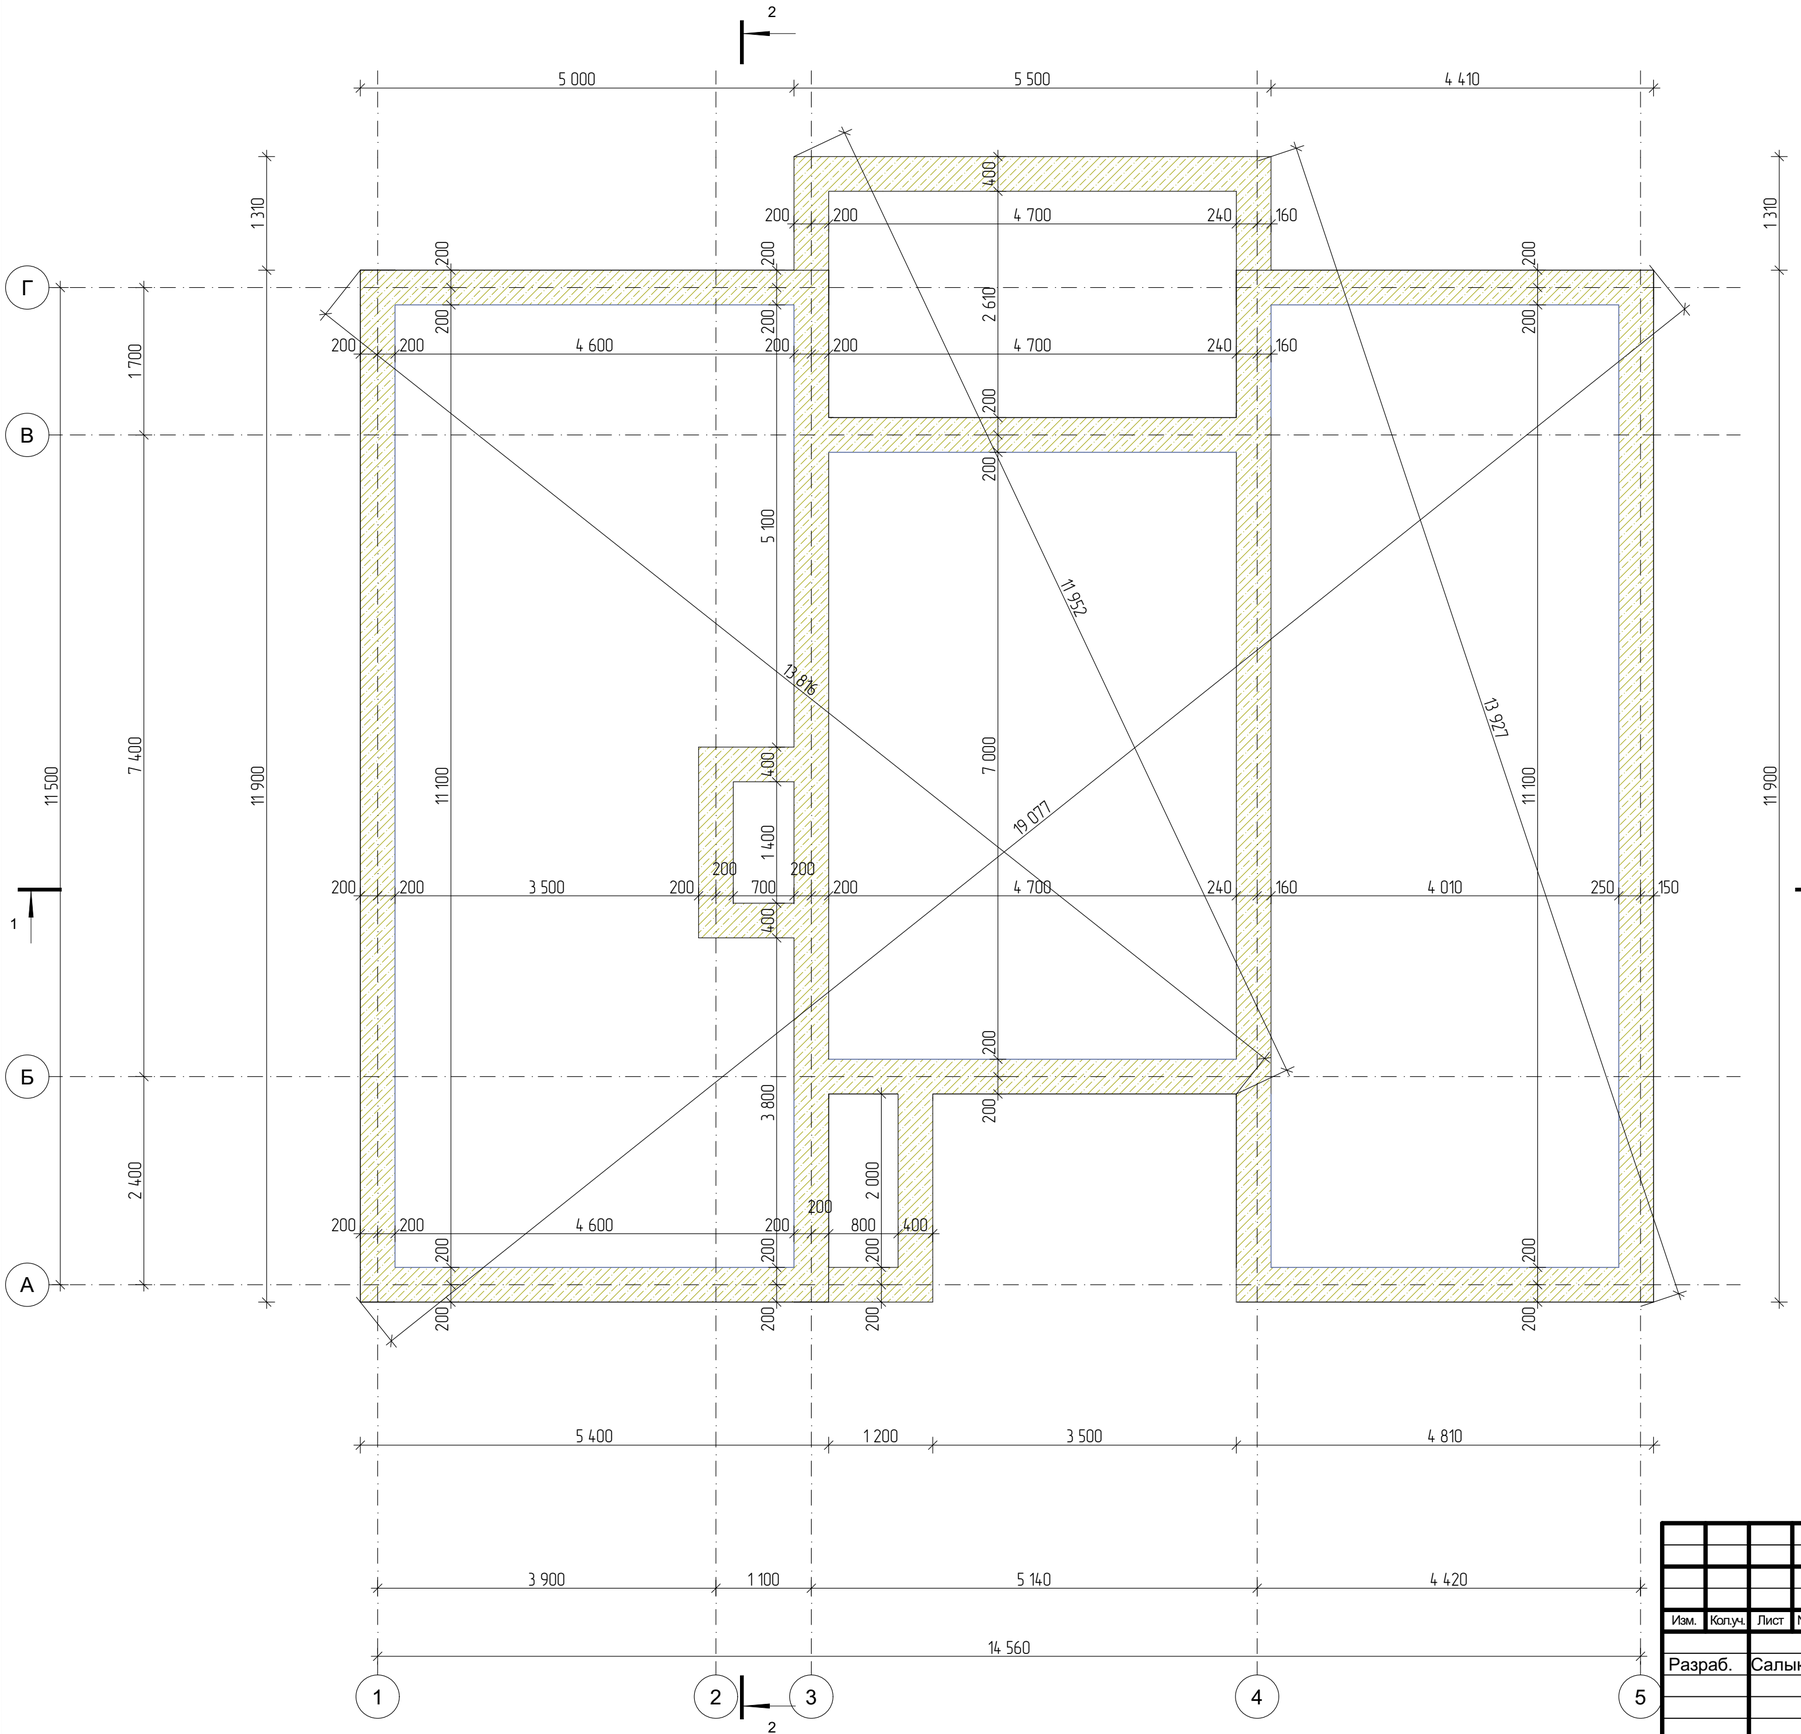


1. Стены фундаменты выполнить из бетона класса В25
2. Все подземные бетонные конструкции огрунтовать битумной мастикой за два раза.

ВЕДОМОСТЬ БЕТОНА

Наименование	Объем, м3
Лента Фундамента	69,81

Изм.	Колуч.	Лист	№Док.	Подп.	Дата	
						кадастровый номер 63:03:0211031:617, Самарская область, г. Кинель, ул. Уральская, 72а Россия
Разраб.		Салыкова		В.		Индивидуальный жилой дом
						План фундамента

Стадия	Лист	Листов
ЭП	06	

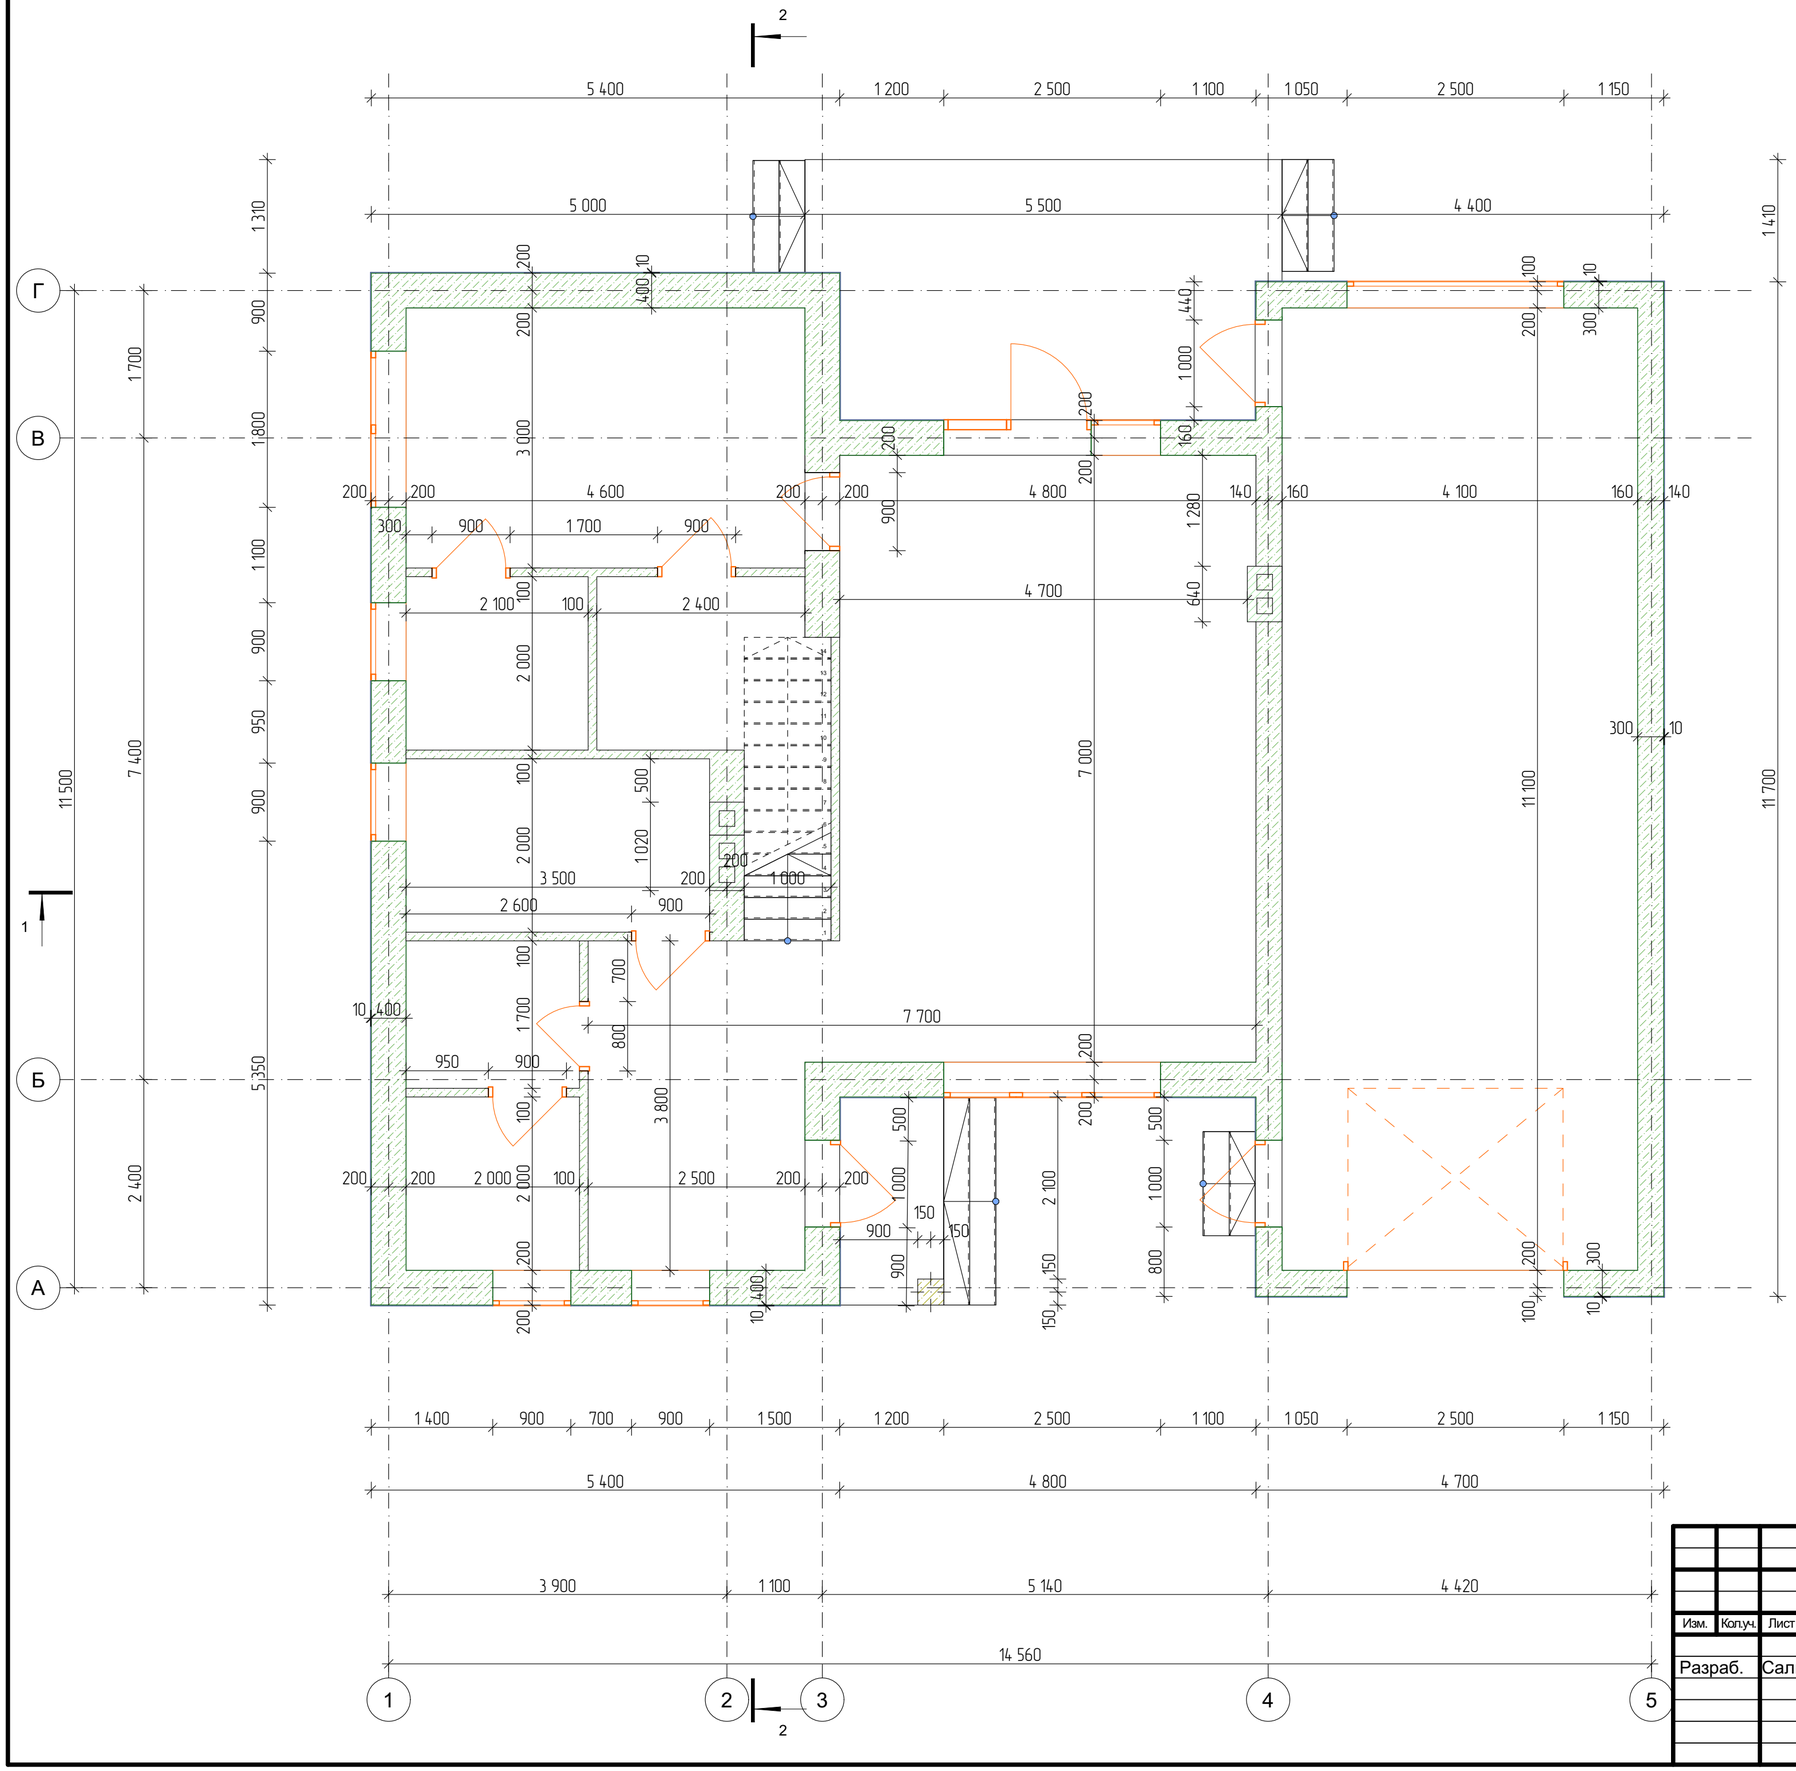

ВЕДОМОСТЬ БЛОКА ДЛЯ СТЕН

ID Элемента	Объем, м3
Несущие 300мм	22,52
Несущие 400мм	68,48
Перегородки 100мм	10,22

Изм.	Колуч.	Лист	№Док.	Подп.	Дата	кадастровый номер 63:03:0211031:617, Самарская область, г. Кинель, ул. Уральская, 72а Россия			
Разраб.		Салыкова В.				Индивидуальный жилой дом	Стадия	Лист	Листов
							ЭП	07	
						План 1 этажа			

ЖБ ригель 400х400


Изм.	Кол.уч.	Лист	№Док.	Подп.	Дата
Разраб.		Салыкова	В.		

кадастровый номер 63:03:0211031:617, Самарская область, г. Кинель, ул. Уральская, 72а Россия

Индивидуальный жилой дом

Стадия	Лист	Листов
ЭП	08	


План 2 этаж

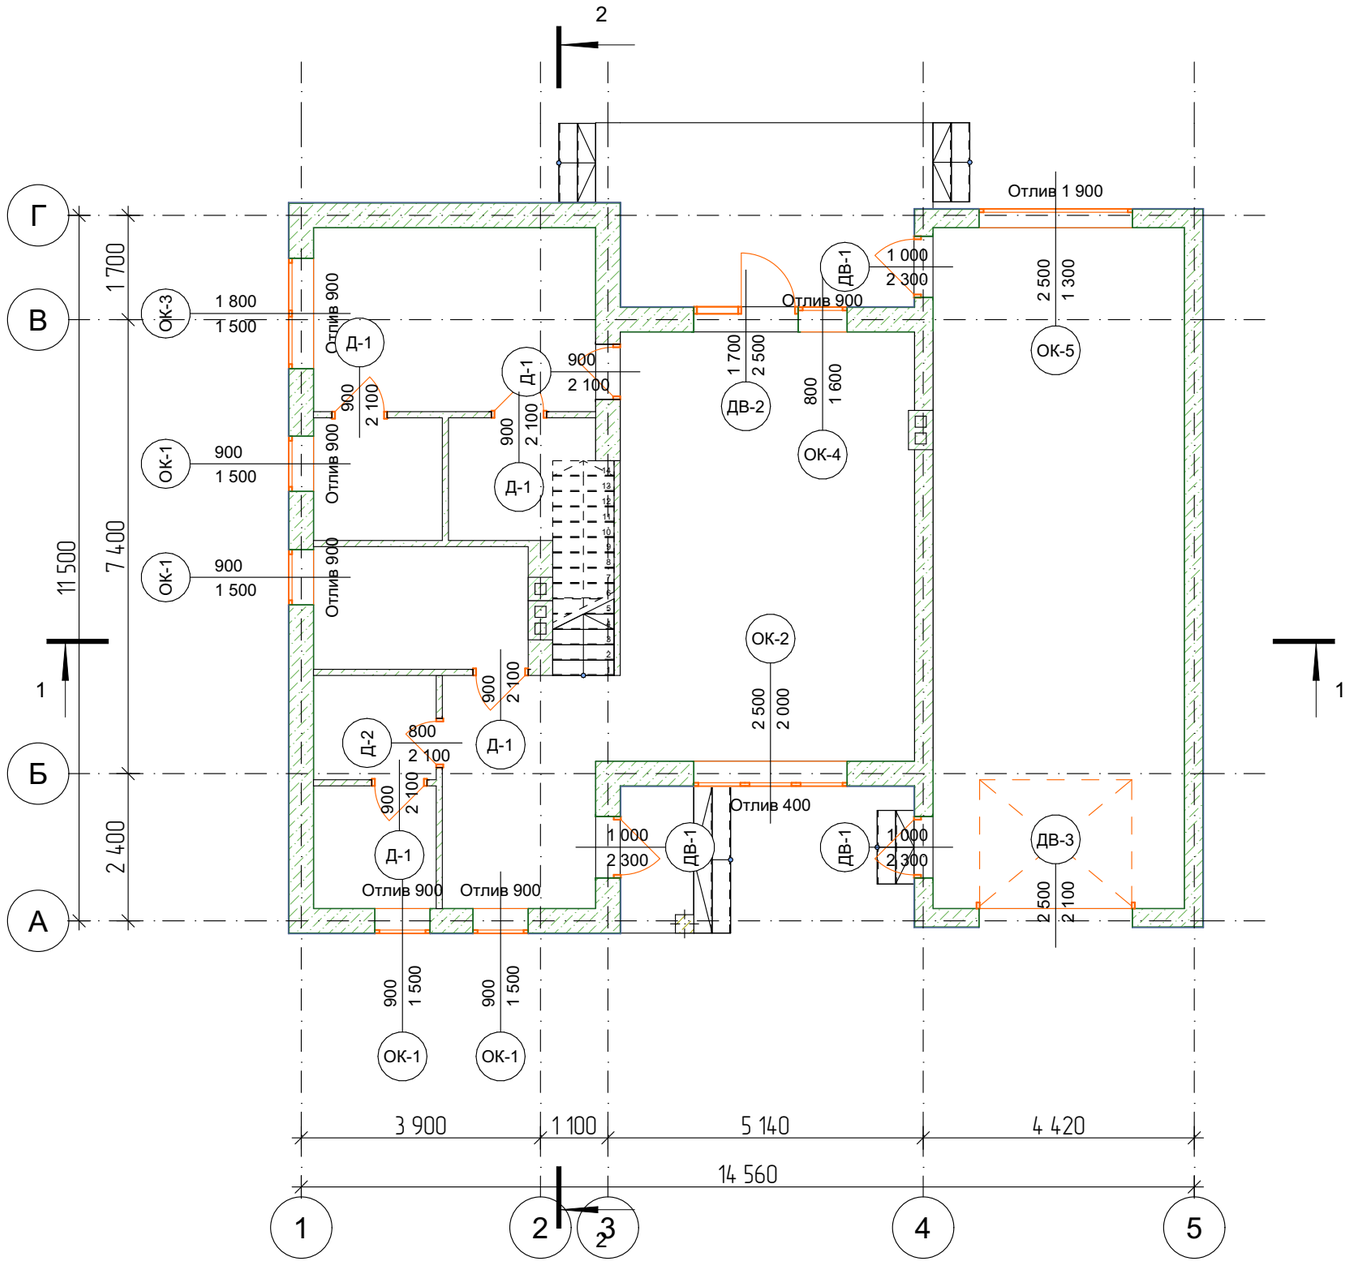

Изм.	Кол.уч.	Лист	№Док.	Подп.	Дата	
Разраб.		Салыкова Е.				








кадастровый номер 63:03:0211031:617, Самарская область, г. Кинель, ул. Уральская, 72а Россия

Индивидуальный жилой дом	Стадия	Лист	Листов
	ЭП	09	
Маркировочный план 1 этаж			

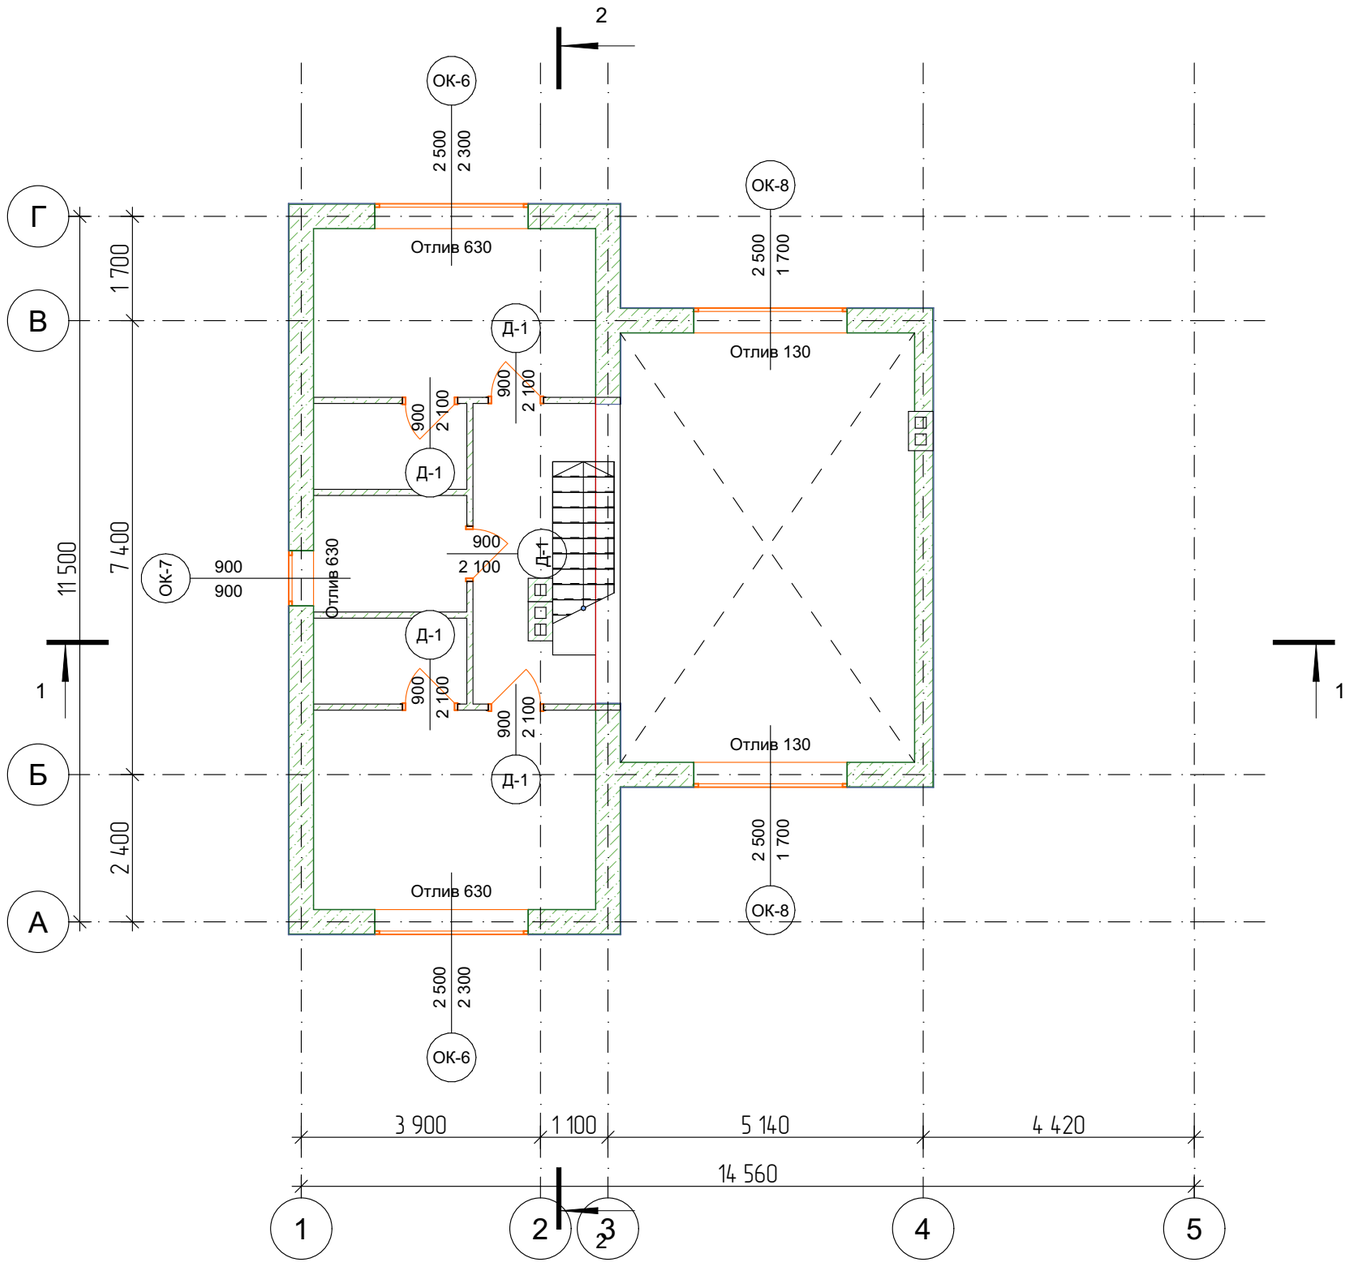







Изм.	Кол.уч.	Лист	№Док.	Подп.	Дата	кадастровый номер 63:03:0211031:617, Самарская область, г. Кинель, ул. Уральская, 72а Россия			
Разраб.		Салыкова Е.				Индивидуальный жилой дом	Стадия	Лист	Листов
							ЭП	10	
						Маркировочный план 2 этаж			

Каталог Дверей

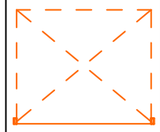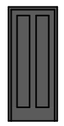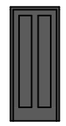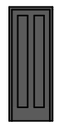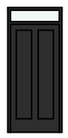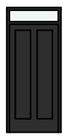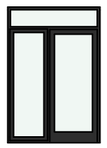
Полный ID Элемента	Д-1	Д-1	Д-2	ДВ-1	ДВ-1	ДВ-2	ДВ-3	П/П
D по Классификации	Дверь -1	Дверь -1	Дверь -2	Дверь -1	Дверь -1	Дверь -2	Дверь -3	Дверь -П/П
Наименование Двери	Однопольная Дверь 27	Однопольная Дверь 27	Однопольная Дверь 27	Однопольная Дверь с Фрамугой 27	Однопольная Дверь с Фрамугой 27	Дверь с Боковой Панелью со Стороны 1 и Фрамугой 27	Ворота Гаражные Подъемные 27	Прямоугольный Дверной Проем 27
Количество	3	7	1	1	2	1	1	1
Размер Ш х В	900×2 100	900×2 100	800×2 100	1 000×2 300	1 000×2 300	1 700×2 500	2 500×2 100	4 900×2 370
Ориентация	Л	П	П	Л	П	П		
Высота Порога Двери	0	0	0	0	0	0	0	-200
Высота Перемычки Двери	2 100	2 100	2 100	2 300	2 300	2 500	2 100	2 170
2D-символ								
Вид со Стороны, Противоположной Стороне Открывания								

Изм.	Кол.уч.	Лист	№Док.	Подп.	Дата			
Разраб.		Салыкова В.				кадастровый номер 63:03:0211031:617, Самарская область, г. Кинель, ул. Уральская, 72а Россия		
						Индивидуальный жилой дом	Стадия: ЭП	Лист: 11
						Каталог дверных проемов		Листов:

Каталог Окон

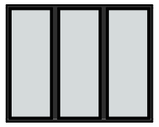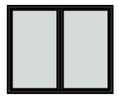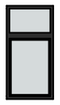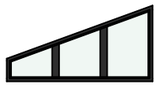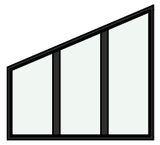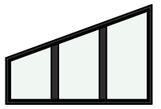
Полный ID Элемента	ОК-1	ОК-2	ОК-3	ОК-4	ОК-5	ОК-6	ОК-7	ОК-8
Наименование Окна	Окно 27	Трехстворчатое Окно 27	Раздвижное Двустворчатое Окно 27	Окно 27	Трапецеидальное Окно 27	Трапецеидальное Окно 27	Окно 27	Трапецеидальное Окно 27
Количество	4	1	1	1	1	2	1	2
Размер Ш x В	900×1 500	2 500×2 000	1 800×1 500	800×1 600	2 500×1 300	2 500×2 300	900×900	2 500×1 700
Высота Подоконника Окна	900	400	900	900	1 900	630	630	130
Высота Перемычки Окна	2 400	2 400	2 400	2 500	3 200	2 930	1 530	1 830
2D-символ								
Вид со Стороны, Противоположной Стороне Открывания								

Изм.	Кол.уч.	Лист	№Док.	Подп.	Дата			
Разраб.		Салыкова Е.				кадастровый номер 63:03:0211031:617, Самарская область, г. Кинель, ул. Уральская, 72а Россия		
						Индивидуальный жилой дом	Стадия: ЭП	Лист: 12	Листов:
						Каталог оконных проемов			

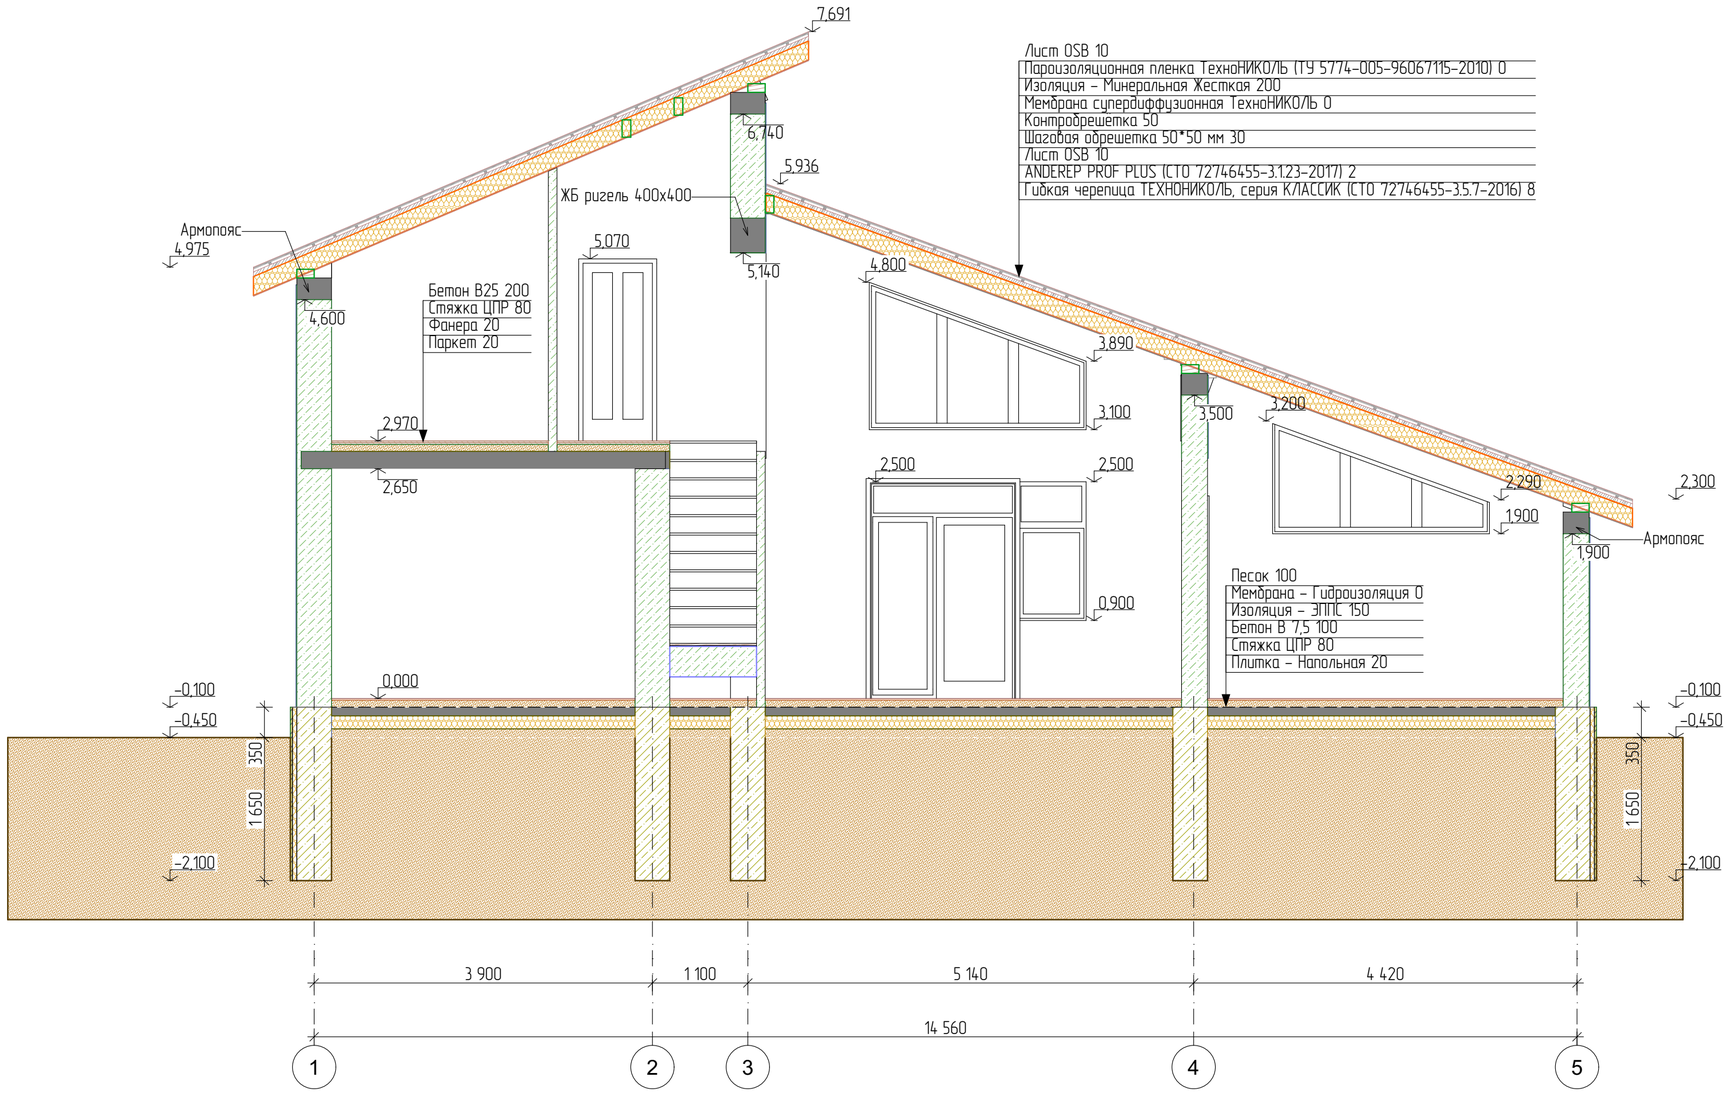

Изм.	Кол.уч.	Лист	№Док.	Подп.	Дата	
						кадастровый номер 63:03:0211031:617, Самарская область, г. Кинель, ул. Уральская, 72а Россия
Разраб.		Салыкова	В.			Индивидуальный жилой дом
						Разрез 1 - 1


Стадия	Лист	Листов
ЭП	13	

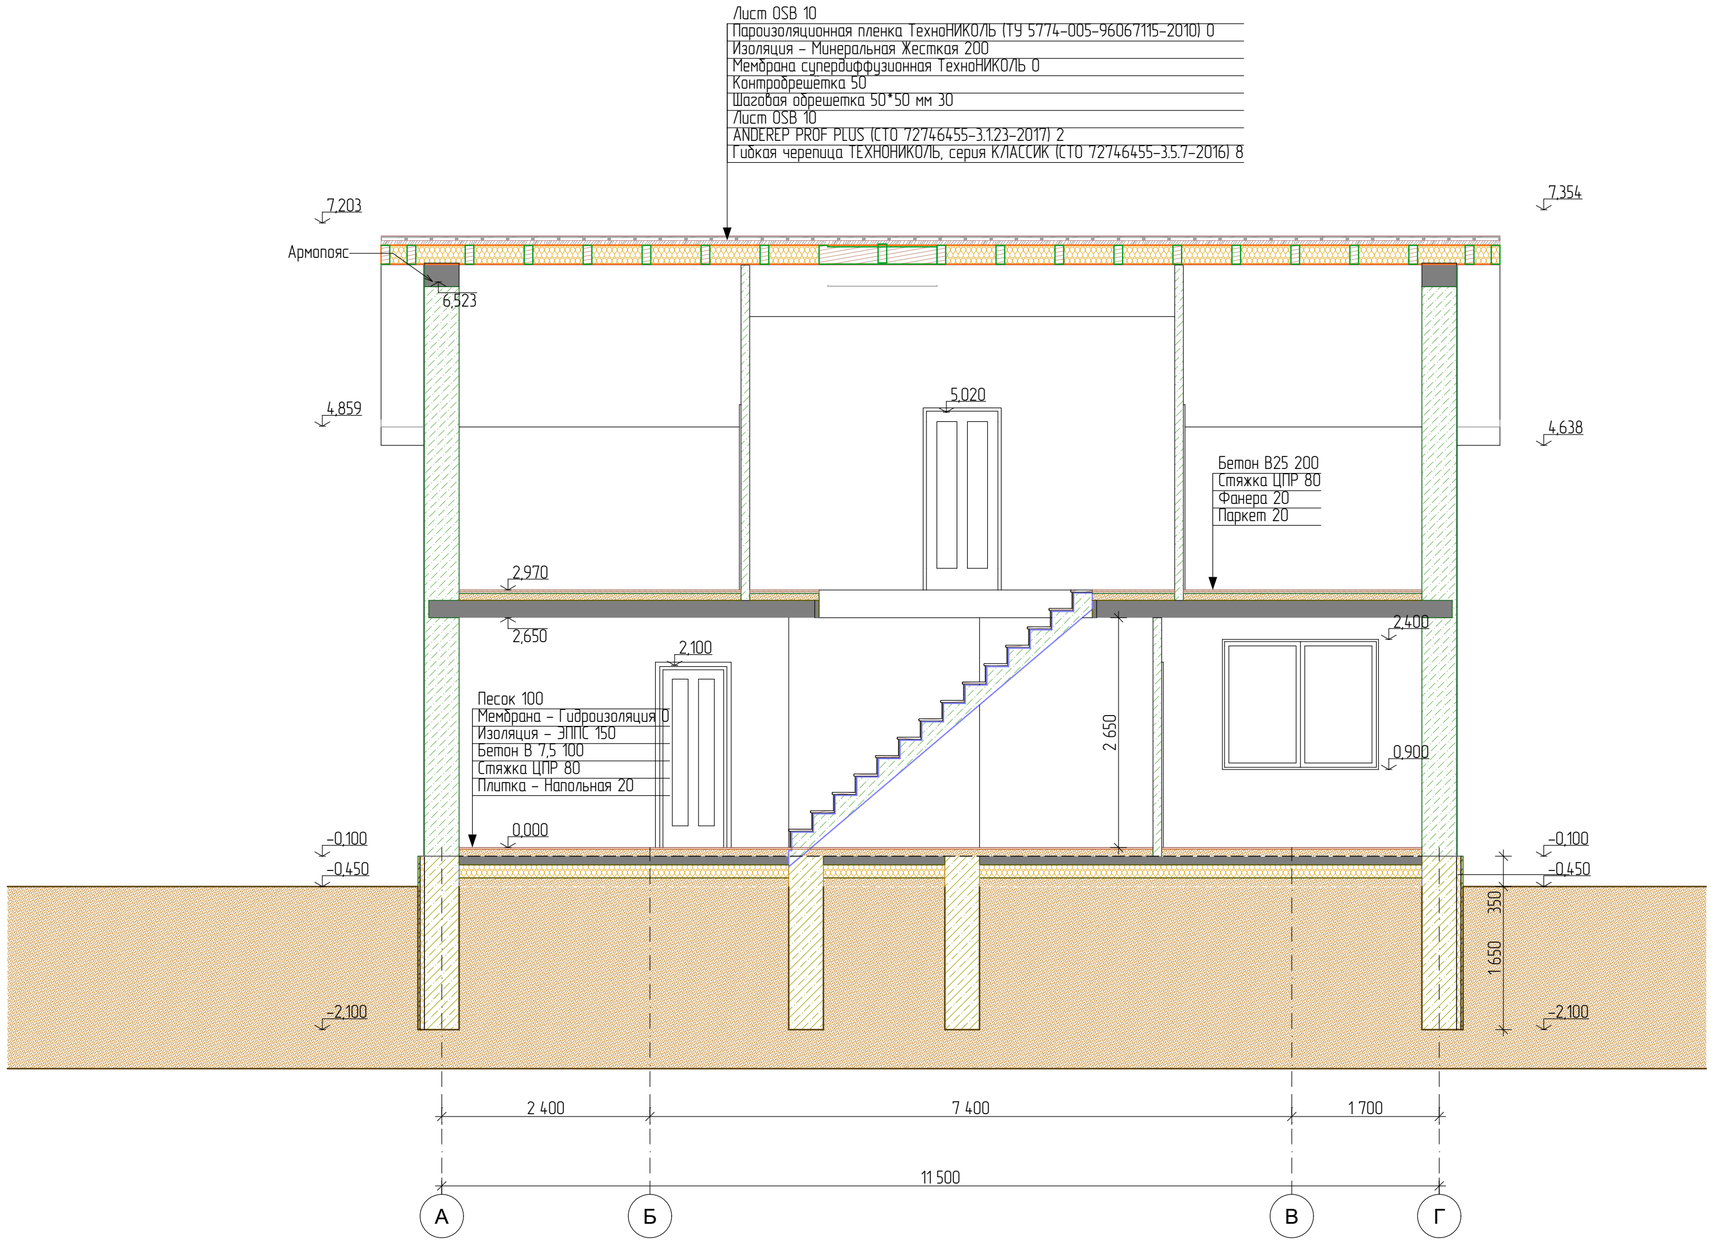

Изм.	Кол.уч.	Лист	№Док.	Подп.	Дата	
						кадастровый номер 63:03:0211031:617, Самарская область, г. Кинель, ул. Уральская, 72а Россия
Разраб.		Салыкова	В.			Индивидуальный жилой дом
						Разрез 2 - 2

Стадия	Лист	Листов
ЭП	14	


Лист OSB 10
Пароизоляционная пленка ТехноНИКОЛЬ (ТУ 5774-005-96067115-2010) 0
Изоляция – Минеральная Жесткая 200
Мембрана супердиффузионная ТехноНИКОЛЬ 0
Контробрешётка 50
Шаговая обрешетка 50*50 мм 30
Лист OSB 10
ANDEREP PROF PLUS (СТО 72746455-3.1.23-2017) 2
Гибкая черепица ТЕХНОНИКОЛЬ, серия КЛАССИК (СТО 72746455-3.5.7-2016) 8

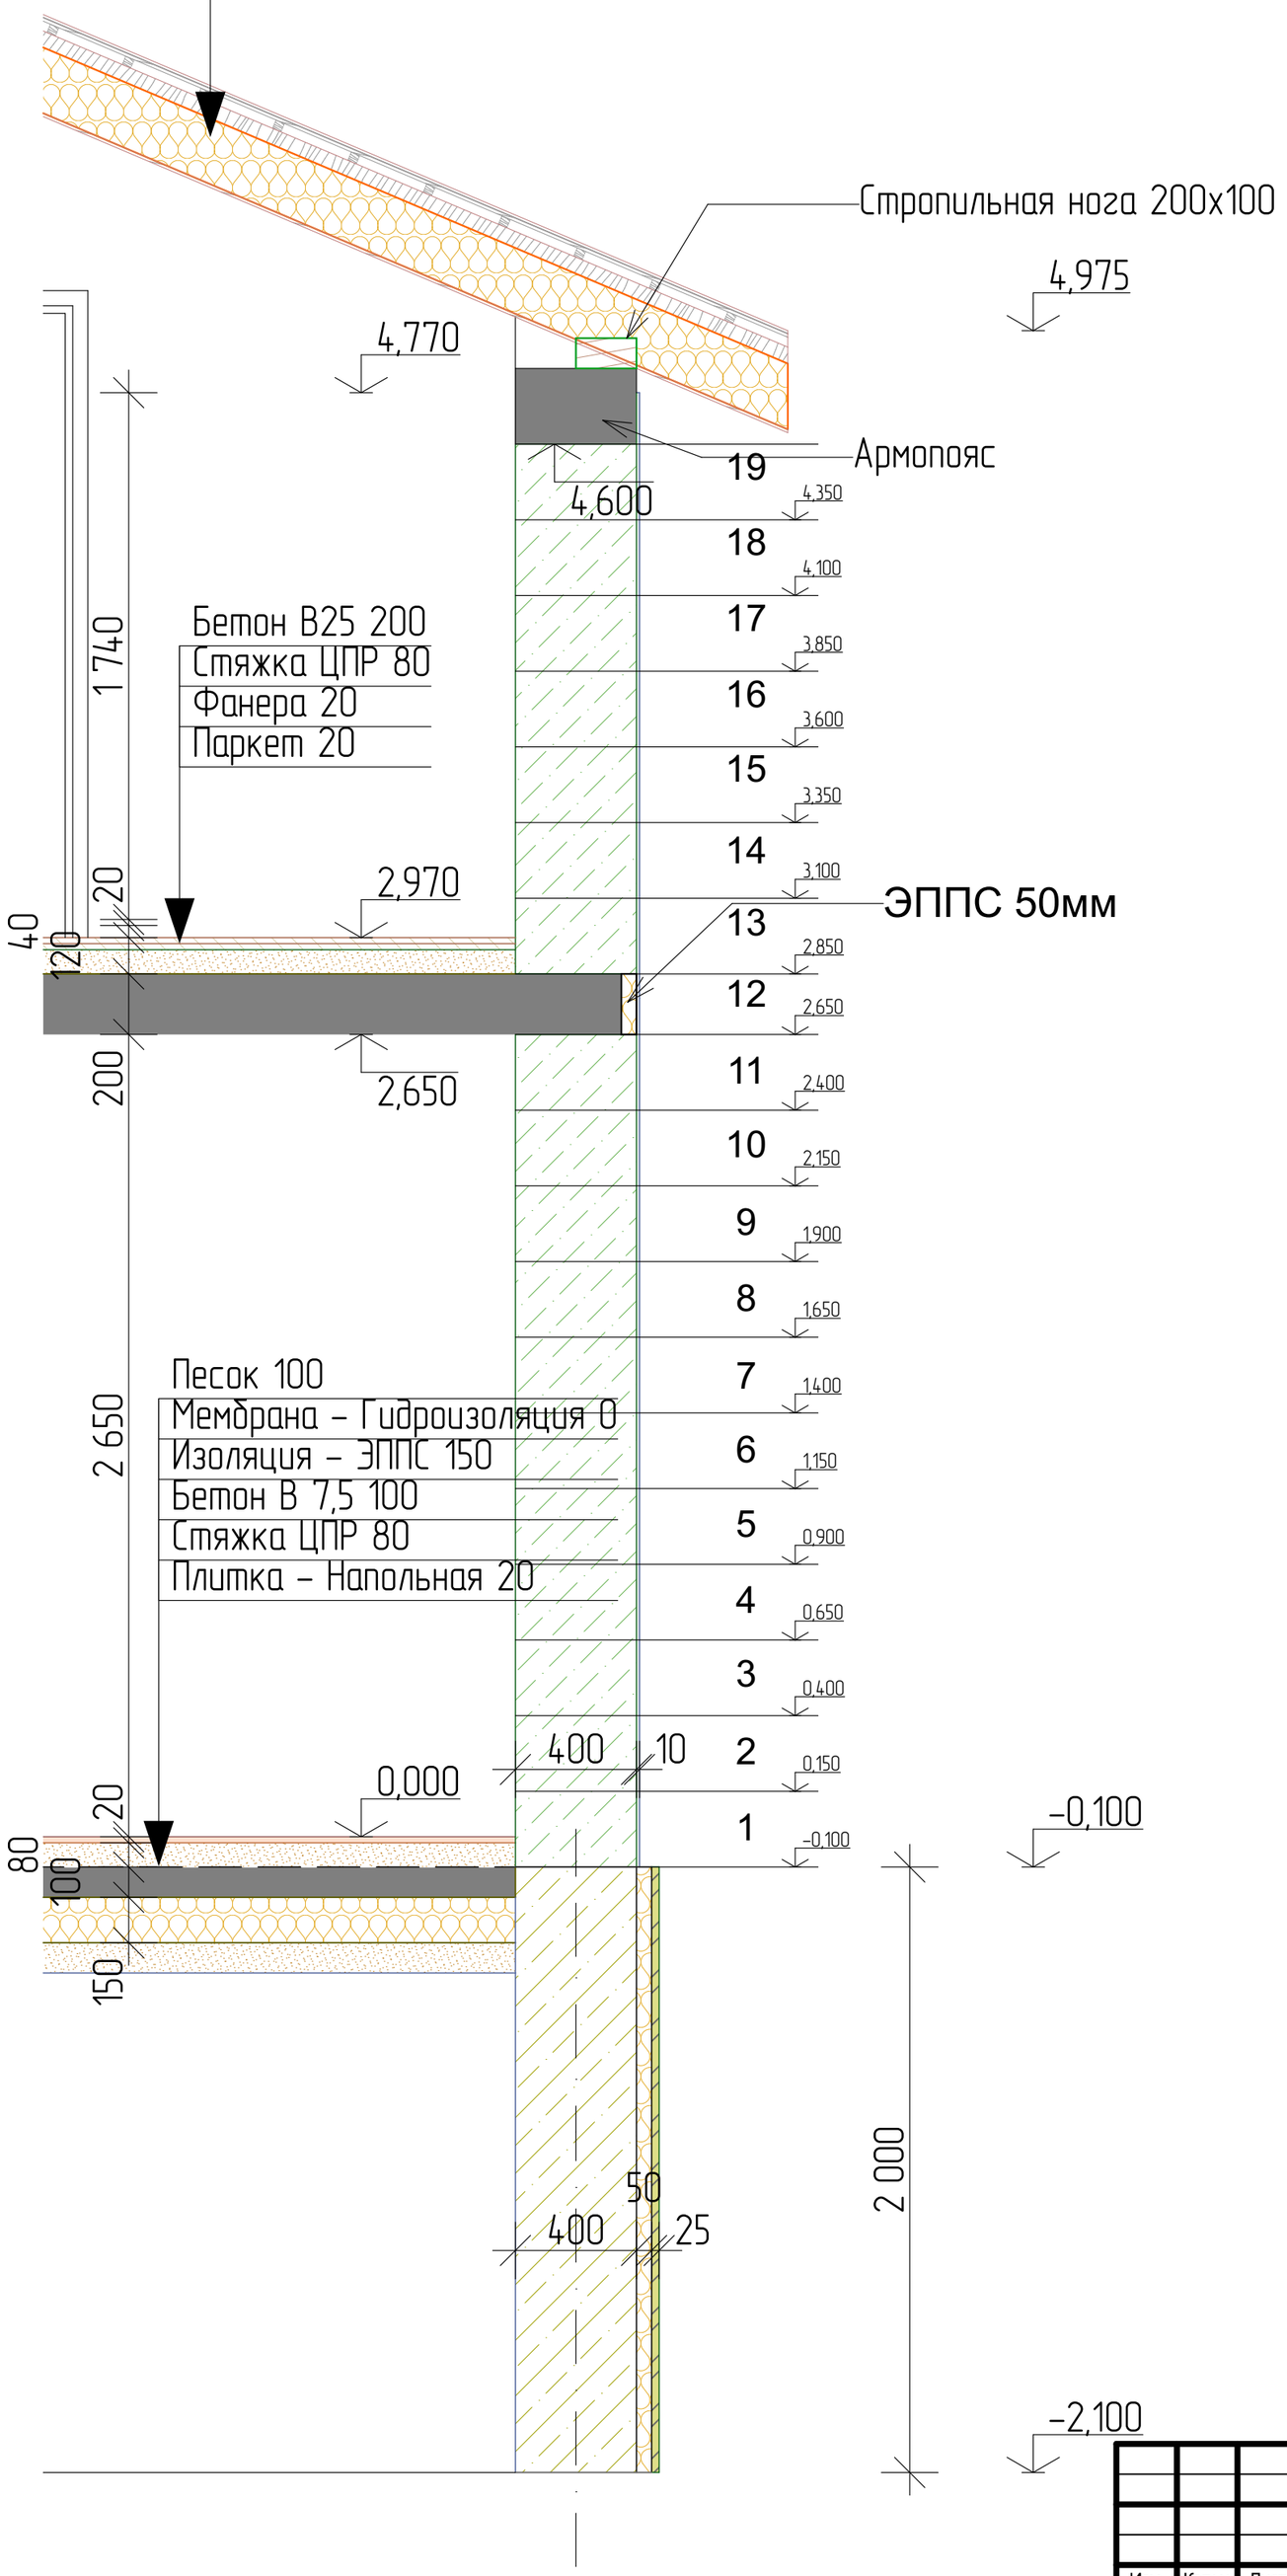

Изм.	Кол.уч.	Лист	№Док.	Подп.	Дата
Разраб.		Салыкова В.			

кадастровый номер 63:03:0211031:617, Самарская область, г. Кинель, ул. Уральская, 72а Россия

Индивидуальный жилой дом	Стадия	Лист	Листов
	ЭП	15	
Разрез по стене			

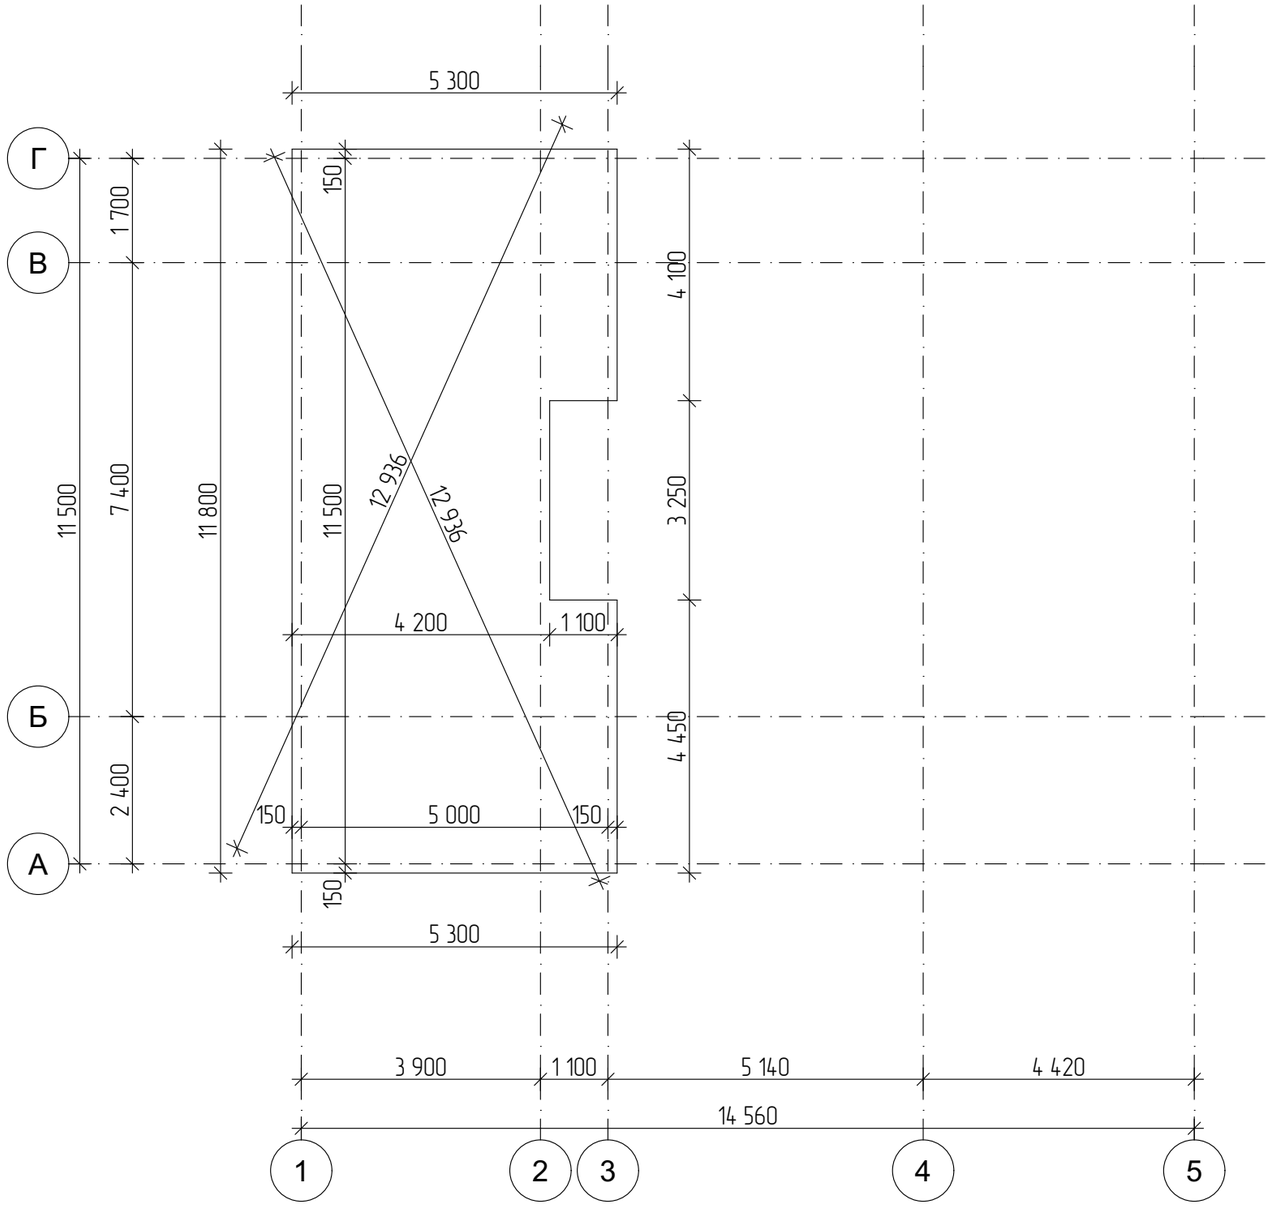



ВЕДОМОСТЬ ПЕРЕКРЫТИЯ

Наименование	Объем ,м3
Монолитное перекрытие	11,79

Изм.	Кол.уч.	Лист	№Док.	Подп.	Дата	
						кадастровый номер 63:03:0211031:617, Самарская область, г. Кинель, ул. Уральская, 72а Россия
Разраб.		Салыкова В.				Индивидуальный жилой дом
						План перекрытия +2,970

Стадия	Лист	Листов
ЭП	16	

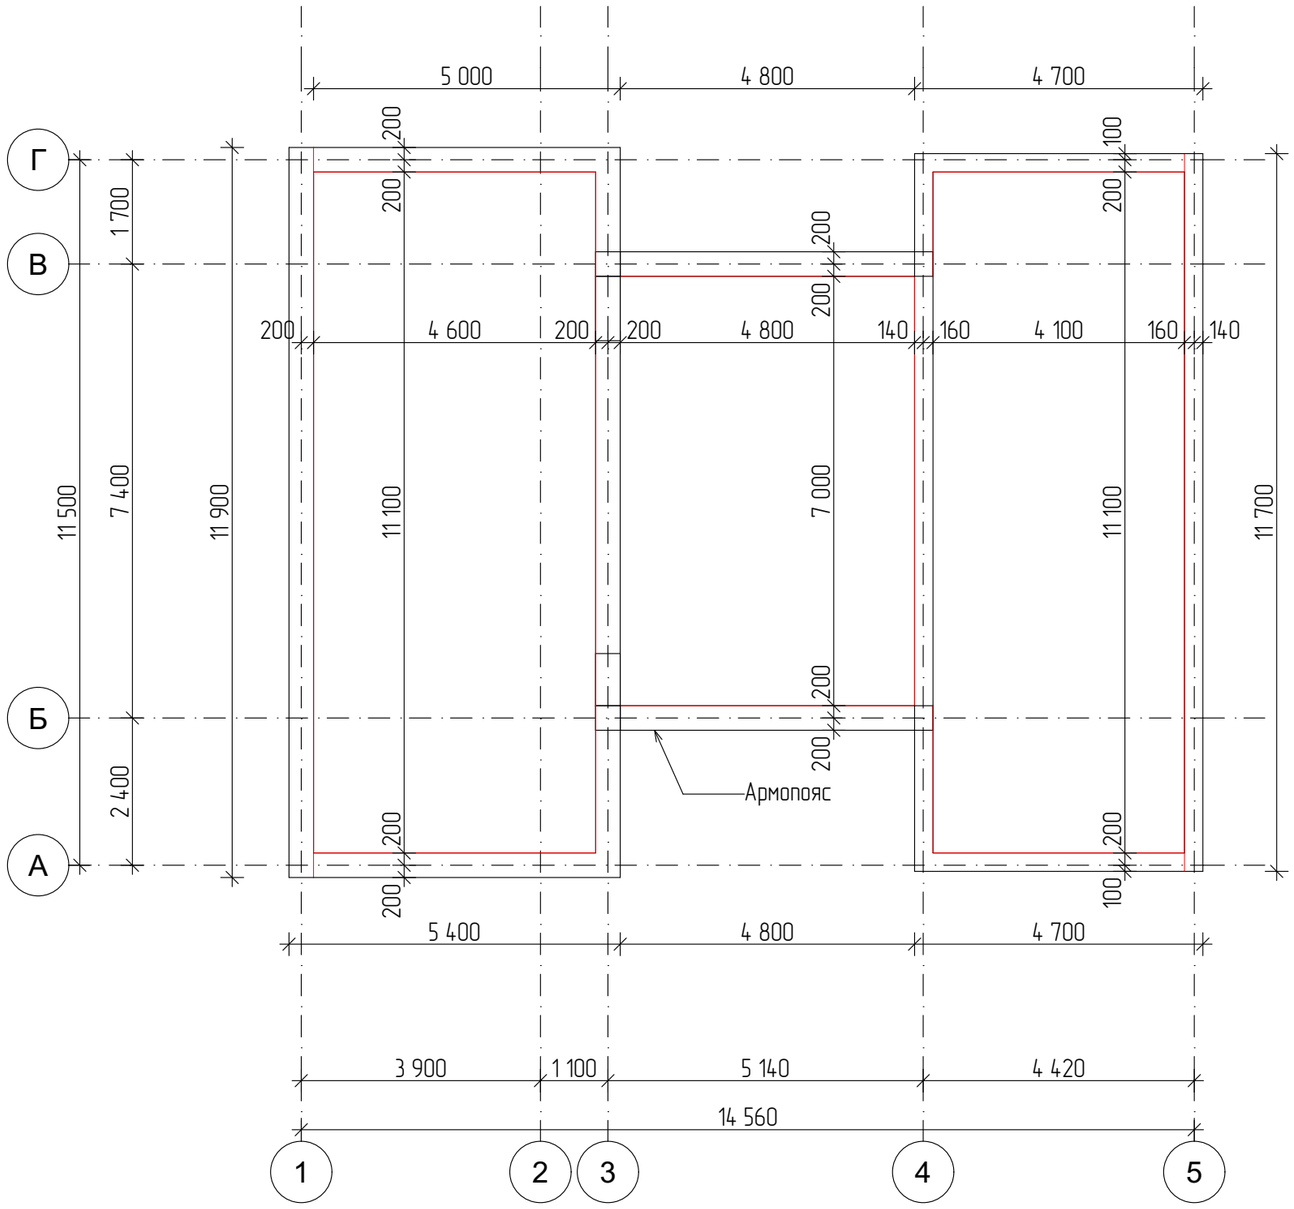

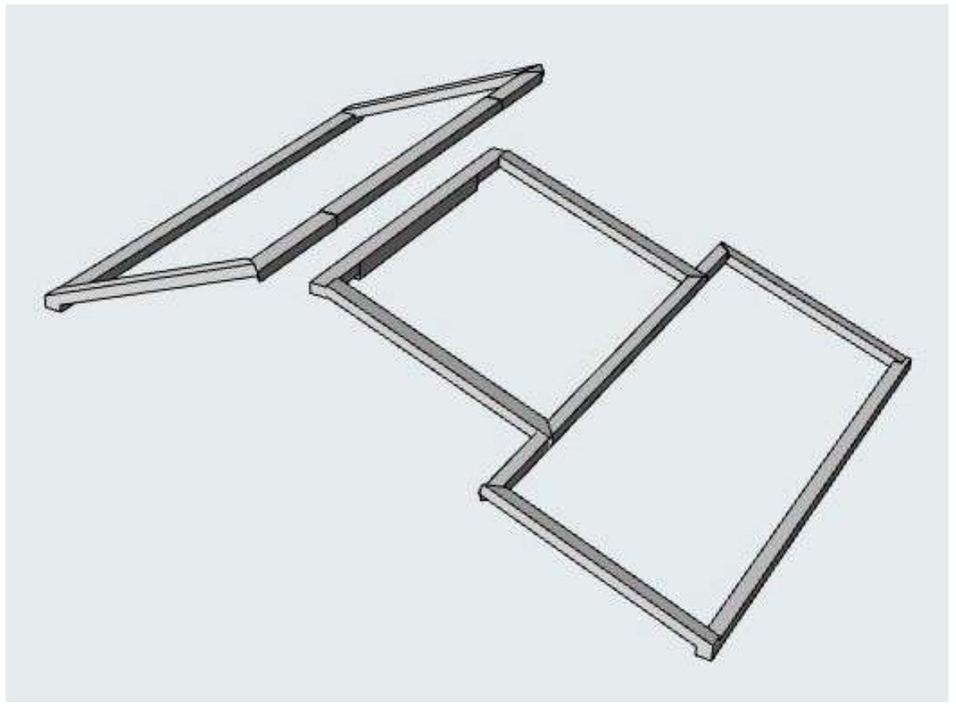


ВЕДОМОСТЬ НА МОНОЛИТНЫЙ ПОЯС 2-ГО ЭТАЖА

Наименование	Объем, м3
	7,16
Армопояс	7,16

Изм.	Кол.уч.	Лист	№Док.	Подп.	Дата	
						кадастровый номер 63:03:0211031:617, Самарская область, г. Кинель, ул. Уральская, 72а Россия
Разраб.		Салыкова Е.				Индивидуальный жилой дом

Стадия	Лист	Листов
ЭП	17	

План армопояса

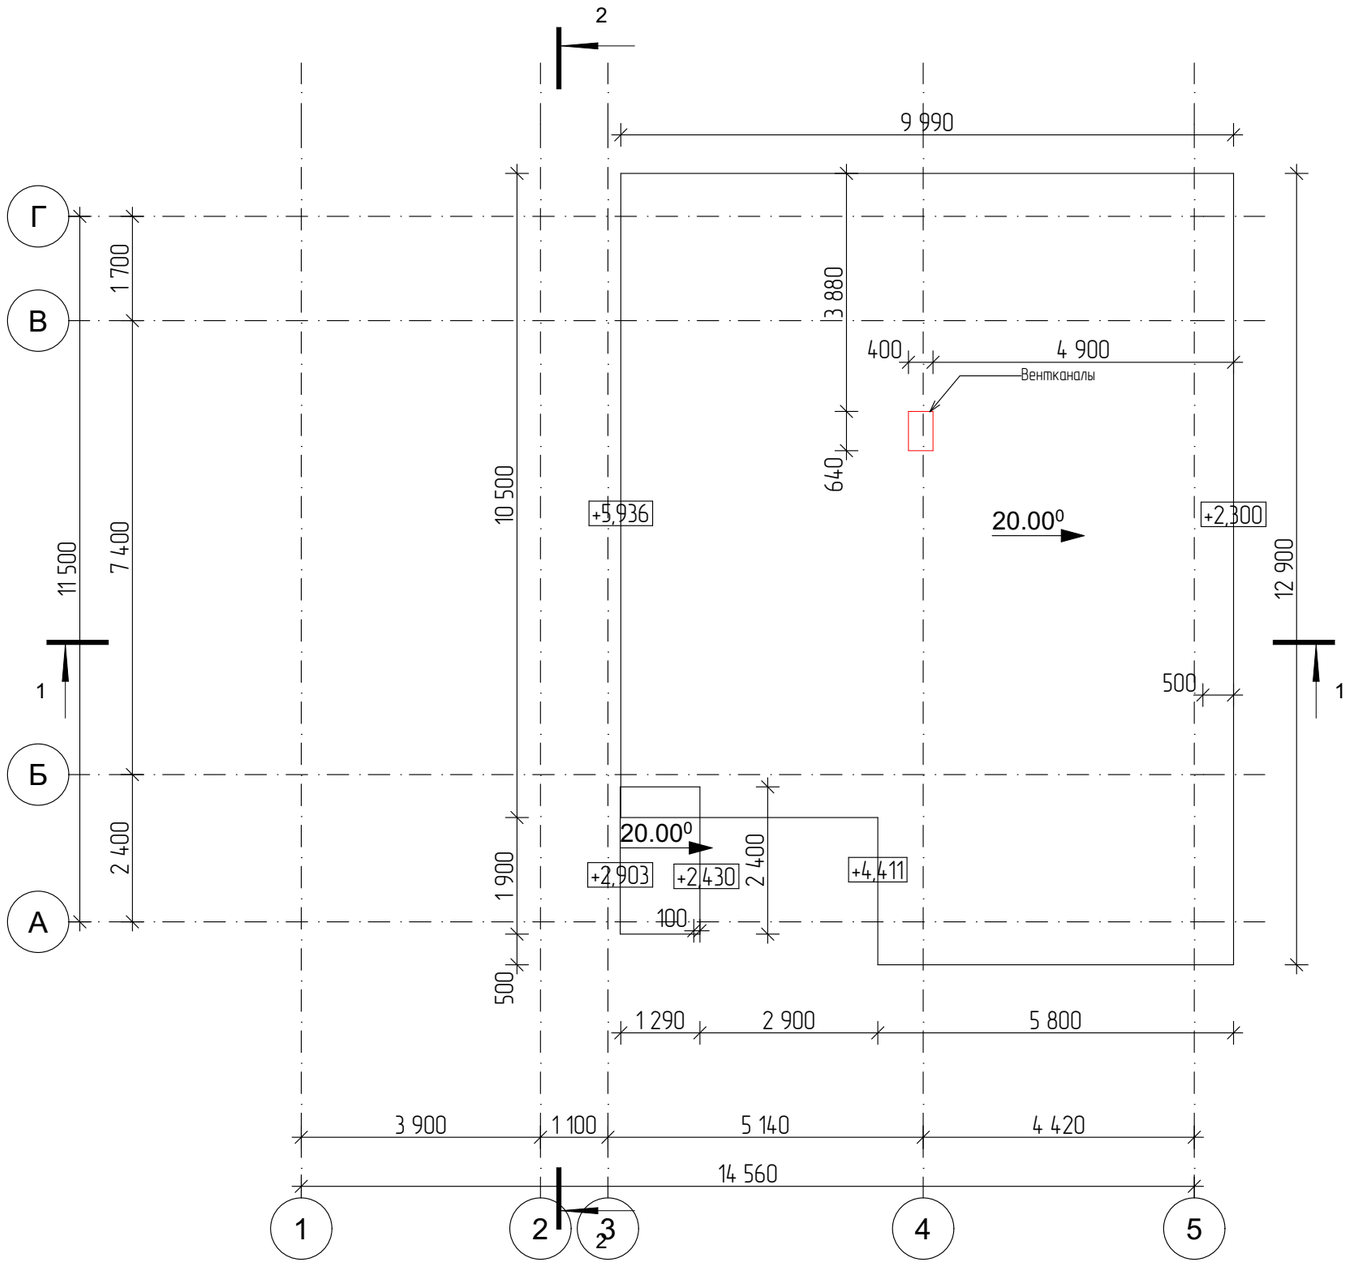




ИКК-03 Кровля

Наименование	Площадь Ве...
Кровля дома	129,76

Изм.	Кол.уч.	Лист	№Док.	Подп.	Дата	
						кадастровый номер 63:03:0211031:617, Самарская область, г. Кинель, ул. Уральская, 72а Россия
Разраб.		Салыкова Е.				Индивидуальный жилой дом

Стадия	Лист	Листов
ЭП	18	

План кровли на отм. +2,300

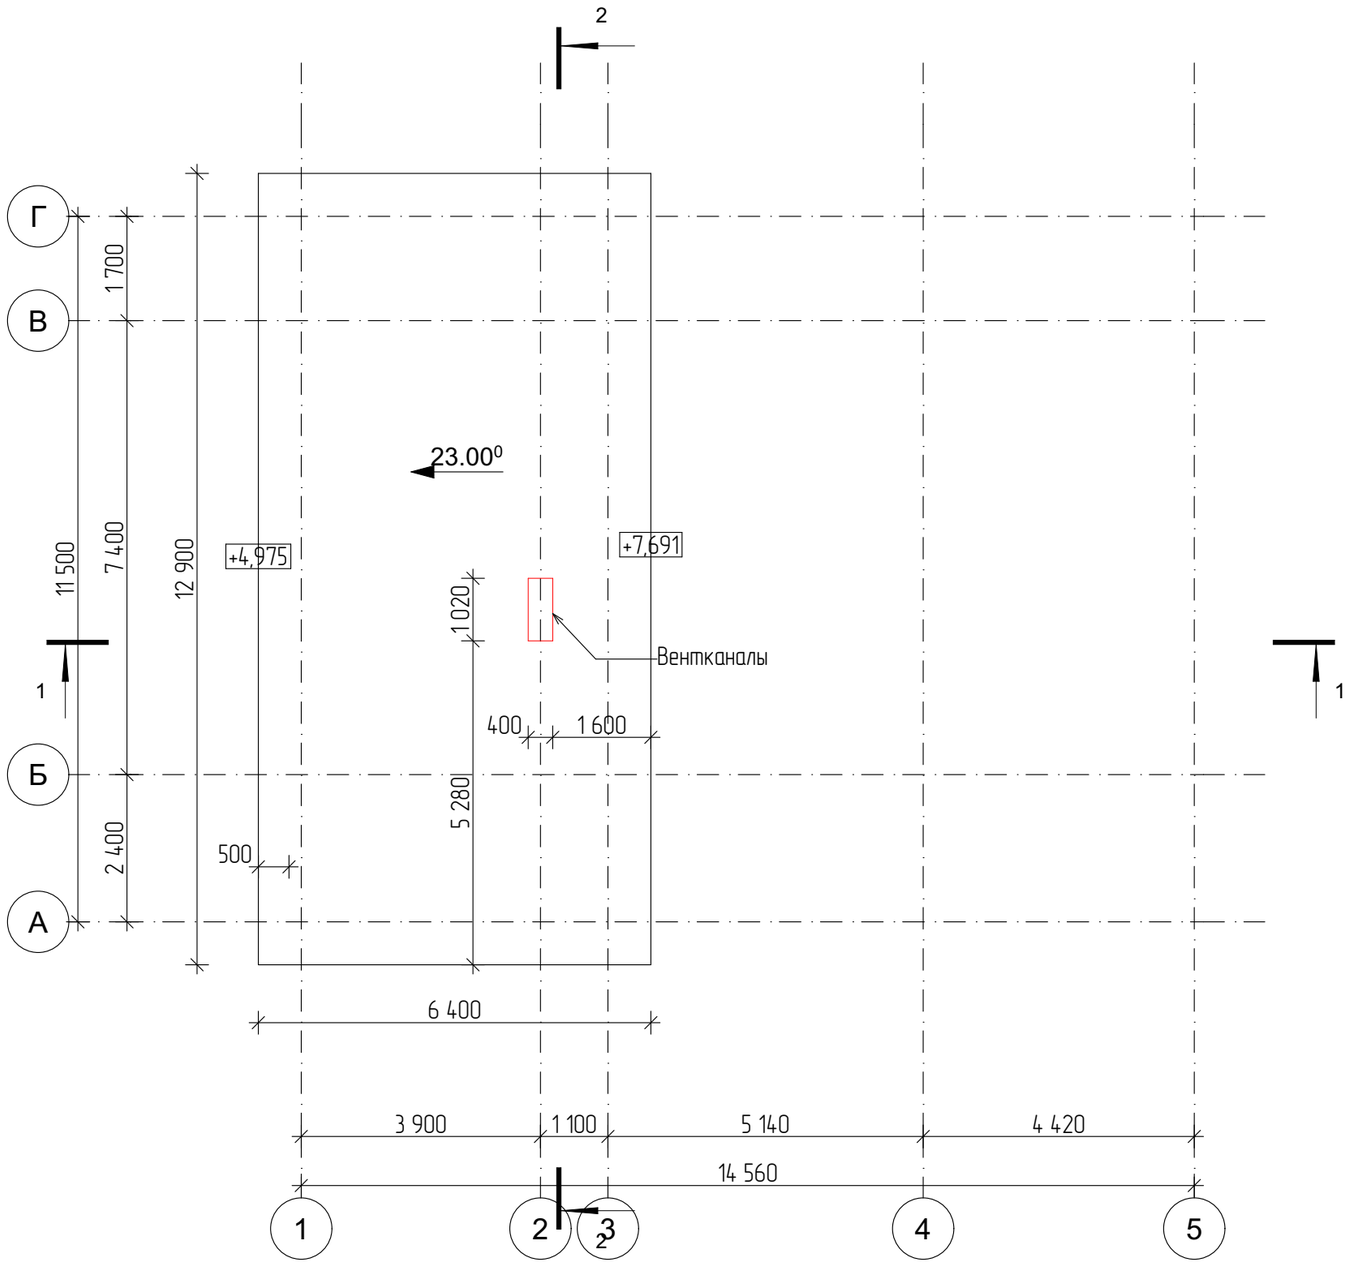


ВЕДОМОСТЬ КРОВЕЛЬНОГО МАТЕРИАЛА

Наименование	Площадь, м2
Кровля дома	89,69


Изм.	Кол.уч.	Лист	№Док.	Подп.	Дата	
						кадастровый номер 63:03:0211031:617, Самарская область, г. Кинель, ул. Уральская, 72а Россия
Разраб.		Салыкова Е.				Индивидуальный жилой дом
						План кровли на отм. +4,975

Стадия	Лист	Листов
ЭП	19	

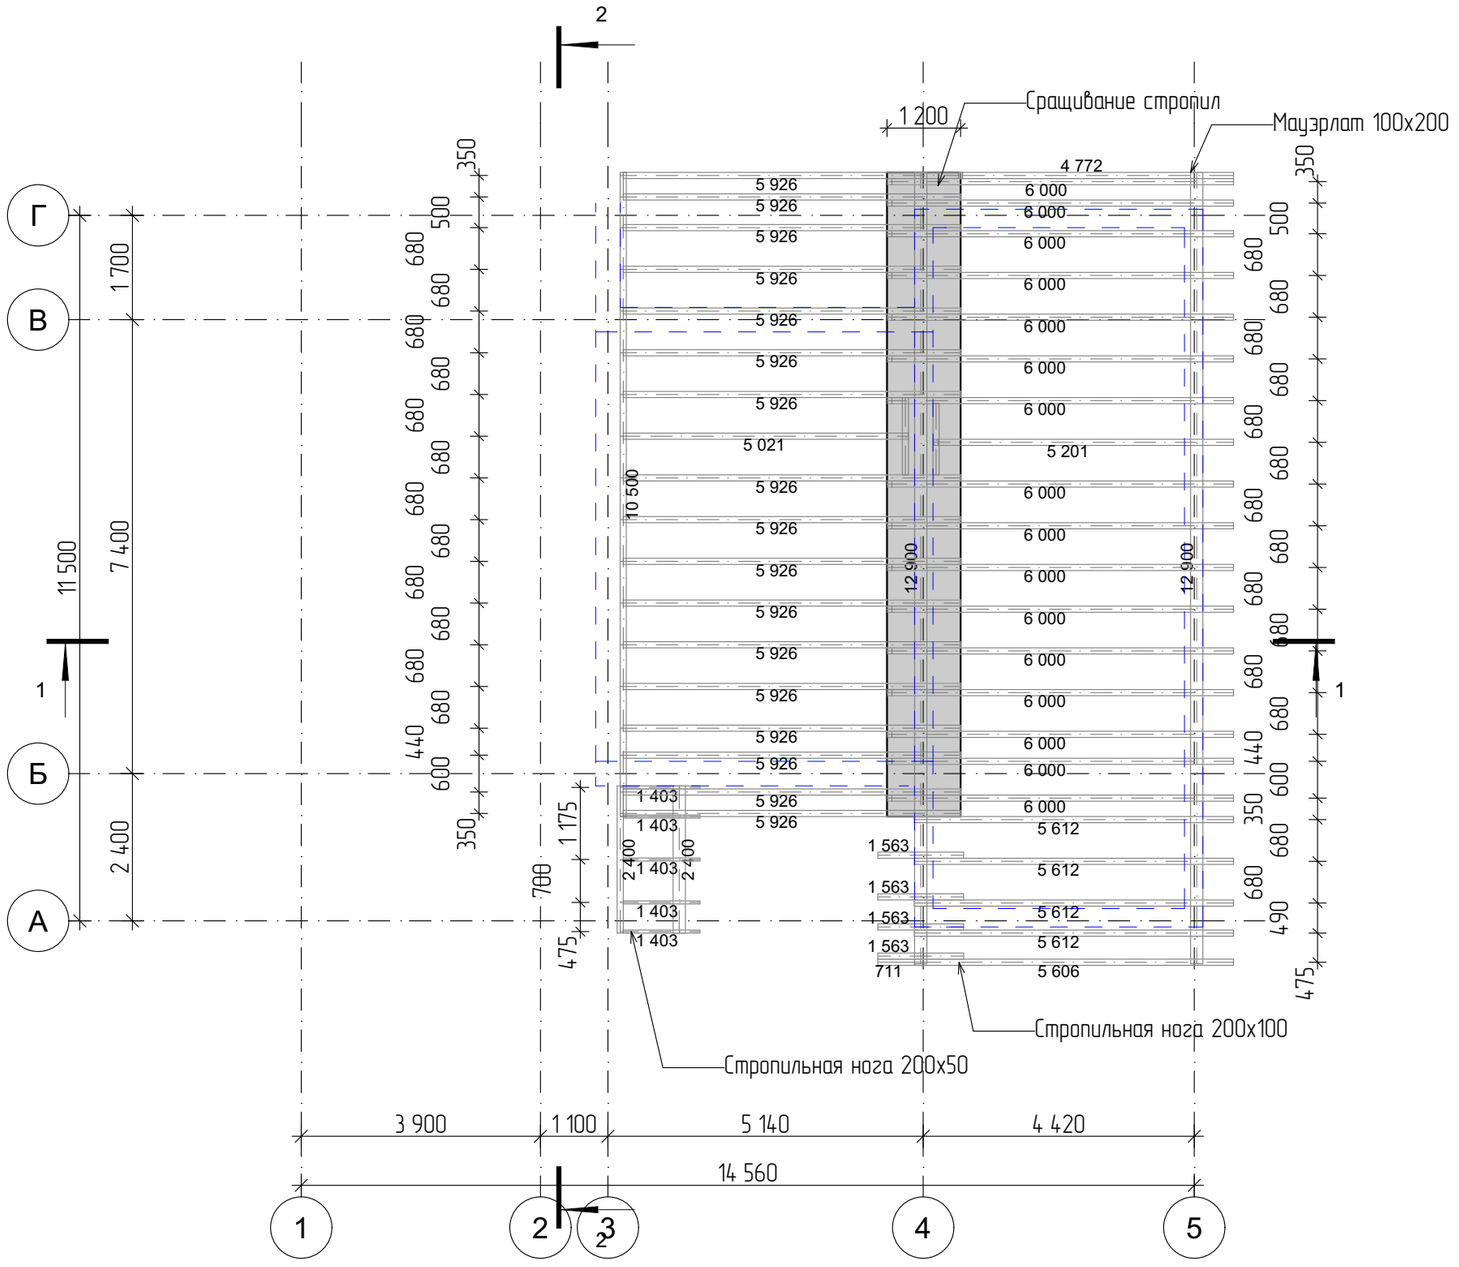

ИКК-03 Стропильная система	
Наименование	Объем, м3
	0,05
Коньковый брус 200х100	0,05
Мауэрлат 100х200	0,57
Стропильная нога 200х50	0,05
Стропильная нога 200х100	5,14

Изм.	Кол.уч.	Лист	№Док.	Подп.	Дата	кадастровый номер 63:03:0211031:617, Самарская область, г. Кинель, ул. Уральская, 72а Россия			
Разраб.		Салыкова Е.				Индивидуальный жилой дом	Стадия	Лист	Листов
							ЭП	20	
						Схема расположения стропил на отм. +2,300			

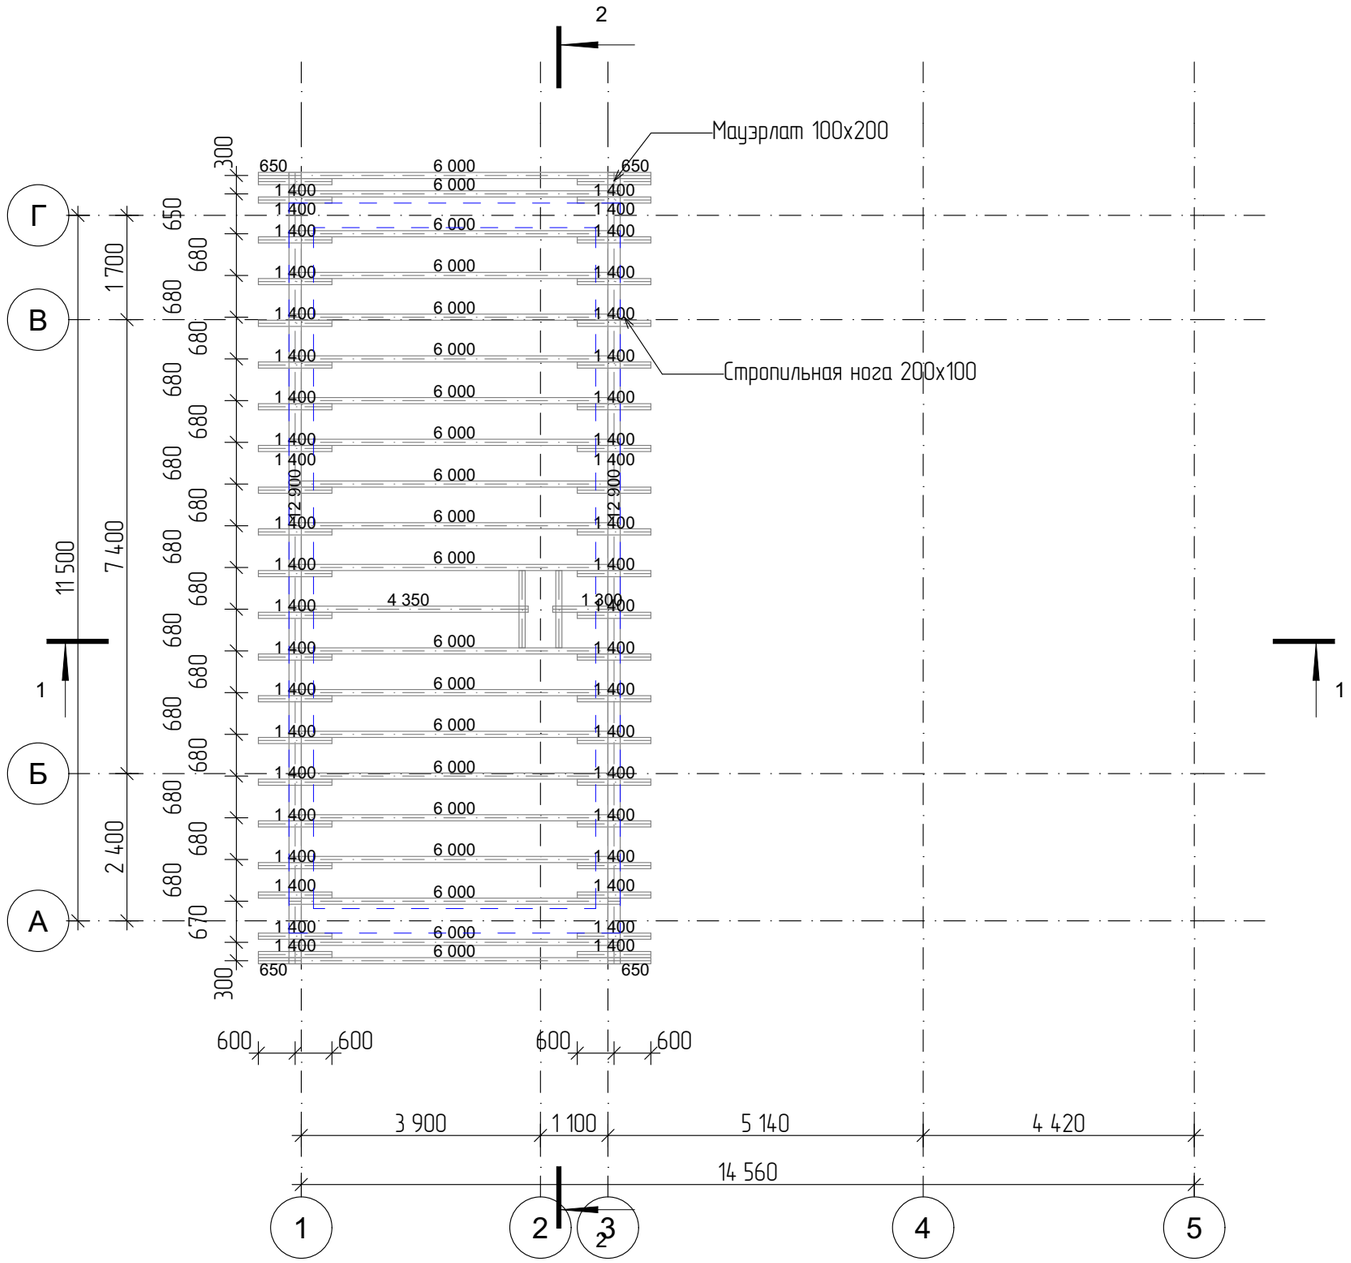



ВЕДОМОСТЬ СТРОПИЛЬНОЙ СИСИТЕМЫ

Наименование	Объем, м3
	0,06
Мауэрлат 100х200	0,26
Стропильная нога 200х100	4,06

Изм.	Кол.уч.	Лист	№Док.	Подп.	Дата	
						кадастровый номер 63:03:0211031:617, Самарская область, г. Кинель, ул. Уральская, 72а Россия
Разраб.		Салыкова Е.				Индивидуальный жилой дом
						Схема расположения стропил на отм. +4,975

Стадия	Лист	Листов
ЭП	21	

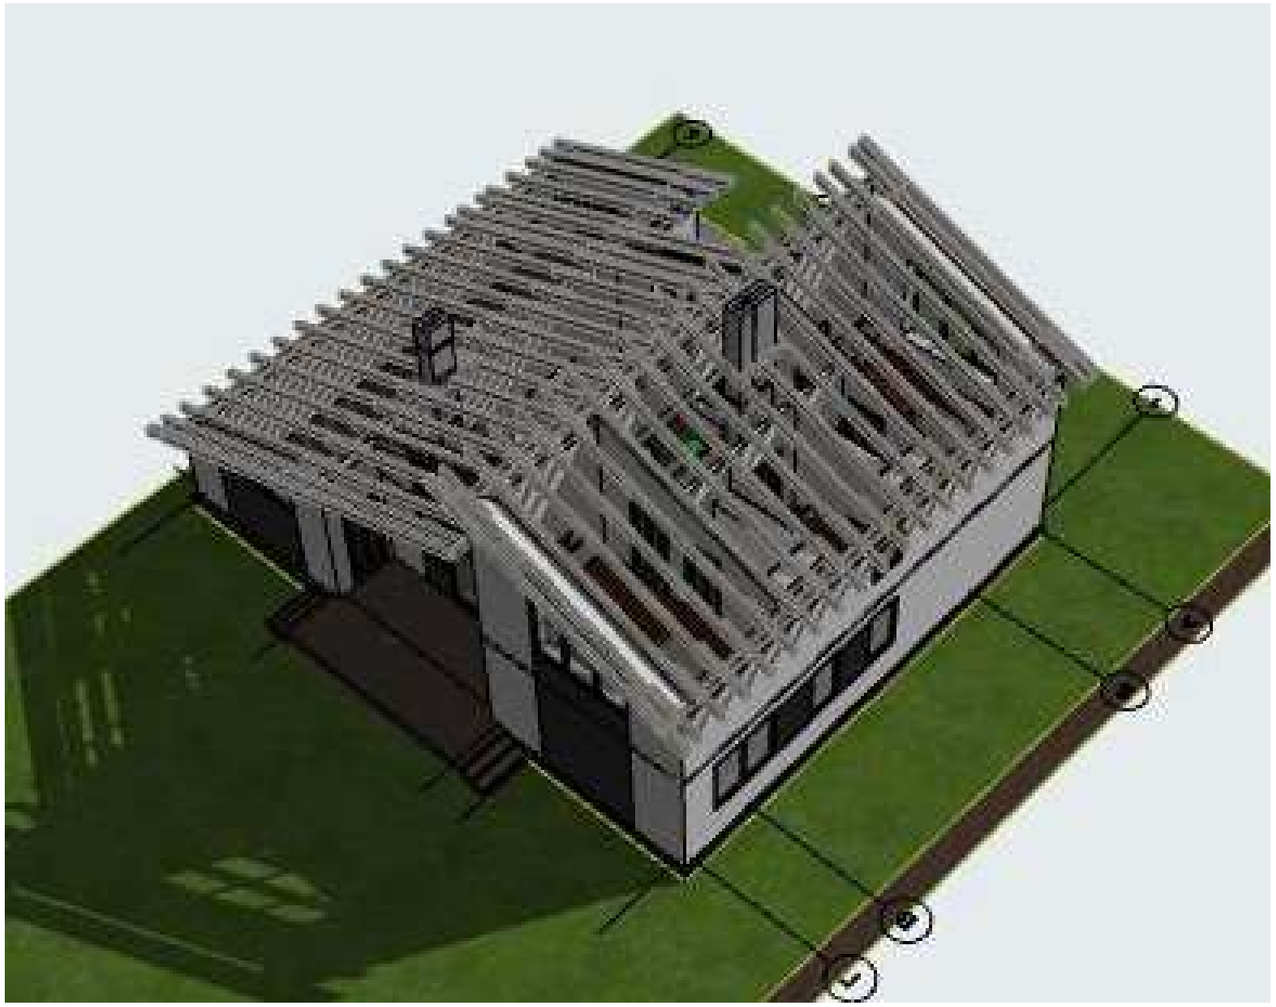


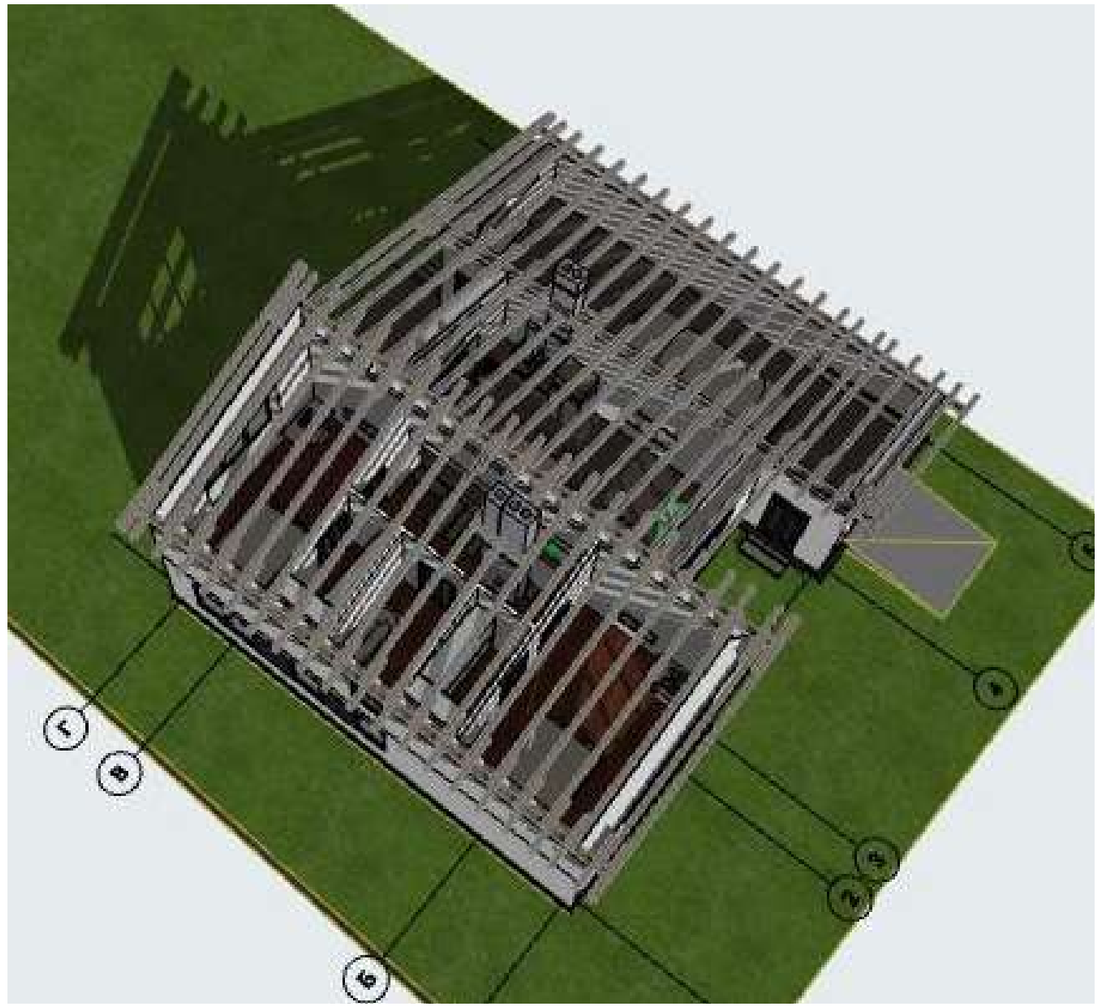


Изм.	Кол.уч.	Лист	№Док.	Подп.	Дата	
Разраб.		Салыкова Е.				

кадастровый номер 63:03:0211031:617, Самарская область, г. Кинель, ул. Уральская, 72а Россия


Индивидуальный жилой дом	Стадия	Лист	Листов
	ЭП	22	
3Д вид стропильной системы			

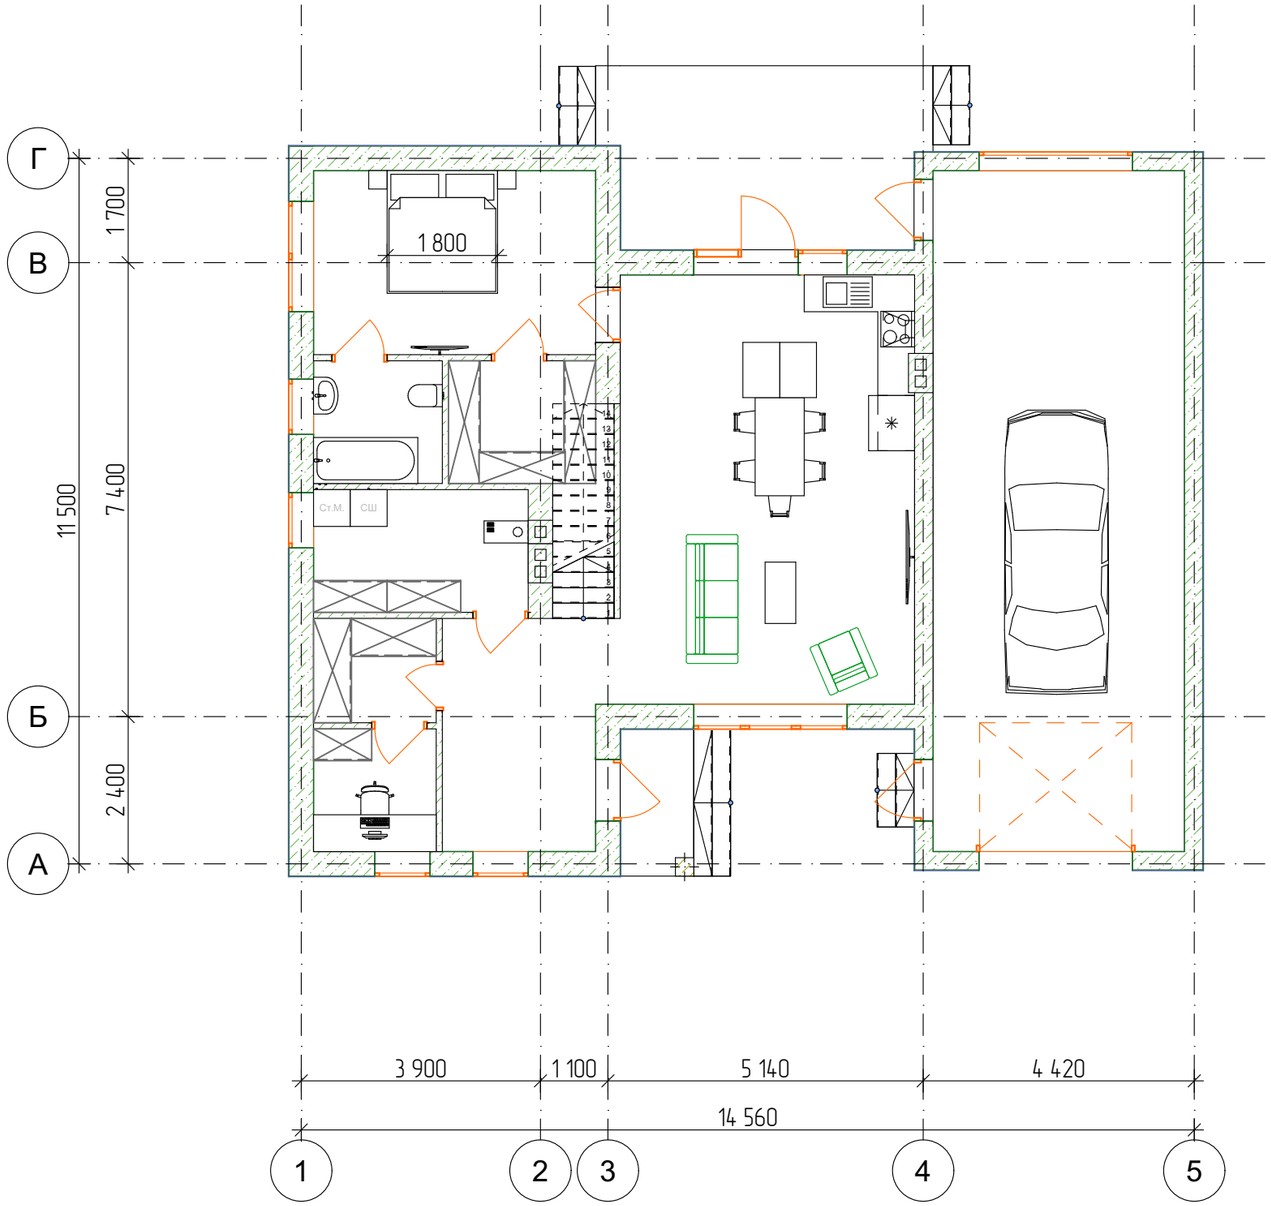

Изм.	Кол.уч.	Лист	№Док.	Подп.	Дата	кадастровый номер 63:03:0211031:617, Самарская область, г. Кинель, ул. Уральская, 72а Россия			
Разраб.		Салыкова Е.				Индивидуальный жилой дом	Стадия	Лист	Листов
							ЭП	23	
						План расстановки мебели 1 этаж			

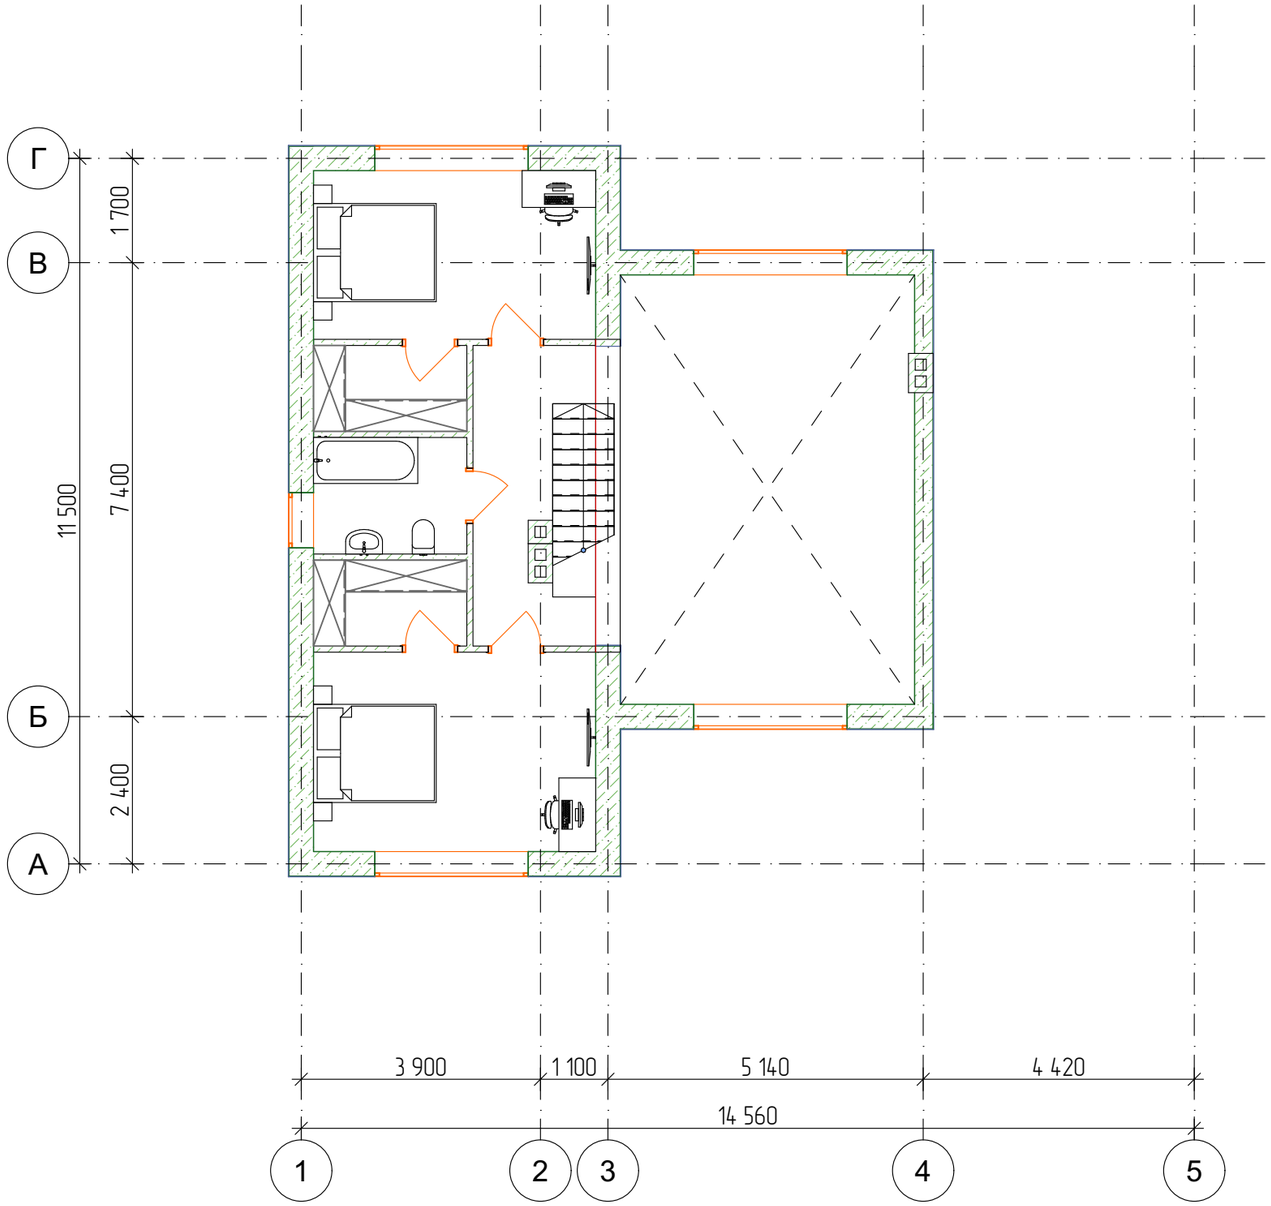


Изм.	Кол.уч.	Лист	№Док.	Подп.	Дата	кадастровый номер 63:03:0211031:617, Самарская область, г. Кинель, ул. Уральская, 72а Россия			
Разраб.		Салыкова Е.				Индивидуальный жилой дом	Стадия	Лист	Листов
							ЭП	24	
						План расстановки мебели 2 этаж			

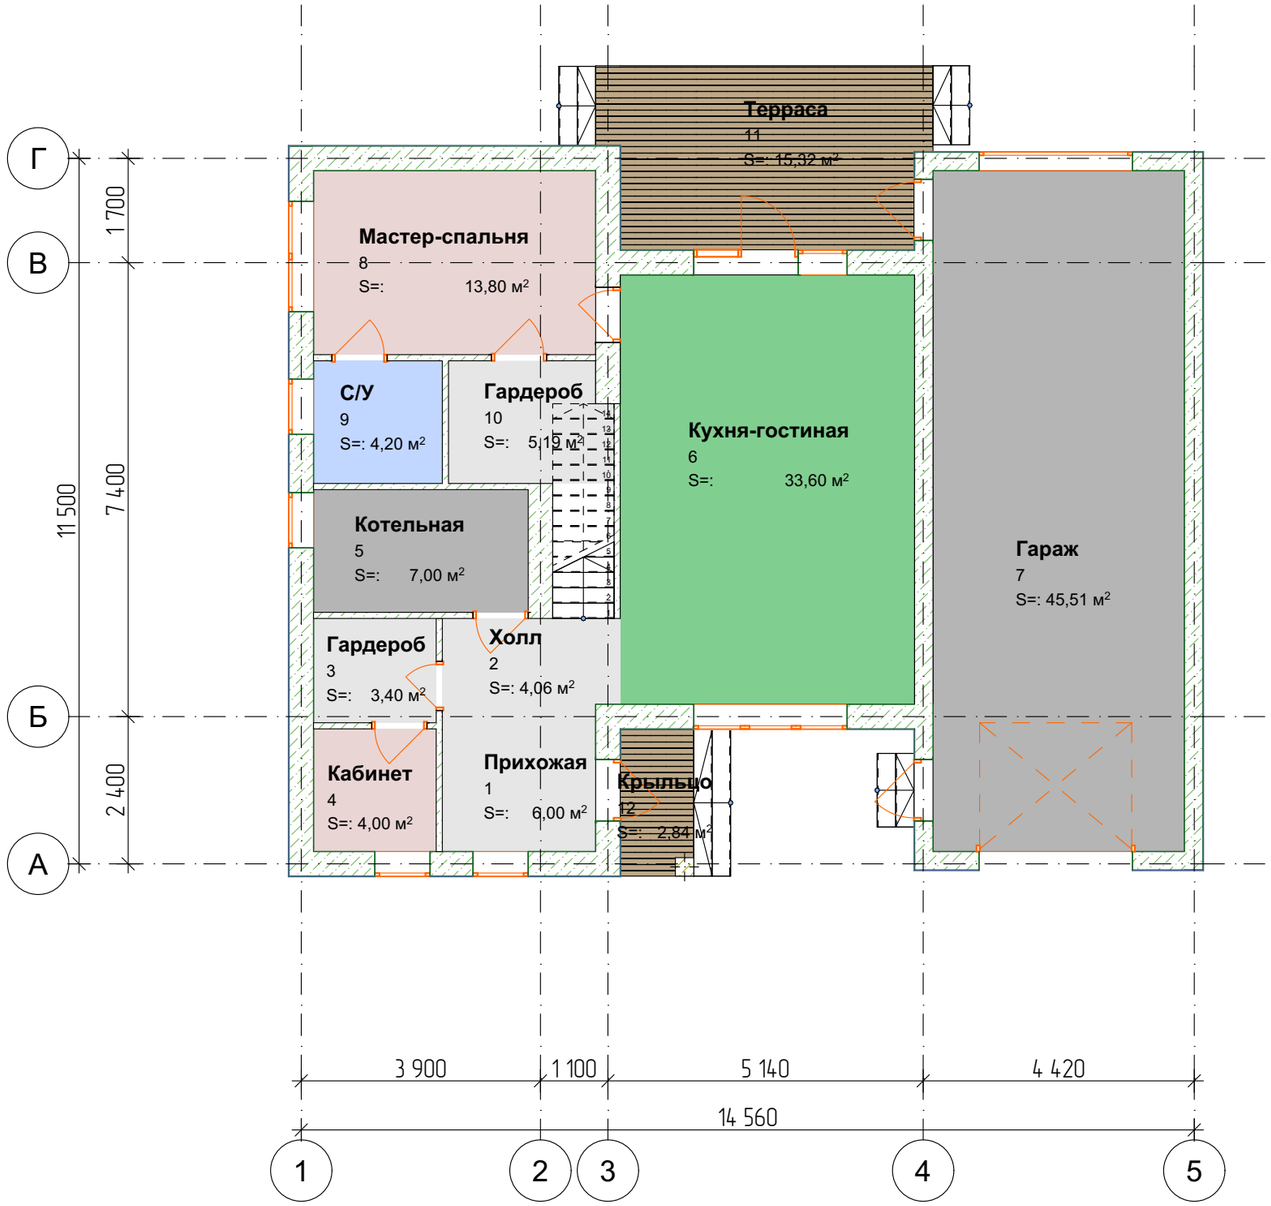

№	Наименование	Площадь
1	Прихожая	6,00
2	Холл	4,06
3	Гардероб	3,40
4	Кабинет	4,00
5	Котельная	7,00
6	Кухня-гостиная	33,60
7	Гараж	45,51
8	Мастер-спальня	13,80
9	С/У	4,20
10	Гардероб	5,19
11	Терраса	15,32
12	Крыльцо	2,84
		144,92 м²

Изм.	Кол.уч.	Лист	№Док.	Подп.	Дата	
						кадастровый номер 63:03:0211031:617, Самарская область, г. Кинель, ул. Уральская, 72а Россия
Разраб.		Салыкова Е.				Индивидуальный жилой дом
						Экспликация помещений 1- го этажа

Стадия	Лист	Листов
ЭП	25	

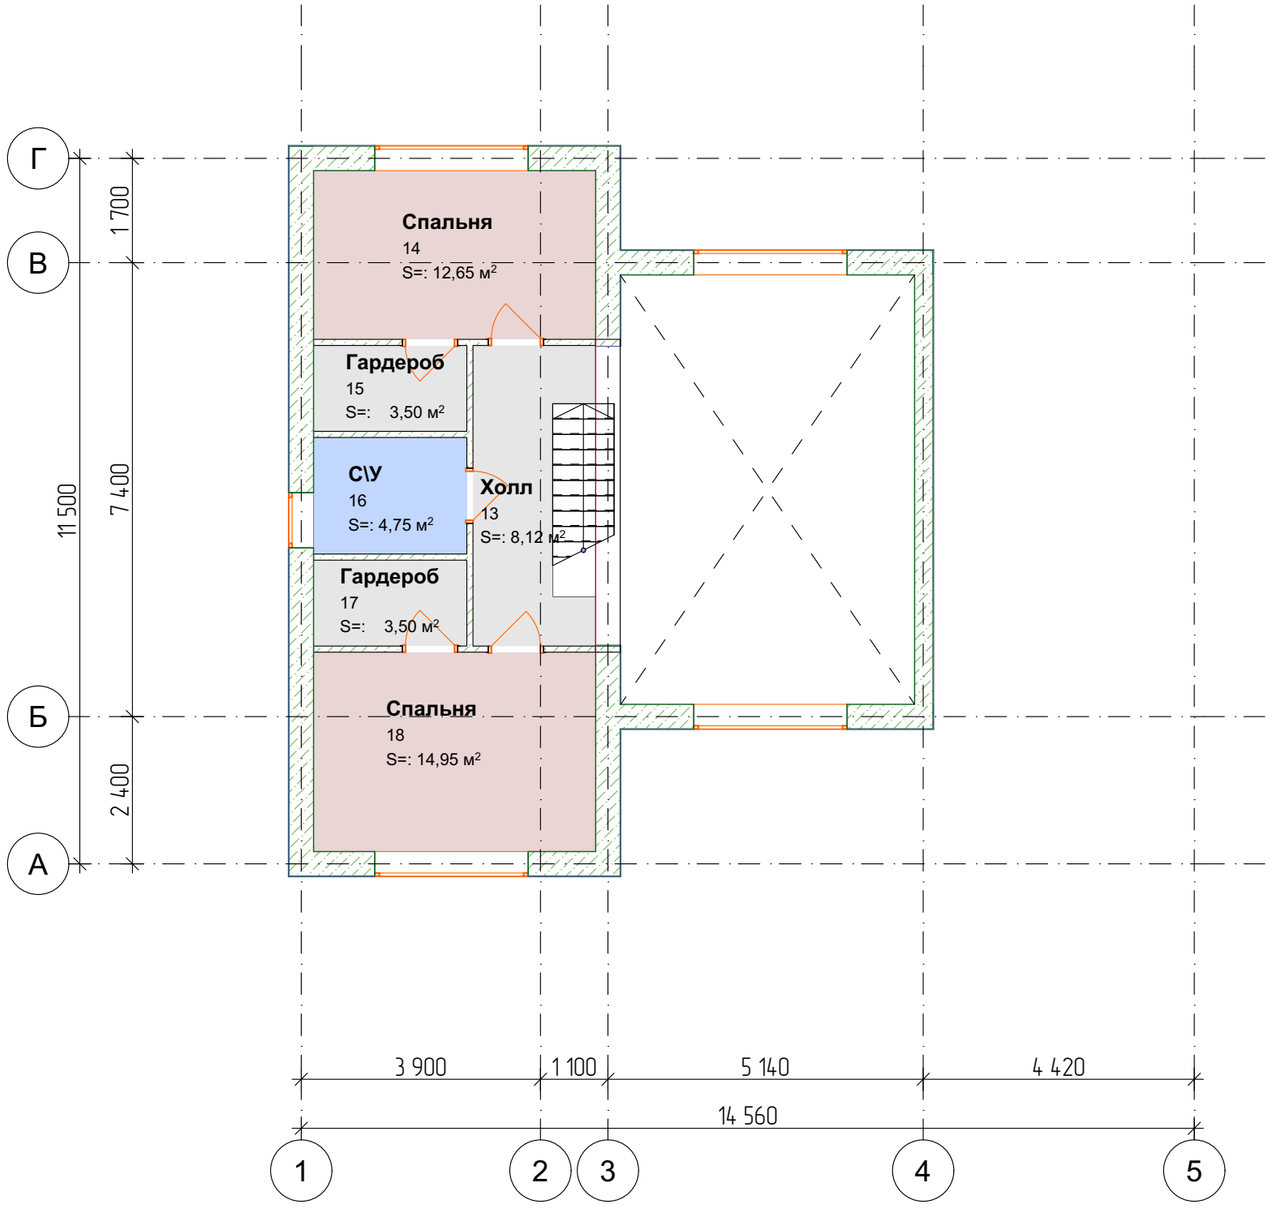

№	Наименование	Площадь
13	Холл	8,12
14	Спальня	12,65
15	Гардероб	3,50
16	С\У	4,75
17	Гардероб	3,50
18	Спальня	14,95
		47,47 м²

Изм.	Кол.уч.	Лист	№Док.	Подп.	Дата	
						кадастровый номер 63:03:0211031:617, Самарская область, г. Кинель, ул. Уральская, 72а Россия
Разраб.		Салыкова Е.				Индивидуальный жилой дом
						Экспликация помещений 2- го этажа

Стадия	Лист	Листов
ЭП	26	






Изм.	Кол.уч.	Лист	№Док.	Подп.	Дата	
Разраб.		Салыкова Е.				

кадастровый номер 63:03:0211031:617, Самарская область, г. Кинель, ул. Уральская, 72а Россия			
Индивидуальный жилой дом	Стадия	Лист	Листов
	ЭП	27	
3Д разрезы			




						кадастровый номер 63:03:0211031:617, Самарская область, г. Кинель, ул. Уральская, 72а Россия
Изм.	Колуч.	Лист	№Док.	Подп.	Дата	
Разраб.		Салыкова	В.			Индивидуальный жилой дом
						Фасад в осях 1-5

Стадия	Лист	Листов
ЭП	28	

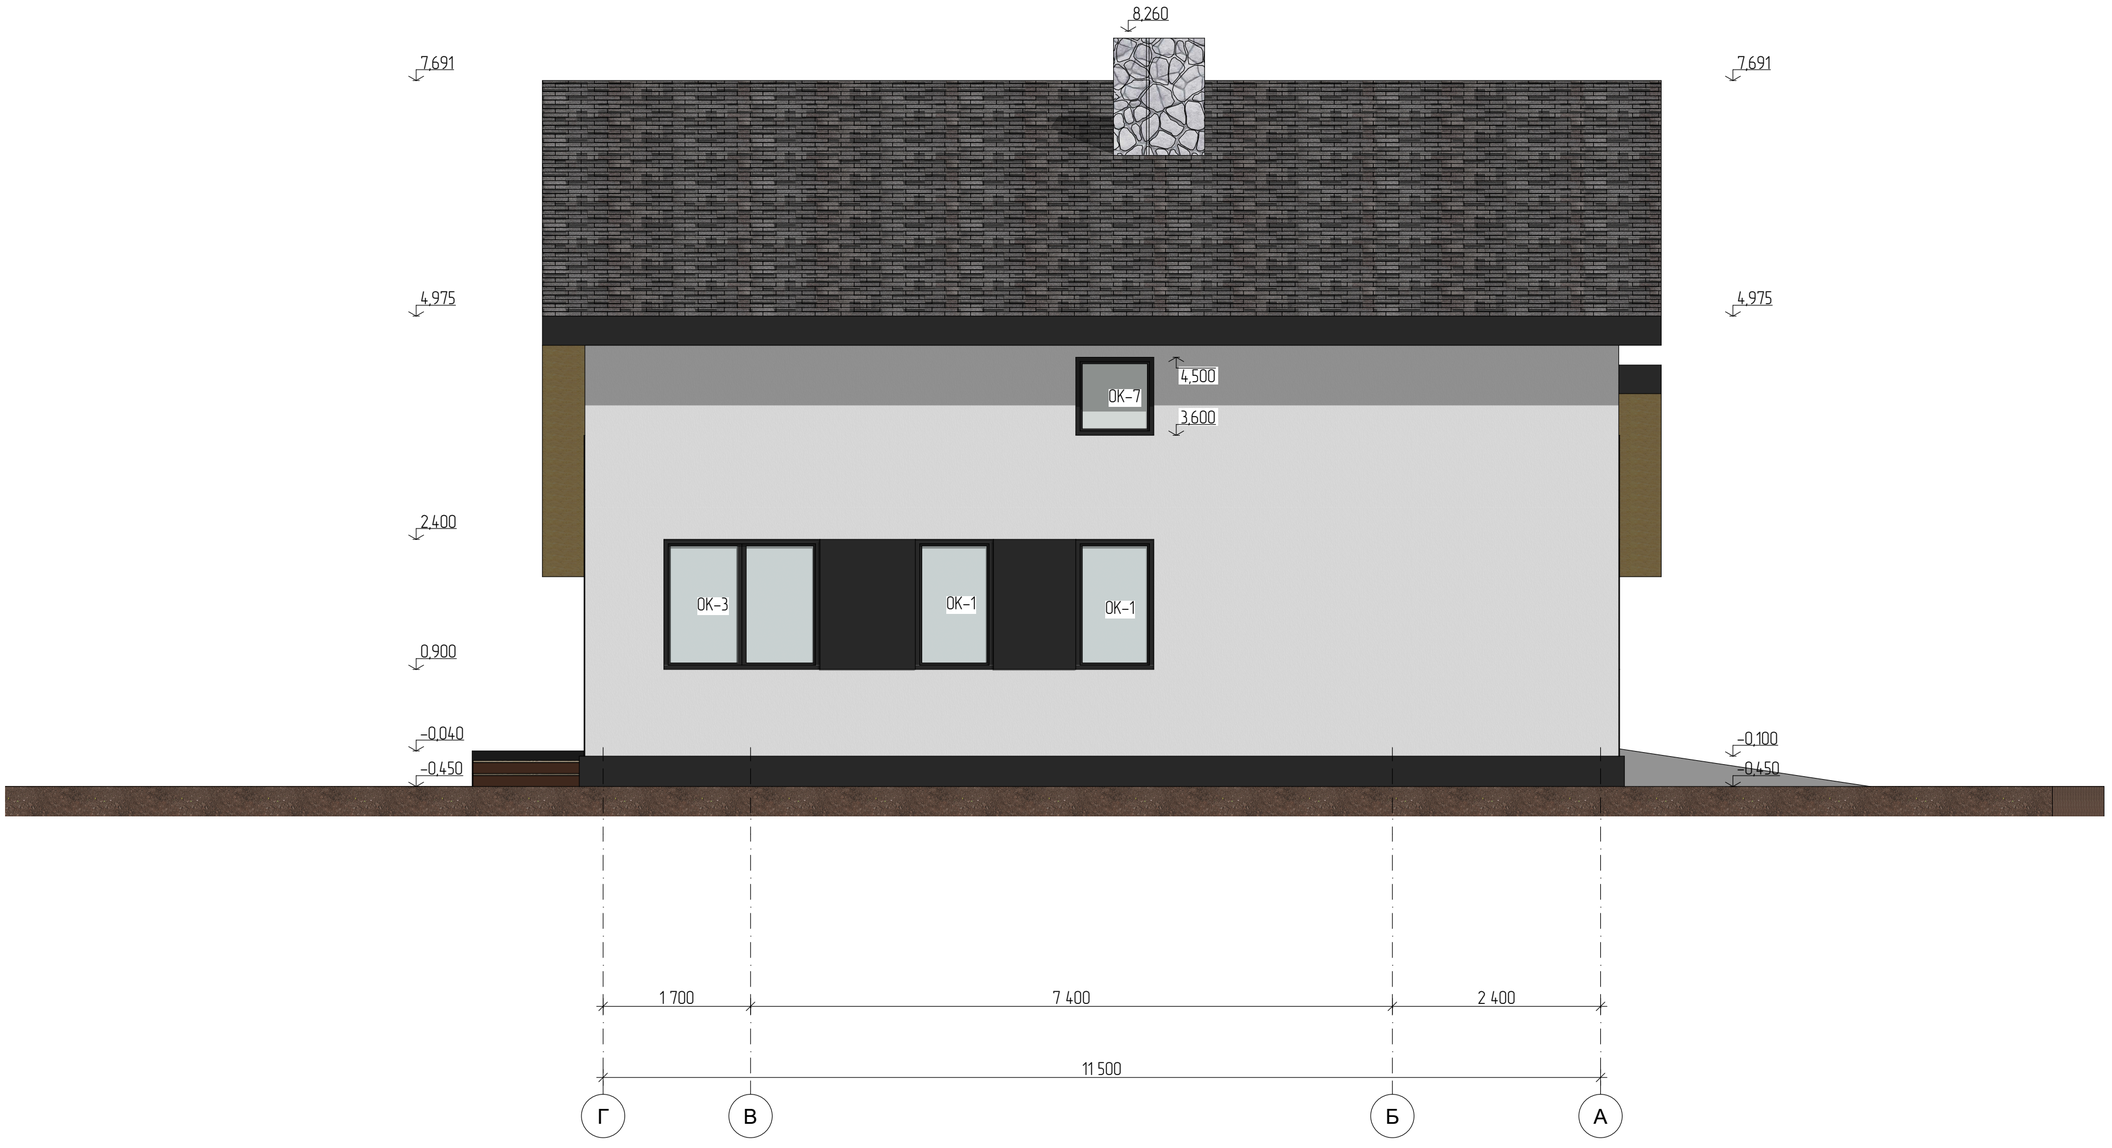

						кадастровый номер 63:03:0211031:617, Самарская область, г. Кинель, ул. Уральская, 72а Россия
Изм.	Кол.уч.	Лист	№Док.	Подп.	Дата	
Разраб.		Салыкова В.				Индивидуальный жилой дом
						Фасад в осях Г-А

Стадия	Лист	Листов
ЭП	29	

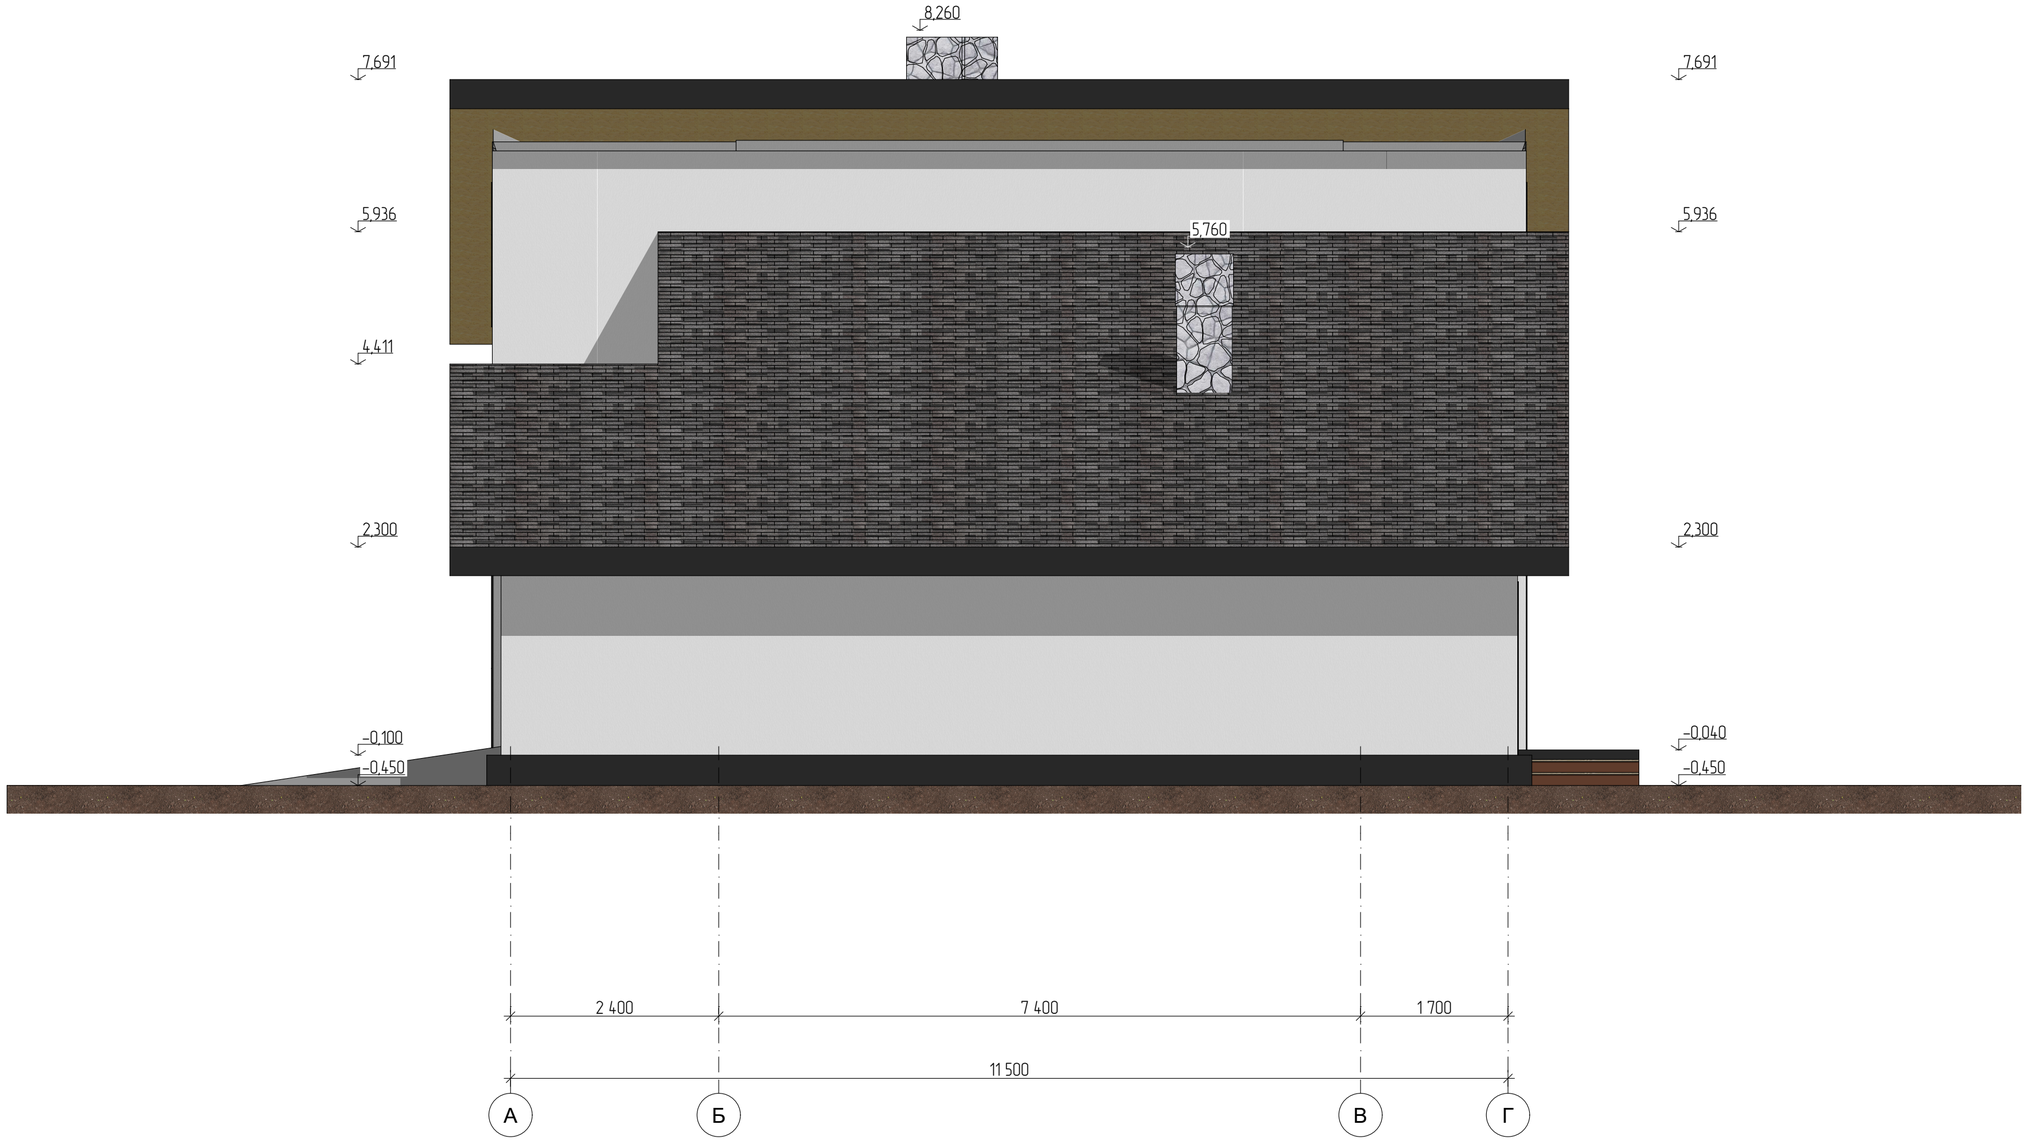

						кадастровый номер 63:03:0211031:617, Самарская область, г. Кинель, ул. Уральская, 72а Россия
Изм.	Кол.уч.	Лист	№Док.	Подп.	Дата	
Разраб.		Салыкова	В.			Индивидуальный жилой дом
						Фасад в осях А-Г

Стадия	Лист	Листов
ЭП	30	



						кадастровый номер 63:03:0211031:617, Самарская область, г. Кинель, ул. Уральская, 72а Россия
Изм.	Кол.уч.	Лист	№Док.	Подп.	Дата	
Разраб.		Салыкова	В.			Индивидуальный жилой дом
						Фасад в осях 5-1

Стадия	Лист	Листов
ЭП	31	