ПРОЕКТНАЯ ДОКУМЕНТАЦИЯ

Индивидуальный жилой дом

кадастровый номер 63:17:0301011:962, Самарская область, муниципальный район Волжский, городское поселение Смышляевка, поселок городского типа Стройкерамика, улица Александровская роща, земельный участок 104 Россия



2025

Ведомость листов	
Наименование	Лист
Обложка	
Общие данные	02
Сводная ведомость материалов	03
Схема организации участка	04
3D Виды	05
План фундамента	06
План плиты	07
План плиты (закладные)	08
План плиты (коммуникации)	09
3Д вид фундамента	10
Схема нижнего армирования плиты	11
Схема верхнего армирования плиты	12
Схема арматурного каркаса плиты	13
Узлы фундамента	14
Схема армирования фундамента	15
План 1 этажа	16
Маркировочный план 1 этаж	17
Каталог проемов	18
Схема расположения перемычек	19
Разрез 1 - 1	20
Разрез 2 - 2	21
Разрез по стене	22
Развертка вентканала	23
План перекрытия +2,900	24
Схема нижнего армирования плиты	25
Схема верхнего армирования плиты	26
Схема арматурного каркаса плиты	27
План кровли	28
План расстановки мебели 1 этаж	29
Экспликация помещений 1- го этажа	30
3Д разрез	31
Фасад в осях 1-6	32
Фасад в осях Б-А	33
Фасад в осях А-Б	34
Фасад в осях 6-1	35

Изм.	Кол.уч.	Лист	№Док.	Подп.	Дата

кадастровый номер 63:17:0301011:962, Самарская область, муниципальный район Волжский, городское поселение Смышляевка, поселок городского типа Стройкерамика, улица Александровская роща, земельный участок 104 Россия

Индивидуальный жилой дом	Стадия	Лист	Листов
	ЭП	02	
Общие данные			

ВЕДОМОСТЬ ПЕРЕКРЫТИЯ	
Наименование	Объем, м3
Монолитная плита	29,29

ИКК-03 Ведомость перекрытий 1	
Наименование	Объем, м3
Монолитная плита	29,30

ИКК-03 Ведомость перекрытий 1	
Наименование	Объем, м3
Монолитная плита	29,30

ВЕДОМОСТЬ НА МОНОЛИТНЫЕ ПЕРЕМЫЧКИ	
Наименование	Объем, м3
	0,99
Монолитная перемычка	0,99

ВЕДОМОСТЬ НА КОЛОННЫ, РИГЕЛИ	
Наименование	Объем, м3
ЖБ колонна 400х400	1,68
ЖБ ригель 400х400	4,62

ИКК-03 Кровля	
Наименование	Площадь, м2
Кровля	124,76

ВЕДОМОСТЬ БЛОКА ДЛЯ СТЕН	
ID Элемента	Объем, м3
Несущие 400мм	73,28
Перегородки 100мм	4,86

ВЕДОМОСТЬ БЕТОНА	
Наименование	Объем, м3
Лента фундамента	61,68

ВЕДОМОСТЬ НА УТЕПЛИТЕЛЬ ДЛЯ СТЕН, ПОЛА ПЕРВОГО ЭТАЖА, РОСТВЕРКА			
Наименование	**Компоненты**		
	Толщина [мм]	**Объем [м3]**	**Площадь [м2]**
Изоляция - Минеральная Жесткая			
	50	7,59	151,94
Изоляция - ЭППС			
	50	5,75	115,04
	150	10,71	71,40
Экструзионный пенополистирол ТЕХНОНИКОЛЬ CARBON PROF (СТО 72746455-3.3.1-2012) (1)			
	100	12,48	124,76
Экструзионный пенополистирол ТЕХНОНИКОЛЬ CARBON PROF SLOPE (СТО 72746455-3.3.1-2012) (1)			
	50	6,24	124,76


Консструкция пола			
Наименование	**Компоненты**		
	Толщина [мм]	**Объем [м3]**	**Площадь [м2]**
Стяжка ЦПР			
	50	2,46	49,14
	80	5,97	74,67


Отделочные материалы		
Наименование	**Компоненты**	
	Толщина [м]	**Площадь [м2]**
Клинкерная плитка (фасадная)		
	20	153,82
Планкен		
	20	57,32


Изм.	Кол.уч.	Лист	№Док.	Подп.	Дата

кадастровый номер 63:17:0301011:962, Самарская область, муниципальный район Волжский, городское поселение Смышляевка, поселок городского типа Стройкерамика, улица Александровская роща, земельный участок 104 Россия

Индивидуальный жилой дом	Стадия	Лист	Листов
	ЭП	03	
Сводная ведомость материалов			

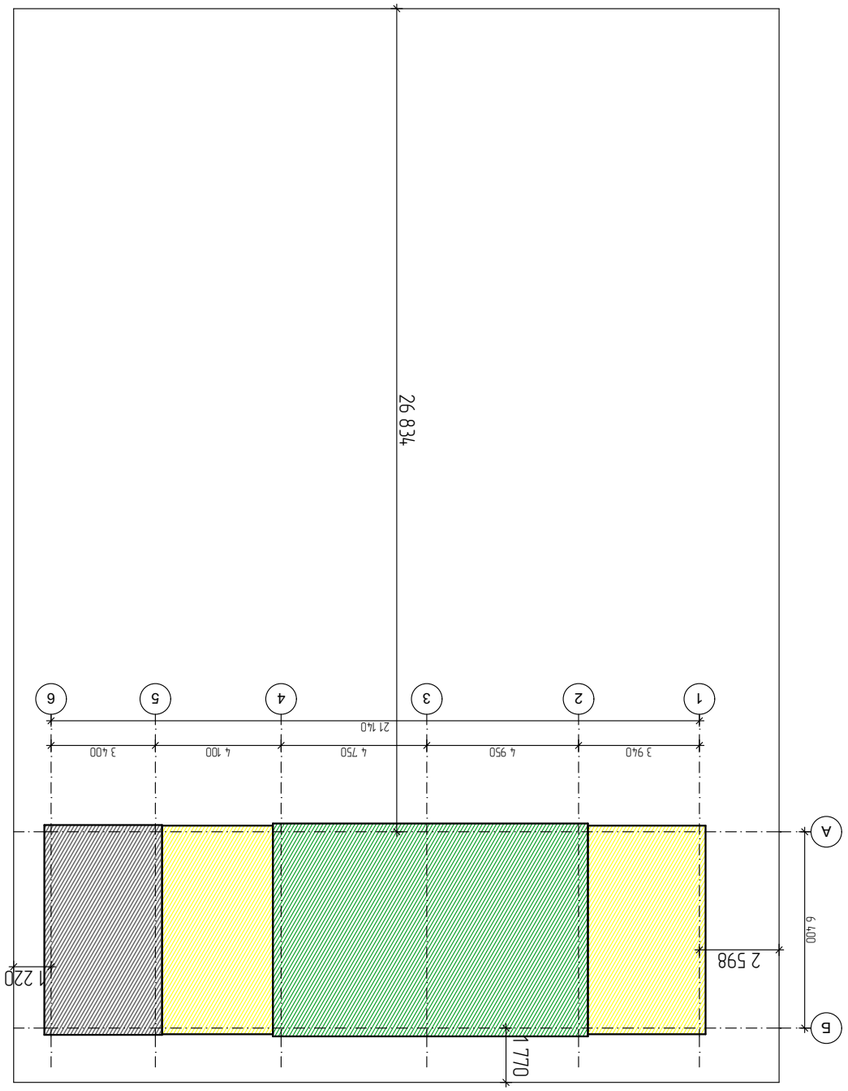

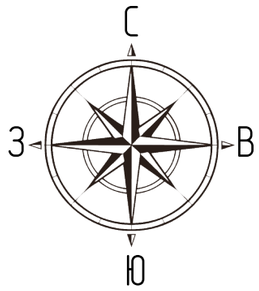

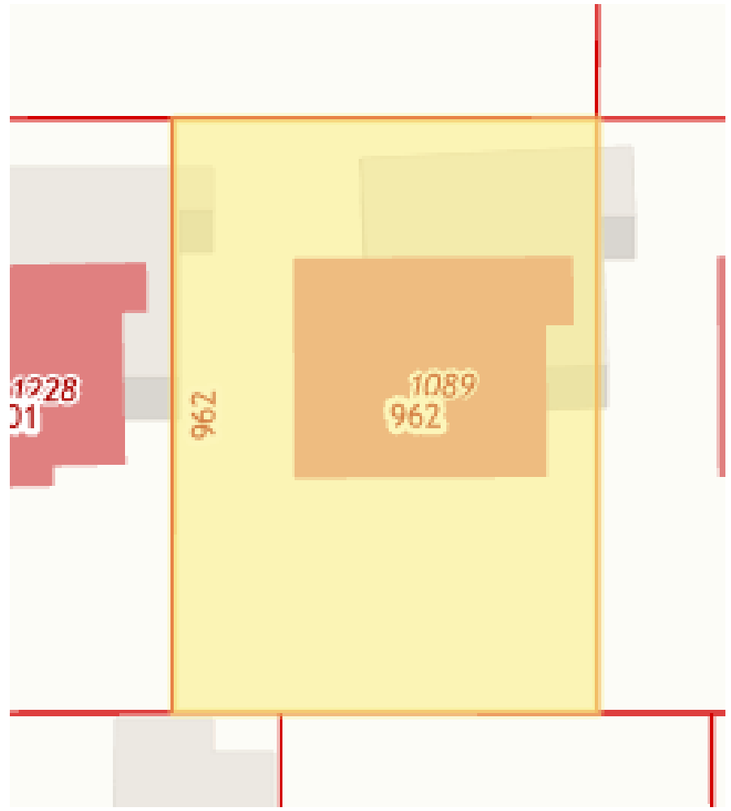

Проектируемый дом

Крыльцо, терраса

Гараж

						кадастровый номер 63:17:0301011:962, Самарская область, муниципальный район Волжский, городское поселение Смышляевка, поселок городского типа Стройкерамика, улица Александровская роща, земельный участок 104 Россия
Изм.	Кол.уч.	Лист	№Док.	Подп.	Дата	
						Индивидуальный жилой дом
						Схема организации участка

Стадия	Лист	Листов
ЭП	04	








Изм.	Кол.уч.	Лист	№Док.	Подп.	Дата	

кадастровый номер 63:17:0301011:962, Самарская область, муниципальный район Волжский, городское поселение Смышляевка, поселок городского типа Стройкерамика, улица Александровская роща, земельный участок 104 Россия

Индивидуальный жилой дом	Стадия	Лист	Листов
	ЭП	05	
3D Виды			

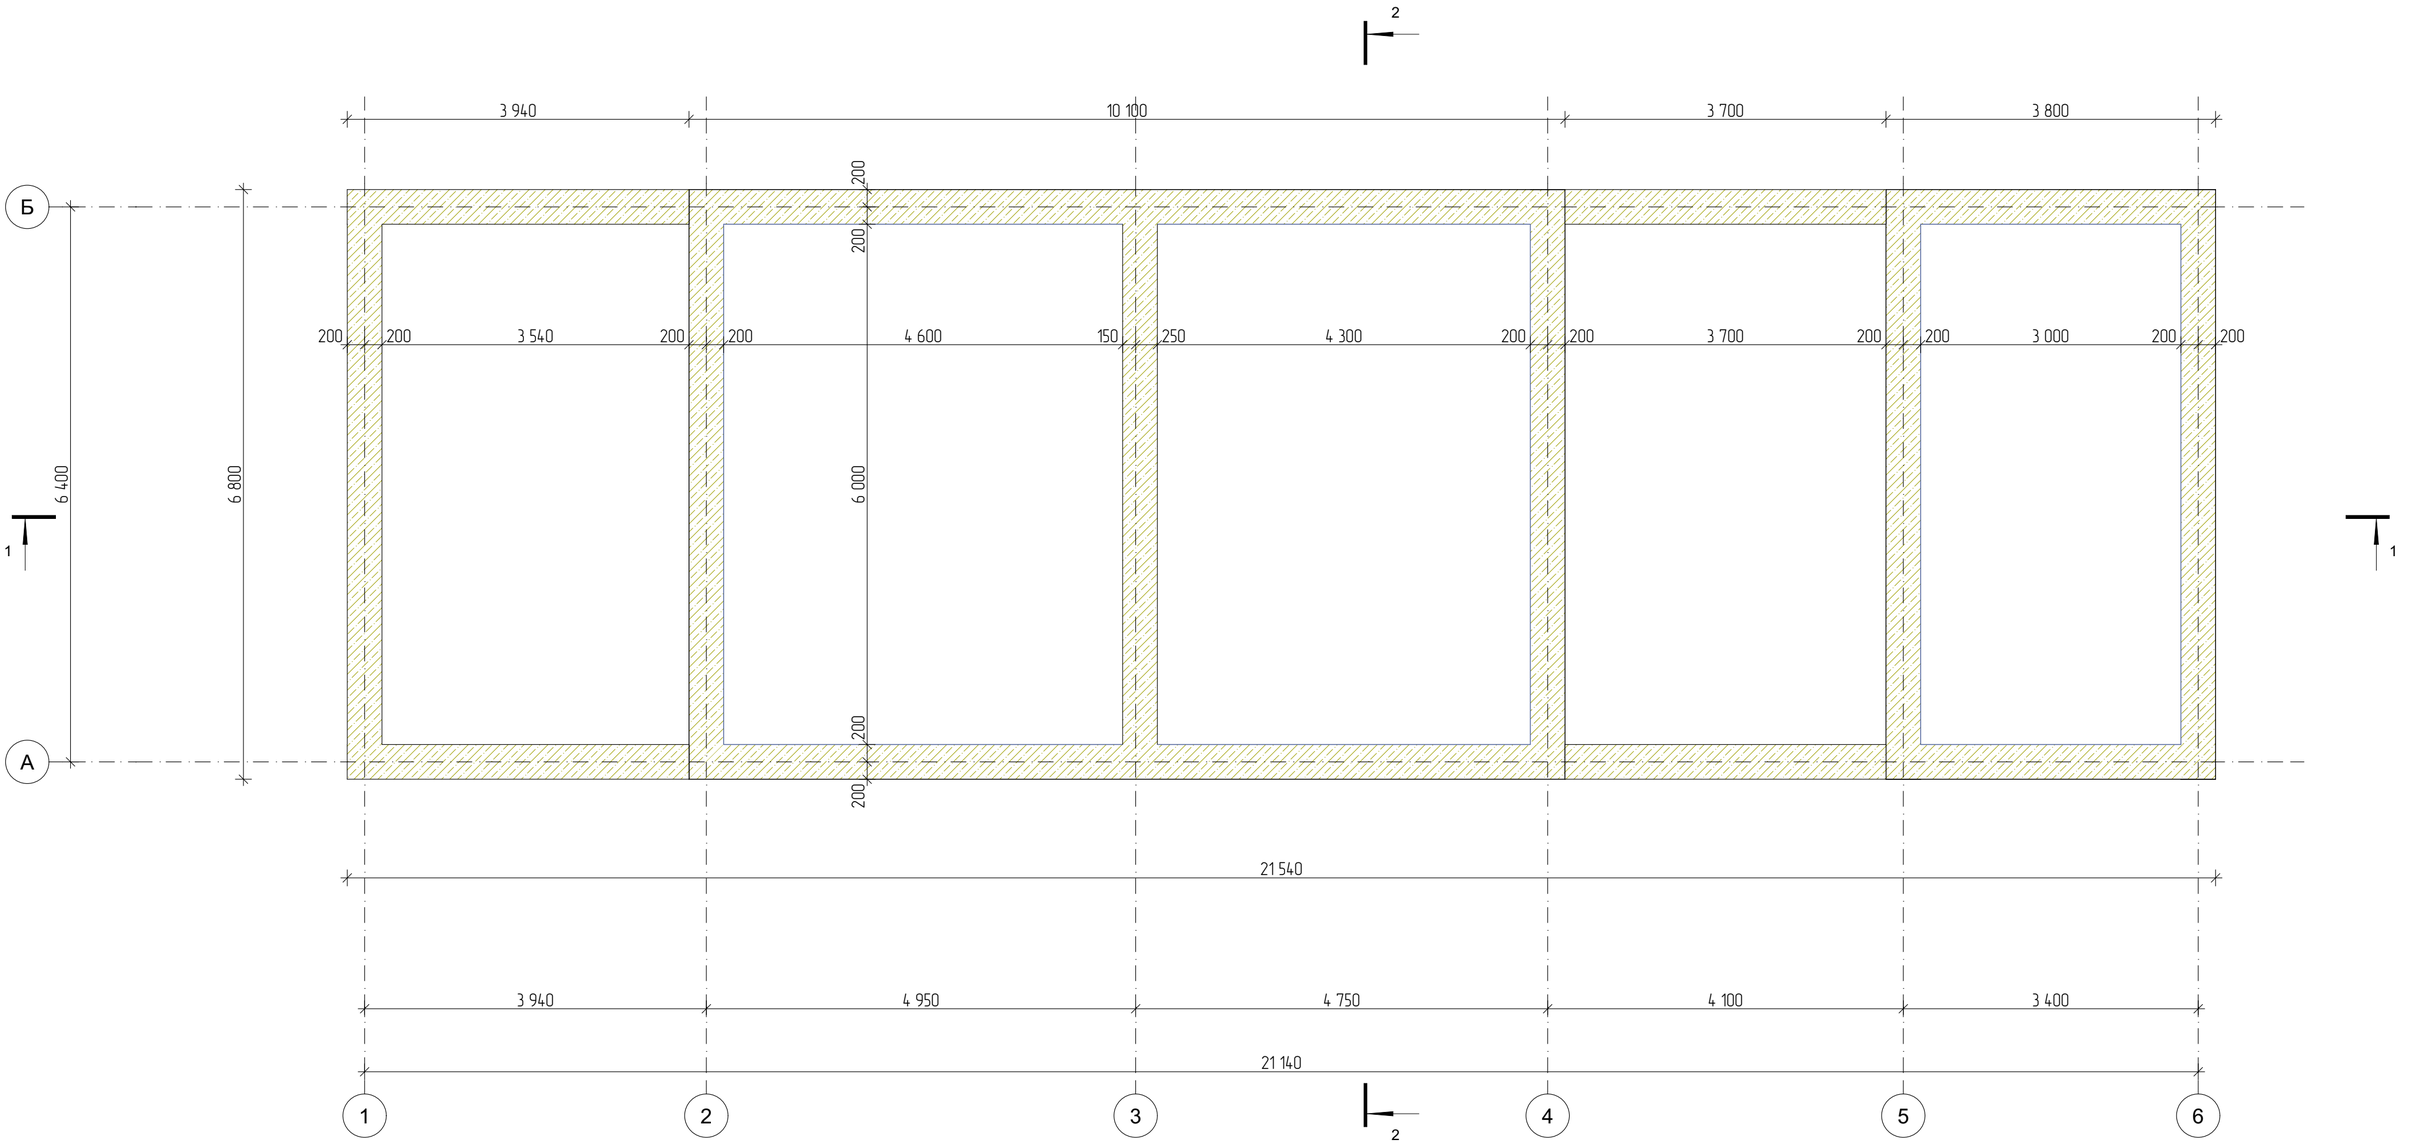


1. Стены фундаменты выполнить из бетона класса В25
2. Все подземные бетонные конструкции огрунтовать битумной мастикой за два раза.

ВЕДОМОСТЬ БЕТОНА

Наименование	Объем, м3
Лента фундамента	61,68

Изм.	Колуч.	Лист	№Док.	Подп.	Дата	кадастровый номер 63:17:0301011:962, Самарская область, муниципальный район Волжский, городское поселение Смышляевка, поселок городского типа Стройкерамика, улица Александровская роща, земельный участок 104 Россия			
						Индивидуальный жилой дом	Стадия	Лист	Листов
							ЭП	06	
						План фундамента			

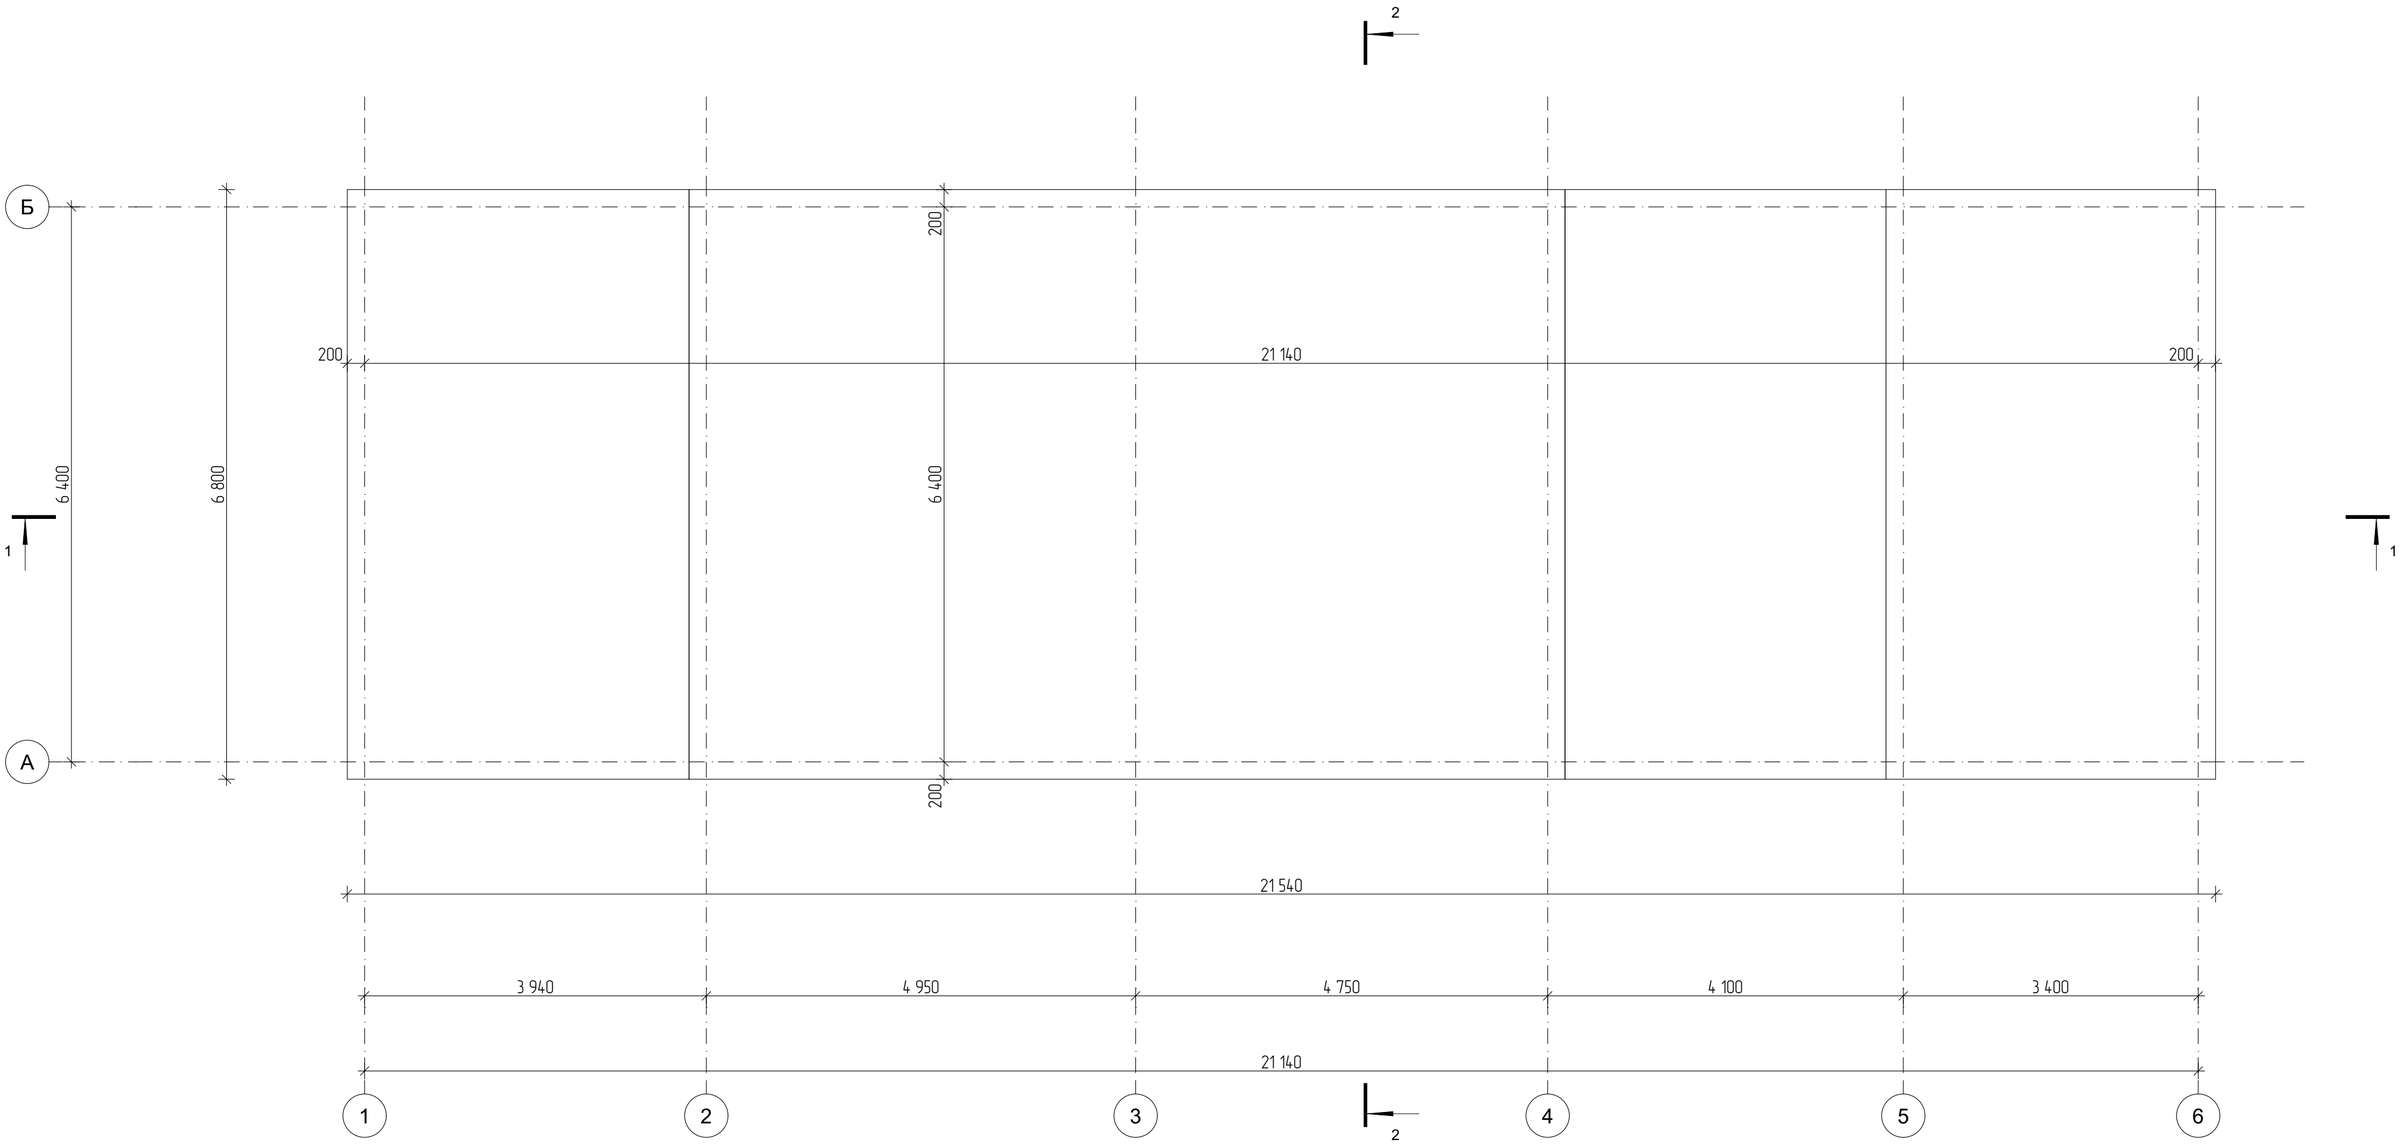


ИКК-03 Ведомость перекрытий 1

Наименование	Объем, м3
Монолитная плита	29,30


Изм.	Кол.уч.	Лист	№Док.	Подп.	Дата

кадастровый номер 63:17:0301011:962, Самарская область, муниципальный район Волжский, городское поселение Смышляевка, поселок городского типа Стройкерамика, улица Александровская роща, земельный участок 104 Россия

Индивидуальный жилой дом	Стадия	Лист	Листов
	ЭП	07	
План плиты			

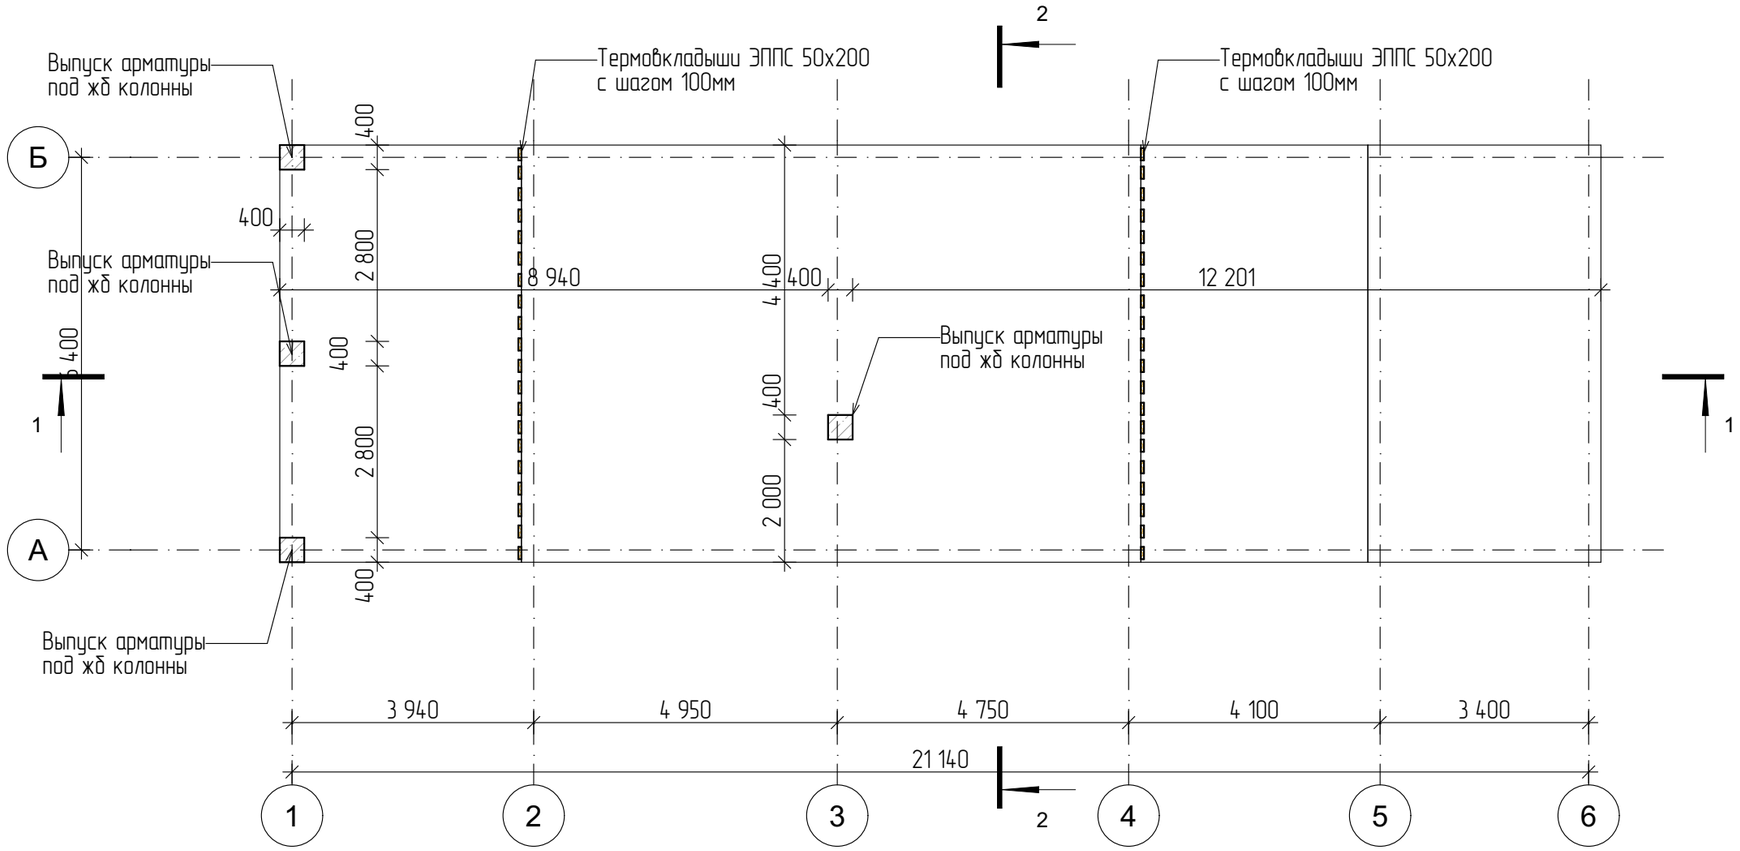



Изм.	Кол.уч.	Лист	№Док.	Подп.	Дата	кадастровый номер 63:17:0301011:962, Самарская область, муниципальный район Волжский, городское поселение Смышляевка, поселок городского типа Стройкерамика, улица Александровская роща, земельный участок 104 Россия			
						Индивидуальный жилой дом	Стадия	Лист	Листов
							ЭП	08	
						План плиты (закладные)			

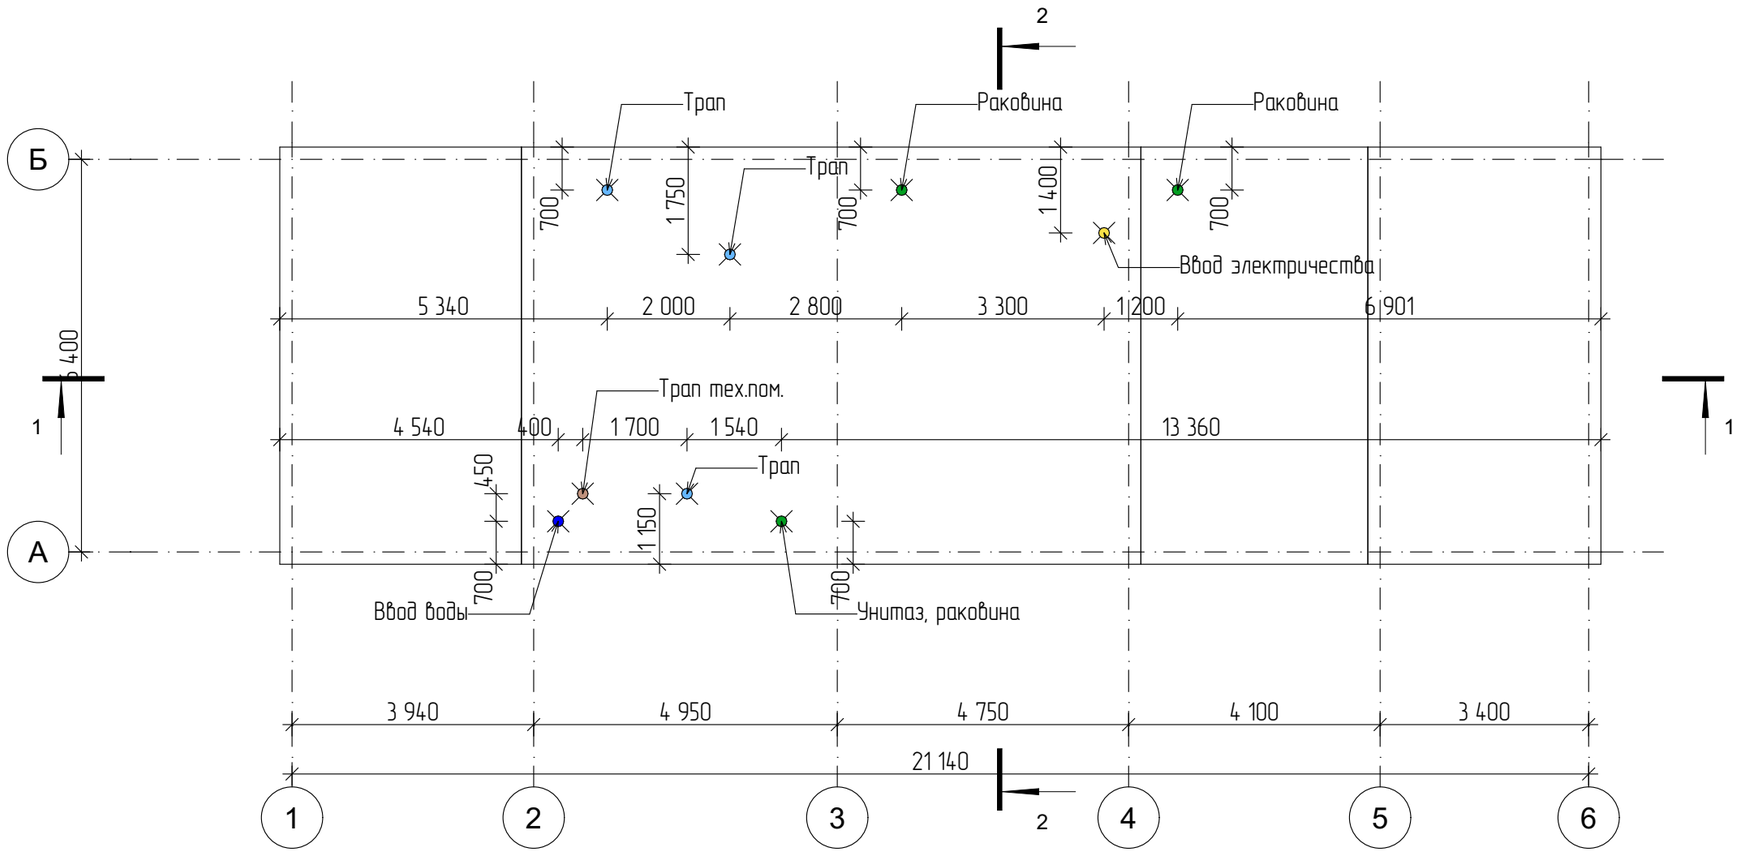


						кадастровый номер 63:17:0301011:962, Самарская область, муниципальный район Волжский, городское поселение Смышляевка, поселок городского типа Стройкерамика, улица Александровская роща, земельный участок 104 Россия
Изм.	Кол.уч.	Лист	№Док.	Подп.	Дата	
						Индивидуальный жилой дом
						План плиты (коммуникации)


Стадия	Лист	Листов
ЭП	09	

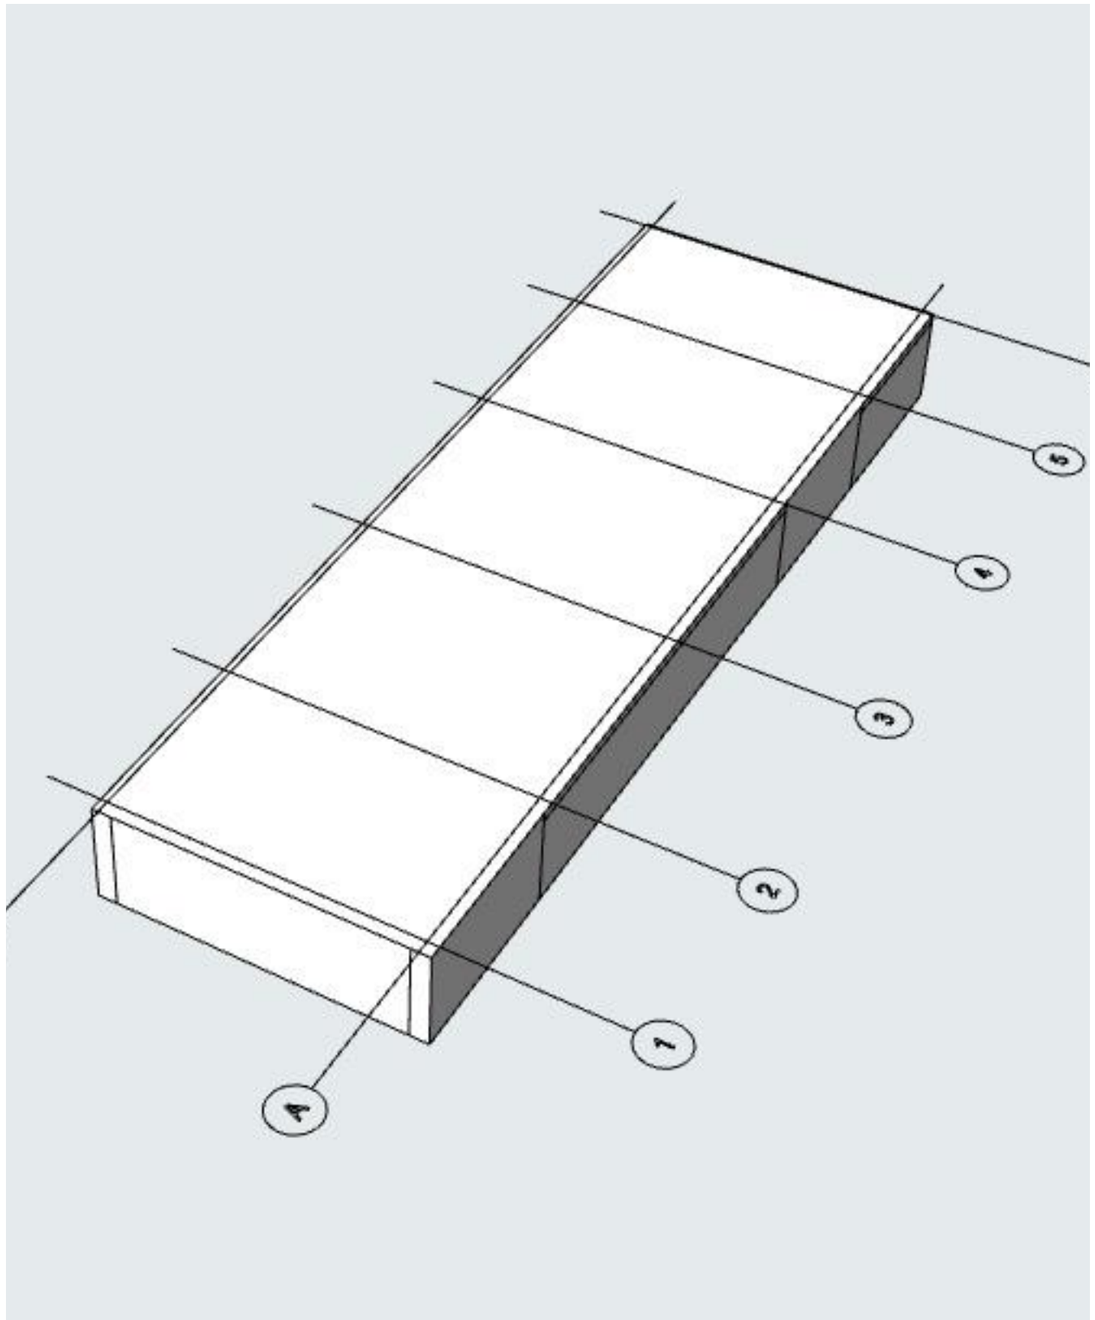

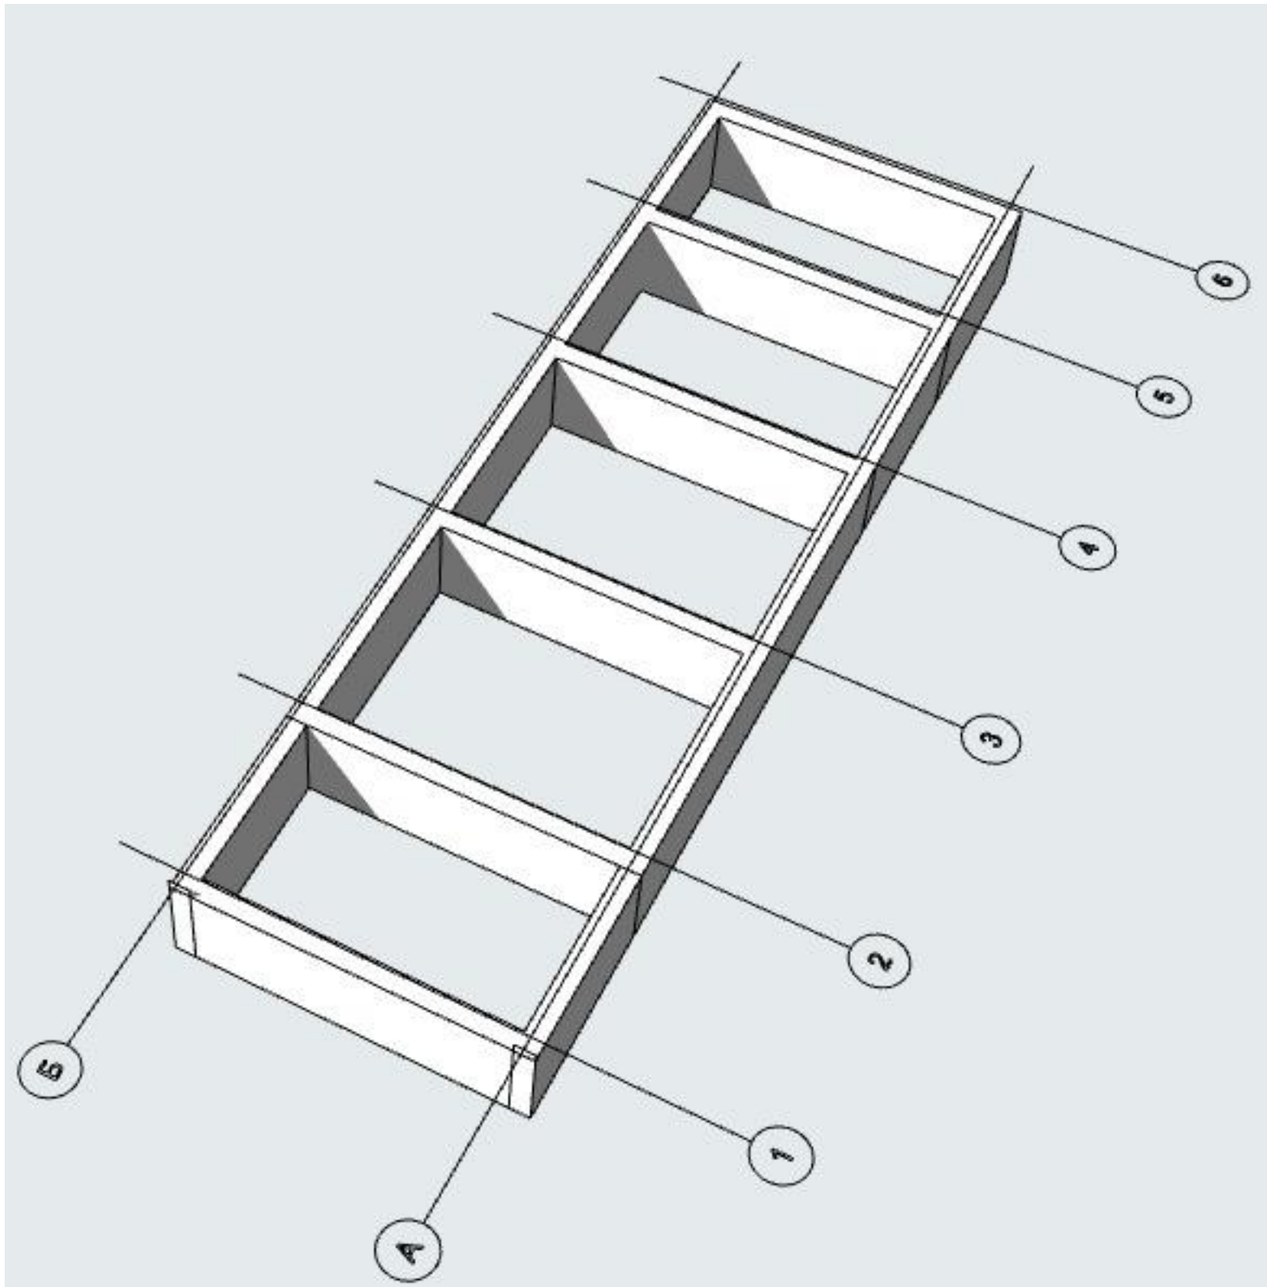


Изм.	Кол.уч.	Лист	№Док.	Подп.	Дата	кадастровый номер 63:17:0301011:962, Самарская область, муниципальный район Волжский, городское поселение Смышляевка, поселок городского типа Стройкерамика, улица Александровская роща, земельный участок 104 Россия			
						Индивидуальный жилой дом	Стадия	Лист	Листов
							ЭП	10	
						3Д вид фундамента			

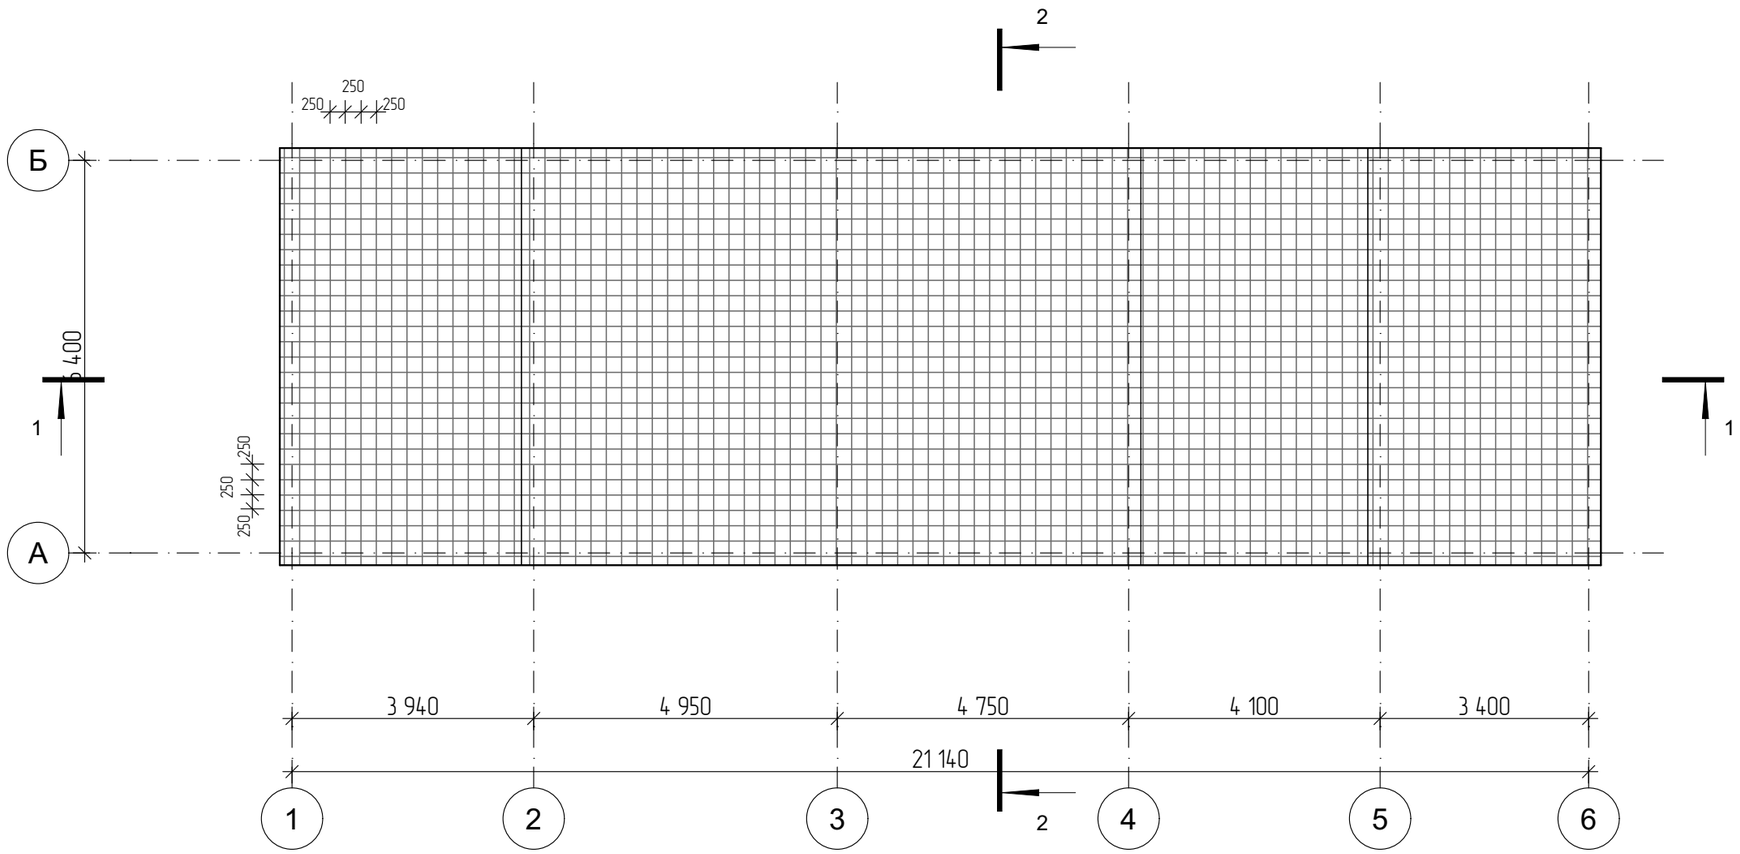


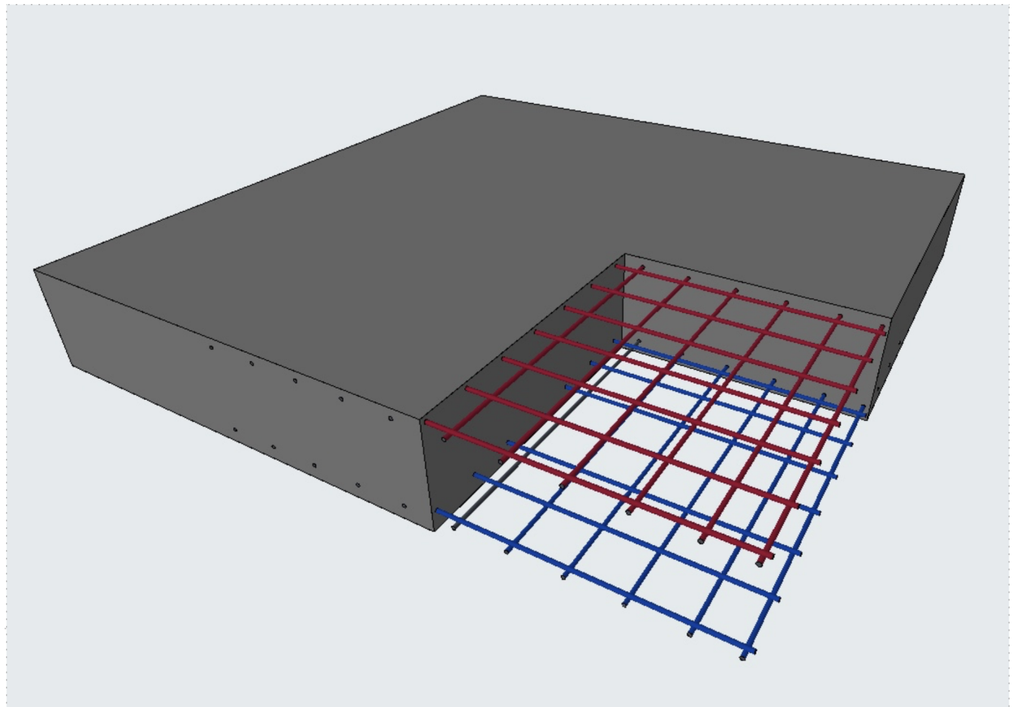

Изм.	Кол.уч.	Лист	№Док.	Подп.	Дата	
						кадастровый номер 63:17:0301011:962, Самарская область, муниципальный район Волжский, городское поселение Смышляевка, поселок городского типа Стройкерамика, улица Александровская роща, земельный участок 104 Россия
						Индивидуальный жилой дом
						Схема нижнего армирования плиты


Стадия	Лист	Листов
ЭП	11	

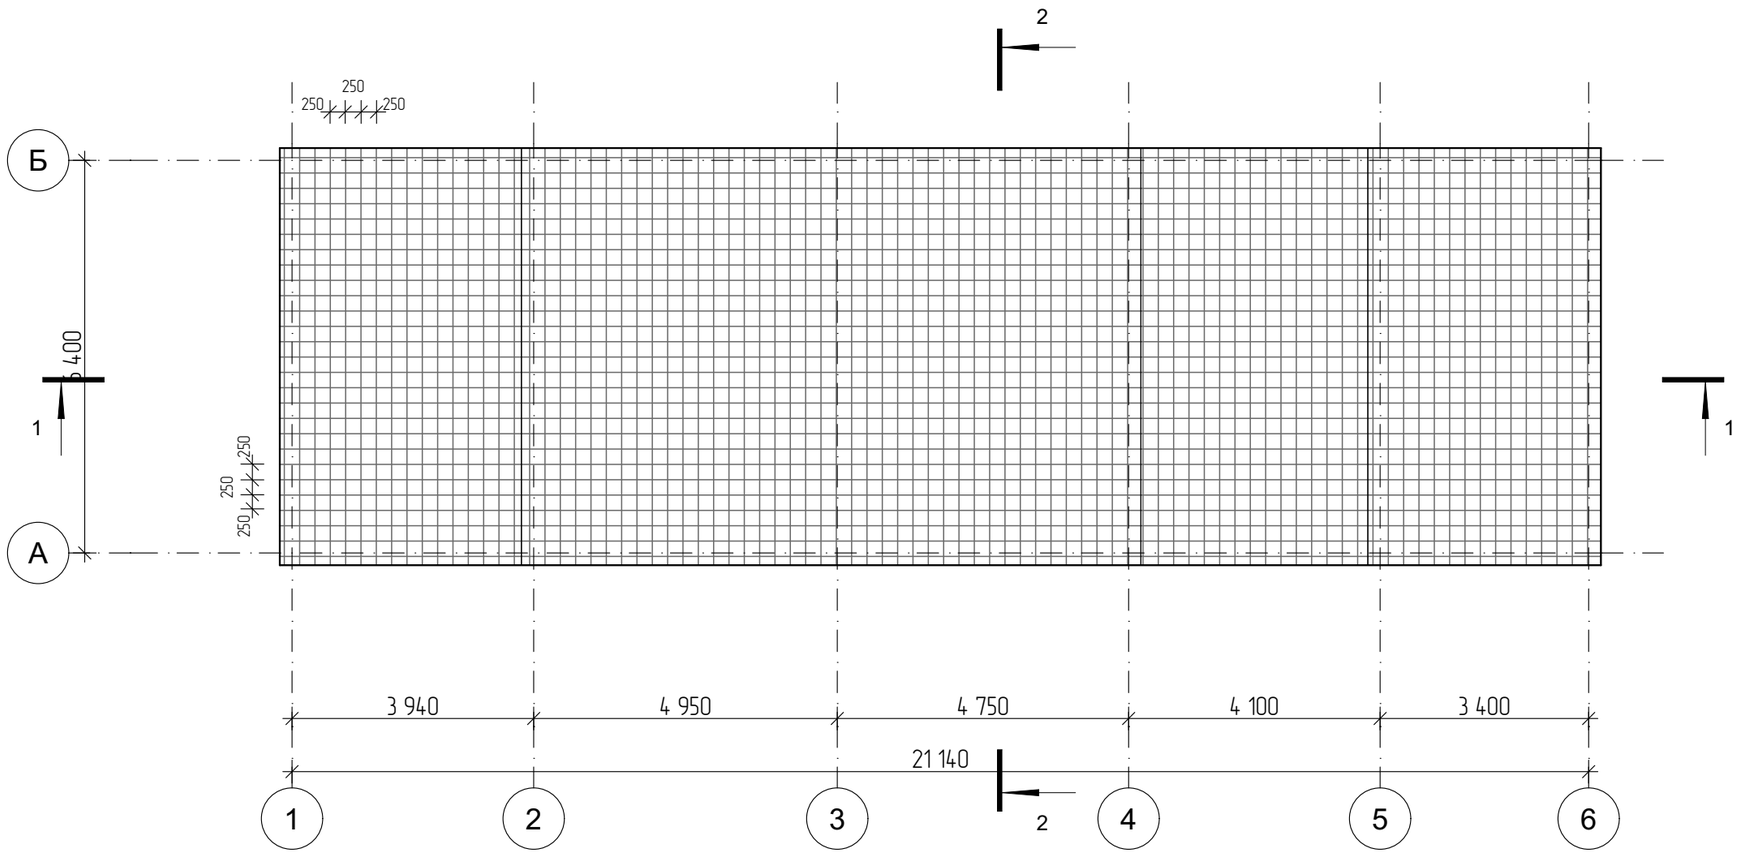


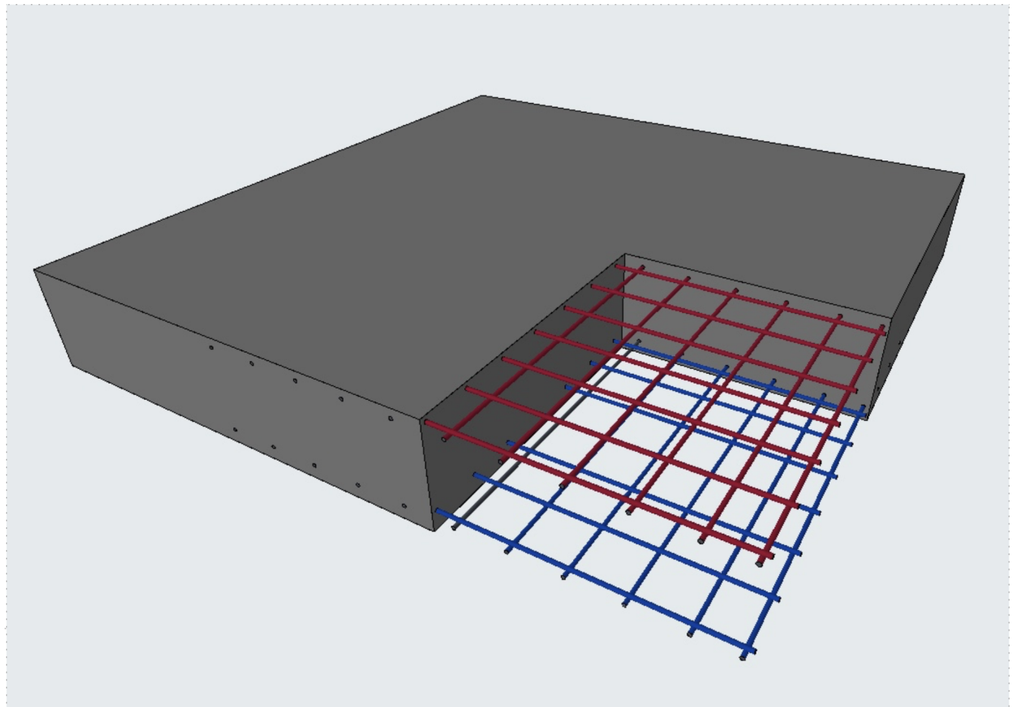


Изм.	Кол.уч.	Лист	№Док.	Подп.	Дата	
						кадастровый номер 63:17:0301011:962, Самарская область, муниципальный район Волжский, городское поселение Смышляевка, поселок городского типа Стройкерамика, улица Александровская роща, земельный участок 104 Россия
						Индивидуальный жилой дом
						Схема верхнего армирования плиты

Стадия	Лист	Листов
ЭП	12	

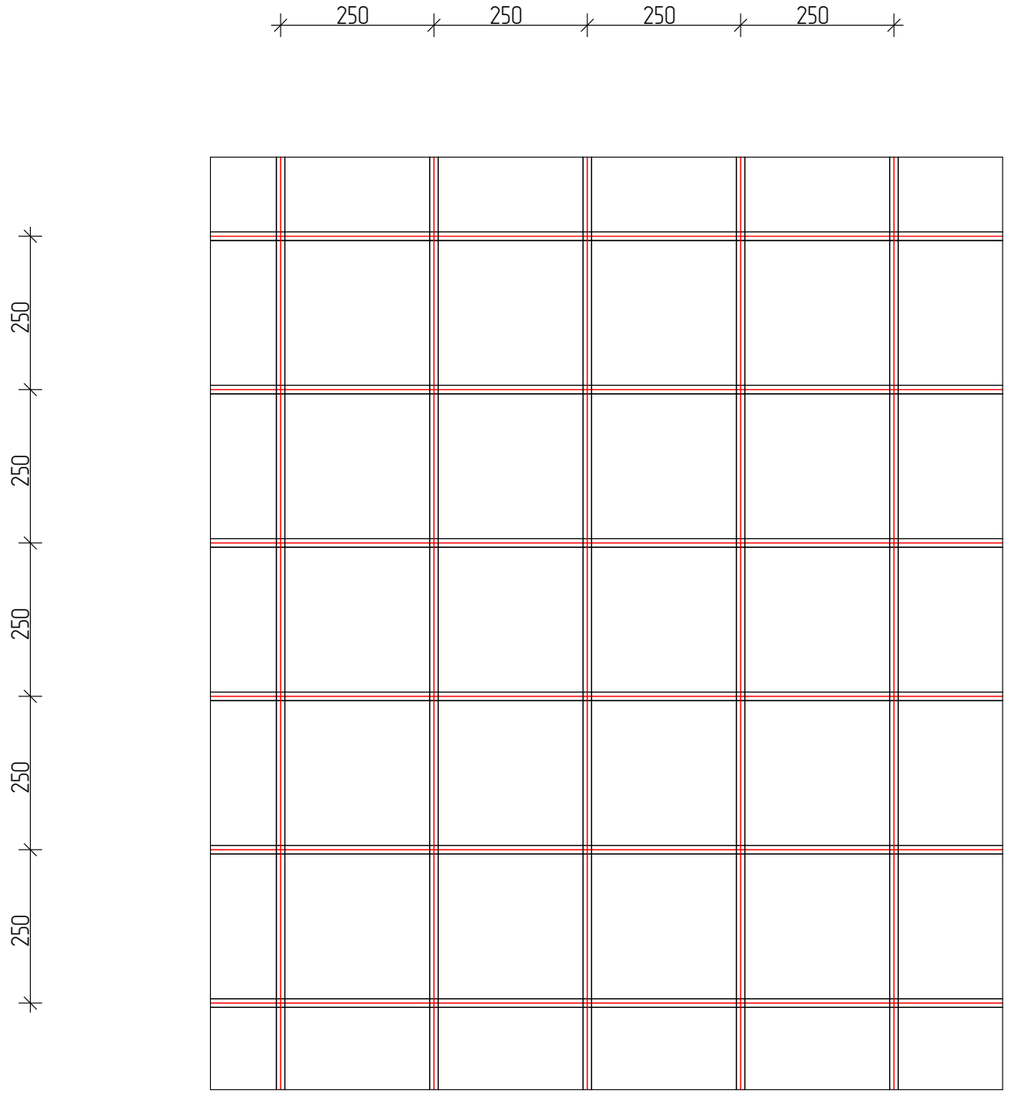

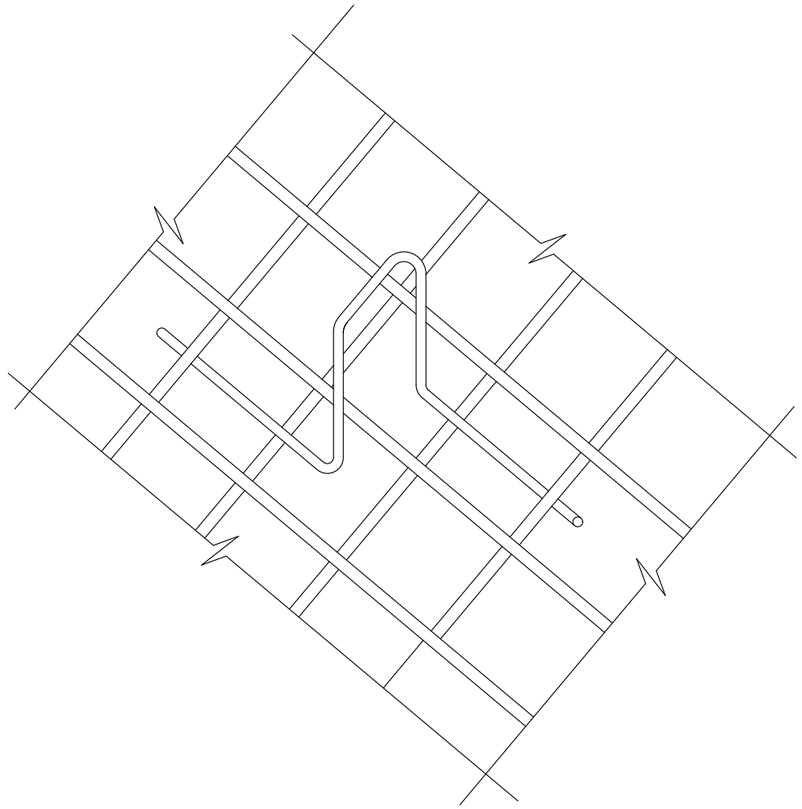

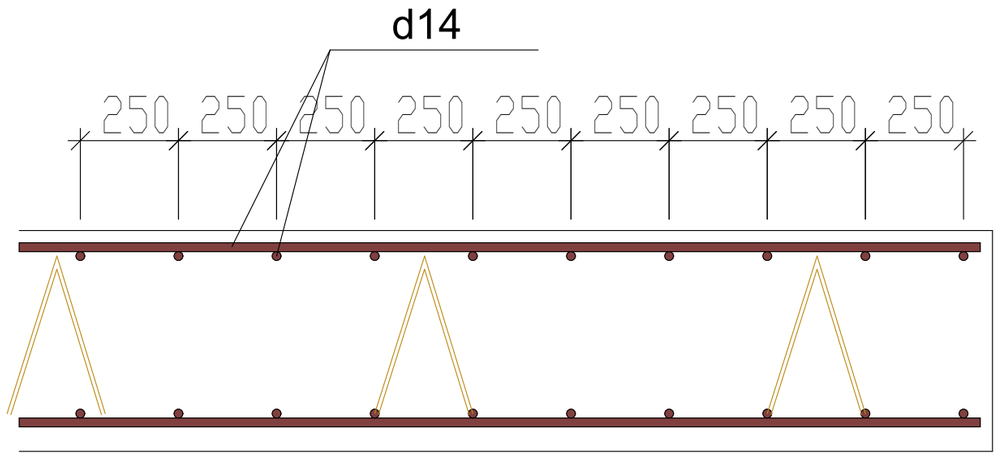

Спецификация элементов к фундаментной плите Фпм–1

МАРКА ПОЗ.	ОБОЗНАЧЕНИЕ	НАИМЕНОВАНИЕ	Кол.	МАССА, КГ	ПРИМЕ–ЧАНИЕ
		Детали			
1		Ø14AIII ГОСТ5781–82* п. м.	2508		


Изм.	Кол.уч.	Лист	№Док.	Подп.	Дата


кадастровый номер 63:17:0301011:962, Самарская область, муниципальный район Волжский, городское поселение Смышляевка, поселок городского типа Стройкерамика, улица Александровская роща, земельный участок 104 Россия

Индивидуальный жилой дом

Стадия	Лист	Листов
ЭП	13	

Схема арматурного каркаса плиты

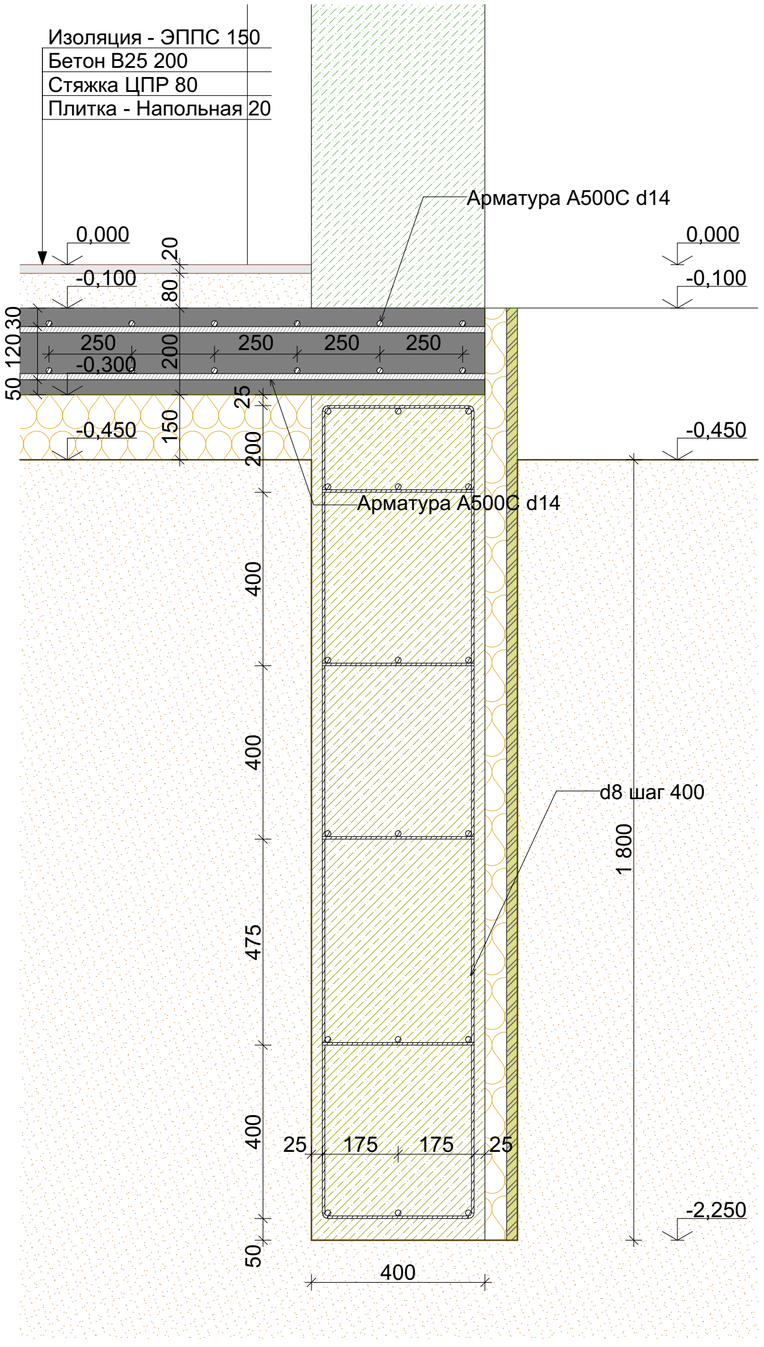

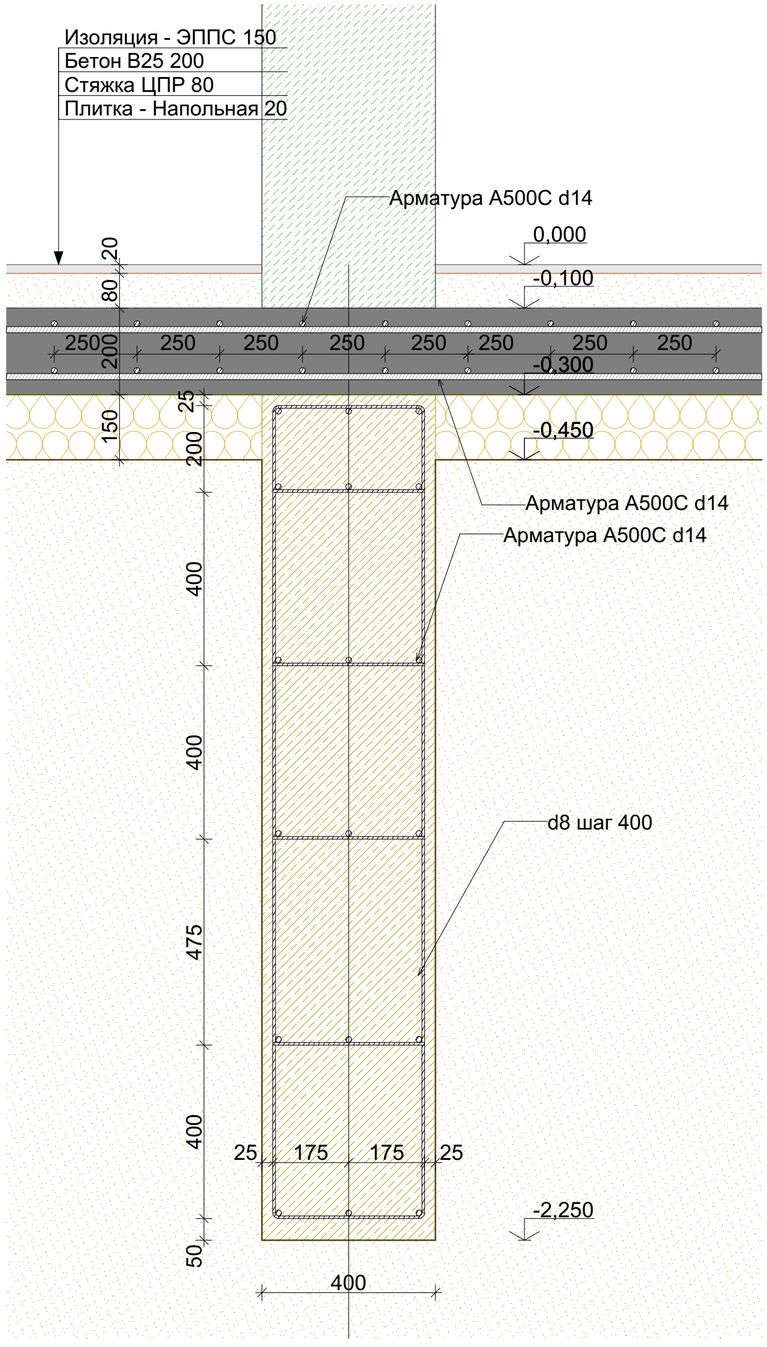


Изм.	Колуч.	Лист	№Док.	Подп.	Дата


кадастровый номер 63:17:0301011:962, Самарская область, муниципальный район Волжский, городское поселение Смышляевка, поселок городского типа Стройкерамика, улица Александровская роща, земельный участок 104 Россия

Индивидуальный жилой дом

Стадия	Лист	Листов
ЭП	14	

Узлы фундамента

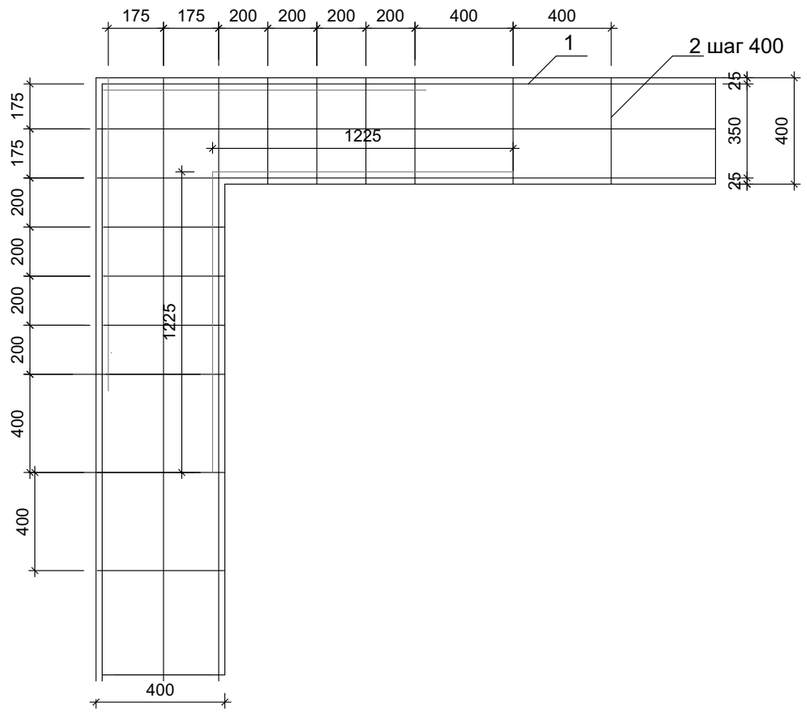

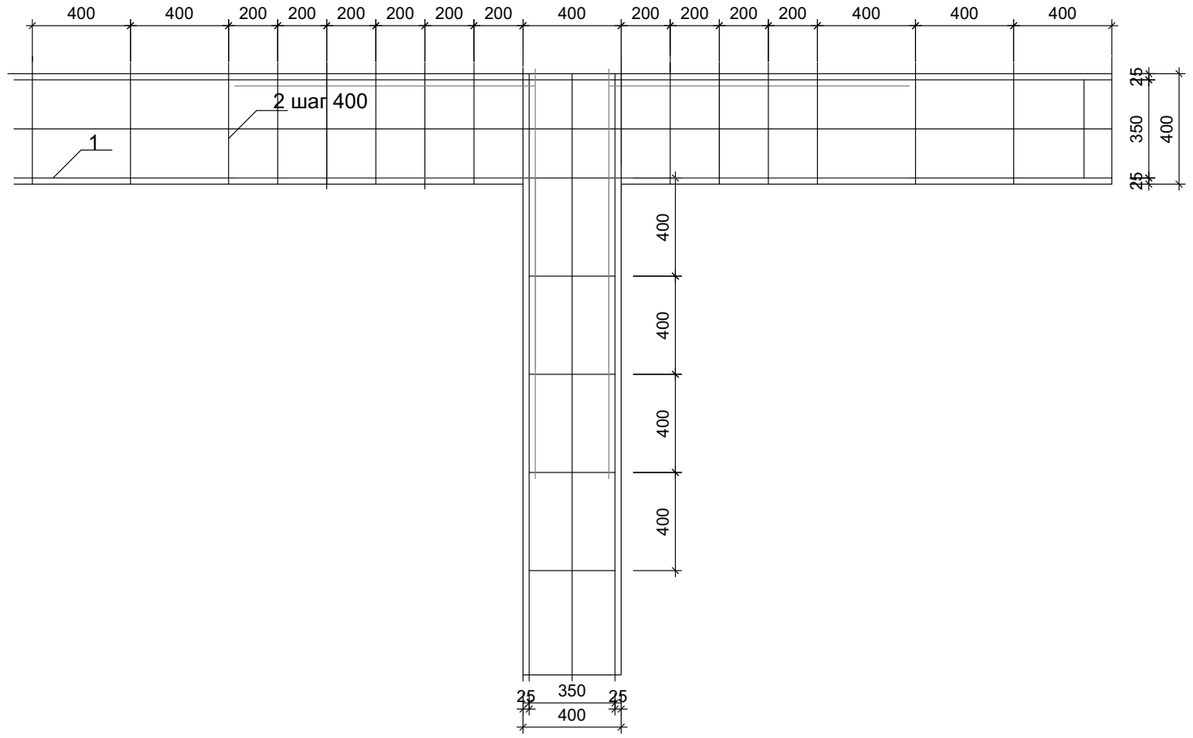

МАРКА ПОЗ.	ОБОЗНАЧЕНИЕ	НАИМЕНОВАНИЕ	Кол.	МАССА, КГ	ПРИМЕ-ЧАНИЕ
		Детали			
1		Ø14AIII ГОСТ5781-82* п.м.	1598 м.п.		
2		Ø8AI(A240) ГОСТ5781-82* l=370	1296 м.п.		


Изм.	Кол.уч.	Лист	№Док.	Подп.	Дата

кадастровый номер 63:17:0301011:962, Самарская область, муниципальный район Волжский, городское поселение Смышляевка, поселок городского типа Стройкерамика, улица Александровская роща, земельный участок 104 Россия


Индивидуальный жилой дом

Стадия	Лист	Листов
ЭП	15	


Схема армирования фундамента

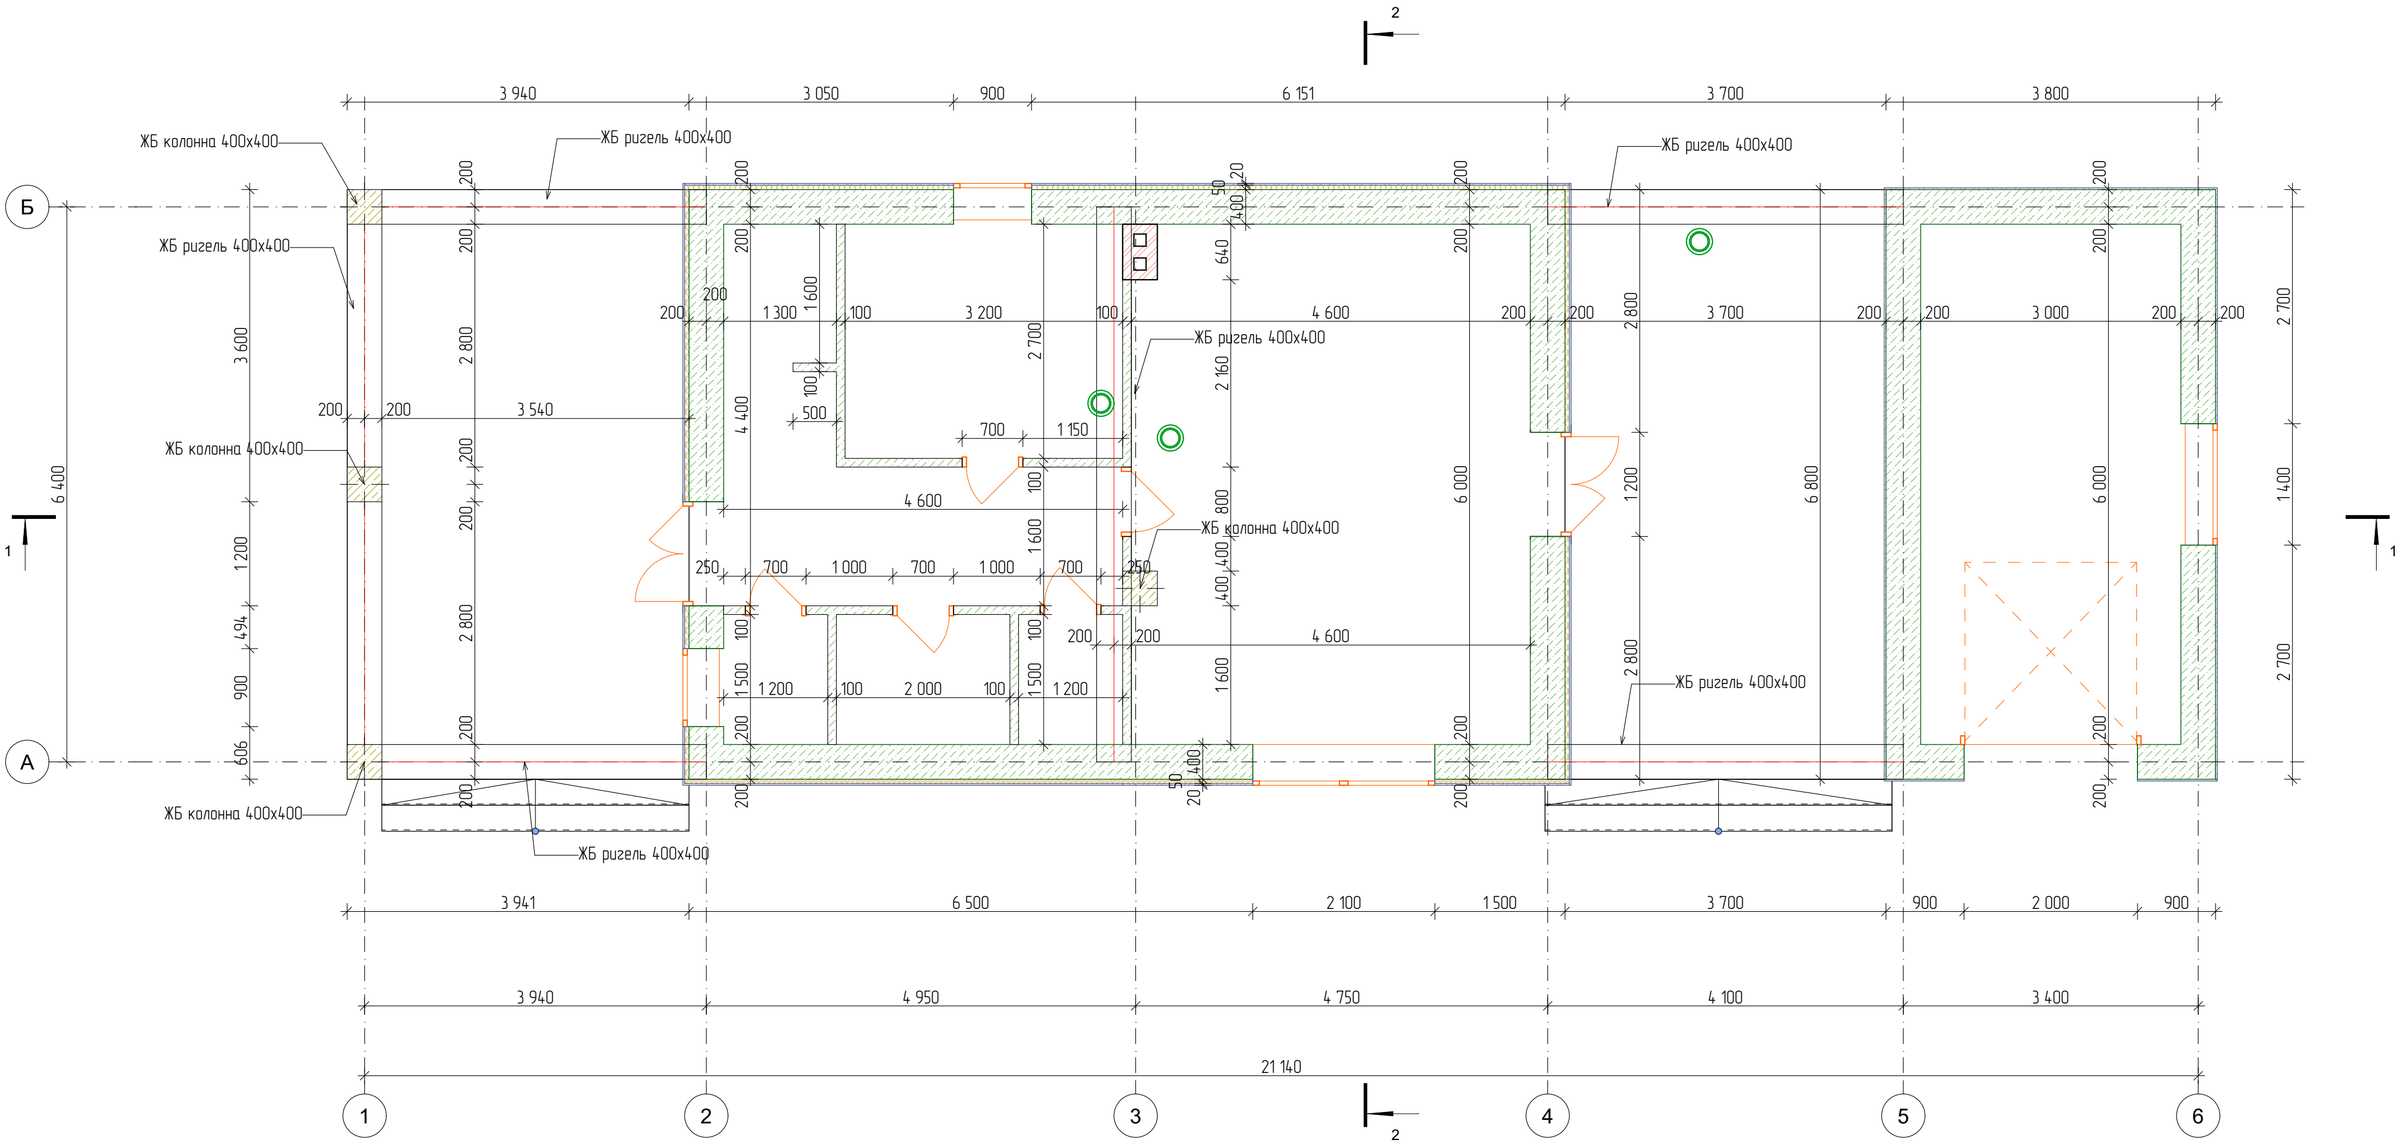

ЖБ ригель 400х400

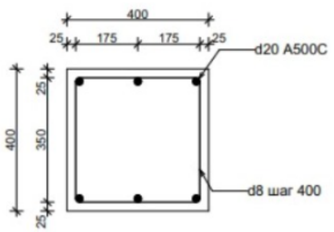

ЖБ Колонна 400х400

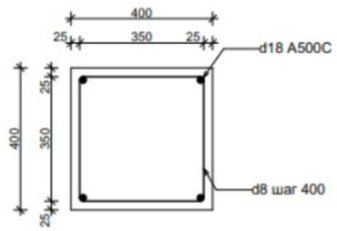

Ø20AIII ГОСТ5781-82* п. м. 132
Ø8AI(A240) ГОСТ5781-82* l=370 166
Ø18AIII ГОСТ5781-82* п. м. 49

ВЕДОМОСТЬ НА КОЛОННЫ, РИГЕЛИ

Наименование	Объем, м3
ЖБ колонна 400х400	1,68
ЖБ ригель 400х400	4,62

ВЕДОМОСТЬ БЛОКА ДЛЯ СТЕН

ID Элемента	Объем, м3
Несущие 400мм	73,28
Перегородки 100мм	4,88


Изм.	Колуч.	Лист	№Док.	Подп.	Дата

кадастровый номер 63:17:0301011:962, Самарская область, муниципальный район Волжский, городское поселение Смышляевка, поселок городского типа Стройкерамика, улица Александровская роща, земельный участок 104 Россия

Индивидуальный жилой дом





Стадия	Лист	Листов
ЭП	16	

План 1 этажа

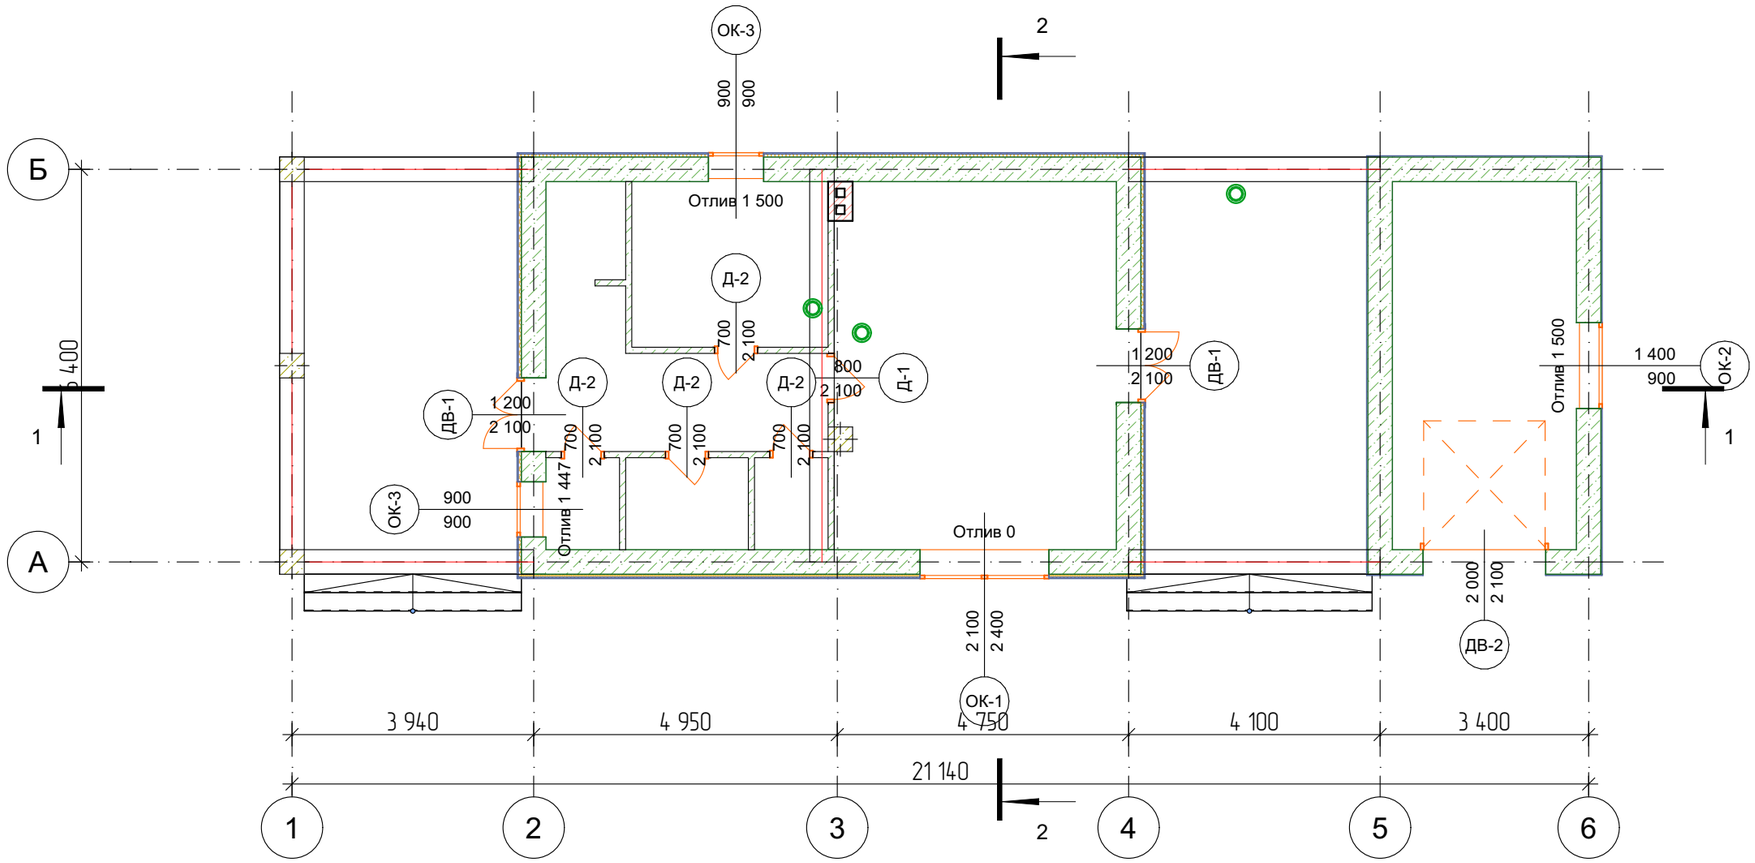


Изм.	Кол.уч.	Лист	№Док.	Подп.	Дата	кадастровый номер 63:17:0301011:962, Самарская область, муниципальный район Волжский, городское поселение Смышляевка, поселок городского типа Стройкерамика, улица Александровская роща, земельный участок 104 Россия			
						Индивидуальный жилой дом	Стадия	Лист	Листов
							ЭП	17	
						Маркировочный план 1 этаж			

Каталог Дверей

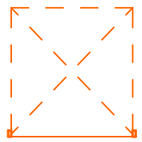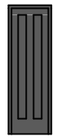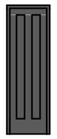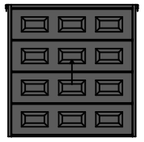Полный ID Элемента	Д-1	Д-2	Д-2	ДВ-1	ДВ-2
D по Классификации	Дверь -1	Дверь -2	Дверь -2	Дверь -1	Дверь -2
Наименование Двери	Однопольная Дверь 27	Однопольная Дверь 27	Однопольная Дверь 27	Двупольная Дверь 27	Ворота Гаражные Подъемные 27
Количество	1	1	3	2	1
Размер Ш x В	800×2 100	700×2 100	700×2 100	1 200×2 100	2 000×2 100
Ориентация	П	П	Л	Л	
Высота Порога Двери	0	0	0	0	0
Высота Перемычки Двери	2 100	2 100	2 100	2 100	2 100
2D-символ					
Вид со Стороны, Противоположной Стороне Открывания					


Каталог Окон

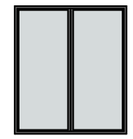Полный ID Элемента	ОК-1	ОК-2	ОК-3	ОК-3
Наименование Окна	Раздвижное Двустворчатое Окно 27	Окно 27	Окно 27	Окно 27
Количество	1	1	1	1
Размер Ш x В	2 100×2 400	1 400×900	900×900	900×900
Высота Подоконника Окна	0	1 500	1 447	1 500
Высота Перемычки Окна	2 400	2 400	2 347	2 400
2D-символ				
Вид со Стороны, Противоположной Стороне Открывания				


Изм.	Кол.уч.	Лист	№Док.	Подп.	Дата

кадастровый номер 63:17:0301011:962, Самарская область, муниципальный район Волжский, городское поселение Смышляевка, поселок городского типа Стройкерамика, улица Александровская роща, земельный участок 104 Россия

Индивидуальный жилой дом	Стадия	Лист	Листов
	ЭП	18	
Каталог проемов			

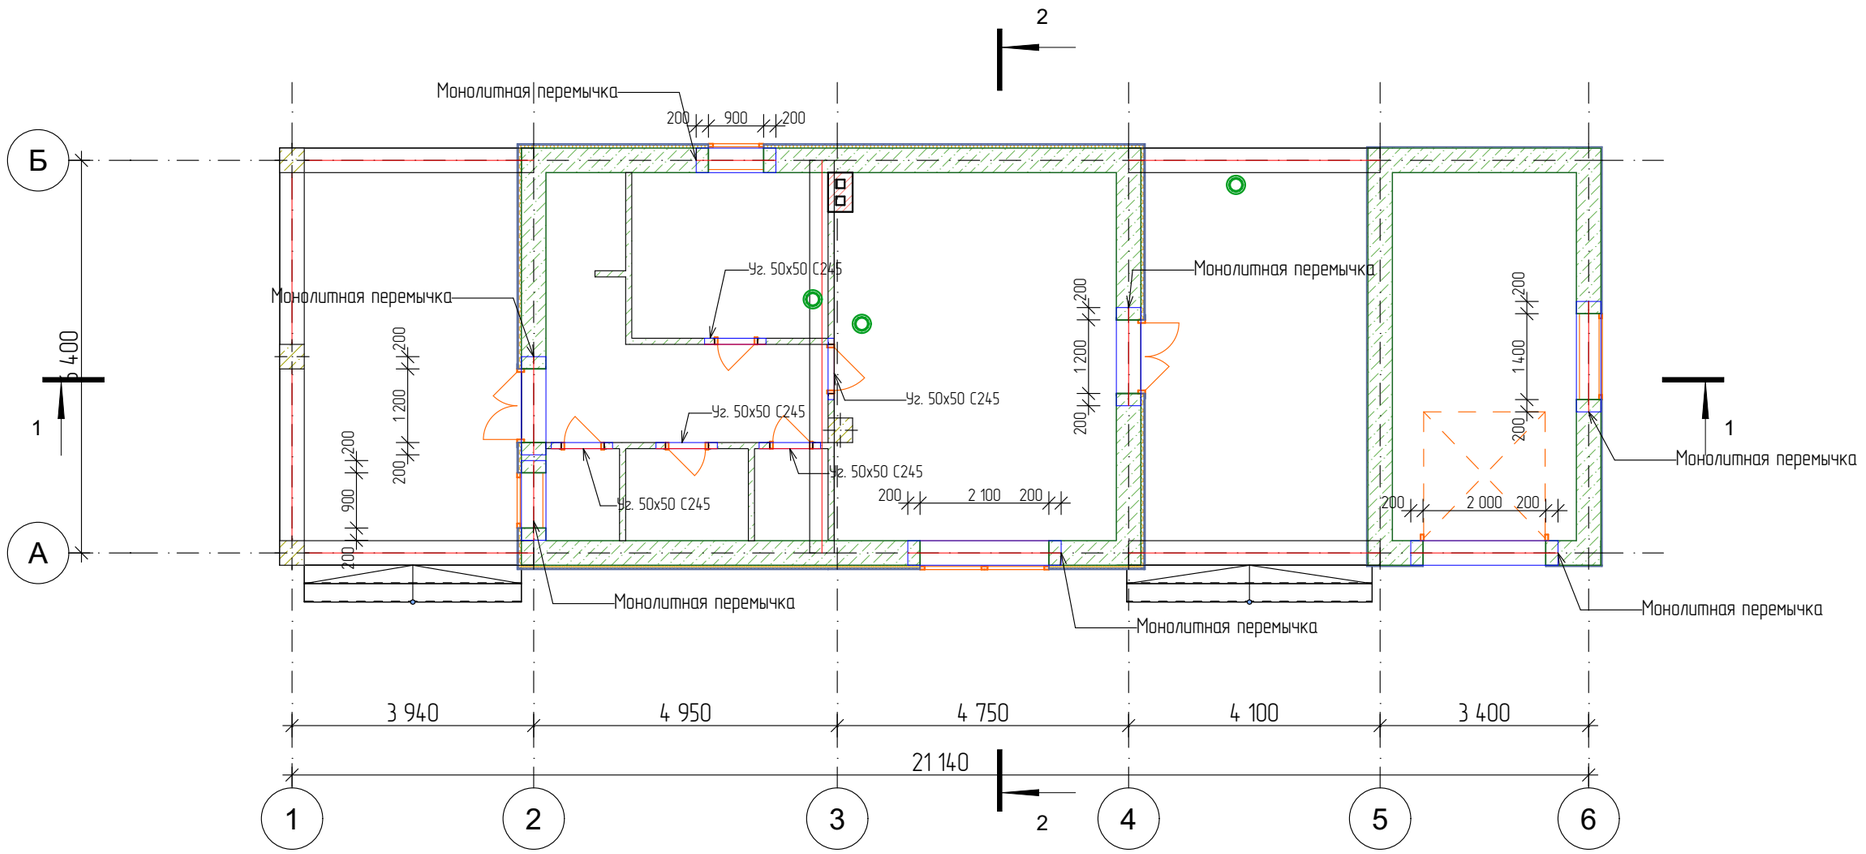

Ø12AIII ГОСТ5781-82* п. м. 58
Ø8AI(A240) ГОСТ5781-82* l=370 35

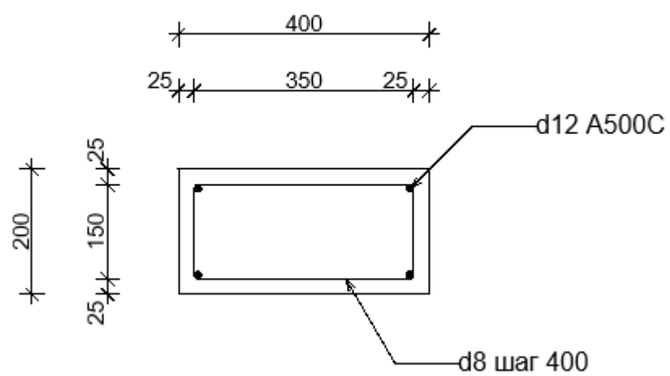


ВЕДОМОСТЬ НА МОНОЛИТНЫЕ ПЕРЕМЫЧКИ

Наименование	Объем, м3
	0,99
Монолитная перемычка	0,99


Изм.	Кол.уч.	Лист	№Док.	Подп.	Дата

кадастровый номер 63:17:0301011:962, Самарская область, муниципальный район Волжский, городское поселение Смышляевка, поселок городского типа Стройкерамика, улица Александровская роща, земельный участок 104 Россия

Индивидуальный жилой дом	Стадия	Лист	Листов
	ЭП	19	
Схема расположения перемычек			

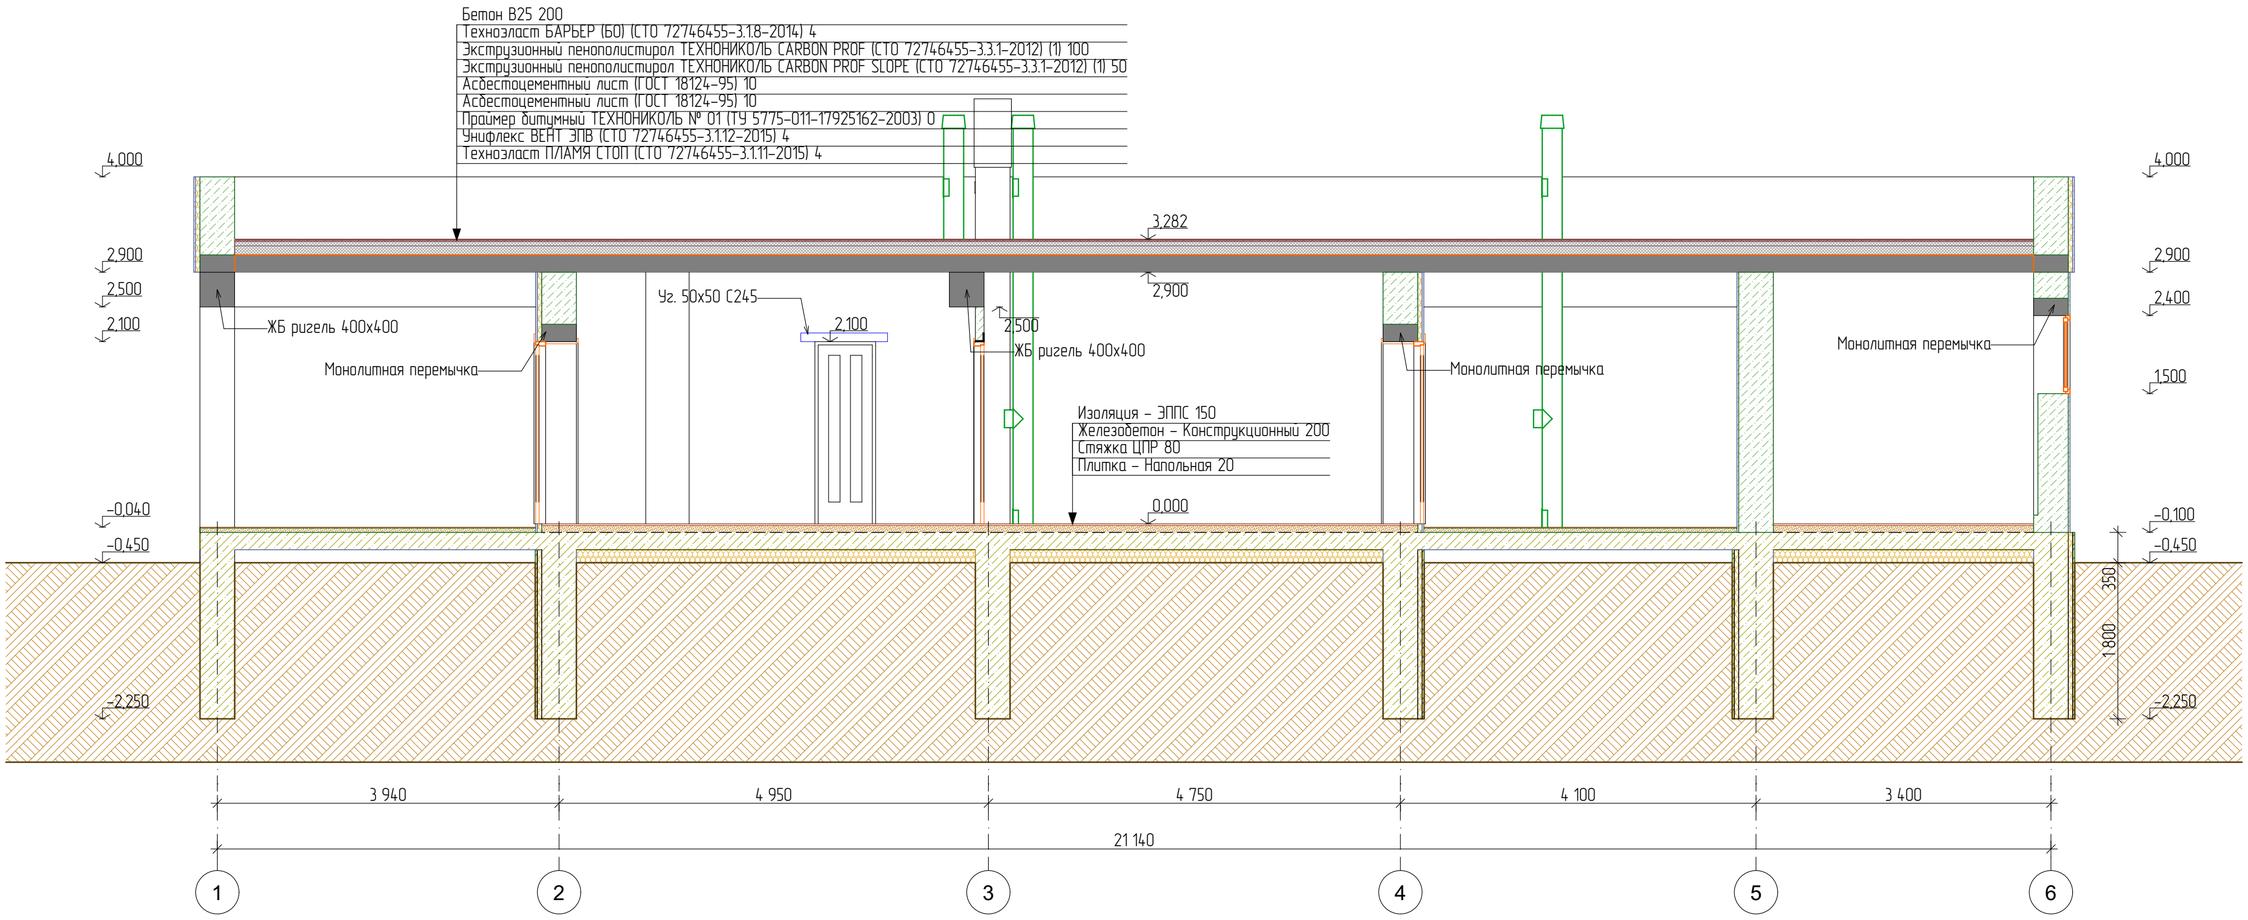


Изм.	Кол.уч.	Лист	№Док.	Подп.	Дата	кадастровый номер 63:17:0301011:962, Самарская область, муниципальный район Волжский, городское поселение Смышляевка, поселок городского типа Стройкерамика, улица Александровская роща, земельный участок 104 Россия			
						Индивидуальный жилой дом	Стадия	Лист	Листов
							ЭП	20	
						Разрез 1 - 1			

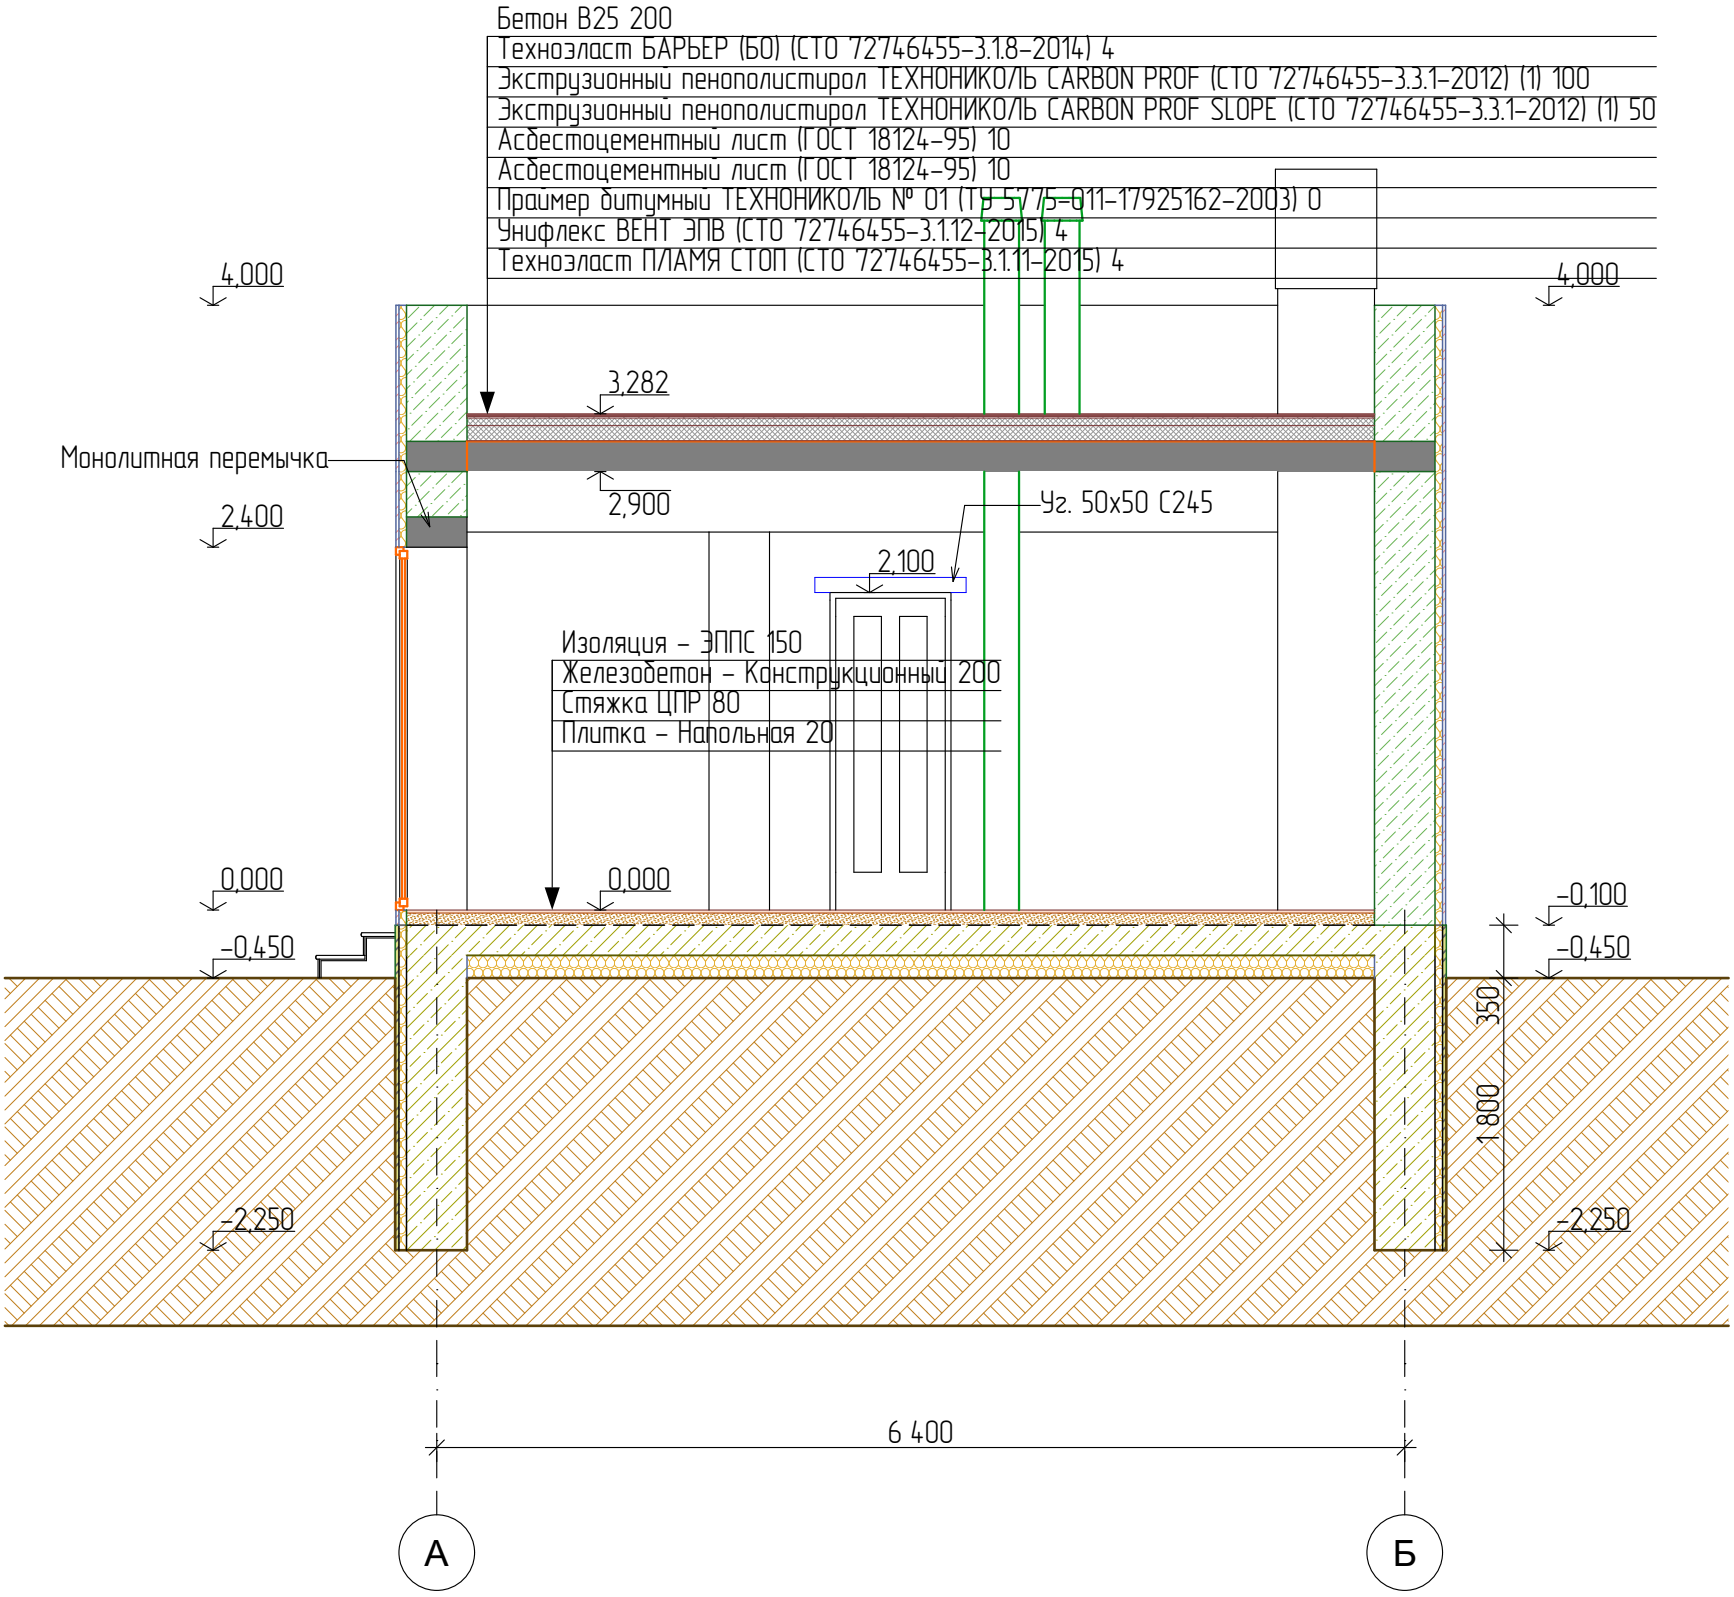


Изм.	Кол.уч.	Лист	№Док.	Подп.	Дата	
						кадастровый номер 63:17:0301011:962, Самарская область, муниципальный район Волжский, городское поселение Смышляевка, поселок городского типа Стройкерамика, улица Александровская роща, земельный участок 104 Россия
						Индивидуальный жилой дом
						Разрез 2 - 2

Стадия	Лист	Листов
ЭП	21	

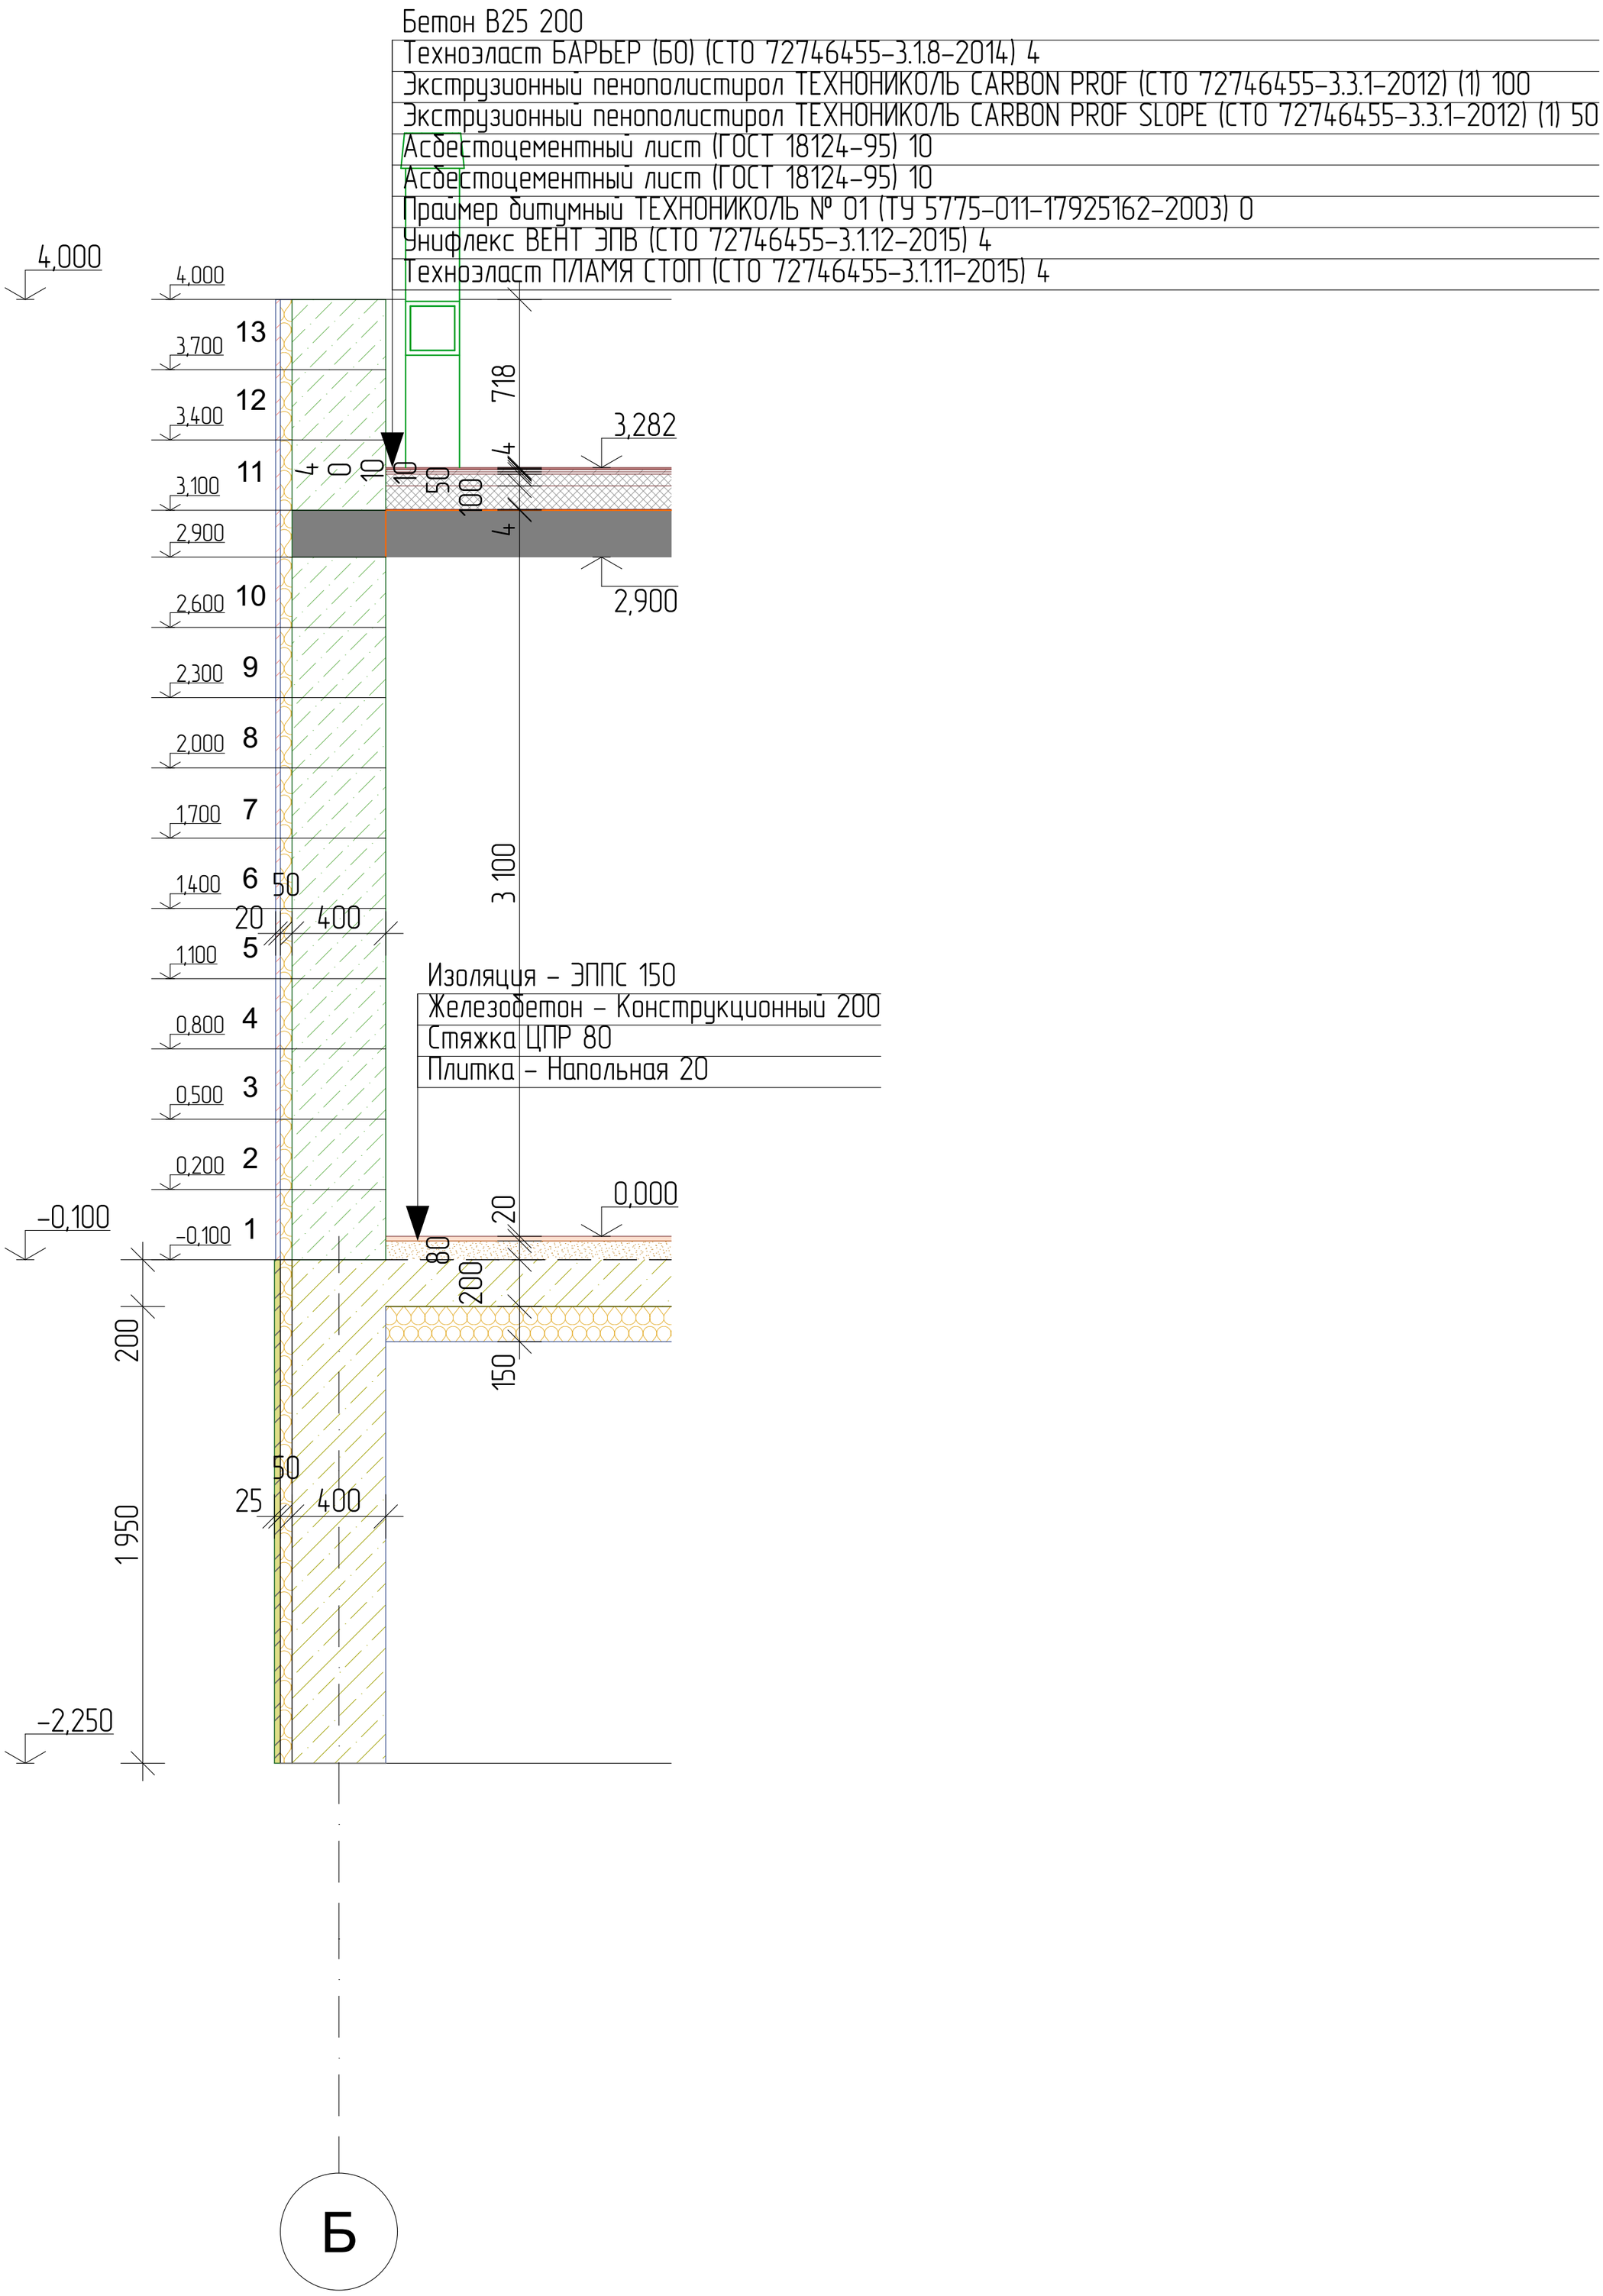


Изм.	Кол.уч.	Лист	№Док.	Подп.	Дата	кадастровый номер 63:17:0301011:962, Самарская область, муниципальный район Волжский, городское поселение Смышляевка, поселок городского типа Стройкерамика, улица Александровская роща, земельный участок 104 Россия			
						Индивидуальный жилой дом	Стадия	Лист	Листов
							ЭП	22	
						Разрез по стене			

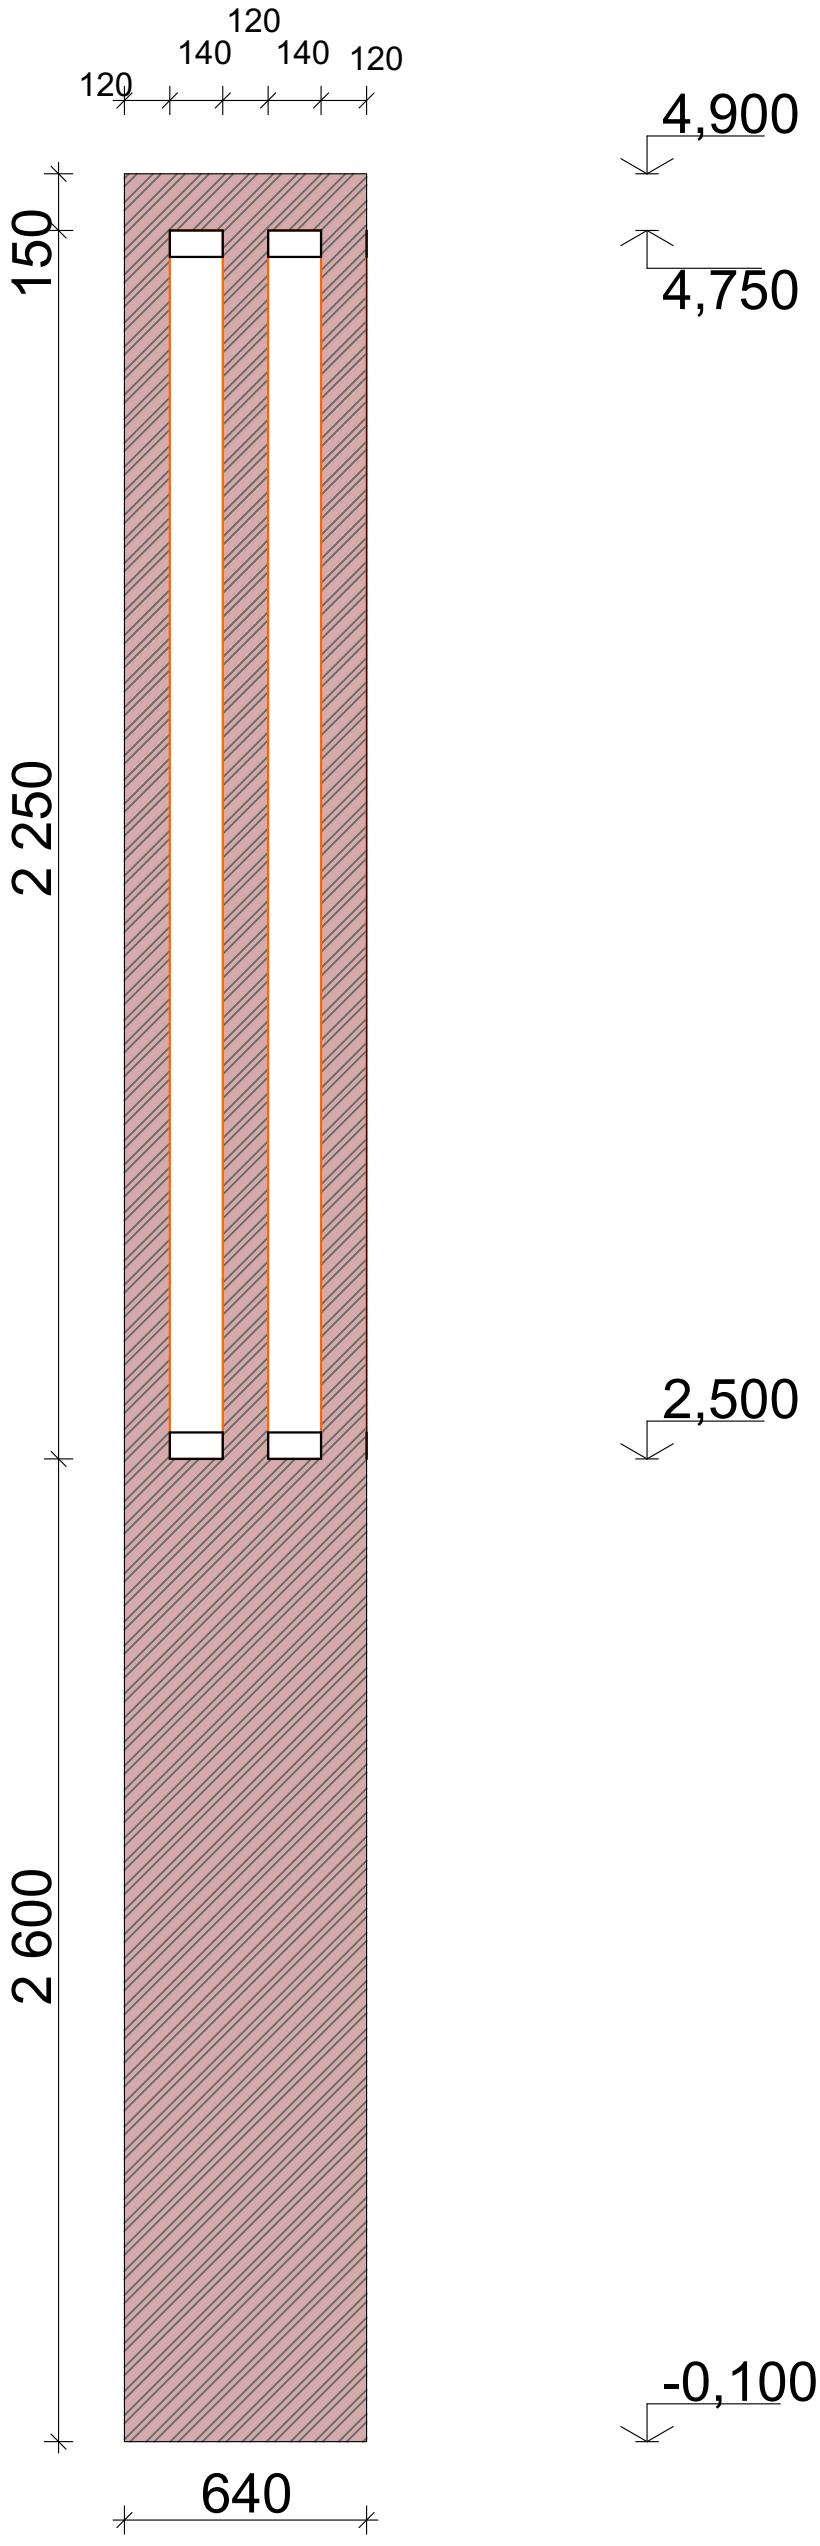



Изм.	Кол.уч.	Лист	№Док.	Подп.	Дата

кадастровый номер 63:17:0301011:962, Самарская область, муниципальный район Волжский, городское поселение Смышляевка, поселок городского типа Стройкерамика, улица Александровская роща, земельный участок 104 Россия

Индивидуальный жилой дом	Стадия	Лист	Листов
	ЭП	23	
Развертка вентканала			

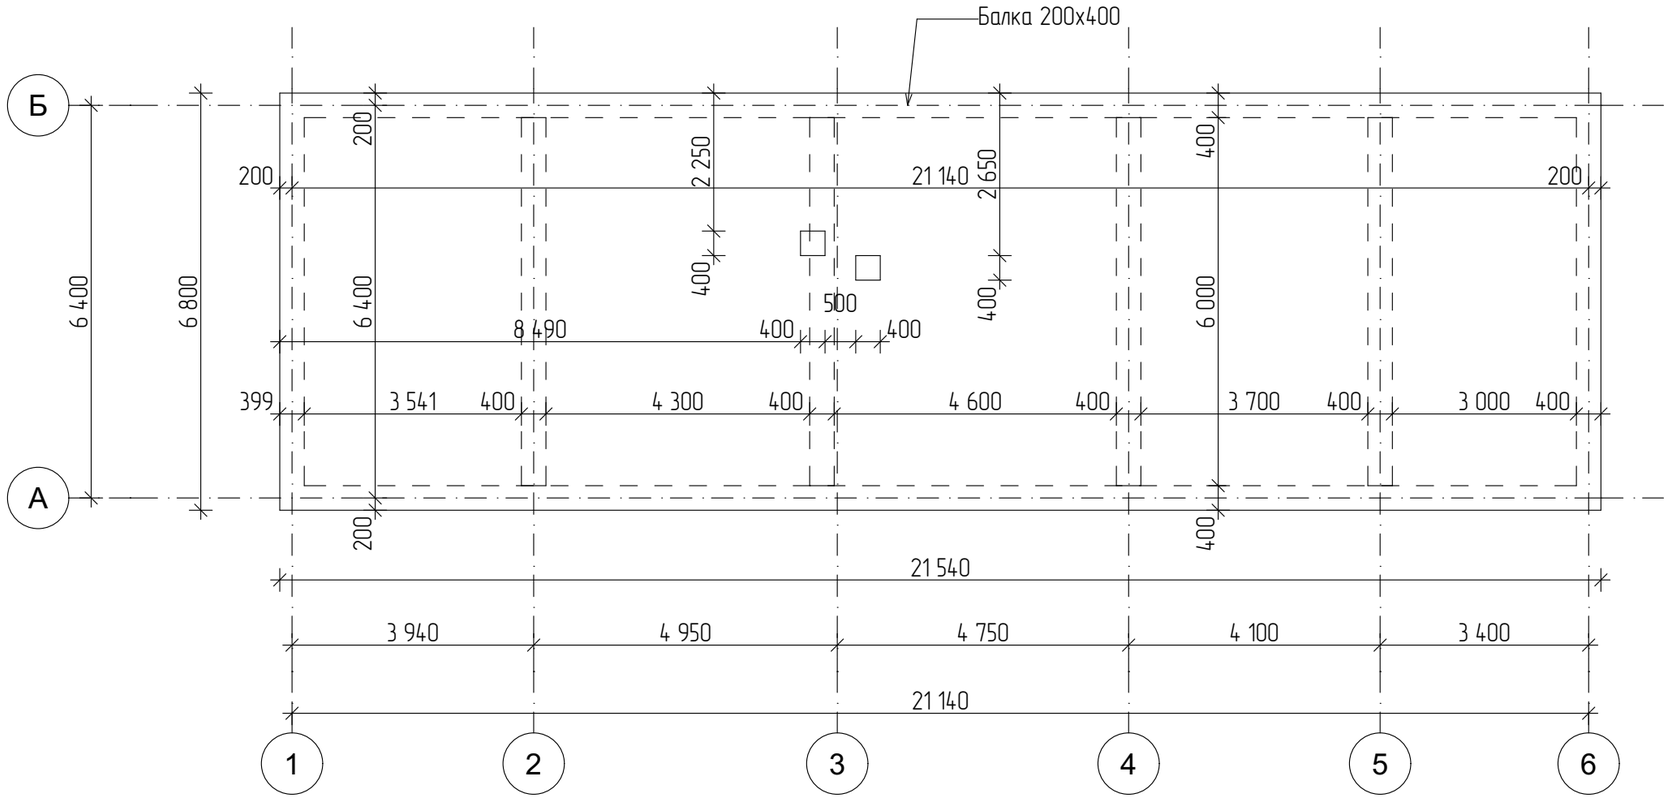

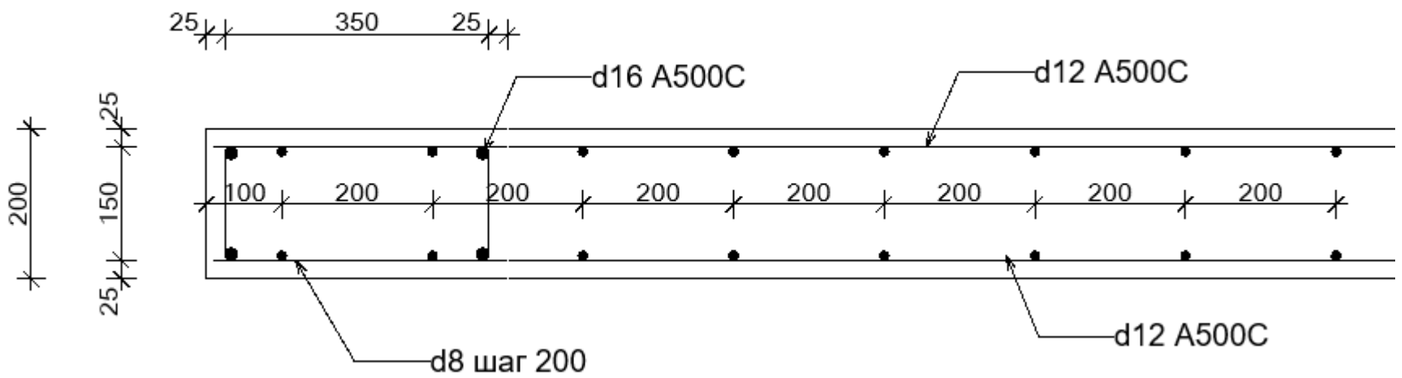

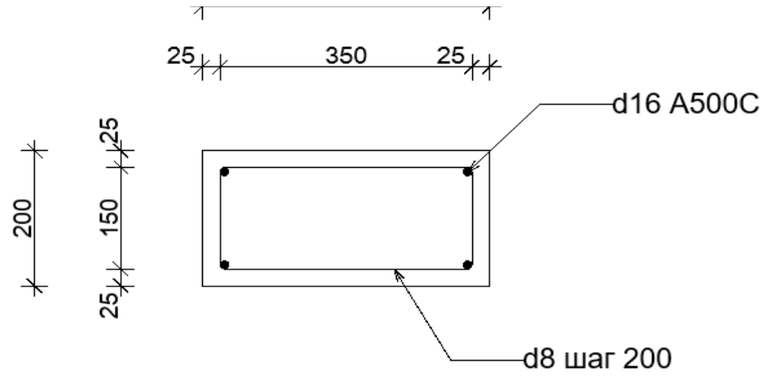

ВЕДОМОСТЬ ПЕРЕКРЫТИЯ

Наименование	Объем, м3
Монолитная плита	29,29


Изм.	Кол.уч.	Лист	№Док.	Подп.	Дата


кадастровый номер 63:17:0301011:962, Самарская область, муниципальный район Волжский, городское поселение Смышляевка, поселок городского типа Стройкерамика, улица Александровская роща, земельный участок 104 Россия

Индивидуальный жилой дом

Стадия	Лист	Листов
ЭП	24	


План перекрытия +2,900

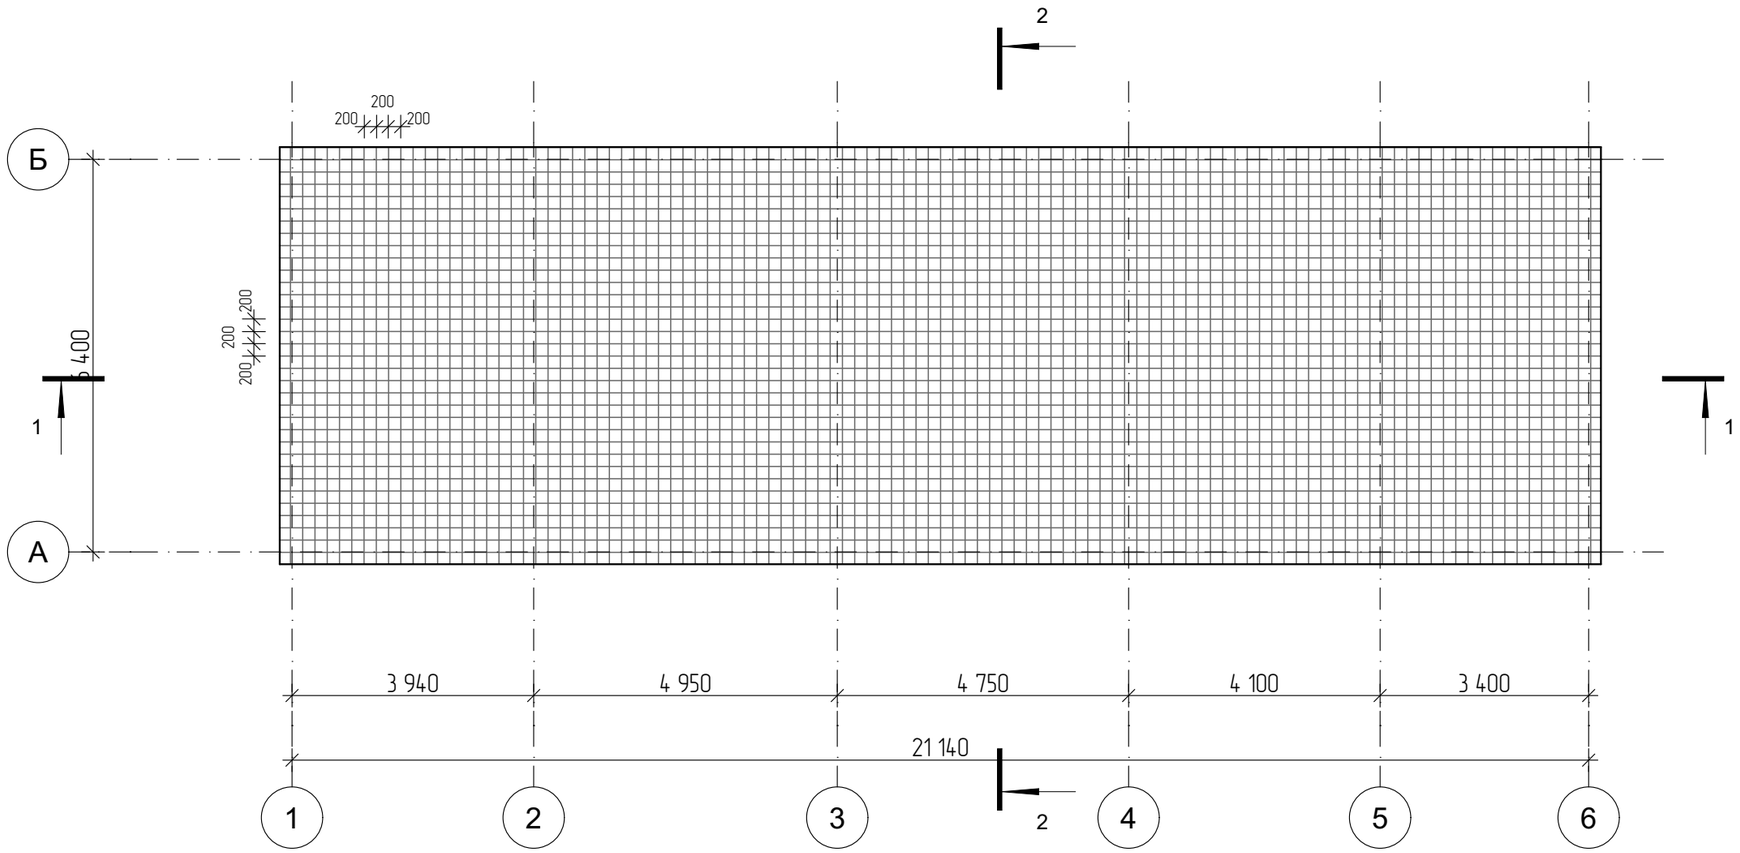


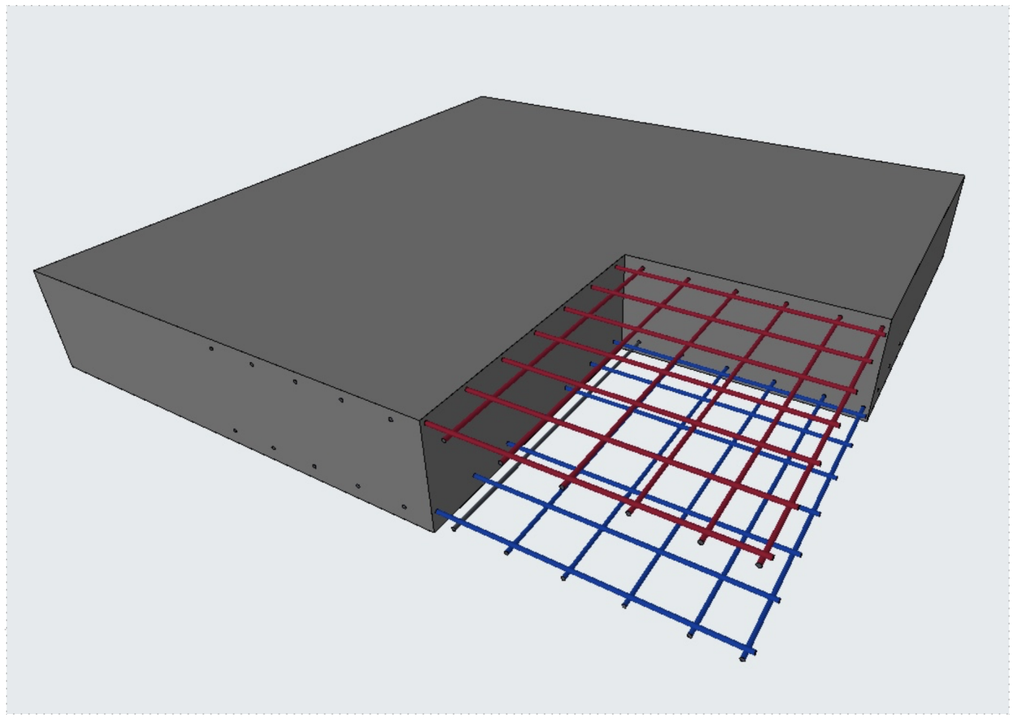

Изм.	Кол.уч.	Лист	№Док.	Подп.	Дата	
						кадастровый номер 63:17:0301011:962, Самарская область, муниципальный район Волжский, городское поселение Смышляевка, поселок городского типа Стройкерамика, улица Александровская роща, земельный участок 104 Россия
						Индивидуальный жилой дом
						Схема нижнего армирования плиты


Стадия	Лист	Листов
ЭП	25	

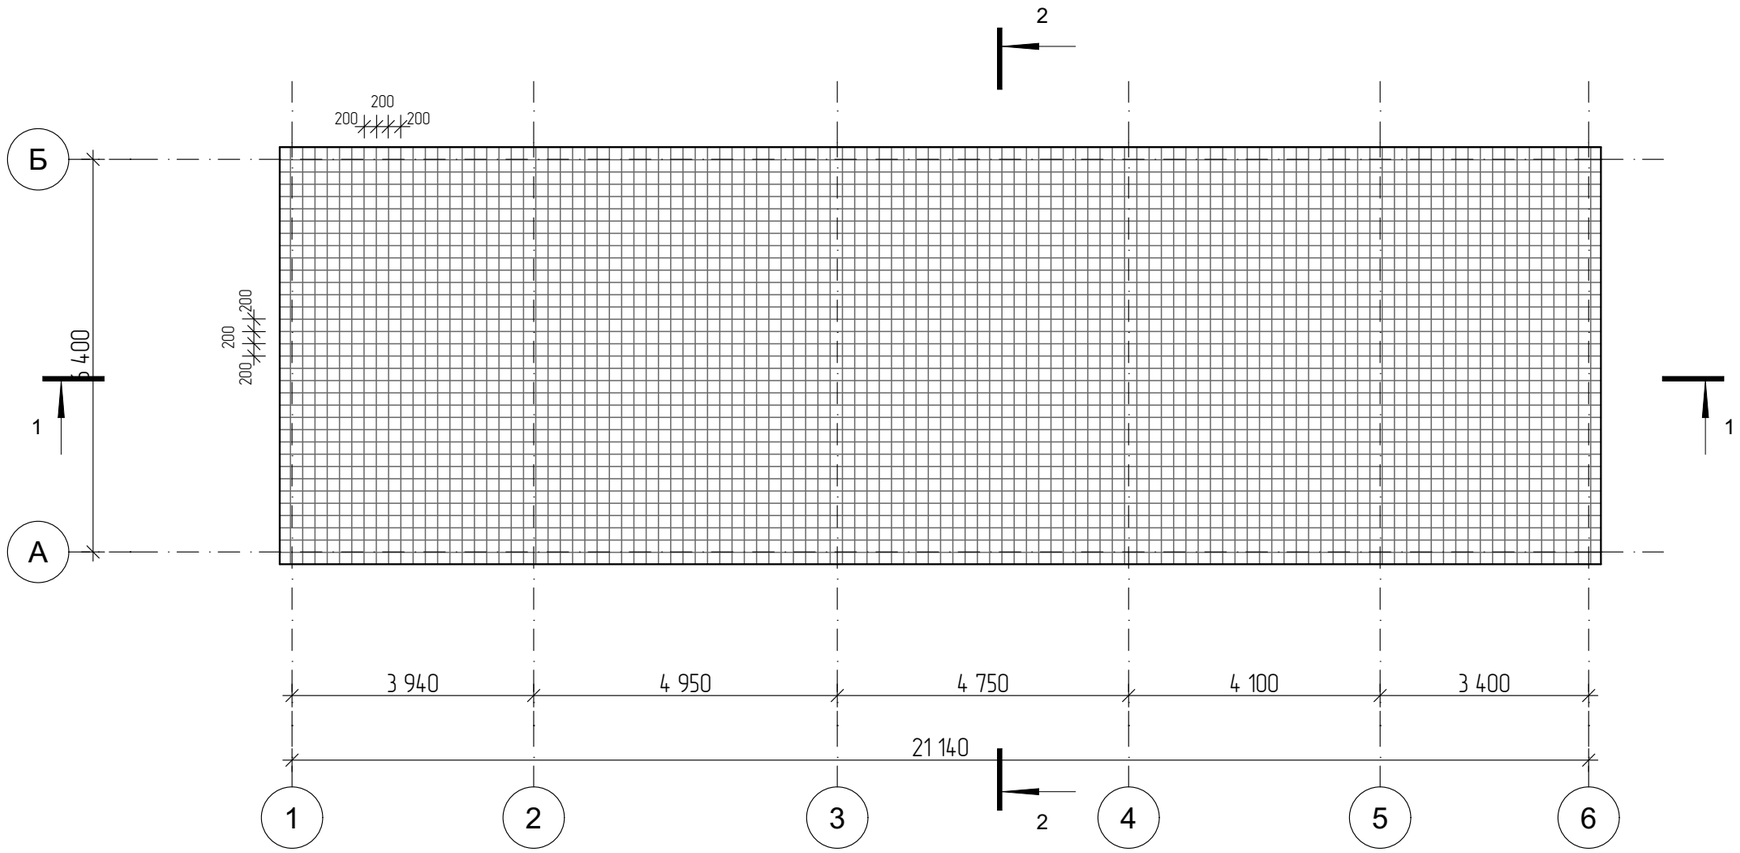


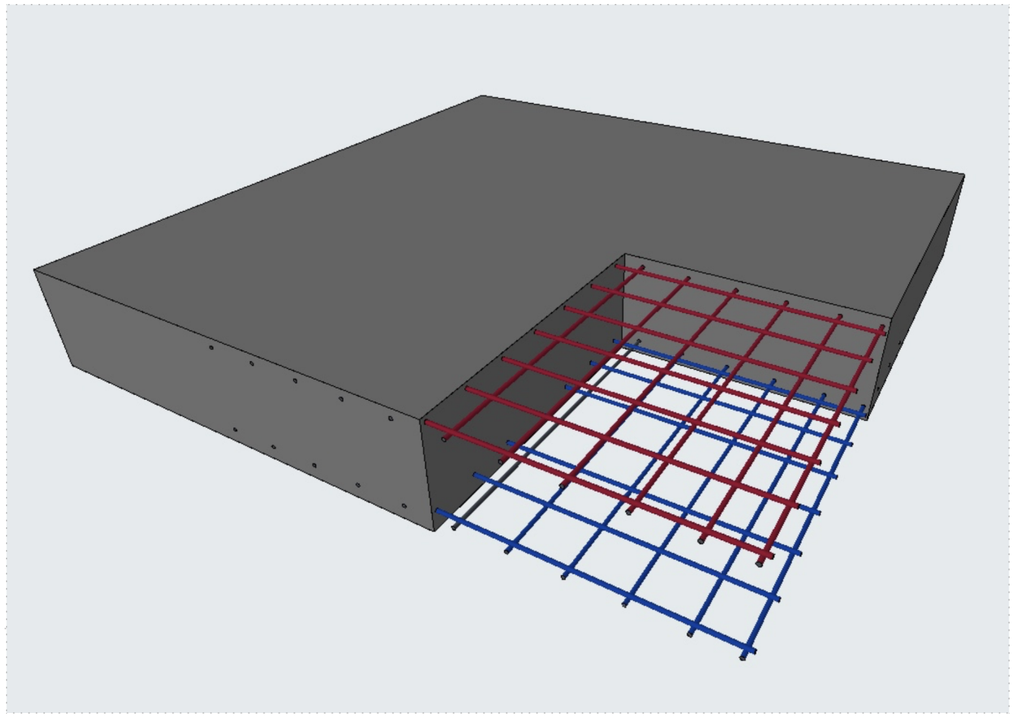


Изм.	Кол.уч.	Лист	№Док.	Подп.	Дата	
						кадастровый номер 63:17:0301011:962, Самарская область, муниципальный район Волжский, городское поселение Смышляевка, поселок городского типа Стройкерамика, улица Александровская роща, земельный участок 104 Россия
						Индивидуальный жилой дом
						Схема верхнего армирования плиты

Стадия	Лист	Листов
ЭП	26	

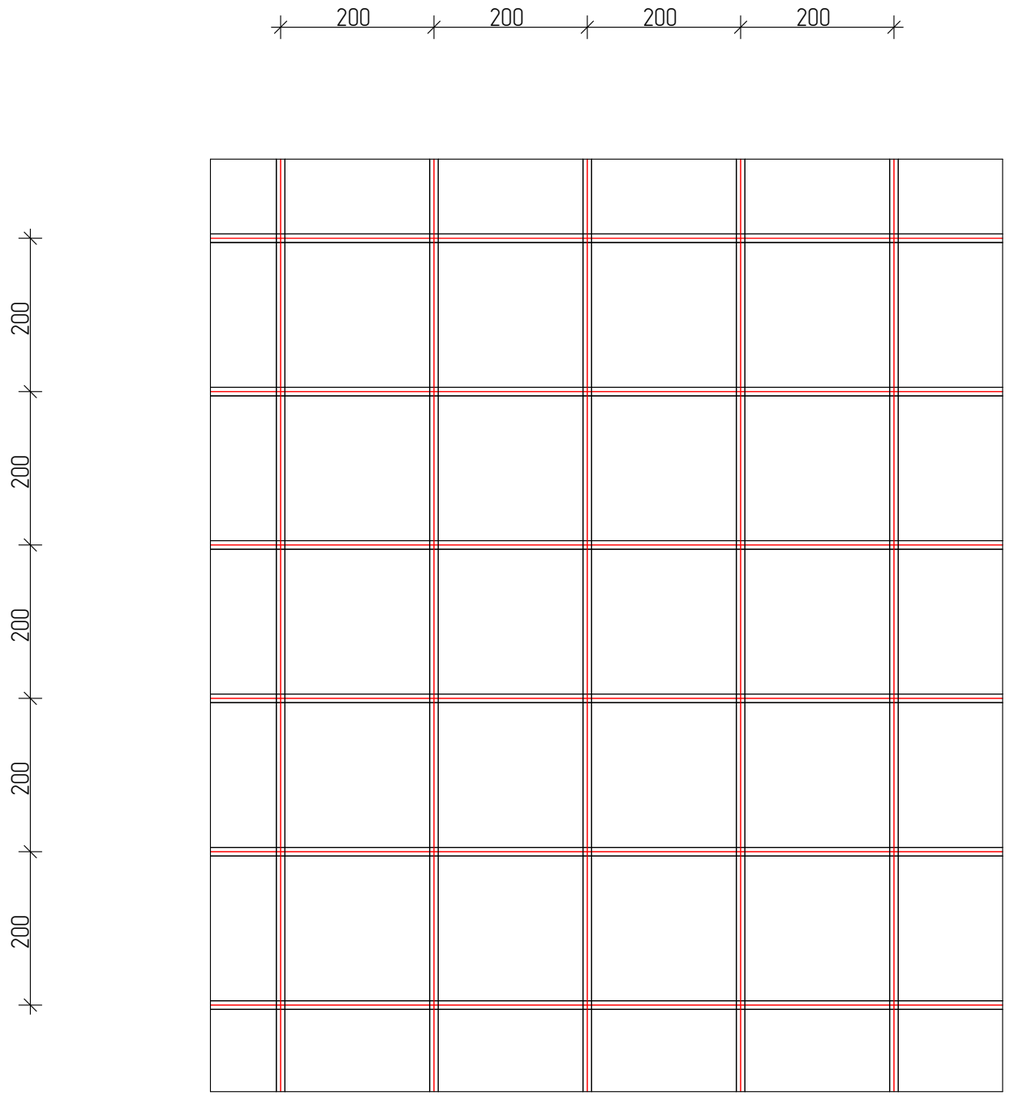

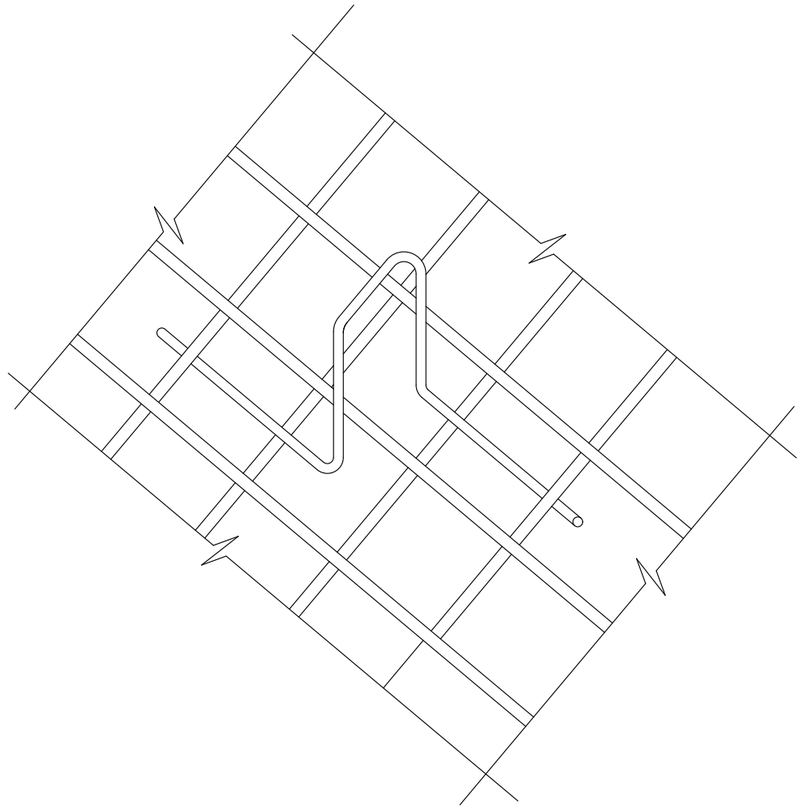

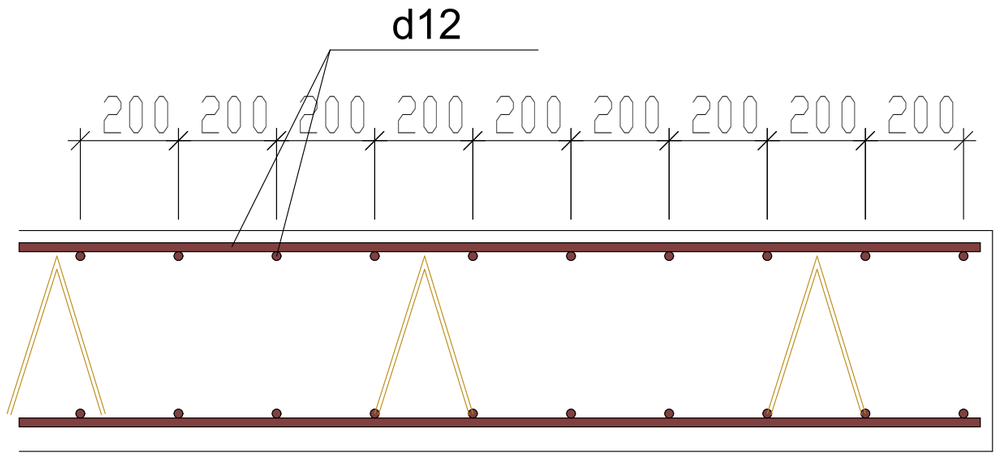

Спецификация элементов к фундаментной плите Фпм–1

МАРКА ПОЗ.	ОБОЗНАЧЕНИЕ	НАИМЕНОВАНИЕ	Кол.	МАССА, КГ	ПРИМЕ–ЧАНИЕ
		Детали			
1		Ø12 AIII ГОСТ5781–82* п. м.	3135		
2		Ø8 AI(A240) ГОСТ5781–82* l=370	216		
3		Ø16 AIII ГОСТ5781–82* п. м.	356		


Изм.	Кол.уч.	Лист	№Док.	Подп.	Дата


кадастровый номер 63:17:0301011:962, Самарская область, муниципальный район Волжский, городское поселение Смышляевка, поселок городского типа Стройкерамика, улица Александровская роща, земельный участок 104 Россия

Индивидуальный жилой дом

Стадия	Лист	Листов
ЭП	27	


Схема арматурного каркаса плиты

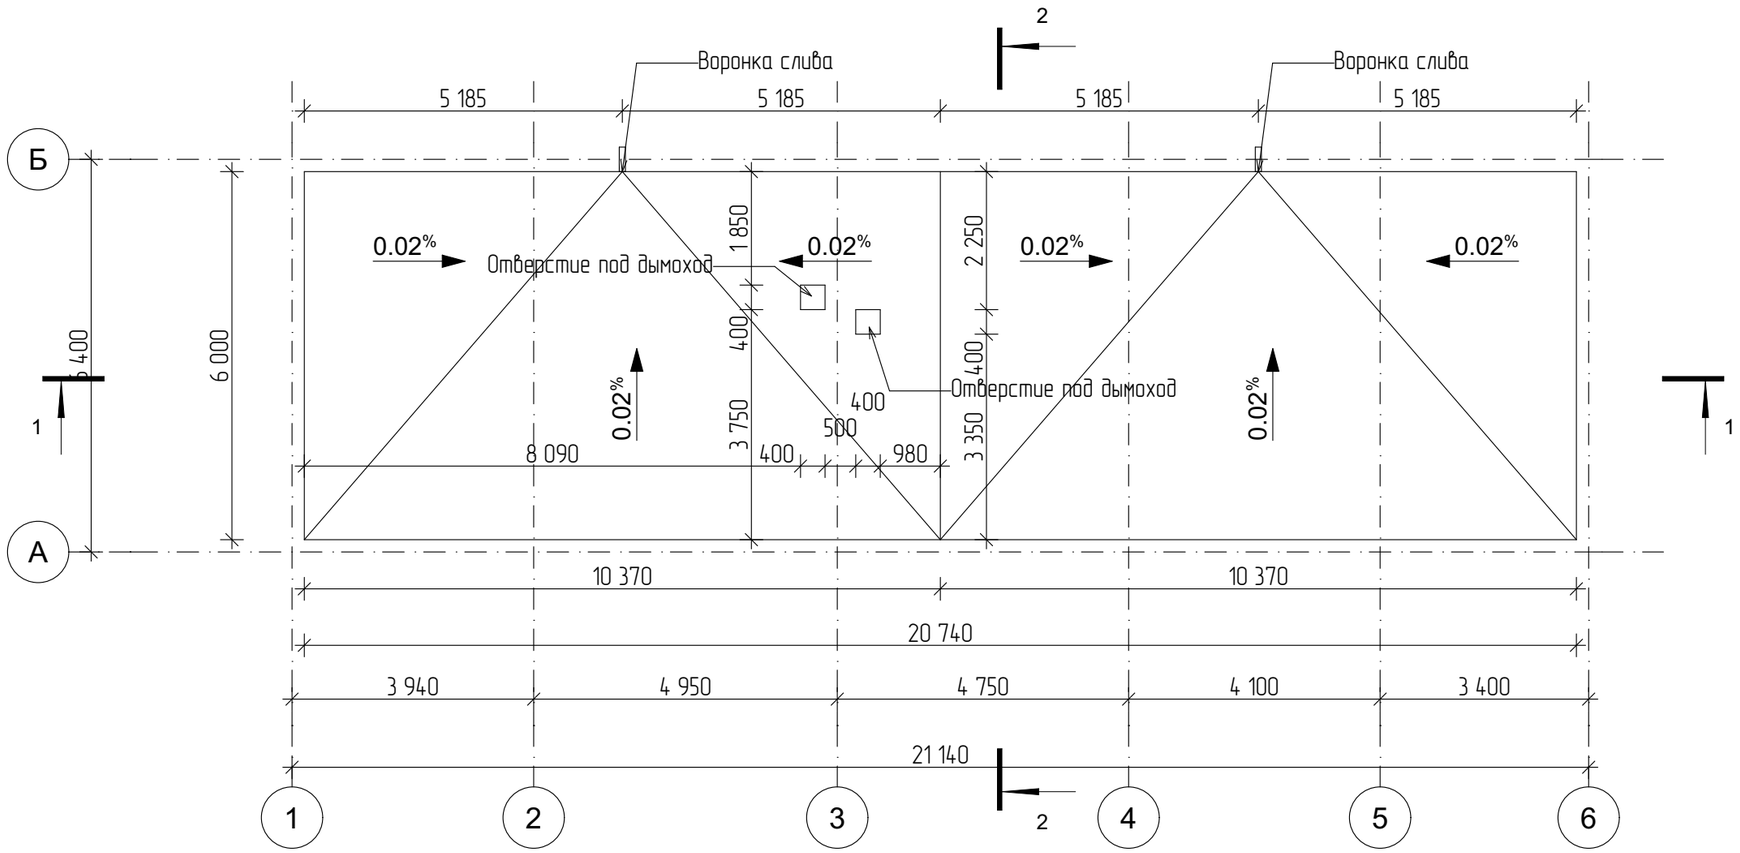

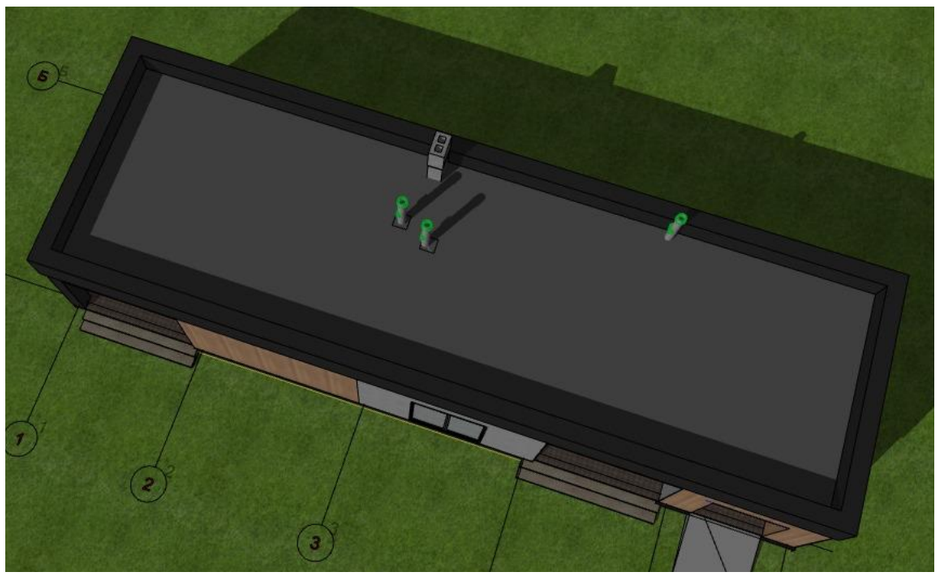

ИКК-03 Кровля	
Наименование	Площадь, м2
Кровля	124,76


Изм.	Кол.уч.	Лист	№Док.	Подп.	Дата	кадастровый номер 63:17:0301011:962, Самарская область, муниципальный район Волжский, городское поселение Смышляевка, поселок городского типа Стройкерамика, улица Александровская роща, земельный участок 104 Россия			
						Индивидуальный жилой дом	Стадия	Лист	Листов
							ЭП	28	
						План кровли			

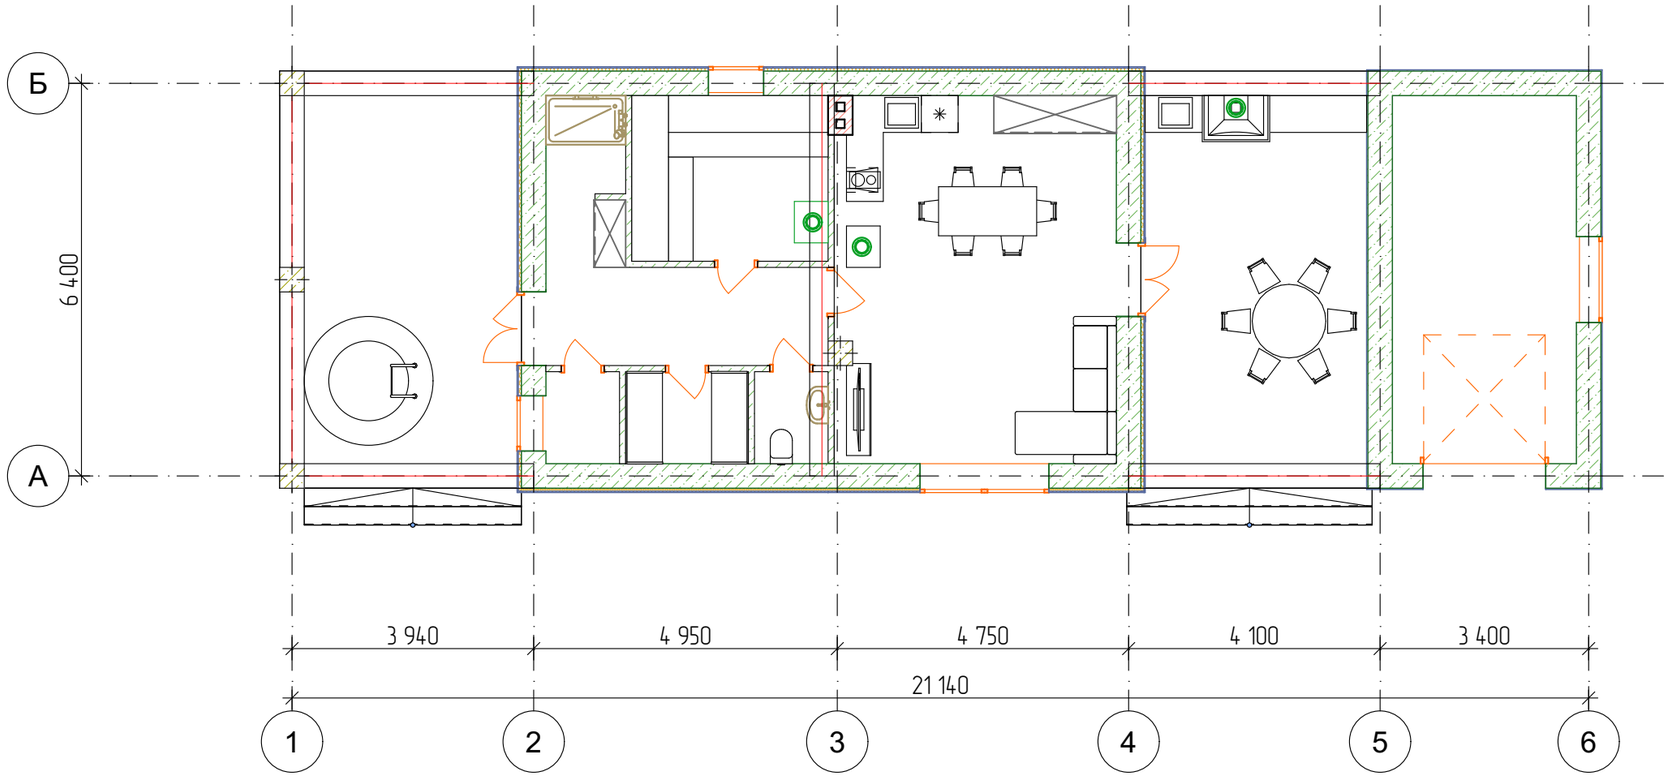

Изм.	Кол.уч.	Лист	№Док.	Подп.	Дата	

кадастровый номер 63:17:0301011:962, Самарская область, муниципальный район Волжский, городское поселение Смышляевка, поселок городского типа Стройкерамика, улица Александровская роща, земельный участок 104 Россия

Индивидуальный жилой дом	Стадия	Лист	Листов
	ЭП	29	
План расстановки мебели 1 этаж			

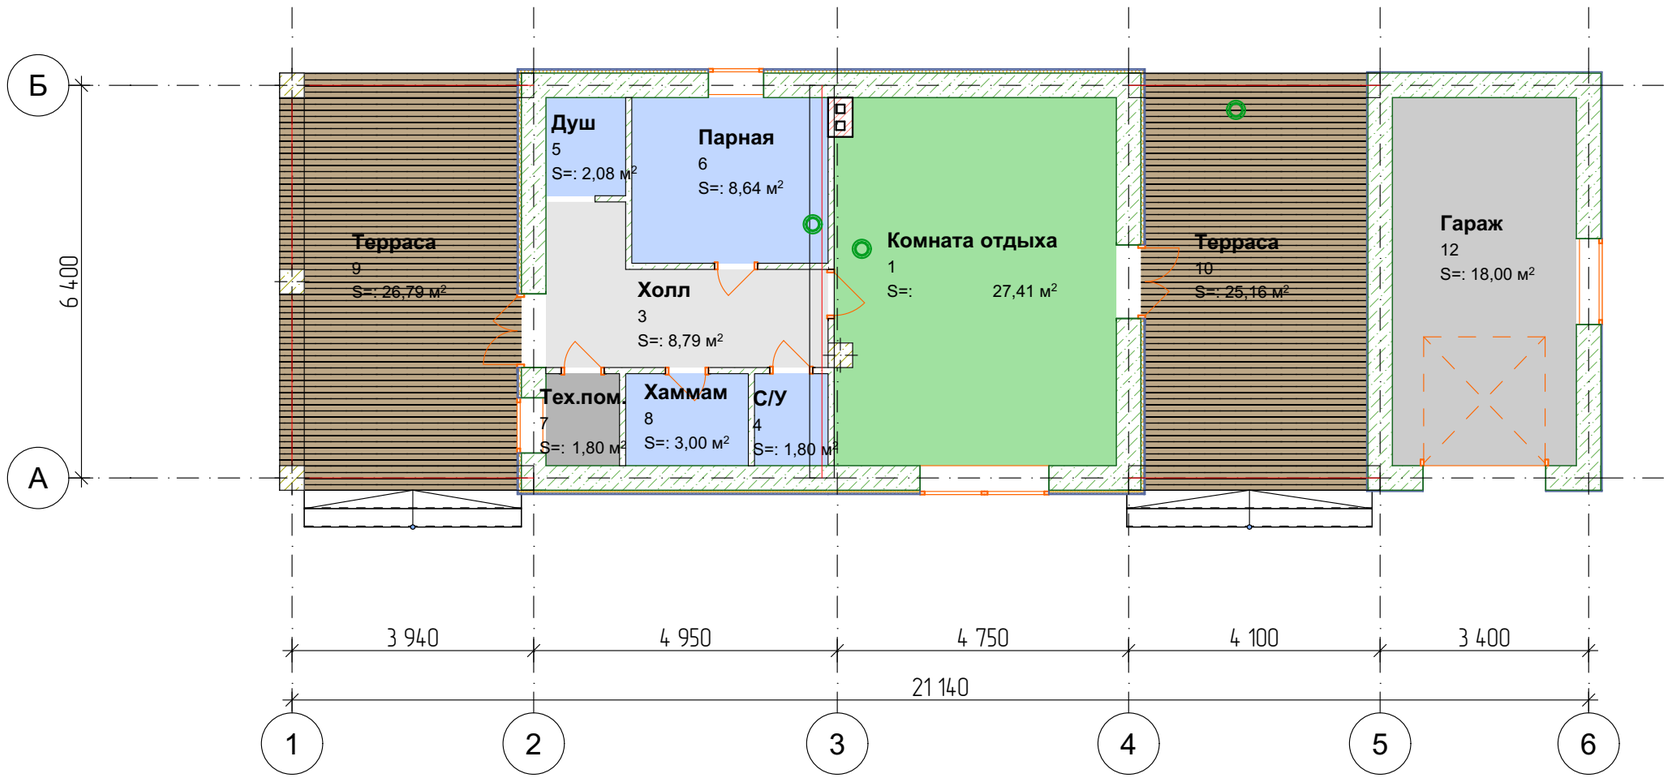

№	Наименование	Площадь
1	Комната отдыха	27,41
3	Холл	8,79
4	С/У	1,80
5	Душ	2,08
6	Парная	8,64
7	Тех.пом.	1,80
8	Хаммам	3,00
9	Терраса	26,79
10	Терраса	25,16
12	Гараж	18,00
		123,47 м²

Изм.	Кол.уч.	Лист	№Док.	Подп.	Дата

кадастровый номер 63:17:0301011:962, Самарская область, муниципальный район Волжский, городское поселение Смышляевка, поселок городского типа Стройкерамика, улица Александровская роща, земельный участок 104 Россия

Индивидуальный жилой дом


Стадия	Лист	Листов
ЭП	30	

Экспликация помещений 1- го этажа




						кадастровый номер 63:17:0301011:962, Самарская область, муниципальный район Волжский, городское поселение Смышляевка, поселок городского типа Стройкерамика, улица Александровская роща, земельный участок 104 Россия
Изм.	Кол.уч.	Лист	№Док.	Подп.	Дата	
						Индивидуальный жилой дом
						3Д разрез


Стадия	Лист	Листов
ЭП	31	

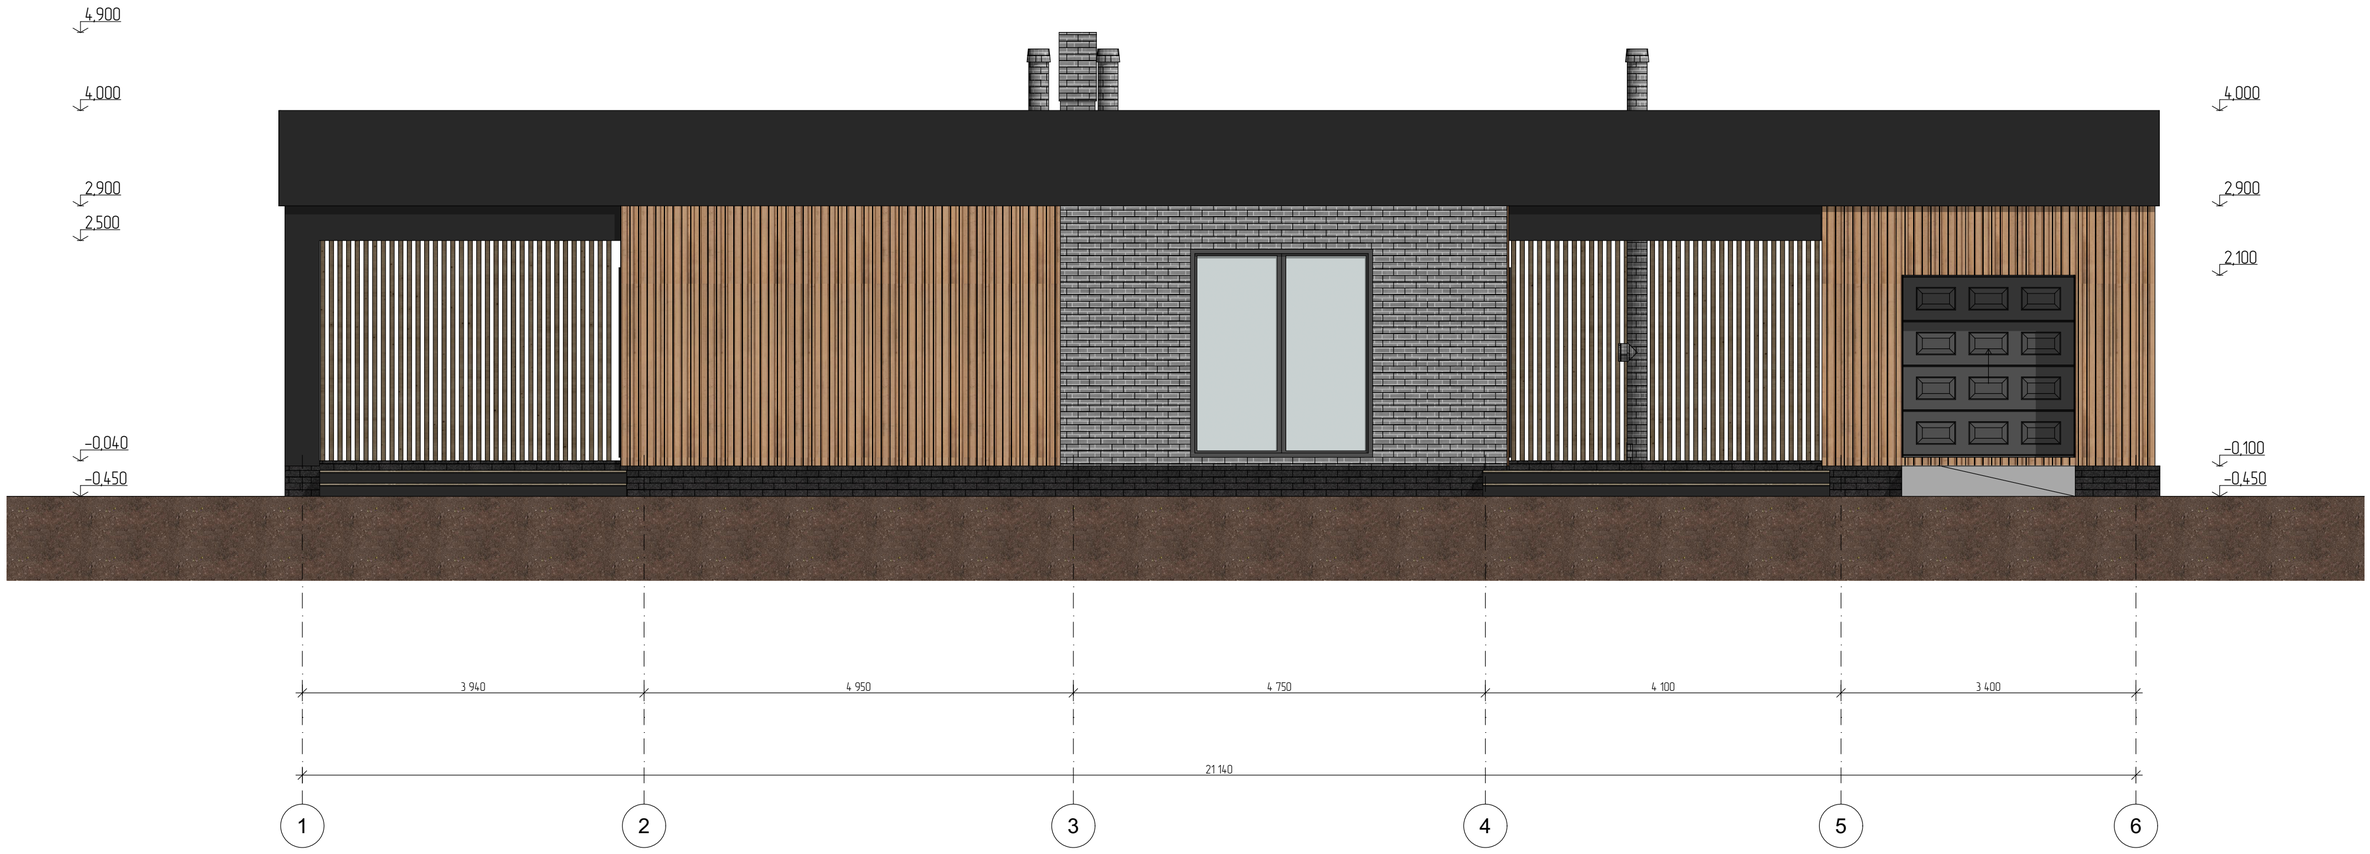


Изм.	Кол.уч.	Лист	№Док.	Подп.	Дата	кадастровый номер 63:17:0301011:962, Самарская область, муниципальный район Волжский, городское поселение Смышляевка, поселок городского типа Стройкерамика, улица Александровская роща, земельный участок 104 Россия			
						Индивидуальный жилой дом	Стадия	Лист	Листов
							ЭП	32	
						Фасад в осях 1-6			

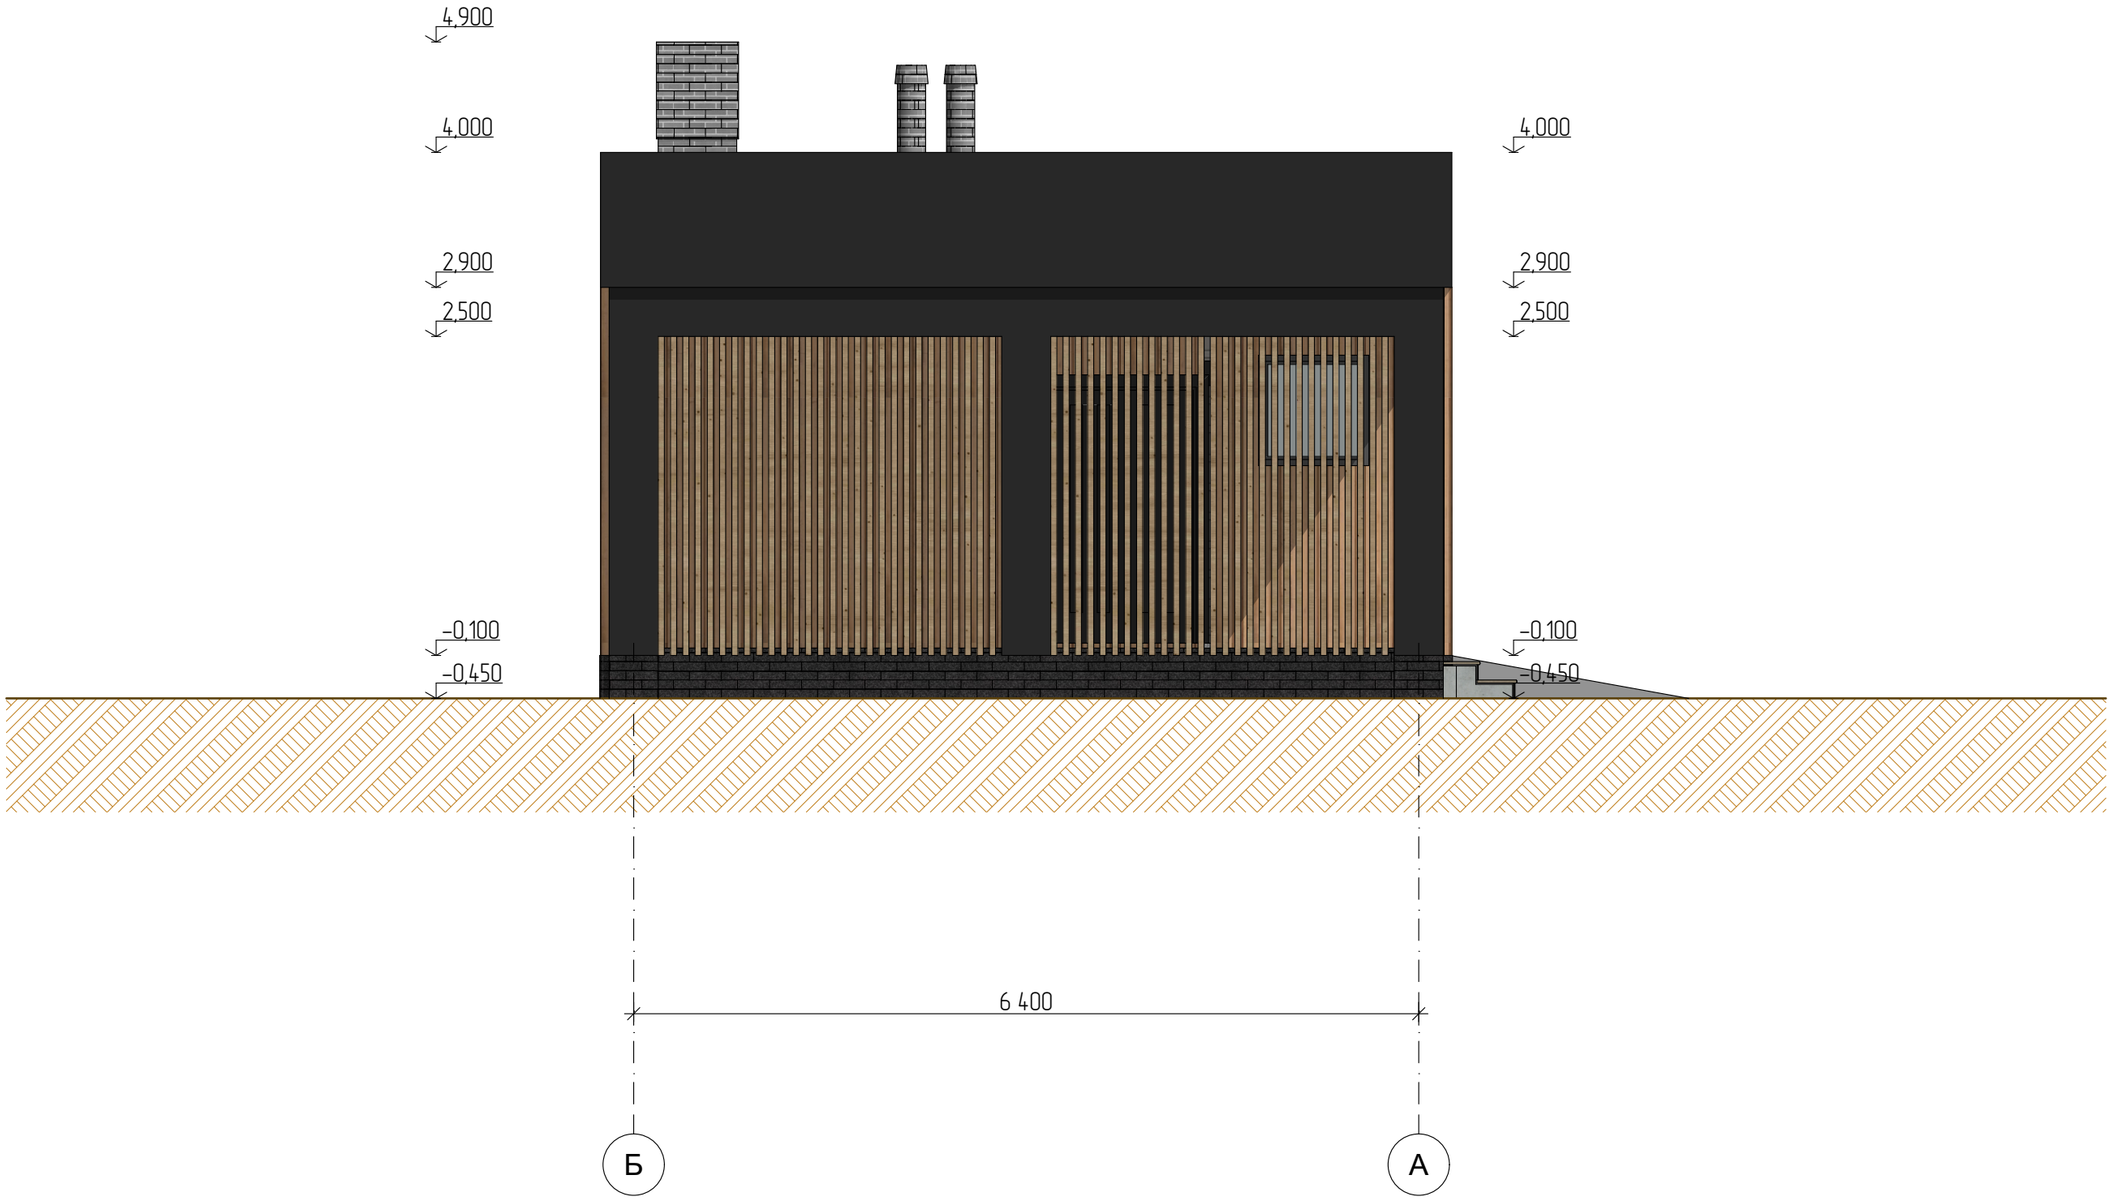

Изм.	Кол.уч.	Лист	№Док.	Подп.	Дата	кадастровый номер 63:17:0301011:962, Самарская область, муниципальный район Волжский, городское поселение Смышляевка, поселок городского типа Стройкерамика, улица Александровская роща, земельный участок 104 Россия			
						Индивидуальный жилой дом	Стадия	Лист	Листов
							ЭП	33	
						Фасад в осях Б-А			

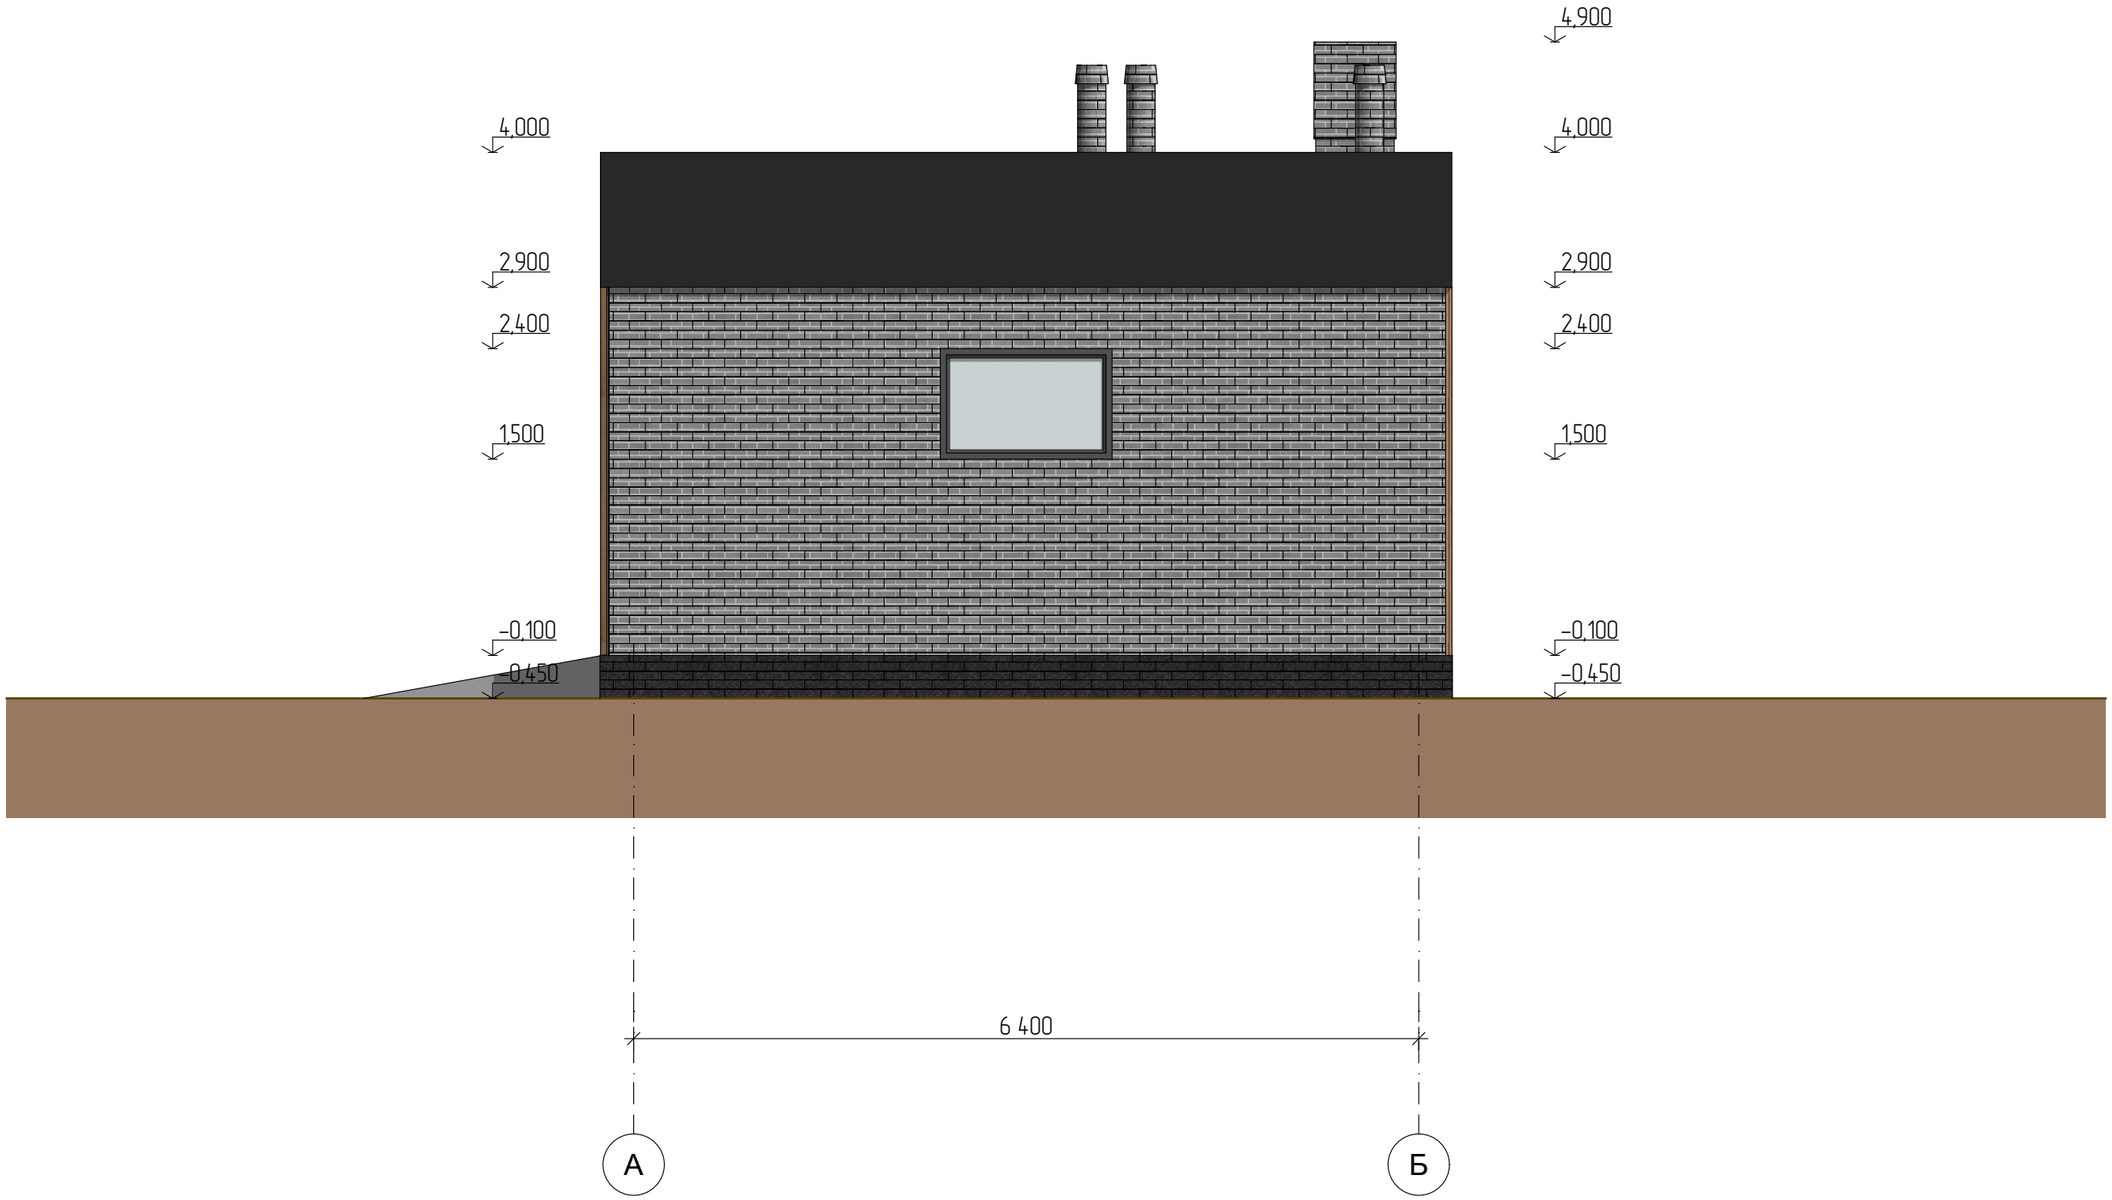

Изм.	Кол.уч.	Лист	№Док.	Подп.	Дата	кадастровый номер 63:17:0301011:962, Самарская область, муниципальный район Волжский, городское поселение Смышляевка, поселок городского типа Стройкерамика, улица Александровская роща, земельный участок 104 Россия			
						Индивидуальный жилой дом	Стадия	Лист	Листов
							ЭП	34	
						Фасад в осях А-Б			

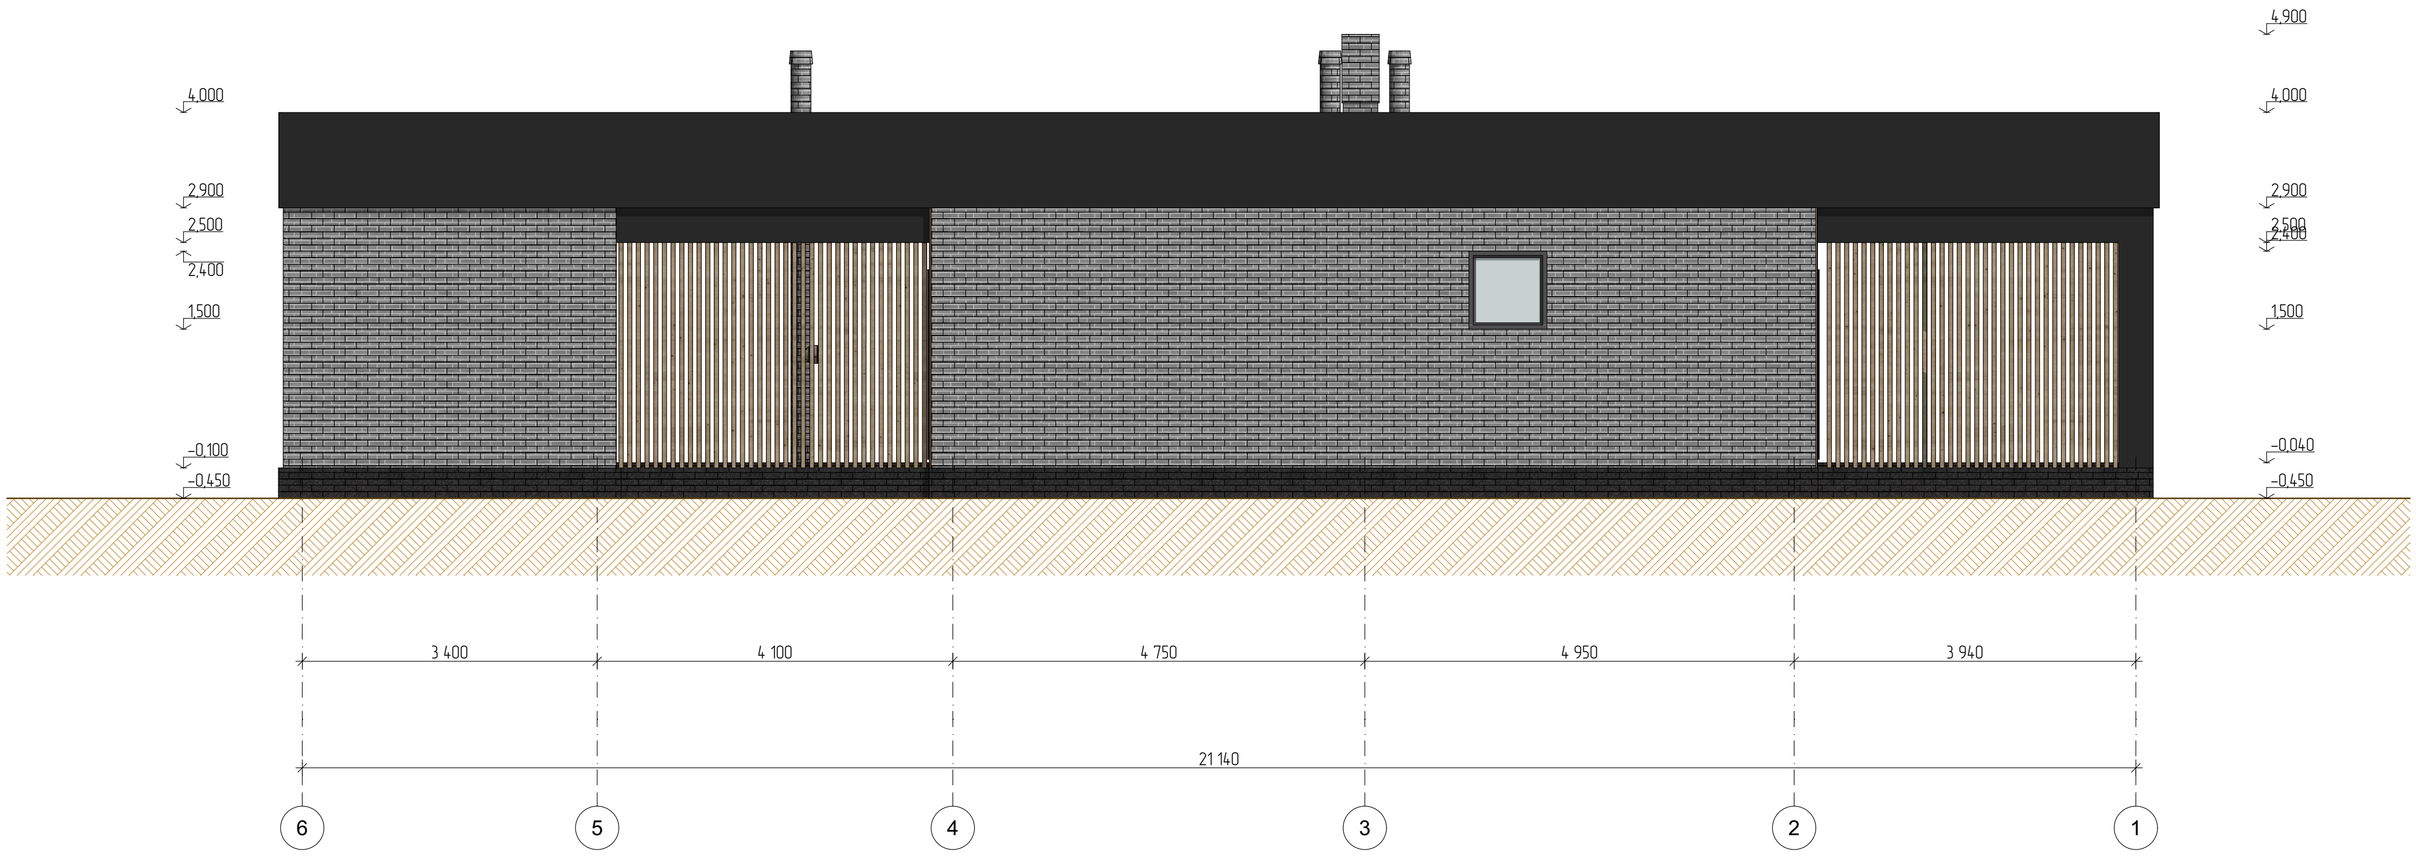

Изм.	Кол.уч.	Лист	№Док.	Подп.	Дата

кадастровый номер 63:17:0301011:962, Самарская область, муниципальный район Волжский, городское поселение Смышляевка, поселок городского типа Стройкерамика, улица Александровская роща, земельный участок 104 Россия

Индивидуальный жилой дом	Стадия	Лист	Листов
	ЭП	35	

Фасад в осях 6-1