ОБЪЕКТ ИНДИВИДУАЛЬНОГО ЖИЛИЩНОГО СТРОИТЕЛЬСТВА



ЭСКИЗНЫЙ ПРОЕКТ

ШИФР: #ID ПРОЕКТА

АРХИТЕКТУРНЫЕ РЕШЕНИЯ

САНКТ-ПЕТЕРБУРГ 2020

ОБЪЕКТ: ОБЪЕКТ ИНДИВИДУАЛЬНОГО ЖИЛИЩНОГО СТРОИТЕЛЬСТВА

ПО АДРЕСУ: #ПОЛНЫЙ АДРЕС ЗАКАЗЧИКА

ЗАКАЗЧИК: _____#ОБРАЩЕНИЕ К ЗАКАЗЧИКУ

АРХИТЕКТОР _____САЛЫКОВА В.Г.

КОНСТРУКТОР _____

ЭСКИЗНЫЙ ПРОЕКТ


ШИФР: #ID ПРОЕКТА

АРХИТЕКТУРНЫЕ РЕШЕНИЯ

САНКТ-ПЕТЕРБУРГ 2020

М 1:100

План 1 этажа с расстановкой мебели

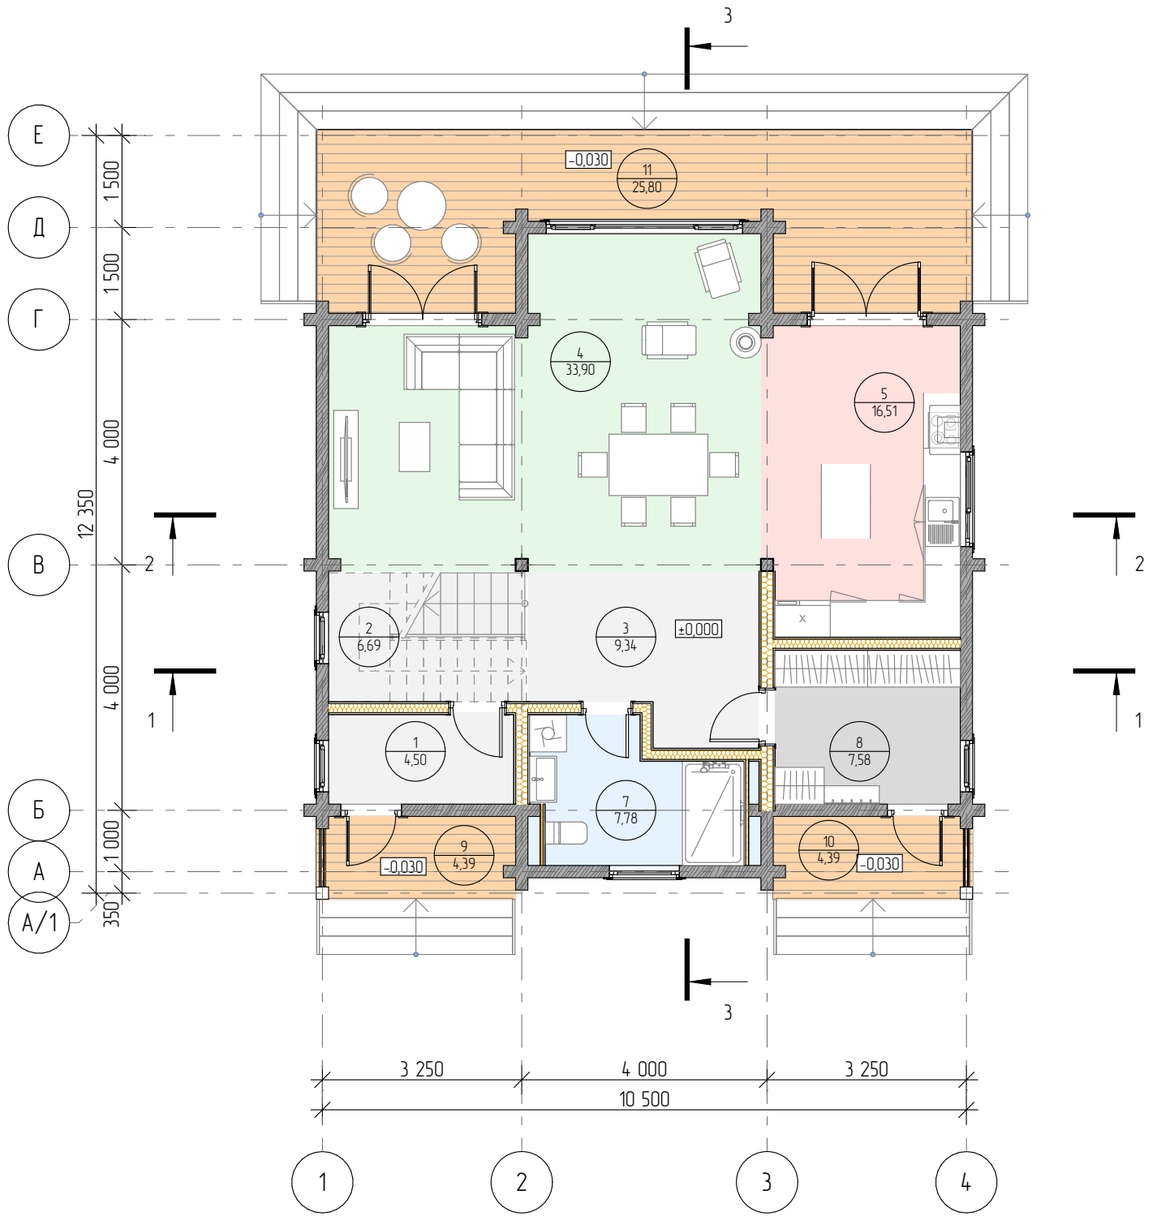

Экспликация 1 этажа

Расположение поиещений	№ п/п	Наименование	Площадь, м2
Внутр. пом.			
	1	Котельная (Электричество)	4,50
	2	Лестничный пролет	6,69
	3	Холл	9,34
	4	Гостиная	33,90
	5	Кухня	16,51
	7	Санузел	7,78
	8	Тамбур	7,58
			86,30 м²
Наружн. пом.			
	9	Крыльцо 1	4,39
	10	Крыльцо 2	4,39
	11	Терраса	25,80
			34,58 м²
			120,88 м²

Согласовано:

Взам. инв. №

Подпись и дата

Инв. № подл.

					2020
Изм.	Кол.уч	Лист	№док.	Подпись	Дата

#ID Проекта


Адрес: #Полный Адрес Участка; к/н #ID Участка

Индивидуальный жилой дом	стадия	лист	листов
	ЭП	2	
План 1 этажа с расстановкой мебели М 1:100			

Архитектор	Салыкова В.Г.
Конструктор	
Заказчик	#Обращение к Заказчику

М 1:100

План 2 этажа с расстановкой мебели

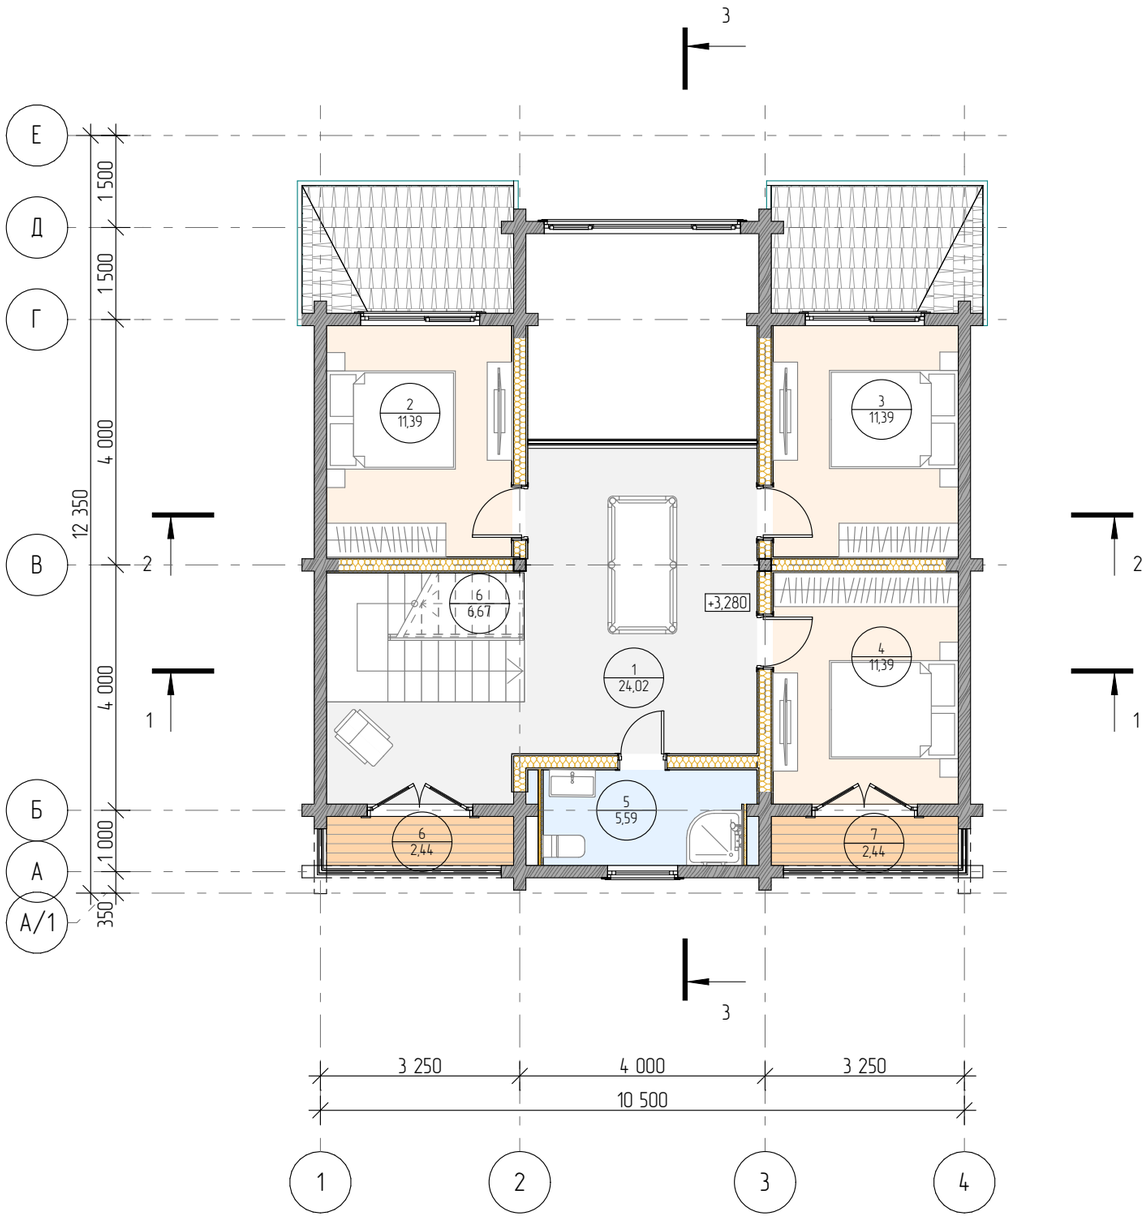

Экспликация 2 этажа

Расположение поиещений	№ п/п	Наименование	Площадь, м2
Внутр. пом.			
	1	Холл	24,02
	2	Спальня	11,39
	3	Спальня	11,39
	4	Спальня	11,39
	5	Санузел	5,59
	6	Лестничный пролет	6,67
			70,45 м²
Наружн. пом.			
	6	Балкон 1	2,44
	7	Балкон 2	2,44
			4,88 м²
			75,33 м²

Примечание:

1) За отметку +3,300 принята отметка чистового пола второго этажа
2) Толщина каркасных перегородок показана без учета отделочных материалов
3) Расположение вентиляционных коммуникаций и прочих инженерных систем показано условно. Проект инженерных коммуникаций будет разрабатываться при заключении договора на инженерные работы. Количество и наличие вентиляционных, фановых и дымовых труб определяется дополнительным согласованием в сметном расчёте на этапе отделочных работ.
4) Габаритные размеры и расположение печи/камина могут измениться в процессе строительства
5) Ответственность за конструктивное решение и расположение печи/камина относительно несущих деревянных конструкций, фундамента, а также соблюдение мер пожарной безопасности при сооружении и эксплуатации печи/камина, полностью лежат на Заказчике

Изм.	Кол.уч	Лист	№док.	Подпись	Дата	2020	#ID Проекта			
							Адрес: #Полный Адрес Участка; к/н #ID Участка			
							Индивидуальный жилой дом	стадия	лист	листов
								ЭП	3	
Архитектор		Салыкова В.Г.					План 2 этажа с расстановкой мебели М 1:100			
Конструктор										
Заказчик		#Обращение к Заказчику								

Согласовано:

Взам. инв. №


Подпись и дата

Инв. № подл.

Фасад 1-4



Фасад Е-А

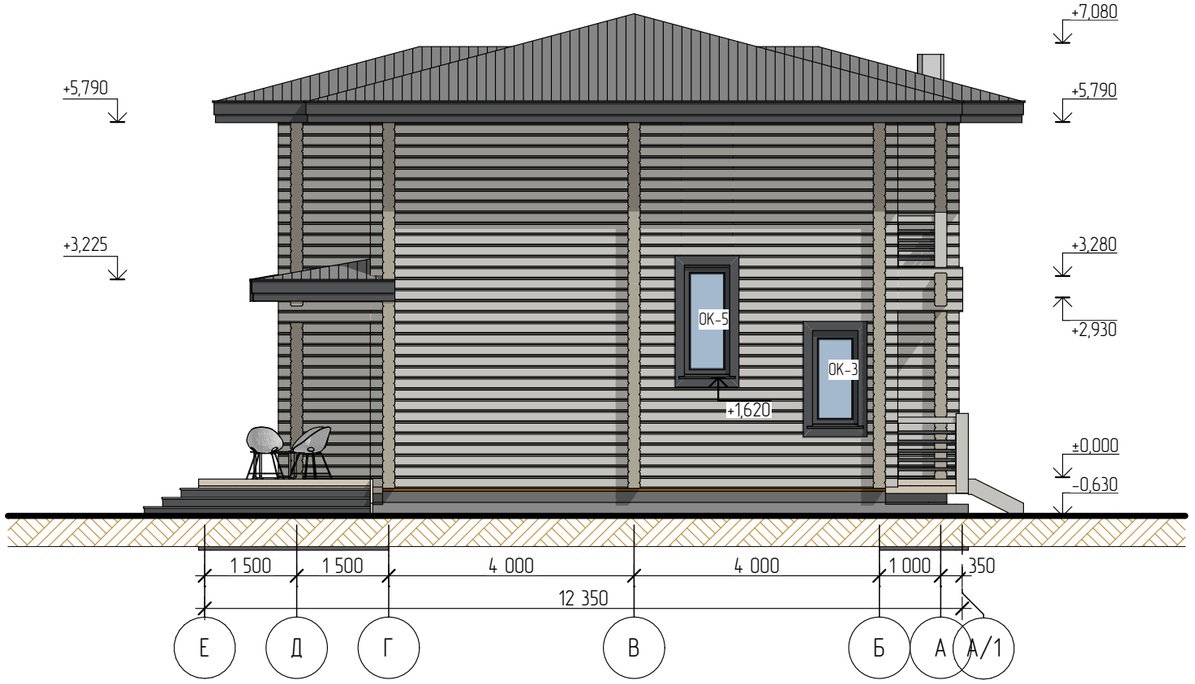

Примечание:
1) За отметку +0,000 принята отметка чистового пола первого этажа
2) За отметку +3,100 принята отметка чистового пола второго этажа
3) Номинальные высотные размеры могут отличаться от фактических в силу технологической усадки стенового комплекта и принимаемых отделочных материалов.
4) Несущие перевязки из бруса могут быть ниже основного уровня потолка
5) Высота фундамента дана без учета перепада. Замер перепада производится на участке при выезде инженера. Изменение габаритов и типа фундаментов согласовывается дополнительным согласованием по смете.
6) Все декоративные элементы показаны условно.

					2020	#ID Проекта			
						Адрес: #Полный Адрес Участка; к/н #ID Участка			
Изм.	Кол.уч	Лист	№док.	Подпись	Дата				
						Индивидуальный жилой дом	стадия	лист	листов
							ЭП	4	
Архитектор		Салыкова В.Г.							
Конструктор						Фасады М 1:100			
Заказчик		#Обращение к Заказчику							


Согласовано:

Взам. инв. №


Подпись и дата

Инв. № подл.

Фасад А-Е

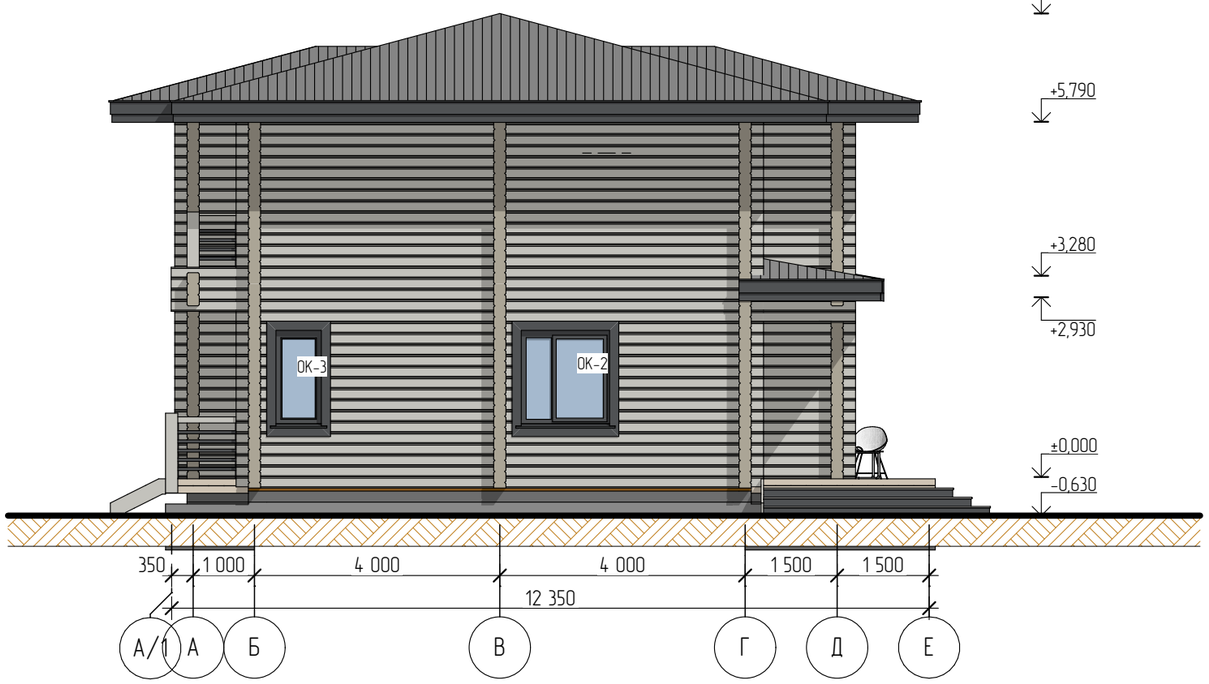

Фасад 4-1

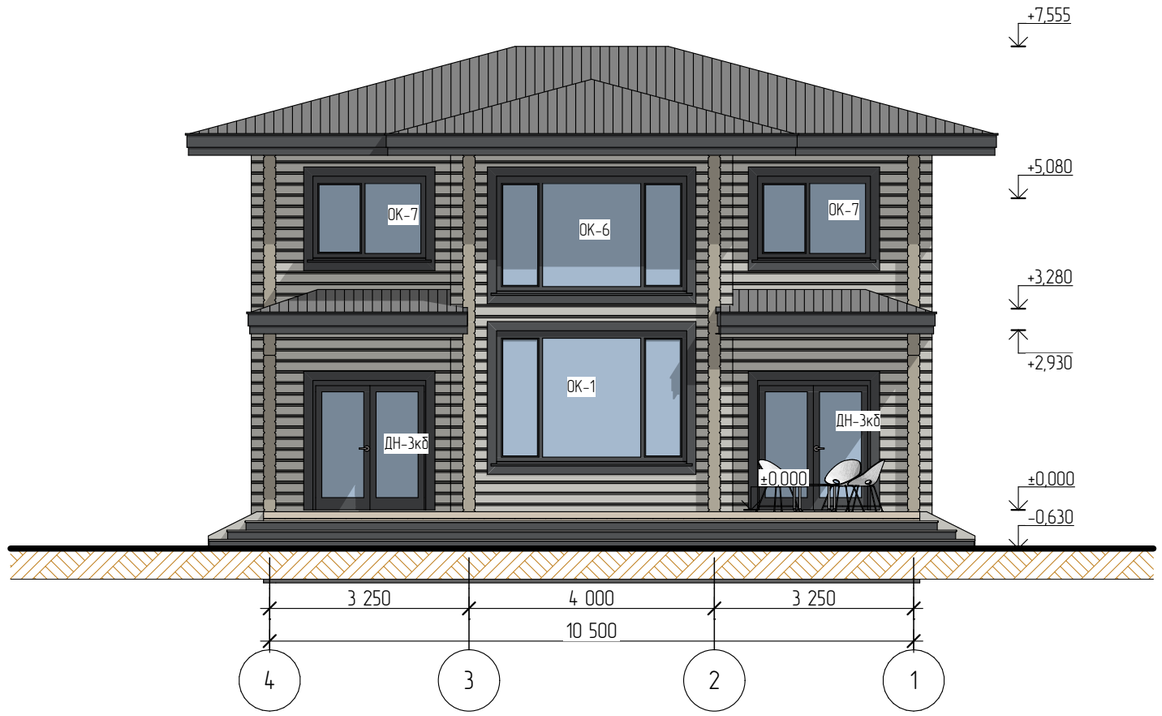

Примечание:
1) За отметку +0,000 принята отметка чистового пола первого этажа
2) За отметку +3,100 принята отметка чистового пола второго этажа
3) Номинальные высотные размеры могут отличаться от фактических в силу технологической усадки стенового комплекта и принимаемых отделочных материалов.
4) Несущие перевязки из бруса могут быть ниже основного уровня потолка
5) Высота фундамента дана без учета перепада. Замер перепада производится на участке при выезде инженера. Изменение габаритов и типа фундаментов согласовывается дополнительным согласованием по смете.
6) Все декоративные элементы показаны условно.

					2020	#ID Проекта			
						Адрес: #Полный Адрес Участка; к/н #ID Участка			
Изм.	Кол.уч	Лист	№док.	Подпись	Дата				
						Индивидуальный жилой дом	стадия	лист	листов
							ЭП	5	
Архитектор		Салыкова В.Г.							
Конструктор									
Заказчик		#Обращение к				Фасады М 1:100			
		Заказчику							

Согласовано:


Взам. инв. №

Подпись и дата

Инв. № подл.

1:75

Разрез 1-1

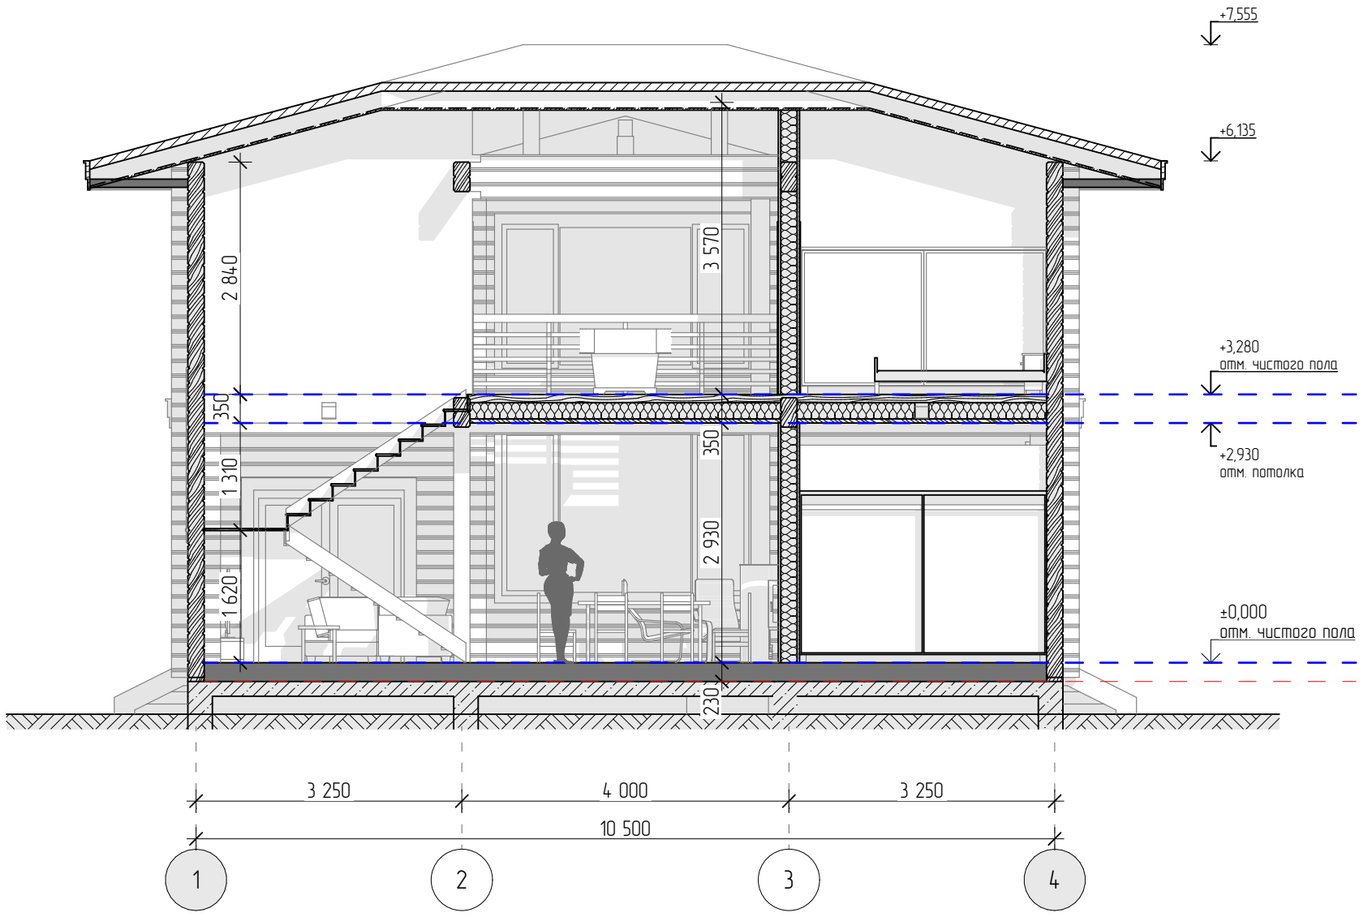

Примечание:

1) За отметку +0,000 принята отметка чистового пола первого этажа
2) За отметку +3,100 принята отметка чистового пола второго этажа
3) Номинальные высотные размеры могут отличаться от фактических в силу технологической усадки стенового комплекта и принимаемых отделочных материалов.
4) Несущие перевязки из бруса могут быть ниже основного уровня потолка
5) Высота фундамента дана без учета перепада. Замер перепада производится на участке при выезде инженера. Изменение габаритов и типа фундаментов согласовывается дополнительным согласованием по смете.
6) Все декоративные элементы показаны условно.

					2020	#ID Проекта			
						Адрес: #Полный Адрес Участка; к/н #ID Участка			
Изм.	Кол.уч	Лист	№док.	Подпись	Дата				
						Индивидуальный жилой дом	стадия	лист	листов
							ЭП	6	
Архитектор		Салыкова В.Г.							
Конструктор						Разрез 1-1 М 1:75			
Заказчик		#Обращение к Заказчику							

Согласовано:


Взам. инв. №

Подпись и дата

Инв. № подл.

1:75

Разрез 2-2

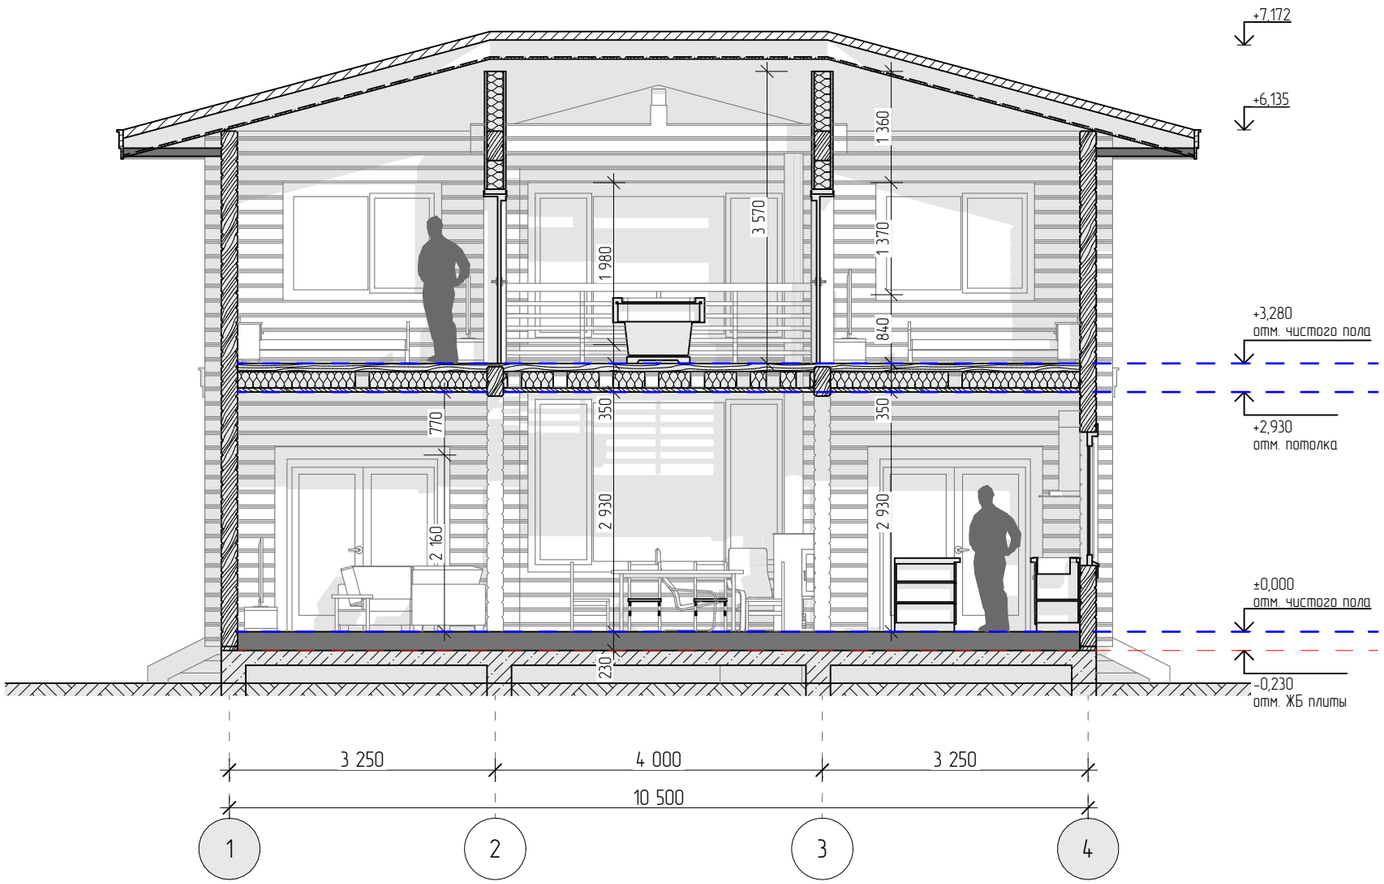

Примечание:

1) За отметку +0,000 принята отметка чистового пола первого этажа
2) За отметку +3,100 принята отметка чистового пола второго этажа
3) Номинальные высотные размеры могут отличаться от фактических в силу технологической усадки стенового комплекта и принимаемых отделочных материалов.
4) Несущие перевязки из бруса могут быть ниже основного уровня потолка
5) Высота фундамента дана без учета перепада. Замер перепада производится на участке при выезде инженера. Изменение габаритов и типа фундаментов согласовывается дополнительным согласованием по смете.
6) Все декоративные элементы показаны условно.

					2020	#ID Проекта			
						Адрес: #Полный Адрес Участка; к/н #ID Участка			
Изм.	Кол.уч	Лист	№док.	Подпись	Дата				
						Индивидуальный жилой дом	стадия	лист	листов
							ЭП	7	
Архитектор		Салыкова В.Г.							
Конструктор						Разрез 2-2 М 1:75			
Заказчик		#Обращение к Заказчику							

Согласовано:


Взам. инв. №

Подпись и дата

Инв. № подл.

1:75

Разрез 3-3

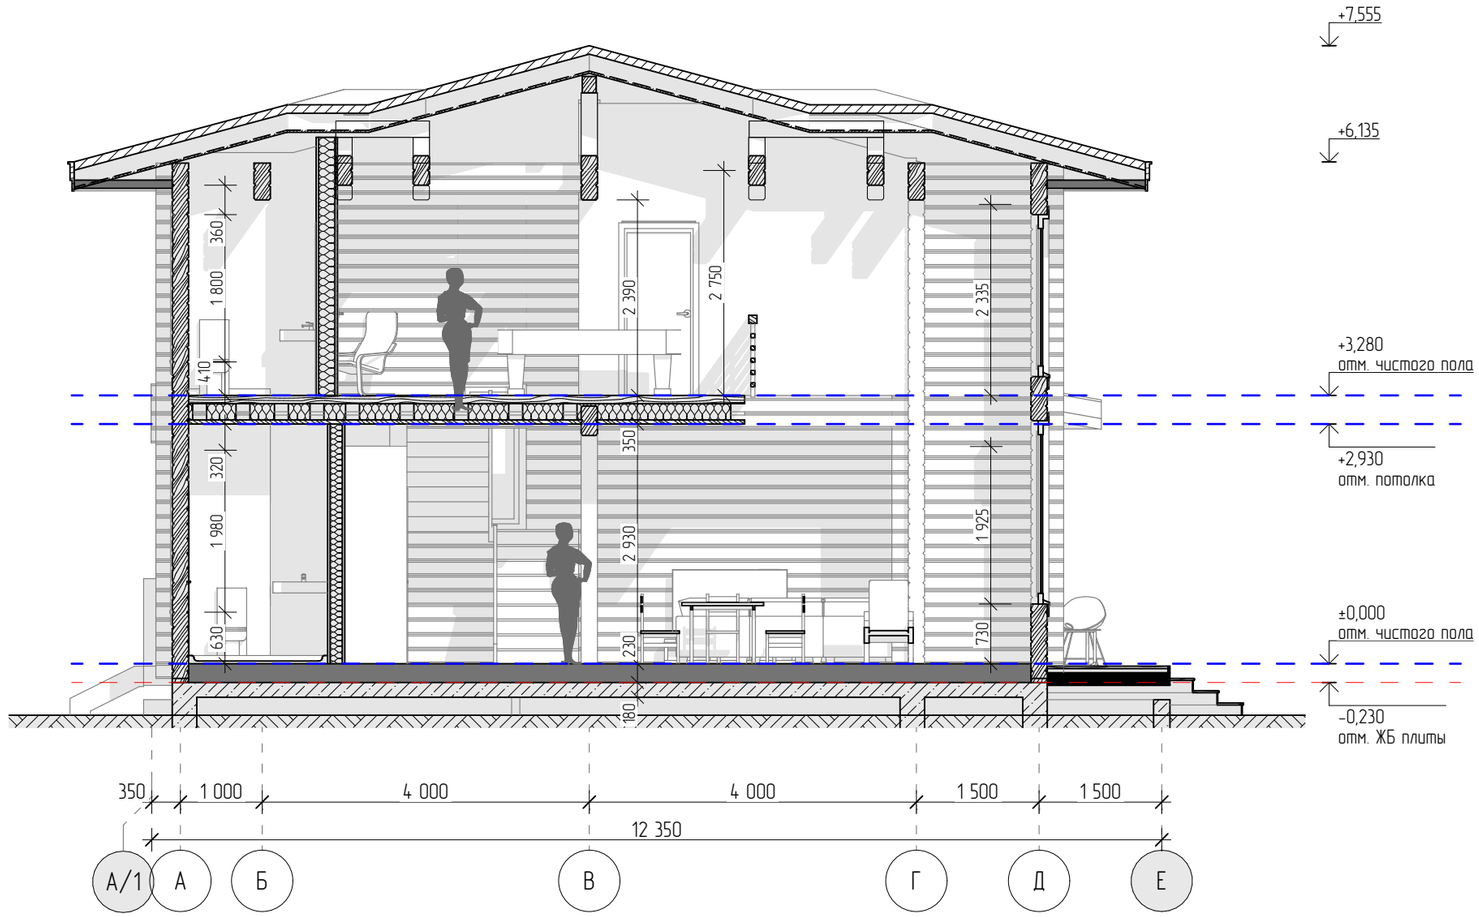

Примечание:

1) За отметку +0,000 принята отметка чистового пола первого этажа
2) За отметку +3,100 принята отметка чистового пола второго этажа
3) Номинальные высотные размеры могут отличаться от фактических в силу технологической усадки стенового комплекта и принимаемых отделочных материалов.
4) Несущие перевязки из бруса могут быть ниже основного уровня потолка
5) Высота фундамента дана без учета перепада. Замер перепада производится на участке при выезде инженера. Изменение габаритов и типа фундаментов согласовывается дополнительным согласованием по смете.
6) Все декоративные элементы показаны условно.

					2020	#ID Проекта		
						Адрес: #Полный Адрес Участка; к/н #ID Участка		
Изм.	Кол.уч	Лист	№док.	Подпись	Дата			
						Индивидуальный жилой дом	стадия	лист	листов
							ЭП	8	
Архитектор		Салыкова В.Г.							
Конструктор						Разрез 3-3 М 1:75			
Заказчик		#Обращение к Заказчику							

Согласовано:

Взам. инв. №

Подпись и дата

Инв. № подл.

Вид 1



Вид 4



Вид 3



Вид 2



Согласовано

Взам. инв. №

Подпись и дата

Инв. № подл.

Общие виды

Лист

АР_Новоселький А_9

Общий вид 1 этаж



Общий вид 2 этаж



Общий вид 2 этаж



Общий вид 1 этаж



Общие виды (поэтажные)

Лист
АР_Новоселький
А_10

Согласовано

Взам. инв. №

Подпись и дата

Инв. № подл.