

М 1:100

Кладочный план 1 этаж

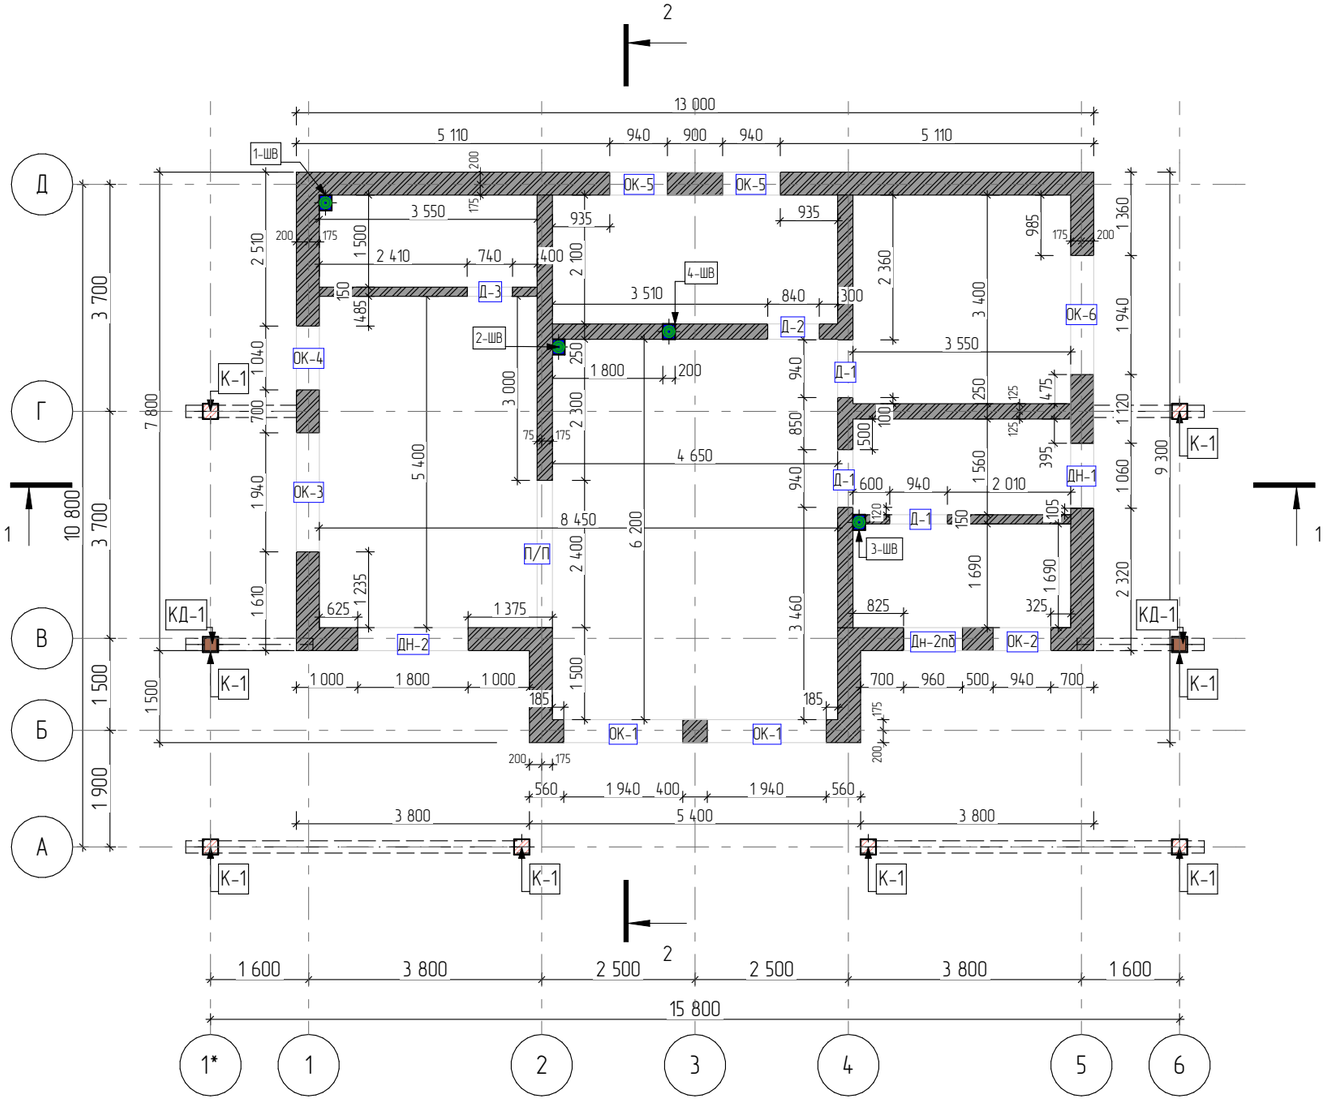



М 1:150

Диагонали 1 этаж

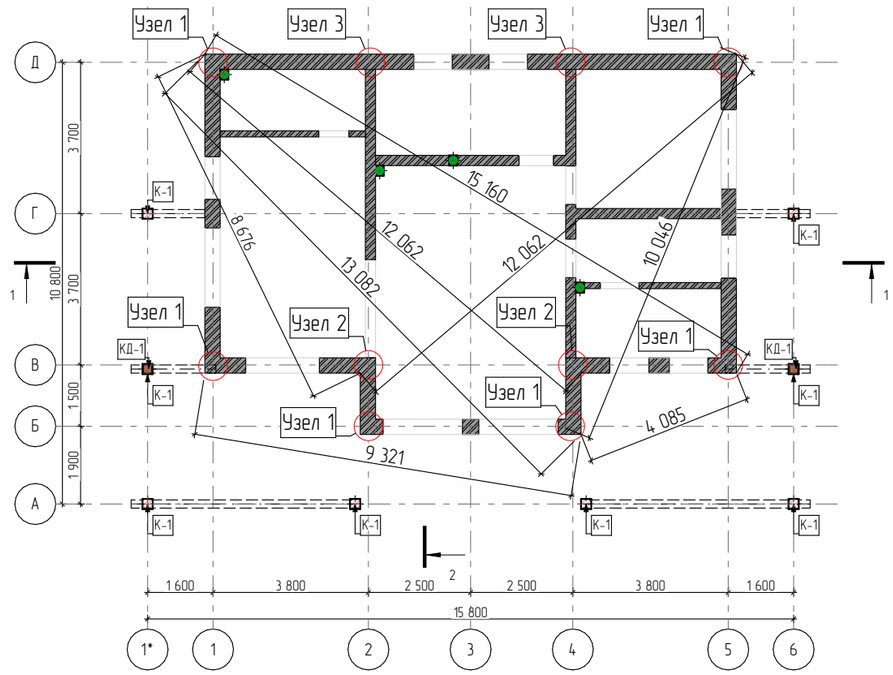



Узел 1

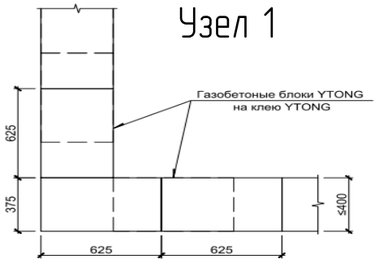

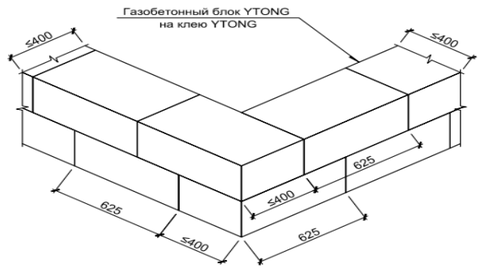


Узел 2

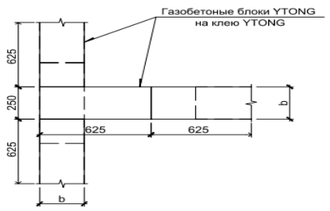

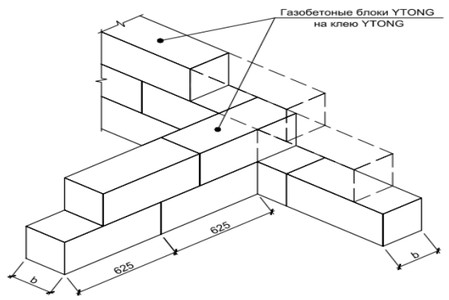

Узел 3

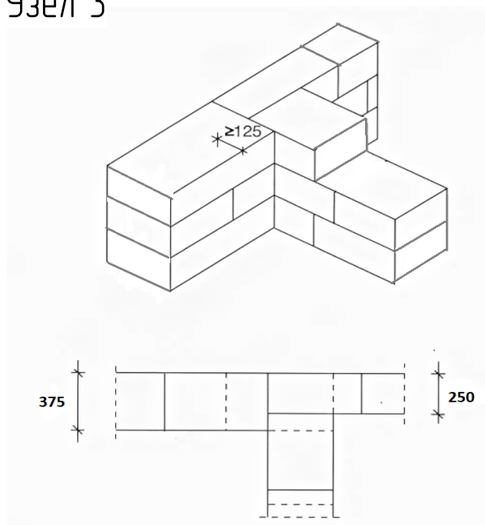

					2021	#ID Проекта	
						Адрес: #Полный Адрес Участка; к/н: #ID Участка	
Изм.	Кол.уч	Лист	№док.	Подпись	Дата		
						Индивидуальный жилой дом	стадия: ЭП; лист: .1; листов:
Архитектор		Салыкова В.Г.					
Заказчик		#Обращение к Заказчику				Кладочный план 1 этаж М 1:100	

Согласовано:


Взам. инв. №

Подпись и дата

Инв. № подл.


М 1:100

Кладочный план 2 этаж

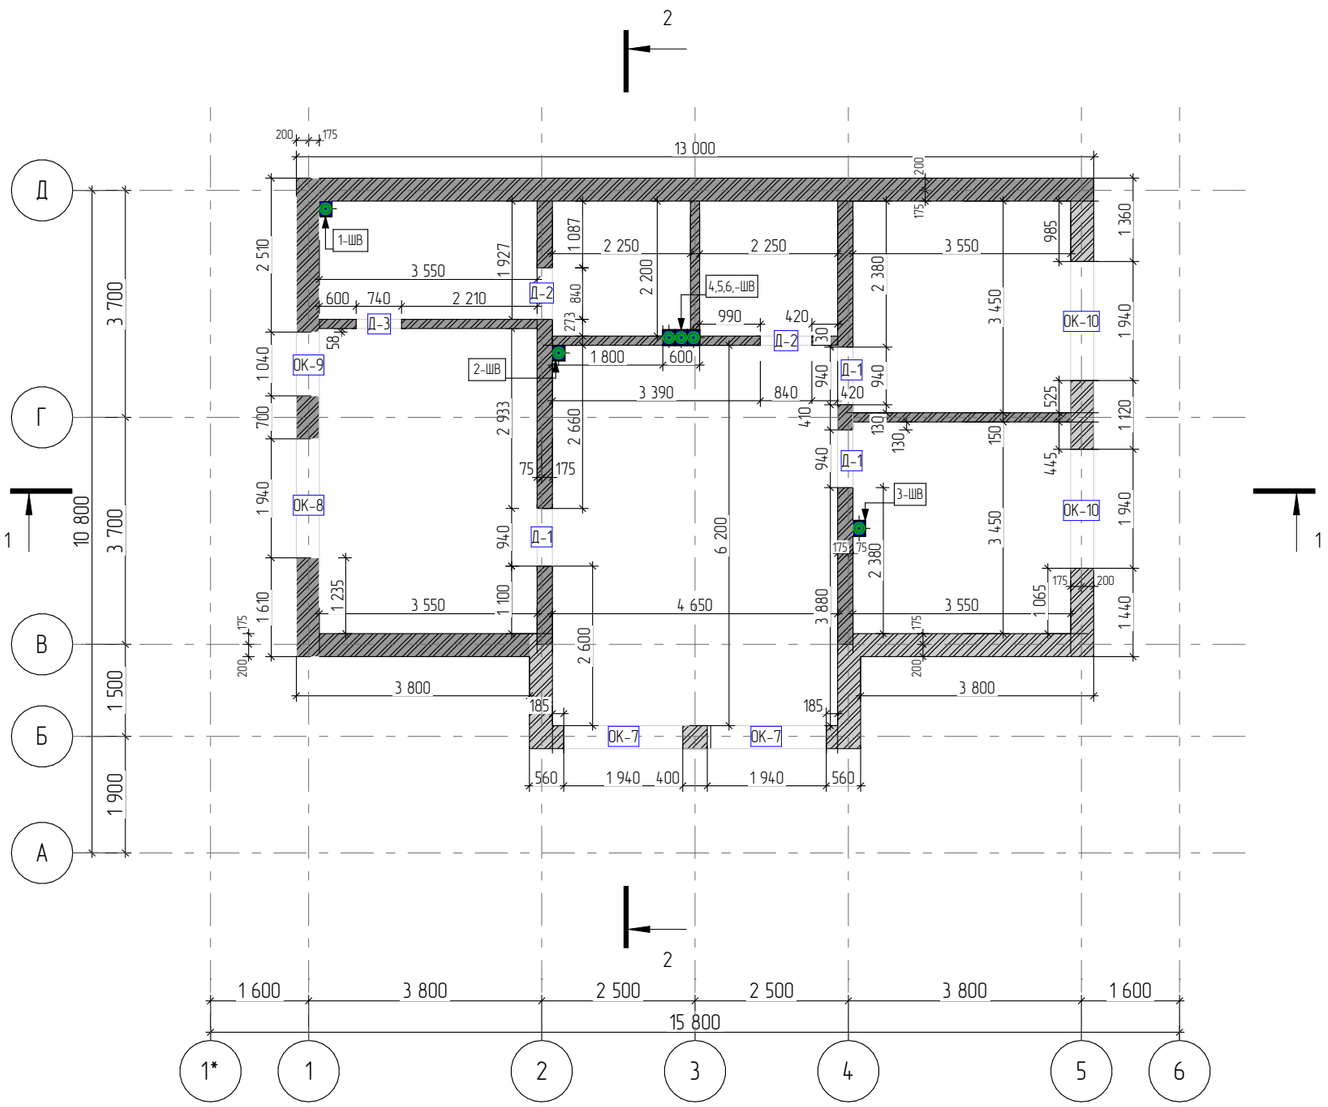

М 1:150

Диагонали 2 этаж

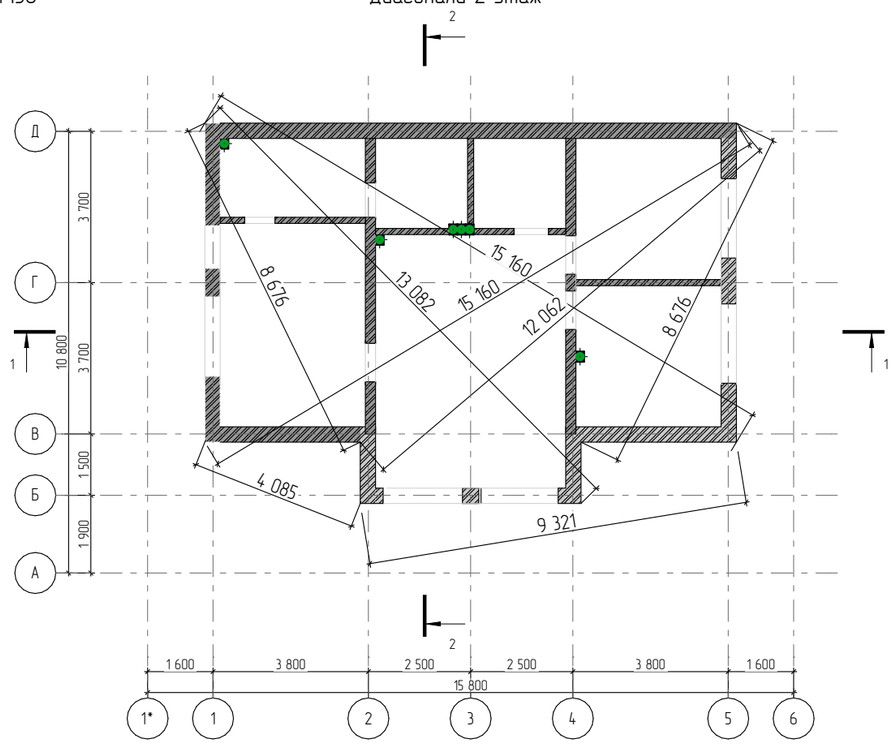

Согласовано:

Взам. инв. №

Подпись и дата


Инв. № подл.

					2021	#ID Проекта	
						Адрес: #Полный Адрес Участка; к/н: #ID Участка	
Изм.	Кол.уч	Лист	№док.	Подпись	Дата		
						Индивидуальный жилой дом	стадия: ЭП; лист: 2; листов:
Архитектор		Салыкова В.Г.					
Заказчик		#Обращение к Заказчику				Кладочный план 2 этаж М 1:100	

М 1:50

разрез

Стена 1

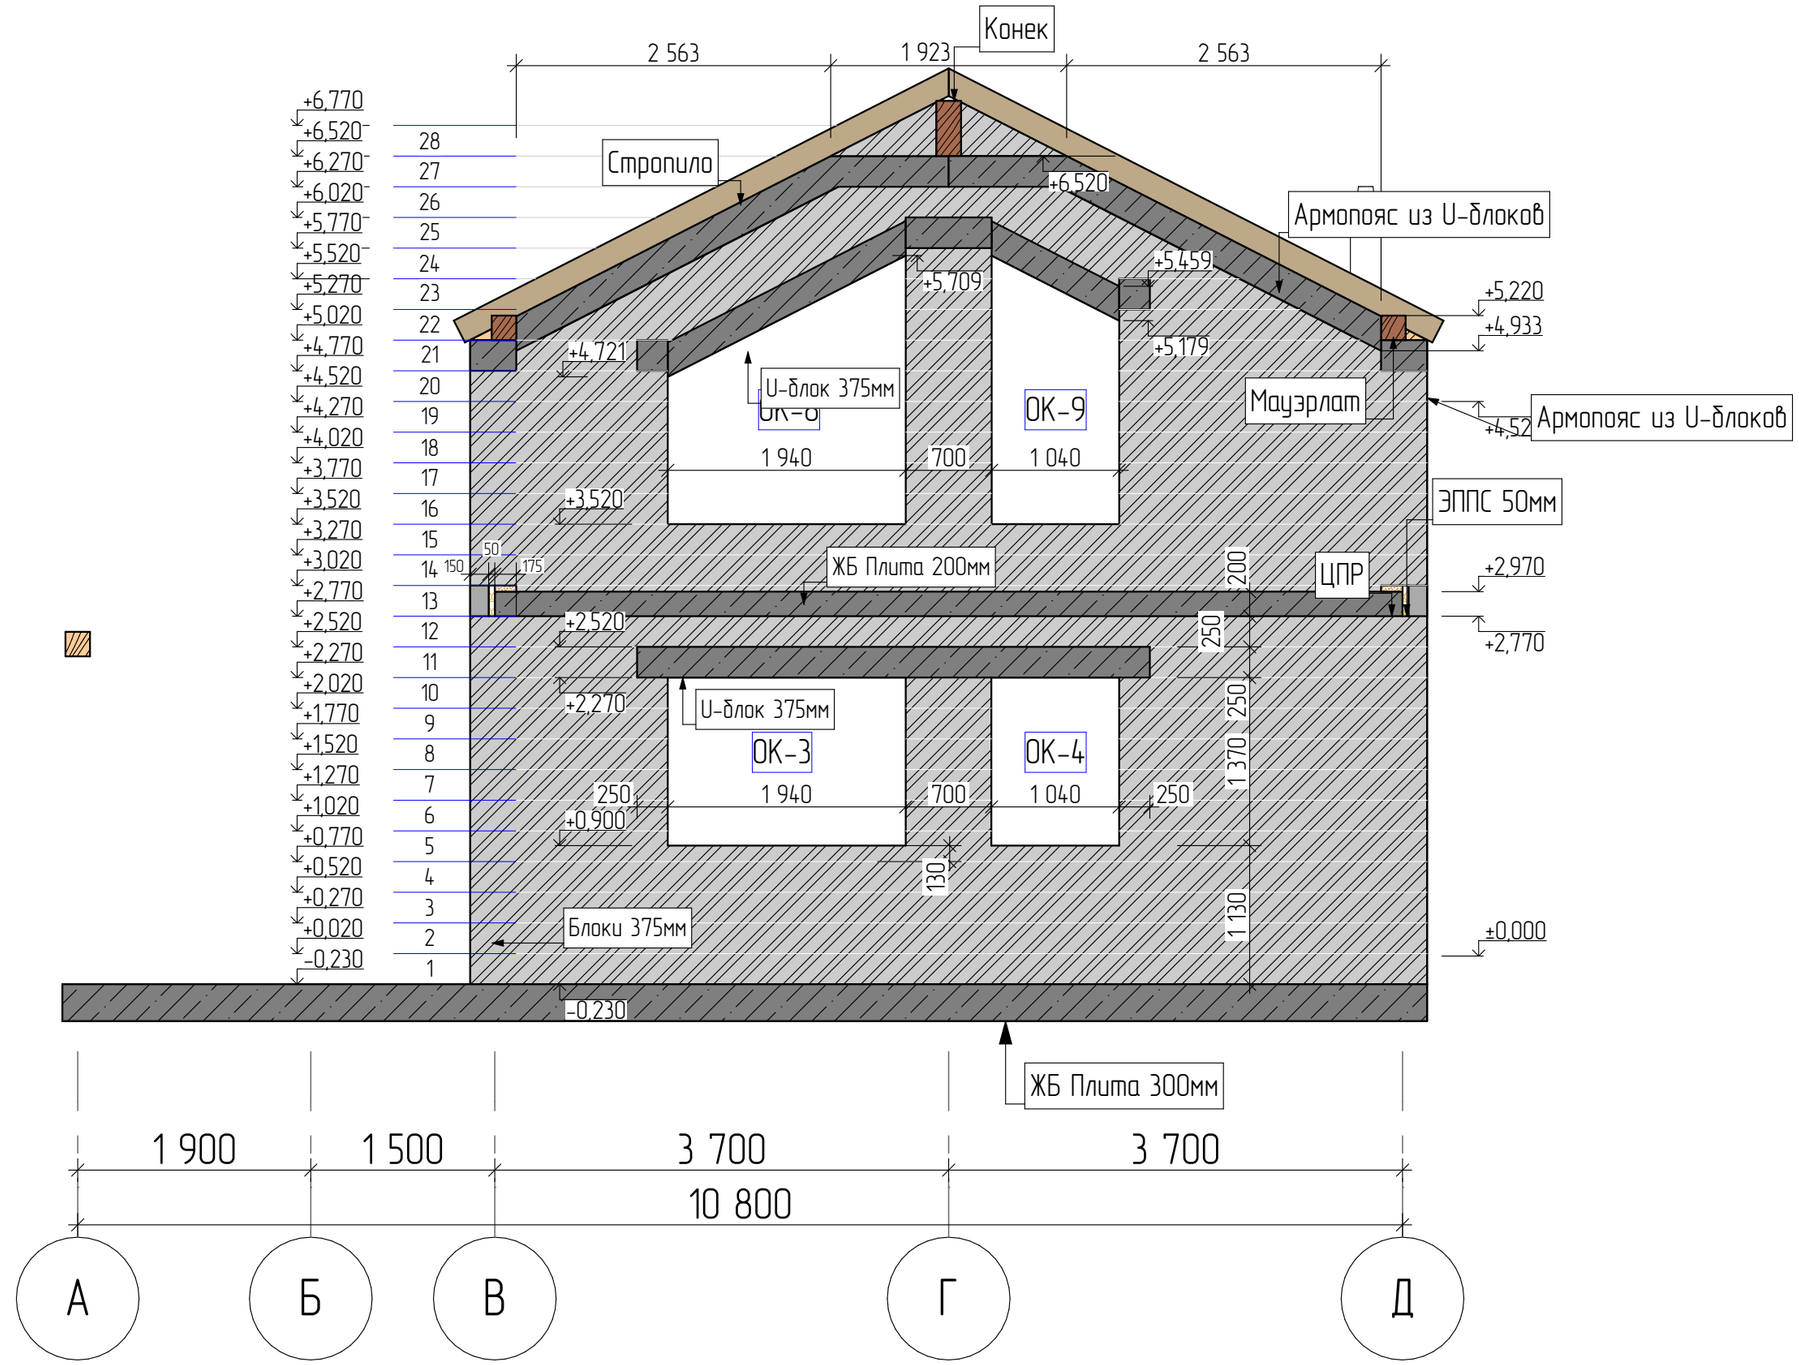

Согласовано

Взам. инв. №

Подпись и дата


Инв. № подл.

Стена 1 М1:50	Лист 3

М 1:50

разрез

Стена 2

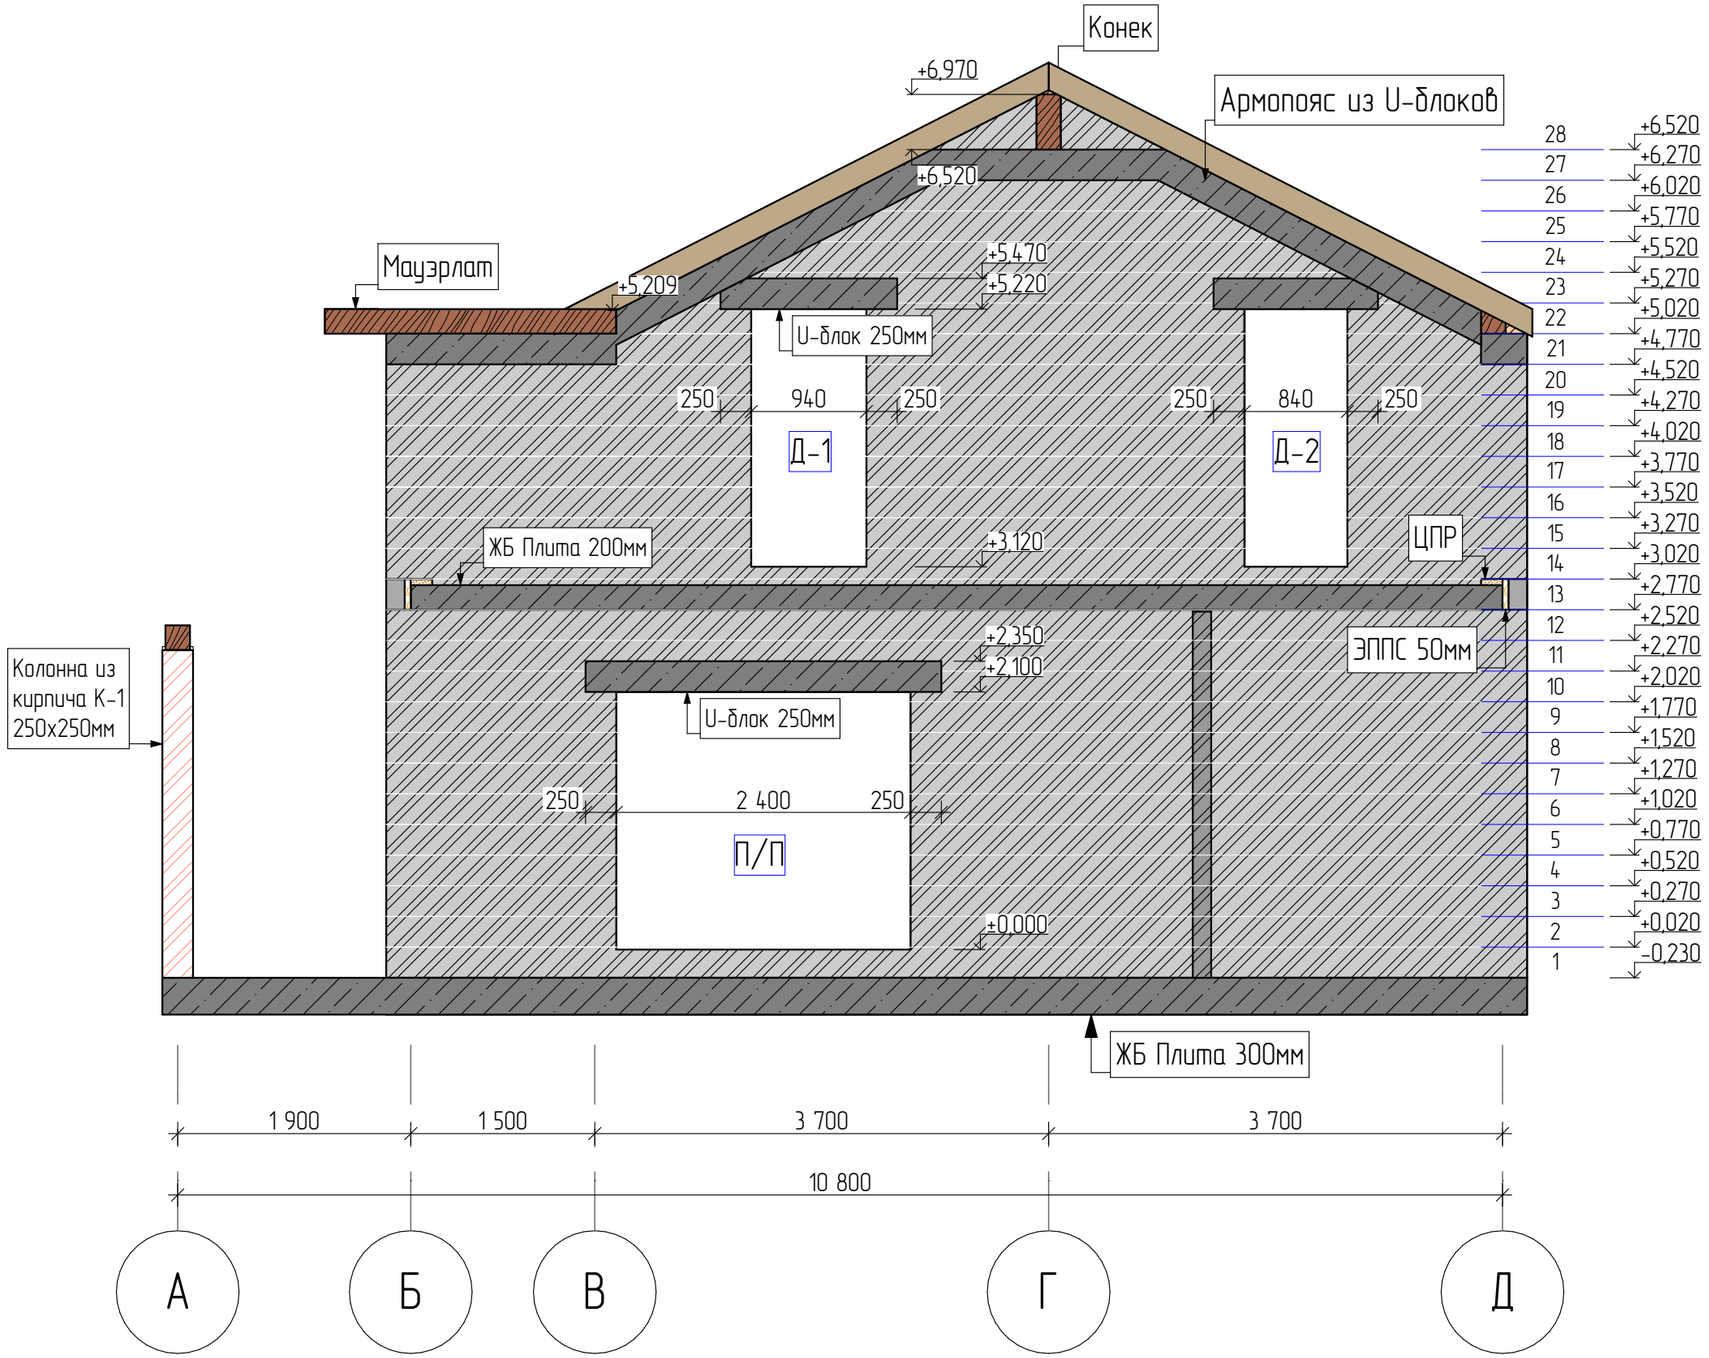

Согласовано

Взам. инв. №

Подпись и дата

Инв. № подл.


Стена 2 М1:50

Лист 4

М 1:50

разрез

Стена 4

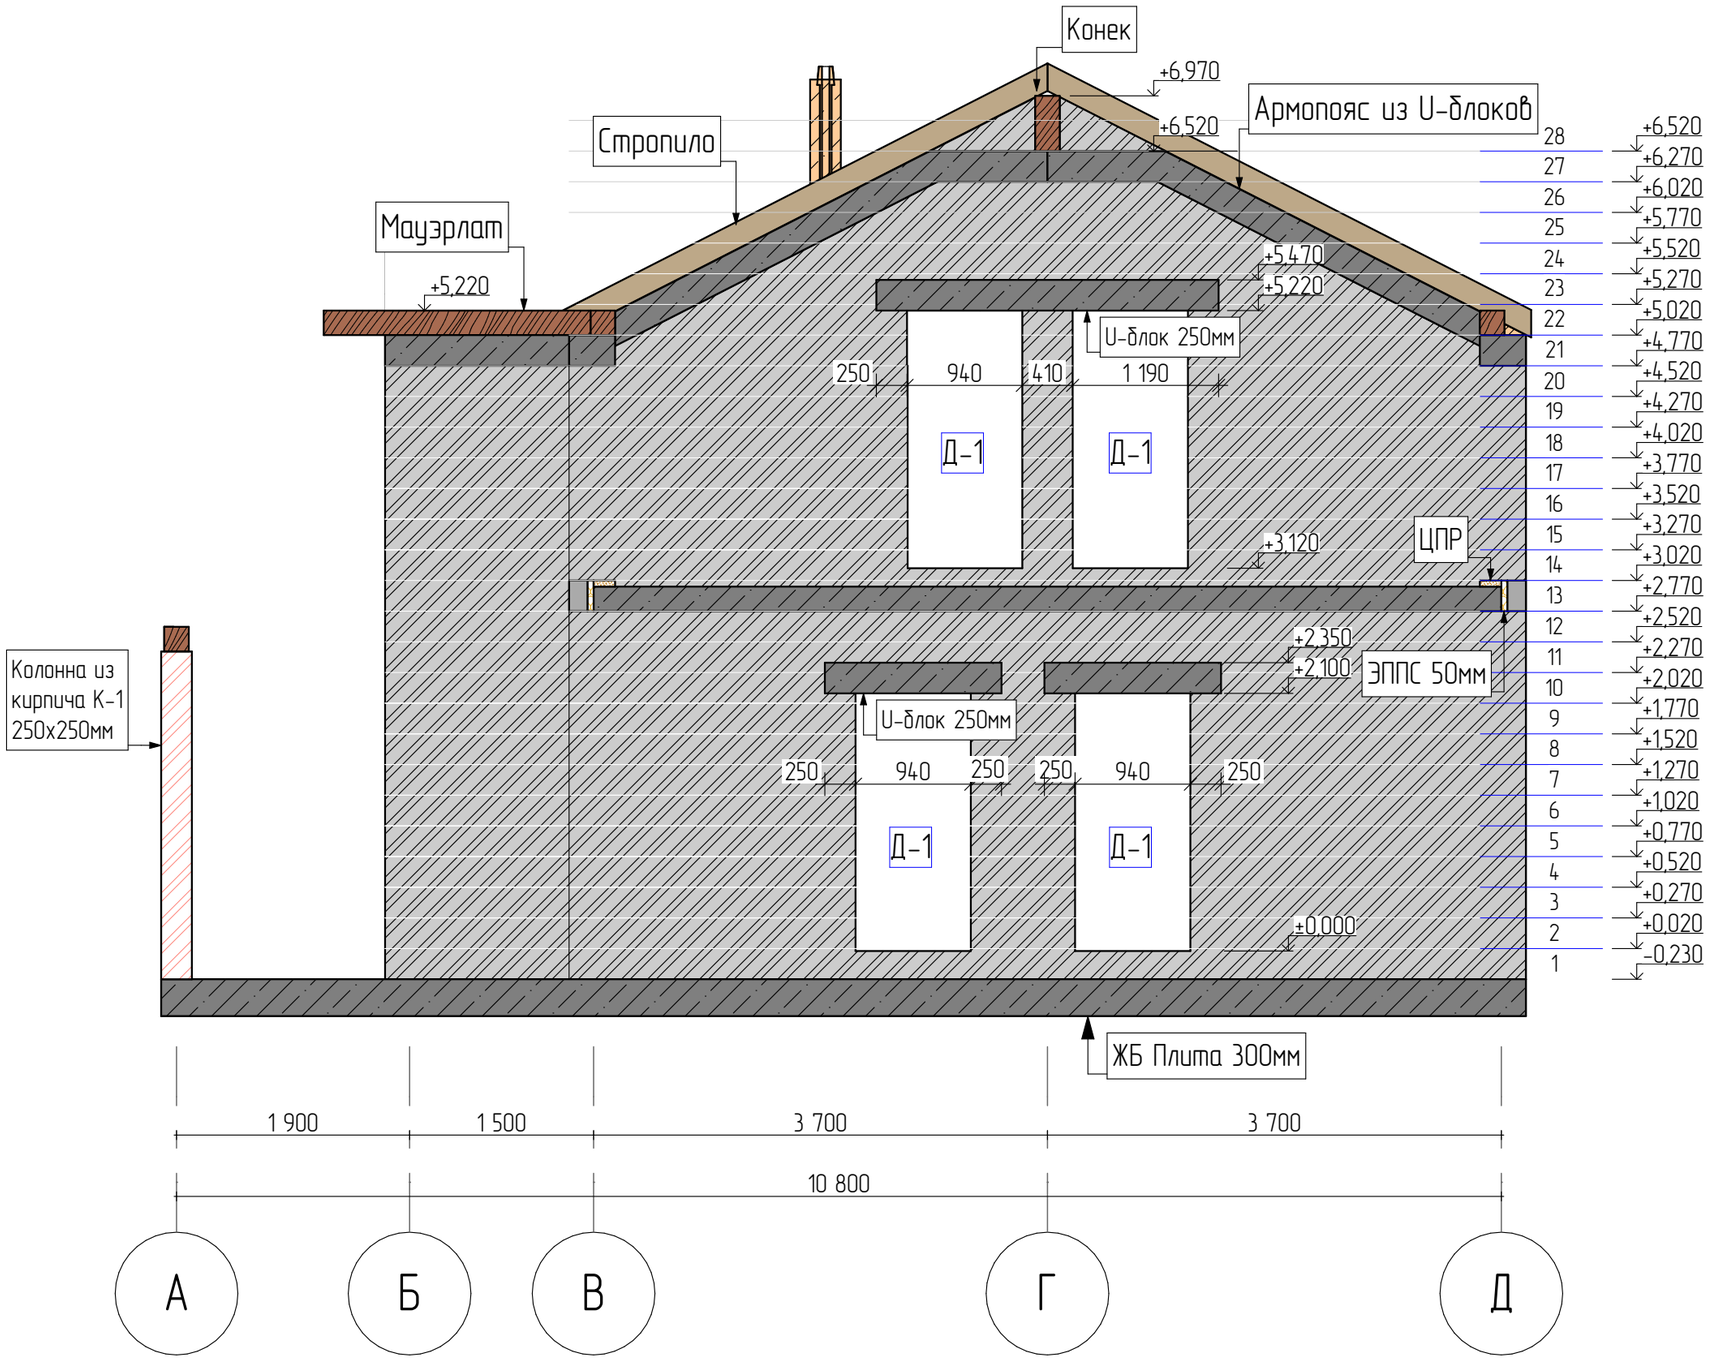

Согласовано

Взам. инв. №

Подпись и дата

Инв. № подл.

Стена 4 М1:50


Лист

5

М 1:50

разрез

Стена 5

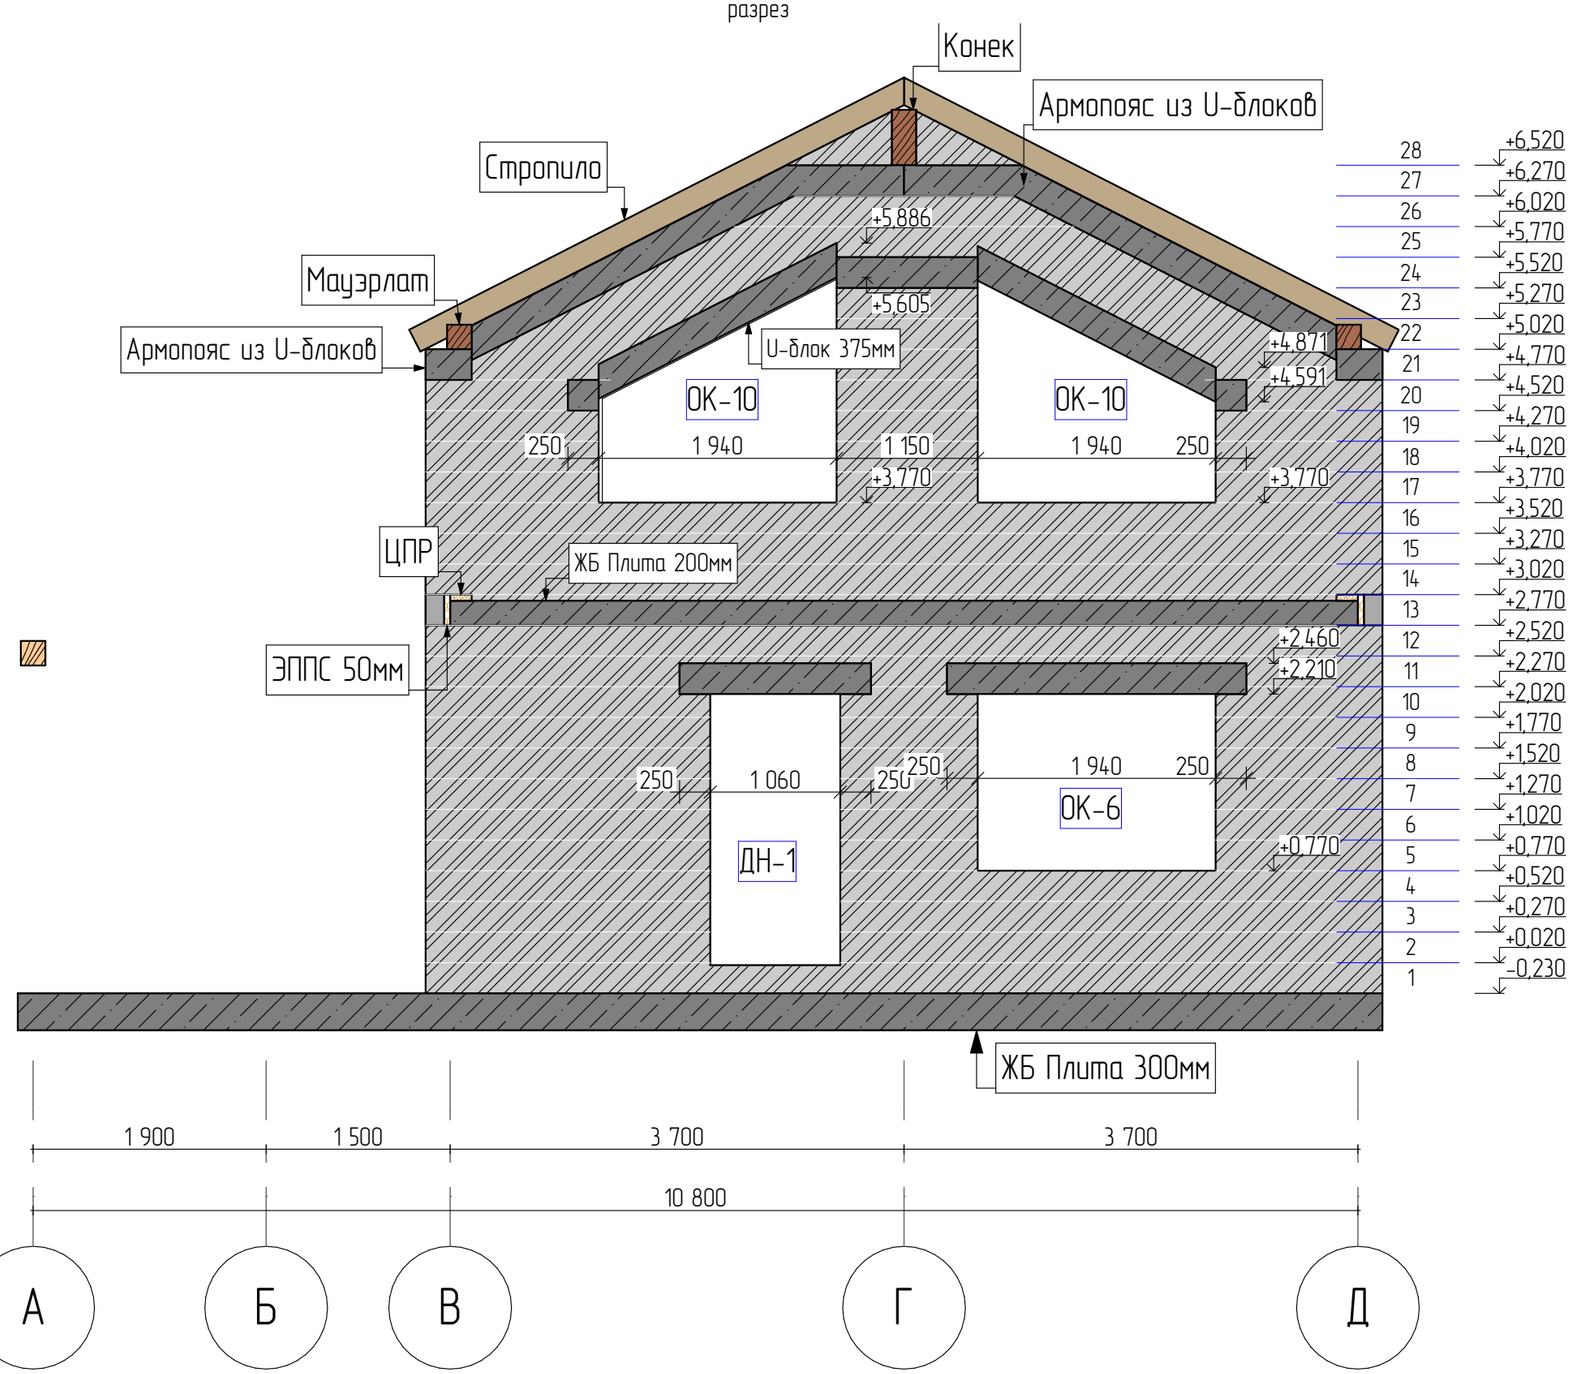

Согласовано

Взам. инв. №

Подпись и дата

Инв. № подл.

Стена 5 М1:50


Лист

6

М 1:50

разрез

Стена Б

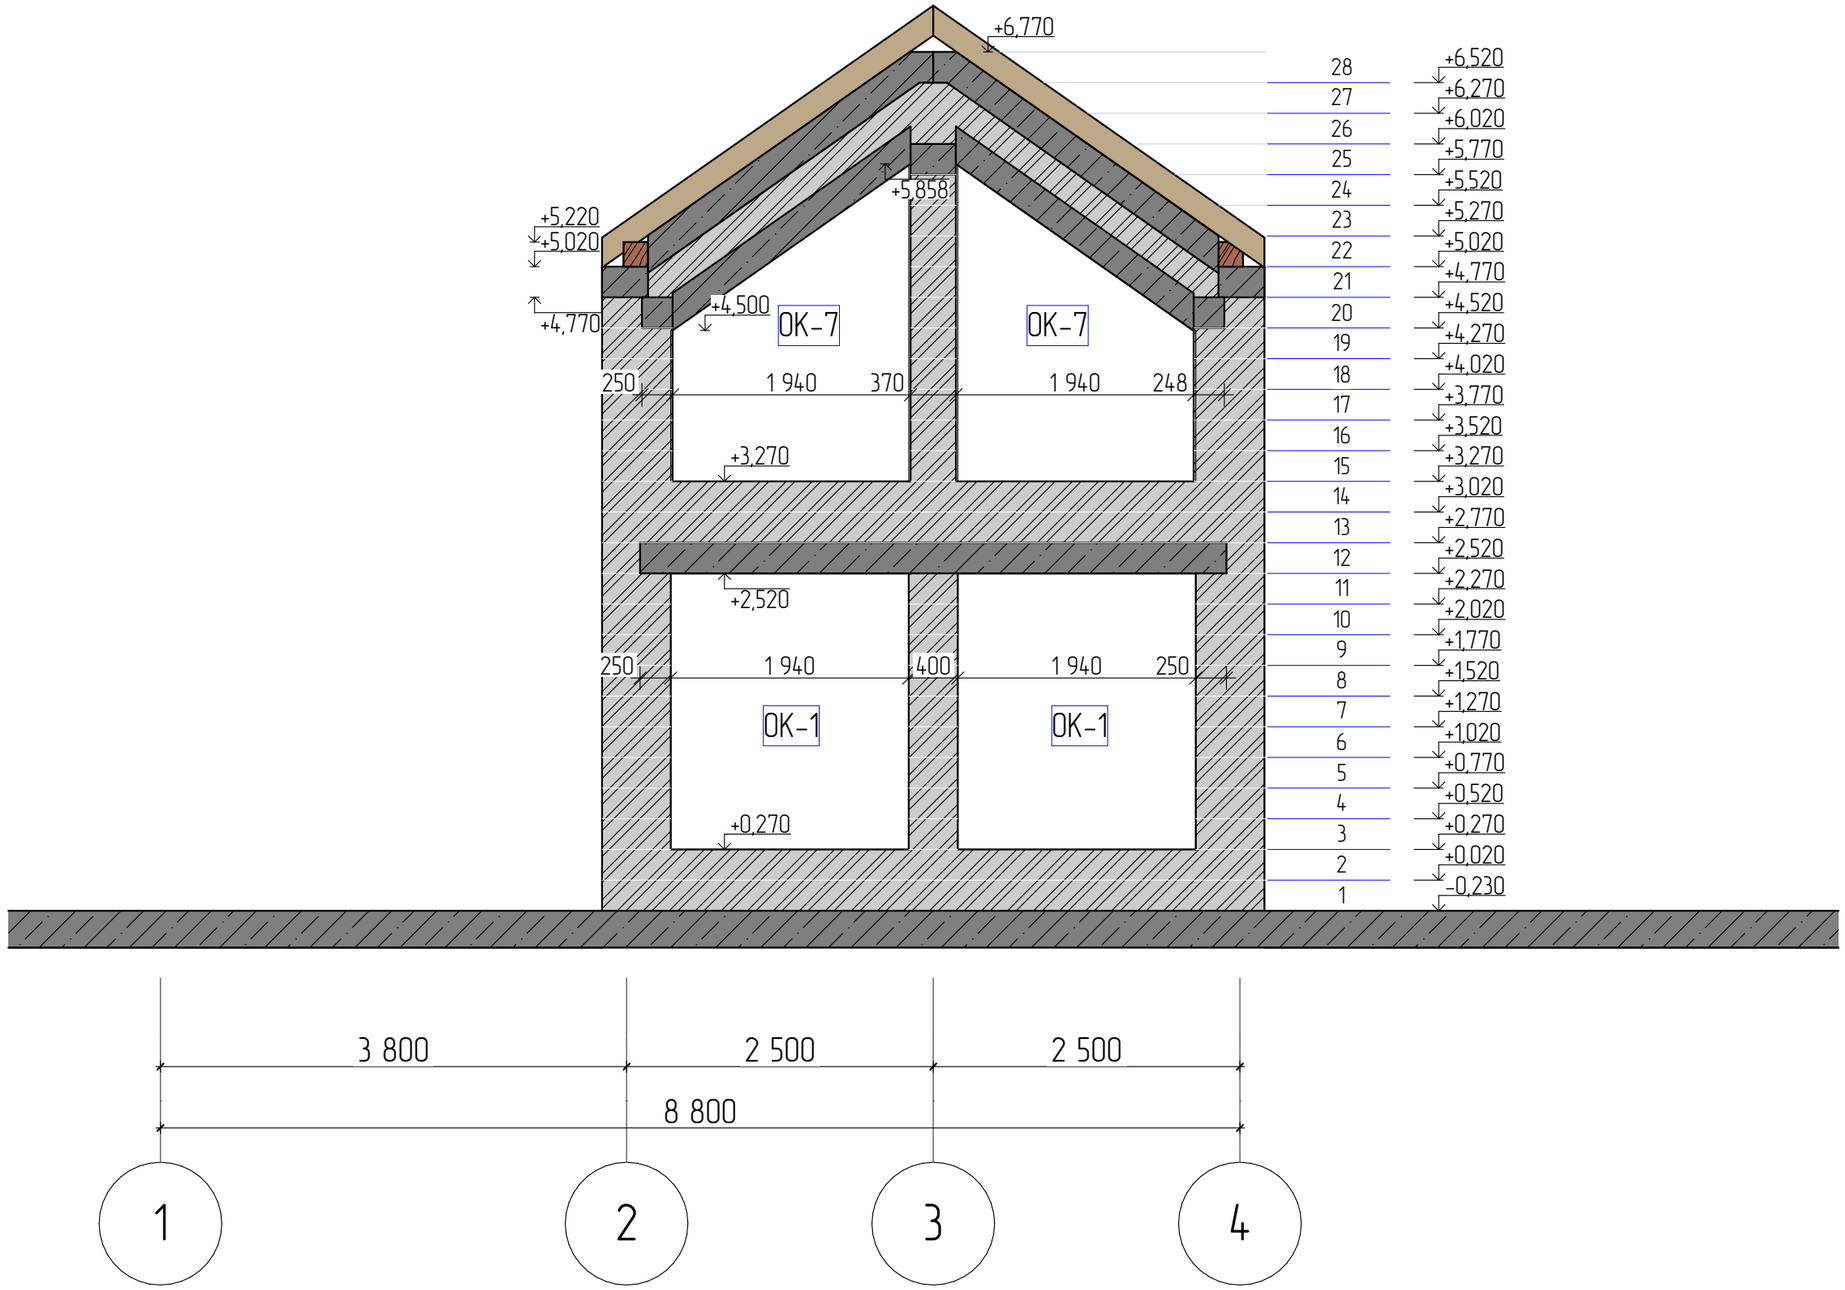

Согласовано

Взам. инв. №

Подпись и дата

Инв. № подл

Стена Б М1:50


Лист

7

М 1:50

разрез

Стена В

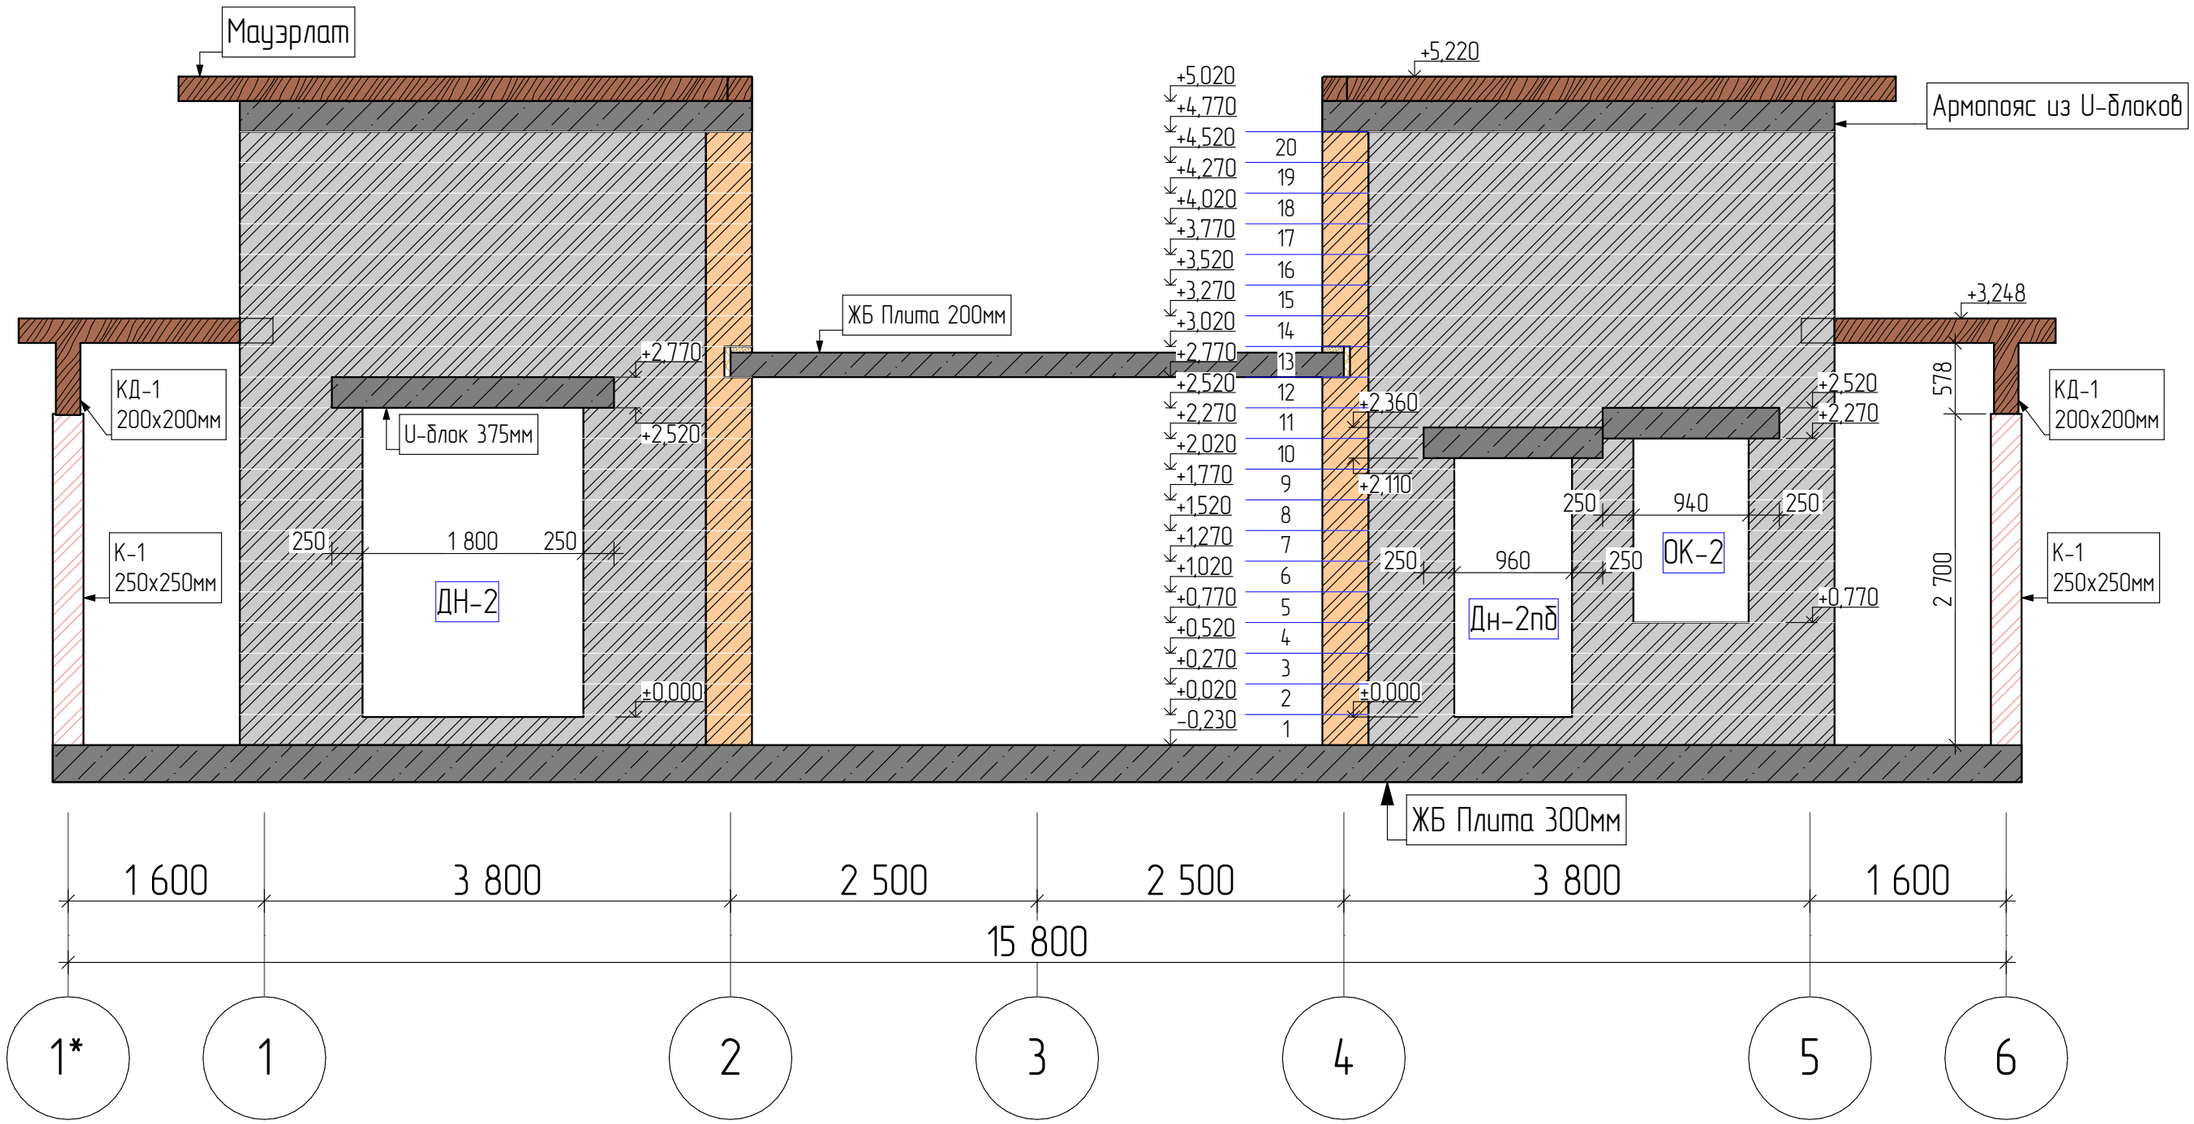

Согласовано

Взам. инв. №

Подпись и дата

Инв. № подл.

Стена В М1:50


Лист

8

М 1:50

разрез

Стена Г

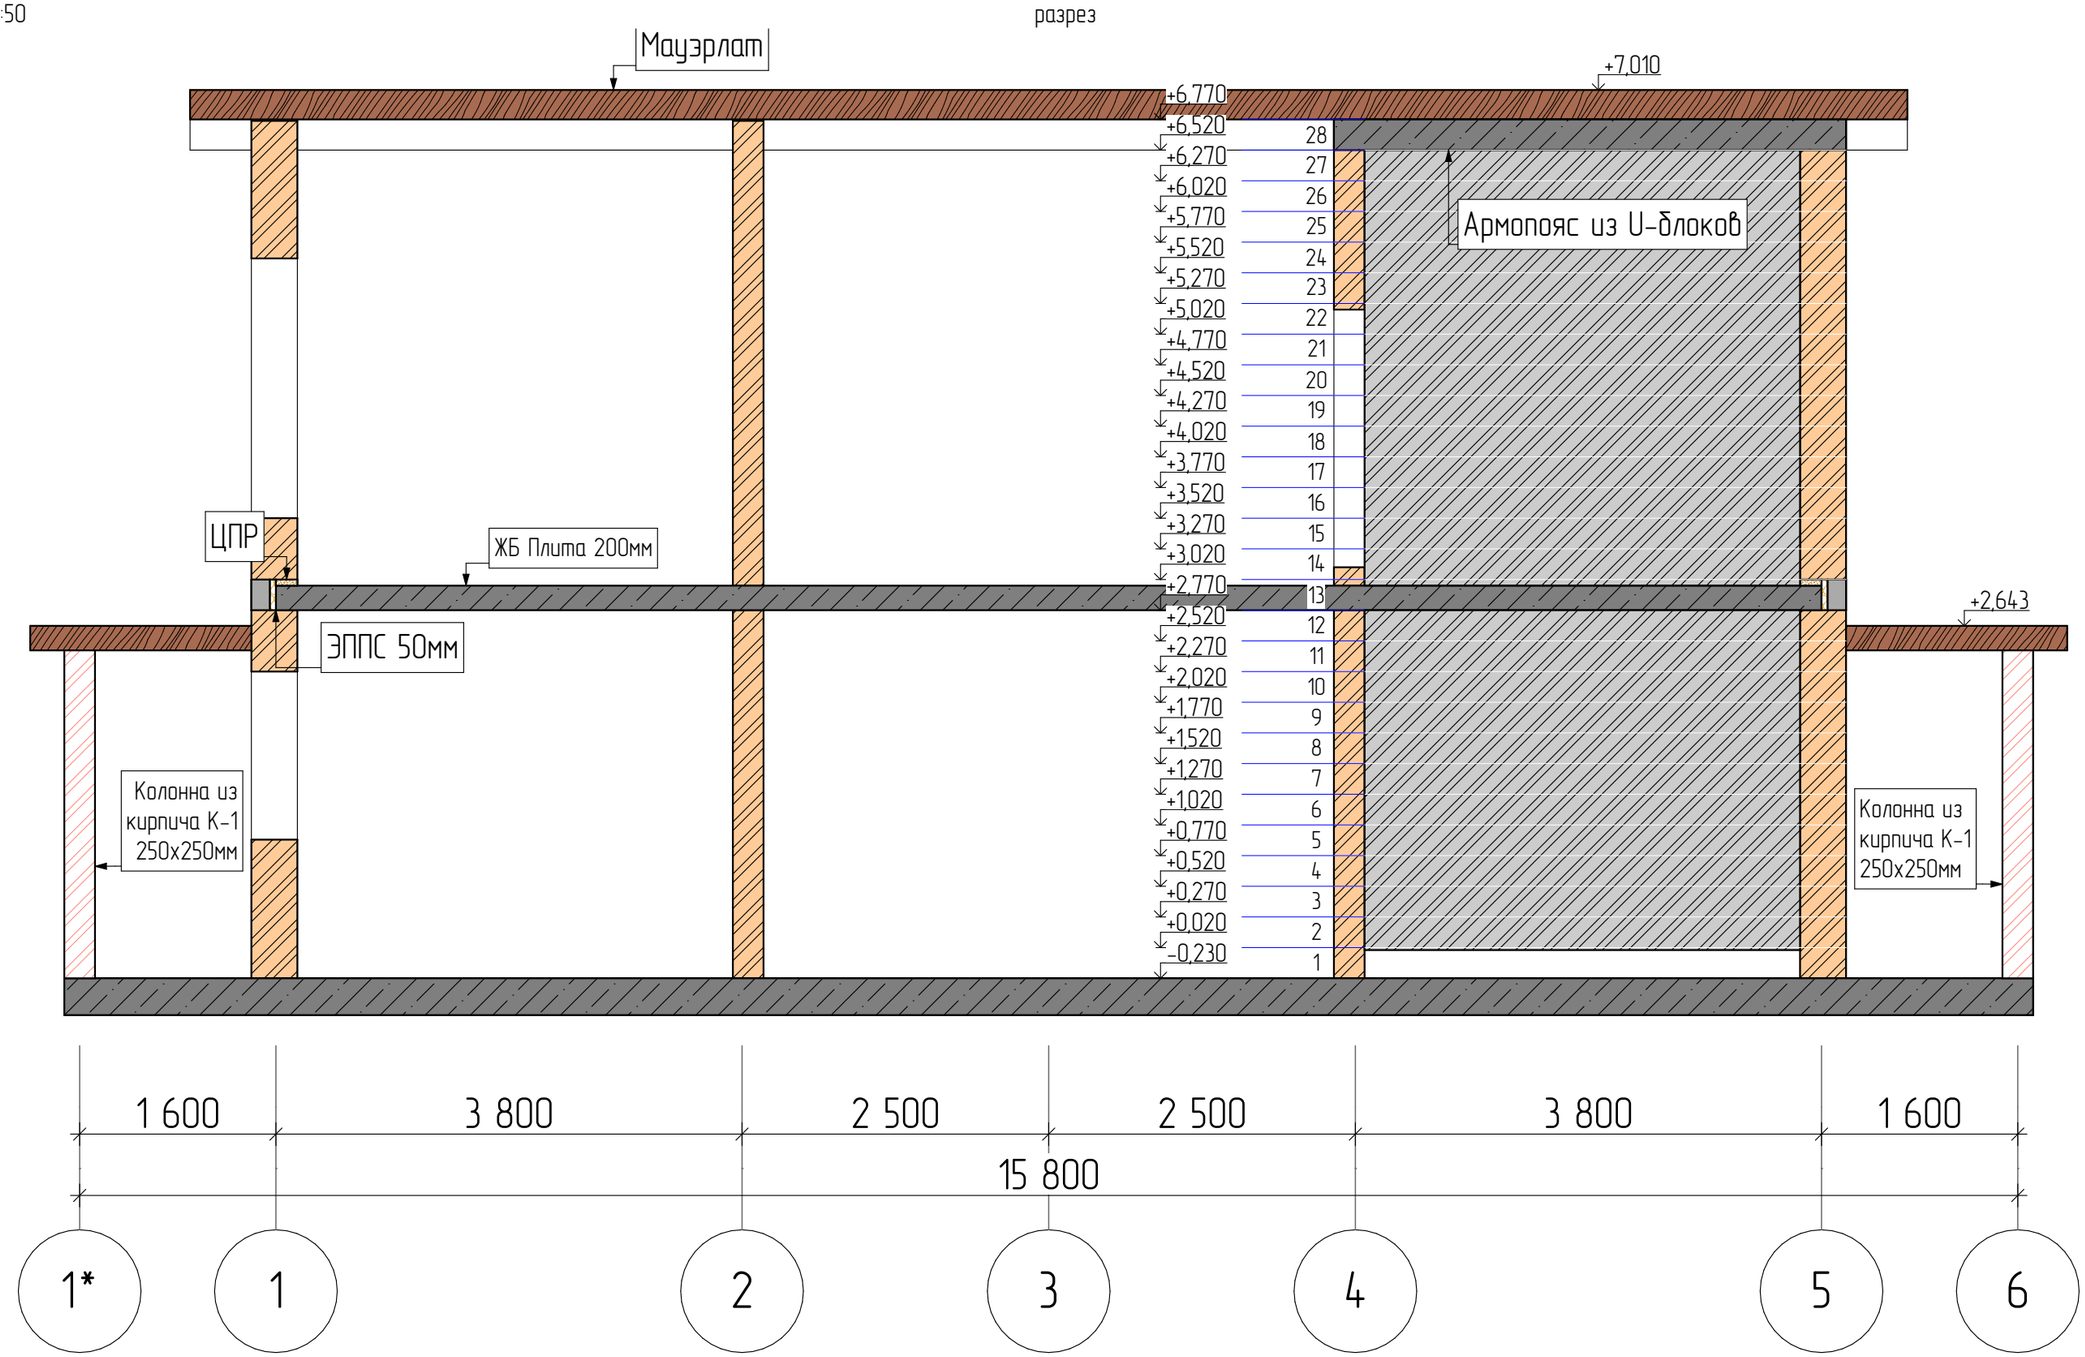

Согласовано

Взам. инв. №

Подпись и дата

Инв. № подл.

Стена Г М1:50


Лист

9

М 1:50

разрез

Стена Д

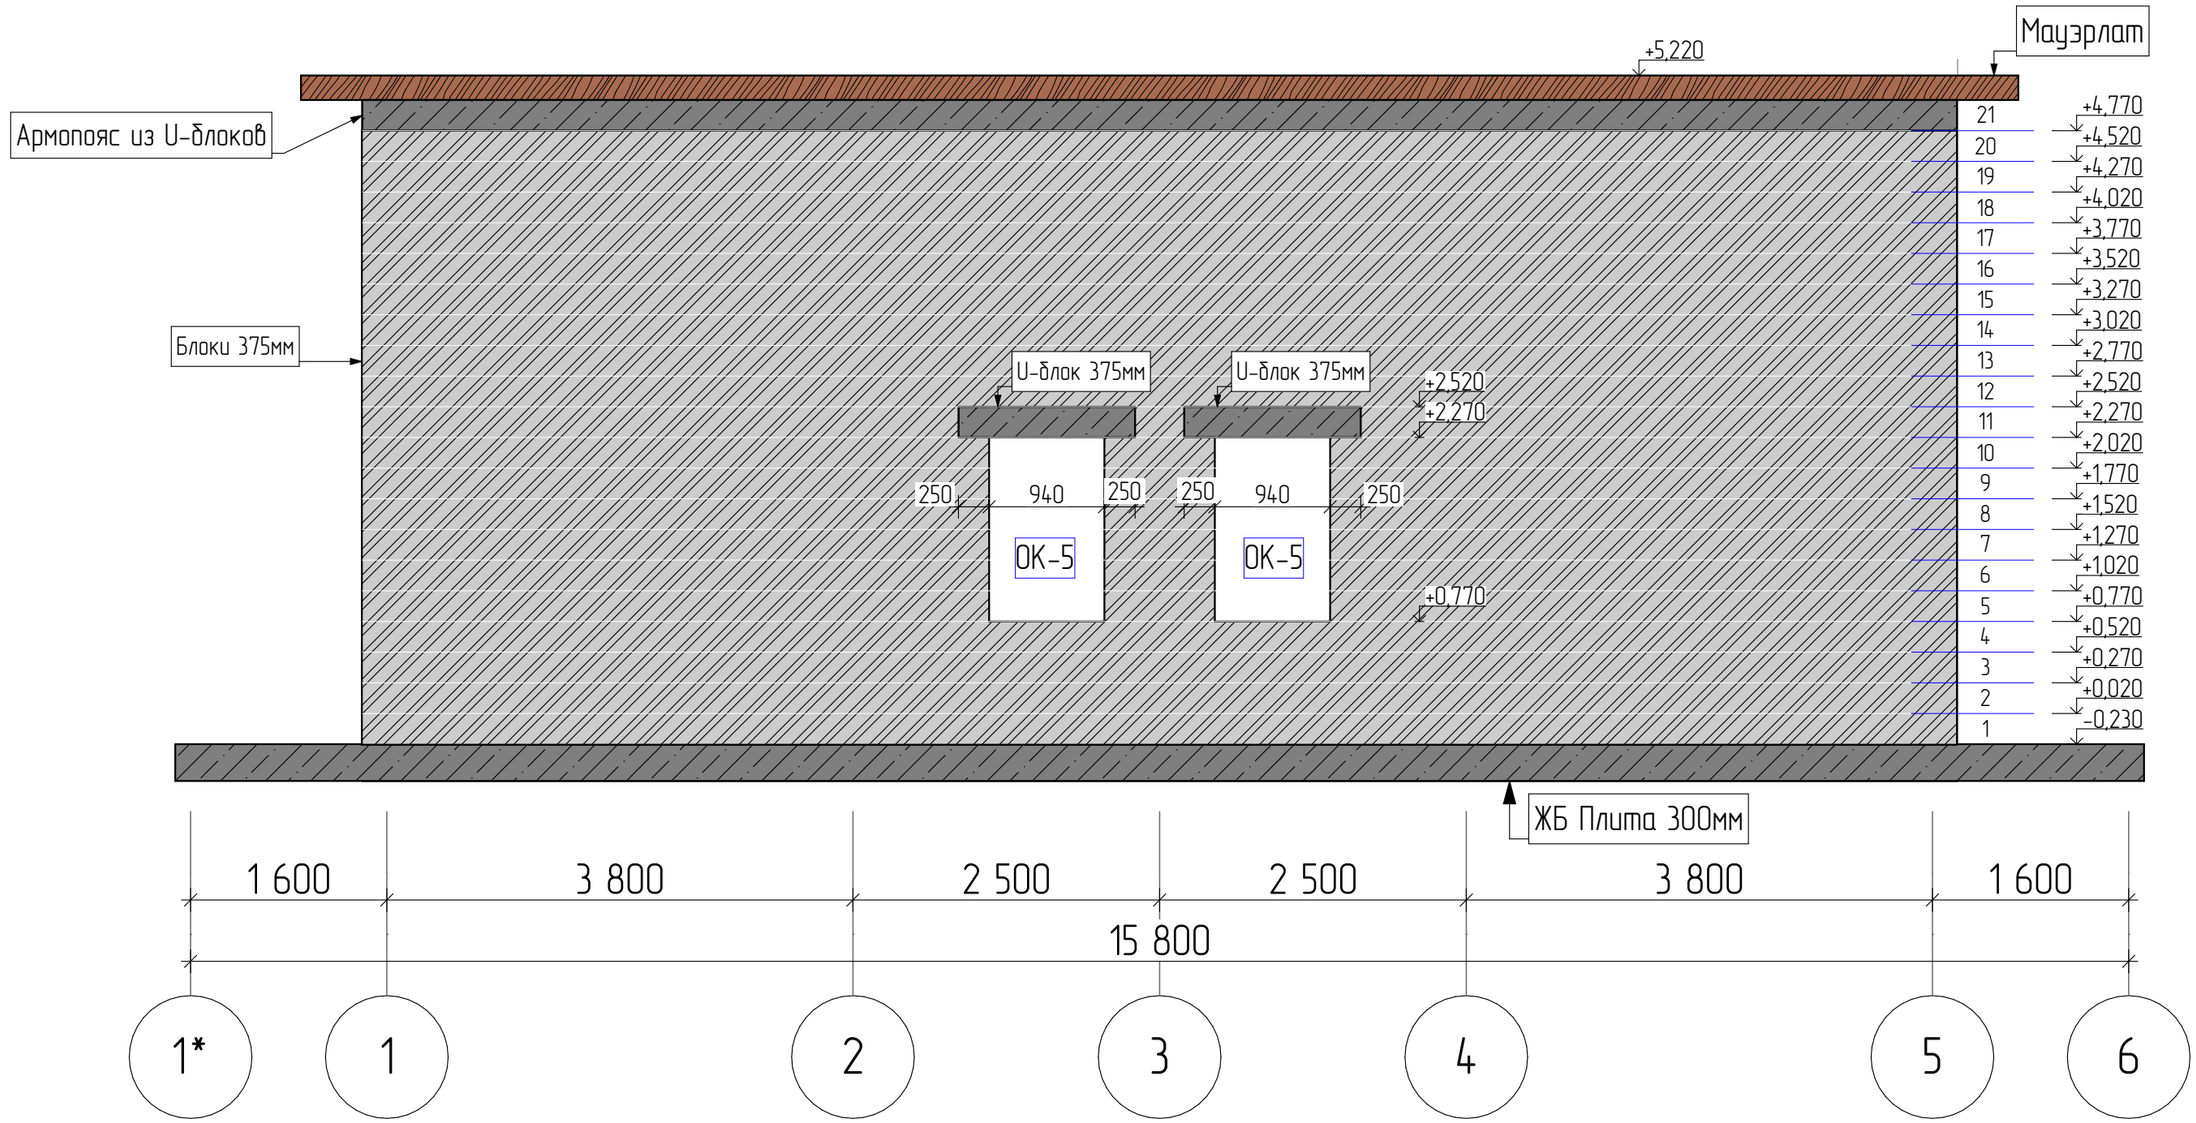

Согласовано

Взам. инв. №

Подпись и дата

Инв. № подл.

Стена Д М1:50


Лист


10


М 1:50

разрез

Шидель

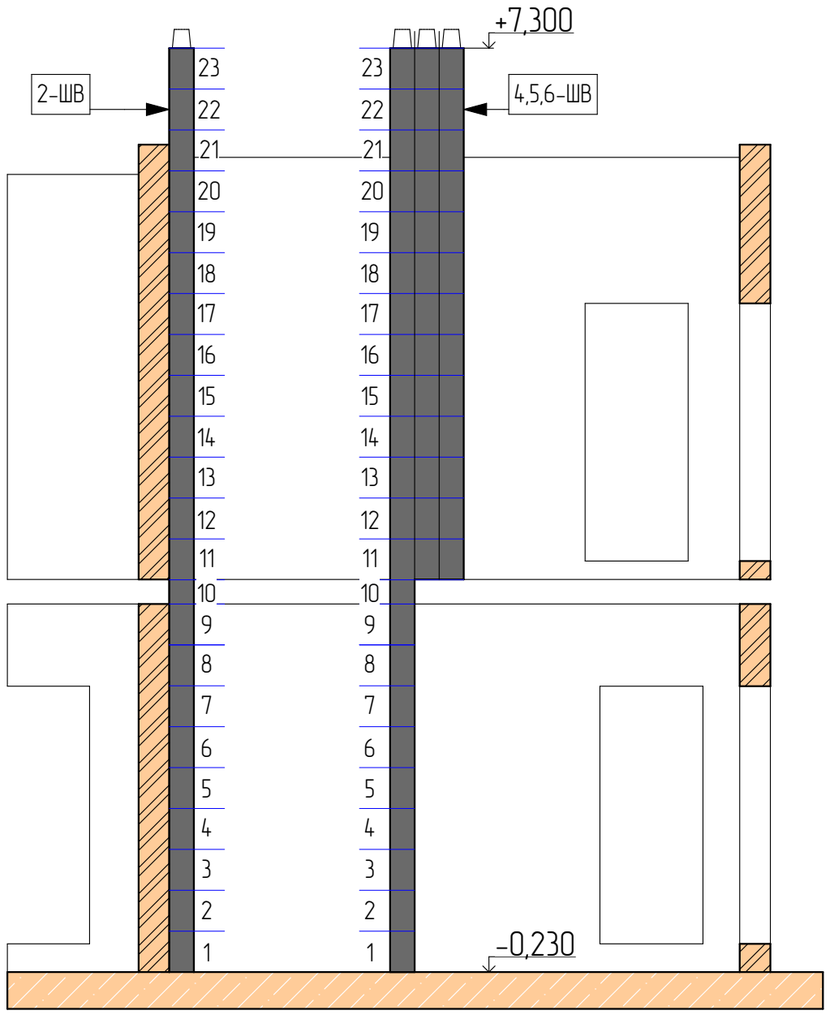

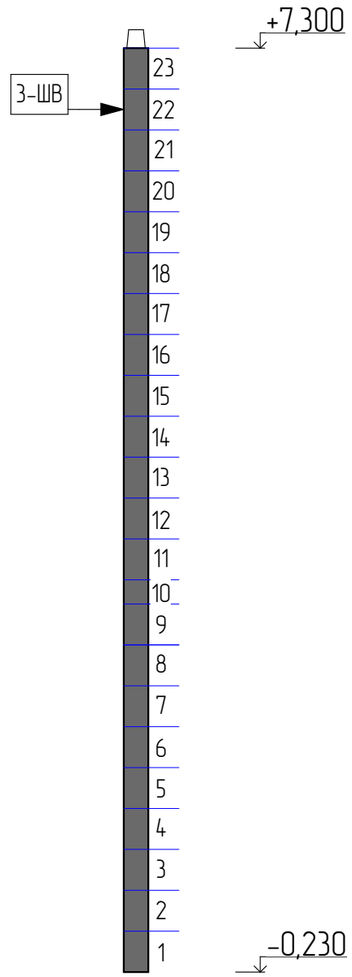

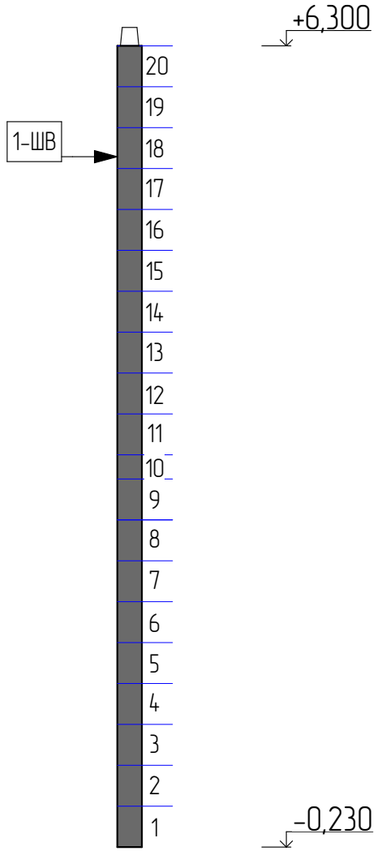

Согласовано

Взам. инв. №

Подпись и дата

Инв. № подл.

Шидель М1:100

Лист

11