ОБЪЕКТ ИНДИВИДУАЛЬНОГО ЖИЛИЩНОГО СТРОИТЕЛЬСТВА



РАБОЧИЙ ПРОЕКТ

ШИФР: #ID ПРОЕКТА

АРХИТЕКТУРНЫЕ РЕШЕНИЯ

САНКТ-ПЕТЕРБУРГ 2021

ОБЪЕКТ: ОБЪЕКТ ИНДИВИДУАЛЬНОГО ЖИЛИЩНОГО СТРОИТЕЛЬСТВА

ПО АДРЕСУ: #ПОЛНЫЙ АДРЕС УЧАСТКА; К/Н; #ID УЧАСТКА

ЗАКАЗЧИК: _____#ОБРАЩЕНИЕ К ЗАКАЗЧИКУ

АРХИТЕКТОР _____САЛЫКОВА В.Г..

РАБОЧИЙ ПРОЕКТ

ШИФР: #ID ПРОЕКТА

АРХИТЕКТУРНЫЕ РЕШЕНИЯ

САНКТ-ПЕТЕРБУРГ 2021

Согласовано:

Взам. инв. №

Подпись и дата

Инв. № подл.

Ведомость чертежей

Лист	Наименование	Примечание
	Обложка	
	Титульный лист	
2	Общие данные (начало)	
3	Общие данные (окончание)	
4	Схема организации участка М 1:300	
5	План 1 этажа с расстановкой мебели М 1:100	
6	План 2 этажа с расстановкой мебели М 1:100	
7	Разрез 1-1 М 1:75	
8	Разрез 2-2 М 1:75	
9	Фасады М 1:100	
10	Фасады М 1:100	
11	План ЖБ плиты М 1:100	
12	План ЖБ плиты с закладными М 1:100	
13	План ЖБ межэтажной плиты	
14	План 1 этажа с размерами М 1:100	
15	План 2 этажа с размерами М 1:100	
16	Маркировочный план 1 этажа М 1:100	
17	Маркировочный план 2 этажа М 1:100	
18	Фрагменты разрезов М 1:25	
19	Схема устройства ЖБ лестницы	
20	План кровли М 1:100	
21	Общий вид крыши	
22	Общие виды	
23	Общие виды (поэтажные)	
24	Спецификация заполнения оконных проёмов	
25	Спецификация заполнения дверных проёмов	

Пояснительная записка /начало/

Проект разработан на основании техзадания, предоставленного заказчиком, соответствует установленным общегосударственным нормам и требованиям малоэтажному строительству в соответствии со СП 55.13330.2011 "Дома жилые одноквартирные". Актуализированная редакция СНиП 31-02-2001; СП 131.13330.2018 "Строительная климатология", ГОСТ 21.501-2011 "Система проектной документации для строительства. Правила выполнения рабочей документации архитектурных и конструктивных решений". СП 63.13330.2012 «Бетонные и железобетонные конструкции», СП 64.13330.2017 "Деревянные конструкции", ГОСТ 8486-86 "Пиломатериалы хвойных пород"

Нормативное значение равномено-распределенной временной нагрузки на перекрытие согласно СП 20.13330.2016 «Нагрузки и воздействия» равно 150,0кг/м2.

Производство работ должно выполняться в строгом соответствии с тербованиями Подрядчика.
Обязательно выполнение работ по водоотведению - дренажных работ с монтажом смотровых колодцев, отмостки и других работ, направленных на отведение воды от пятна застройки. Выполняется в объеме, определенном сметой.

Гарантия на фундаментные работы осуществляется только при условии надлежащей системы водоотведения и ее эксплуатации.

Данные о фактических размерах участка, габаритов его границ, наличие заборов, крупных растений, близость соседских построек, различных ограничений, схемы с точной привязкой их расположения на территории участка предоставляет заказчик. Точность вышеописанных сведений лежит на Заказчике. Подрядчиком не проводятся работы по межеванию и он основывается на данных, предоствленных Заказчиком.

Характеристика проектируемого объекта:

- этажность - 2 этажа
- класс функциональной пожарной опасности здания - Ф 1,4 (по СП 112.13330.2011)

Строительно-климатический район IIВ в соответствии с СП 131.13330.2018 со следующими характеристиками условий:
- температура наружного воздуха наиболее холодных суток - -32оС
- температура наружного воздуха наиболее холодной пятидневки - -28оС
- рассчетная снеговая нагрузка по району - 180кг/м2
- нормативное давление ветра - 23кгс/м2

					2021	#ID Проекта
						Адрес: #Полный Адрес Участка
Изм.	Кол.уч	Лист	№док.	Подпись	Дата	
						Индивидуальный жилой дом
Архитектор		Салыкова В.Г.				
Заказчик		#Обращение к Заказчику				Общие данные (начало)

стадия	лист	листов
РП	2	

Пояснительная записка /окончание/

Архитектурно-планировочные решения:

Проектируемый коттедж одноквартирный, двухэтажный . Размеры в осях 15,18х10,8 м.

На первом этаже дома размещаются помещения: тамбур, котельная, холл, санузел, спальня, кухня, гостиная-столовая, кладовая, лестничный холл 2 террасы.

На втором этаже размещаются: холл, санузел, 2 спальни, мастер-спальня, санузел, гардероб.

Дом без чердака. За отм. 0,000 принят уровень чистого пола первого этажа дома. За отм. 3,100 принят уровень чистого пола второго этажа дома. Покрытие кровли - согласно смете. Водосточная система - водосточные трубы и желоба , цвет индивидуальный. Окна - ПВХ или деревянные, 2- камерные стеклопакеты, индивидуального изготовления. Двери наружные - металлические, сендвич, внутренняя сторона МДФ или индивидуального изготовления. Двери внутренние - деревянные по индивидуальному проекту. Отмостка -утепленная, бетонная толщ.100мм из бетона Кл.В7.5 по гравийно-песчаному основанию шириной 1000мм.

Конструктивные решения:

Фундамент представляет собой монолитную железобетонную плиту 300мм.
Полы первого этажа, (крыльца и террасы) выполнены по монолитной ЖБ плите.
Межэтажное перекрытие: по монолитной ж/б плите толщиной 200мм.
Наружние несущие стены выполнены из газобетонных блоков
-Ytong 1/625x375x250/D400/B2,5/F100 ГОСТ 31360-2007.
Внутренние несущие стены выполнены из газобетонных блоков
-Ytong 1/625x250x250/D500/B3,5/F100 ГОСТ 31360-2007 .
Перегородки выполнены из газобетонных блоков
- Ytong 1/625x150x250
Кладка из газобетонных блоков может эксплуатироваться без отделки. Обязательной является только защита от намокания мест потенциального переувлажнения: подоконных зон, примыкания к отмостке, козырькам – мест, где возможно образование снеговых карманов, потоков и пр. Для наружной отделки, наносимой непосредственно на поверхность кладки (штукатурка, окраска, наклейка плитки или каменных плит), существуют дополнительные ограничения. Слой такой отделки должен обладать достаточной паропроницаемостью, т.е.обеспечивать удаление из кладки начальной технологической влаги и не вызывать значительного увлажнения кладки за отделкой в отопительный сезон.

Номинальные, проектные линейные и высотные размеры отдельных применяемых материалов строения могут отличаться от фактических в силу технических и технологических особенностей, выполняемых работ и применяемых материалов, нормативных допусков и отклонений от предельных размеров строения и материалов в частности, сезонности и влажности, погодных явлений и других обстоятельств.

Крыша - двускатная из деревянных наслонных стропил с обрешеткой, покрытие согласно смете. Между стропилами укладывается утеплитель толщ.200мм.

Стропила- сухая строганая доска 40х180мм.

Материалы, технология работ и способы исполнения, гарантийные обязательства, способы эксплуатации и другое, связанное с использованием строения, а также его монтажом регулируется ТУ 16.23.19-001-17010764-2018

ТЕХНИКО-ЭКОНОМИЧЕСКИЕ ПОКАЗАТЕЛИ	
Площадь застройки, м2	221,3
Общая площадь, м2	289,82
Жилая площадь, м2	133,37
Строительный объем, м3	981,28

*Площадь помещений указана без учета отделочных материалов и понижающего коэффициента

Проект строительства жилого дома разработан в соответствии с действующими строительными, технологическими и санитарными нормами и правилами, предусматривает мероприятия, обеспечивающие конструктивную надежность, врзрывопожарную и пожарную безопасность объекта, защиту окружающей природной среды при его эксплуатации и отвечает требованиям законодательства Российской Федерации в области капитального строительства.

Архитектор проекта Салыкова В.Г.

Согласовано:

Взам. инв. №

Подпись и дата

Инв. № подл.

					2021
Изм.	Кол.уч	Лист	№док.	Подпись	Дата
Архитектор		Салыкова В.Г.			
Заказчик		#Обращение к Заказчику			


#ID Проекта


Адрес: #Полный Адрес Участка

Индивидуальный жилой дом

стадия	лист	листов
РП	3	

Общие данные (окончание)

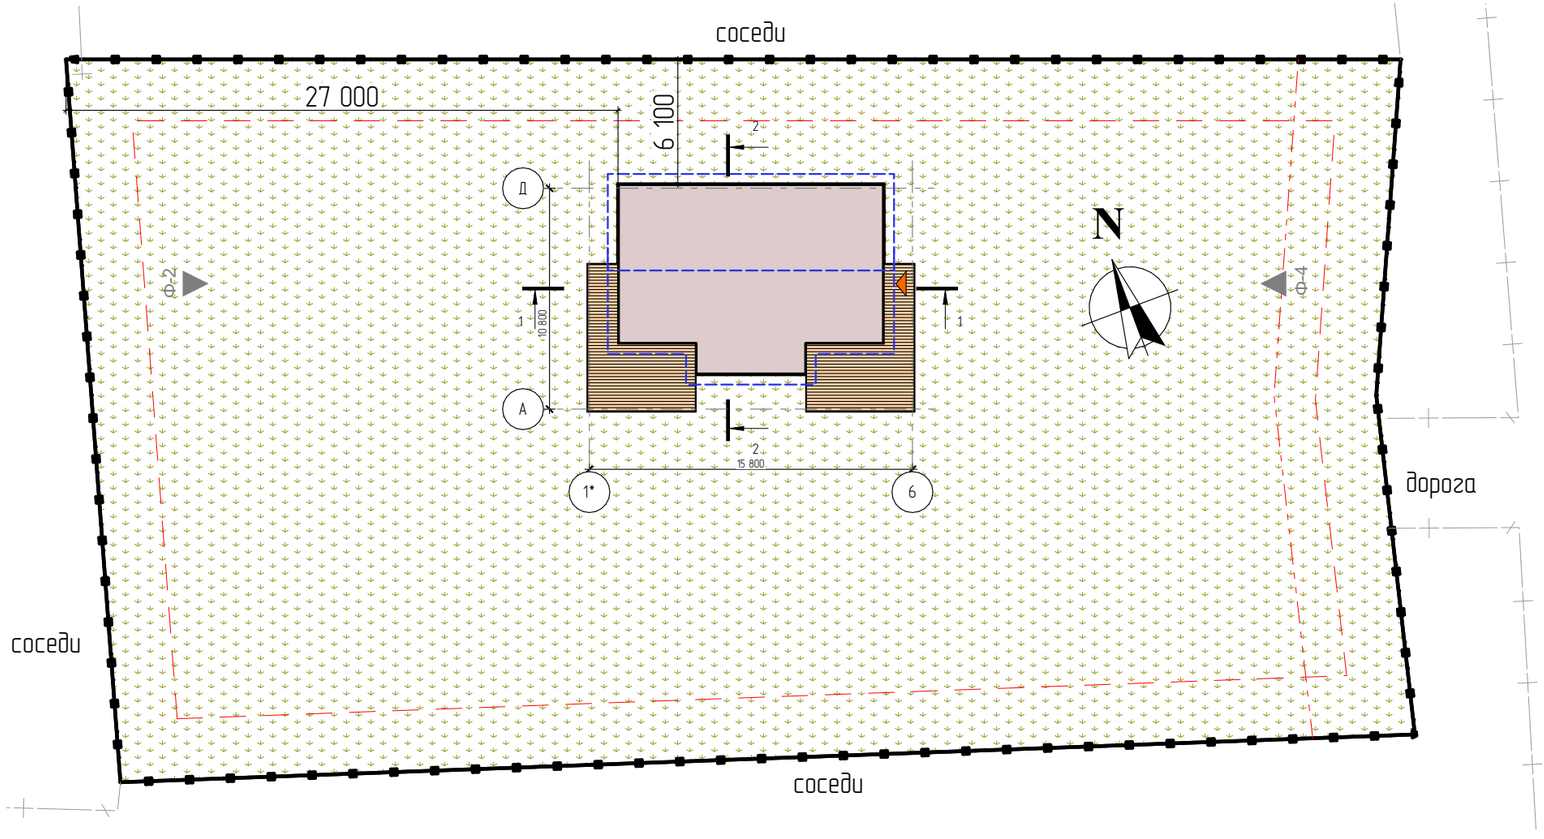

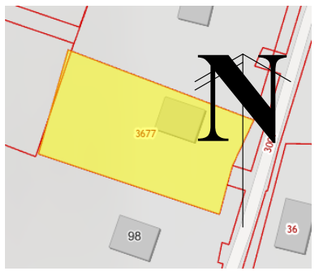


#ID Участка

Примечание:
1) Расположение дома показано от забора до края фундамента.
2) Привязка показана условно. Скорректировать по месту.
3) При расположении дома учитывать требования по противопожарным расстояниям между строениями на соседних участках в соответствии с СП 53.13330.2011
4) Монтаж и расположение наружных сетей согласовывается с инженером по месту.

Условные обозначения:

- Проектируемое здание
- Терраса/крыльцо/веранда
- Вход
- Контур кровли
- Зона отступа от края участка (красной линии улицы) = 5,0 м
- Зона отступа от края участка = 3,0 м
- Граница участка

Инсоляция по временам года

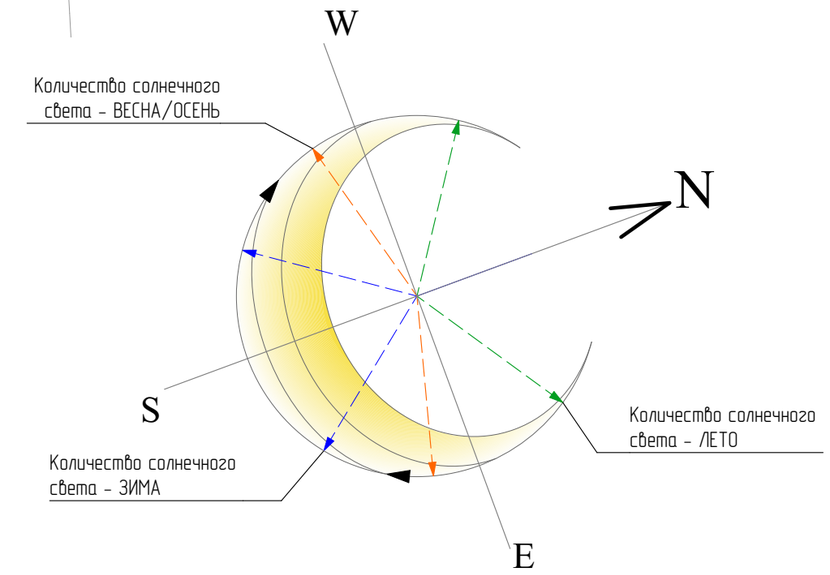

Согласовано:

Взам. инв. №

Подпись и дата

Инв. № подл.

					2021
Изм.	Кол.уч	Лист	№док.	Подпись	Дата
Архитектор		Салыкова В.Г.			
Заказчик		#Обращение к Заказчику			

#ID Проекта

Адрес: #Полный Адрес Участка


Индивидуальный жилой дом

стадия	лист	листов
РП	4	

Схема организации участка М 1:300

М 1:100

План 1 этажа с расстановкой мебели

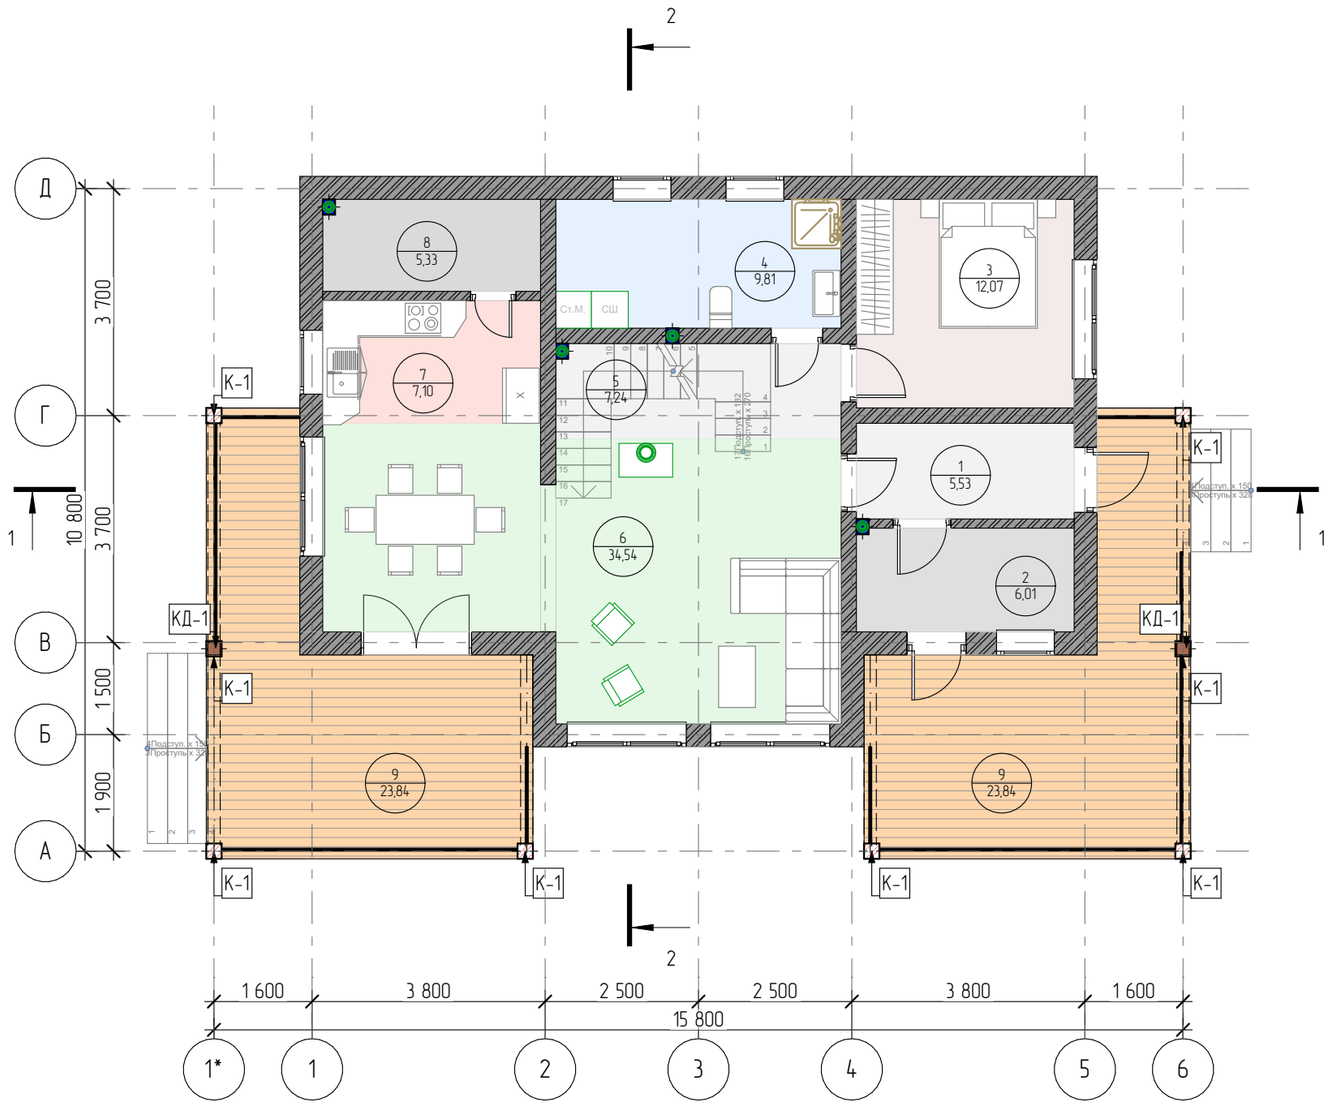

Экспликация 1 этажа

Расположение поиещений	№ п/п	Наименование	Площадь, м2
Внутр. пом.			
	1	Тамбур	5,53
	2	Котельная	6,01
	3	Спальня	12,07
	4	Постирочная	9,81
	5	Лестничный холл	7,24
	6	Гостиная-Столовая	34,54
	7	Кухня	7,10
	8	Кладовая	5,33
			87,63 м²
Наружн. пом.			
	9	Терраса	23,84
	9	Терраса	23,84
			47,68 м²
			135,31 м²

Примечание:
1) Вся показанная мебель, а также назначение комнат носят условный характер
2) Расположение сан.технических приборов не подлежит перемещению.
3) Площадь помещений показана без учета отделочных материалов и понижающего коэффициента по периметру пола.
4) Все декоративные элементы подлежат дополнительному сметному согласованию.

					2021	#ID Проекта	
						Адрес: #Полный Адрес Участка; к/н: #ID Участка	
Изм.	Кол.уч	Лист	№док.	Подпись	Дата		
						Индивидуальный жилой дом	стадия: ЭП; лист: 5; листов:
Архитектор		Салыкова В.Г.					
Заказчик		#Обращение к Заказчику				План 1 этажа с расстановкой мебели М 1:100	

Согласовано:


Взам. инв. №

Подпись и дата

Инв. № подл.

М 1:100

План 2 этажа с расстановкой мебели

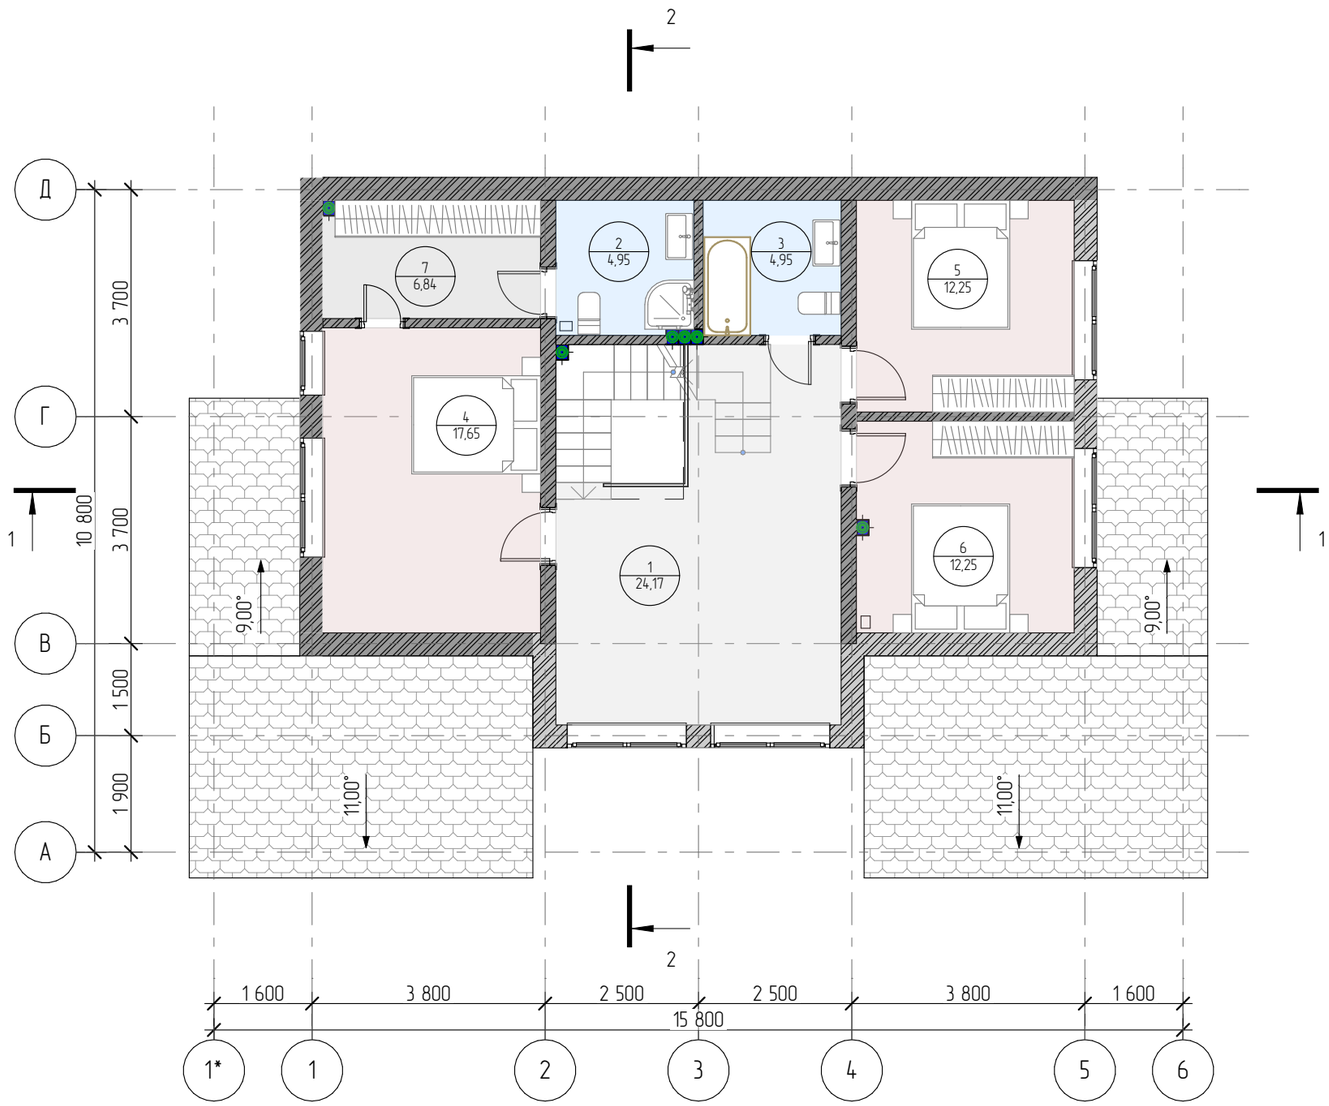

Экспликация 2 этажа

Расположение поиещений	№ п/п	Наименование	Площадь, м2
Внутр. пом.			
	1	Холл	24,17
	2	Санузел 1	4,95
	3	Санузел 2	4,95
	4	Мастер-спальня	17,65
	5	Спальня 1	12,25
	6	Спальня 2	12,25
	7	Гардероб	6,84
			83,06 м²

Примечание:
1) Вся показанная мебель, а также назначение комнат носят условный характер
2) Расположение сан.технических приборов не подлежит перемещению.
3) Площадь помещений показана без учета отделочных материалов и понижающего коэффициента по периметру пола.
4) Все декоративные элементы подлежат дополнительному сметному согласованию.

Согласовано:

Взам. инв. №

Подпись и дата

Инв. № подл.

					2021
Изм.	Кол.уч	Лист	№док.	Подпись	Дата
Архитектор		Салыкова В.Г.			
Заказчик		#Обращение к Заказчику			

#ID Проекта

Адрес: #Полный Адрес Участка;
к/н: #ID Участка


Индивидуальный жилой дом

стадия	лист	листов
ЭП	6	

План 2 этажа с расстановкой мебели
М 1:100

1:75

Разрез 1-1

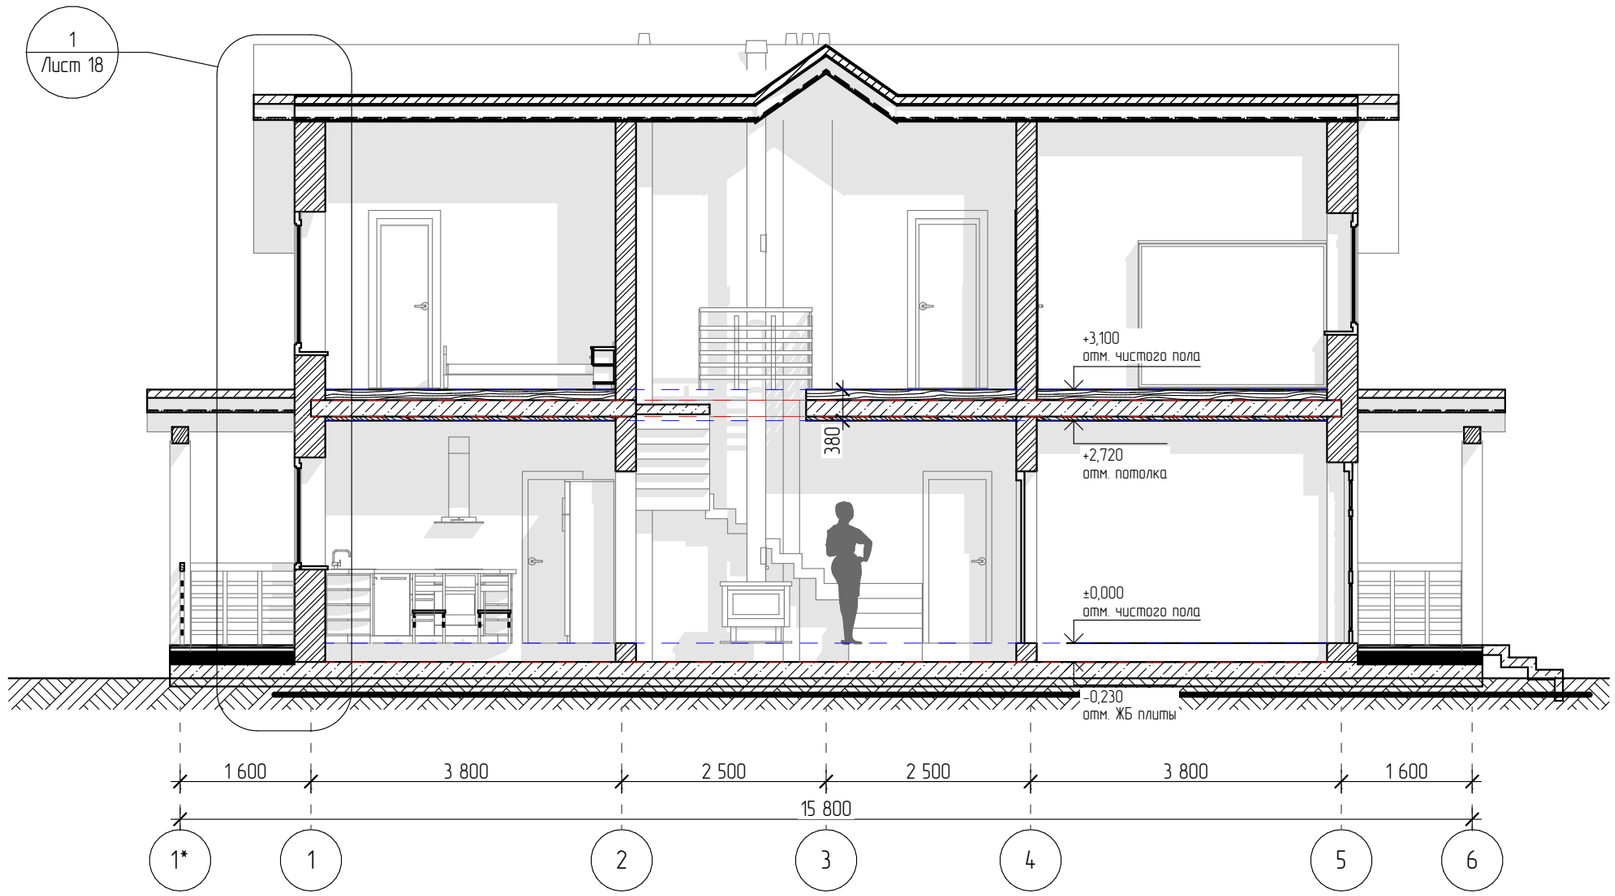

Примечание:

1) За отметку +0,000 принята отметка чистового пола первого этажа
2) За отметку +3,100 принята отметка чистового пола второго этажа
3) Номинальные высотные размеры могут отличаться от фактических
4) Высота фундамента дана без учета перепада. Замер перепада производится на участке при выезде инженера. Изменение габаритов и типа фундаментов согласовывается дополнительным согласованием по смете.
5) Все декоративные элементы показаны условно.

					2021	#ID Проекта			
						Адрес: #Полный Адрес Участка			
Изм.	Кол.уч	Лист	№док.	Подпись	Дата	Индивидуальный жилой дом	стадия	лист	листов
							РП	7	
Архитектор		Салыкова В.Г.							
Заказчик		#Обращение к Заказчику				Разрез 1-1 М 1:75			

Согласовано


Взам. инв. №

Подпись и дата

Инв. № подл.

1:75

Разрез 2-2

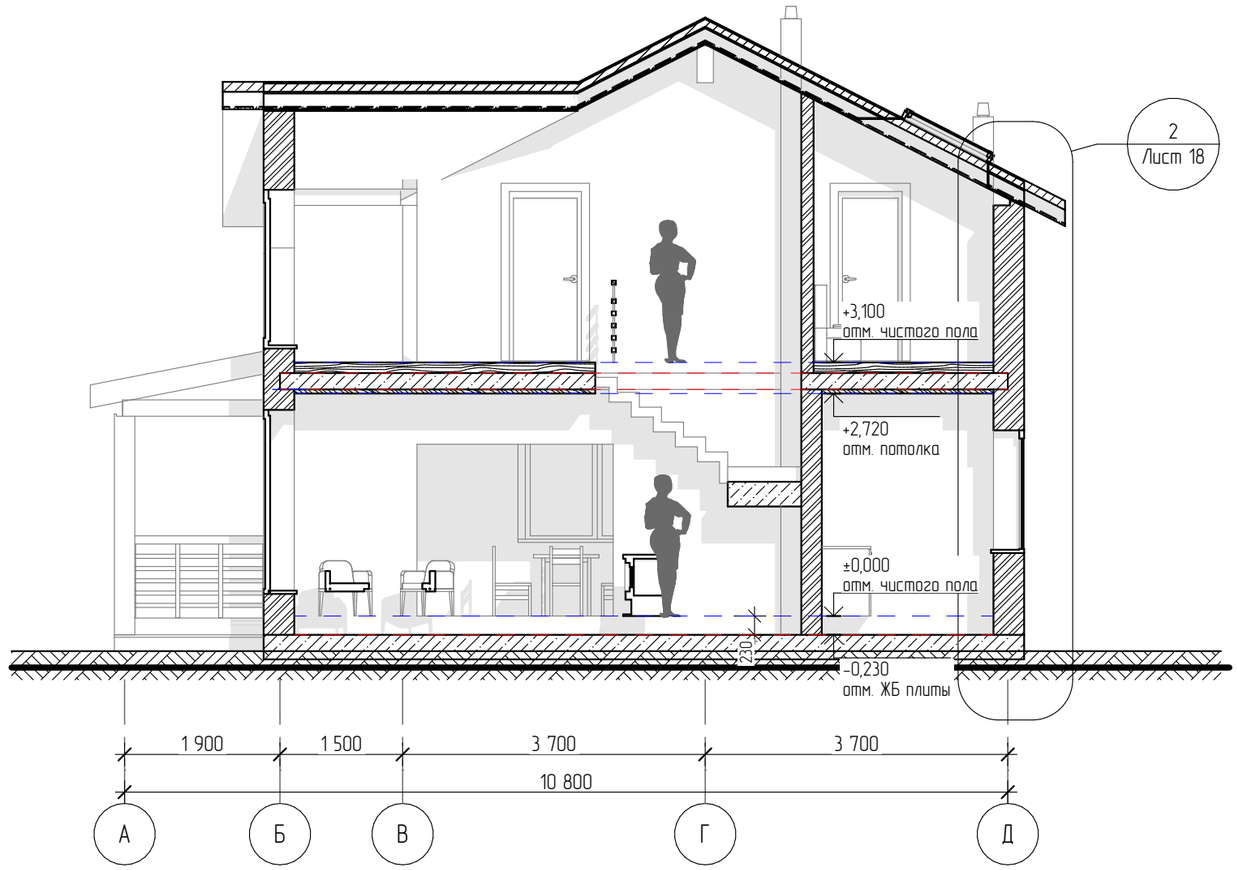

Примечание:

1) За отметку +0,000 принята отметка чистового пола первого этажа
2) За отметку +3,100 принята отметка чистового пола второго этажа
3) Номинальные высотные размеры могут отличаться от фактических
4) Высота фундамента дана без учета перепада. Замер перепада производится на участке при выезде инженера. Изменение габаритов и типа фундаментов согласовывается дополнительным согласованием по смете.
5) Все декоративные элементы показаны условно.

					2021	#ID Проекта		
						Адрес: #Полный Адрес Участка		
Изм.	Кол.уч	Лист	№док.	Подпись	Дата			
						Индивидуальный жилой дом	стадия	лист	листов
							РП	8	
Архитектор		Салыкова В.Г.							
Заказчик		#Обращение к Заказчику				Разрез 2-2 М 1:75			

Согласовано:

Взам. инв. №


Подпись и дата

Инв. № подл.

Фасад 1-5



Фасад Д-А

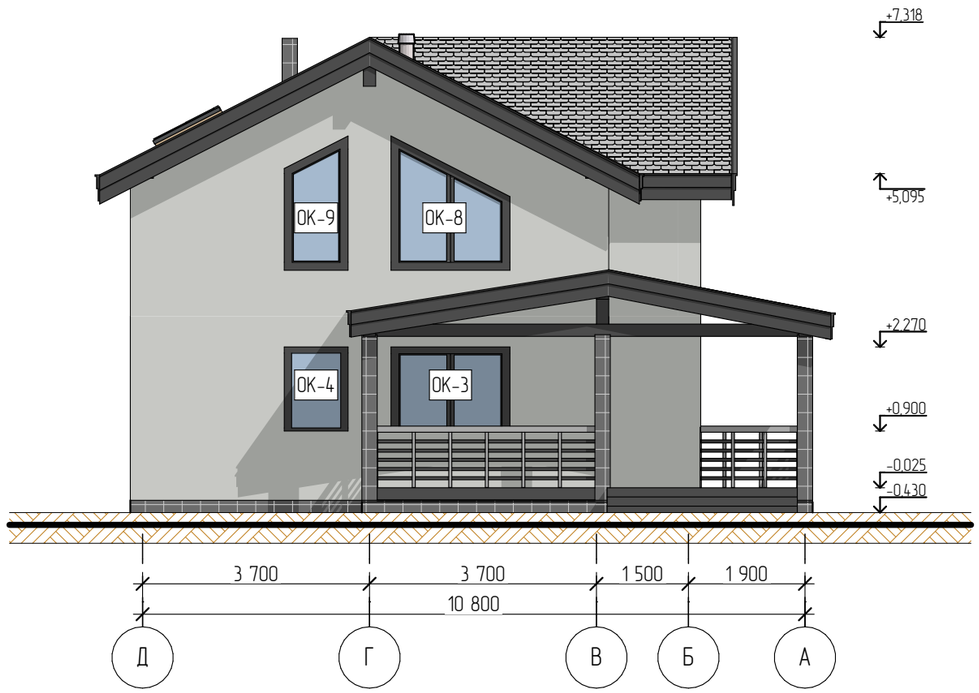

Примечание:
1) За отметку +0,000 принята отметка чистового пола первого этажа
2) За отметку +3,100 принята отметка чистового пола второго этажа
3) Номинальные высотные размеры могут отличаться от фактических.
4) Все декоративные элементы показаны условно.

					2021	#ID Проекта			
						Адрес: #Полный Адрес Участка; к/н: #ID Участка			
Изм.	Кол.уч	Лист	№док.	Подпись	Дата				
						Индивидуальный жилой дом	стадия	лист	листов
							ЭП	9	
Архитектор		Салыкова В.Г.							
						Фасады М 1:100			
Заказчик		#Обращение к Заказчику							


Согласовано

Взам. инв. №


Подпись и дата

Инв. № подл.

Фасад 5-1

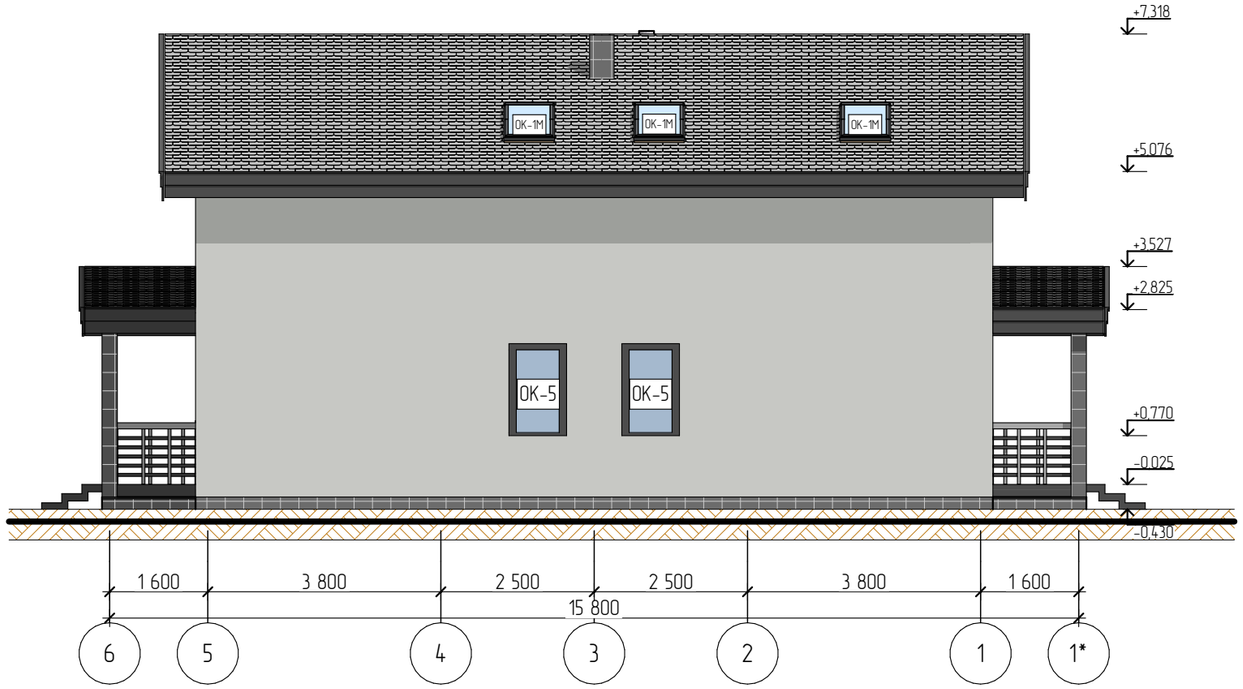

Фасад А-Д

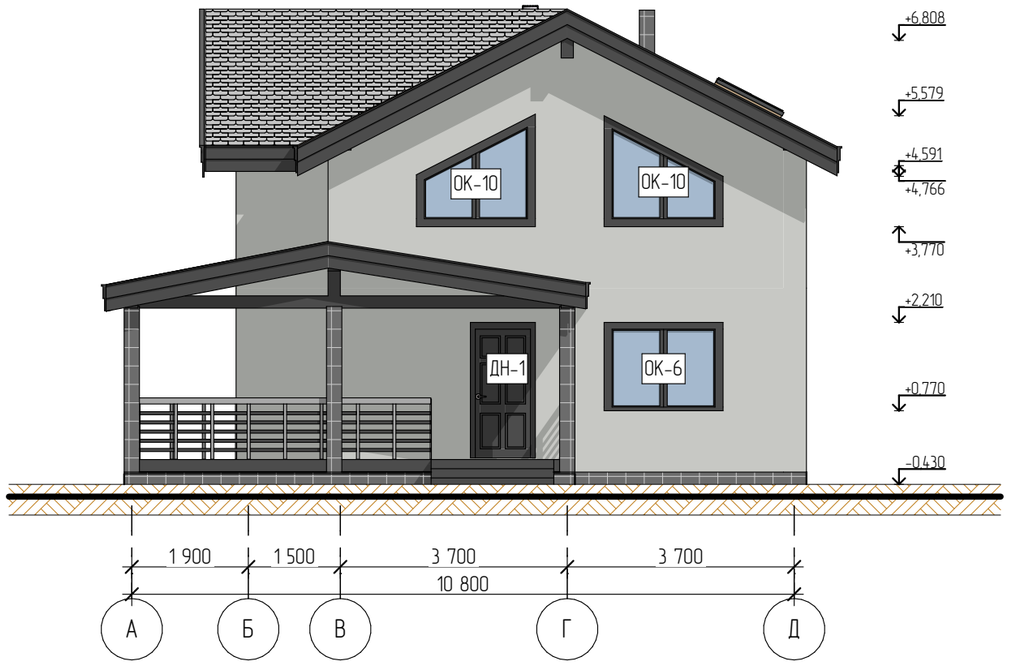

Примечание:
1) За отметку +0,000 принята отметка чистового пола первого этажа
2) За отметку +3,100 принята отметка чистового пола второго этажа
3) Номинальные высотные размеры могут отличаться от фактических.
4) Все декоративные элементы показаны условно.

					2021	#ID Проекта			
						Адрес: #Полный Адрес Участка; к/н: #ID Участка			
Изм.	Кол.уч	Лист	№док.	Подпись	Дата				
						Индивидуальный жилой дом	стадия	лист	листов
							ЭП	10	
Архитектор		Салыкова В.Г.							
Заказчик		#Обращение к Заказчику				Фасады М 1:100			

Согласовано


Взам. инв. №

Подпись и дата

Инв. № подл.

М 1:100

План ЖБ плиты

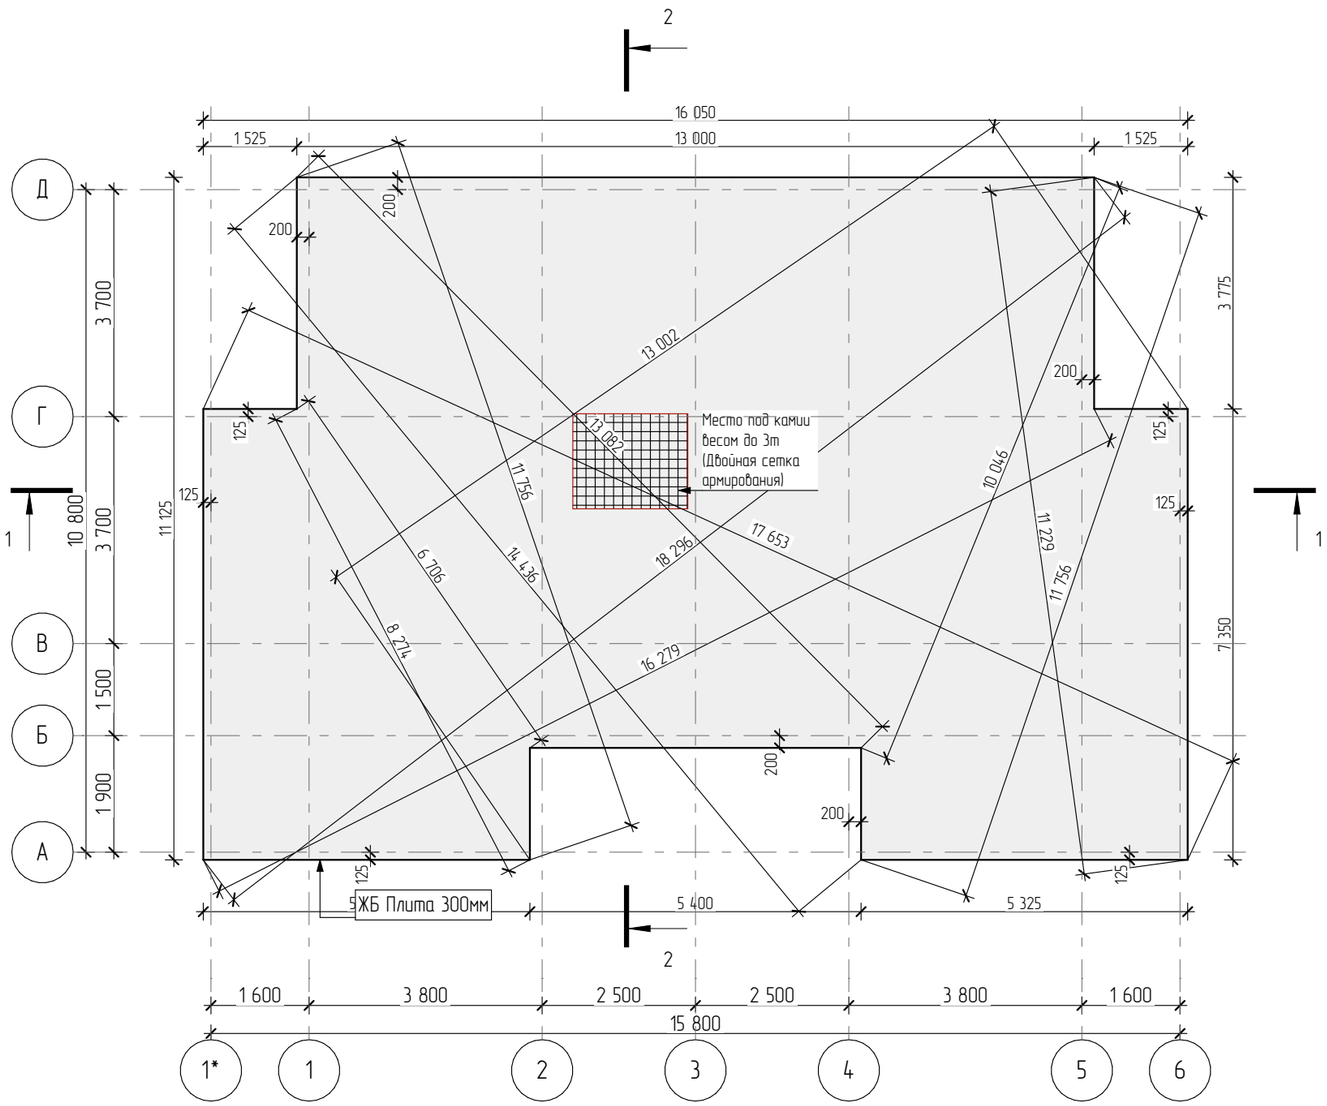

Примечание:

1) Отметка 0,000 задана по верху чистого пола первого этажа
2) Диагональная привязка фундамента осуществляется по наружной грани фундамента

					2021	#ID Проекта		
						Адрес: #Полный Адрес Участка		
Изм.	Кол.уч	Лист	№док.	Подпись	Дата			
						Индивидуальный жилой дом	стадия	лист	листов
							РП	11	
Архитектор		Салыкова В.Г.							
						План ЖБ плиты М 1:100			
Заказчик		#Обращение к Заказчику							

Согласовано:


Взам. инв. №

Подпись и дата

Инв. № подл.

М 1:100

Плита фундамента закладные

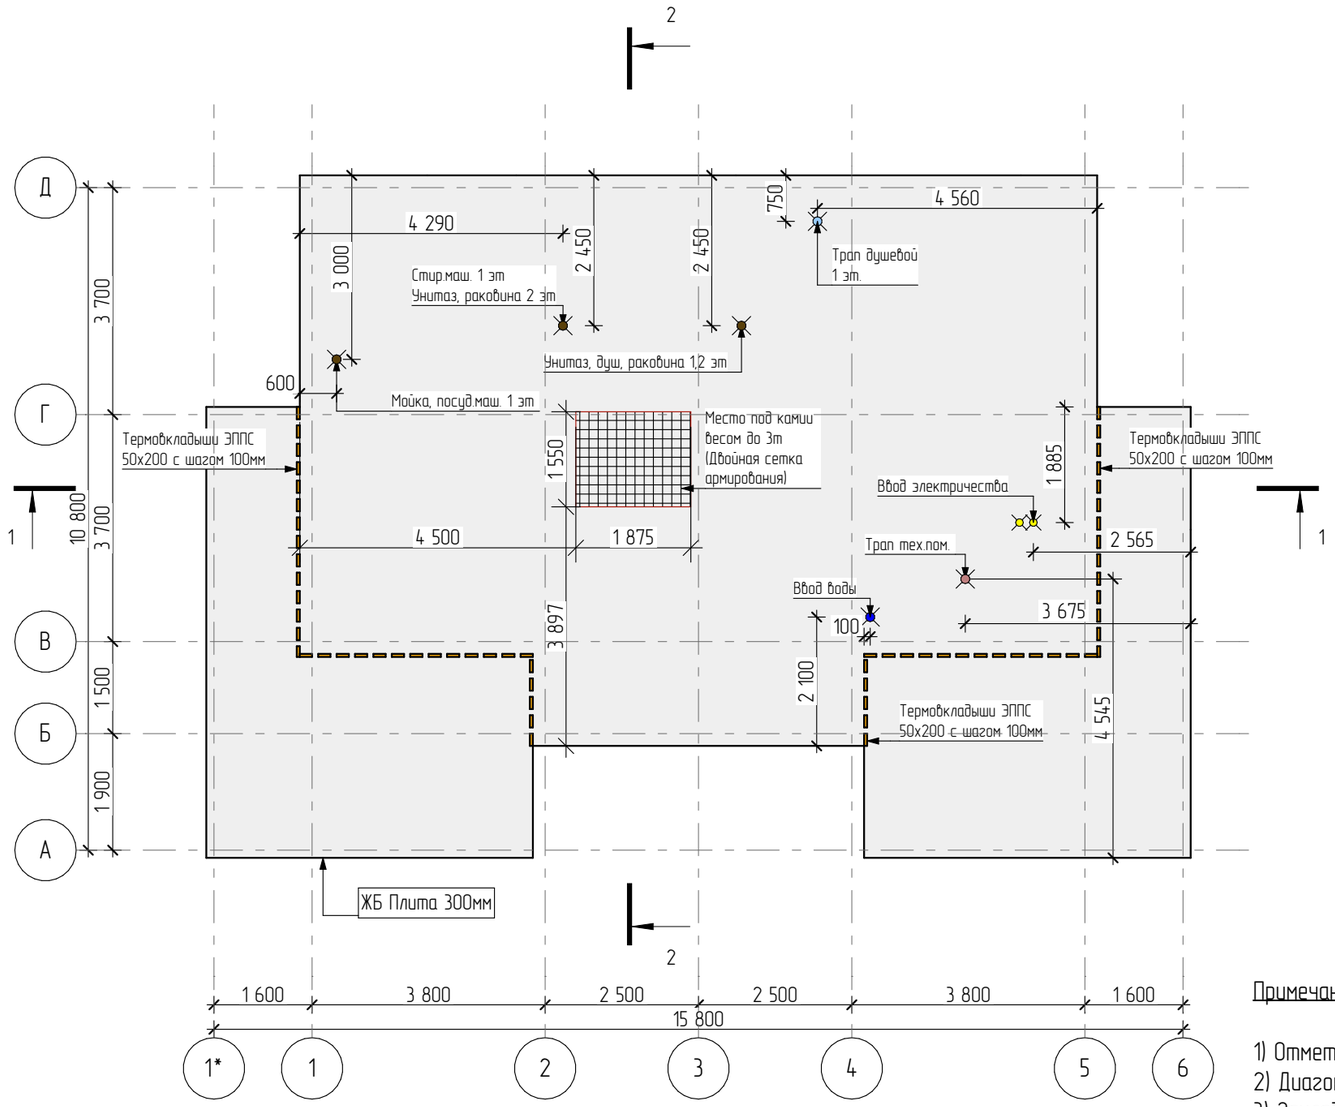

Примечание:

1) Отметка 0,000 задана по верху чистого пола первого этажа
2) Диагональная привязка фундамента осуществляется по наружной грани фундамента
3) Закладные в железобетонной плите перекрытия устанавливаются в соответствии с расположением сантехнических приборов во время заливки жб плиты.
4) Расположение вентиляционных коммуникаций и прочих инженерных систем показано условно. Точное расположение отверстий, их кол-во и типоразмеры уточнять по месту.
5) Рекомендуется к разработке проект инженерных коммуникаций. Количество и наличие вентиляционных, фановых и дымовых труб определяется дополнительным согласованием в сметном расчёте.


					2021	#ID Проекта		
						Адрес: #Полный Адрес Участка		
Изм.	Кол.уч	Лист	№док.	Подпись	Дата			
						Индивидуальный жилой дом	стадия: РП	лист: 12	листов:
Архитектор		Салыкова В.Г.						
Заказчик		#Обращение к Заказчику				План ЖБ плиты с закладными М 1:100		

Согласовано

Взам. инв. №

Подпись и дата

Инв. № подл.

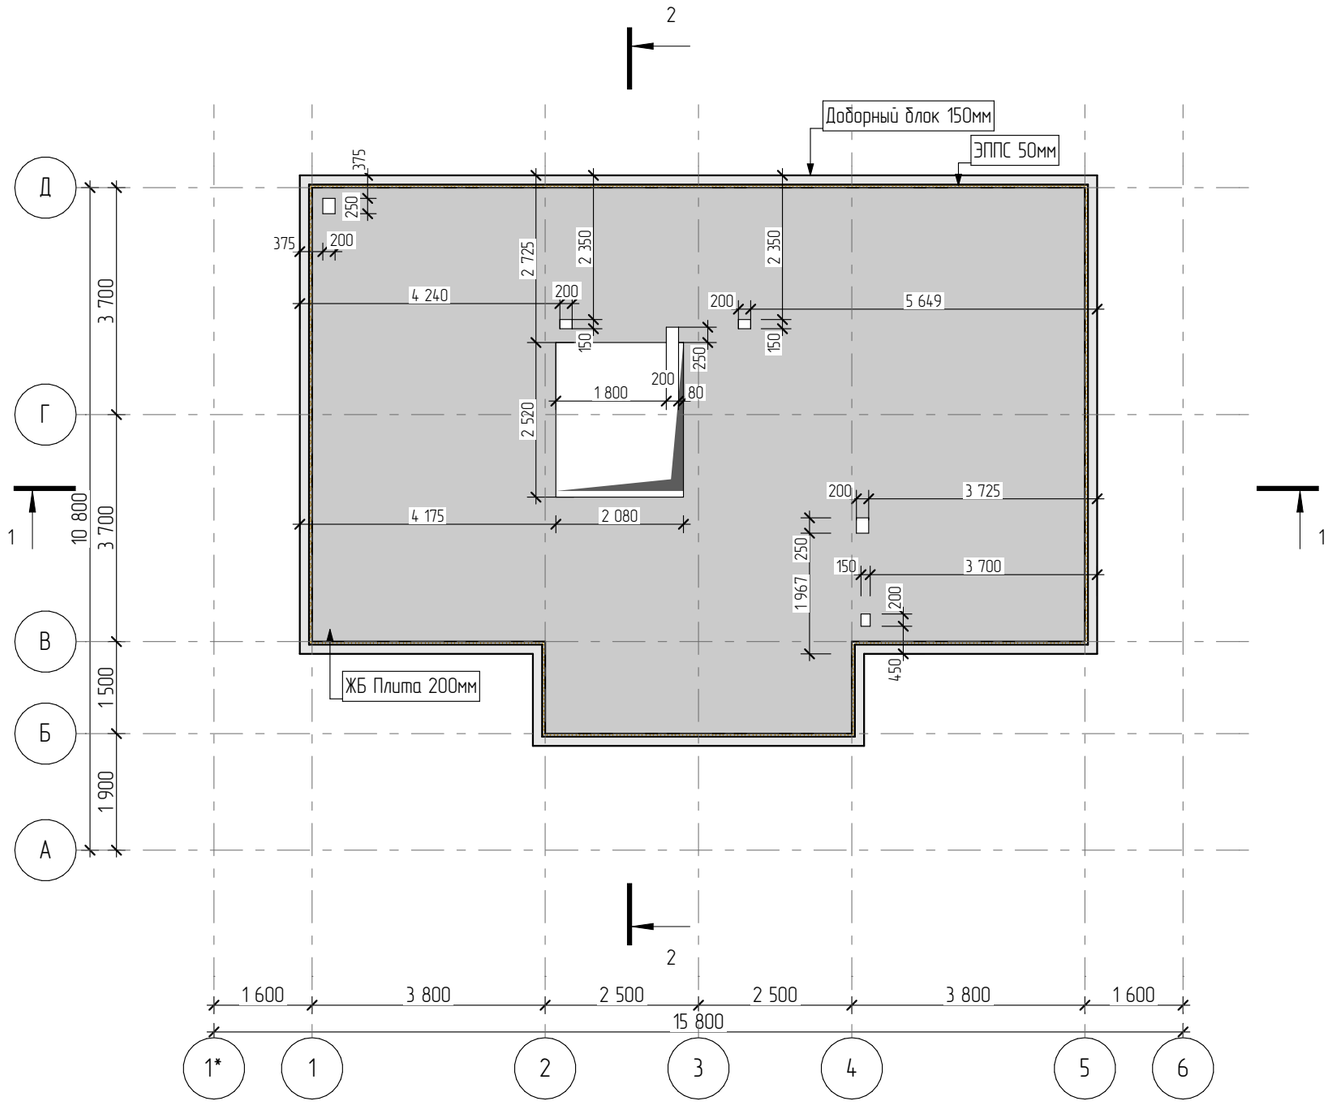

Согласовано

Взам. инв. №

Подпись и дата

Инв. № подл.

					2021
Изм.	Кол.уч	Лист	№док.	Подпись	Дата
Архитектор		Салыкова В.Г.			
Заказчик		#Обращение к Заказчику			

#ID Проекта


Адрес: #Полный Адрес Участка;
к/н: #ID Участка

Индивидуальный жилой дом	стадия	лист	листов
	ЭП	13	

План ЖБ межэтажной плиты

М 1:100

Монтажный план 1 этажа

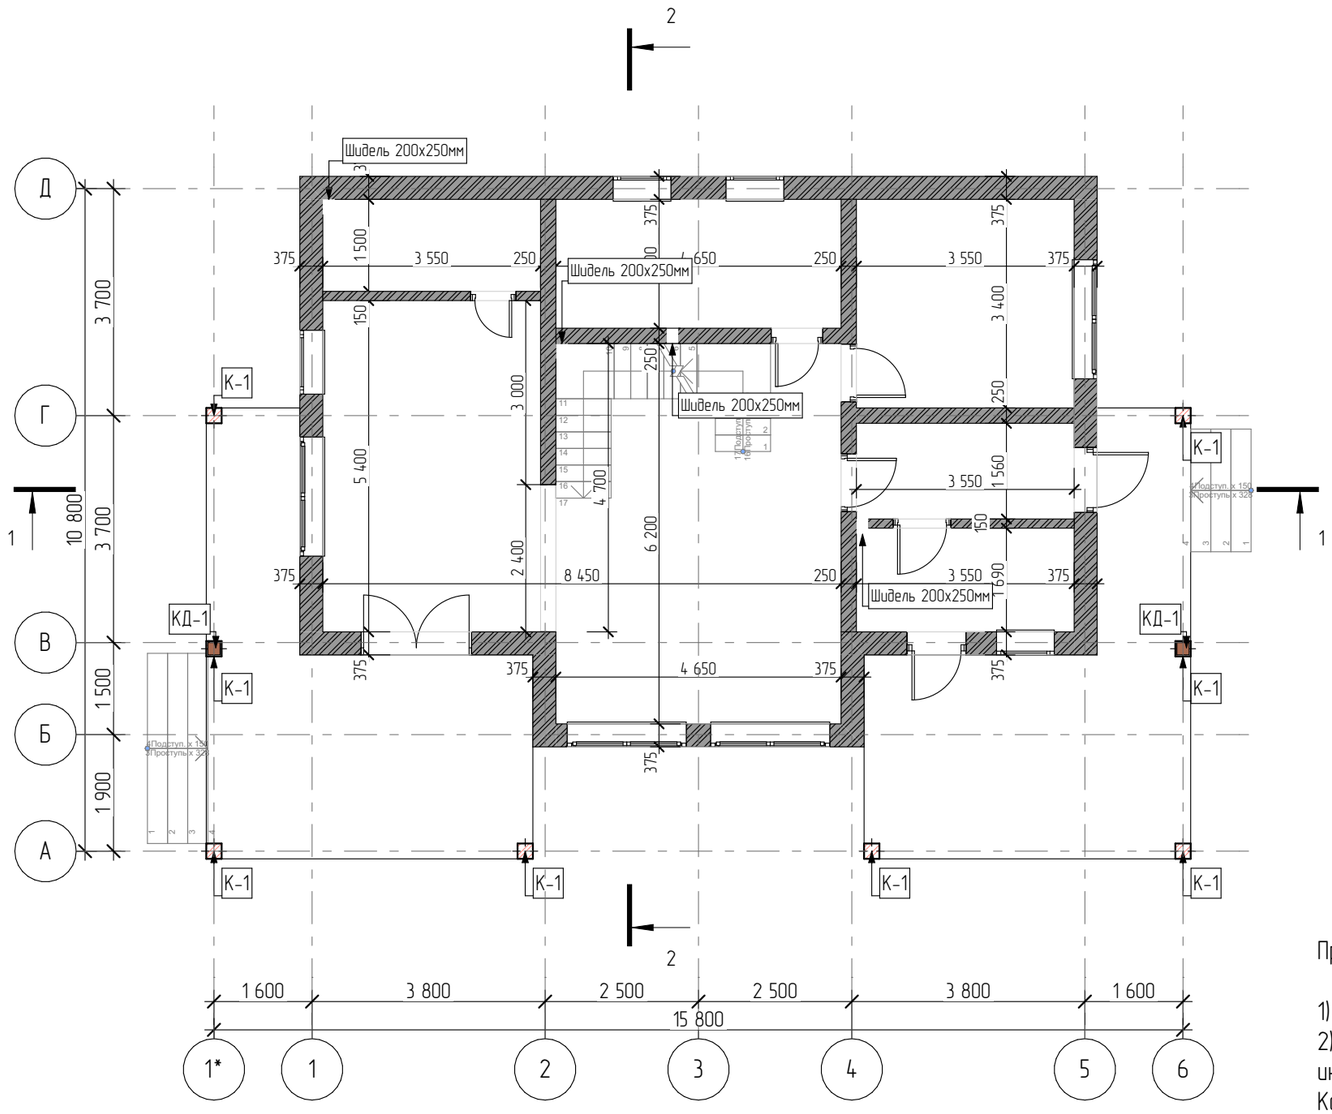

Примечание:

1) За отметку +-0,000 принята отметка чистового пола первого этажа
2) Расположение вентиляционных коммуникаций и прочих инженерных систем показано условно. Проект инженерных коммуникаций будет разрабатываться при заключении договора на инженерные работы. Количество и наличие вентиляционных, фановых и дымовых труб определяется дополнительным согласованием в сметном расчёте на этапе отделочных работ.
3) Габаритные размеры и расположение печи/камина могут измениться в процессе строительства
4) Ответственность за конструктивное решение и расположение печи/камина относительно фундамента, а также соблюдение мер пожарной безопасности при сооружении и эксплуатации печи/камина, полностью лежат на Заказчике

					2021	#ID Проекта		
						Адрес: #Полный Адрес Участка		
Изм.	Кол.уч	Лист	№док.	Подпись	Дата			
						Индивидуальный жилой дом	стадия	лист	листов
							РП	14	
Архитектор		Салыкова В.Г.							
Заказчик		#Обращение к Заказчику				План 1 этажа с размерами М 1:100			

Согласовано:


Взам. инв. №

Подпись и дата

Инв. № подл.

М 1:100

Монтажный план 2 этажа

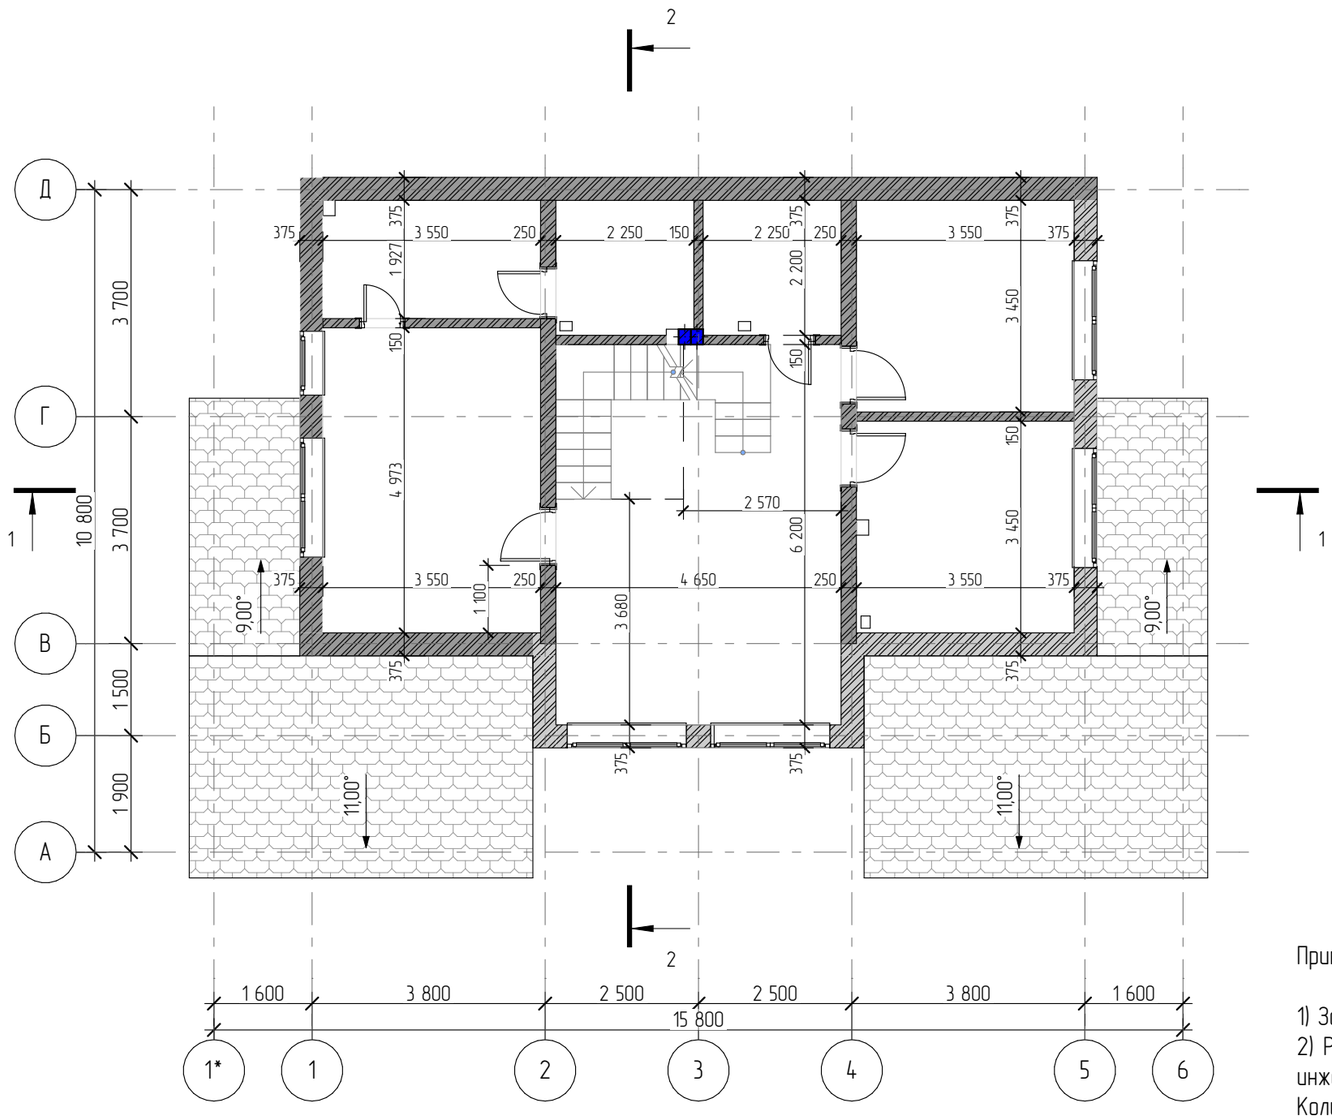

Примечание:

1) За отметку +3,100 принята отметка чистового пола второго этажа
2) Расположение вентиляционных коммуникаций и прочих инженерных систем показано условно. Проект инженерных коммуникаций будет разрабатываться при заключении договора на инженерные работы. Количество и наличие вентиляционных, фановых и дымовых труб определяется дополнительным согласованием в сметном расчёте на этапе отделочных работ.
3) Габаритные размеры и расположение печи/камина могут измениться в процессе строительства
4) Ответственность за конструктивное решение и расположение печи/камина относительно несущих конструкций, фундамента, а также соблюдение мер пожарной безопасности при сооружении и эксплуатации печи/камина, полностью лежат на Заказчике

					2021	#ID Проекта		
						Адрес: #Полный Адрес Участка		
Изм.	Кол.уч	Лист	№док.	Подпись	Дата			
						Индивидуальный жилой дом	стадия	лист	листов
							РП	15	
Архитектор		Салыкова В.Г.							
						План 2 этажа с размерами М 1:100			
Заказчик		#Обращение к Заказчику							

Согласовано:


Взам. инв. №

Подпись и дата

Инв. № подл.

М 1:100

Маркировочный план 1 этажа

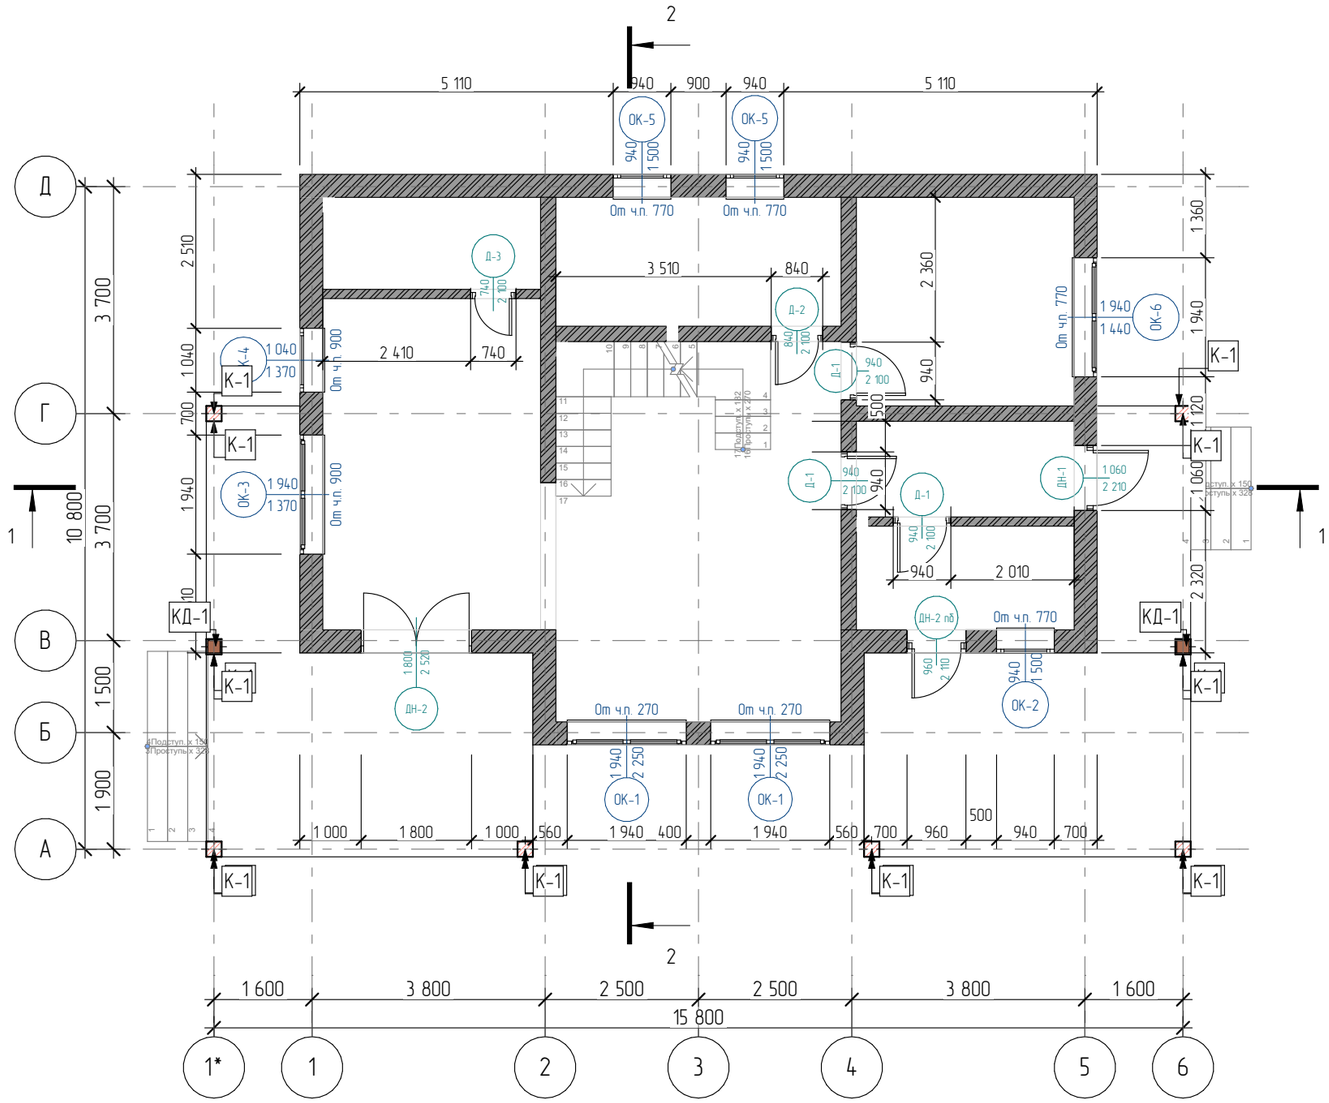

Согласовано

Взам. инв. №


Подпись и дата

Инв. № подл.

					2021	#ID Проекта			
						Адрес: #Полный Адрес Участка			
Изм.	Кол.уч	Лист	№док.	Подпись	Дата				
						Индивидуальный жилой дом	стадия	лист	листов
							РП	16	
Архитектор		Салыкова В.Г.				Маркировочный план 1 этажа М 1:100			
Заказчик		#Обращение к Заказчику							

М 1:100

Маркировочный план 2 этажа

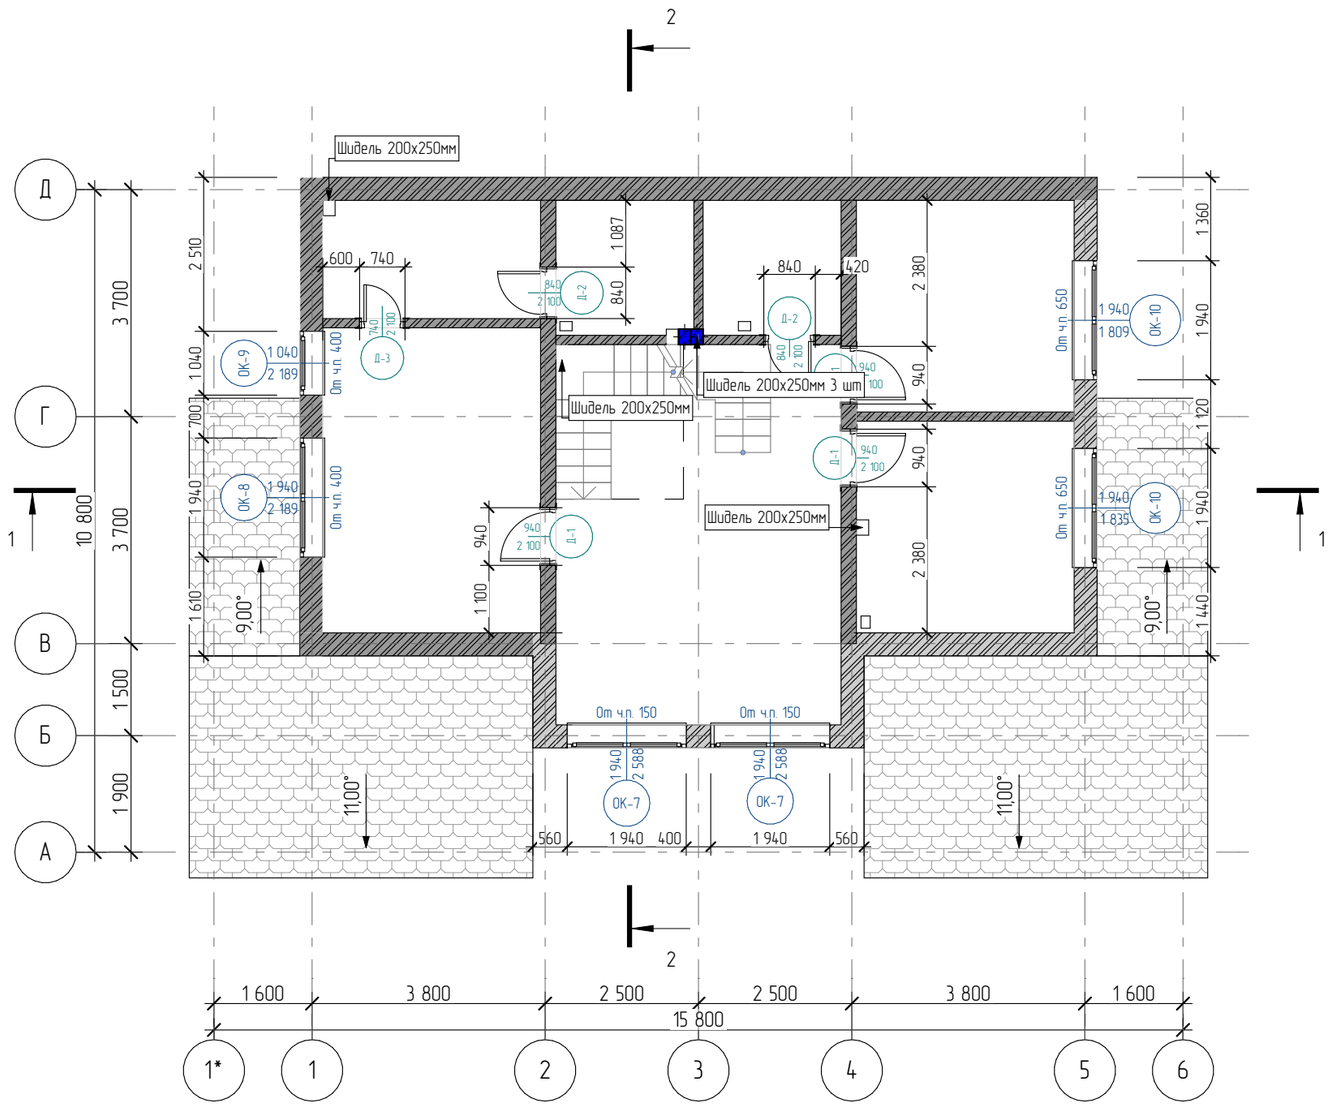

Согласовано:

Взам. инв. №


Подпись и дата

Инв. № подл.

					2021	#ID Проекта			
						Адрес: #Полный Адрес Участка			
Изм.	Кол.уч	Лист	№док.	Подпись	Дата				
						Индивидуальный жилой дом	стадия	лист	листов
							РП	17	
Архитектор		Салыкова В.Г.				Маркировочный план 2 этажа М 1:100			
Заказчик		#Обращение к Заказчику							


М 1:25

1

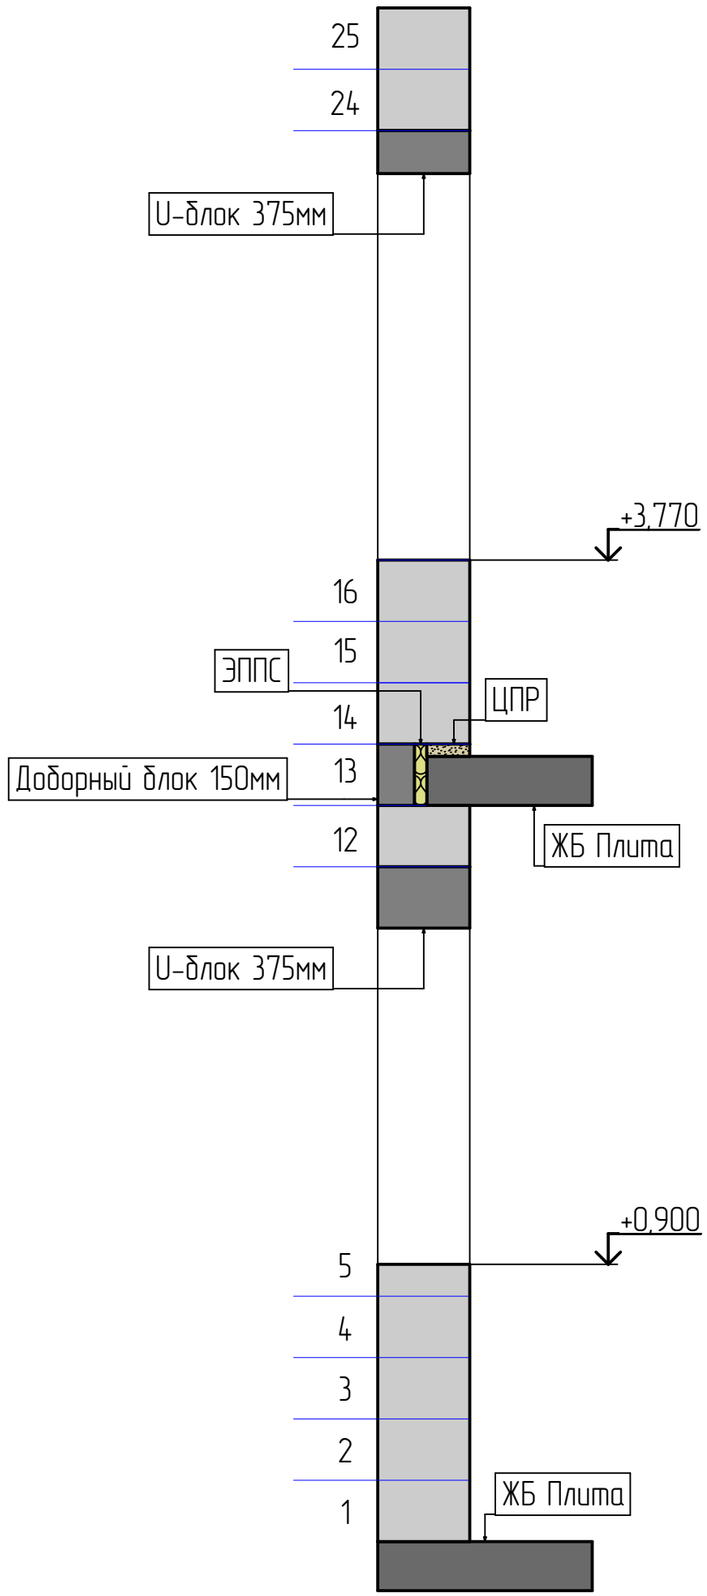

М 1:25

2

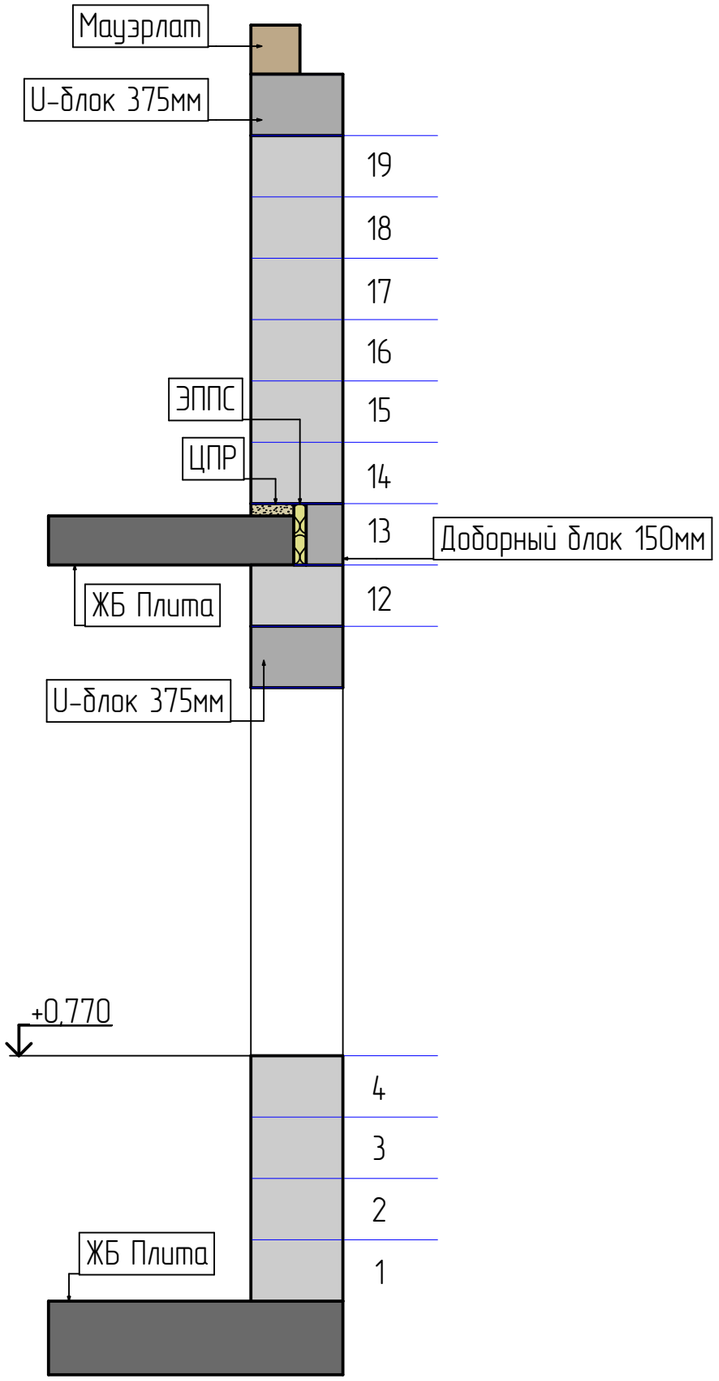


Согласовано:


Взам. инв. №

Подпись и дата

Инв. № подл.

					2021	#ID Проекта	
						Адрес: #Полный Адрес Участка	
Изм.	Кол.уч	Лист	№док.	Подпись	Дата		
						Индивидуальный жилой дом	стадия: РП; лист: 18; листов:
Архитектор		Салыкова В.Г.					
Заказчик		#Обращение к Заказчику				Фрагменты разрезов М 1:25	

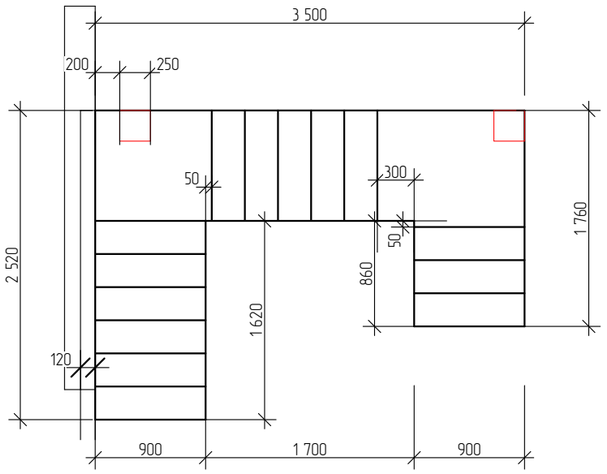

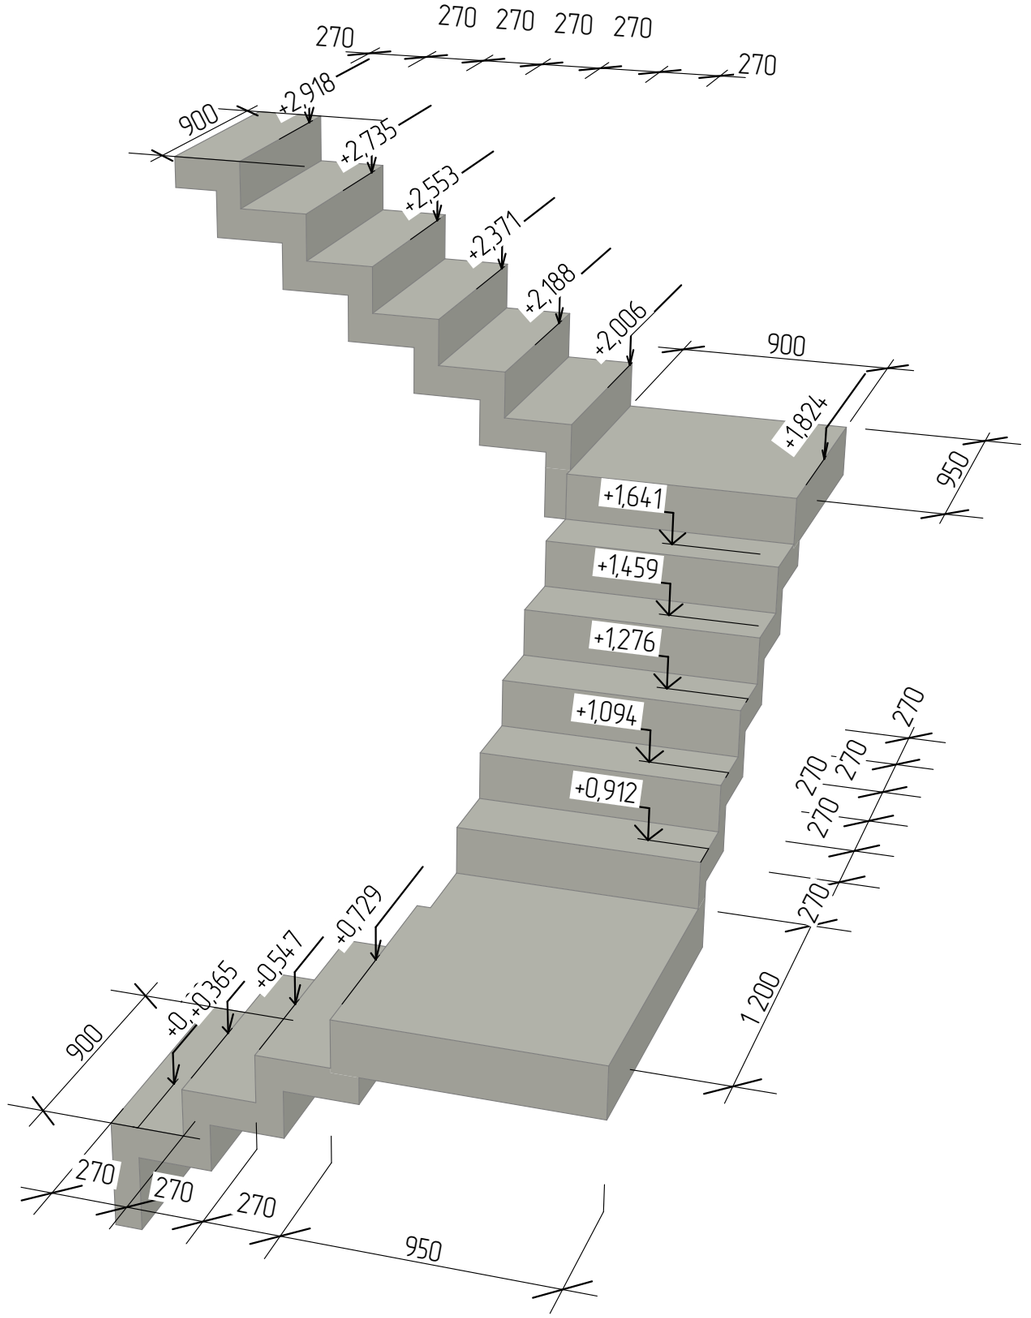

Согласовано:

Взам. инв. №


Подпись и дата

Инв. № подл.

					2021	#ID Проекта			
						Адрес: #Полный Адрес Участка			
Изм.	Кол.уч	Лист	№док.	Подпись	Дата				
						Индивидуальный жилой дом	стадия	лист	листов
							РП	19	
Архитектор		Салыкова В.Г.				Схема устройства ЖБ лестницы			
Заказчик		#Обращение к Заказчику							

М 1:100

План кровли

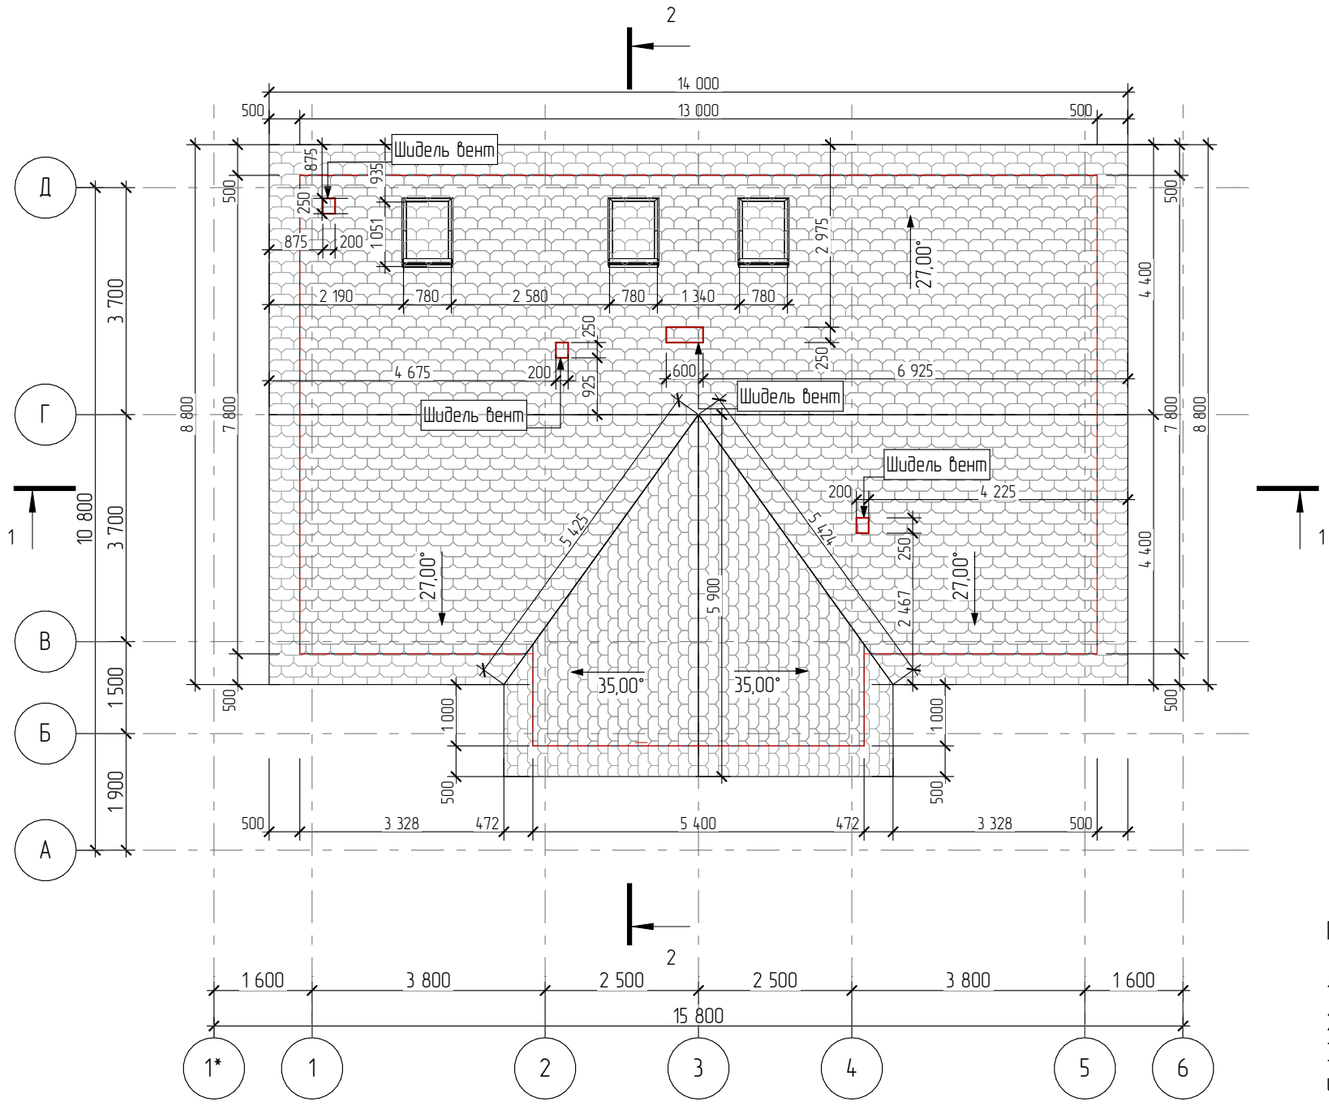

Условные обозначения:

- - - - - - контур наружной стены

Примечание:

1) Все размеры даны в горизонтальной проекции
2) Наличие снегозадержателей и водосточной системы определяется сметным расчётом.
3) Монтаж кровельного покрытия выполнять в соответствии с инструкциями завода-изготовителя.
4) Расположение вентиляционных коммуникаций и прочих инженерных систем показано условно. Проект инженерных коммуникаций будет разрабатываться при заключении договора на инженерные работы. Количество и наличие вентиляционных, фановых и дымовых труб определяется дополнительным согласованием в сметном расчёте на этапе отделочных работ.

Согласовано:

Взам. инв. №

Подпись и дата

Инв. № подл.

					2021	#ID Проекта	
						Адрес: #Полный Адрес Участка	
Изм.	Кол.уч	Лист	№док.	Подпись	Дата		
						Индивидуальный жилой дом	стадия: РП; лист: 20; листов:
Архитектор		Салыкова В.Г.					
Заказчик		#Обращение к Заказчику				План кровли М 1:100	



Общий вид крыши

Лист 21

Согласовано

Взам. инв. №

Подпись и дата

Инв. № подл.

Общий вид 1



Общий вид 2



Общий вид 3



Общий вид 4



Согласовано

Взам. инв. №

Подпись и дата

Инв. № подл.

Общие виды

Лист

22


Общий вид 1 этаж




Общий вид 1 этаж



Общий вид 2 этаж

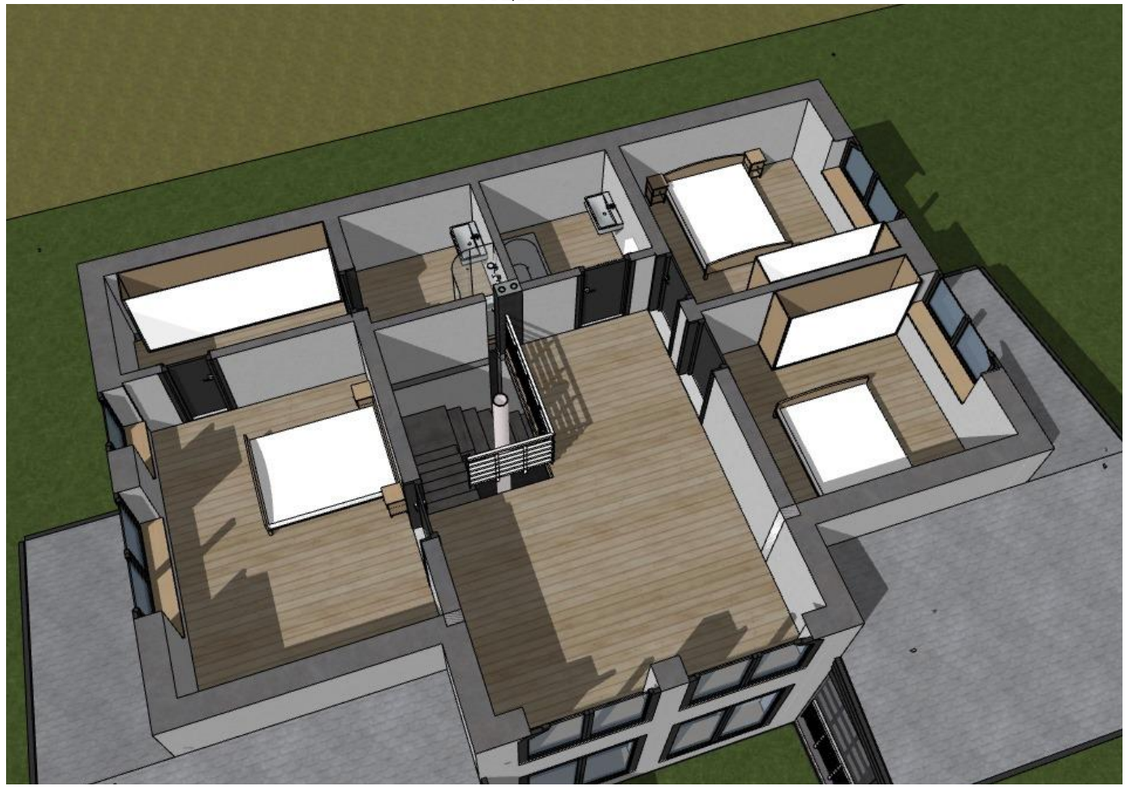

Общий вид 2 этаж

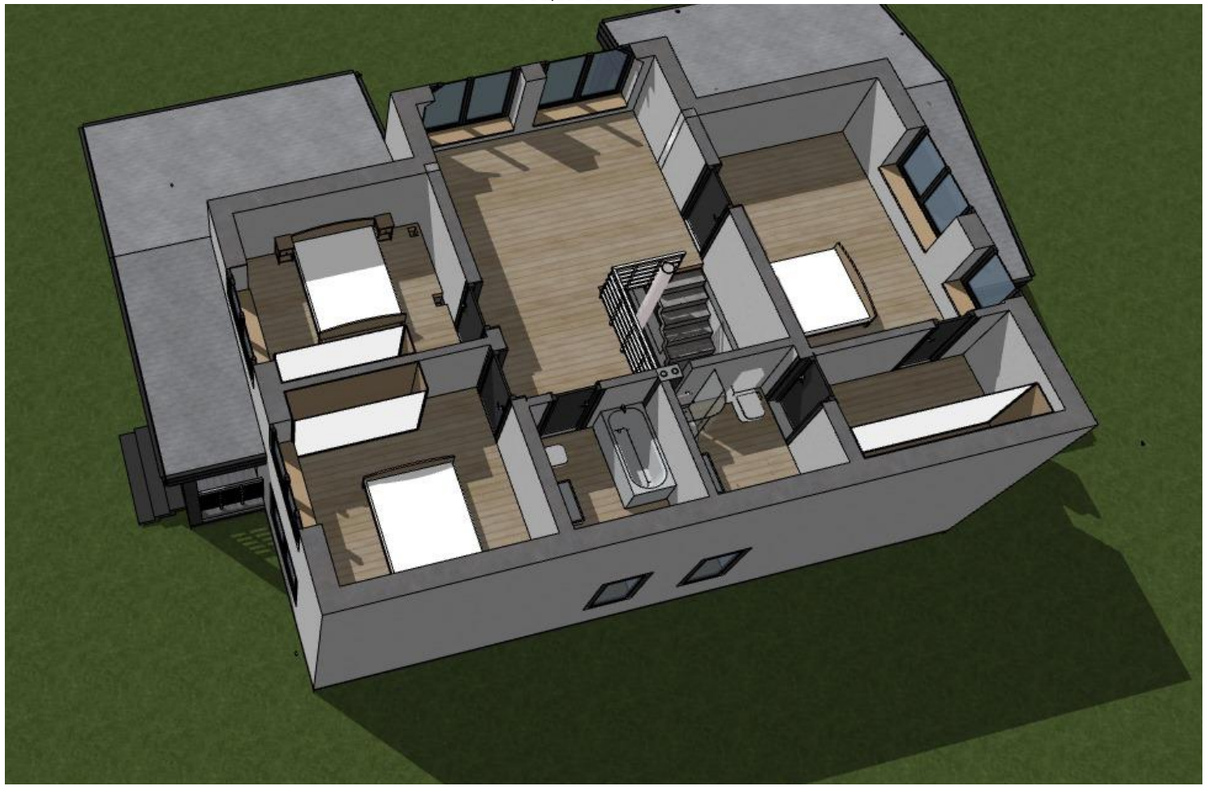

Согласовано

Взам. инв. №













Подпись и дата

Инв. № подл.

Общие виды (поэтажные)

Лист

23

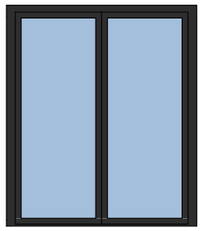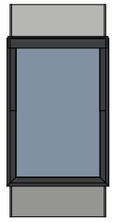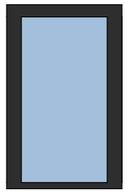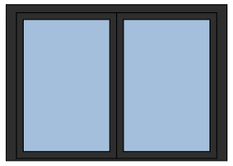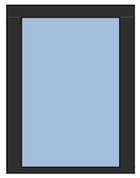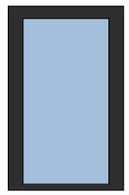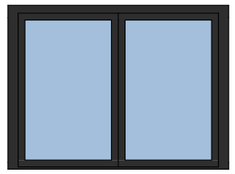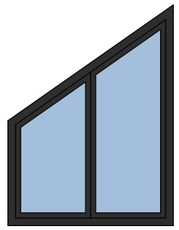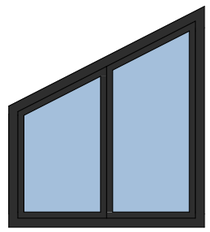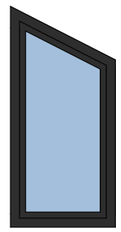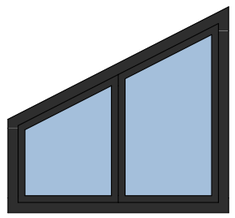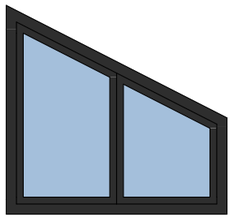Поз.	ОК-1	ОК-1М	ОК-2	ОК-3
Общий вид				
Проем, мм	1 800×2 200	---	800×1 450	1 800×1 320
Поз.	ОК-4	ОК-5	ОК-6	ОК-7
Общий вид				
Проем, мм	900×1 320	800×1 450	1 800×1 390	1 800×2 448
Поз.	ОК-8	ОК-9	ОК-10	ОК-10
Общий вид				
Проем, мм	1 800×2 049	900×2 049	1 800×1 669	1 800×1 695

Спецификация оконных проемов и заполнений

Поз.	Размеры проема, мм.	Размеры блока, мм.	Кол-во, шт	Этаж	Примечание
ОК-1	1 940×2 250	1 800×2 200	2	1 этаж	
ОК-2	940×1 500	800×1 450	1	1 этаж	
ОК-3	1 940×1 370	1 800×1 320	1	1 этаж	
ОК-4	1 040×1 370	900×1 320	1	1 этаж	
ОК-5	940×1 500	800×1 450	2	1 этаж	
ОК-6	1 940×1 440	1 800×1 390	1	1 этаж	
ОК-7	1 940×2 588	1 800×2 448	2	2 этаж	Косое
ОК-8	1 940×2 189	1 800×2 049	1	2 этаж	Косое
ОК-9	1 040×2 189	900×2 049	1	2 этаж	Косое
ОК-10	1 940×1 809	1 800×1 669	1	2 этаж	Косое
ОК-10	1 940×1 835	1 800×1 695	1	2 этаж	Косое

Мансардные окна Спецификация

Поз.	Обозначение	Проем, мм	Кол-во, шт	Этаж	Примечание
ОК-1М		780×1 180	3	Кровля	

Примечание:

1) Открывание окон, итоговые размеры оконных/дверных проемов и блоков, и их конструкции, расположение, кол-во, наличие шпросов, а также доп. декоративных и конструктивных элементов согласовывается с фирмой производителем/Подрядчиком.

2) Окна показаны снаружи.

3) Итоговый материал изготовления окон определяется сметным расчётом


Согласовано:

Взам. инв. №

Подпись и дата

Инв. № подл.

					2021	#ID Проекта			
						Адрес: #Полный Адрес Участка			
Изм.	Кол.уч	Лист	№док.	Подпись	Дата				
						Индивидуальный жилой дом	стадия	лист	листов
Архитектор		Салыкова В.Г.					РП	24	
Заказчик		#Обращение к Заказчику				Спецификация заполнения оконных проёмов			

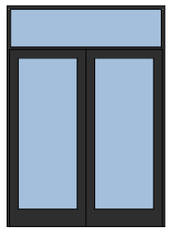Поз.	Д-1	Д-2	Д-3
Общий вид			
Проем, мм	800×2 000	700×2 000	600×2 000
Поз.	ДН-1	ДН-2	ДН-2
Общий вид			
Проем, мм	900×2 100	1 800×2 520	2 400×2 100
Поз.	ДН-2 пб		
Общий вид			
Проем, мм	800×2 000		

Примечание:

1) Открывание дверных проемов; расположение, количество и наличие шпросов согласовывается с фирмой производителем в отдельной спецификации.

2) Двери показаны снаружи.

3) Итоговый материал изготовления дверей определяется сметным расчётом

Спецификация дверных проемов и заполнений

Поз.	Размеры проема	Размеры Блока	Кол-во, шт	Этаж	Примечание
Д-1	940×2 100	880×2 040	3	1 этаж	
Д-1	940×2 100	880×2 040	3	2 этаж	
Д-2	840×2 100	780×2 040	1	1 этаж	
Д-2	840×2 100	780×2 040	2	2 этаж	
Д-3	740×2 100	680×2 040	1	1 этаж	
Д-3	740×2 100	680×2 040	1	2 этаж	
ДН-1	1 060×2 210	1 000×2 150	1	1 этаж	
ДН-2	1 800×2 520	1 800×2 520	1	1 этаж	
ДН-2	2 400×2 100	2 400×2 100	1	1 этаж	
ДН-2 пб	960×2 110	900×2 050	1	1 этаж	

Согласовано

Взам. инв. №

Подпись и дата

Инв. № подл.

Изм.	Кол.уч	Лист	№док.	Подпись	Дата
					2021
Архитектор		Салыкова В.Г.			
Заказчик		#Обращение к Заказчику			

#ID Проекта

Адрес: #Полный Адрес Участка

Индивидуальный жилой дом

стадия	лист	листов
РП	25	

Спецификация заполнения дверных проёмов