ОБЪЕКТ ИНДИВИДУАЛЬНОГО ЖИЛИЩНОГО СТРОИТЕЛЬСТВА



ЭСКИЗНЫЙ ПРОЕКТ


ШИФР: #ID ПРОЕКТА

АРХИТЕКТУРНЫЕ РЕШЕНИЯ

САНКТ-ПЕТЕРБУРГ 2021

М 1:100

План 1 этажа с расстановкой мебели

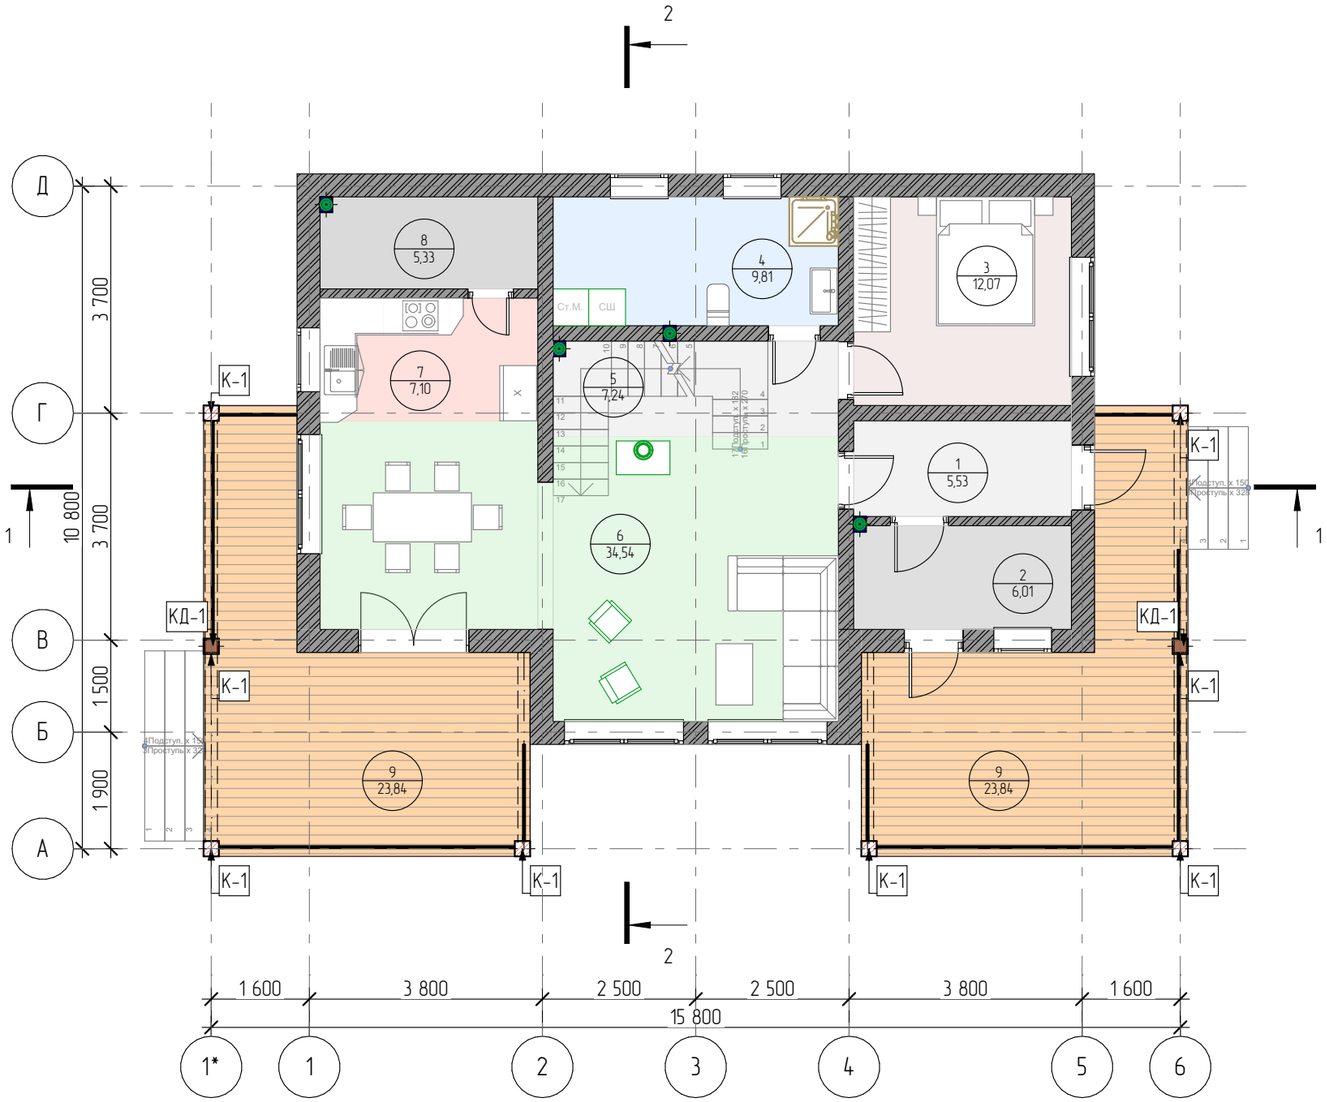

Экспликация 1 этажа

Расположение поиещений	№ п/п	Наименование	Площадь, м2
Внутр. пом.			
	1	Тамбур	5,53
	2	Котельная	6,01
	3	Спальня	12,07
	4	Постирочная	9,81
	5	Лестничный холл	7,24
	6	Гостиная-Столовая	34,54
	7	Кухня	7,10
	8	Кладовая	5,33
			87,63 м²
Наружн. пом.			
	9	Терраса	23,84
	9	Терраса	23,84
			47,68 м²
			135,31 м²

Согласовано

Взам. инв. №

Подпись и дата

Инв. № подл.

					2021
Изм.	Кол.уч	Лист	№док.	Подпись	Дата

#ID Проекта

Адрес: #Полный Адрес Участка

Архитектор	Салыкова В.Г.		
Заказчик	#Обращение к Заказчику		


Индивидуальный жилой дом

стадия	лист	листов
РП	1	

План 1 этажа с расстановкой мебели
М 1:100

М 1:100

План 2 этажа с расстановкой мебели

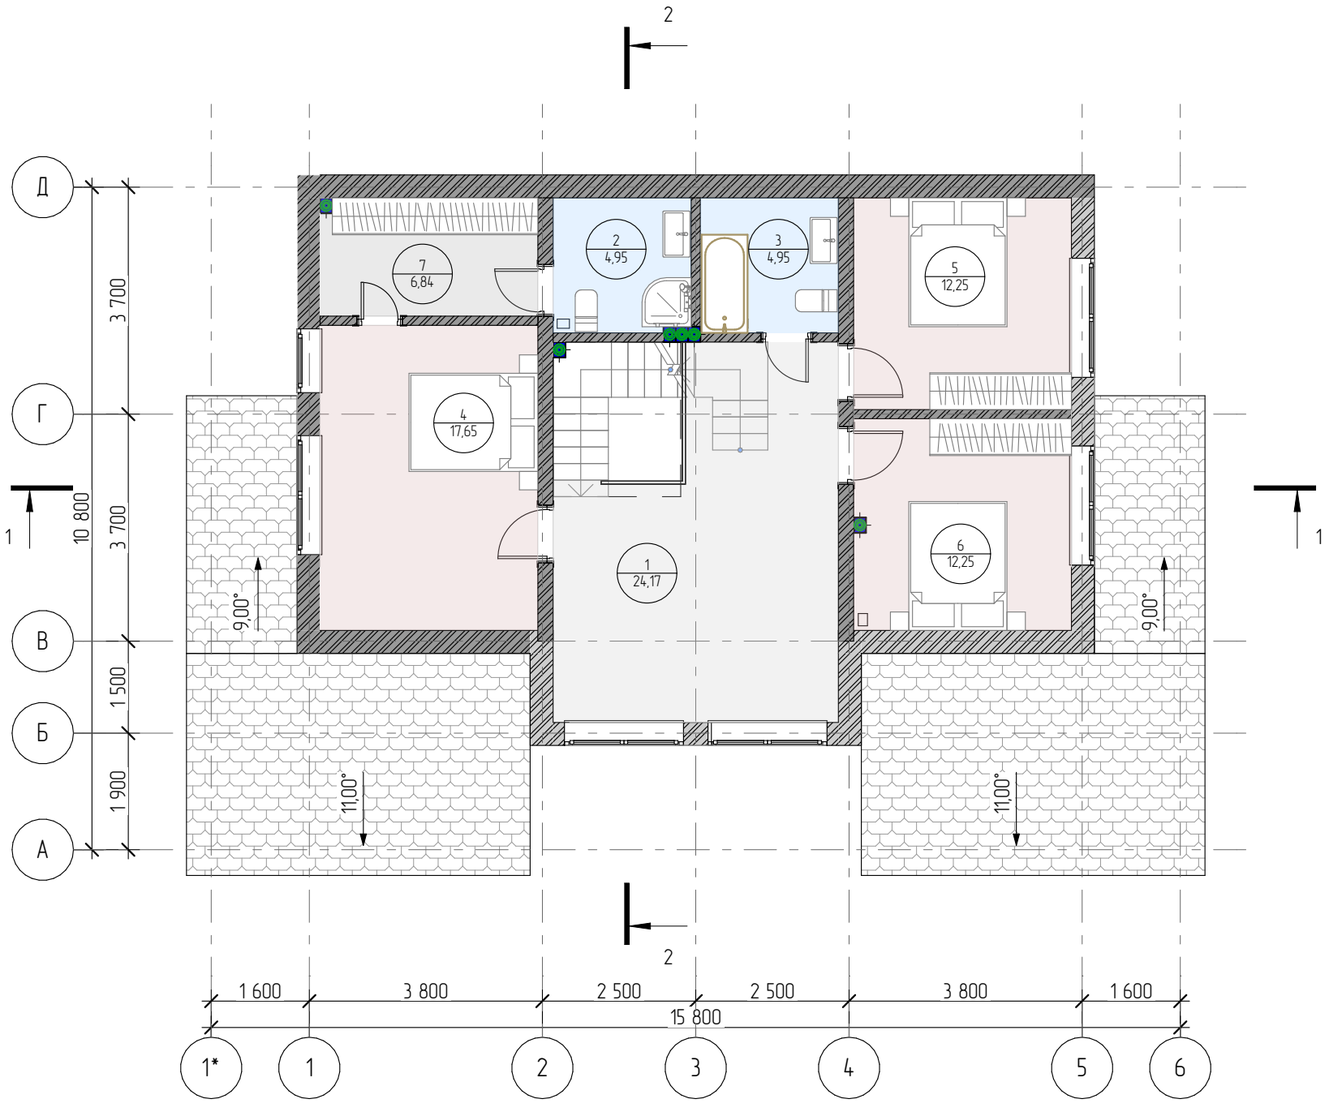

Экспликация 2 этажа

Расположение поиещений	№ п/п	Наименование	Площадь, м2
Внутр. пом.			
	1	Холл	24,17
	2	Санузел 1	4,95
	3	Санузел 2	4,95
	4	Мастер-спальня	17,65
	5	Спальня 1	12,25
	6	Спальня 2	12,25
	7	Гардероб	6,84
			83,06 м²

Согласовано:

Взам. инв. №

Подпись и дата


Инв. № подл.

					2021	#ID Проекта			
						Адрес: #Полный Адрес Участка			
Изм.	Кол.уч	Лист	№док.	Подпись	Дата				
						Индивидуальный жилой дом	стадия	лист	листов
							РП	2	
Архитектор		Салыкова В.Г.				План 2 этажа с расстановкой мебели М 1:100			
Заказчик		#Обращение к Заказчику							

Фасад 1-5



Фасад Д-А

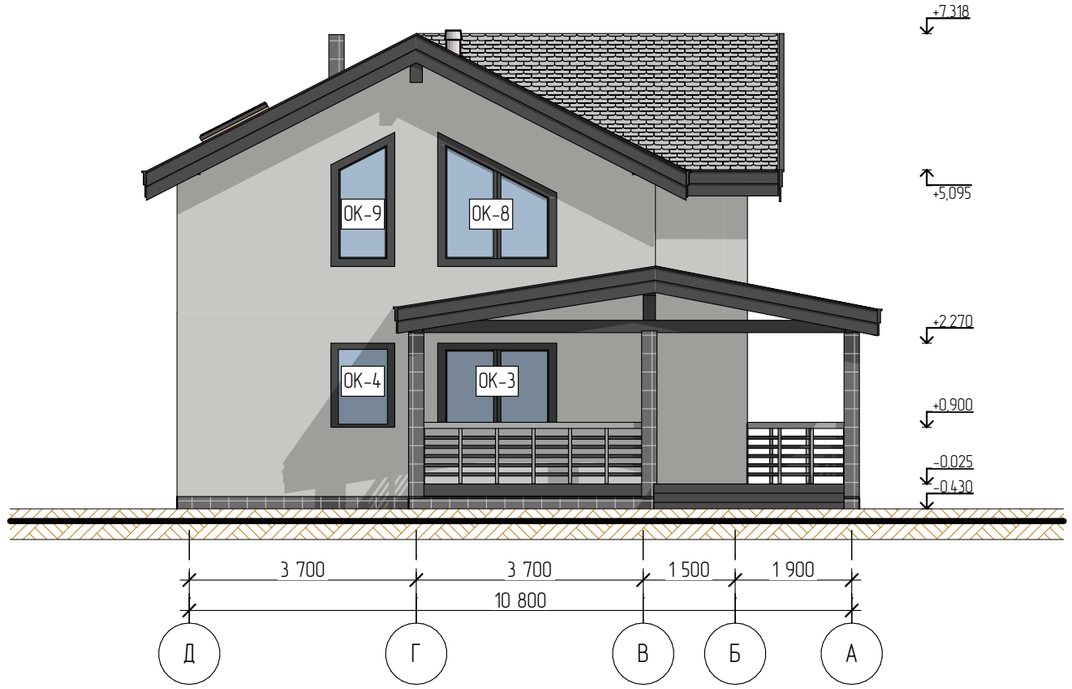

Согласовано:


Взам. инв. №

Подпись и дата


Инв. № подл.

					2021	#ID Проекта			
						Адрес: #Полный Адрес Участка			
Изм.	Кол.уч	Лист	№док.	Подпись	Дата				
						Индивидуальный жилой дом	стадия	лист	листов
							РП	3	
Архитектор		Салыкова В.Г.							
Заказчик		#Обращение к Заказчику				Фасады М 1:100			

Фасад 5-1

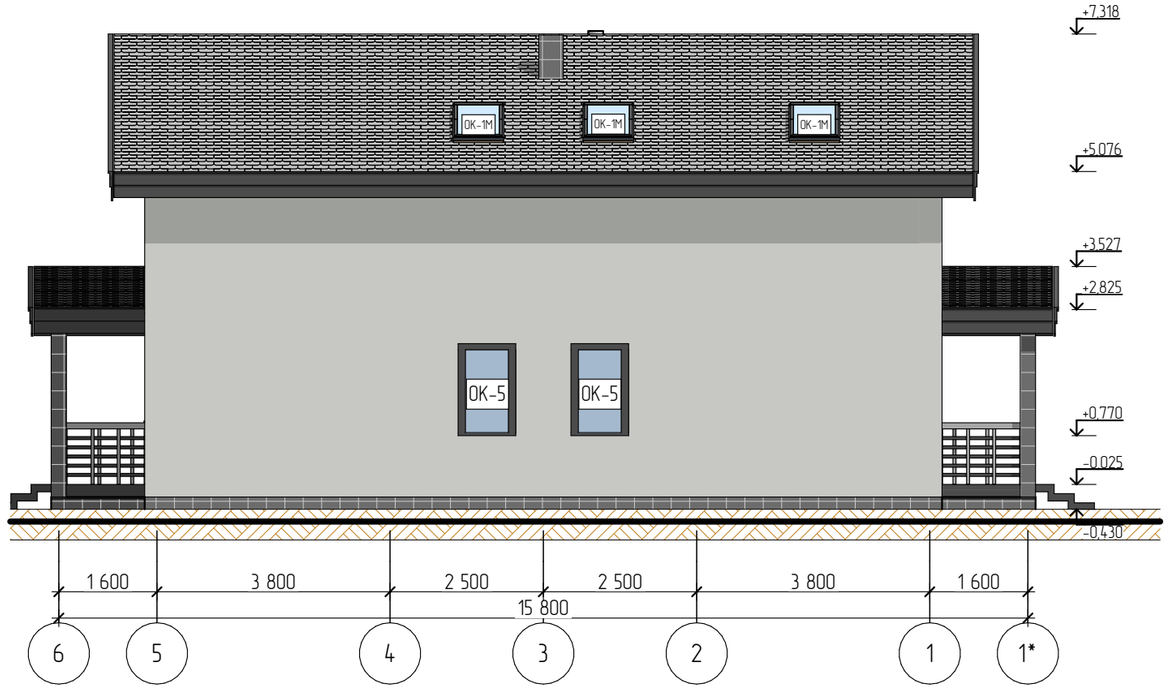

Фасад А-Д

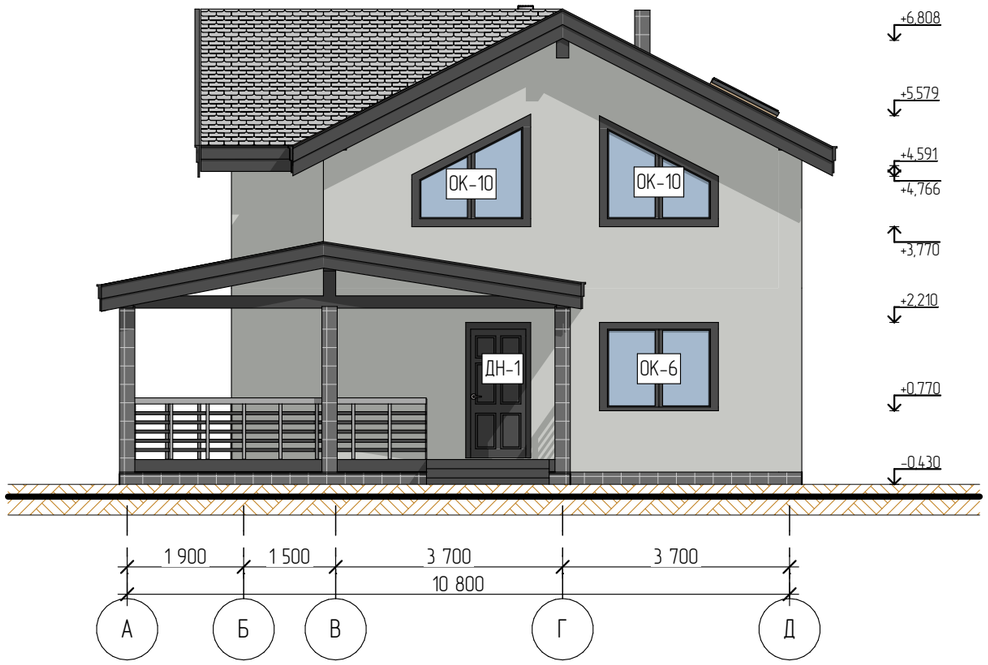

Согласовано

Взам. инв. №

Подпись и дата

Инв. № подл.

					2021	#ID Проекта	
						Адрес: #Полный Адрес Участка	
Изм.	Кол.уч	Лист	№док.	Подпись	Дата		
						Индивидуальный жилой дом	стадия: РП; лист: 4; листов:
Архитектор		Салыкова В.Г.					
Заказчик		#Обращение к Заказчику				Фасады М 1:100	

Общий вид 1



Общий вид 2



Общий вид 3



Общий вид 4



Согласовано

Взам. инв. №

Подпись и дата

Инв. № подл.

Общие виды

Лист

5


Общий вид 1 этаж




Общий вид 1 этаж



Общий вид 2 этаж

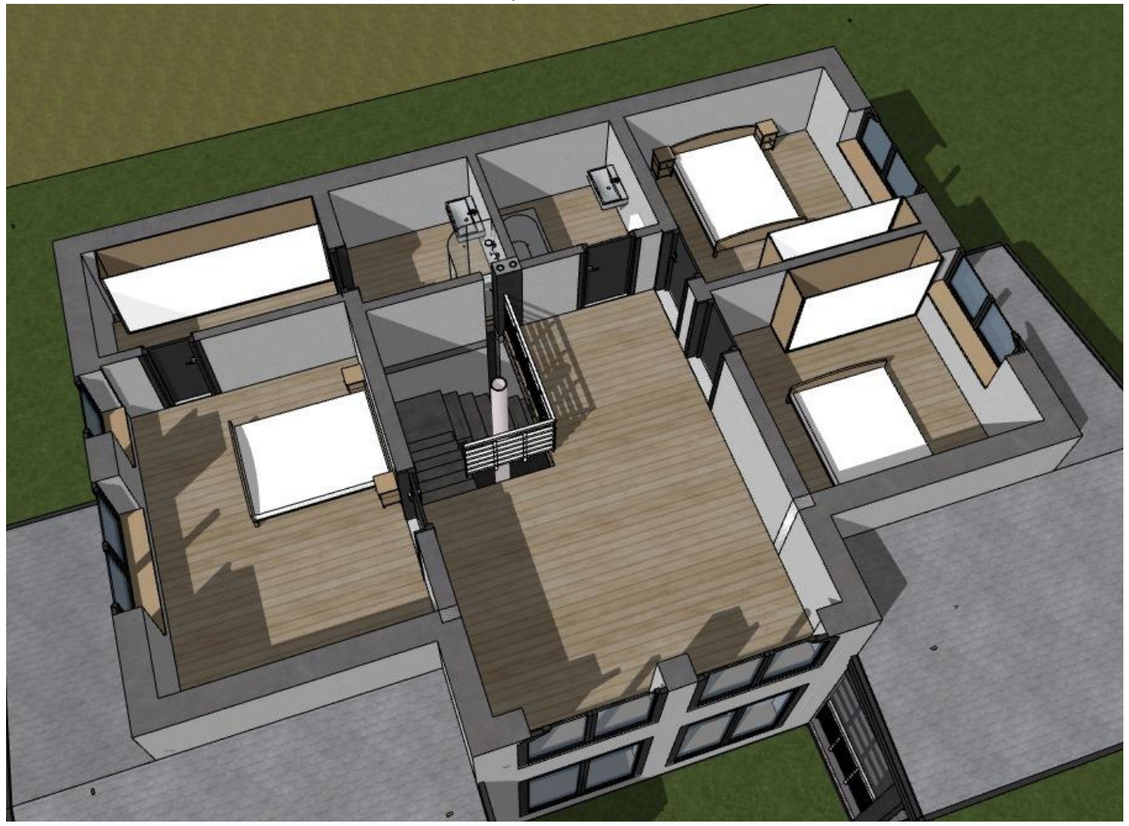

Общий вид 2 этаж

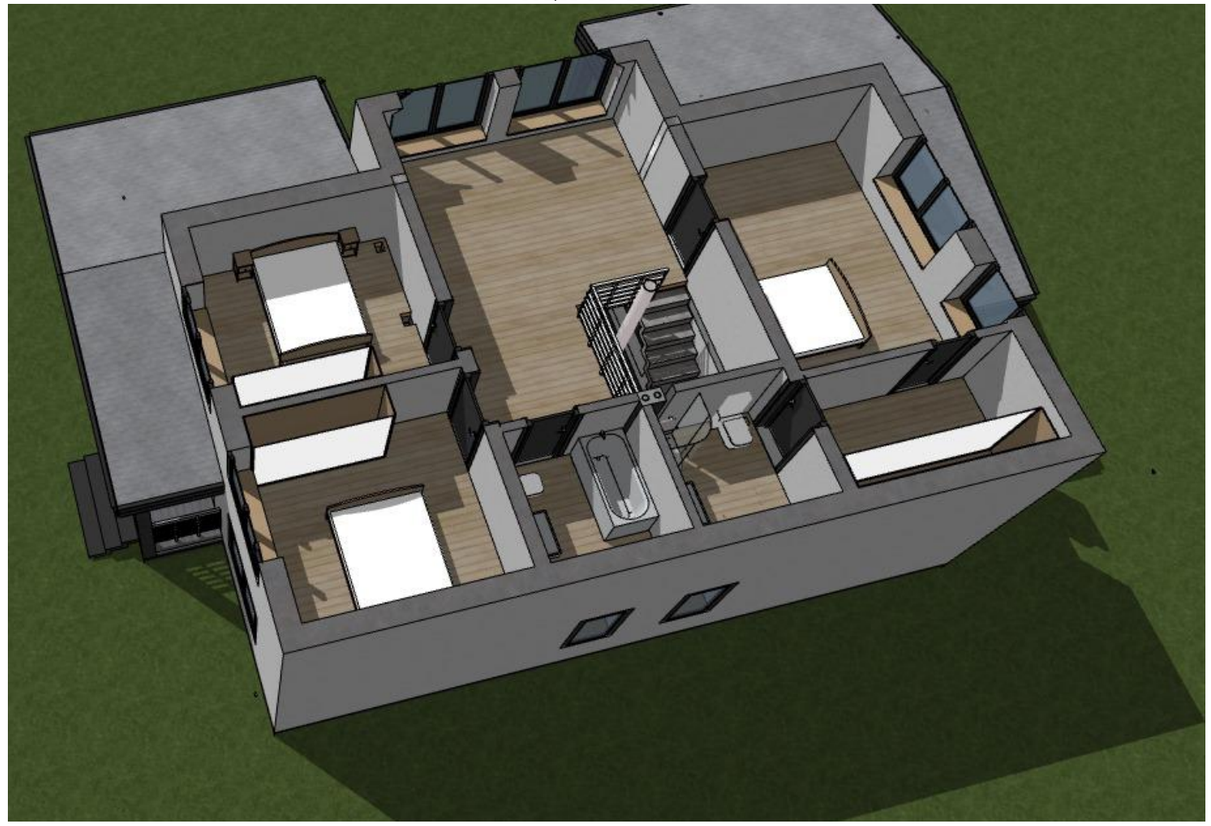

Согласовано

Взам. инв. №

Подпись и дата

Инв. № подл.

Общие виды (поэтажные)

Лист

6